20

005

עיריית תל-אביב-יפו
[illegible] ה
04 -12- 1985
אגף הרישוי
תיק 4/86

תכנית זו מתאימה לדרישות
חוק ההנחיות והתנאים הכלליים
להיתר בניה ותעודת גמר.
חתימה
תאריך 6/12/86

חוק התכנון והבניה, התשכ״ה—1965
תקנות התכנון והבניה (בקשה להיתר, תנאיו ואגרות), התש״ל—1970
טופס 2 (תקנה 2(א))

הוועדה המקומית לתכנון ולבניה
תל-אביב-יפו

מיפרט

במסגרת פרויקט "בנה ביתך" בשכ' התקוה

תיק מס' 21481

א· תיאור הבנין

מגרש	תכנית מיתאר מקומית או מפורטת	חלקה	גוש	מס'	הרחוב	1. המקום
21481		44 חלק	6135	38	ששון	שכונת התקוה

מס' הטלפון	המען	השם	
395698	פ"ד 20 ש. התקוה	ביטון אילנה	2. המבקש
859494	שד' ירושלים 45 יפו	חלמיש	3. בעל הזכות בנכס
239997	אדם הכהן 16 ת.א.	פרחי אדריכל'ס בע"מ	4. עורך הבקשה*
737060	חיבת ציון 22 ר.ג.	י. לבני מהנדס	5. האחראי לביצוע השלד

6. אזור הבניה: ☒ מגורים ☐ מסחר ☐ תעשיה ☐ בנין ציבורי ☐ חקלאי ☐ ……………

7. שטח: המגרש/החלקה: 117.66 מ"ר. אחוז הבניה המותר: 140 % 60% בק.ק.

8. מטרת הבנין: ☒ מגורים ☐ הארחה ☐ עסקים ☐ תעשיה ☐ חקלאי ☐ ציבורי ☐ ……………

9. מהות הבנין ותכליתו: בית מגורים במסגרת פרויקט "בנה ביתך" בש. התקוה חל' חלמיש.

10. תיאור העבודה המוצעת: ☒ בנין חדש ☐ תוספת לבנין קיים ☐ הריסה ☐ תיקונים ☐ שינוי בבנין ☐ ……………
☐ שינוי בשימוש ממטרה: …………… למטרה: ……………

11. האם הבניה היא בעד: ☐ משרד ממשלתי ☐ הרשות המקומית ☐ הסוכנות היהודית

ב· היקף הבניה

קומה	קיים	מוצע	סך הכל	אחוז הבניה	מגורים בדירות: עד 45 מ"ר	עד 65 מ"ר	עד 90 מ"ר	עד 100 מ"ר	מעל 100 מ"ר	עסק; הארחה; וכו'	ציבורי	שונות	מס' חדרים: קיים	מוצע
1	2	3	4	5	6	7	8	9	10	11	12	13	14	15
מרתף														
הכניסה הקובעת לבנין		54.76	54.76	46.54										
א		57.15	57.15	48.57										
ב														
ג														
ד														
ה														
ו														
ז														
חדרי מדרגות														
בניני עזר														
סך הכל		111.91	111.91	95.11										

הנפח המוצע: של הבנין העיקרי …………… מ"ק. של בנין עזר ……………מ"ק.

מינהל ההנדסה
אגף הרישוי
חתימה

ג· השימוש בבנין
1. הבניה המוצעת למגורים

דירות בנות:	שטח כל דירה מ"ר	מספר דירות מכל סוג	שטחים — מ"ר: כל הדירות	מזה: רצפות חדרי דיור בלבד, ומרפסות מקורות	רצפות חדרי שירות ופרוזדורים בלבד	רצפות של מרפסות בלתי מקורות	מספר חדרים: דירות	מטבחות	אמבטיות	בתי שימוש	אחרות
1	2	3	4	5	6	7	8	9	10	11	13
חדר אחד	ראה השטחים סכימתי של שטחי הבניה בכל קומה. המציין מספר החדרים ושטח כל דירה.										
2 חדרים											
3 חדרים											
4 חדרים											
5 חדרים											
6 חדרים											
7 חדרים ויותר											
חדרים נוספים לדירות קיימות											
בניני עזר											
סך הכל											

נסרק

ביטון ש. התקוה 1/5

2. הבניה הקיימת והמוצעת לתעשיה ולמלאכה

פרטים	קיים: שטח	גובה	נפח	% הבניה	מוצע: שטח	גובה	נפח	% הבניה	סך הכל: שטח	נפח	% הבניה	הערות
1	2	3	4	5	6	7	8	9	10	11	12	13
אולמי מלאכה												
משרדים												
חדרי שירות												
סככות												
בניני עזר												
הדרי מדרגות												
סך הכל												

3. הבניה המוצעת למטרות אחרות (הארחה, עסקים ומשרדים, בניני ציבור, בניני משק חקלאי, מטרות שונות).

השימוש המיועד	שטחים — מ"ר: סך הכל מ"ר	מזה: חדרים	אולמות	אחסנה	חדרי שירות	מספר הדרים, אולמות וכו': הדרים	אולמות	אחסנה	חדרי שירות
1	2	3	4	5	6	7	8	9	10
בניני עזר (למעט אלה המפורטים ב־ג(4))									

4. חלקי בנין אחרים — הבניה המוצעת, שטח במ"ר.

חדרי מדרגות	מרפסות שלא נכללו לעיל	מעליות	חדרי הסקה	חדרי כביסה	מקלטים	קומת עמודים מפולשת	מחסנים	מוסכים	בניני עזר נוספים	סך הכל
1	2	3	4	5	6	7	8	9	10	11
					6.30					

ד· חומר הבניה

קירות חיצונים	☐ בטון מזוין	☐ לבני בטון או בלוקים	☐ לבני סיליקט	☐ לבנים שרופות	☐ אבן טבעית
	☐ אבן מלאכותית	☐ איטונג	☐ עץ	☐ ברזל	☐ חמרים אחרים
תקרות	☐ בטון מזוין	☐ עץ	☐ חומר אחר ……………		
גג	☐ בטון מזוין	☐ רעפים	☐ אסבסט	☐ פח	☐ חומר אחר ……………

ה· גדרות קיימות……………מ"א מוצעות……………מ"א

ו· מקרא
- 🟦 בטון או בטון מזוין
- ☐ אבן
- ☐ עץ
- ☐ איטונג
- 🟥 בלוקים או לבנים מבטון
- ☐ סיליקט או לבנים אדומות
- ☐ חומר אחר
- ☐ להריסה

הערות: ______________________

הנני מאשר כי הנתונים הנ"ל נכונים

תאריך ________ חתימת המבקש ביטון אילנה ________ התימת עורך הבקשה* ________

חתימת האחראי לביצוע השלד י. לבני ________ חתימת בעל הזכות בנכס ________

לשימוש הוועדה המקומית בלבד	מס' ההיתר	תאריך ההיתר	תאריך התחלת הבניה	תאריך גמר הבניה

אישורים של רשויות חוץ:

הותמת הוועדה המקומית

* הי' מספר עורכי בקשה, כאמור בתקנה 2ה'. יבוא במקום כל אלה הראשון שברשימת עורכי הבקשה, כאמור בטופס 1.

ד.מ. ר-ה גלופה

חשוב שטח:

ק. קרקע:
7.10 x 8.60 = 61.06
הורדה 2.10 x 3.00 = 6.30
סה שטח 54.76

ק. א:
7.10 x 8.60 = 61.06
1.70 x 2.30 = 3.91
סה שטח 57.15

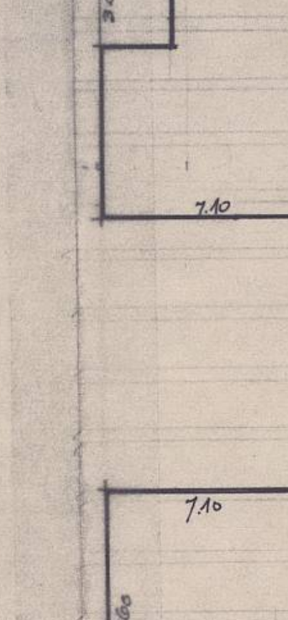
2.10
30
8.00
7.10
7.10
8.60
1.7
2.3

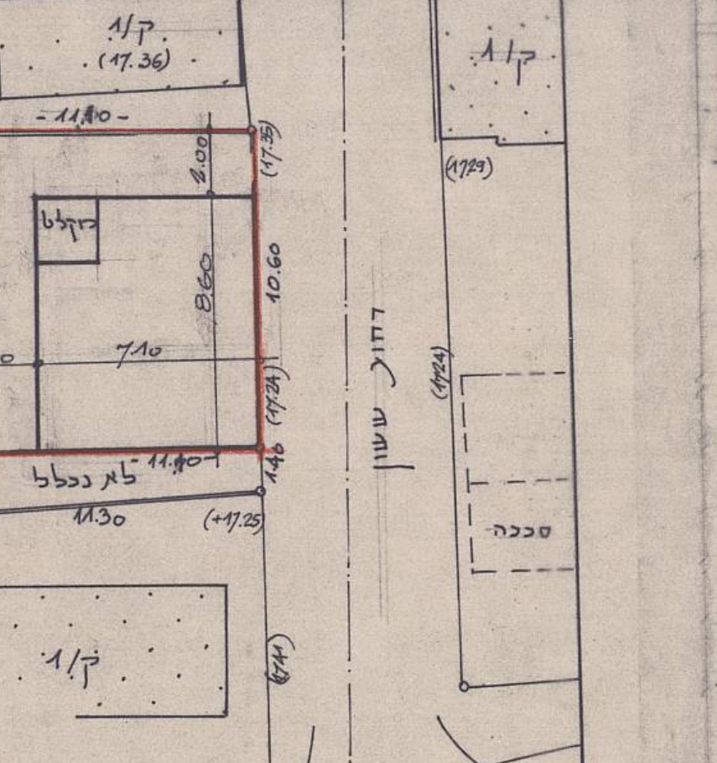
ק/1
(17.36)
בכוי
-11.10-
(17.45)
(17.35)
מקלט
10.60
2.00
8.60
10.60
4.00
7.10
(17.24)
לא נכלל
11.10
2.25
1.46
11.30
(+17.25)
ק/1
גדר
רחוב ששון
(17.29)
(17.24)
ק/1
סככה
דרך לוד

תרשים המגרש 1:250

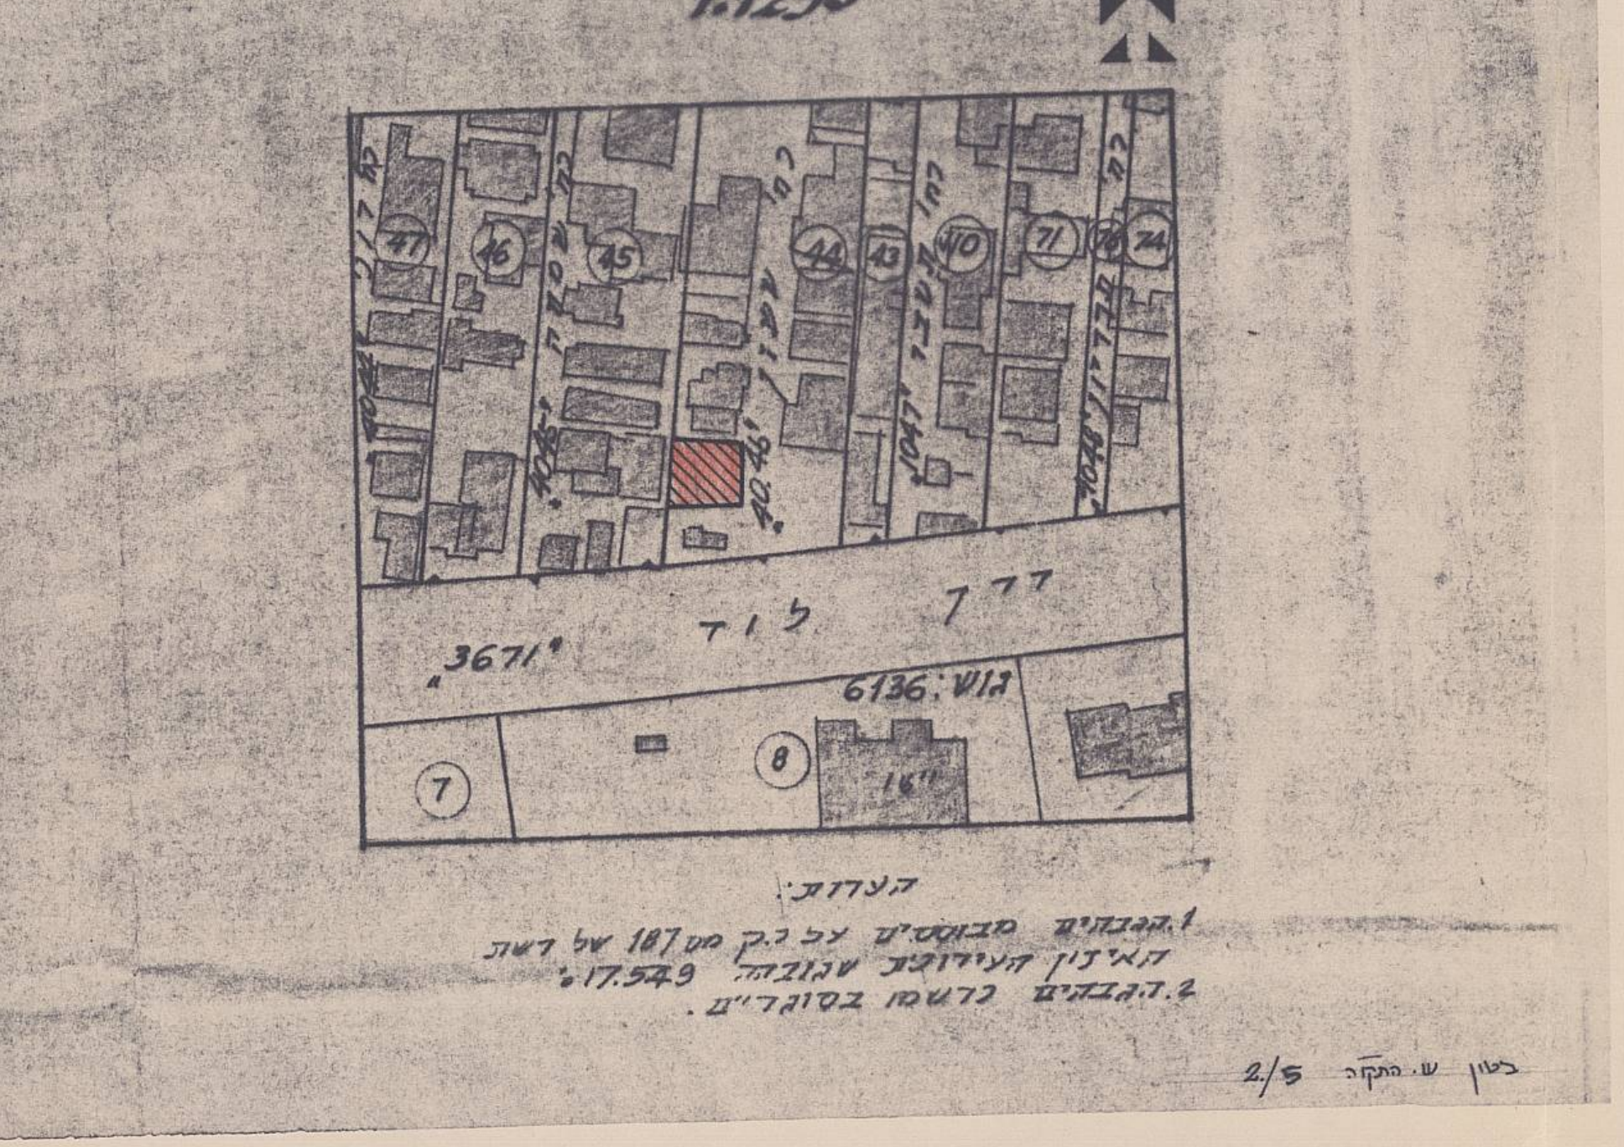
דרך לוד
ששון
גוש 6136
3671
47
46
45
44
43
40
71
74
7
8

תרשים הסביבה 1:1250

הערות:
1. הבניינים מבוססים עפ"י ב.ק מס' 187 של רשות המדידות הישראלית שגובהו 17.579
2. הבניינים נרשמו בסקר"ש.

ביטון ש. התקוה 2/5

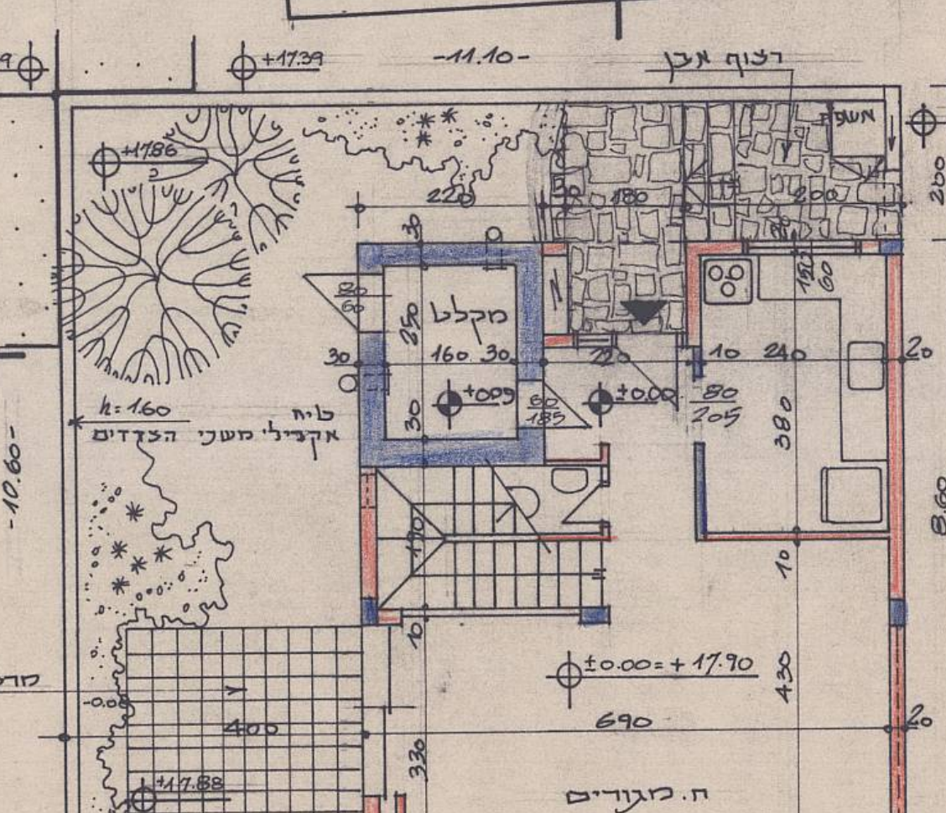
ב
+17.69
+17.39
-11.10-
ריצוף אבן
משטח
+17.35
+17.86
220
180
200
200
מקלט
160 30
30
±0.00
±0.00
טיח אקרילי משני הצדדים
h:1.60
-10.60-
240
380
8.60
מרצפות בטון 45/45/5
±0.00=+17.90
690
400
430
330
+17.88
ח. מגורים
+17.24
400
7.10
+17.26
לא נכלל
+17.43
א
רח' ששון
רצוף מדרכה בתאום עם מח' דרכים

תכנית ק. קרקע 1:100

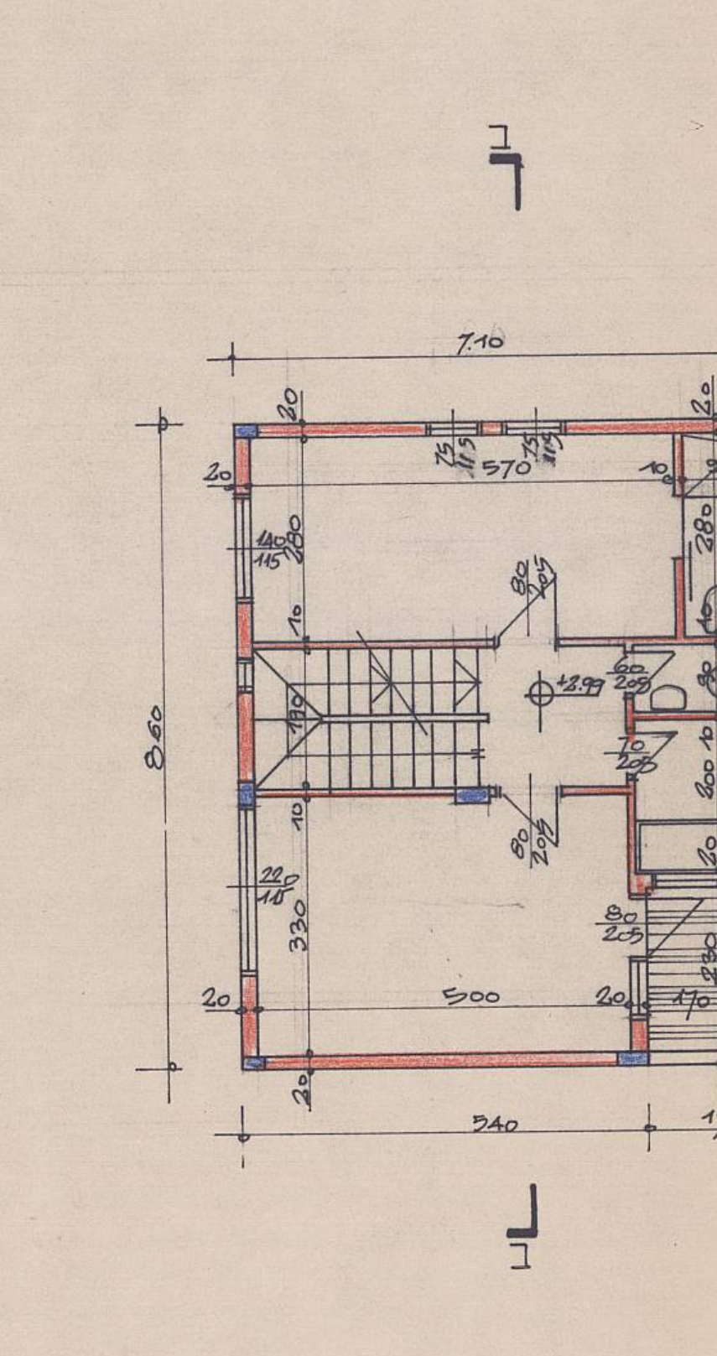
ב
7.10
570
8.60
א
5.00
2.40
1.70

תכנית ק. א 1:100

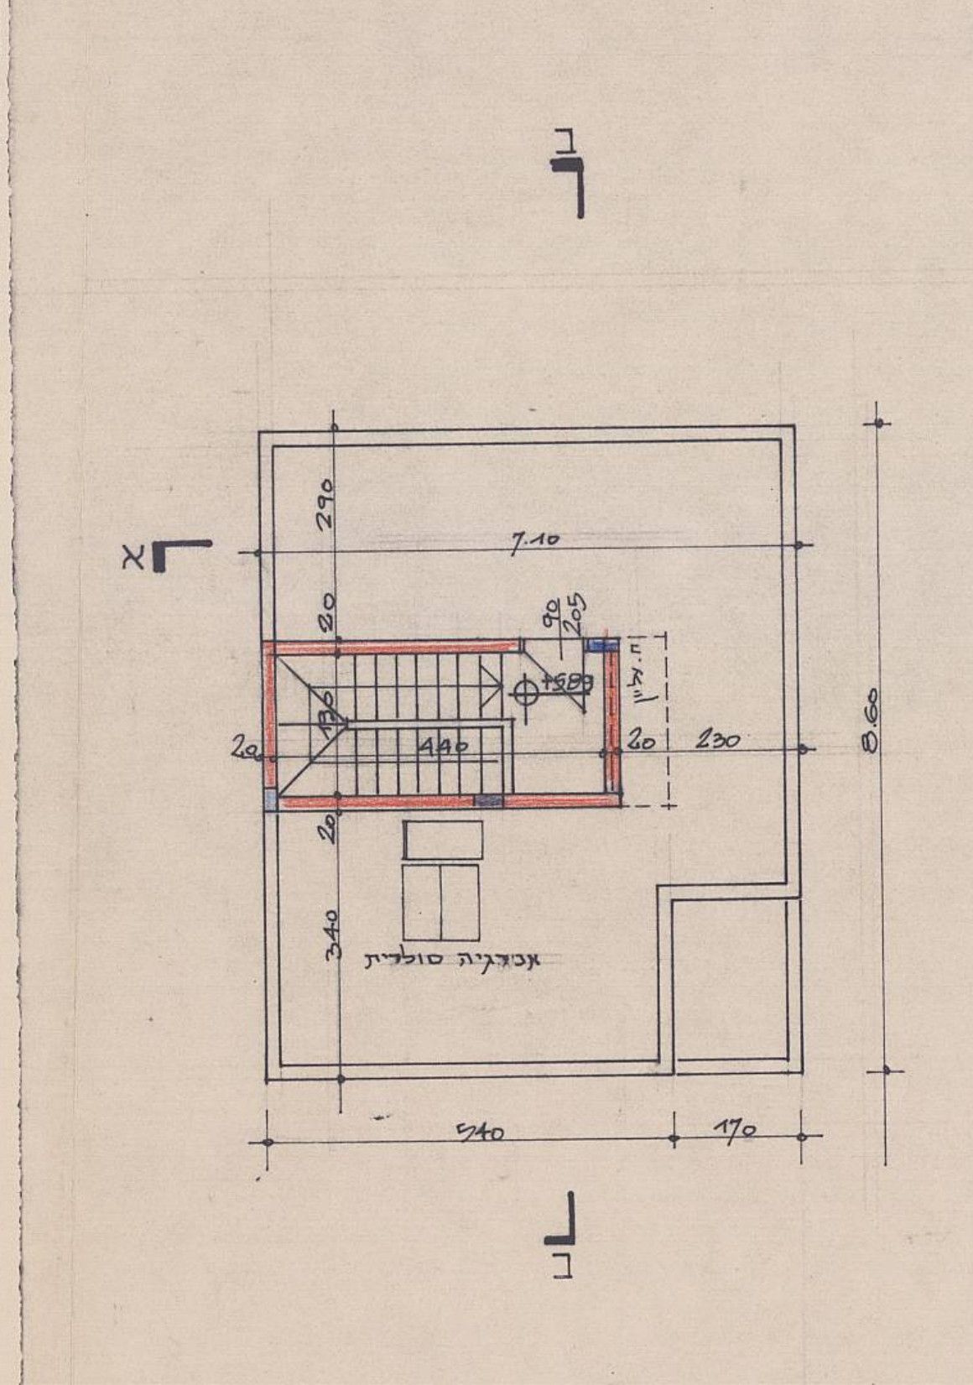
ב
2.90
7.10
4.00
2.30
8.60
א
אנרגיה סולרית
5.40
1.70

תכנית הגג 1:100

ביטון ש. התקוה 3/5

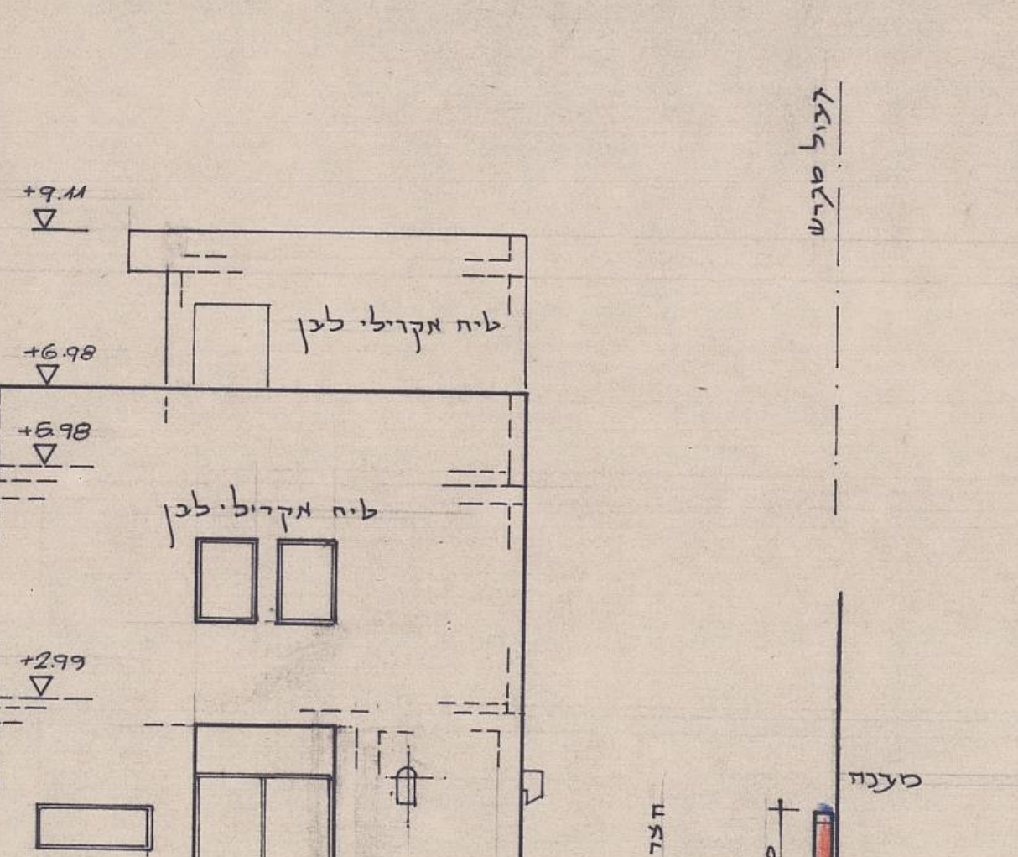
גבול מגרש
+9.11
טיח אקרילי לבן
+6.98
+5.98
+2.99
רח' ששון
±0.00=+17.90
+17.35
+17.56
גדר
מעקה

ת. צפונית 1:100

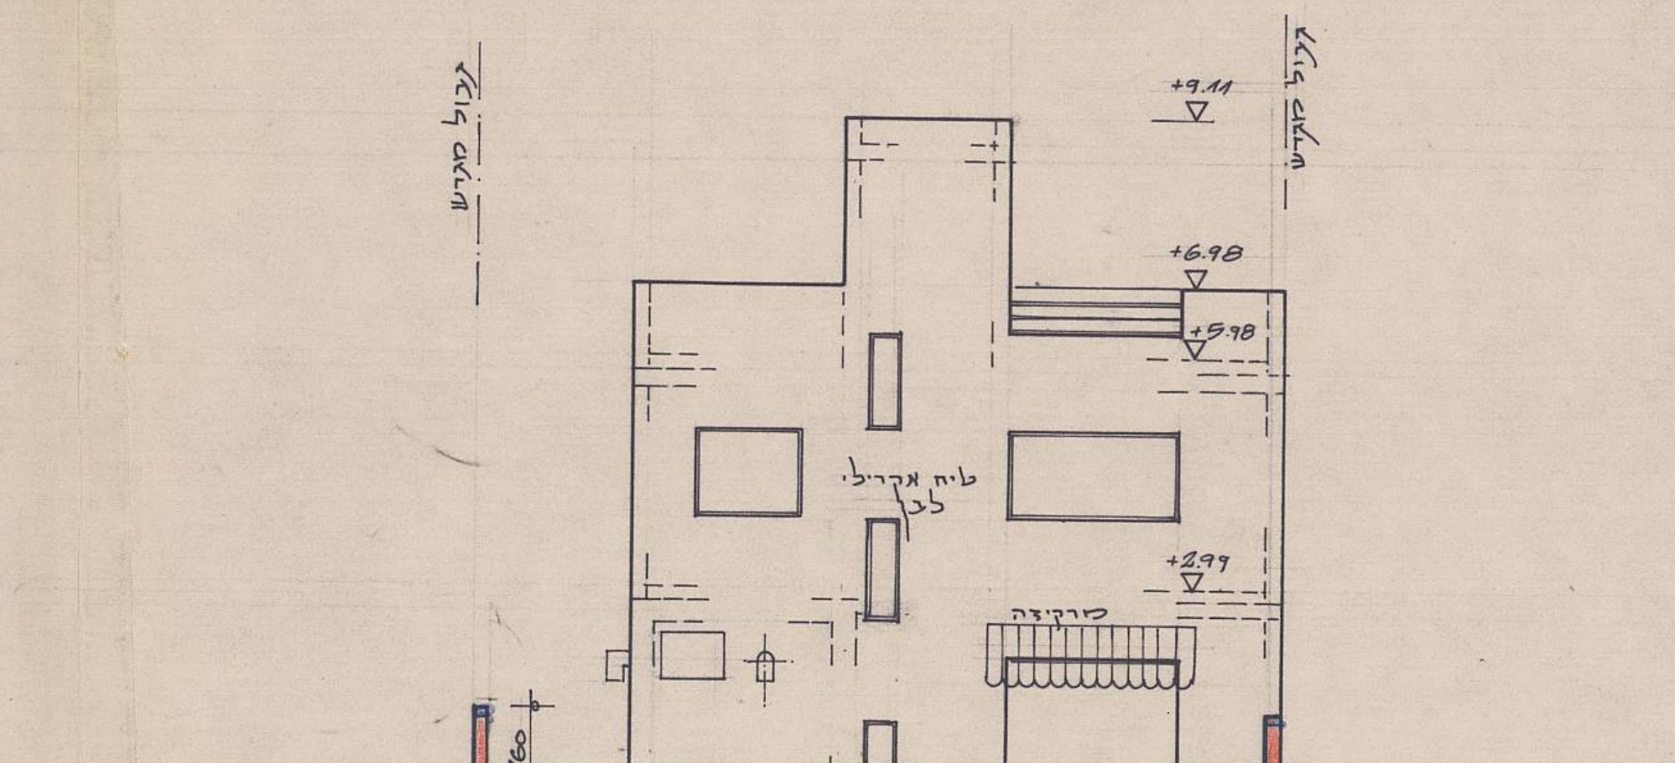
גבול מגרש
+9.11
+6.98
+5.98
טיח אקרילי לבן
+2.99
פרגולה
+17.88
±0.00
+17.39
+17.43

ת. מערבית 1:100

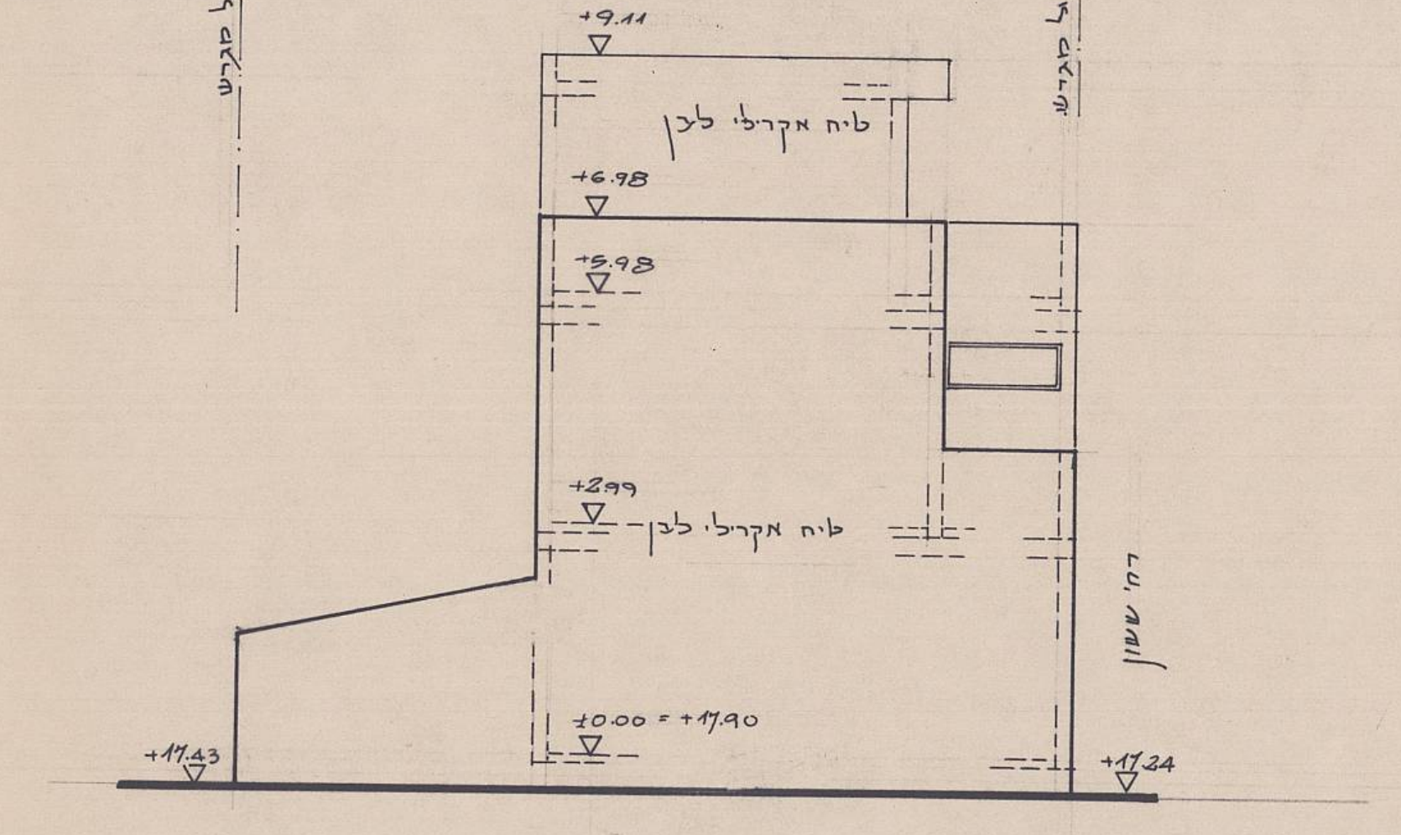
גבול מגרש
+9.11
טיח אקרילי לבן
+6.98
+5.98
+2.99
טיח אקרילי לבן
רח' ששון
±0.00=+17.90
+17.43
+17.24

ת. דרומית 1:100

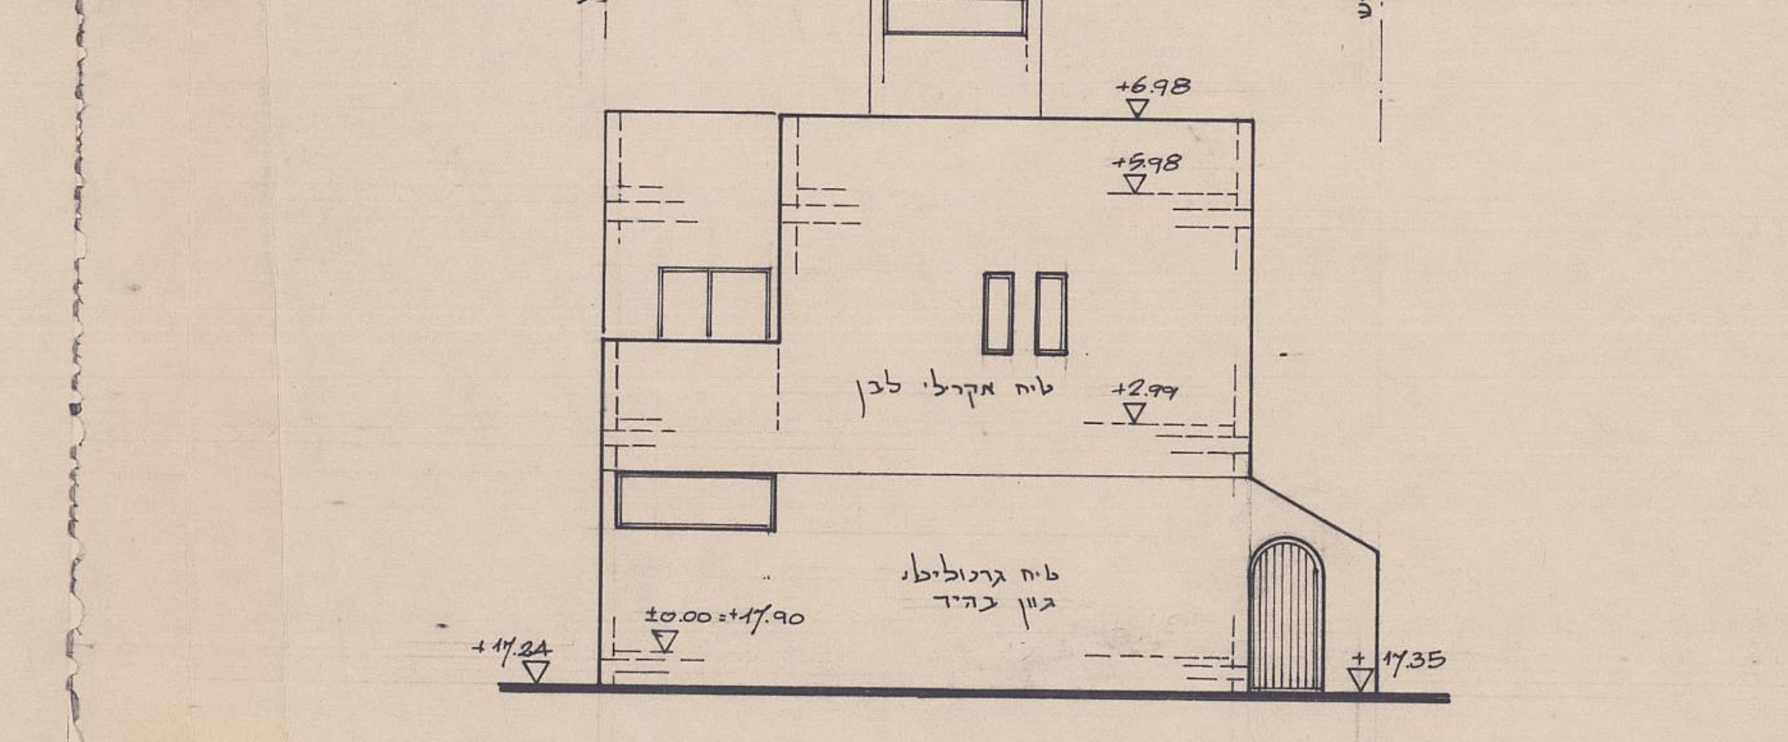
גבול מגרש
+9.11
+6.98
+5.98
טיח אקרילי לבן
+2.99
טיח גרנוליט בגוון בהיר
±0.00=+17.90
+17.24
+17.35

ת. מזרחית (רח' ששון) 1:100

ביטון ש. התקוה 4/5

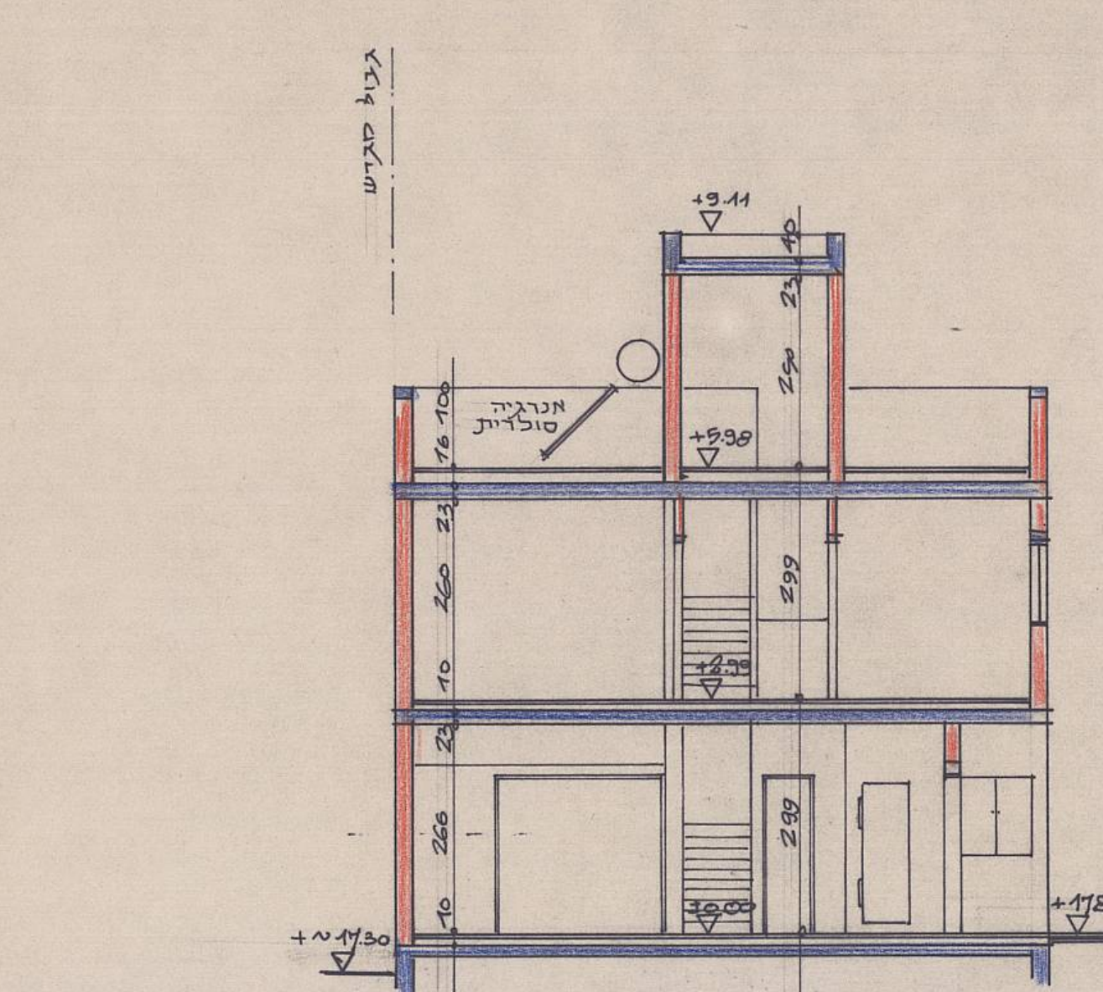
גבול מגרש
+9.11
אנרגיה סולרית
+5.98
+2.99
±0.00
+17.30
+17.83
+17.30

חתך ב־ב 1:100

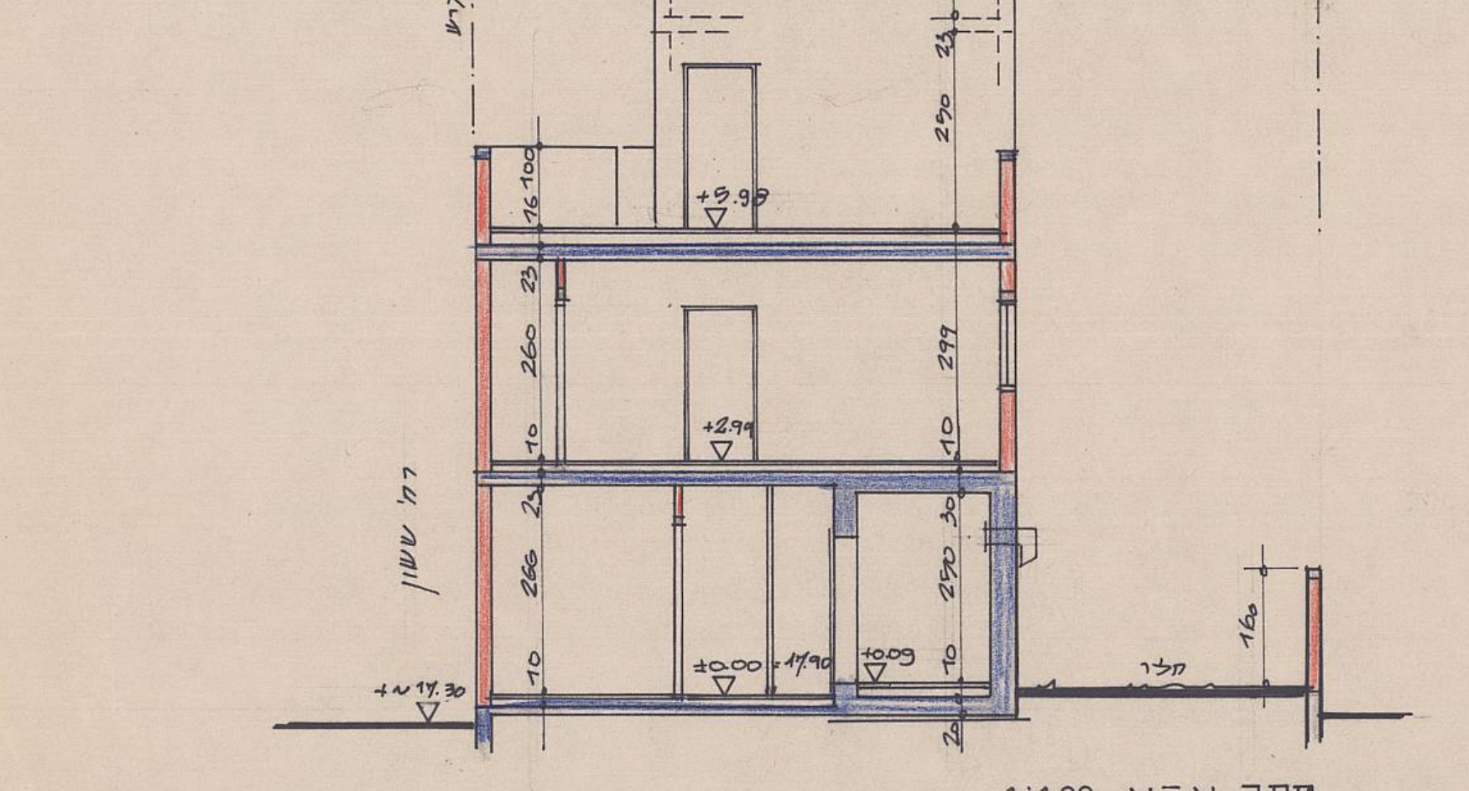
גבול מגרש
+9.11
+5.98
+2.99
רח' ששון
±0.00=+17.90
+17.30
מדרכה

חתך א־א 1:100

ביטון ש. התקוה 5/5

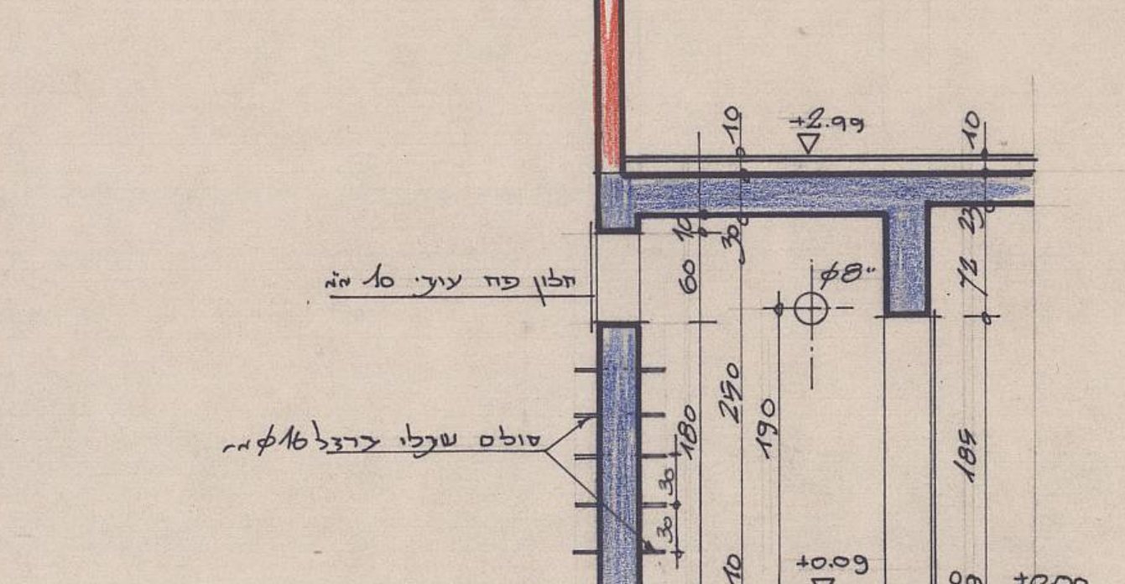
+2.99
חלון פח עיוור 10 מ"מ
סולם שלבי ברזל ⌀16 מ"מ
290
190
+0.09
±0.00

חתך 1־1 1:50

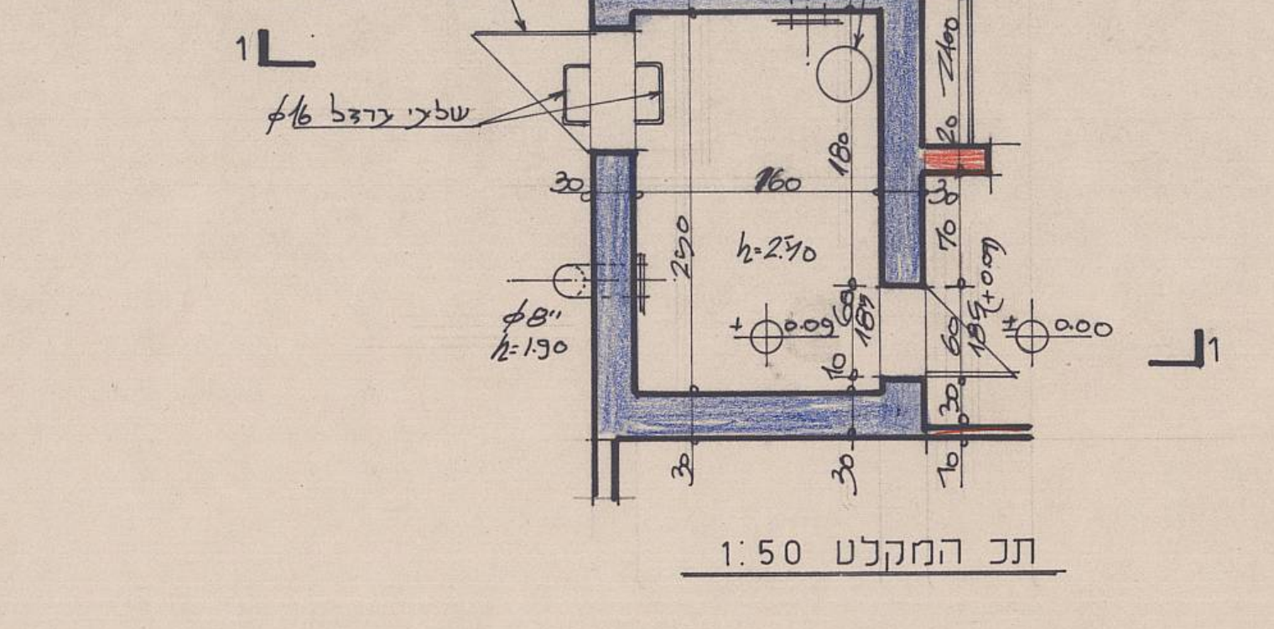
⌀8"
h:1.90
סולמים 30
חלון פח 10 מ"מ
שלבי ברזל ⌀16
160
h:2.40
+0.09
±0.00
⌀8"
h:1.90
1
1

תכ המקלט 1:50

שטח המקלט 1.60 x 2.40 = 4.00

הוראות ביצוע למקלט על-קרקעי

בטון רזה ב-150. תשתית בטון מתחת לרצפה.

בטון המקלט ב-300 - לפי התקן הישראלי 118 שנבדק ע"י מכון התקנים הישראלי או מוסד מוסמך אחר.

פלדת הזיון לפי תקן ישראלי 31, 580, 893, 739.

לפי המפורט במפרט הכללי למקלטים (58).

על הקבלן / המבקש להזמין את המהנדס האחראי על ביצוע השלד ולקבל אישור לביצוע כל שלבי המקלט.
עבודות הבידוד יש לבצע בהתאם למפרט הכללי למקלטים (58).
יש להזמין את המפקח מטעם הרשות המקומית לבדיקת שלבי בניית המקלט.

על הרשות המקומית להקפיד על מסירתה לועדה המקומית תצהיר של האחראי לביצוע השלד - בהתאם לקובץ התקנות 8392 מיום 21.9.78 (חוק התכנון והבניה תשכ"ה - 1965, תקנות בדבר תצהיר על הקמת שלד מקלט).

יש להזמין בדיקה באמצעות מכון התקנים לפי ממפ"כ מס' 20 - אינסטלציה כמתחייב מ-ה"ח 11 מאפריל 1980.

הוועדה המקומית לתכנון ולבניה
לשכת תכנון תל-אביב-יפו
בהתאם לסעיף 18 (ב) לתקנות התכנון והבניה (בקשה להיתר, תנאיו ואגרות) תש"ל-1970 הריני לאשר כי לטפסה זו צורף היתר בניה/שימוש מס' 4188
מיום 20.2.86 ומהווה חלק בלתי נפרד ממנו.
מהנדס העיר
8 -01- 1986
תאריך