


מפה טופוגרפית 1:250

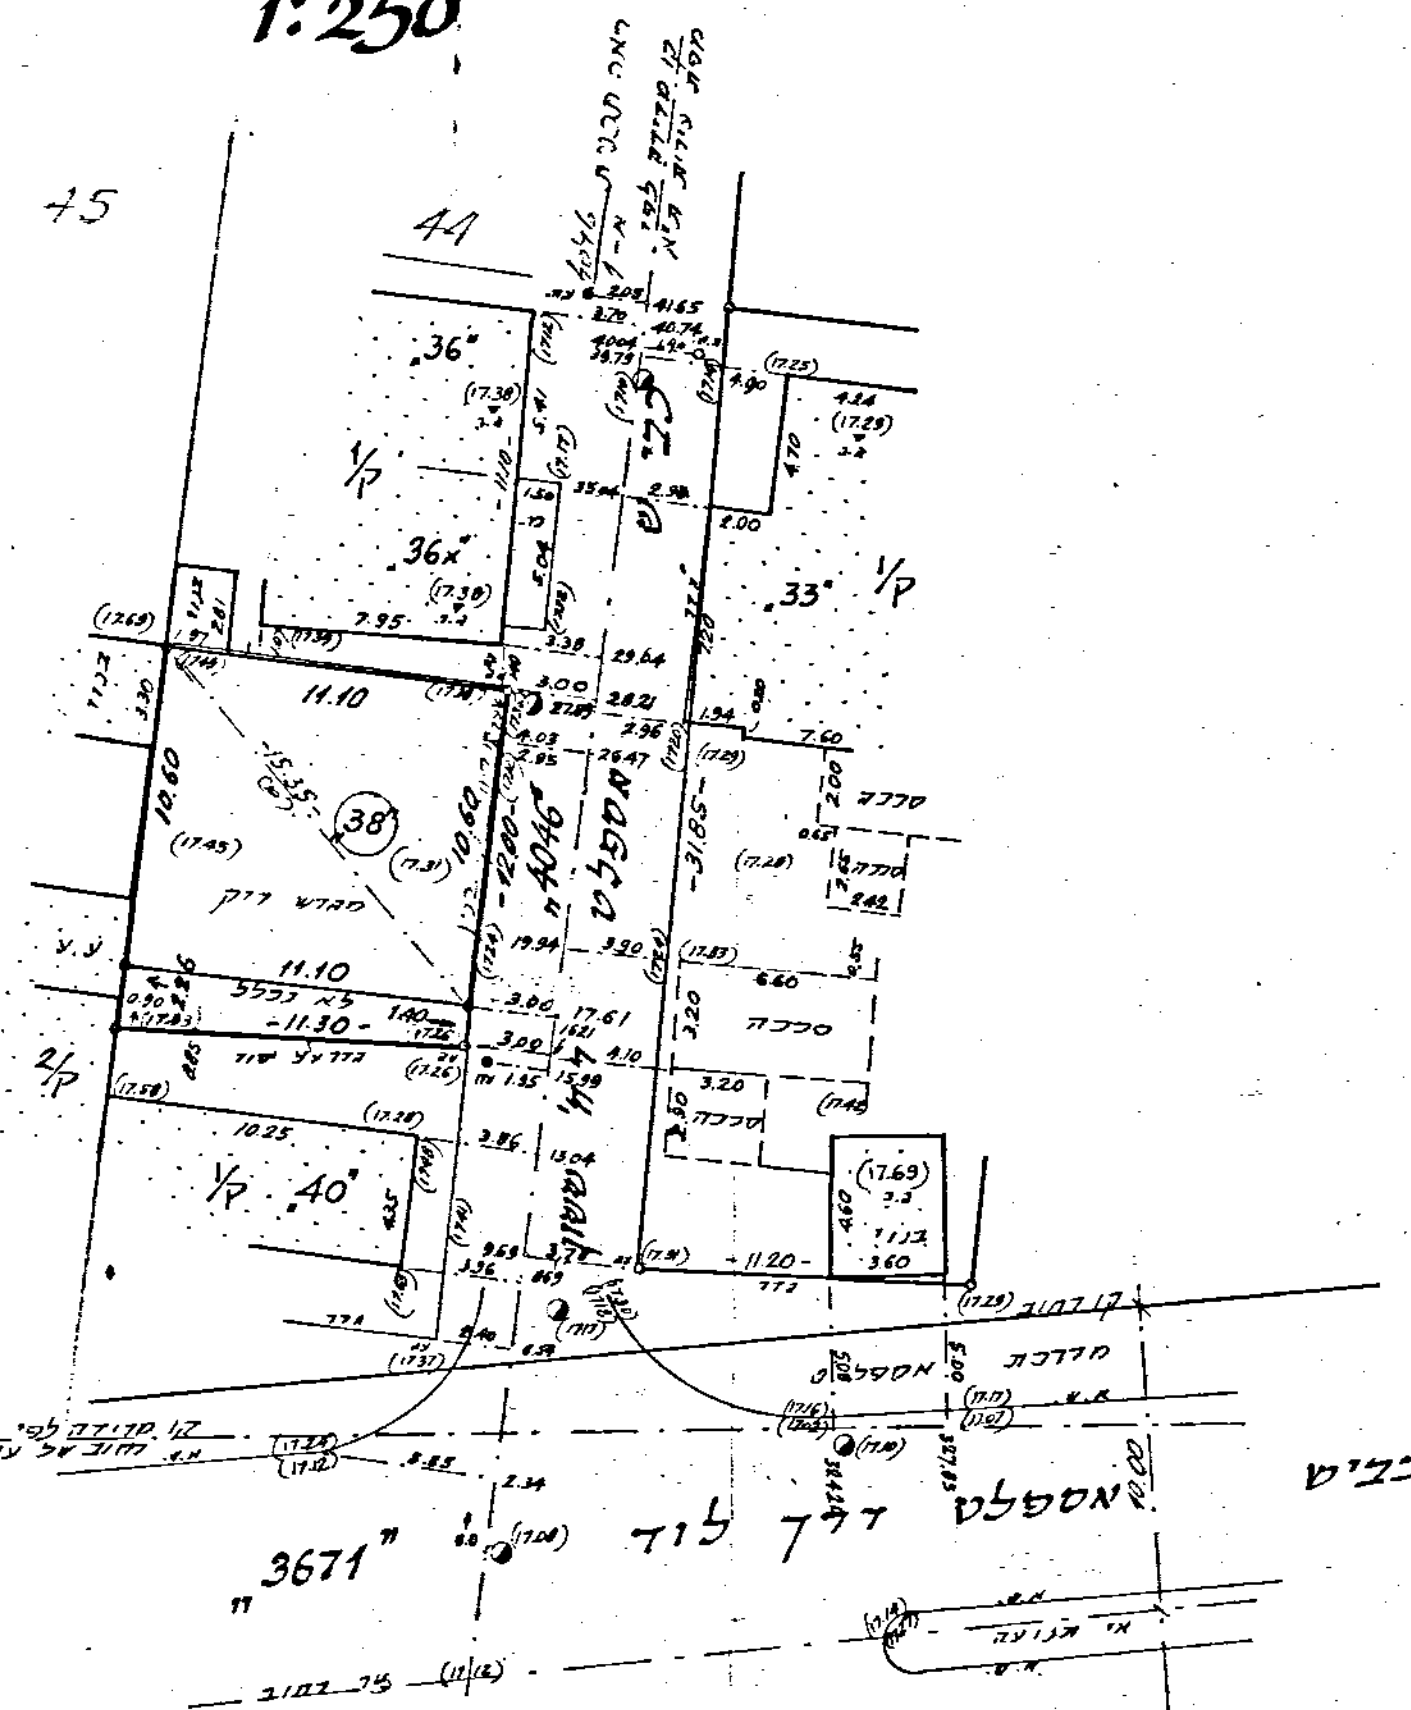

קו מספר

ערכון מסד טופוגרפית
1.4.85

לא לערכי רשום!

לאופר ראובן-מודד מוססן (ס"ס רשמי 574)
מועד טכני למדידות
רחוב אינשטיין 19 רמת-אביב
טל 03-414535

נתיב תל-אביב-יפו / סניף הנהלה
מחלקת מדידות / מדור השילוט והמסמך

חשור כתובת
38/116
דואר
מיקוד
939.8
תאריך

תל-אביב גוש: 6135 חלקה: 44 (חלק)

רח' ששון 38, שכונת התקווה
חוקן עבוד: חברה חלסיס, בניס

שטח מדוד: 117.66 מ'ר

לפי ת.ב.ג. 2215 (פרט מוסדה)
רח' - 4016
רוחב הרחוב 5-8 מ' או רוחב הקיים
קו בנין 0.
נתיב להוציא חיתר בניה במקומות ההפקדה
לפי סעיף 97 א' לחוק.
פרטים נוספים בקשר הבניה יש לקבל ממח'
אדריכלות (גב' ר. פולר).

20.9.85


26.9.85
נתיב תל-אביב-יפו
סניף הנהלה
מחלקת הדוכים

עיריית תל-אביב-יפו / סניף הנהלה
מחלקת מדידות

תאריך: 23.9.85
חתימה: ס"ס
חתימה: (א.ח.)

שטח הפקעה (לצורך חשוב זכויות בניה)
מאושר (ת.ב.ע.) מימור (גרמי)
מוצע (ת.ב.ע.) מימור (גרמי)
הערה: שטח הפקעה סופי יקבע במסמך לערכי רשום

תרשים הסביבה
1:1250

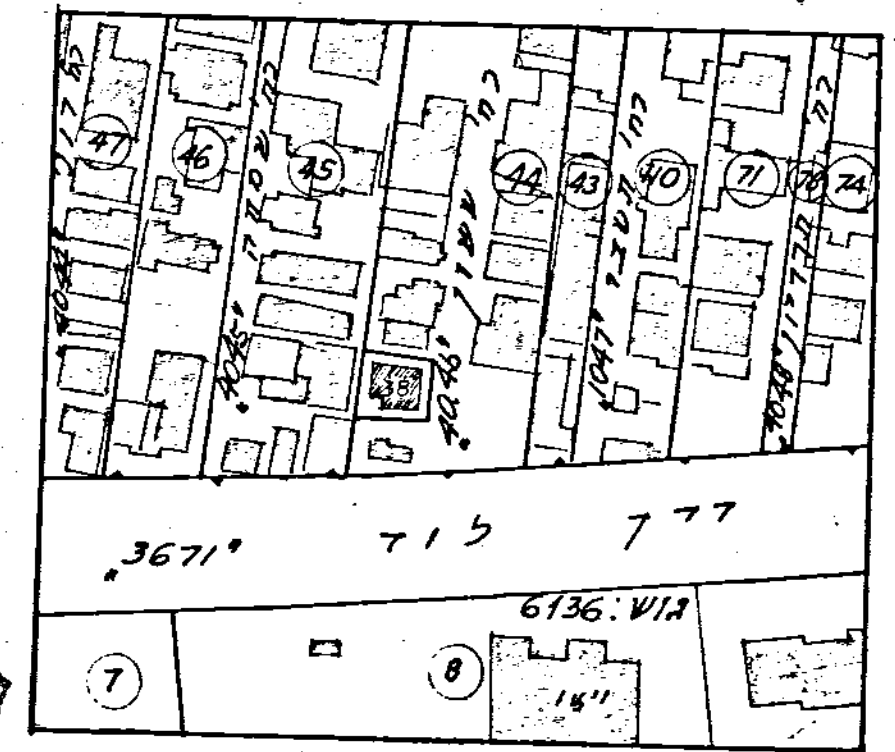

פיון השמירני - אדריכלים
ומתכננים (1980) ר"מ
רח' אביב-יפו 44, תל-אביב

8.9.85

הערות:
1. הגבהים מבוססים על כ"ק מס' 187 של רשם
האיזון העירוני שגובהו 17.549
2. הגבהים כרומו בסוקר"ם.

איכות נמוכה