215-0044

24

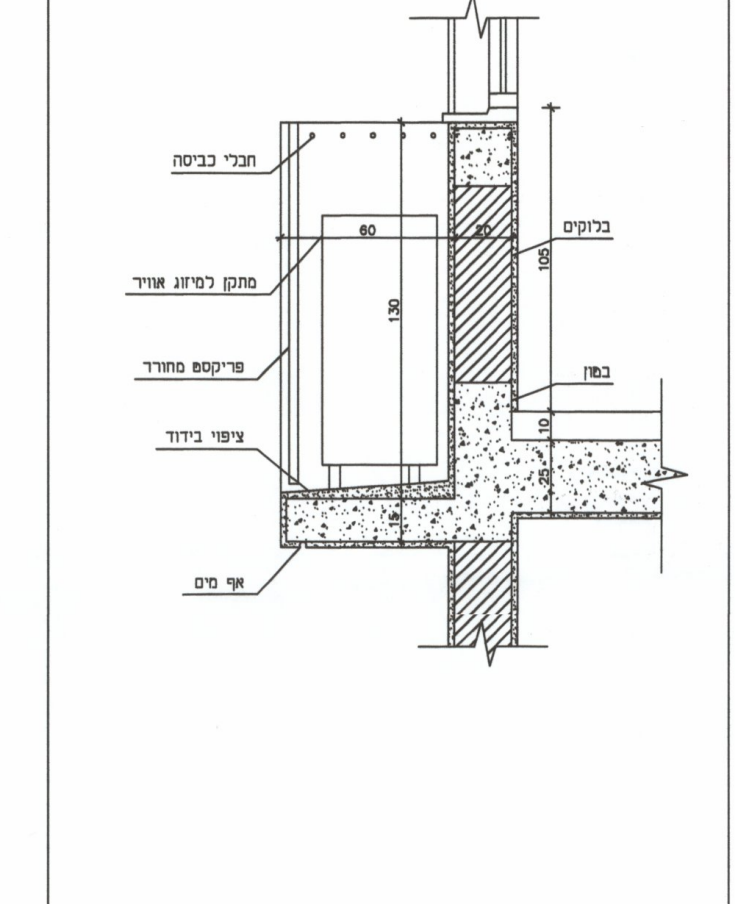

חגורי בקרה
בלוקים
מתקן לפינוי אוויר
פוליסטירן מחורר
ציפוי בידוד
איטום
בטון

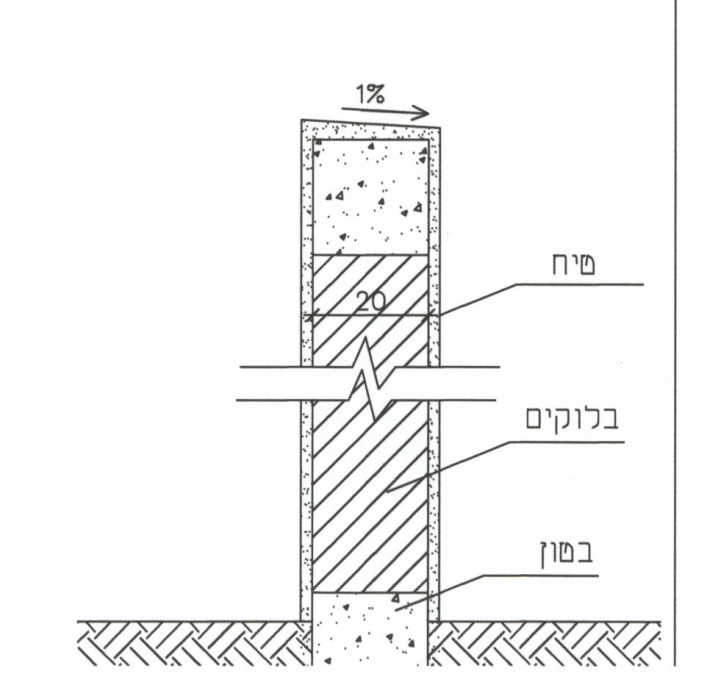

מיח
בלוקים
בטון

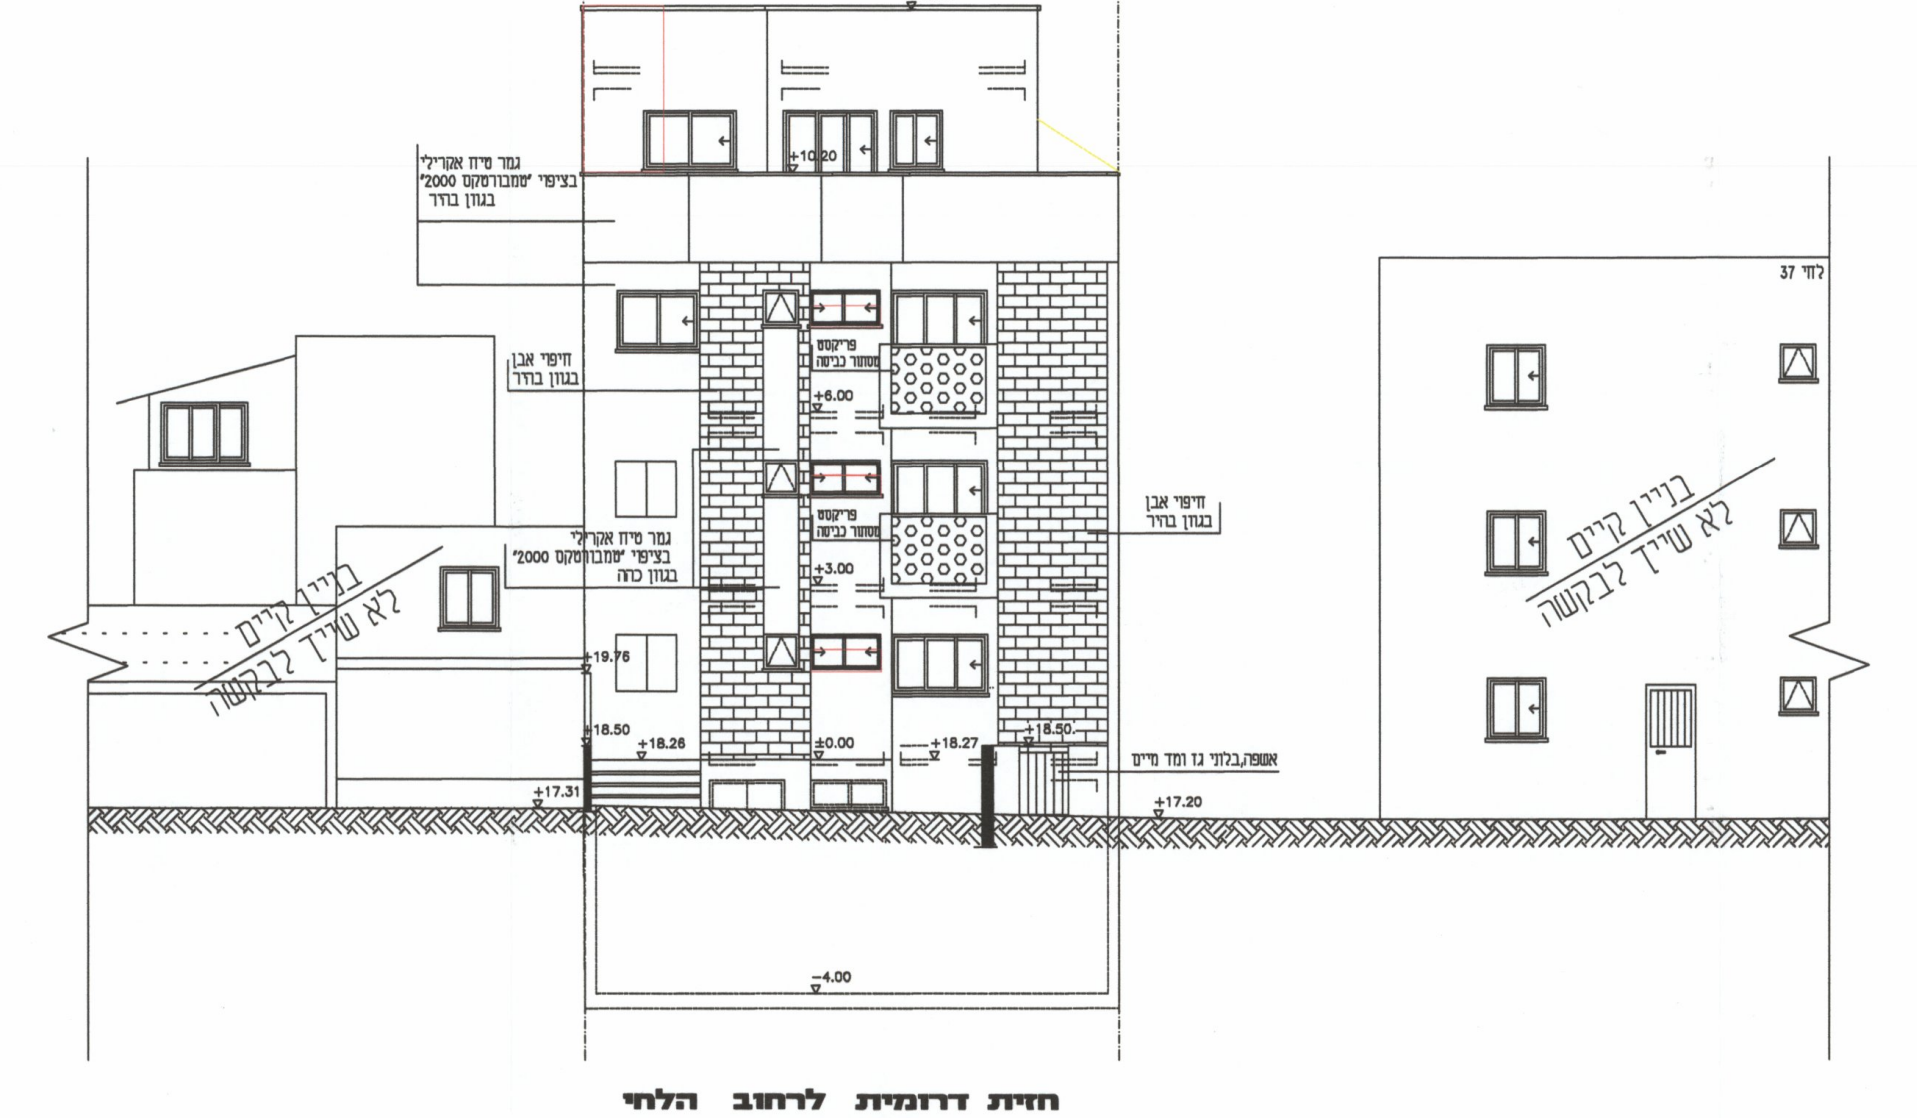

בניין קיים לא שייך לבקשה

חזית דרומית לרחוב הלחי
קנה מידה 1:100

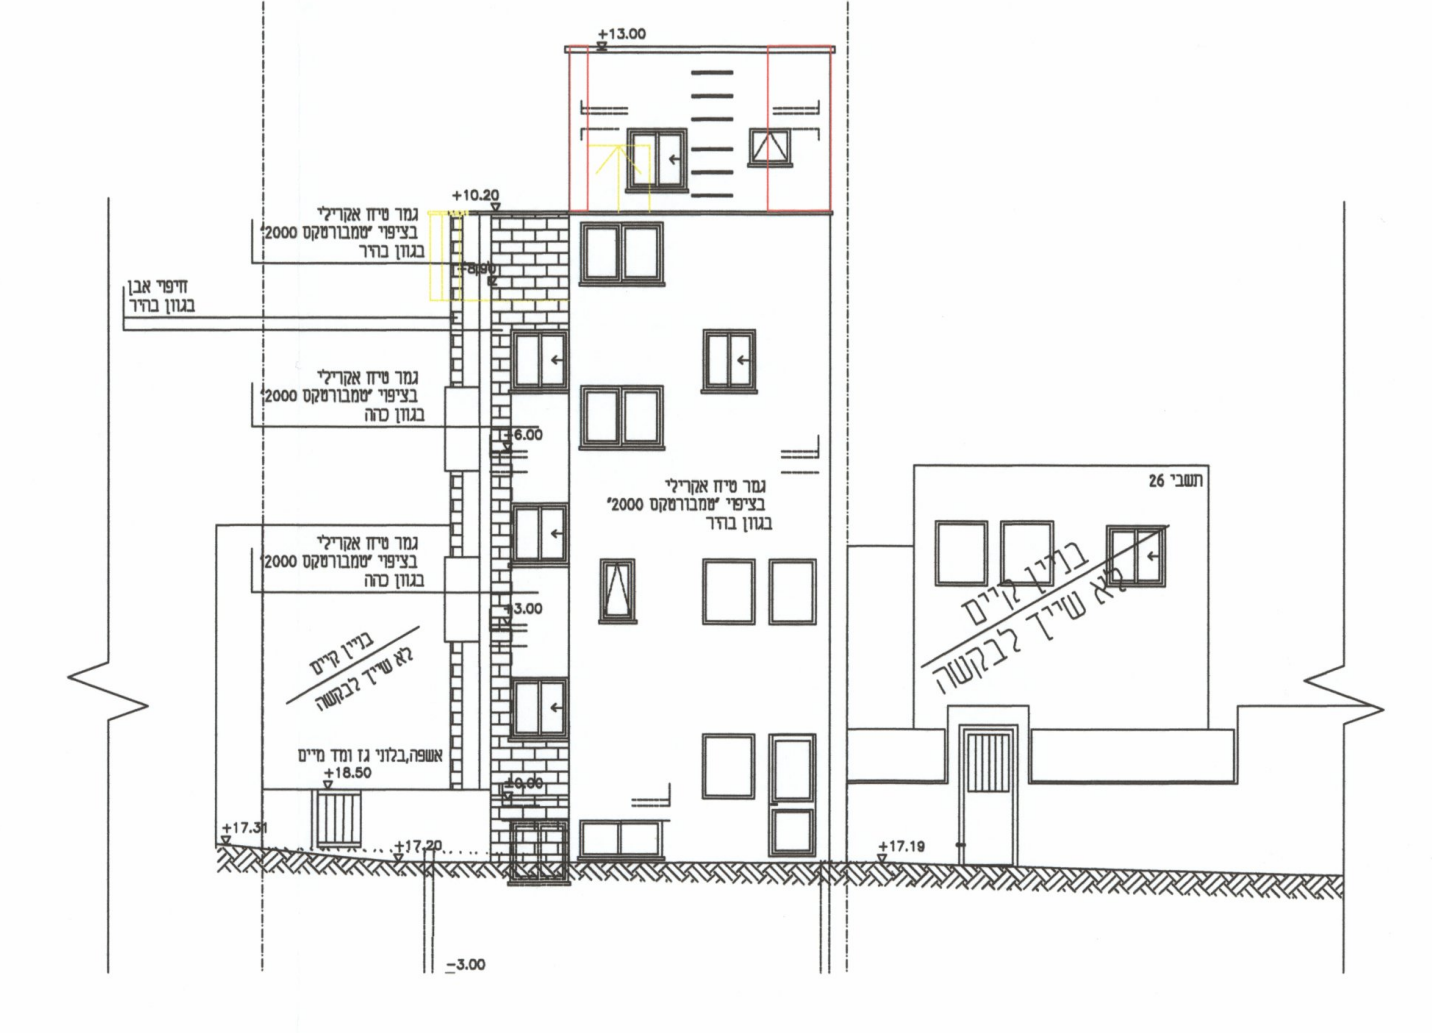

בניין קיים לא שייך לבקשה

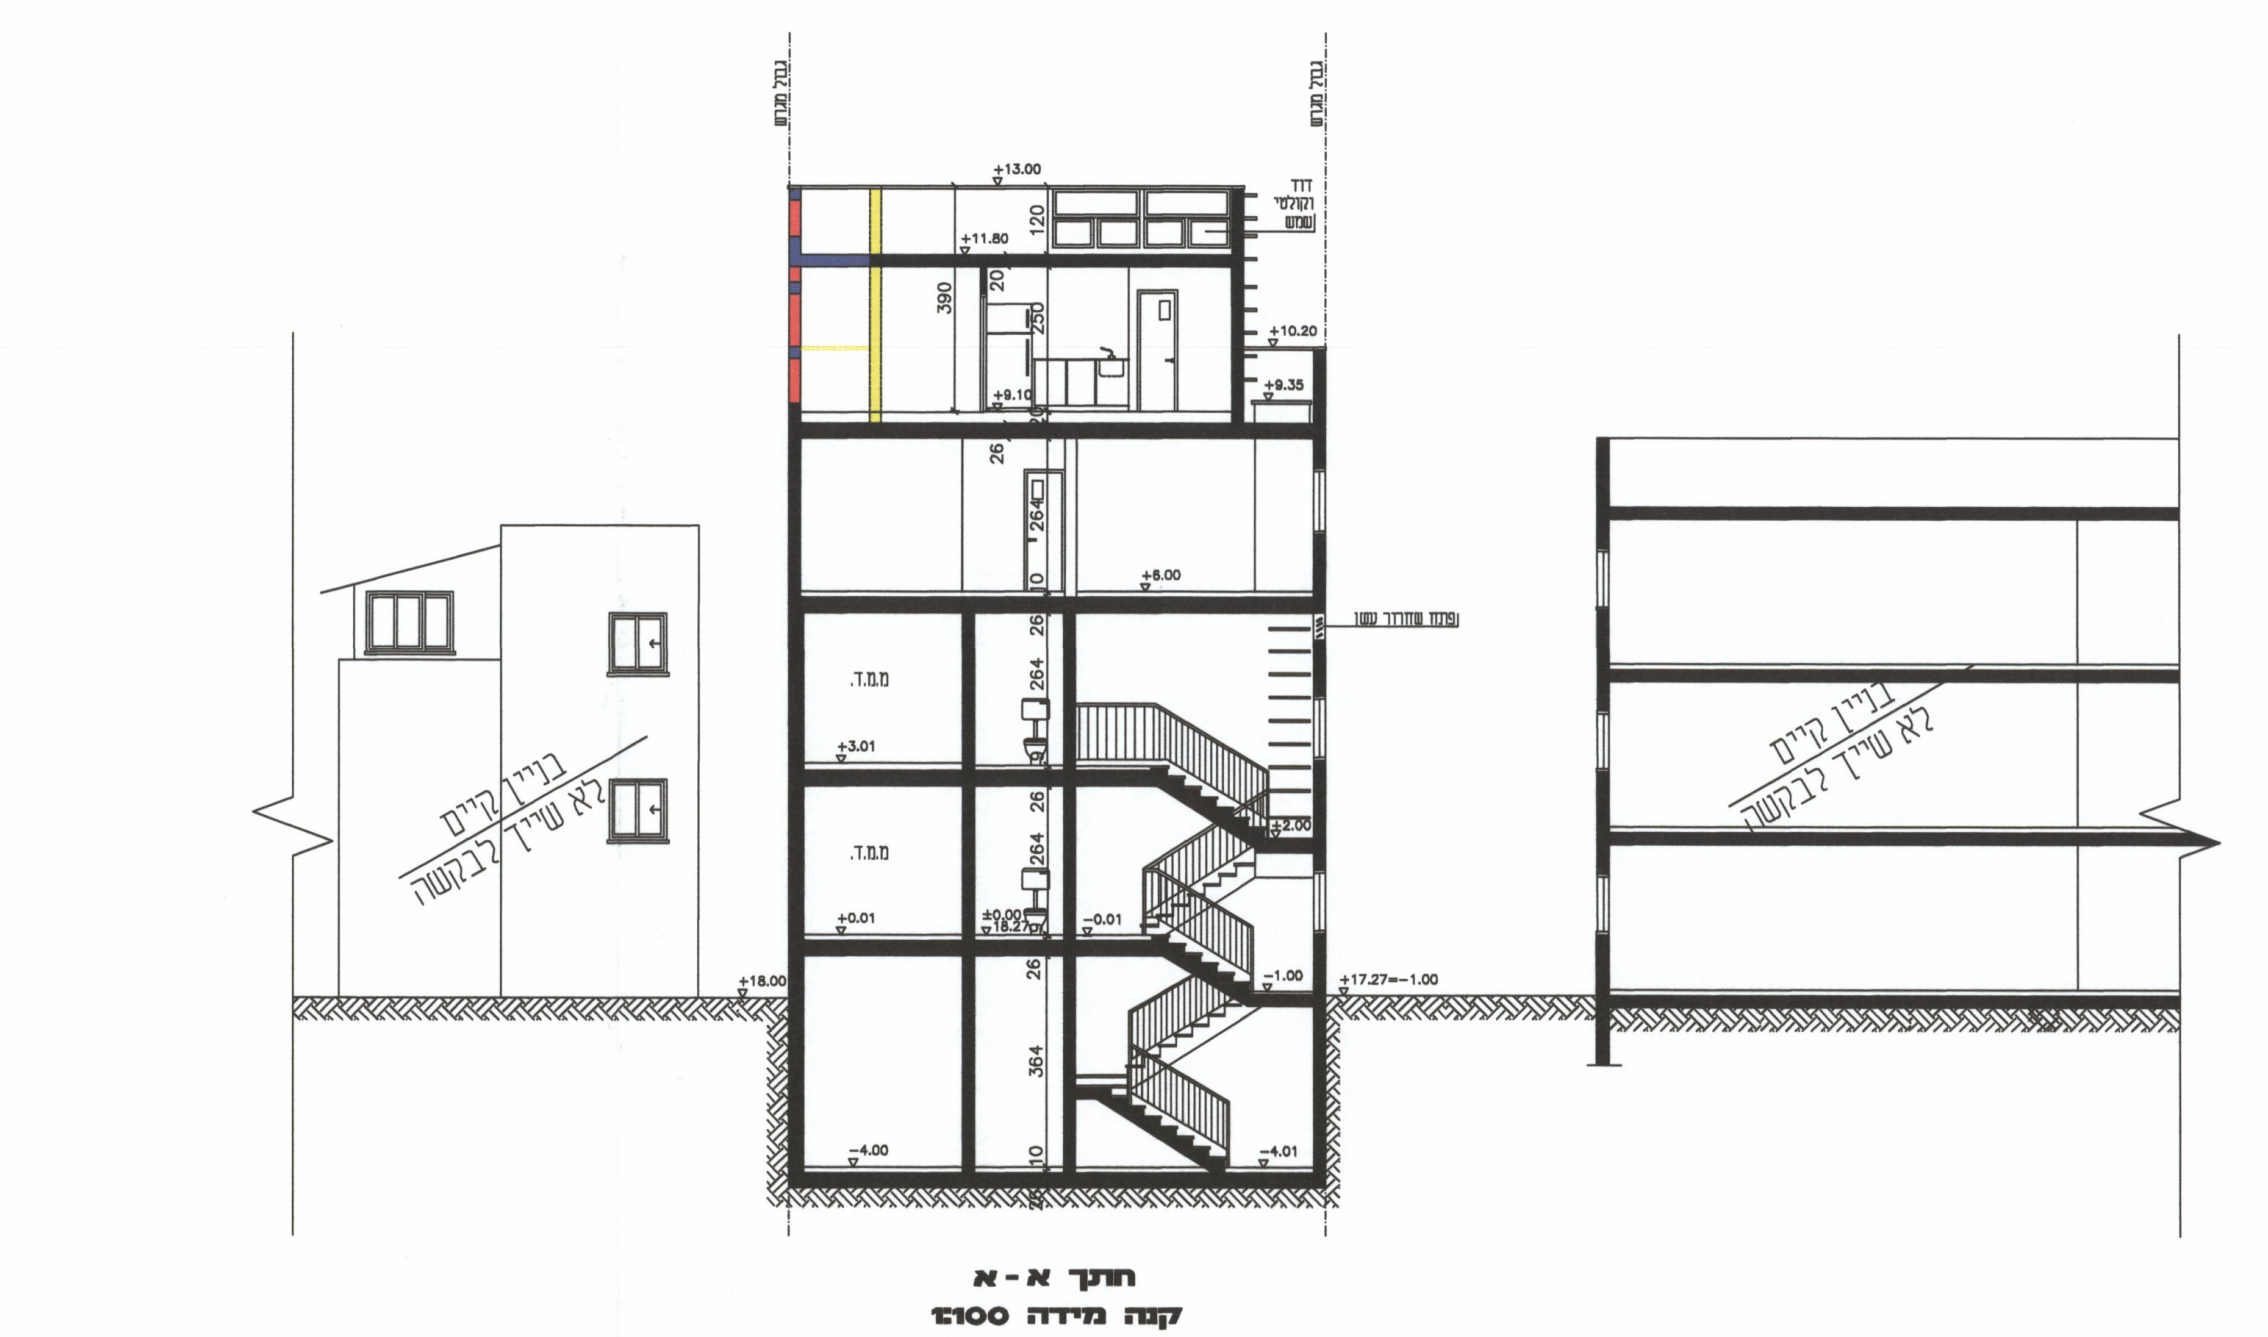

בניין קיים לא שייך לבקשה

חתך א - א
קנה מידה 1:100

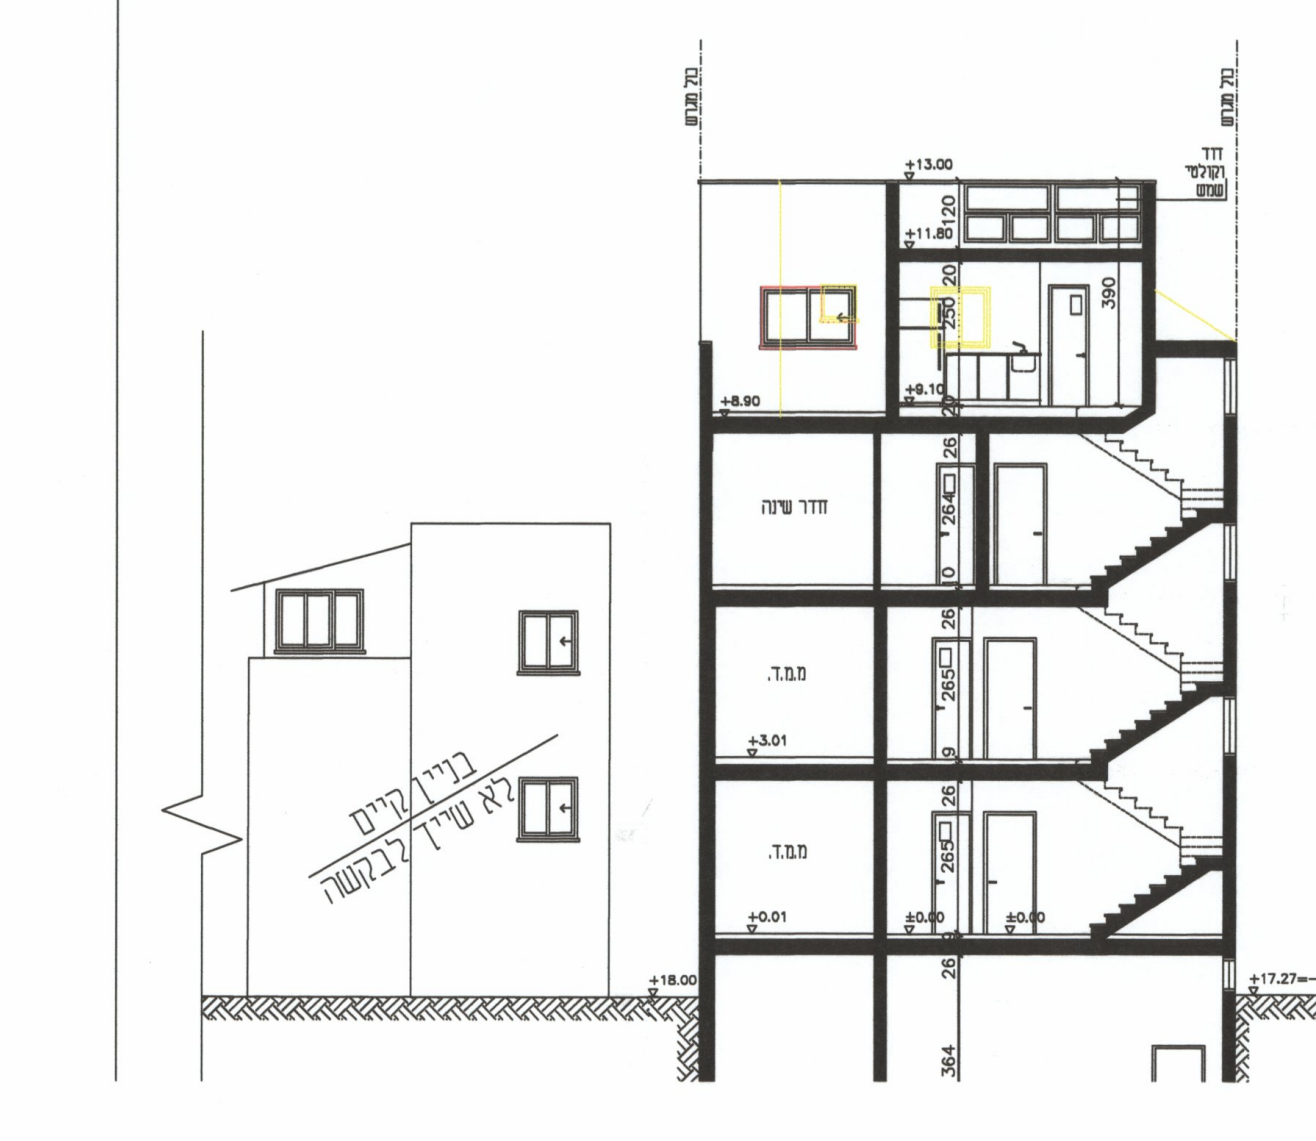

בניין קיים לא שייך לבקשה

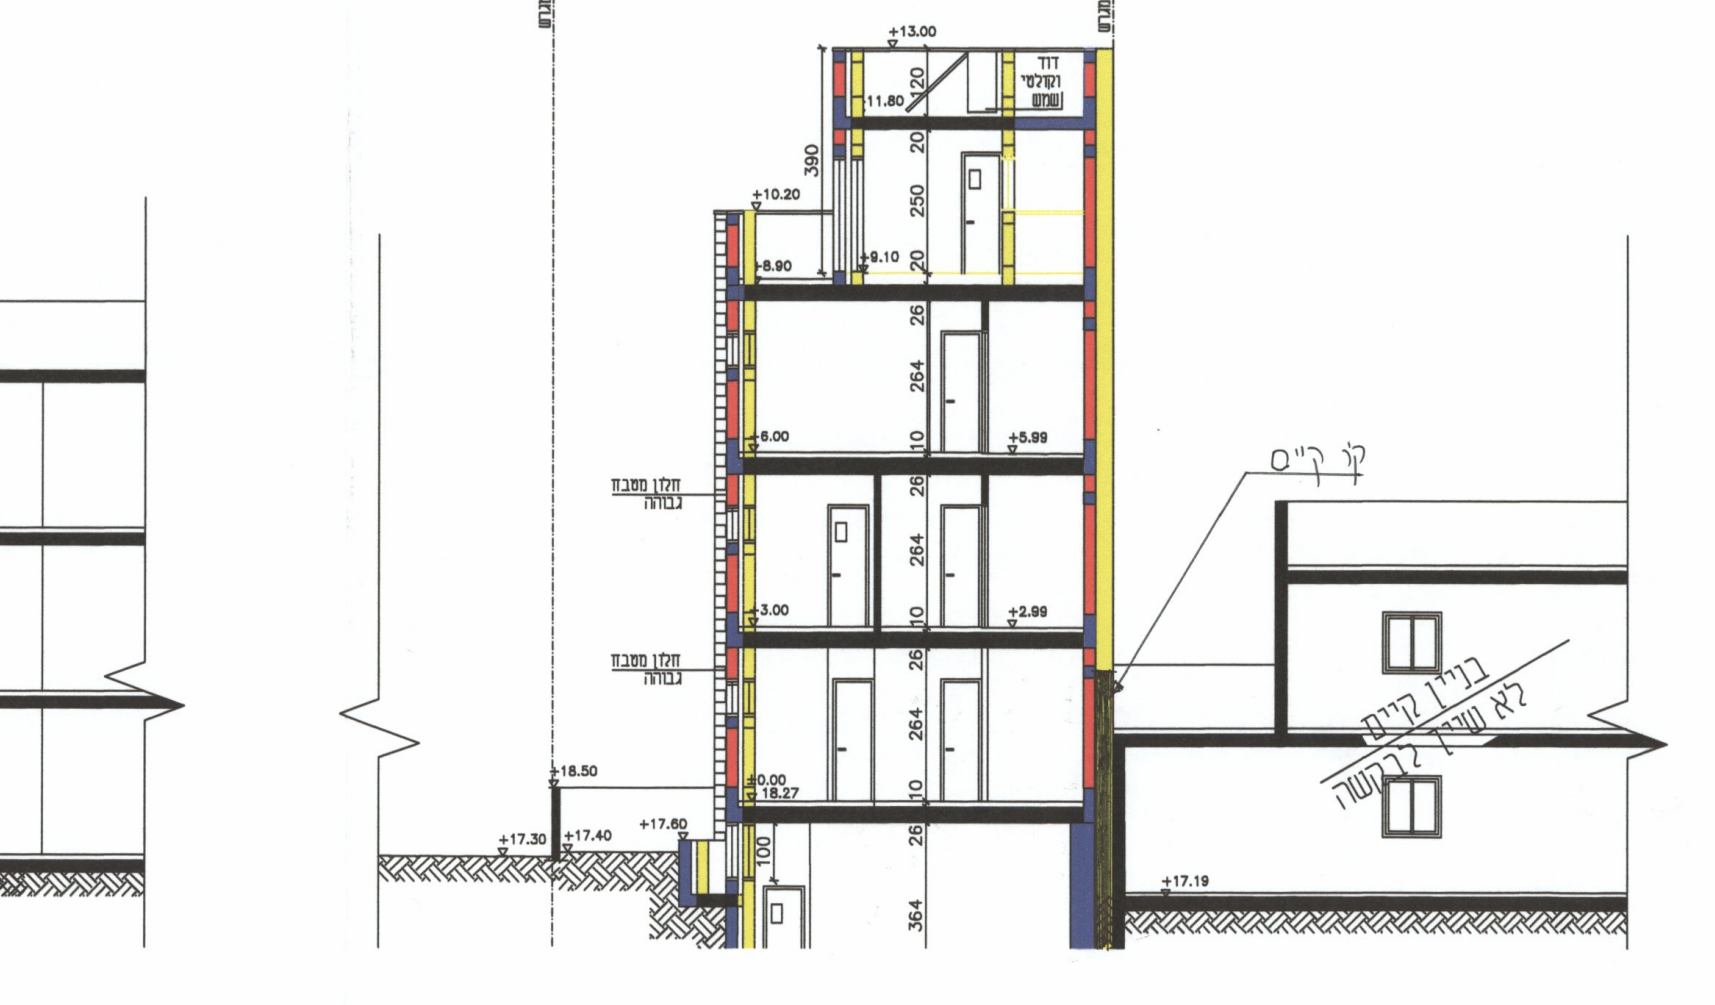

בניין קיים לא שייך לבקשה
ק' ר"ס

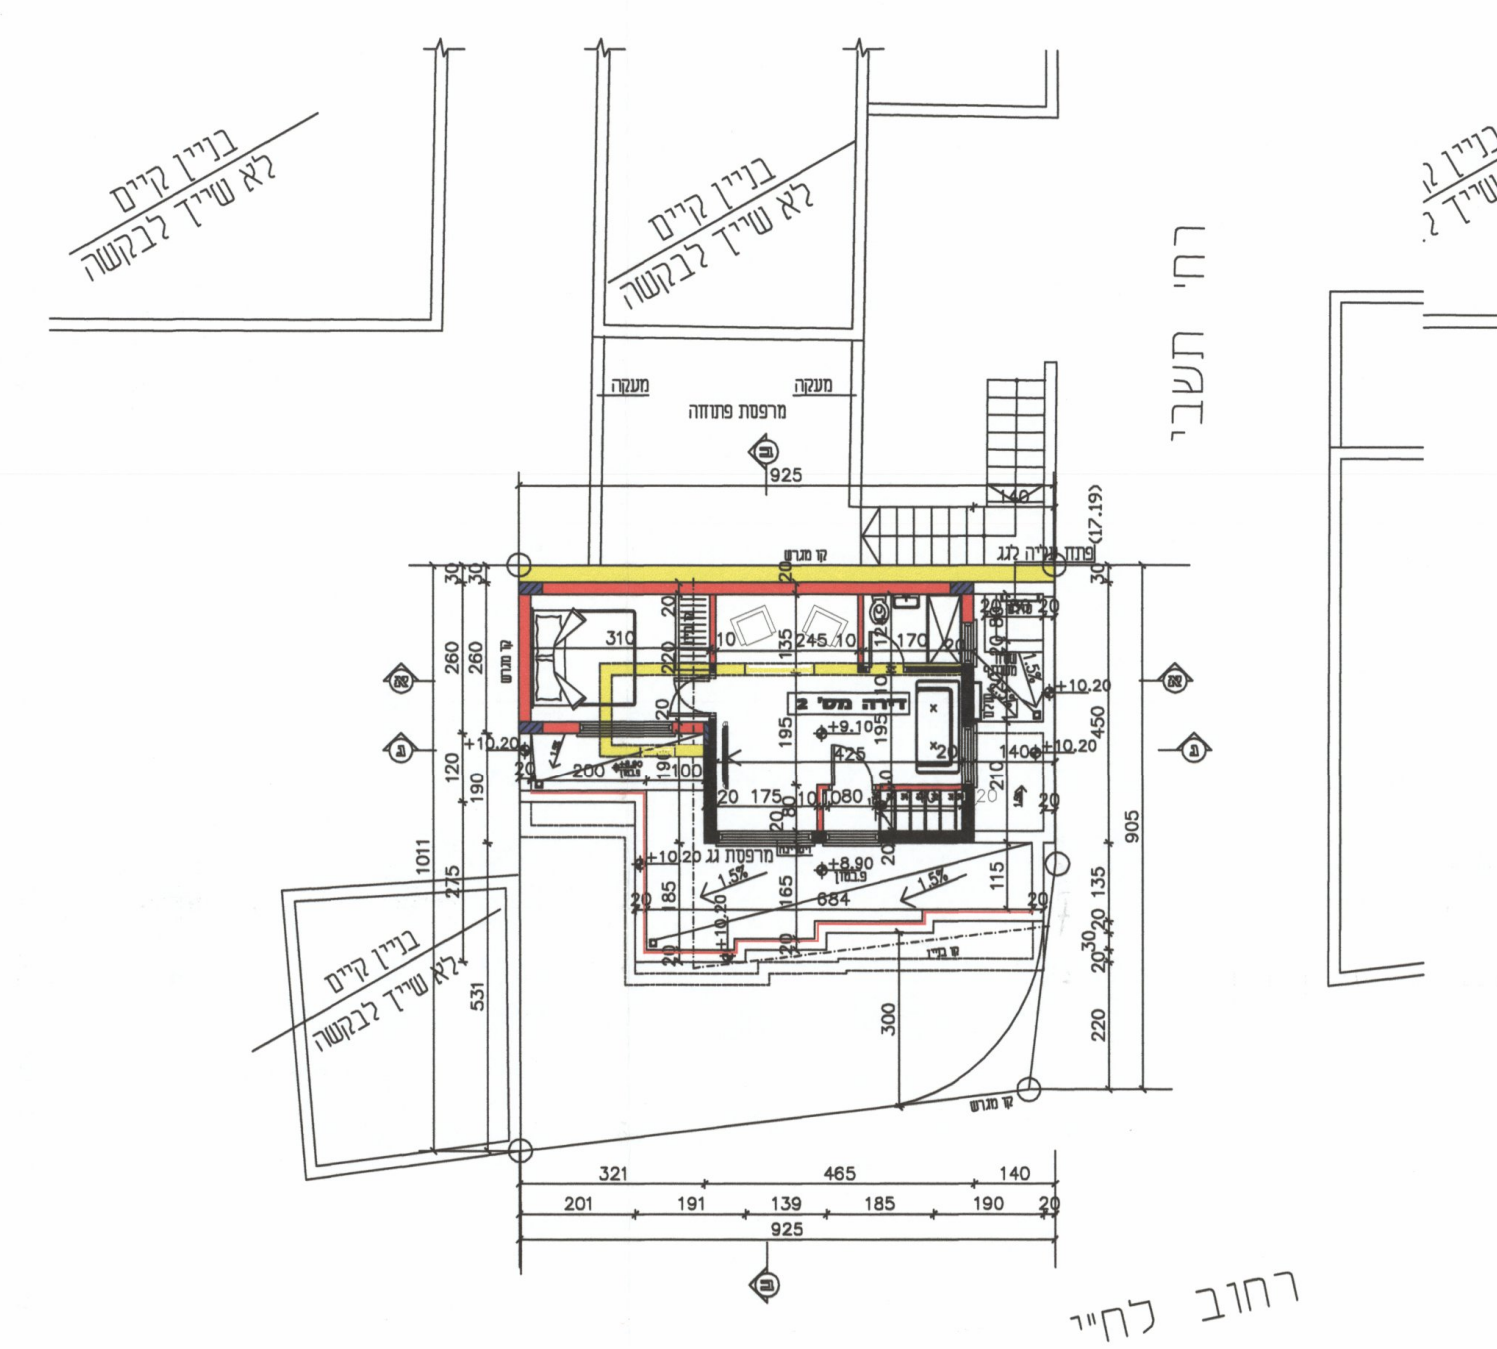

בניין קיים לא שייך לבקשה
רח' תשבי
רחוב לח"י

תכנית עליית גג
קנה מידה 1:100

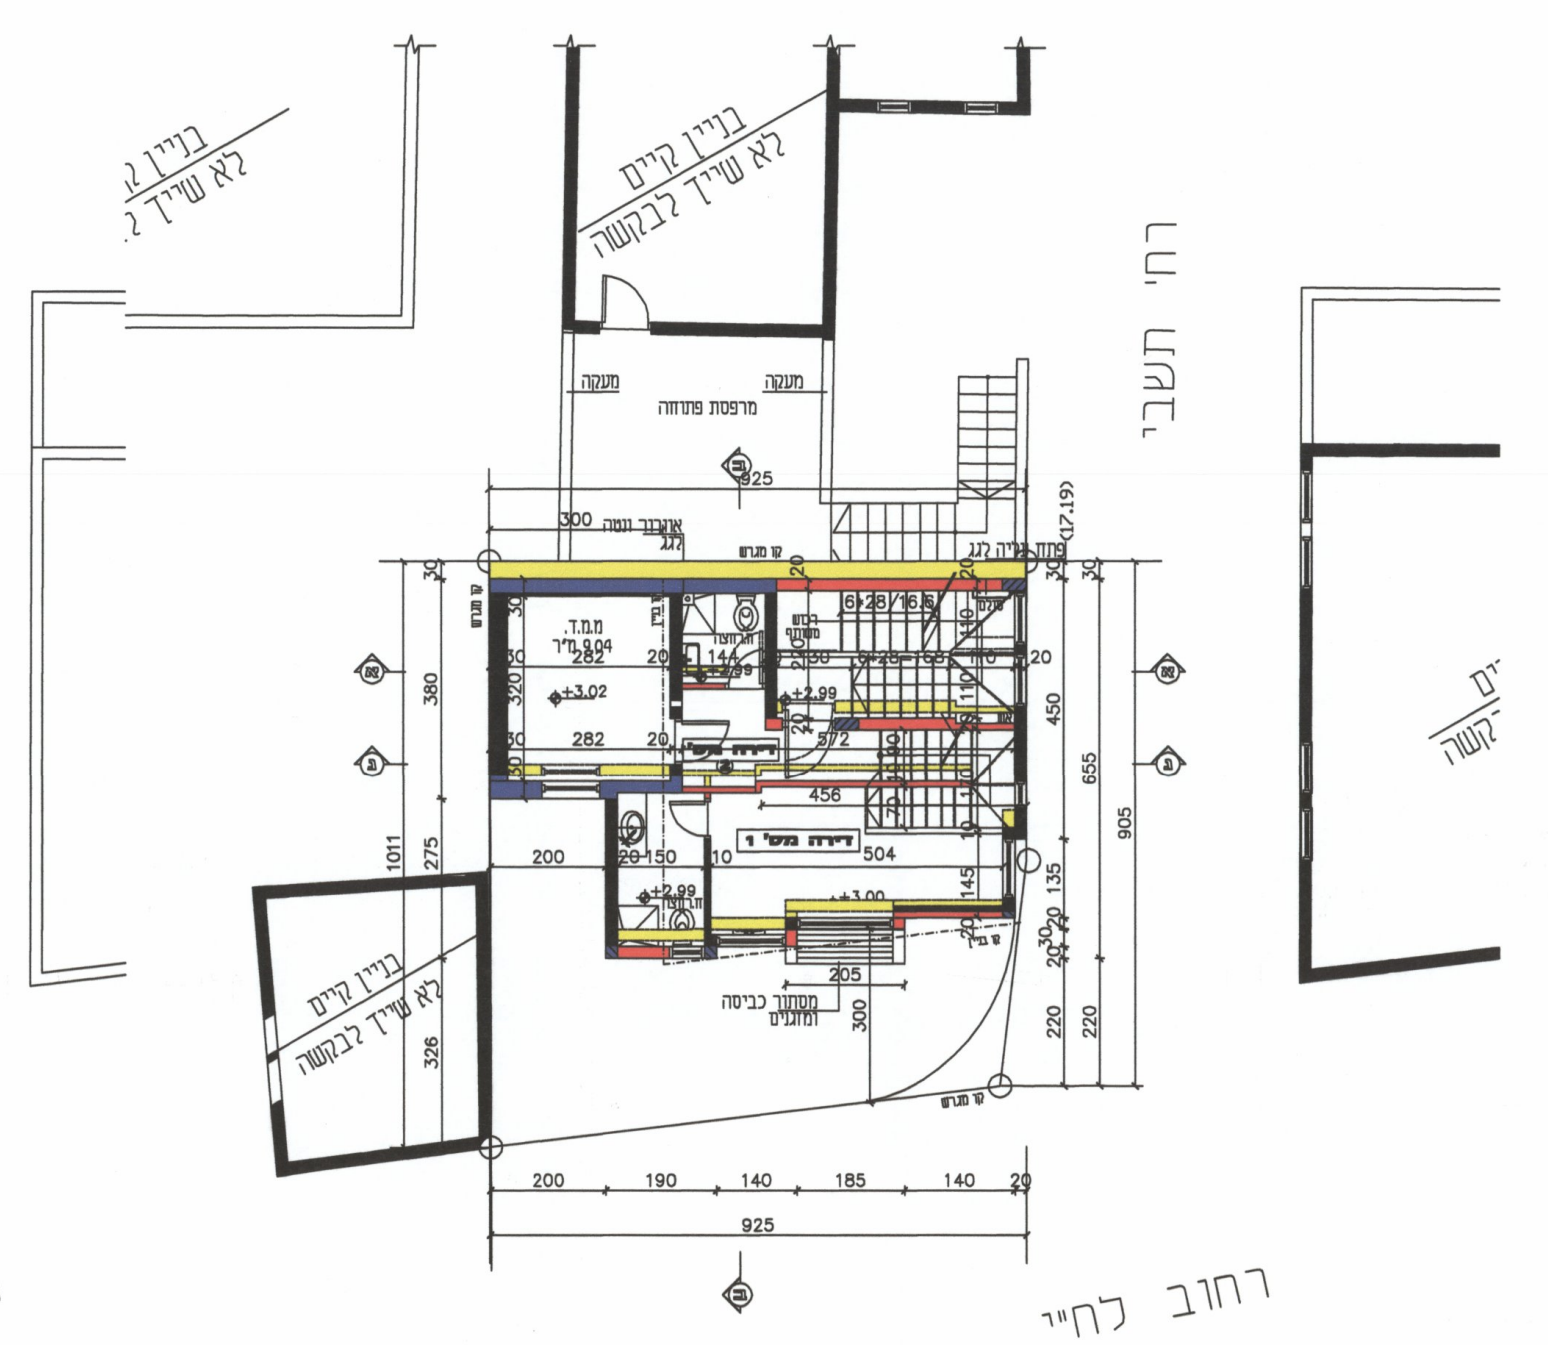

בניין קיים לא שייך לבקשה
רח' תשבי
רחוב לח"י

תכנית קומה ראשונה
קנה מידה 1:100

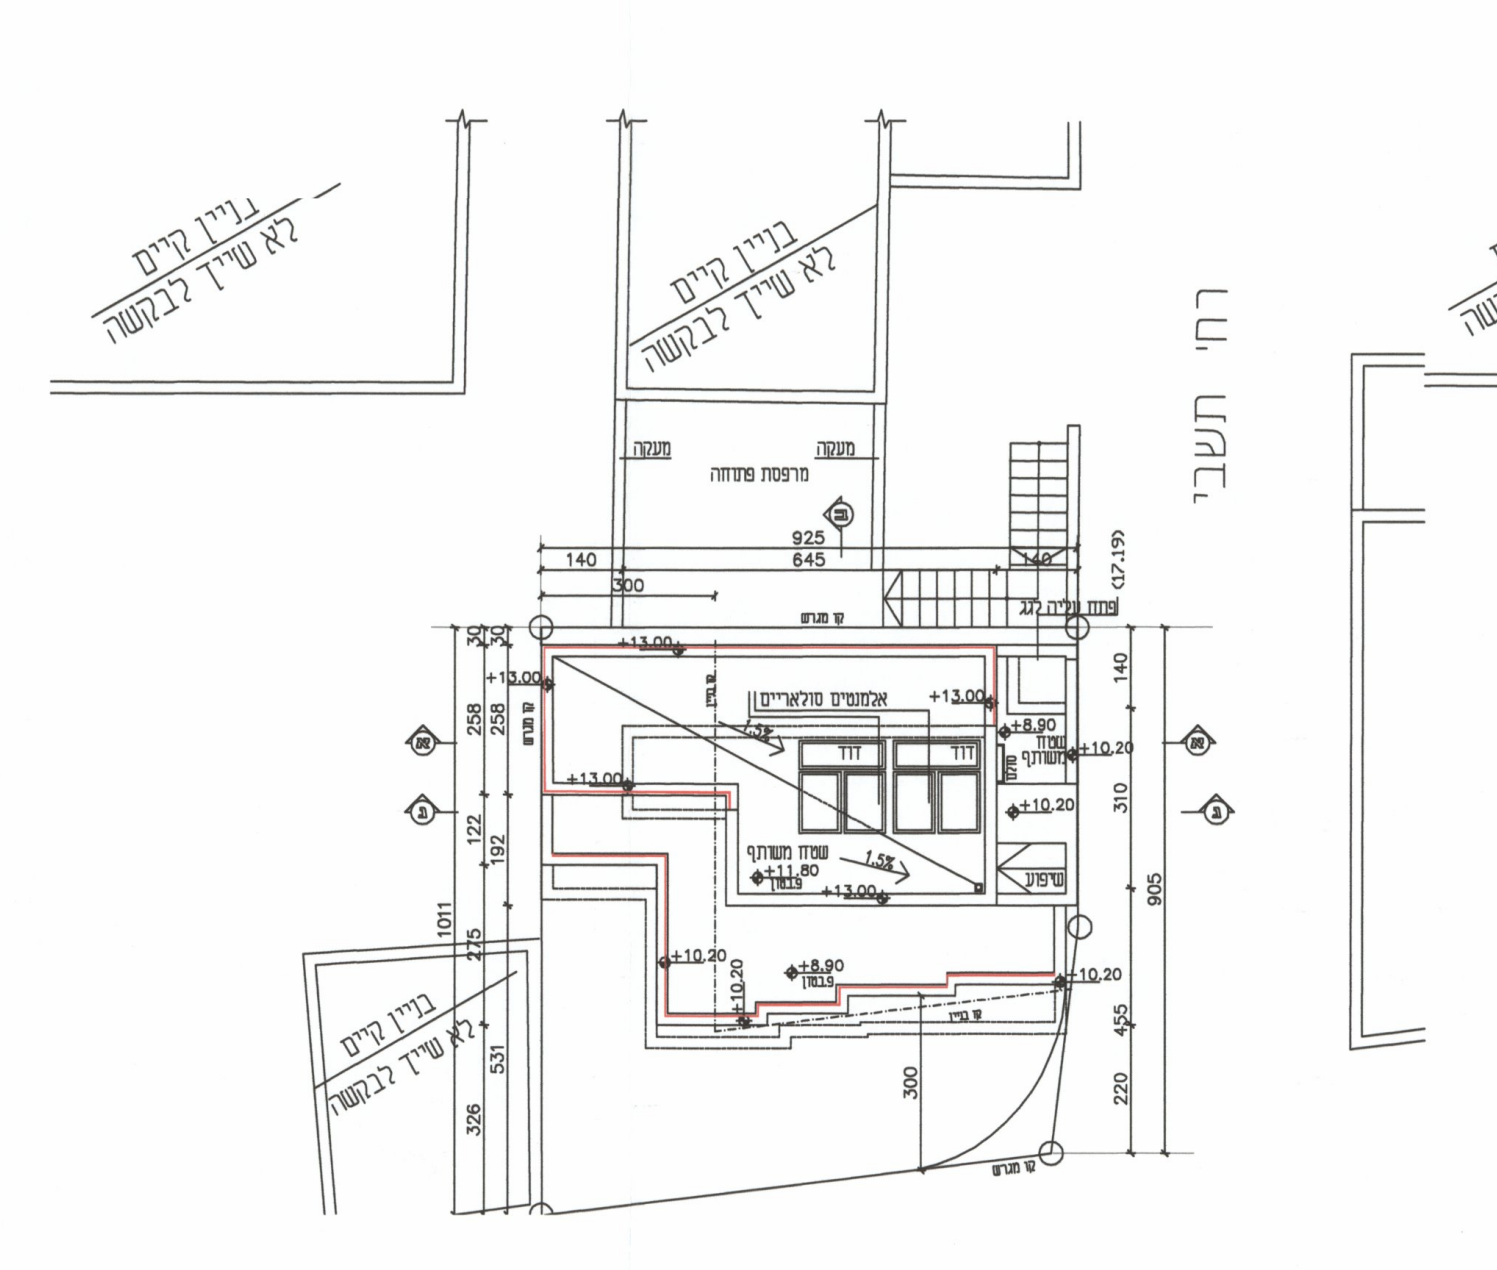

בניין קיים לא שייך לבקשה
רח' תשבי

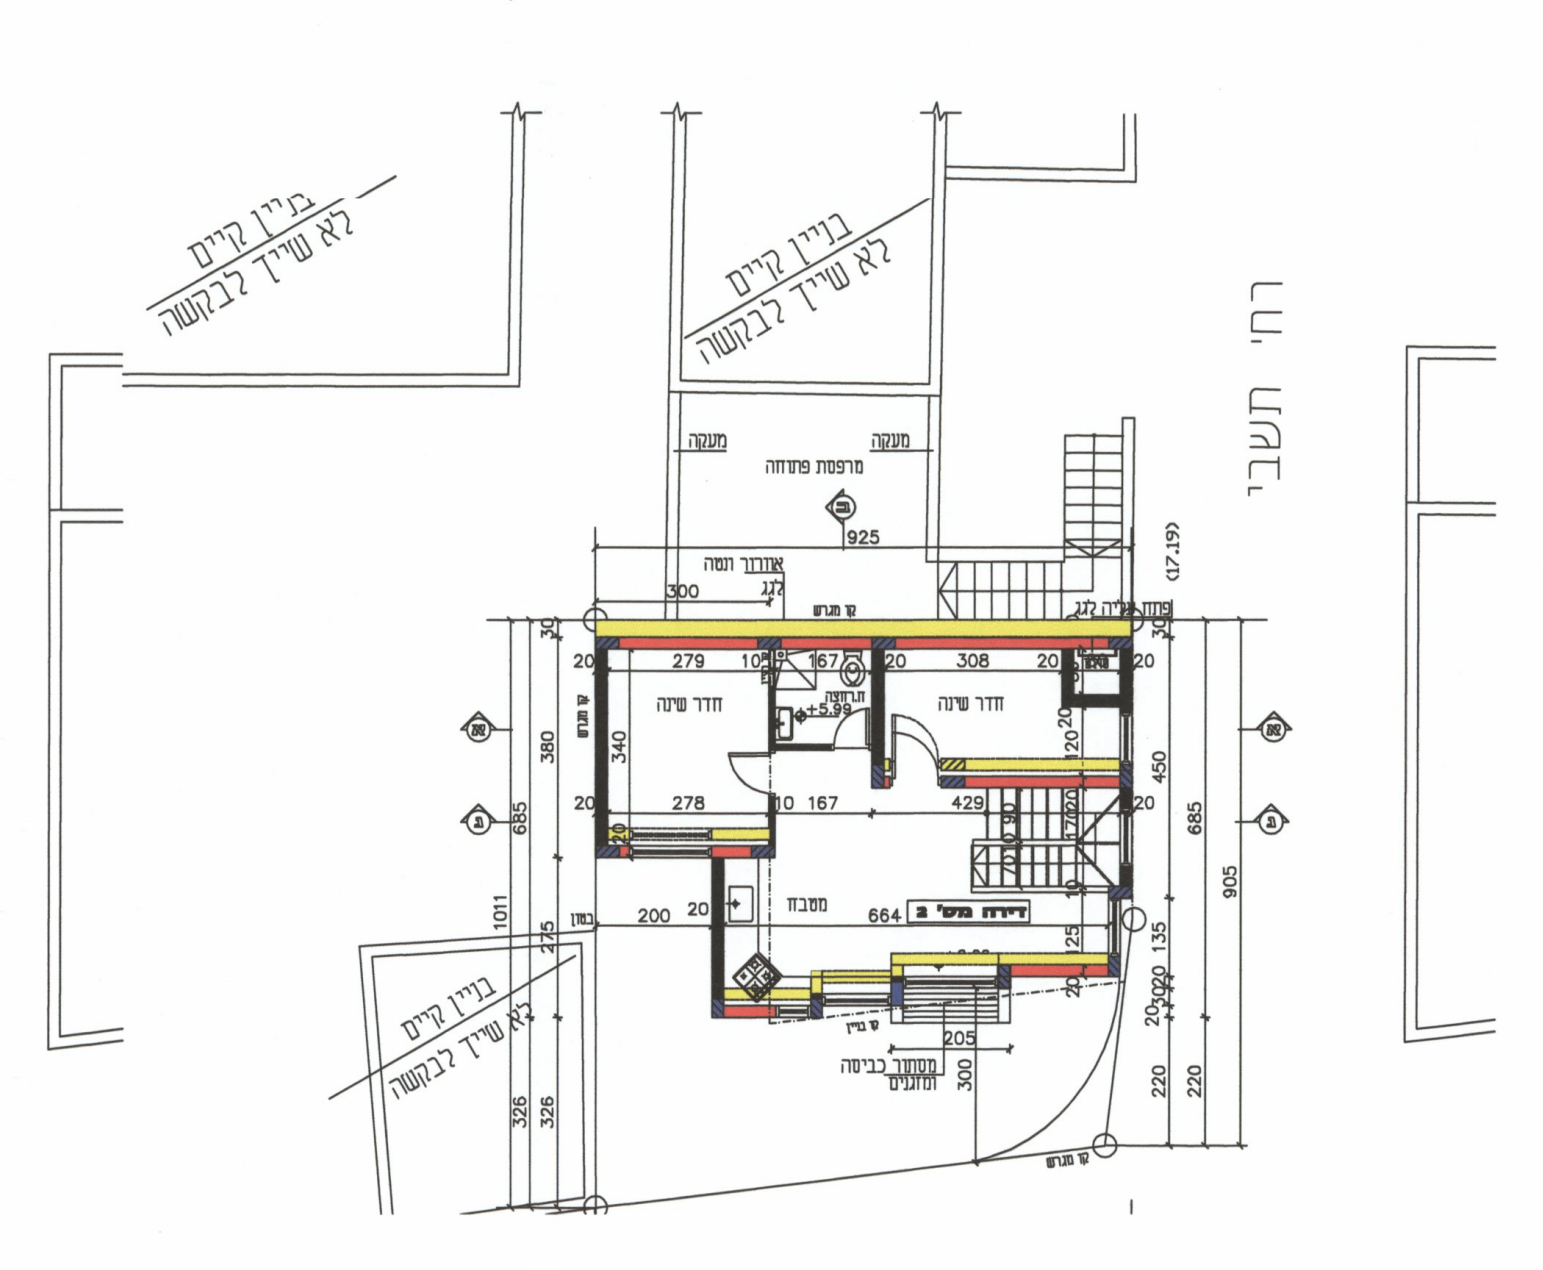

בניין קיים לא שייך לבקשה
רח' תשבי

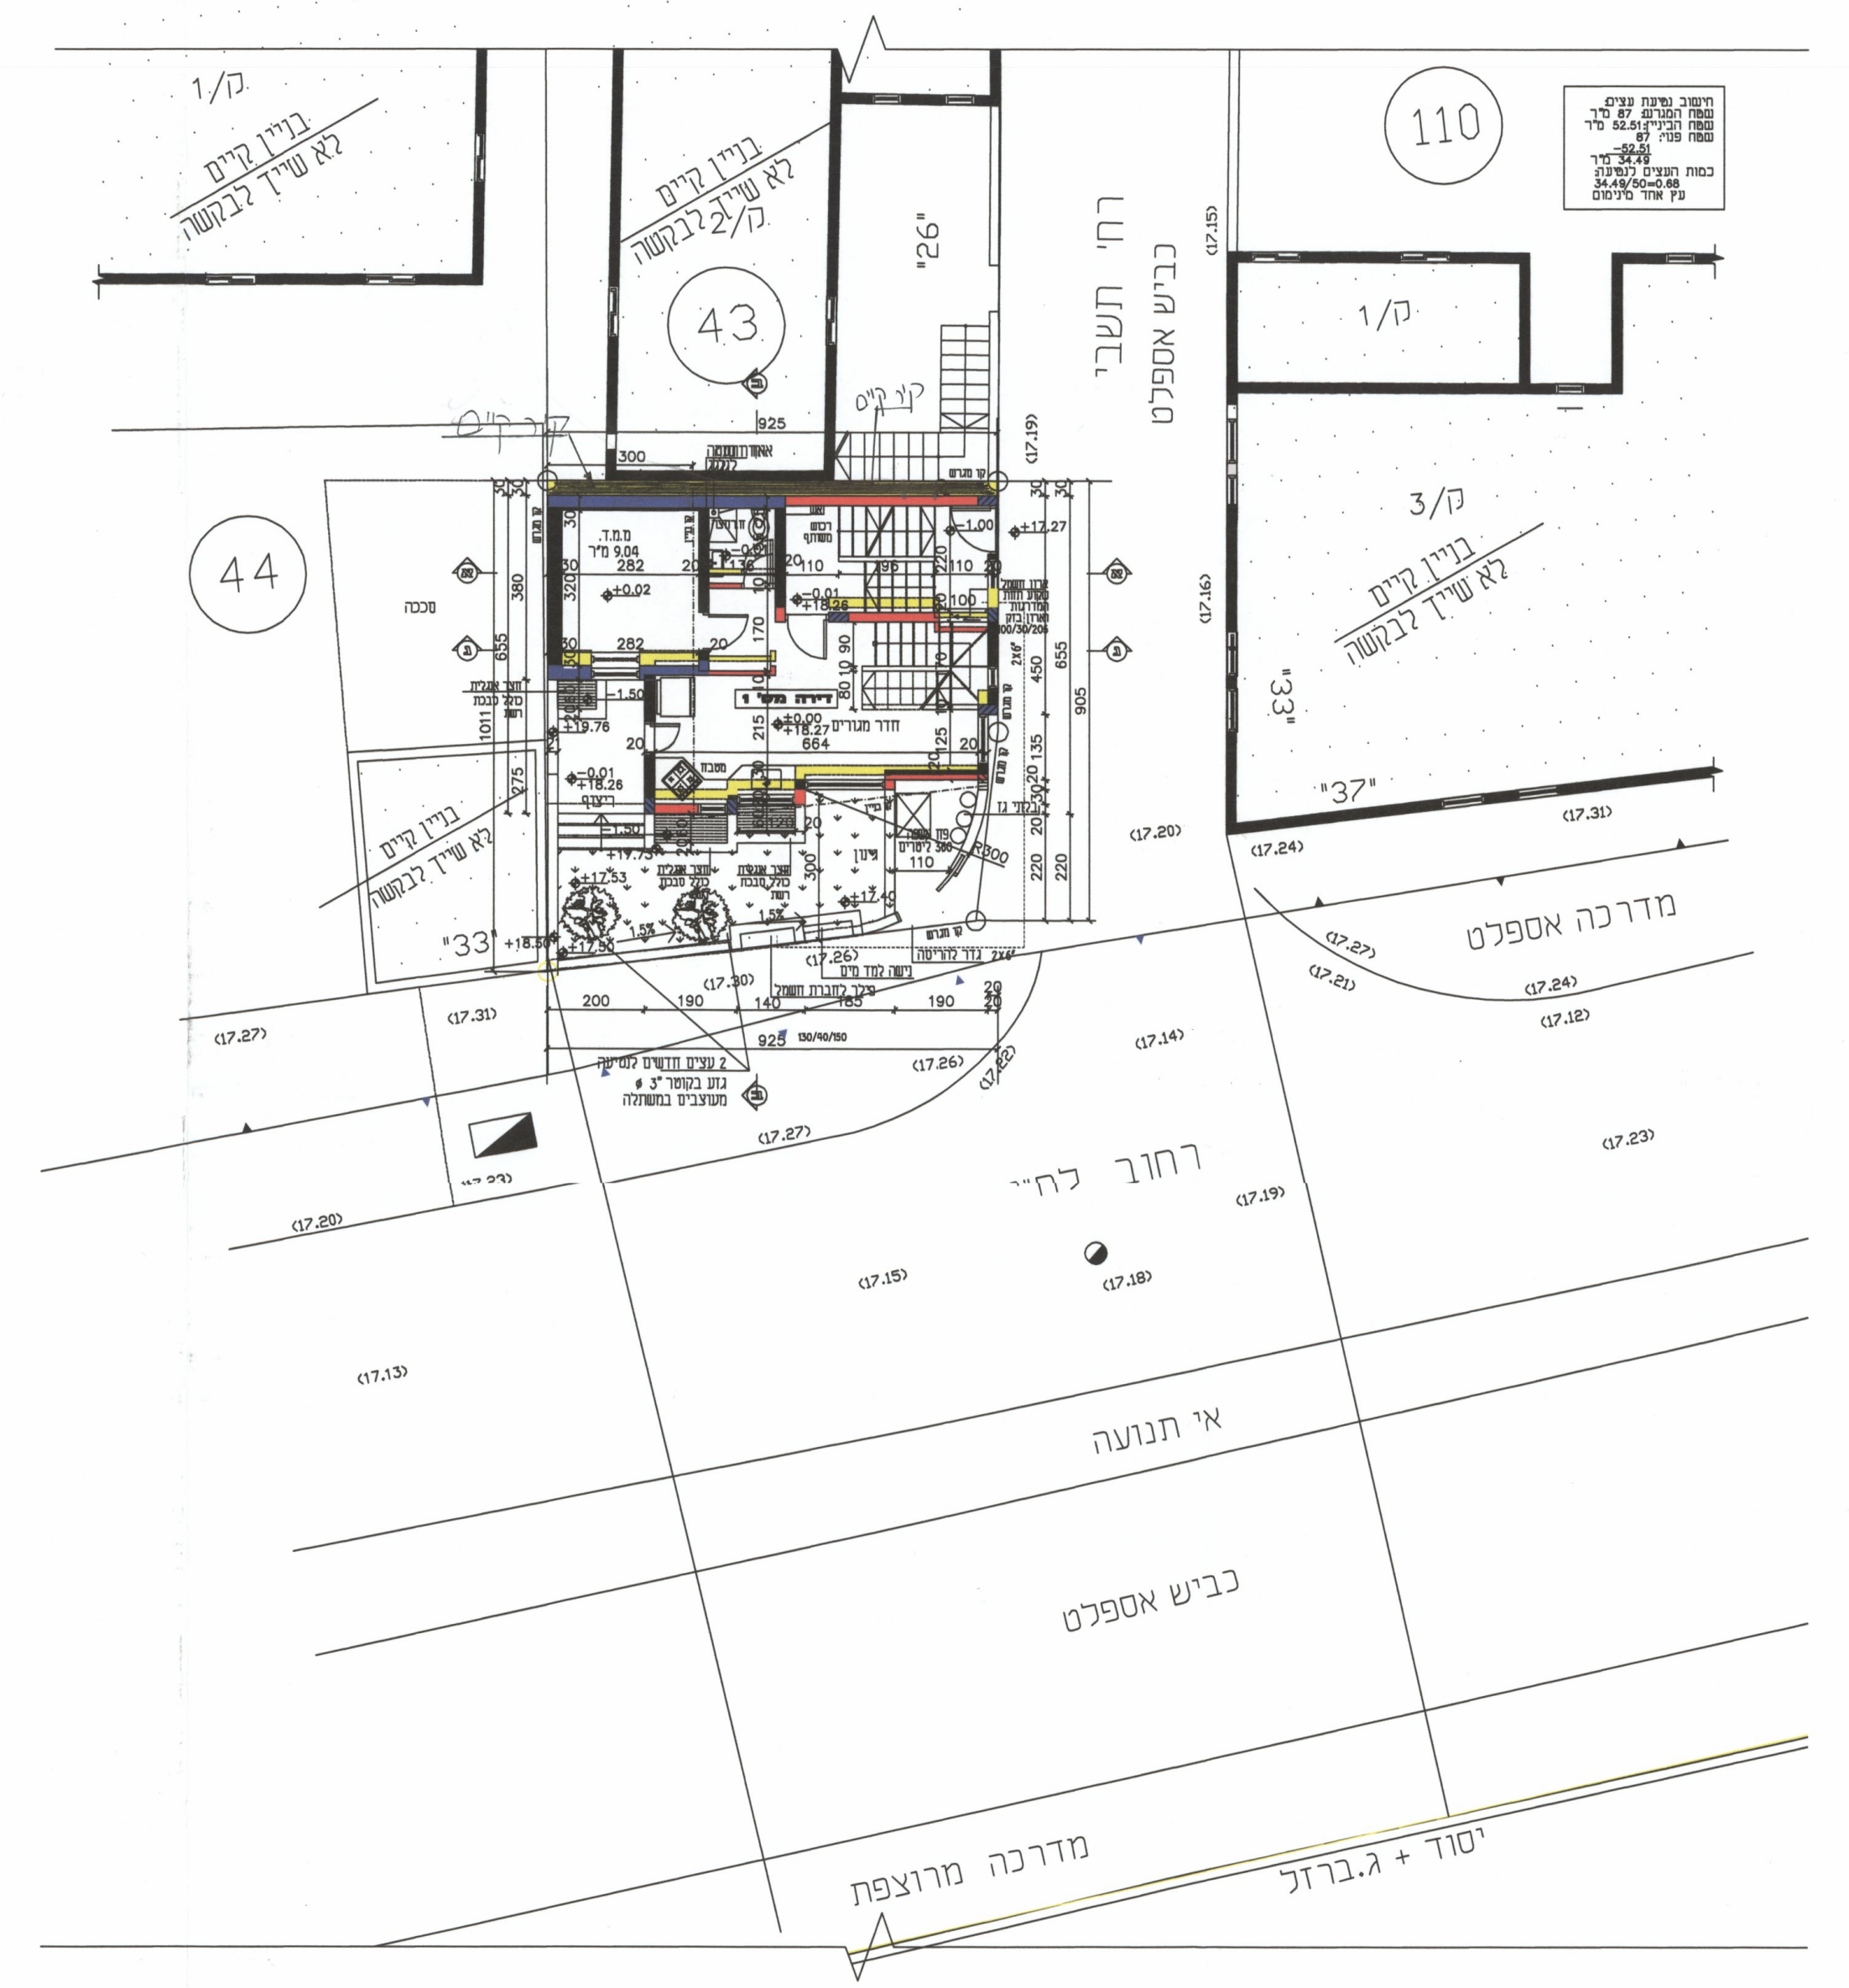

110
44
43
ק/1
ק/3
בניין קיים לא שייך לבקשה
רח' תשבי
כביש אספלט
מדרכה אספלט
רחוב לח"י
אי תנועה
מדרכה מרוצפת
יסוד + ג.ברזל

תכנית קומת קרקע

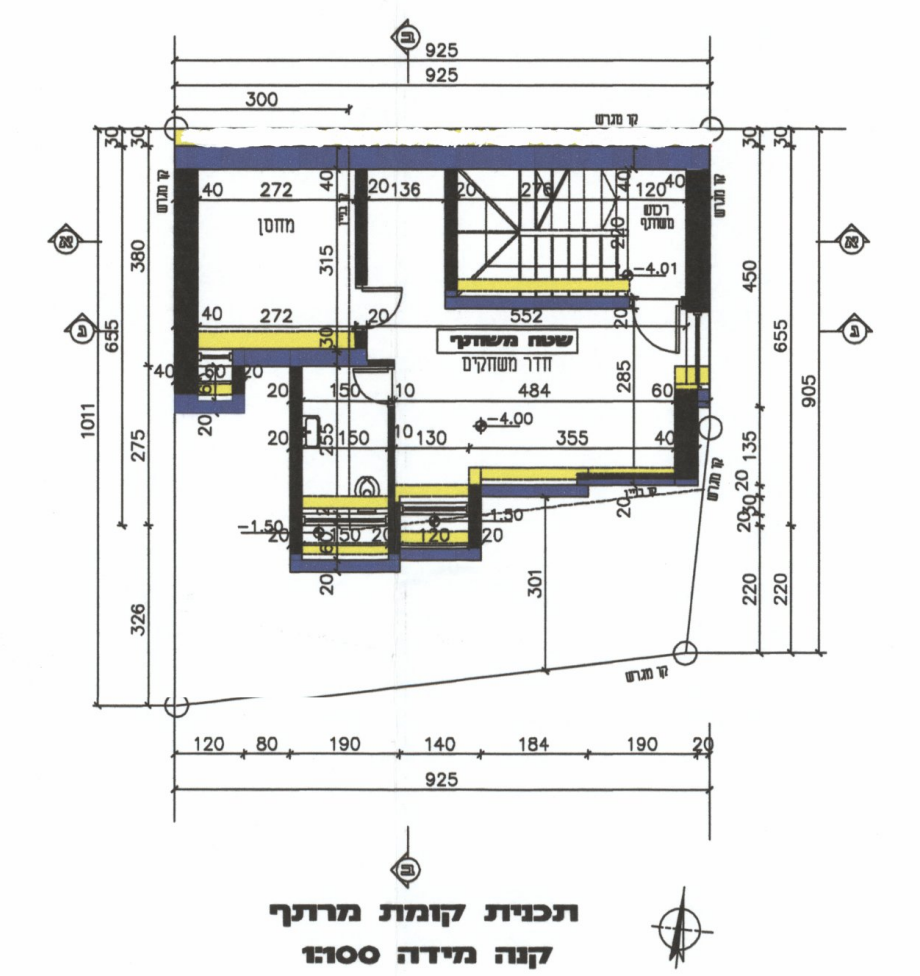

תכנית קומת מרתף
קנה מידה 1:100

חישוב שטחים

חישוב שטח קומה: קומת מרתף מוצע

שטח מסגרת	60.58	מ"ר	9.25*6.55=
שטח להורדה			
	5.50	מ"ר	① 2.00*2.75=
	1.98	מ"ר	② 3.95*0.50=
	0.69	מ"ר	③ (0.20*1.55)+(1.9*02)=
	0.28	מ"ר	④ 1.40*0.20=
סה"כ ההורדות	8.45	מ"ר	
סה"כ השטח	52.13	מ"ר	

תכנית קומת מרתף
קנה מידה 1:200

חישוב שטח קומה: קומה שניה מוצע

שטח מסגרת	60.58	מ"ר	9.25*6.55=
שטח להורדה			
	5.50	מ"ר	① 2.75*2.00=
	1.98	מ"ר	② 3.95*0.50=
	0.69	מ"ר	③ (0.20*1.55)+(1.9*02)=
	0.28	מ"ר	④ 1.40*0.20=
	0.64	מ"ר	⑤ 0.80*0.80=
סה"כ ההורדות	9.09	מ"ר	
סה"כ השטח	51.49	מ"ר	

תכנית קומה שניה
קנה מידה 1:200

חישוב שטח קומה: קומת קרקע מוצע

שטח מסגרת	60.58	מ"ר	9.25*6.55=
שטח להורדה	5.50	מ"ר	① 2.00*2.75=
	1.98	מ"ר	② 3.95*0.50=
	0.69	מ"ר	③ (0.20*1.55)+(1.9*02)=
	0.28	מ"ר	④ 1.40*0.20=
שטח מ.מ.ד נטו	9.04	מ"ר	⑤ 2.74*3.30=
שטח קירות	3.08	מ"ר	12.12-9.04=
שטח מ.מ.ד ברוטו	12.12	מ"ר	9.04+3.08=
שטח מ.מ.ד להורדה	12	מ"ר מקס'	
סה"כ ההורדות	20.45	מ"ר	
סה"כ השטח	40.13	מ"ר	

תכנית קומת קרקע
קנה מידה 1:200

חישוב שטח קומה: קומת גג מוצע

	8.32	מ"ר	① 3.2*2.6=
	20.92	מ"ר	② 4.65*4.5=
שטח חדר על הגג	29.24	מ"ר מקס'	
שטח מסגרת	60.58	מ"ר	9.25*6.55=
שטח להורדה			
	5.5	מ"ר	③ 2.0*2.75=
	0.28	מ"ר	④ 0.20*1.4=
	1.98	מ"ר	⑤ 3.95*0.5=
	0.69	מ"ר	⑥ (0.2*1.55)+(1.9*0.2)=
שטח משותף	6.30	מ"ר	⑦ 1.40*4.50=
מרפסת הגג	16.59	מ"ר	60.58-43.99=

תכנית חדר על הגג
קנה מידה 1:200

סה"כ ההורדות 14.75 מ"ר
סה"כ חדר על הגג 29.24 מ"ר
סה"כ מרפסת הגג 16.59 מ"ר
סה"כ שטח (חדר+ מרפסת) 29.24+16.59=45.83 מ"ר
היחס בין החדר על הגג לשטח הגג 29.24/45.3=64.54%

חישוב שטח קומה : קומה ראשונה מוצע

שטח מסגרת	60.58	מ"ר	9.25*6.55=
שטח להורדה			
	5.50	מ"ר	① 2.75*2.00=
	1.98	מ"ר	② 3.95*0.50=
	0.69	מ"ר	③ (0.20*1.55)+(1.9*02)=
	0.28	מ"ר	④ 1.40*0.20=
שטח מ.מ.ד נטו	9.04	מ"ר	⑤ 2.74*3.30=
שטח קירות	3.08	מ"ר	12.12-9.04=
שטח מ.מ.ד ברוטו	12.12	מ"ר	9.04+3.08=
שטח מ.מ.ד להורדה	12	מ"ר מקס'	
סה"כ ההורדות	20.45	מ"ר	
סה"כ השטח	40.13	מ"ר	

תכנית קומה ראשונה
קנה מידה 1:200

התפלגות הדירות:

דירה מס' 2 ... 3.55*4.56= מ"ר 16.19

טבלת התפלגות דירות:

מס'	שטח הדירה ללא מ.מ.ד	מ.מ.ד	סה"כ	חדר על הגג	סה"כ	מרפסות
1)	18.12+40.13= 58.25	12	71.25	—	71.25	—
2)	22.01+51.49=	12	85.50	29.24	114.74	16.59

תל-אביב
גוש : 6135
חלקה : 43(חלק)
כתובת : רח' לח"י 35
הוכן עבור : חילבה ישעיהו
מטרת המדידה : הגדרת מגרש משני עפ"י תב"ע 2215

מפה טופוגרפית
1 : 250

שם הבעלים כרשום בנסח טאבו+מס' ת.ז : מועלם טל 032021289

שטח לפי נסח :
שטח החלקה כולה : 3.575 ד.מ.
בעלות בחלקים(כרשום בנסח טאבו) : מועלם טל 174/7150

בעלות במ"ר : 87
שטח מדוד(מ"ר) : 87

שטח מגרש משני : 0.87 ד.מ.
שטח לגריעה : ד.מ.

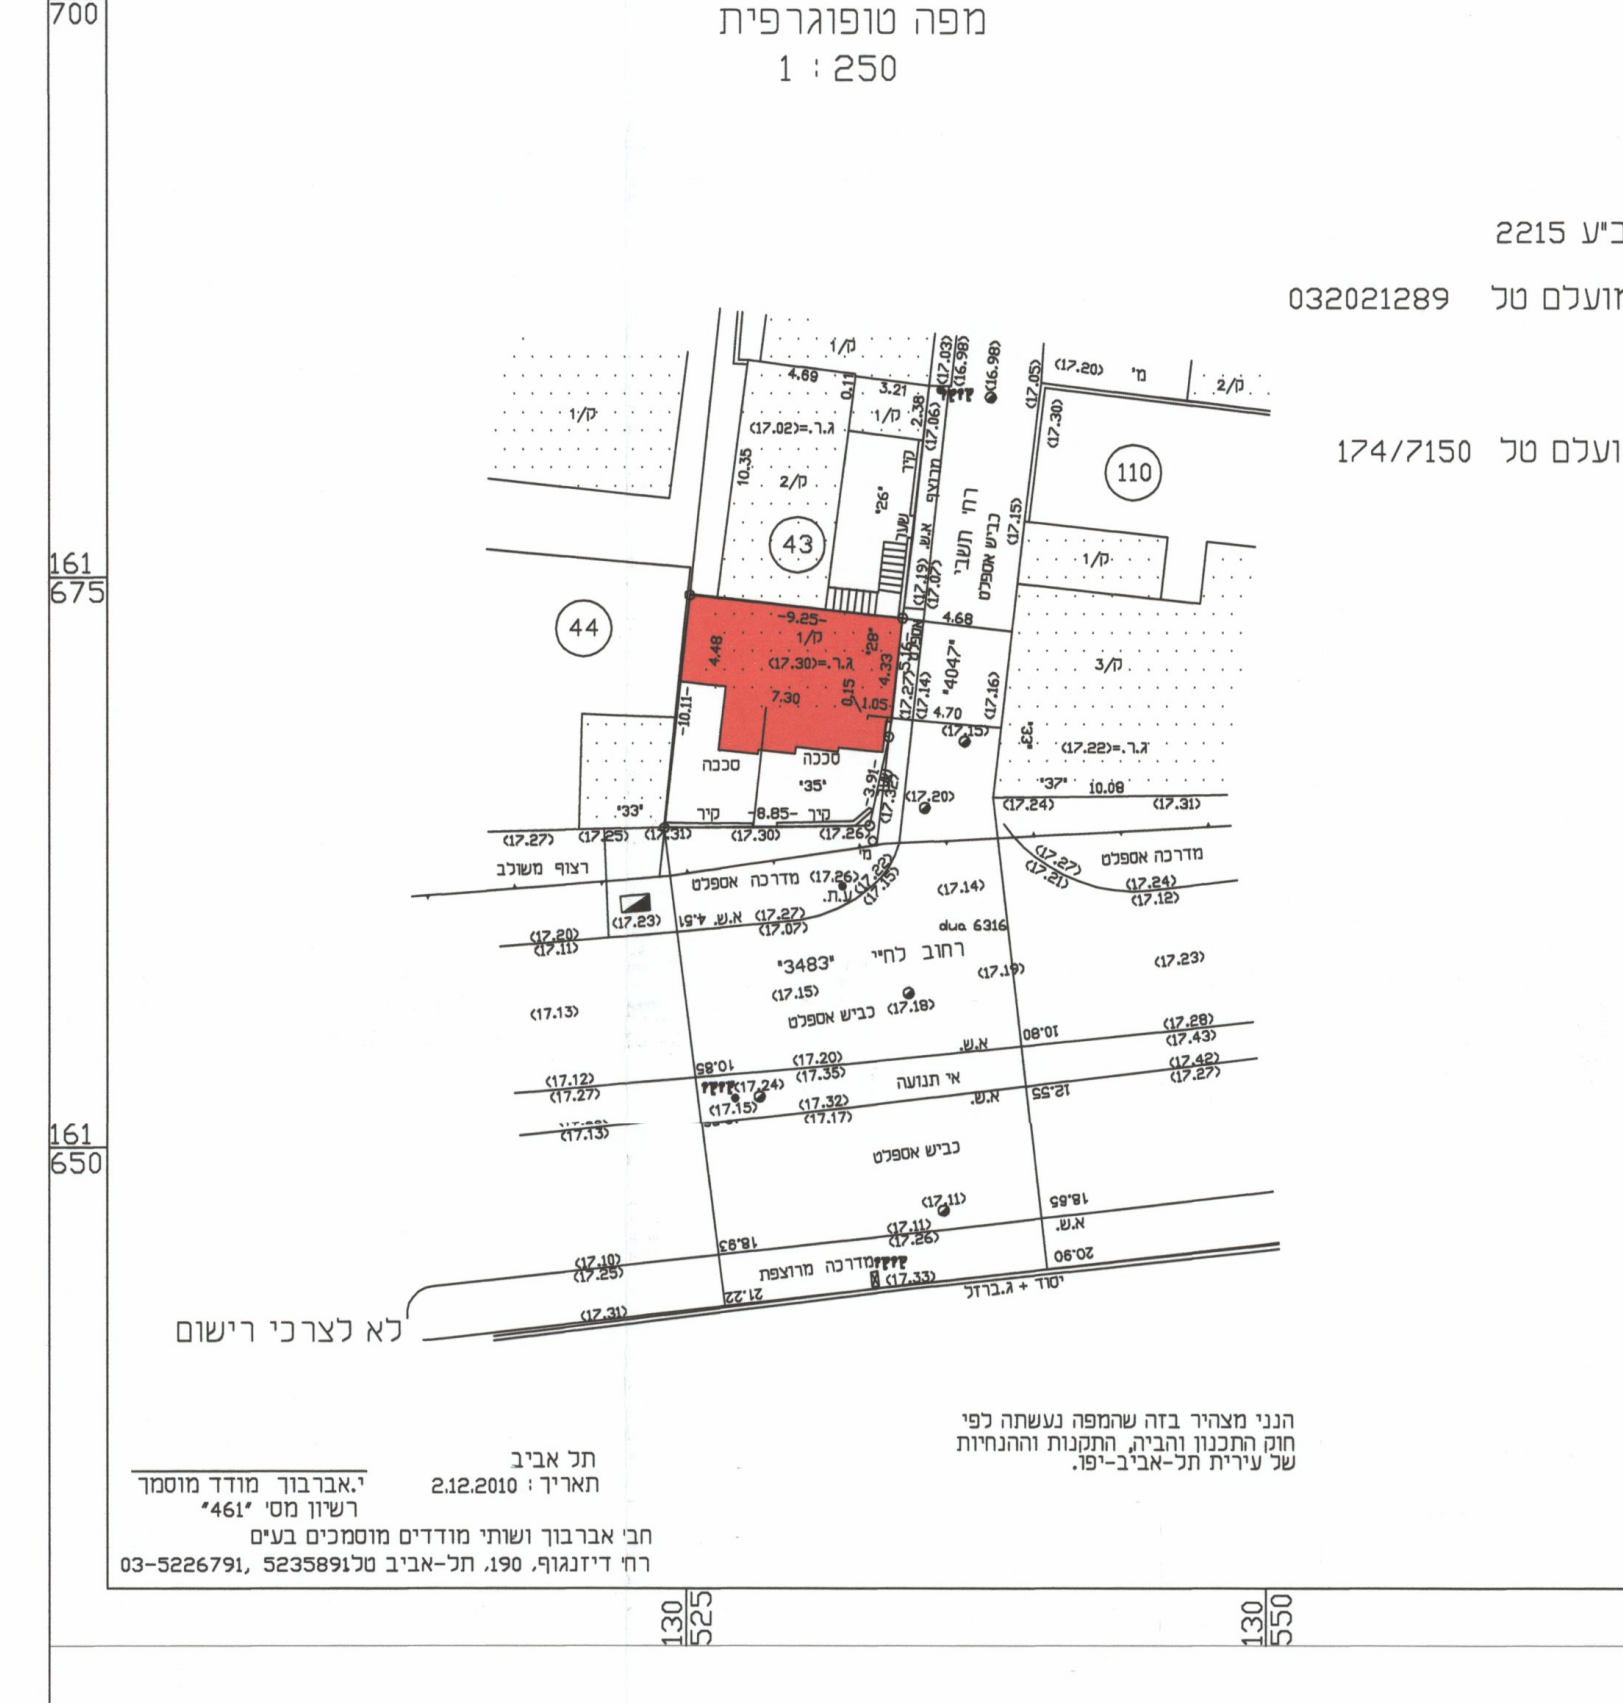

161 700
130 525
130 550
130 575
161 675
161 650
110
43
44
ק/1
ק/2
ק/3
רח' תשבי
כביש אספלט
מדרכה אספלט
רחוב לח"י
אי תנועה
מדרכה מרוצפת
יסוד + ג.ברזל
לא לצרכי רישום

תרשים הסביבה 1:1250

רח' לח"י
"3843"
"4046"
"4047"
35
110

הנני מצהיר בזה שהמפה נעשתה לפי
חוק התכנון והבניה, התקנות וההנחיות
של עירית תל-אביב-יפו.

תל אביב
תאריך : 2.12.2010
י.אברבוך מודד מוסמך
רשיון מס' "461"
חב' אברבוך ושותי מודדים מוסמכים בעים
רח' דיזנגוף, 190, תל-אביב טל5235891, 03-5226791

הערות:
1. המספרים בסוגריים מציינים גבהים.
2. הגבהים מבוססים על נ.ק. עירונית מס' 187 שגובהה 17.549 מ'.

נסרק

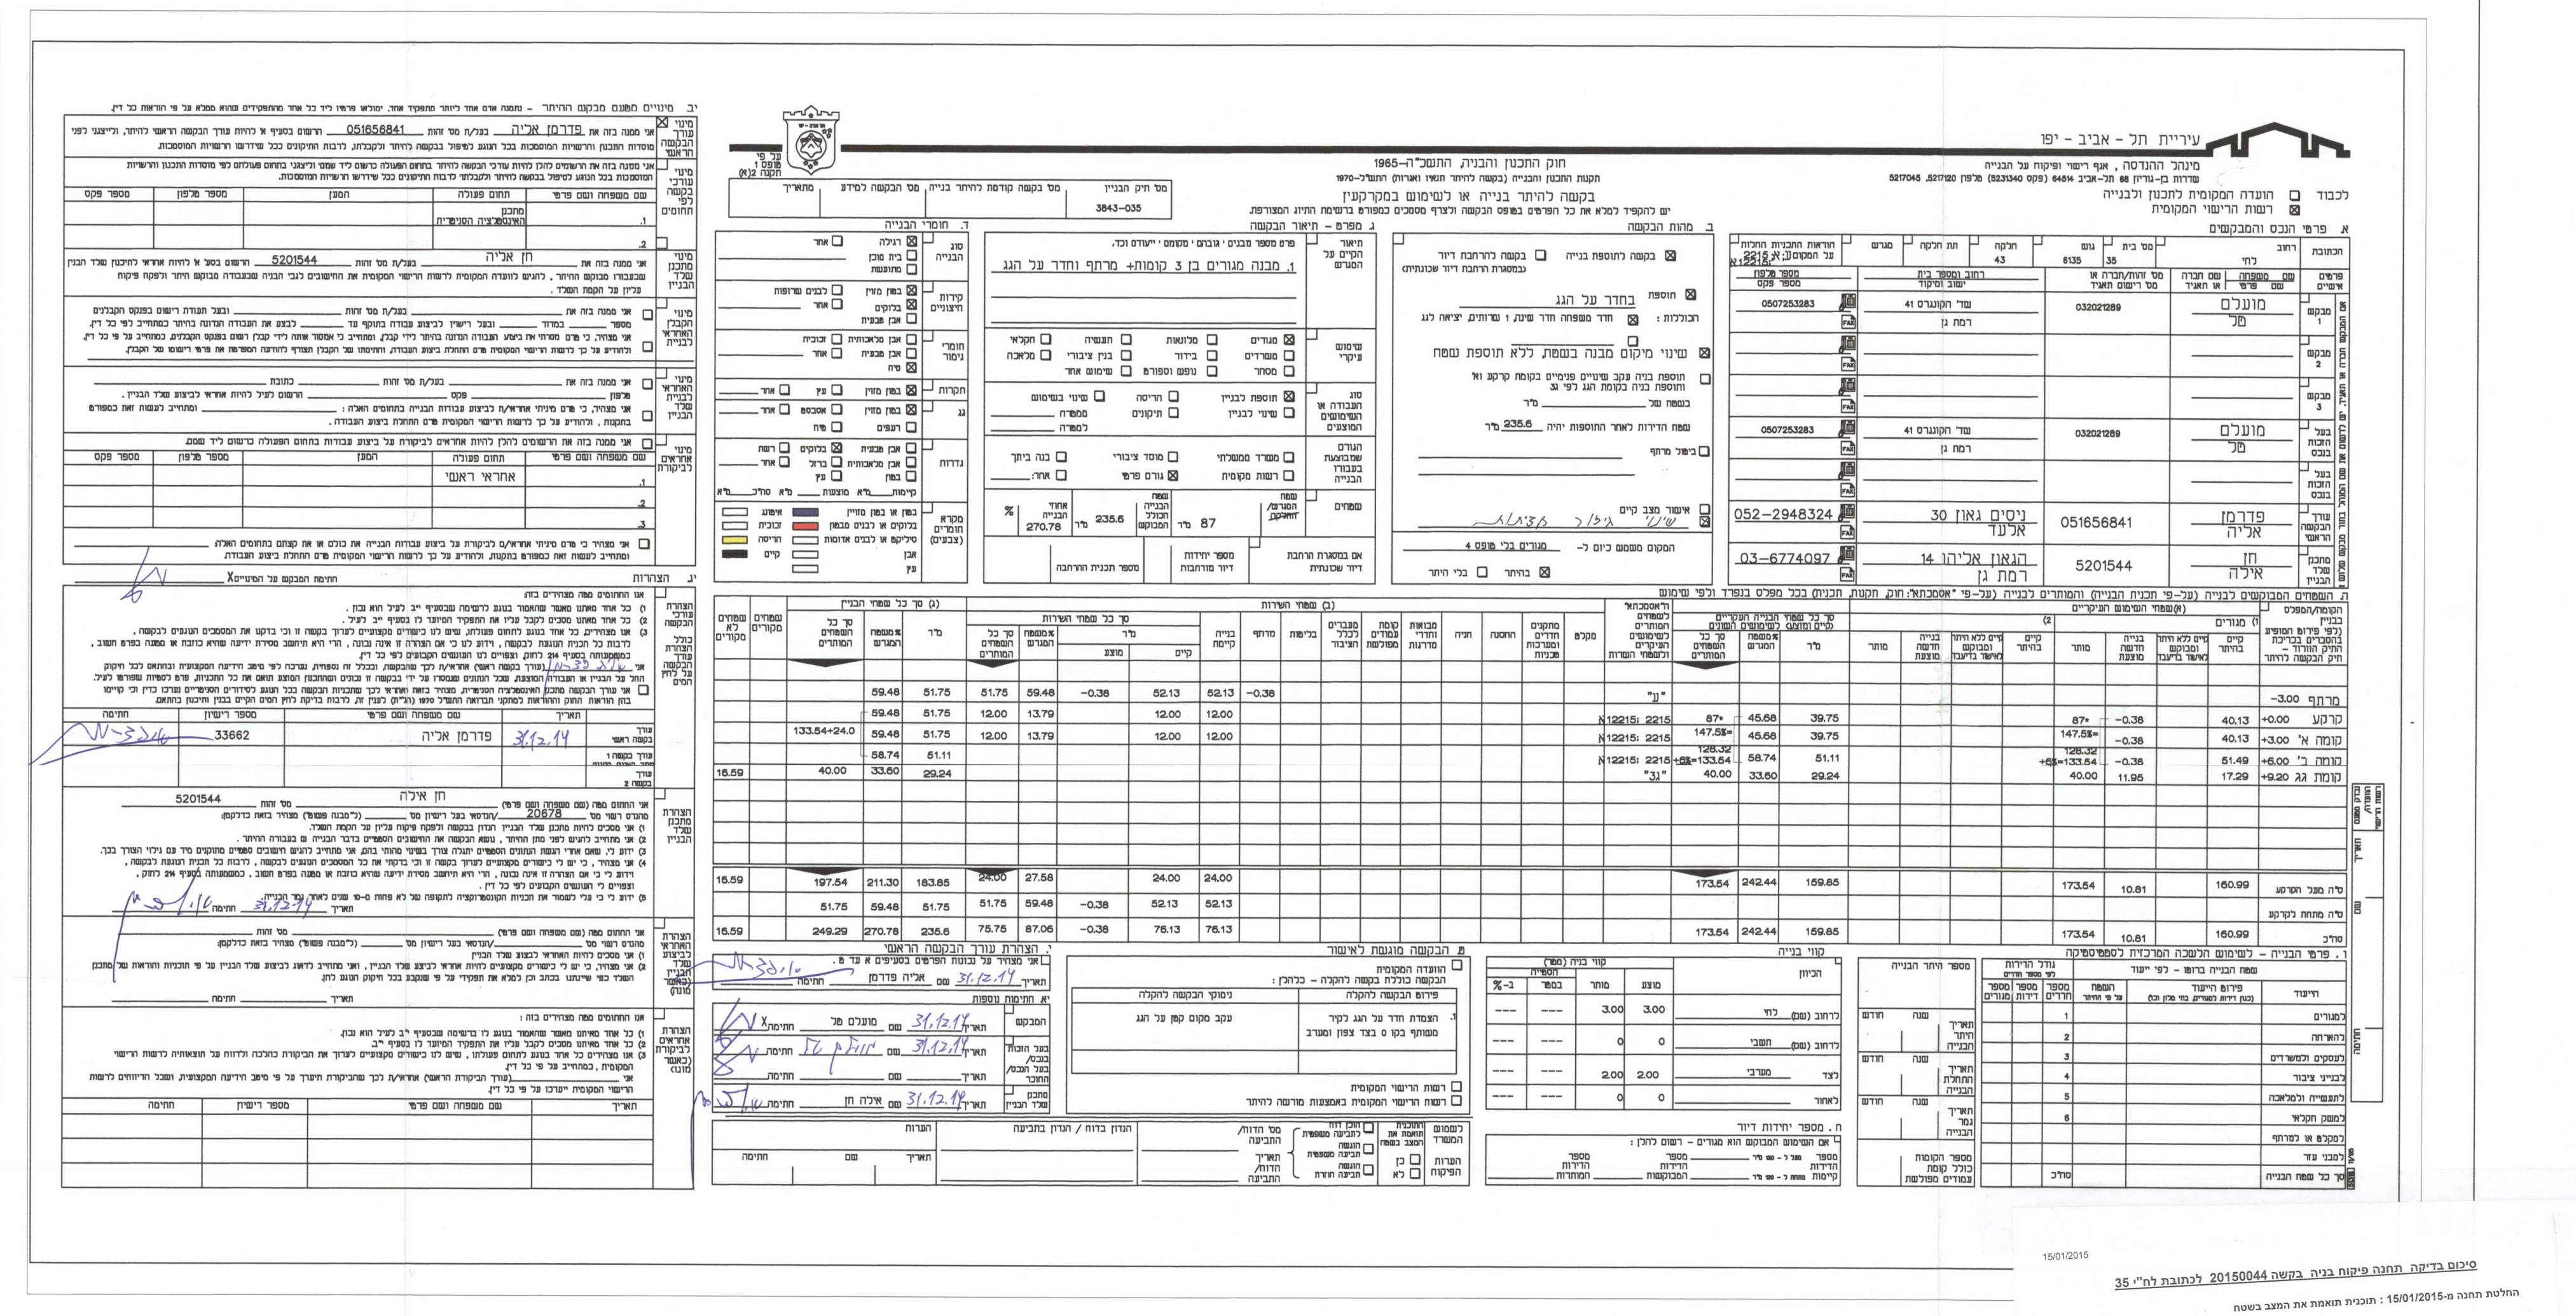

עיריית תל - אביב - יפו
מינהל ההנדסה , אגף רישוי ופיקוח על הבנייה
שדרות בן-גוריון 68 תל-אביב 64514 (פקס 5231340) טלפון 5217120, 5217045

חוק התכנון והבניה, התשכ"ה-1965
תקנות התכנון והבנייה (בקשה להיתר תנאיו ואגרות) התש"ל-1970
בקשה להיתר בנייה או לשימוש במקרקעין
יש להקפיד למלא את כל הפרטים בטופס הבקשה ולצרף מסמכים כמפורט ברשימת התיוג המצורפת.

לכבוד
☐ הועדה המקומית לתכנון ולבנייה
☒ רשות הרישוי המקומית

מס' תיק הבניין 3843-035

א. פרטי הנכס והמבקשים

הכתובת	רחוב	מס' בית	גוש	חלקה	תת חלקה	מגרש	הוראות התכניות החלות על המקום
	לחי	35	6135	43			2215

	שם משפחה / שם פרטי	מס' זהות/חברה	רחוב ומספר בית / ישוב ומיקוד	מספר טלפון
מבקש 1	מועלם טל	032021289	שד' הקונגרס 41 רמת גן	0507253283
בעל הזכות בנכס	מועלם טל	032021289	שד' הקונגרס 41 רמת גן	0507253283
	פרדמן איה	051656841	ניסים גאון 30 אשדוד	052-2948324
	חן אילה	5201544	הצאת אליהו 14 רמת גן	03-6774097

ב. מהות הבקשה
☒ בקשה לתוספת בנייה ☐ בקשה להרחבת דיור (במסגרת הרחבת דיור שכונתית)
☒ תוספת בחדר על הגג
הכוללות : ☒ חדר משפחה חדר שינה, 1 שרותים, יציאה לגג
☒ שינוי מיקום מבנה בשטח, ללא תוספת שטח
שטח הדירות לאחר התוספות יהיה 235.6 מ"ר
☐ ביטול מרתף

ג. מפרט - תיאור הבקשה
1. מבנה מגורים בן 3 קומות+ מרתף וחדר על הגג

שימוש עיקרי: ☒ מגורים
סוג העבודה: ☒ תוספת לבניין
הגורם שמבצעת בעבודה: ☒ גורם פרטי

מספר רישיון 33662

ח. מספר יחידות דיור

15/01/2015
סיכום בדיקה תחנה פיקוח בניה בקשה 20150044 לכתובת לח"י 35
החלטת תחנה מ-15/01/2015 : תוכנית תואמת את המצב בשטח
תוכנית תואמת את המצב בשטח המבוקש בבניה:
מטפל: מאיר ראובן
האינג' ראובן מאיר
מהנדס מפקח
מח' פיקוח על הבניה
עיריית תל-אביב - יפו