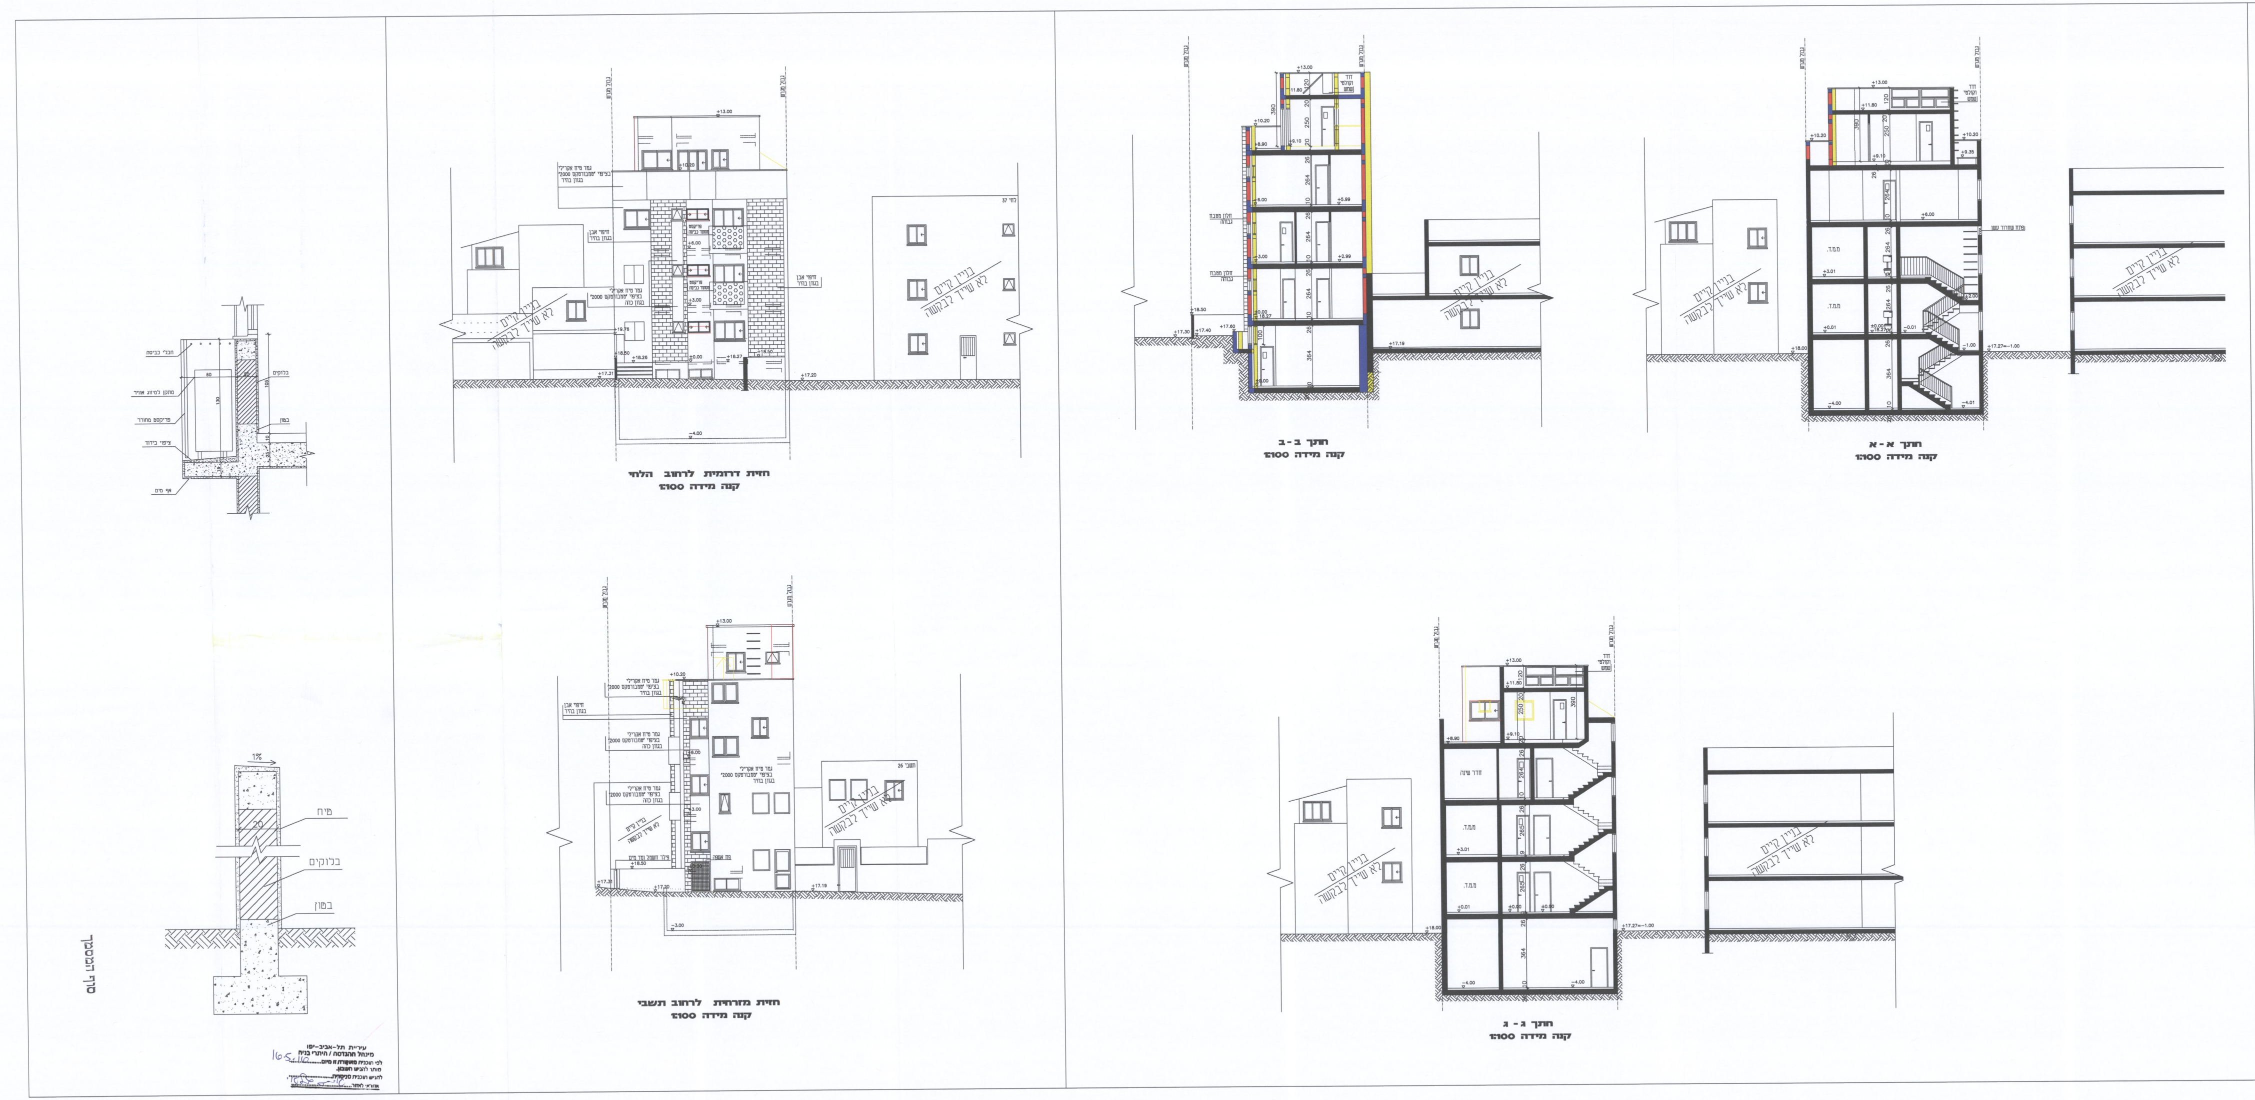

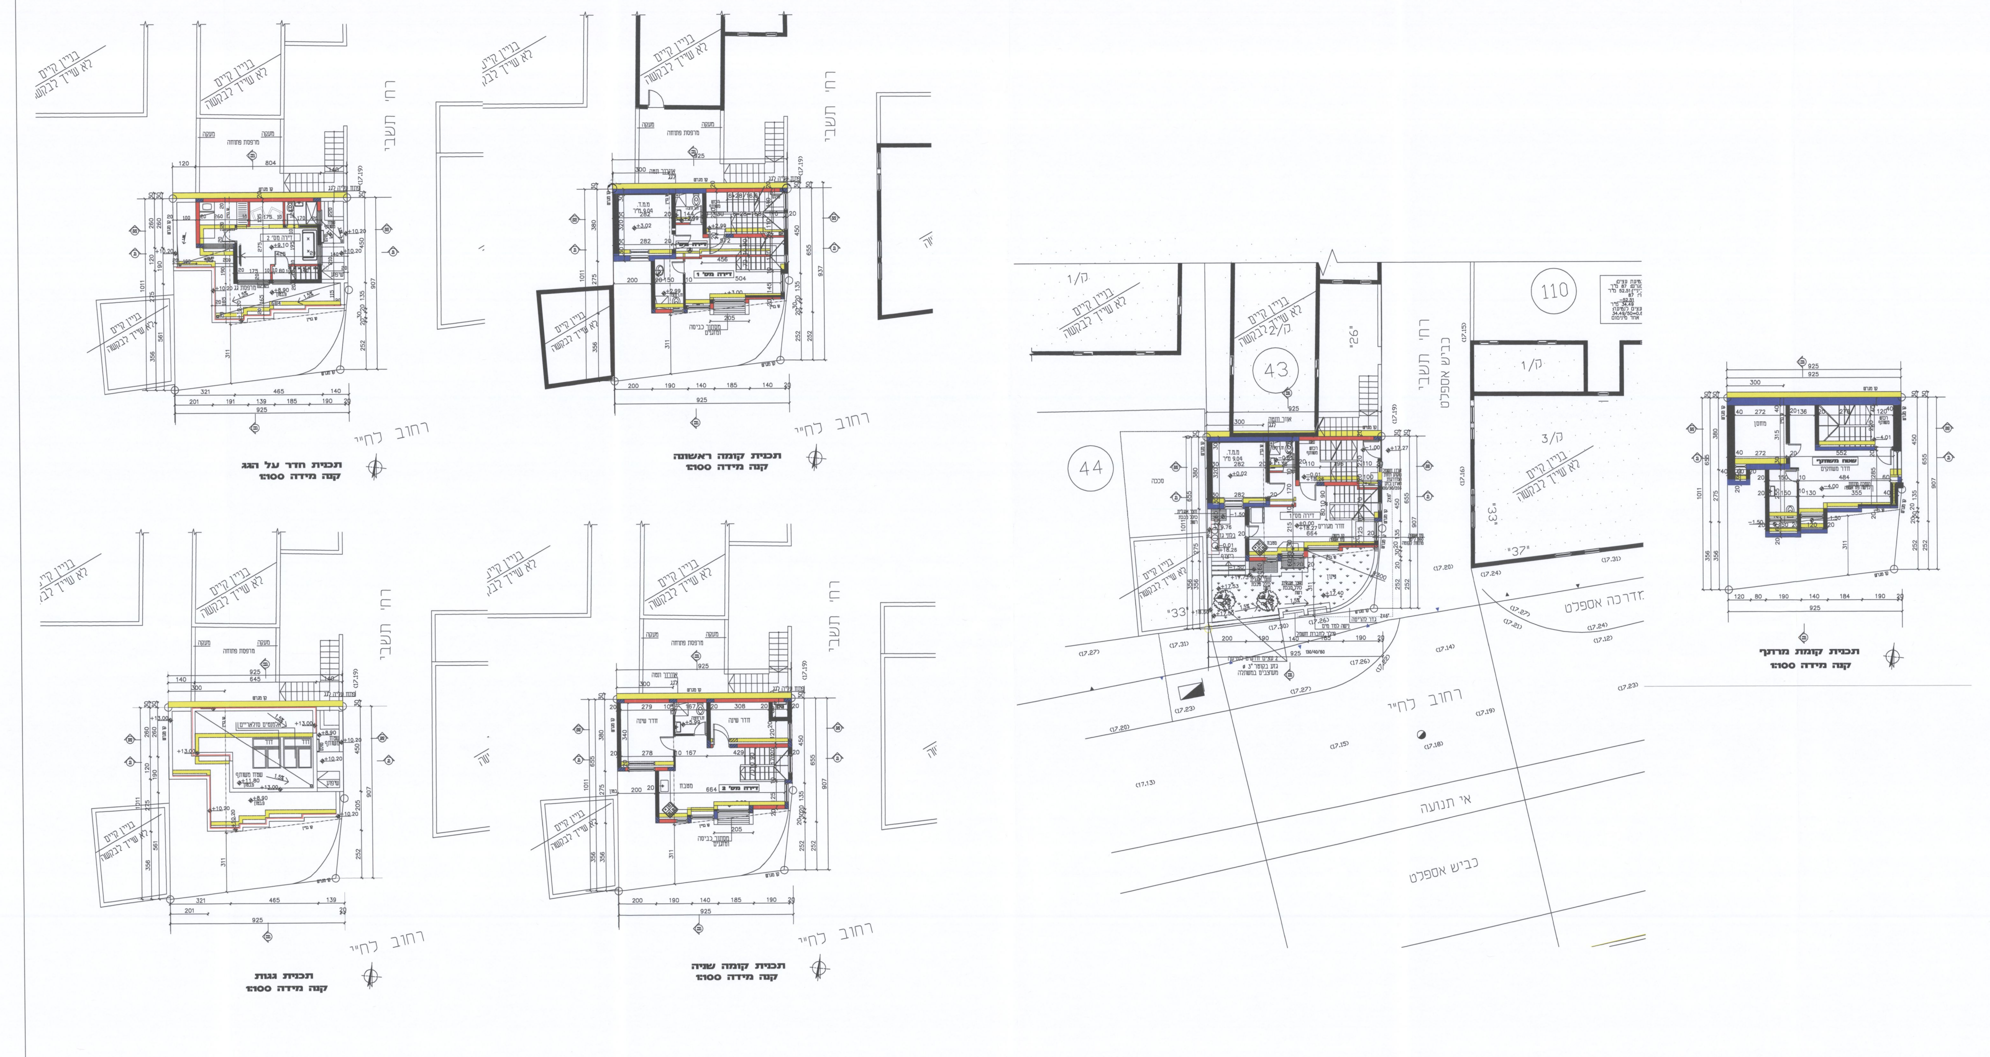

חישוב שטחים

חישוב שטח קומה: קומת מרתף מוצע

שטח מסגרת	9.25*6.55=	מ"ר	60.58
שטח להורדה			
①	2.00*2.75=	מ"ר	5.50
②	3.95*0.50=	מ"ר	1.98
③	(0.20*1.55)+(1.9*02)=	מ"ר	0.69
④	1.40*0.20=	מ"ר	0.28
סה"כ ההורדות		מ"ר	8.45
סה"כ השטח		מ"ר	52.13

תכנית קומת מרתף
קנה מידה 1:200

חישוב שטח קומה : קומה שניה מוצע

שטח מסגרת	9.25*6.55=	מ"ר	60.58
שטח להורדה			
①	2.75*2.00=	מ"ר	5.50
②	3.95*0.50=	מ"ר	1.98
③	(0.20*1.55)+(1.9*02)=	מ"ר	0.69
④	1.40*0.20=	מ"ר	0.28
⑤	0.80*0.80=	מ"ר	0.64
סה"כ ההורדות		מ"ר	9.09
סה"כ השטח		מ"ר	51.49

תכנית קומה שניה
קנה מידה 1:200

חישוב שטח קומה: קומת קרקע מוצע

שטח מסגרת	9.25*6.55=	מ"ר	60.58
שטח להורדה			
①	2.00*2.75=	מ"ר	5.50
②	3.95*0.50=	מ"ר	1.98
③	(0.20*1.55)+(1.9*02)=	מ"ר	0.69
④	1.40*0.20=	מ"ר	0.28
⑤ שטח מ.מ.ד נטו	2.74*3.30=	מ"ר	9.04
שטח קירות	12.12-9.04=	מ"ר	3.08
שטח מ.מ.ד ברוטו	9.04+3.08=	מ"ר	12.12
שטח מ.מ.ד להורדה		מ"ר מקס'	12
סה"כ ההורדות		מ"ר	20.45
סה"כ השטח		מ"ר	40.13

תכנית קומת קרקע
קנה מידה 1:200

חישוב שטח קומה: קומת גג מוצע

①	2.0*2.6=	מ"ר	5.2
②	4.65*4.5=	מ"ר	20.92
שטח חדר על הגג		מ"ר מקס'	26.12
שטח מסגרת	9.25*6.55=	מ"ר	60.58
שטח להורדה			
③	2.0*2.75=	מ"ר	5.5
④	0.20*1.4=	מ"ר	0.28
⑤	3.95*0.5=	מ"ר	1.98
⑥	(0.2*1.55)+(1.9*0.2)=	מ"ר	0.69
⑦ שטח משותף	1.40*4.50=	מ"ר	6.30
סה"כ ההורדות		מ"ר	14.75
מרפסת הגג	60.58-26.12-14.75=	מ"ר	19.71

תכנית חדר על הגג
קנה מידה 1:200

סה"כ ההורדות	14.75	מ"ר
סה"כ חדר על הגג	26.12	מ"ר
סה"כ מרפסת הגג	19.71	מ"ר
סה"כ שטח (חדר+ מרפסת)	26.12+19.71=45.83	מ"ר
היחס בין החדר על הגג לשטח הגג	26.12/45.3=57.66%	

חישוב שטח קומה : קומה ראשונה מוצע

שטח מסגרת	9.25*6.55=	מ"ר	60.58
שטח להורדה			
①	2.75*2.00=	מ"ר	5.50
②	3.95*0.50=	מ"ר	1.98
③	(0.20*1.55)+(1.9*02)=	מ"ר	0.69
④	1.40*0.20=	מ"ר	0.28
⑤ שטח מ.מ.ד נטו	2.74*3.30=	מ"ר	9.04
שטח קירות	12.12-9.04=	מ"ר	3.08
שטח מ.מ.ד ברוטו	9.04+3.08=	מ"ר	12.12
שטח מ.מ.ד להורדה		מ"ר מקס'	12
סה"כ ההורדות		מ"ר	20.45
סה"כ השטח		מ"ר	40.13

תכנית קומה ראשונה
קנה מידה 1:200

התפלגות הדירות:

דירה מס' 2	① 3.55*4.56=	מ"ר	16.19
	② 4.69*3.80=	מ"ר	17.82
סה"כ השטח (כולל ממ"ד)		מ"ר	34.01
דירה מס' 1	40.13+12-34.01=	מ"ר	18.12

טבלת התפלגות דירות:

מס'	שטח הדירה ללא מ.מ.ד	מ.מ.ד	סה"כ	חדר על הגג	סה"כ	מרפסות
1)	18.12+40.13= 58.25	12	71.25	—	71.25	—
2)	22.01+51.49= 73.50	12	85.50	26.12	111.62	19.71

מפה טופוגרפית
1 : 250

תל-אביב
גוש : 6135
חלקה : 43(חלק)
כתובת : רח' לחי 35
הוכן עבור : חילבה ישעיהו
מטרת המדידה : הגדרת מגרש משני עפ"י תב"ע 2215

שם הבעלים כרשום בנסח טאבו+מס' ת.ז : מועלם טל 032021289

שטח לפי נסח :
שטח החלקה כולה : 3.575 ד.מ.
בעלות בחלקים(כרשום בנסח טאבו) : מועלם טל 174/7150

בעלות במ"ר : 87
שטח מדוד(מ"ר) : 87

שטח מגרש משני : 0.87 ד.מ.
שטח לגריעה : ד.מ.

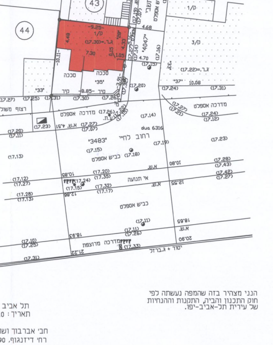

תרשים הסביבה 1:1250

הנני מצהיר בזה שהמפה נעשתה לפי חוק התכנון והביה, התקנות וההנחיות של עיריית תל-אביב-יפו.

תל אביב
תאריך : 2.12.2010

י.אברבוך מודד מוסמך
רשיון מס' "461"
חב' אברבוך ושותי מודדים מוסמכים בעים
רח' דיזנגוף 190, תל-אביב טל5235891, 03-5226791

הערות:
1. המספרים בסוגריים מציינים גבהים.
2. הגבהים מבוססים על נ.ק. עירונית מס' 187 שגובהה 17.549 מ'.

עיריית תל - אביב - יפו
מינהל ההנדסה, אגף רישוי ופיקוח על הבנייה

חוק התכנון והבניה, התשכ"ה–1965

בקשה להיתר בנייה או לשימוש במקרקעין

נסרק