215-0044

22

13-296
2.5.13

נסרק

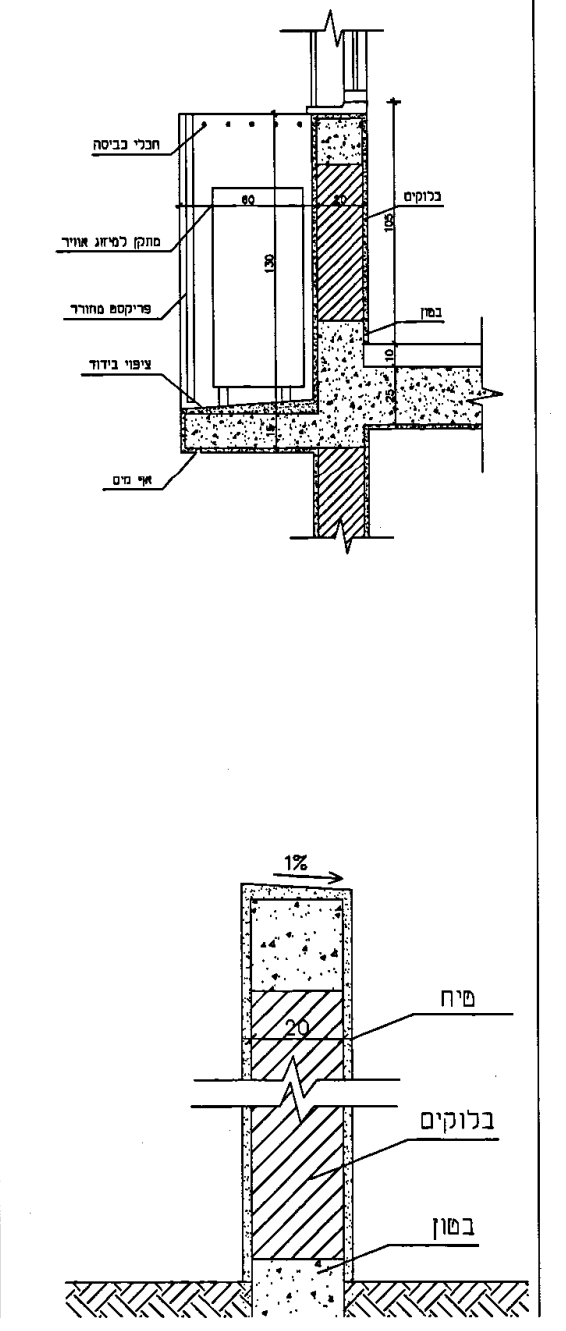
פיח
בלוקים
בטון
1%

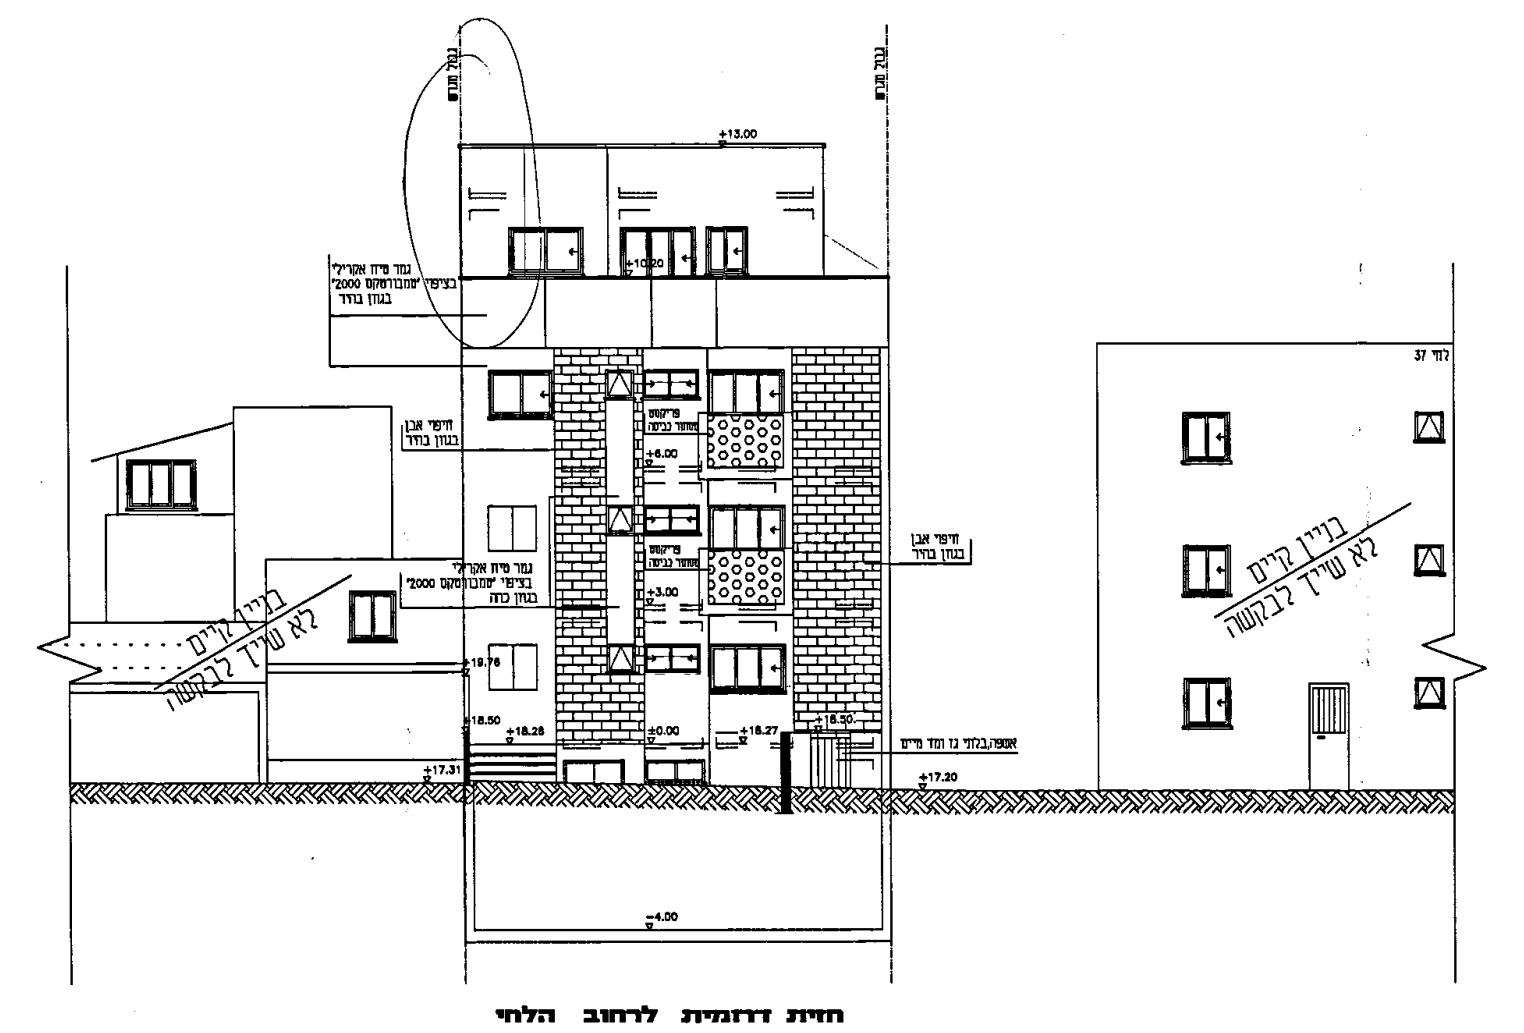
בניין קיים לא שייך לבקשה

חזית דרומית לרחוב הלחי
קנה מידה 1:100

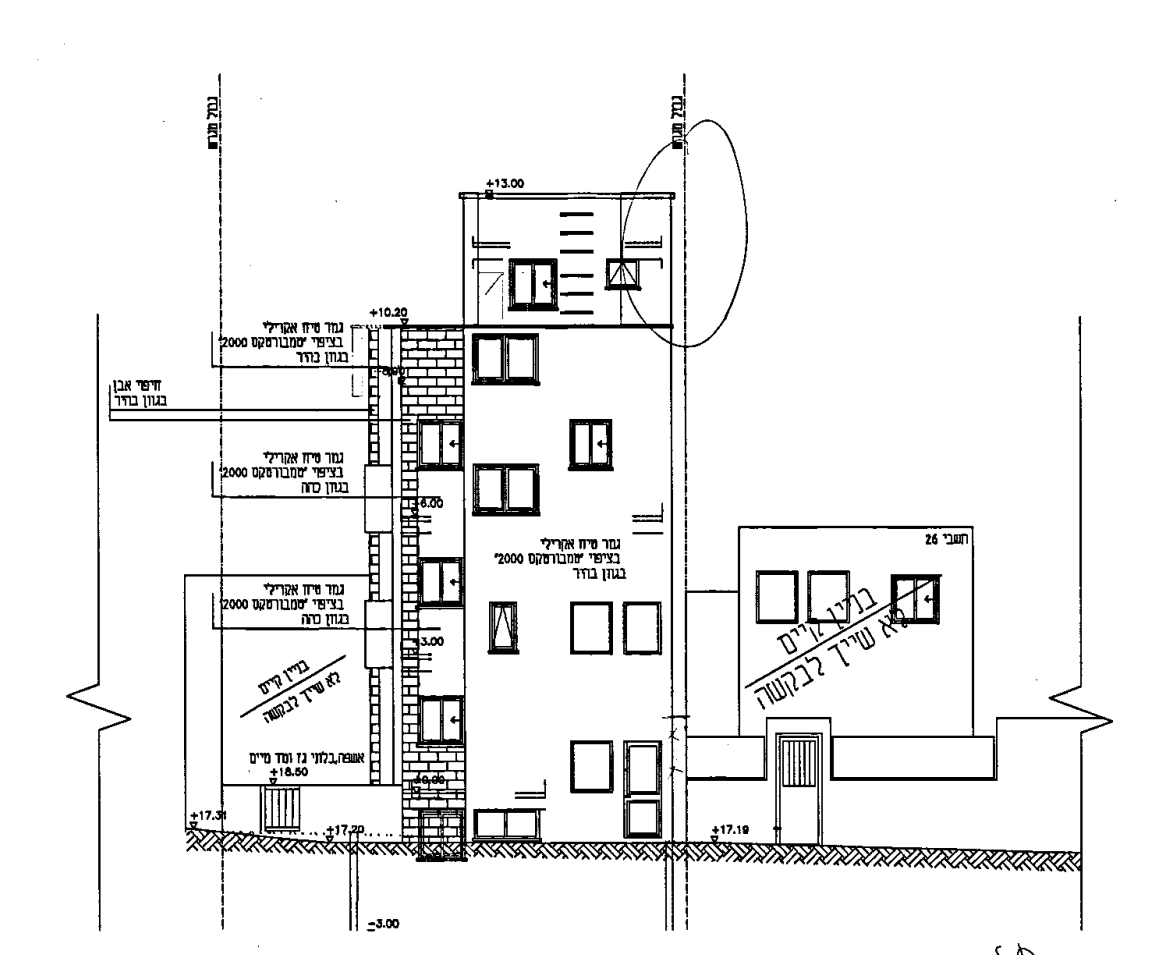
בניין קיים לא שייך לבקשה

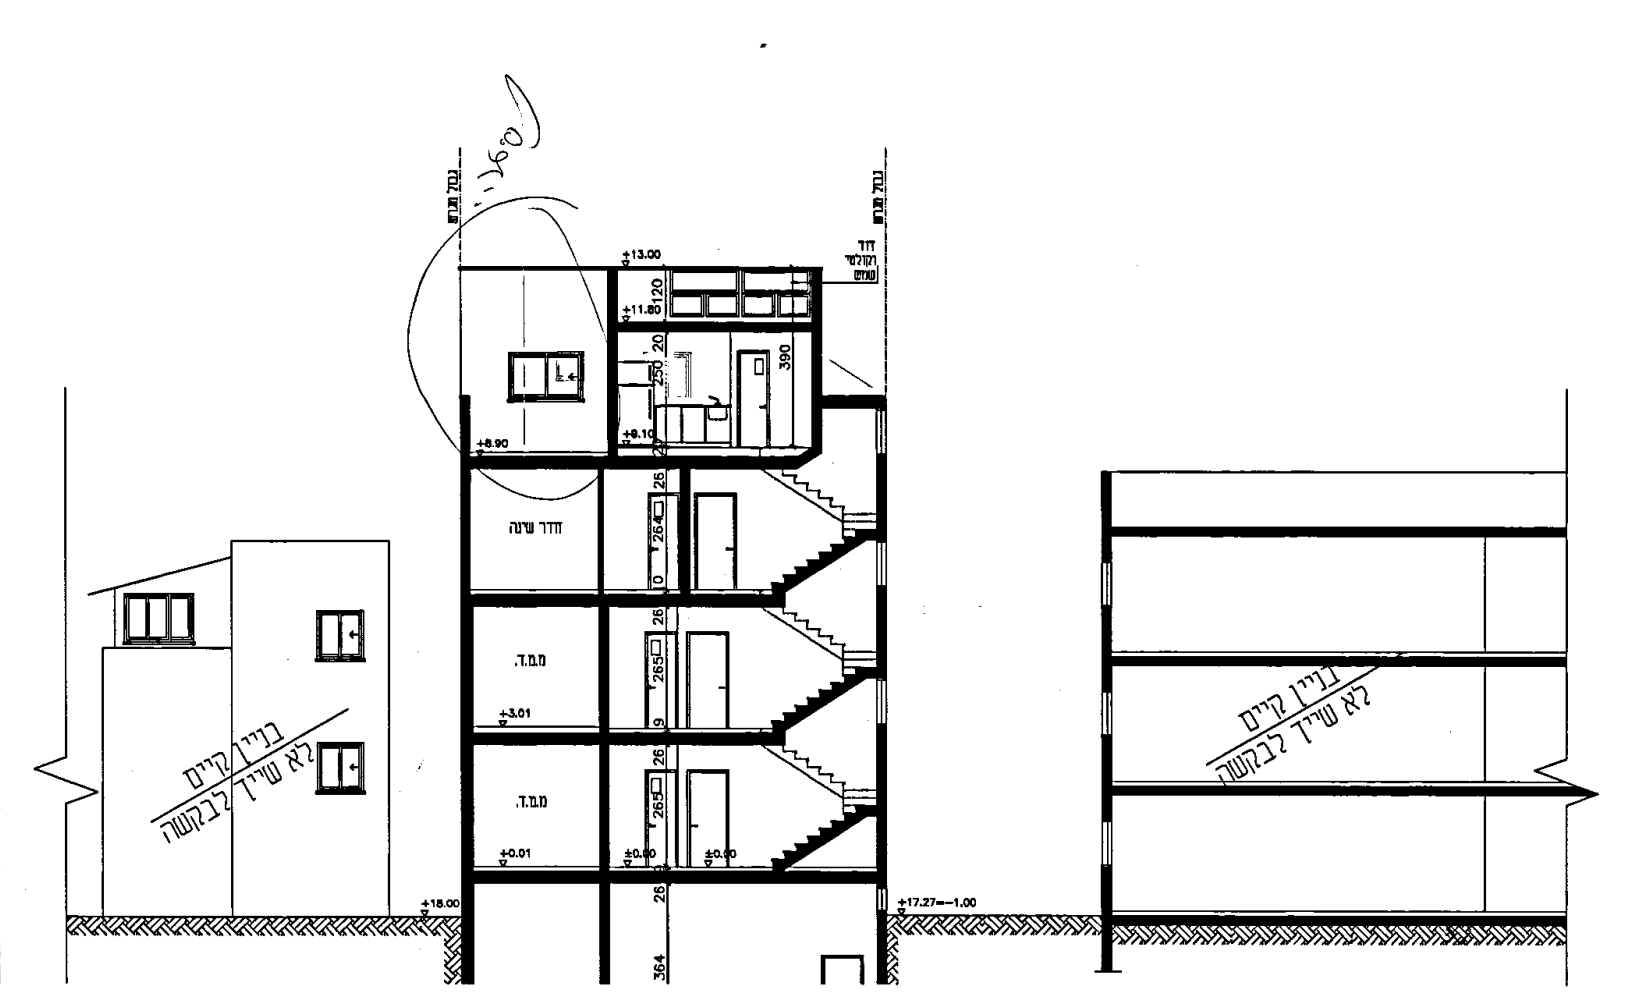
בניין קיים לא שייך לבקשה
ממ"ד
חדר שינה

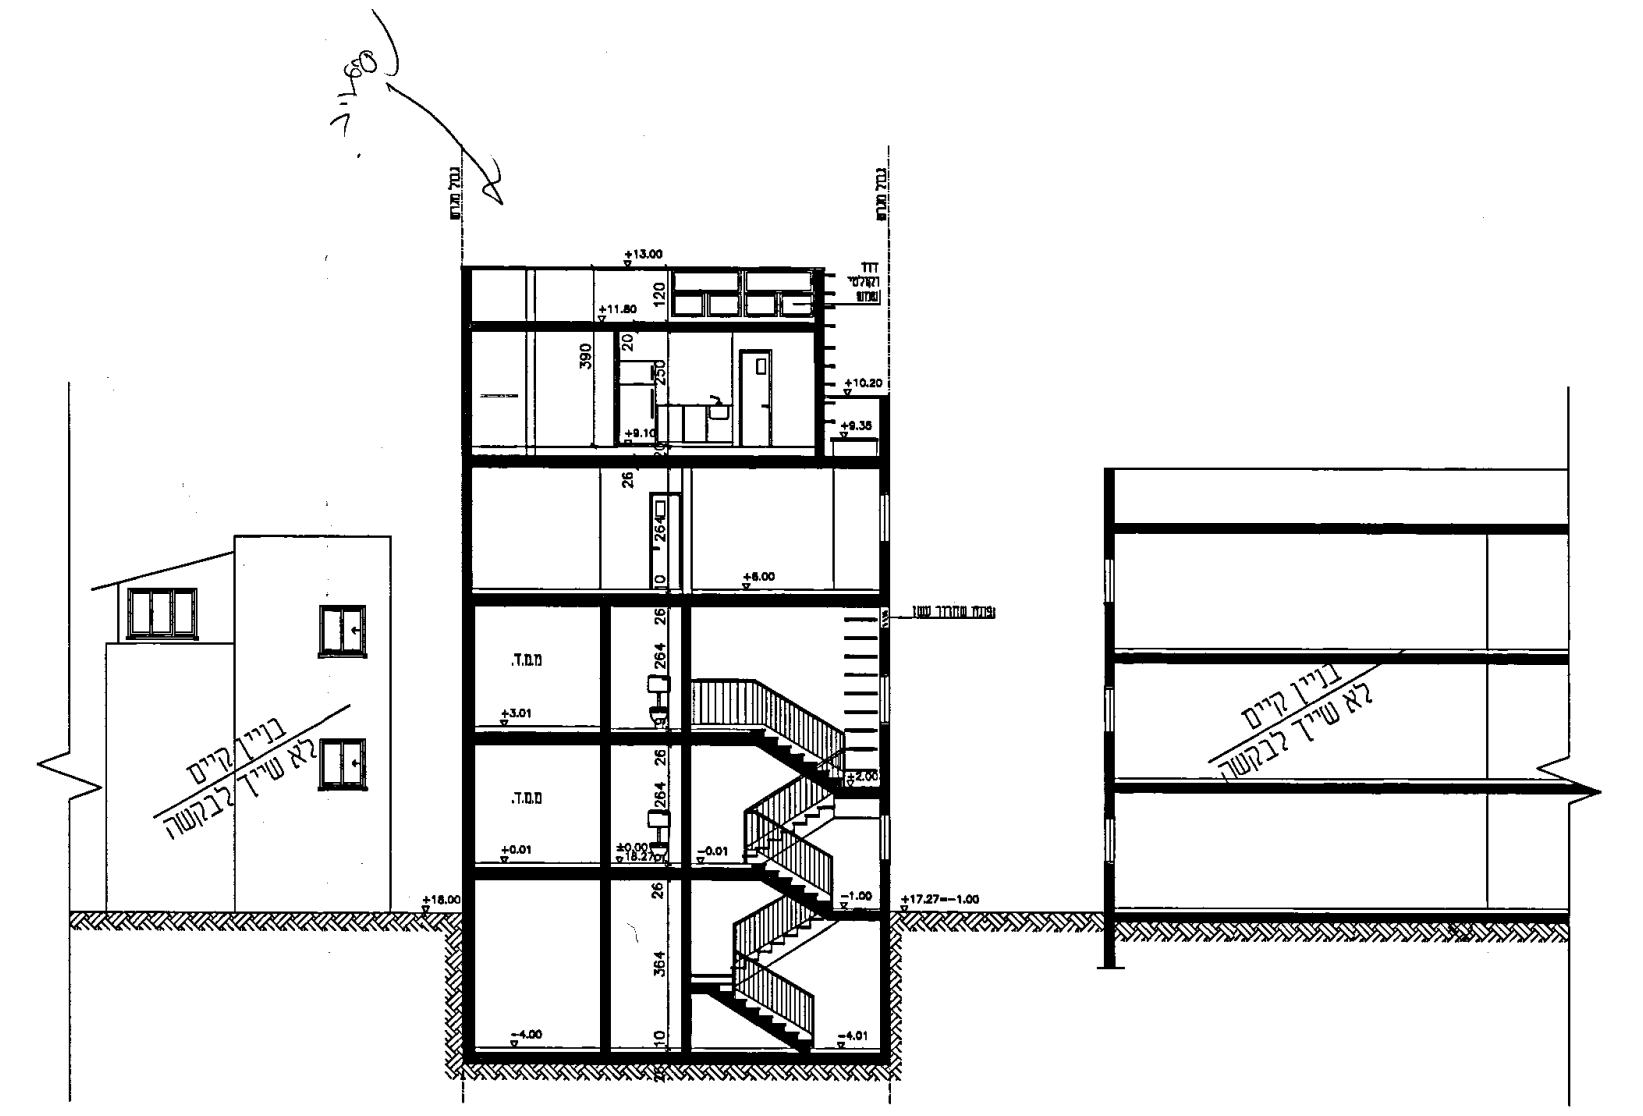
בניין קיים לא שייך לבקשה
ממ"ד

חתך א-א
קנה מידה 1:100

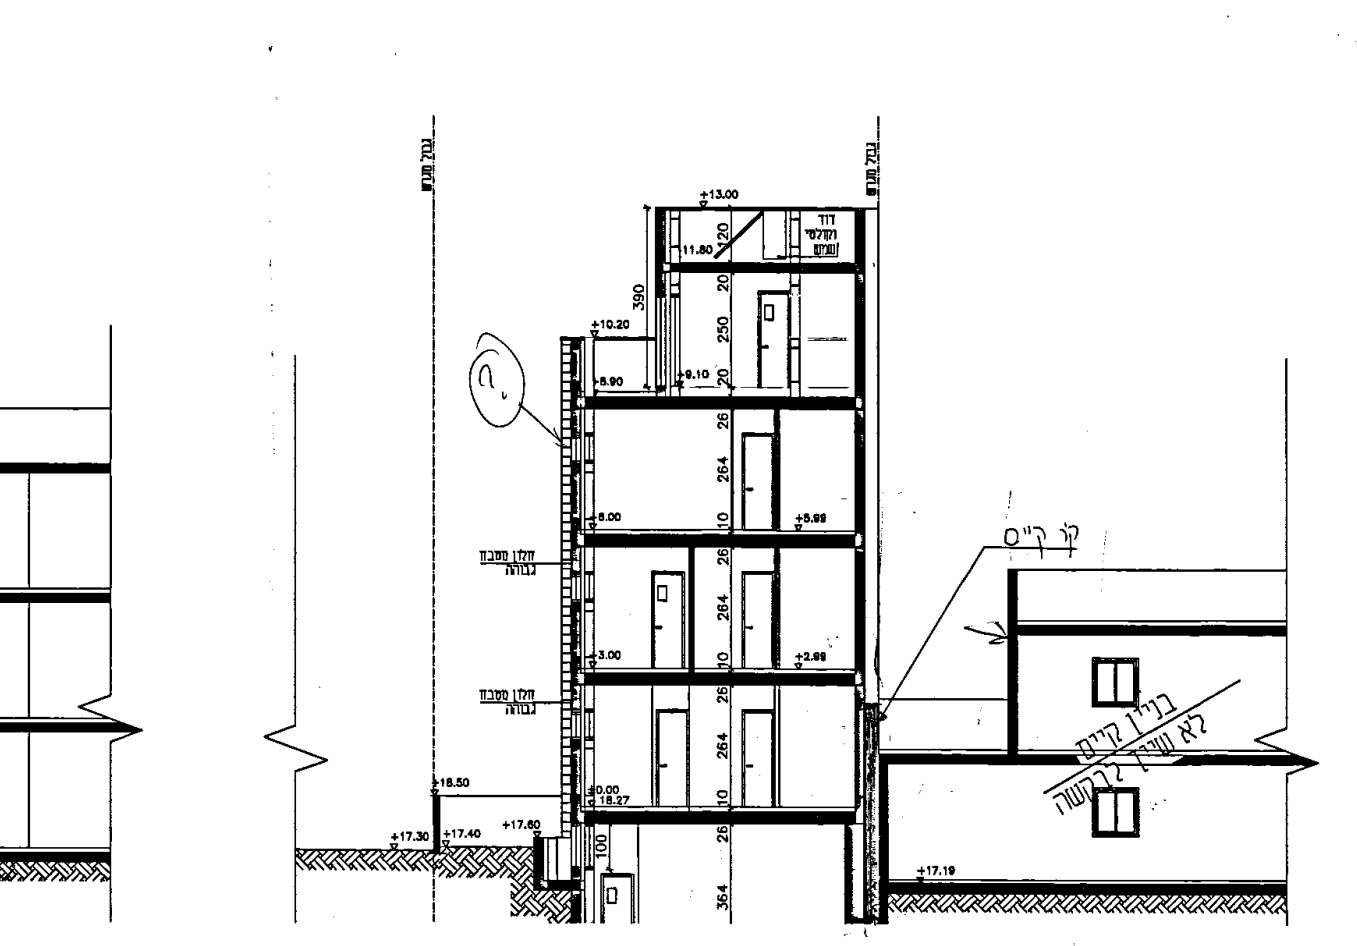
בניין קיים לא שייך לבקשה

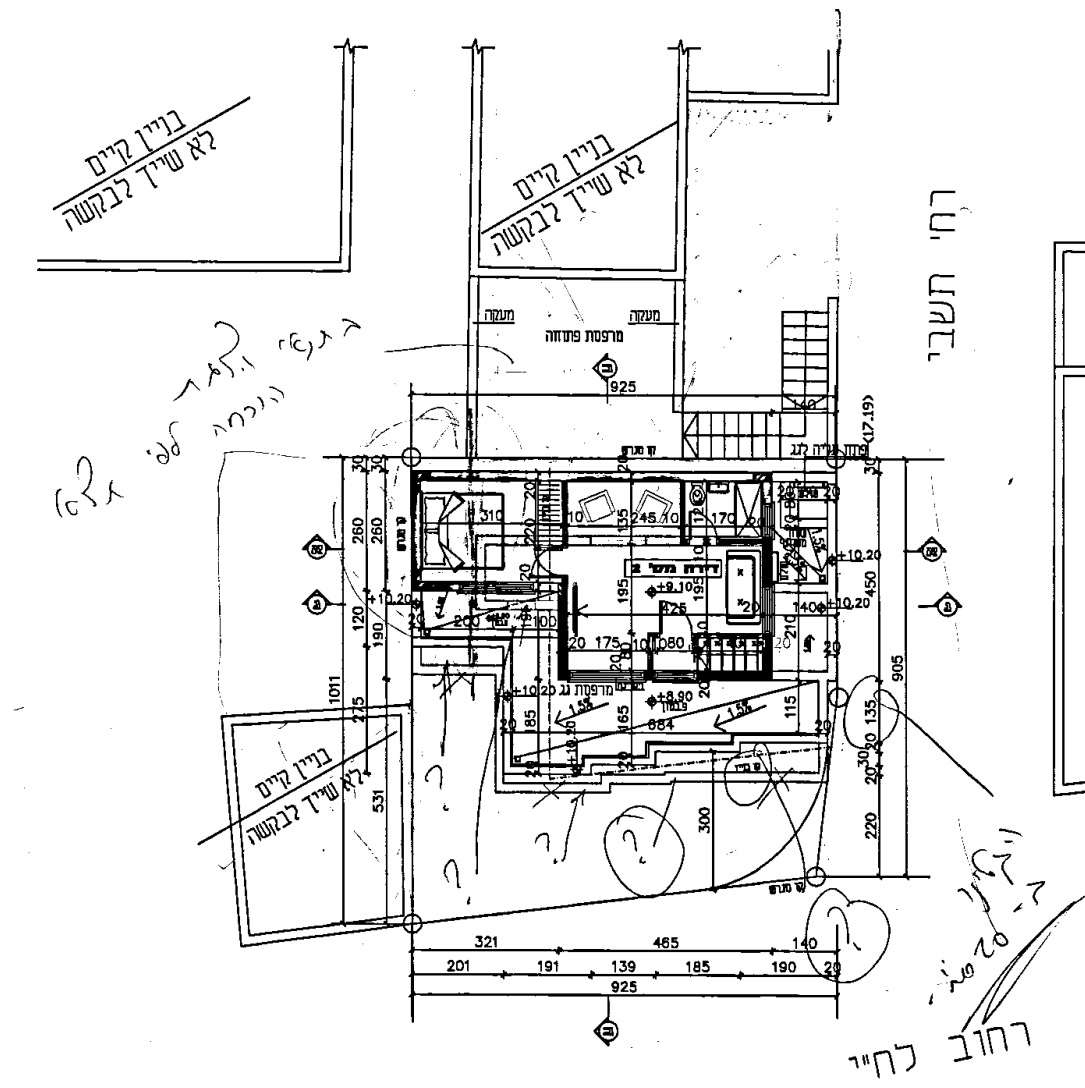
בניין קיים לא שייך לבקשה
רח' תשבי
925

תכנית עליית גג
קנה מידה 1:100

רחוב לח"י

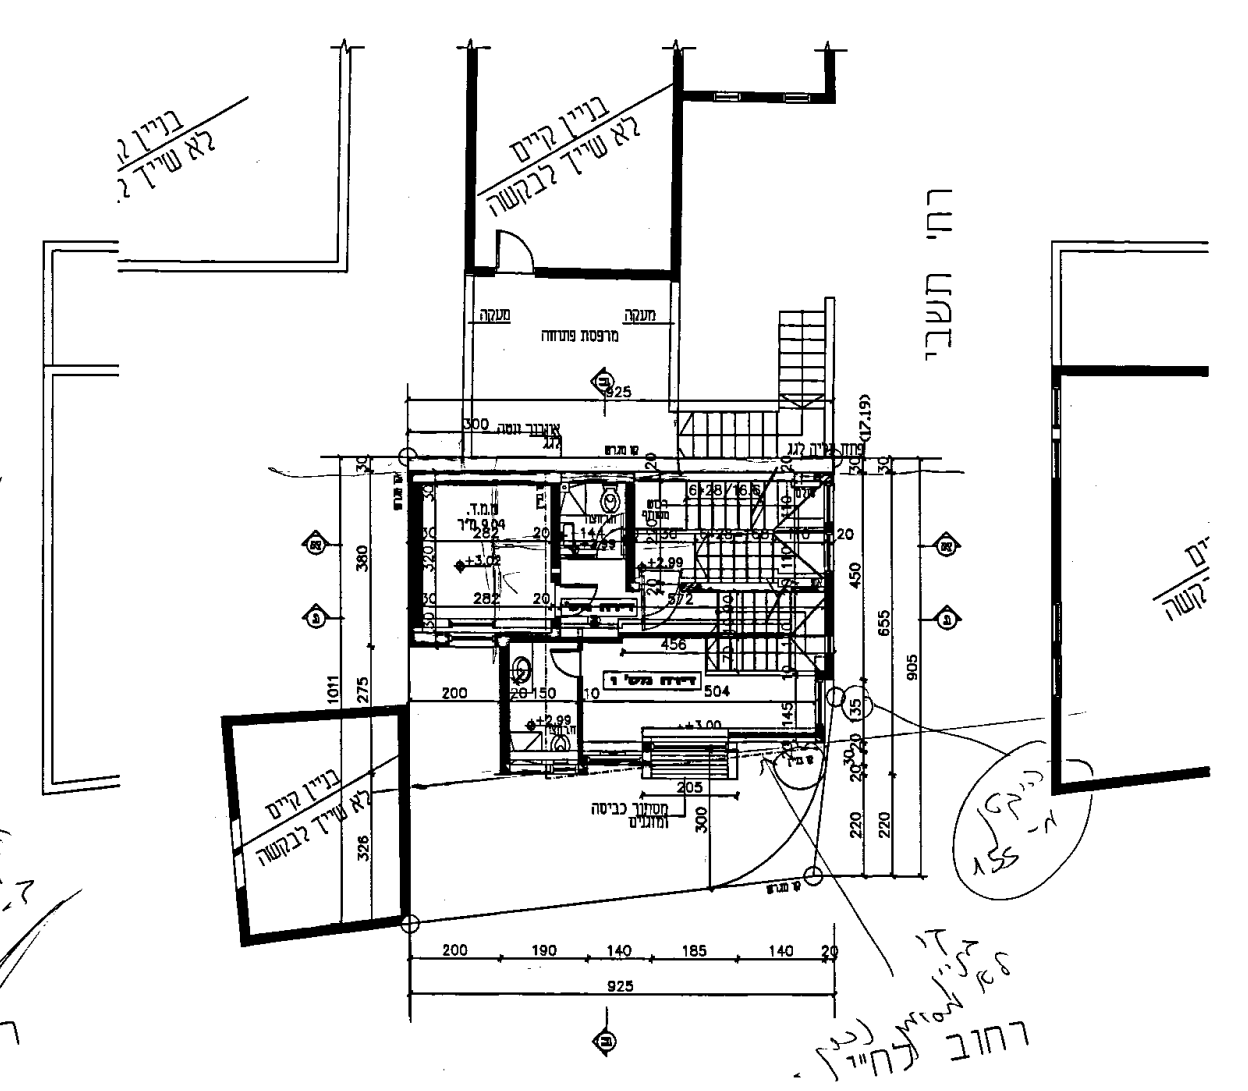
בניין קיים לא שייך לבקשה
רח' תשבי
925

תכנית קומה ראשונה
קנה מידה 1:100

רחוב לח"י

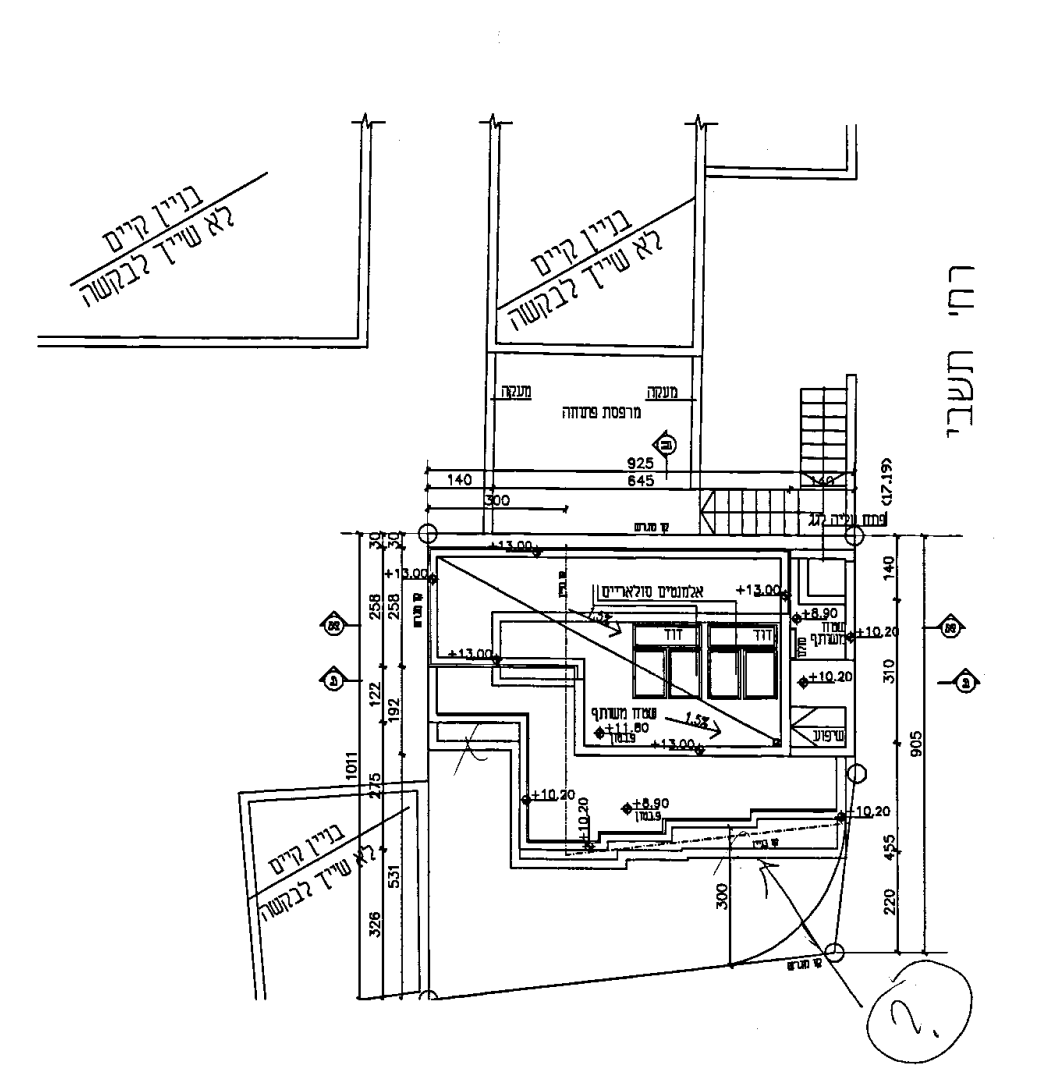
בניין קיים לא שייך לבקשה
רח' תשבי

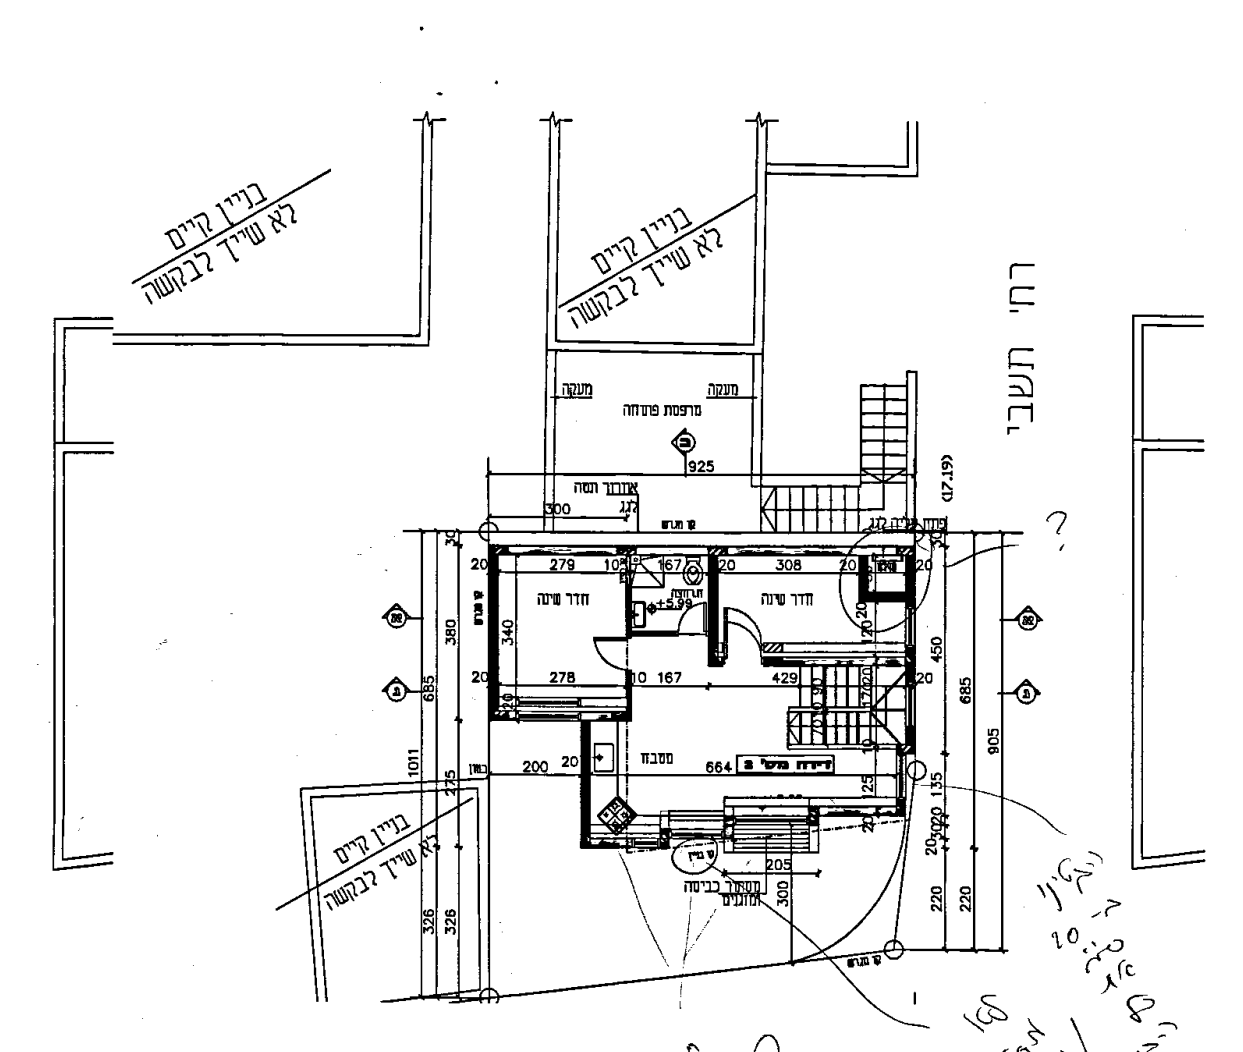
בניין קיים לא שייך לבקשה
רח' תשבי
חדר שינה

ח תוספת שטח

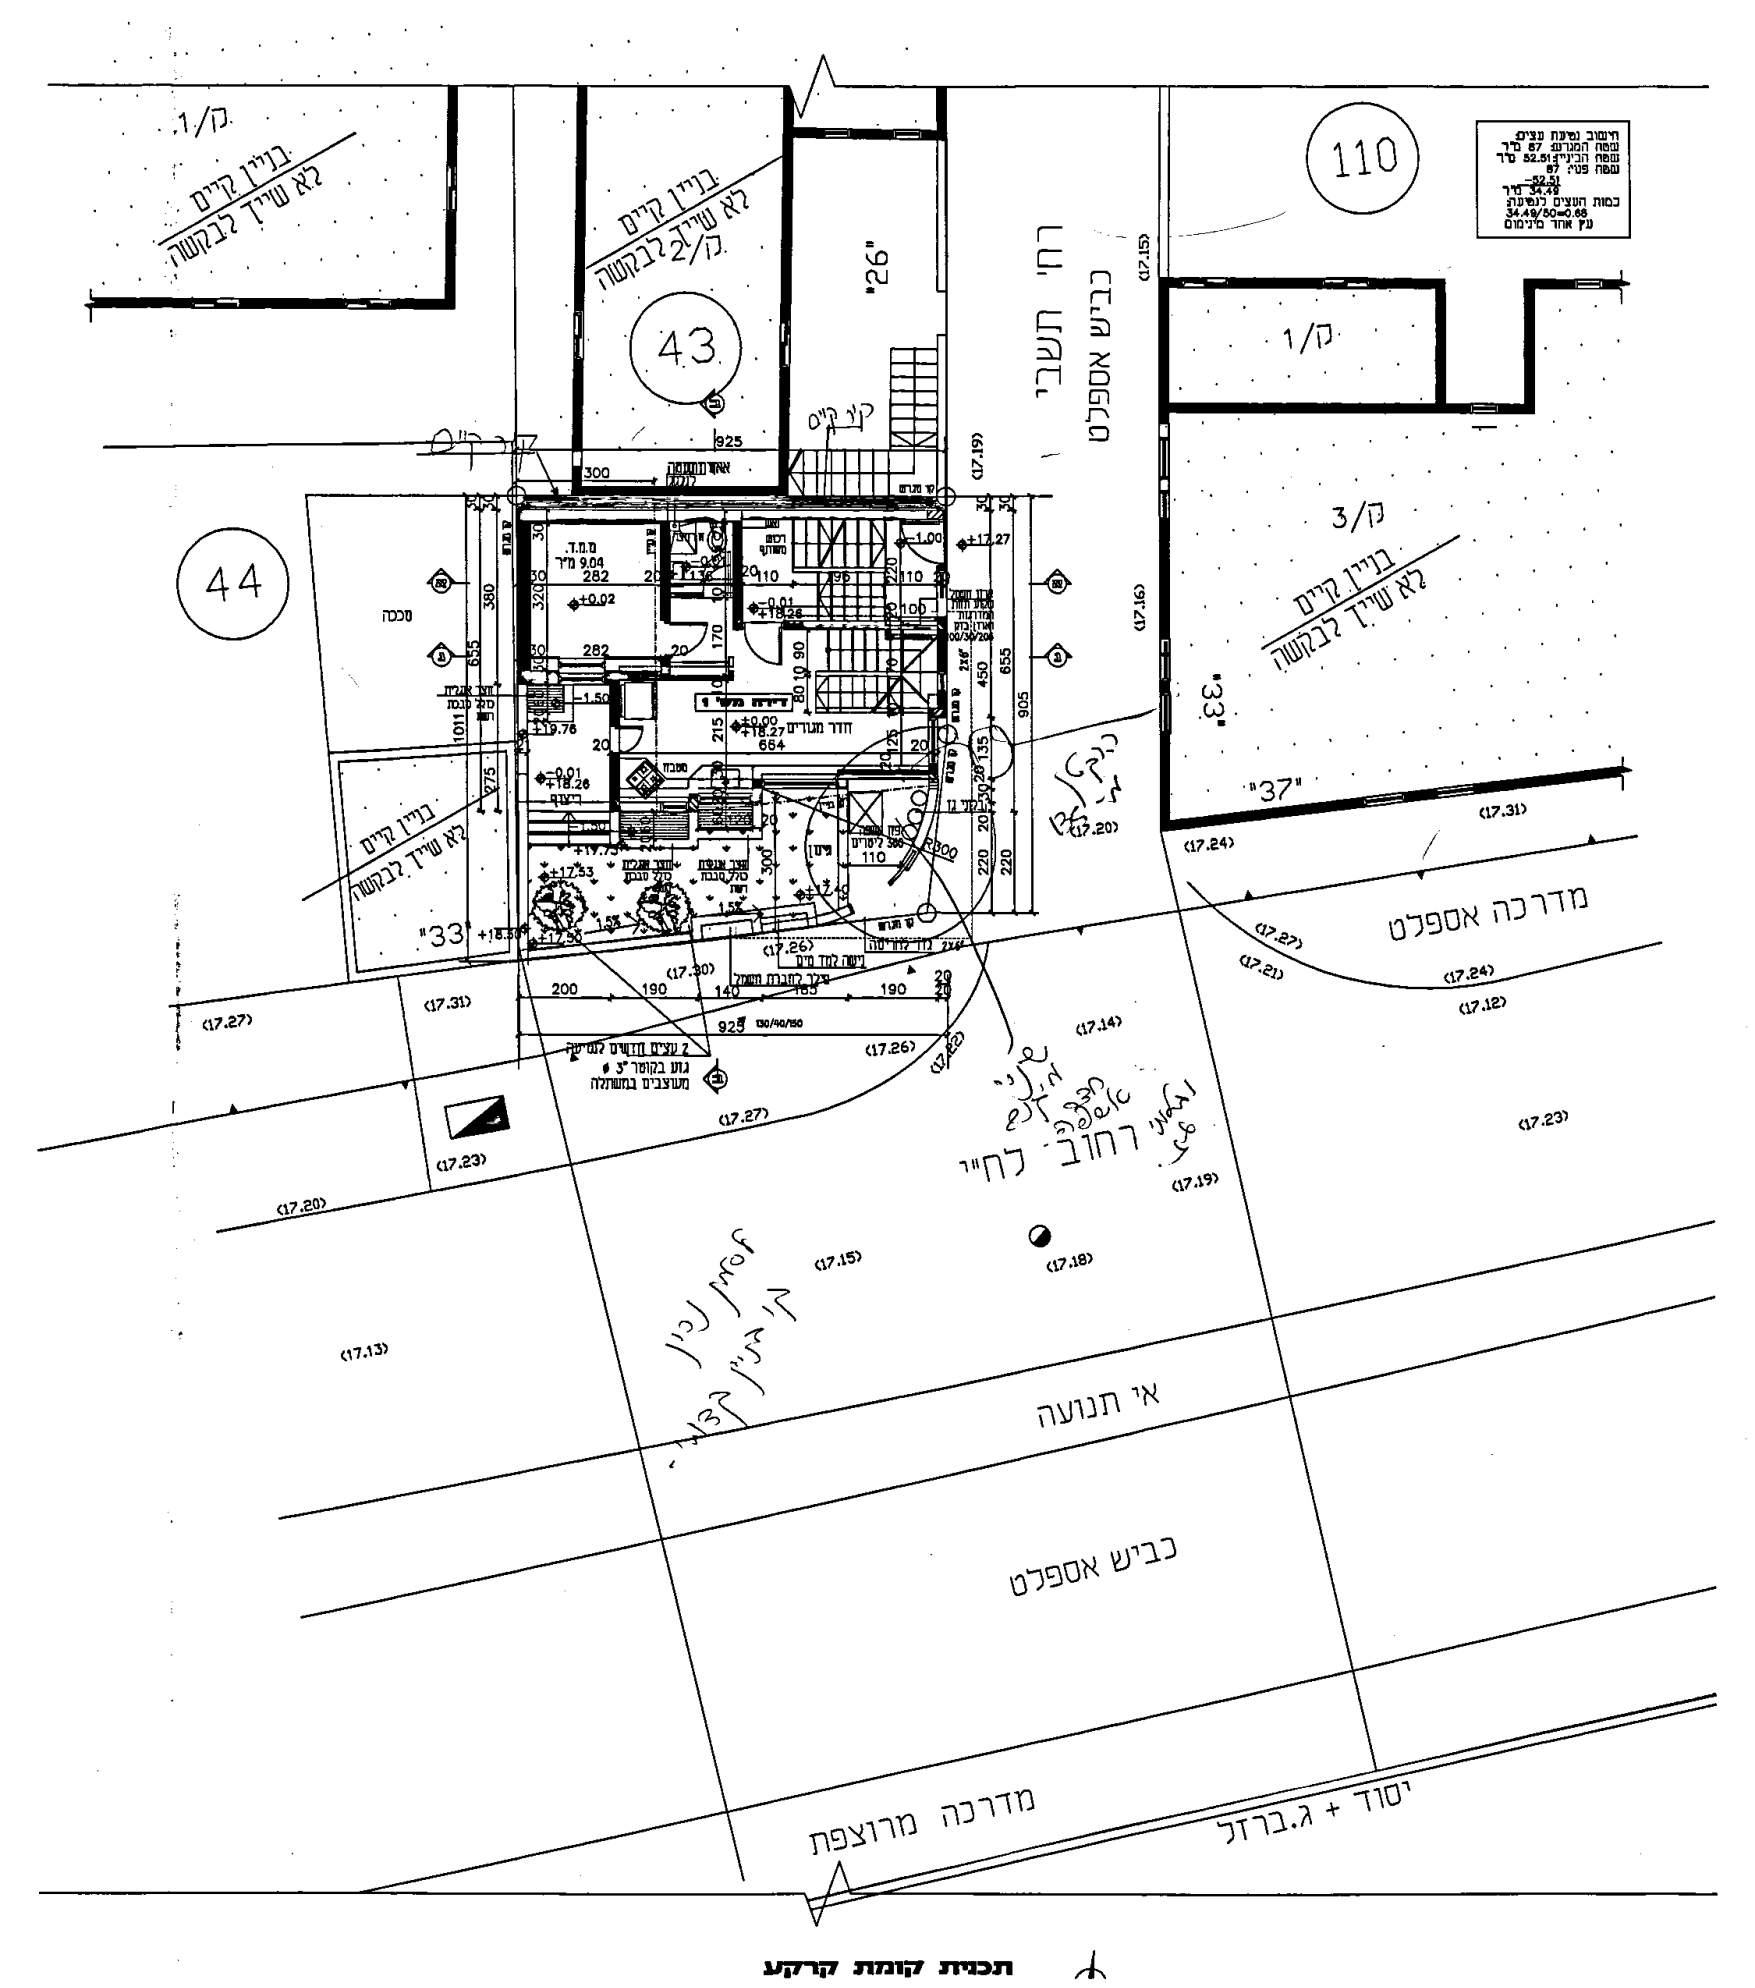
110
43
44
ק/1
ק/2
ק/3
בניין קיים לא שייך לבקשה
רח' תשבי
כביש אספלט
מדרכה אספלט
רחוב לח"י
אי תנועה
כביש אספלט
מדרכה מרוצפת
יסוד + ג.ברזל

תכנית קומת קרקע

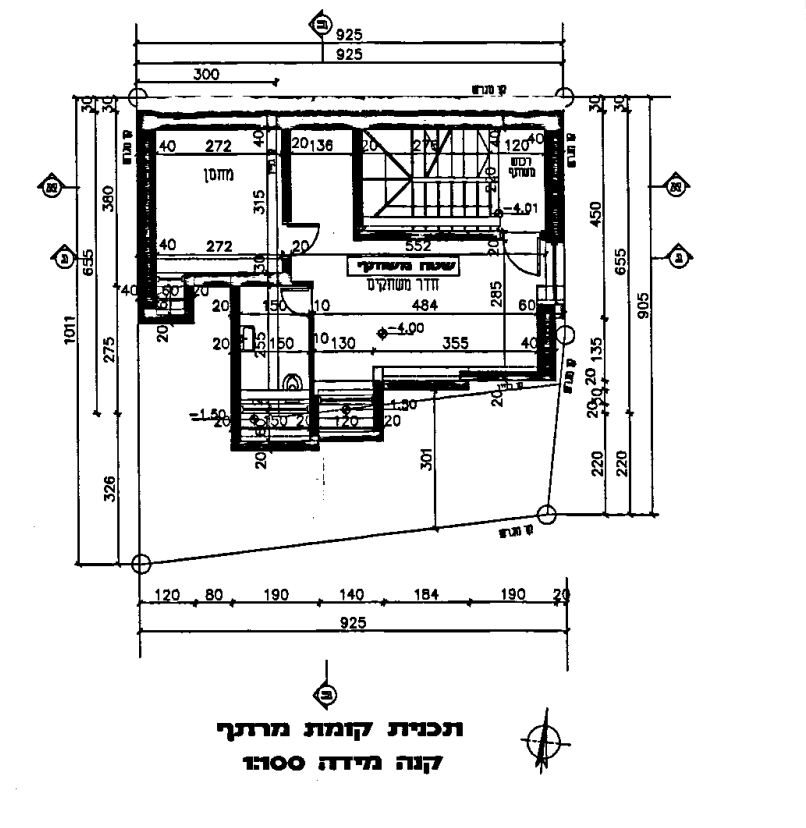

תכנית קומת מרתף
קנה מידה 1:100

חישוב שטחים

חישוב שטח קומה: קומת מרתף מוצע

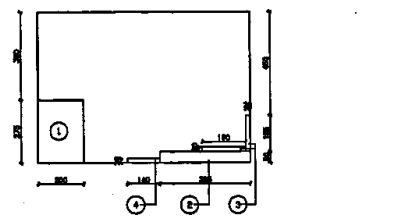

תכנית קומת מרתף
קנה מידה 1:200

שטח מסגרת	60.58	מ"ר	9.25*6.55=
שטח להורדה			
	5.50	מ"ר	① 2.00*2.75=
	1.98	מ"ר	② 3.95*0.50=
	0.69	מ"ר	③ (0.20*1.55)+(1.9*02)=
	0.28	מ"ר	④ 1.40*0.20=
סה"כ ההורדות	8.45	מ"ר	
סה"כ השטח	52.13	מ"ר	

חישוב שטח קומה: קומת קרקע מוצע

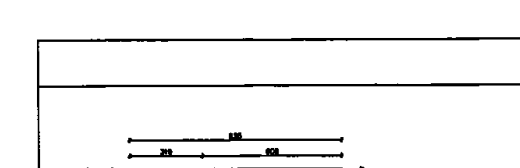

תכנית קומת קרקע
קנה מידה 1:200

שטח מסגרת	60.58	מ"ר	9.25*6.55=
שטח להורדה	5.50	מ"ר	① 2.00*2.75=
	1.98	מ"ר	② 3.95*0.50=
	0.69	מ"ר	③ (0.20*1.55)+(1.9*02)=
	0.28	מ"ר	④ 1.40*0.20=
שטח מ.מ.ד נטו	9.04	מ"ר	⑤ 2.74*3.30=
שטח קירות	3.08	מ"ר	12.12-9.04=
שטח מ.מ.ד ברוטו	12.12	מ"ר	9.04+3.08=
שטח מ.מ.ד להורדה	12	מ"ר מקס'	
סה"כ ההורדות	20.45	מ"ר	
סה"כ השטח	40.13	מ"ר	

חישוב שטח קומה : קומה ראשונה מוצע

תכנית קומה ראשונה
קנה מידה 1:200

שטח מסגרת	60.58	מ"ר	9.25*6.55=
שטח להורדה			
	5.50	מ"ר	① 2.75*2.00=
	1.98	מ"ר	② 3.95*0.50=
	0.69	מ"ר	③ (0.20*1.55)+(1.9*02)=
	0.28	מ"ר	④ 1.40*0.20=
שטח מ.מ.ד נטו	9.04	מ"ר	⑤ 2.74*3.30=
שטח קירות	3.08	מ"ר	12.12-9.04=
שטח מ.מ.ד ברוטו	12.12	מ"ר	9.04+3.08=
שטח מ.מ.ד להורדה	12	מ"ר מקס'	
סה"כ ההורדות	20.45	מ"ר	
סה"כ השטח	40.13	מ"ר	

התפלגות הדירות:

דירה מס' 2 — ① 3.55*4.56= מ"ר 16.19

חישוב שטח קומה : קומה שניה מוצע

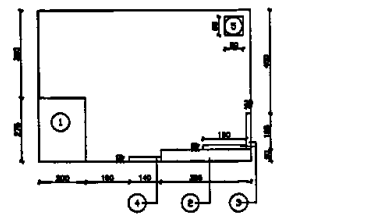

תכנית קומה שניה
קנה מידה 1:200

שטח מסגרת	60.58	מ"ר	9.25*6.55=
שטח להורדה			
	5.50	מ"ר	① 2.75*2.00=
	1.98	מ"ר	② 3.95*0.50=
	0.69	מ"ר	③ (0.20*1.55)+(1.9*02)=
	0.28	מ"ר	④ 1.40*0.20=
	0.64	מ"ר	⑤ 0.80*0.80=
סה"כ ההורדות	9.09	מ"ר	
סה"כ השטח	51.49	מ"ר	

חישוב שטח קומה: קומת גג מוצע

תכנית חדר על הגג
קנה מידה 1:200

	8.32	מ"ר	① 3.2*2.6=
	20.92	מ"ר	② 4.65*4.5=
שטח חדר על הגג	29.24	מ"ר מקס'	
שטח מסגרת	60.58	מ"ר	9.25*6.55=
שטח להורדה			
	5.5	מ"ר	③ 2.0*2.75=
	0.28	מ"ר	④ 0.20*1.4=
	1.98	מ"ר	⑤ 3.95*0.5=
	0.69	מ"ר	⑥ (0.2*1.55)+(1.9*0.2)=
שטח משותף	6.30	מ"ר	⑦ 1.40*4.50=
מרפסת הגג	16.59	מ"ר	60.58-43.99=

סה"כ ההורדות 14.75 מ"ר
סה"כ חדר על הגג 29.24 מ"ר
סה"כ מרפסת הגג 16.59 מ"ר
סה"כ שטח (חדר + מרפסת) 29.24+16.59=45.83 מ"ר
היחס בין החדר על הגג לשטח הגג 29.24/45.3=64.54%

טבלת התפלגות דירות:

מס'	שטח הדירה ללא מ.מ.ד	מ.מ.ד	סה"כ	חדר על הגג	סה"כ	מרפסות
1)	18.12+40.13= 58.25	12	71.25	—	71.25	—
2)	22.01+51.49=	12	85.50	29.24	114.74	16.59

מפה טופוגרפית
1 : 250

תל-אביב
גוש : 6135
חלקה : 43(חלק)
כתובת : רח' לח"י 35
הוכן עבור : חילבה ישעיהו
מטרת המדידה : הגדרת מגרש משני עפ"י תב"ע 2215
שם הבעלים כרשום בנסח טאבו+מס' ת.ז : מועלם טל 032021289

שטח לפי נסח :
שטח החלקה כולה : 3.575 ד.מ.
בעלות בחלקים(כרשום בנסח טאבו) : מועלם טל 174/2150
בעלות במ"ר : 87
שטח מדוד(מ"ר) : 87

שטח מגרש משני : 0.87 ד.מ.
שטח לגריעה : ד.מ.

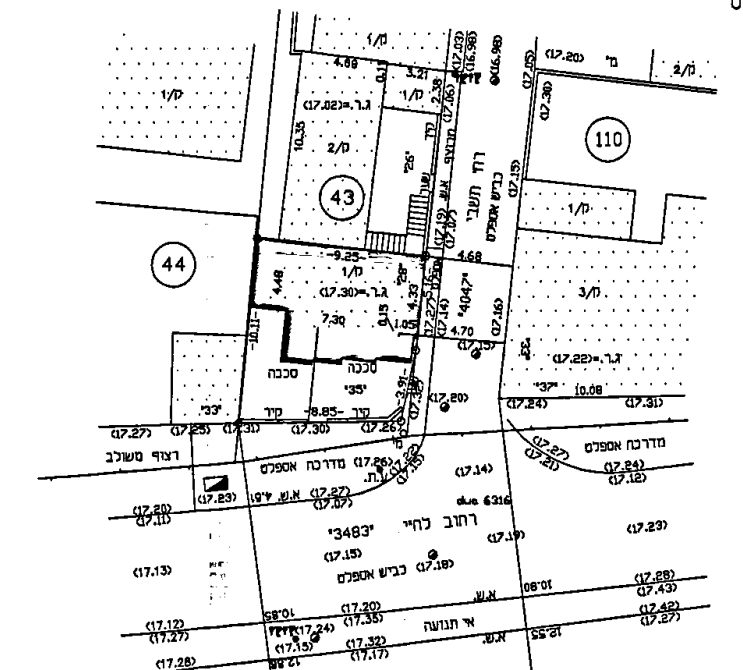
161 700
161 675
161 650
130 525
130 550
130 575
110
43
44
ק/1
ק/2
ק/3
רח' תשבי
כביש אספלט
מדרכה אספלט
רחוב לח"י
כביש אספלט
אי תנועה
מדרכה מרוצפת
יסוד + ג.ברזל
סככה

לא לצרכי רישום

תרשים הסביבה 1:1250

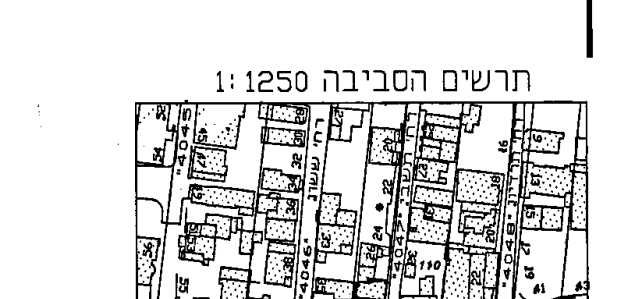
רח' לח"י
3843
4045
4046
4047
4048
3672

הנני מצהיר בזה שהמפה נעשתה לפי חוק התכנון והבניה, התקנות וההנחיות של עיריית תל-אביב-יפו.

תל אביב
תאריך : 2.12.2010

י.אברבוך מודד מוסמך
רשיון מס' "461"
חב' אברבוך ושותי מודדים מוסמכים בע"מ
רח' דיזנגוף 190, תל-אביב טל 5235891, 03-5226791

הערות:
1. המספרים בסוגריים מציינים גבהים.
2. הגבהים מבוססים על נ.ק. עירונית מס' 187 שגובהה 17.549 מ'.

עיריית תל - אביב - יפו
מינהל ההנדסה , אגף רישוי ופיקוח על הבנייה
חוק התכנון והבנייה התשכ"ה-1965
בקשה להיתר בנייה או לשימוש במקרקעין

לכבוד
☐ הועדה המקומית לתכנון ולבנייה
☒ רשות הרישוי המקומית

מס' תיק הבניין 3843-035

א. פרטי הנכס והמבקשים

כתובת	רחוב	מס' בית	גוש	חלקה
	לח"י	35	6135	43

	שם משפחה / שם פרטי	מס' זהות	רחוב ומספר בית / ישוב	טלפון
מבקש 1	מועלם טל	032021289	שד' הקונגרס 41, רמת גן	0507253283
בעל הזכות בנכס	מועלם טל	032021289	שד' הקונגרס 41, רמת גן	0507253283
עורך הבקשה הראשי	פדרמן אליה	051656841	ניסים גאון 30, אלעד	052-2948324
מתכנן שלד הבניין	חן אילה	5201544	הגאון אליהו 14, רמת גן	03-6774097

ב. מהות הבקשה
☒ בקשה לתוספת בנייה
☒ תוספת בחדר על הגג
☒ שינוי מיקום מבנה בשטח ללא תוספת שטח
שטח הדירות לאחר התוספות יהיה 235.6 מ"ר

ג. מפרט – תיאור הבקשה
1. מבנה מגורים בן 3 קומות+ מרתף וחדר על הגג

שטח המגרש 87 מ"ר; שטח הבנייה 235.6 מ"ר; אחוז הבנייה 270.78 %

הקומה/המפלס							
מרתף -3.00		52.13	12.00	51.75	59.46		
קרקע +0.00	40.13	-0.36	39.75	45.68	12.00	51.75	59.46
קומה א' +3.00	40.13	-0.36	39.75	45.68	12.00	51.75	59.46
קומה ב' +6.00	51.49	-0.36	51.11	58.74		51.11	58.74
קומת גג +9.20	17.29	11.96	29.24	33.60		29.24	33.60

ח. מספר יחידות דיור

15/01/2015

סיכום בדיקה תחנה פיקוח בניה בקשה 20150044 לכתובת לח"י 35

החלטת תחנה מ-15/01/2015 : תוכנית תואמת את המצב בשטח

תוכנית תואמת את המצב בשטח המבוקש בבניה:

מטפל: מאיר ראובן

האינג' ראובן מאיר
מהנדס מפקח
מח' פיקוח על הבניה
עיריית תל-אביב - יפו