

מפה טופוגרפית

תל-אביב

גוש : 6135

חלקה : 43 (חלק)

כתובת : רח' לחיי 35

הוכן עבור : חילבה ישעיהו

מטרת המדידה : הגדרת מגרש משני עפ"י תב"ע 2215

שם הבעלים כרשום בנסח טאבו+מס' ת.ז : מועלים טל 032021289

שטח לפי נסח :

שטח החלקה כולה : 3.575 ד.מ.

בעלות בחלקים כרשום בנסח טאבו : מועלים טל 174/7150



בעלות במ"ר : 87

שטח מדוד (מ"ר) : 87

שטח מגרש משני : 0.87 ד.מ.

שטח לגריעה : ד.מ.

תרשים הסביבה 1:1250

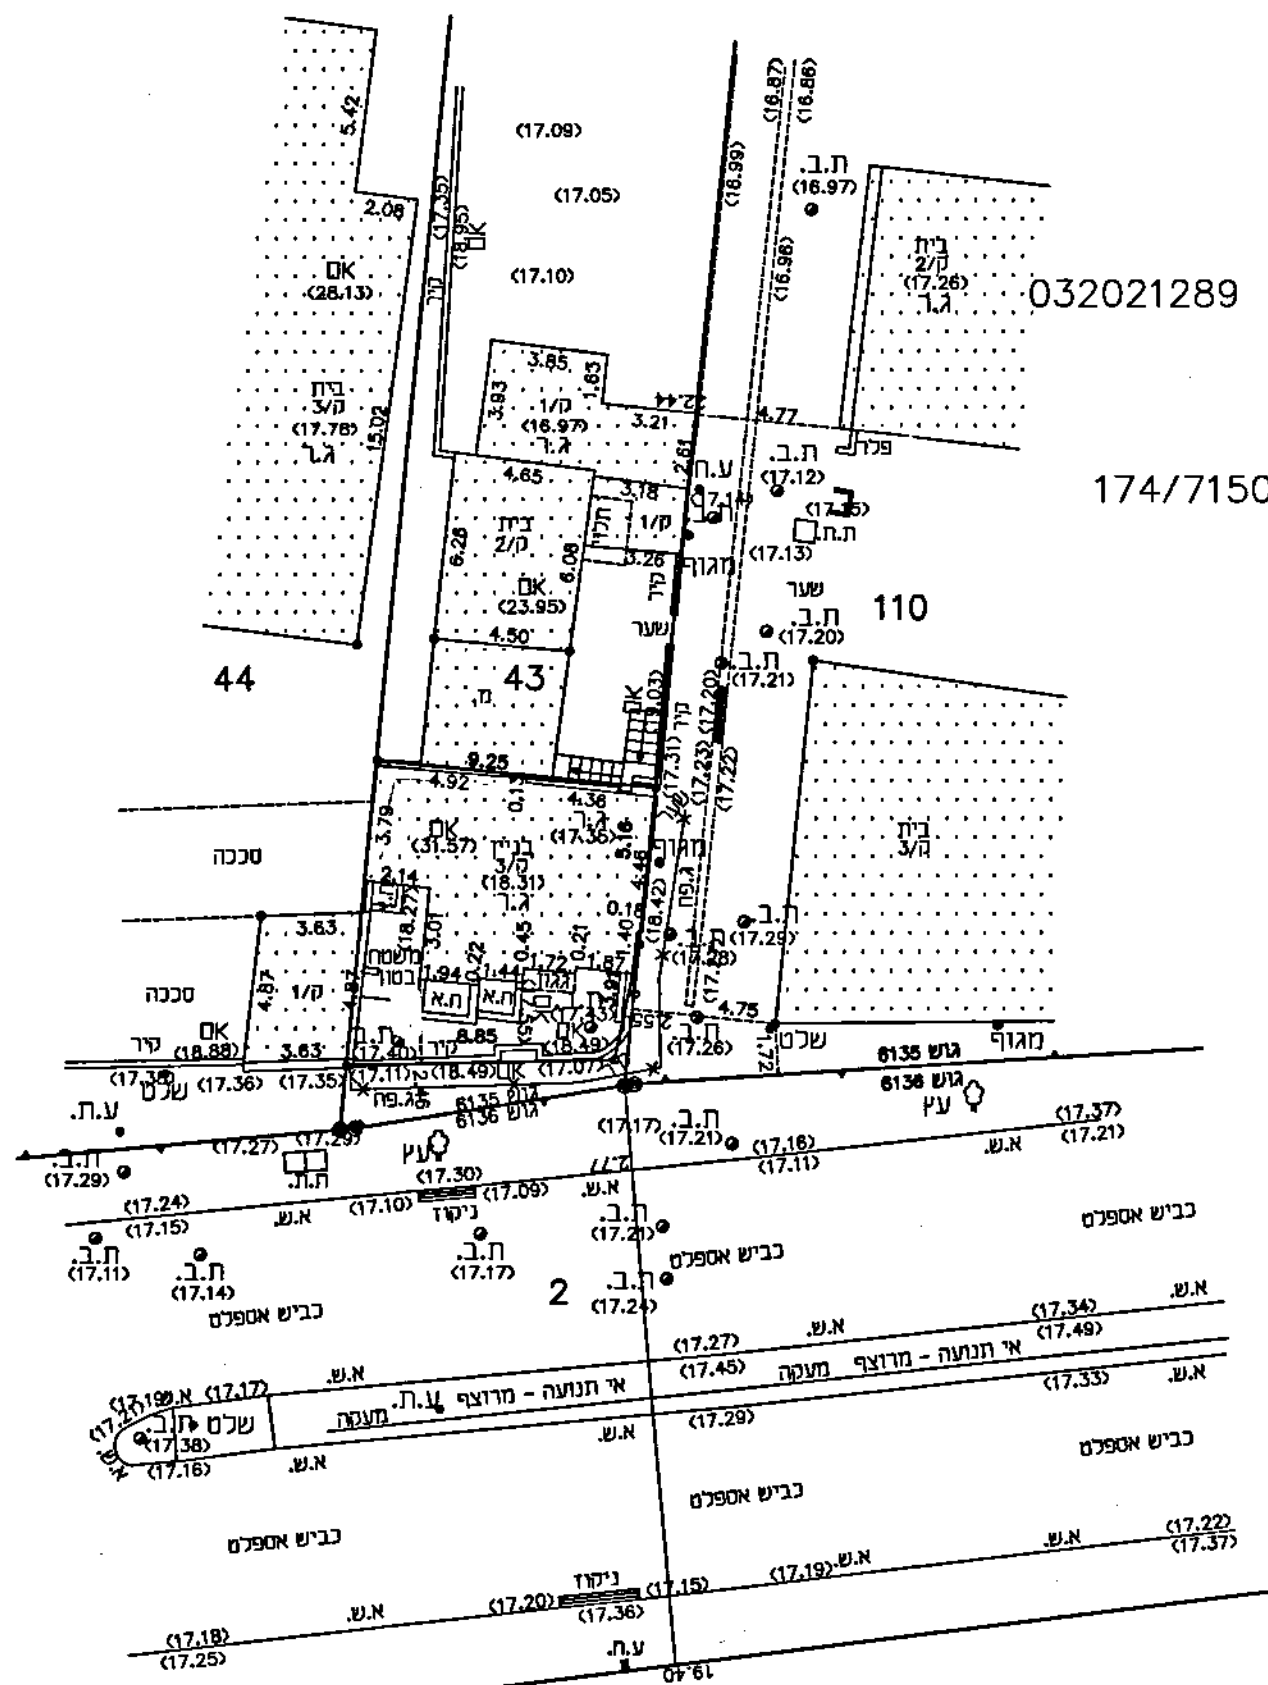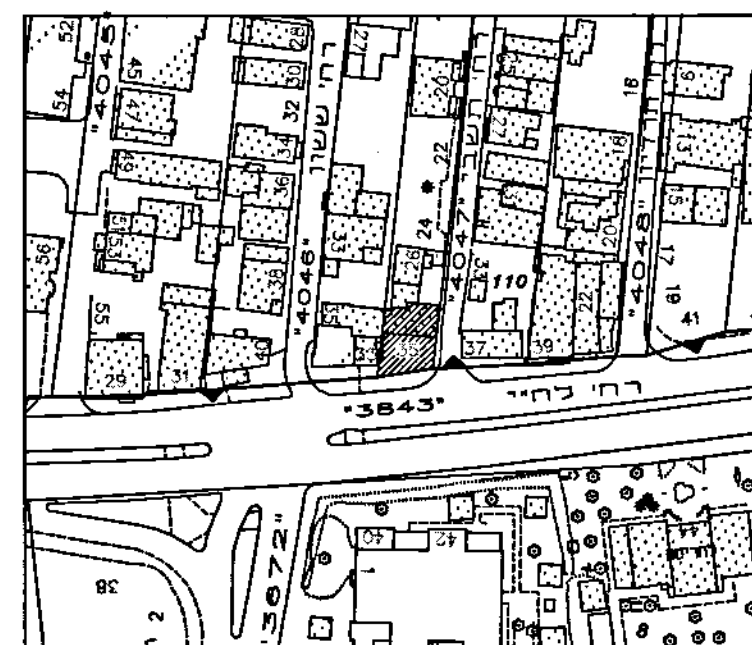


המפה עודכנה בתאריך 15.02.2015
המפה עודכנה בתאריך 23.06.2014

לא לצרכי רישום

אני מאשר בזה כי מפה זו היא העתק נכון של המפה הטופוגרפית שהכנתי על סמך מדידה שהסתיימה ביום 23.04 שנת 2014 וכי כל הפרטים שצוינו במפה הם מדויקים ודרגתה היא א', המפה בוצעה בהתאם לתקנות המודדים (מדידה ומיפוי) התשנ"ח-1998.

מסארוה חוסאם - מודד מוסמך מ.ר. 894
תייבה משולש 40400 טל. 0522-650723
טלפ. 09-7990140
פקס. 09-7996748
EMAIL-MHMEDEBEZE@INT.net
הנדסת מדידות

קנה מידה 1:250

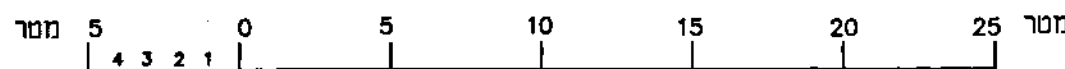

- הערות
1. המספרים בסוגריים מציינים גבהים.
 2. הגבהים מבוססים על נ.ק. עירונית מס' 187 שגובהה 17.549 מ.
 3. המפה קשורה לנקודות בקרה YKS 174 YKS 175
 4. התכנית מבוססת על תצליר תנ"מ