

①

37 316.3

3A7 / 4cc / 125/3

רשינו 777
1999



רשם הקבלנים

רשיון קבלן

לעבודות הנדסה בנאיות

מס' קבלו	מס' יחיד	מס' קבלו	מס' יחיד
21741	מחאגנה מוחמד	25858226	
31.12.99	אום אל- פחם1001		1
בתוקף עד	מיקוד	שם הישוב	כתובת

הנ"ל רשום בפנקס הקבלנים לפי חוק ורישום קבלנים לעבודות הנדסה בנאיות תשכ"ט-1969, ורשאי לבצע עבודות הנדסה בנאיות כדלקמן:

סניל	תאור	קב'	סיו
100	בניה	ג	1

0*082
 0/40/27 82 502092
 760208 000000 000000
 000000 000000 000000

תאריך תחילת רישום - 12/04/1999

חותמת הבנק

380.00 | אגרת רשיון בסך

מספר חשבון בבנק הדואר: 0-05636-0


רשיון זה הוא בר-תוקף כשהוא מוחתם
בחותמת הבנק

גא לקרוא את דברי ההסבר מעבר לרשיון





ת.ר.ש.ם לסמוך קו בנין ונקודות הגובה 3843-037 תיק בנין מס' 79/14/2/1953/17
רשום מחלקת המדידות מס' 171 פנקס שדה
בנין הא' 3843 רחוב ת.ר.ש.ם בית מספר 37 ת.ב.ע. 2215
מגרש מס' 6135 גוש מס' 110 חלקה מס' 110
בנין כ.מ.ה.ת.ש.י קו 3843
גובה הכביש בעתיד כ.מ.ה.ת.ש.י הגובה המסומן לפי תכנית

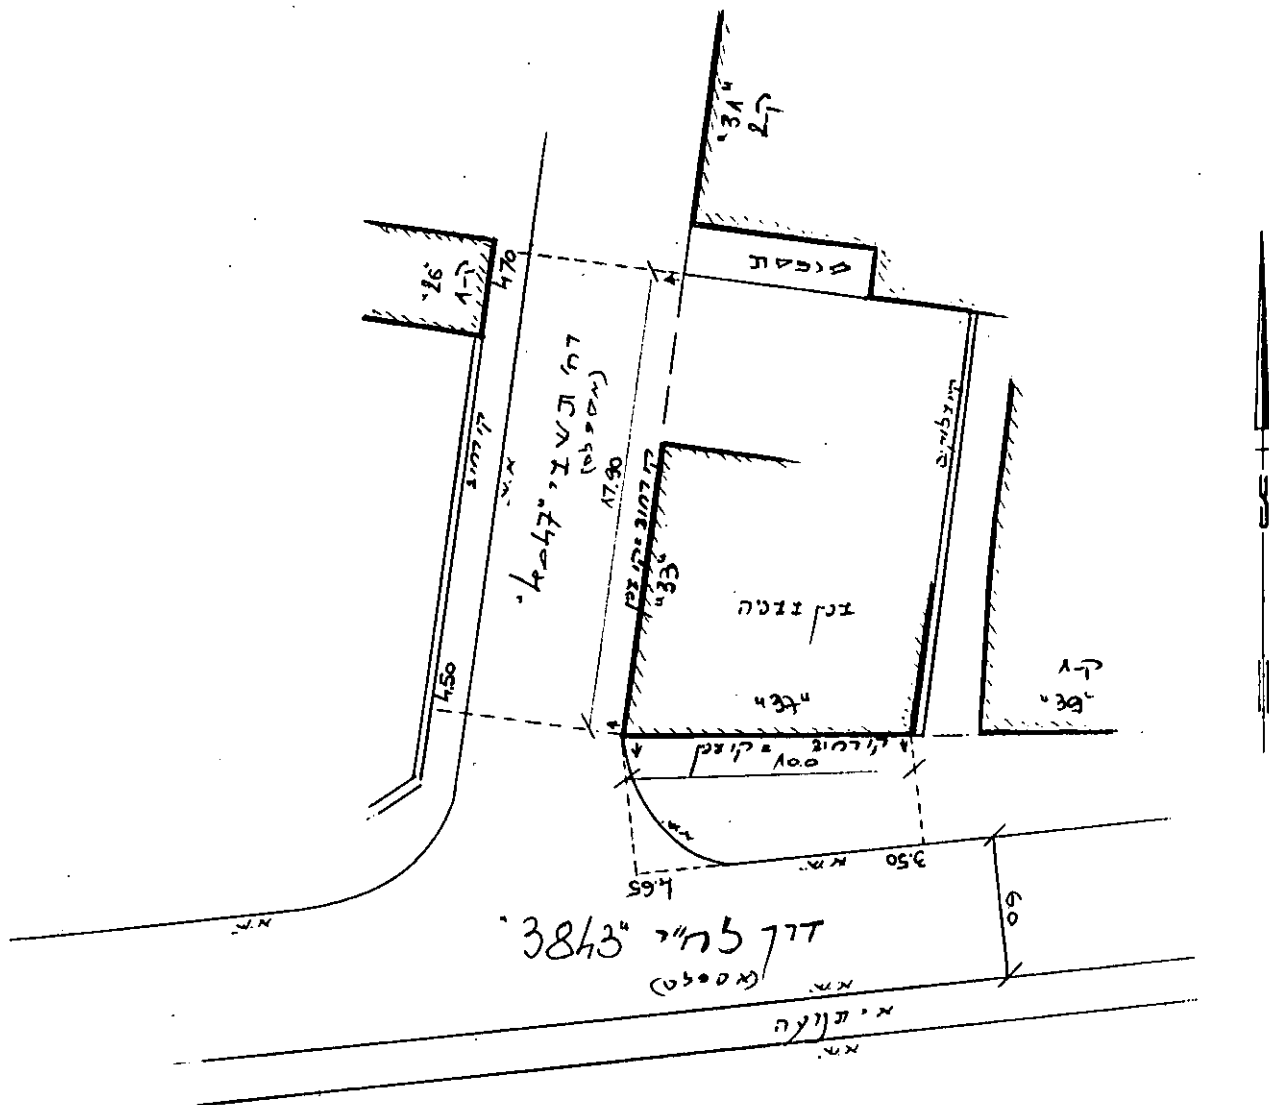

הערות: _____
סומן במקום ע"י 7.12.53 ביום 3.05.1953 בוקר ע"י [Signature]
תאריך 4.05.1953

מנהל מח' המדידות

העתק תרשים זה עכלתי ביום _____

51 451

יחידת צמיד

22.6.99

יצחק דודוב
מרחוב מחרוזת 1 תל אביב

מאת:

לכבוד
מחלקת פיקוח ובנייה
עיריית תל אביב יפו.

א.ג.מ.,

הנידון: התפטרות

הנני להביא לתשומת לבכם כי אני מהנדס יצחק דודוב, אחראי
לשעבר לביצוע שלד, התפטרתי מיום 22.06.99.

בקשר לאחריותי למקום זה שברחוב לחייה-37 תל אביב.
הקבלן עשה קידוח 30 סמ"ר במקום 50 סמ"ר, עומק
הקידוח הקבלן עשה 4 מטר במקום 7 מטר לפי הדרישה של
המציאות במקום שאני דורש התפטרות.


בכבוד רב

יצחק דודוב
מהנדס אחראי לשעבר לביצוע שלד

1

עוות תיאורית
מינהל הנדסה
מח' פיקוח על הבנייה
מתקבל ביום
התימה.

27/6/00

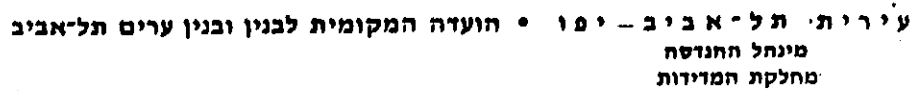

תרשים לסמון קו $\frac{\text{בנין}}{\text{גבר}}$ ונקודות הגובה

[illegible]


סומן במקום ע"י ז"י סגור סייל ביום 3.05.1999 בוקר ע"י  4.05.1999 תאריך

אשר יצאנו ממצרים

51 451

מפה טופוגרפית

1:250

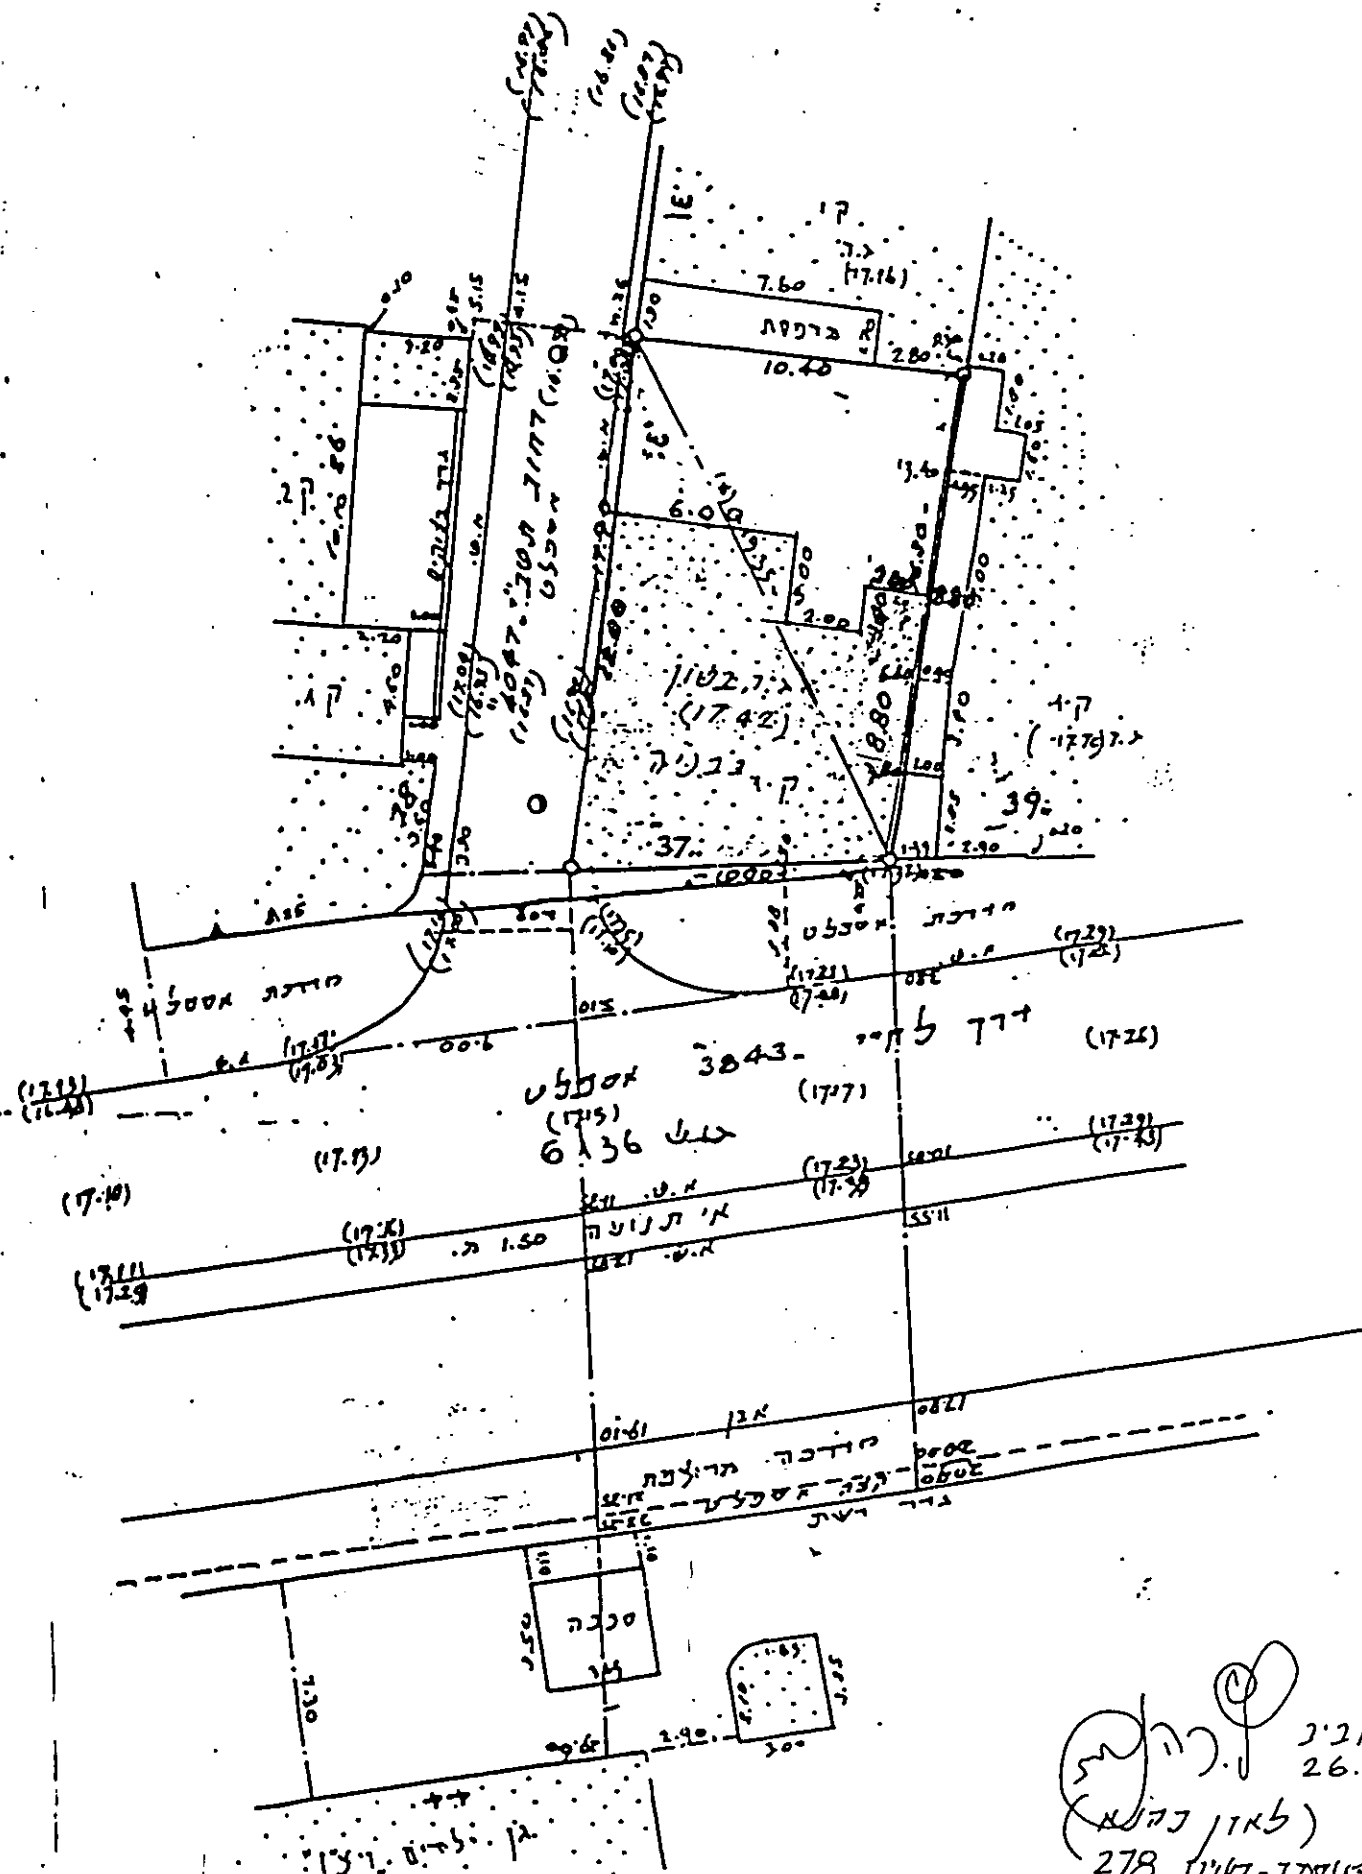

תל אביב - יפו

גוש 6135


חלקה 100 (חלק)

השטח 174 מ"ר - מדוד

השטח לפני נסח 220 מ"ר

הוכן בטבל : מר. ששון

תל אביב - יפו 1:1250

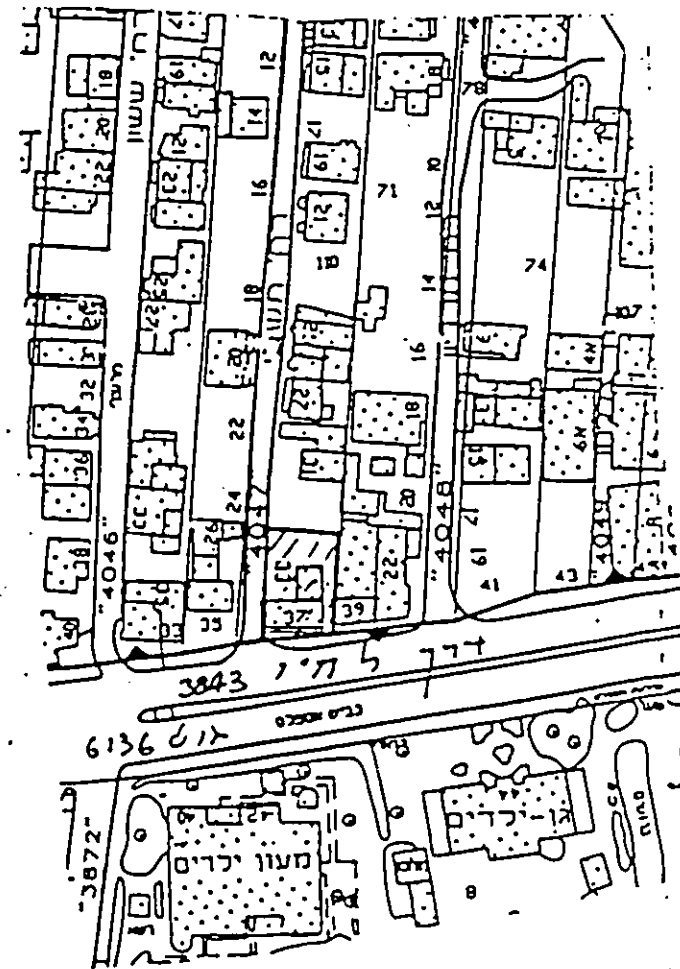

אין מאשר שהתפה נעשתה לפי חוק תכנון והבניה
הודאית והנחיות עדיית תל אביב-יפו

תל אביב
26.04.1999
(לאון כהן)
מודד מוסמך-דשון 278
ד"ר צבטונסקי 152
תל אביב

37
052-426251

1/200

לא לצדכי די שום