PRODUCED BY AN AUTODESK EDUCATIONAL PRODUCT

פרטי הבקשה להיתר:
מספר פנייה: 27245
כתובת: תרדיון 22
תאריך הדפסה: 18/05/2024

תצהיר

אני החתום/ה מטה: אלפרוביץ זאב
בעל/ת ת.ז. 065121402
מצהיר/ה כי:

1. ביום 26/09/2022 הגשתי לעיריית תל אביב קבצי המחשב במסגרת הגשת בקשה להיתר בניה בפניה שמספרה 27245
2. את הקבצים הניל, המפורטים ברשימה להלן, חתמתי בעצמי בחתימתי האלקטרונית.
3. רשימת הקבצים:

100_lechi11new1-Model.dwf
150_lechi.dwg
1500_lechi11new1-Model.dwf
160_lechu11-demo.dwg
1800_למשח תרבח.pdf
2000_ילניגרוא ןוידרת השיבר סמ.pdf
2100_east.jpg
2100_north.jpg
2100_south.jpg
2100_west.jpg
2100_םינפב 1.jpg
2100_םינפב.jpg
2200_Nesach26589620230624160901619.pdf
2200_permit eti.jpg
2200_permit zeev.pdf
2200_sagi id.jpg
2200_WhatsApp Image 2024-04-07 at 20.45.30_54790613.jpg
2320_Color 1325.pdf
2380_260124 קית םימוסרפ.pdf
2380_קית סרוק.pdf
2380_ריהצת לע םודעה.pdf
2500__nas01_rishuymekuvan_prod_HelpDocument_PgishatYeutzPtichatBakasha (11).pdf
2500__nas01_rishuymekuvan_Prod_HelpDocument_PgishatYeutzPtichatBakasha (4).pdf
2500_100-lechi11new1-Model.dwf
2500_achuzi bniya.docx
2500_demo1.pdf
2500_demo2.pdf
2500_הינב תויוכז .docx
500_fire road.docx
500_tradion-fire Model.pdf
5200_lechi11-Model.dwf
600_SRV_6135-71B-Model.dwf
6100_.pdf
7300_SRV_6135-71B Model.pdf
7600_תורגא.pdf
7700_רוטפ החבשהמ תנוכשב הווקתה.pdf

4. השוותי בין התכנית המצויה בקבצים הניל לבין התכנית המצויה בגיליון הנייר עליו מודבק תצהיר זה ומצאתי כי התכנית זהה בשניהם (בקבצים ובנייר).

שם ____ תאריך ____ חתימה ____

פניה 27245
תאריך יצירה 18.05.2024
בקשה 24-0203
תל אביב יפו TEL AVIV YAFO

לתשומת לב החותם על תכנית הבקשה להיתר:

1) אין לחתום על תכנית הבקשה להיתר, אלא אם היא חלק מהדפסה רציפה (גרמוקשה / הרמוניקה) בנייר הכוללת את טופס1(פרטים ונתונים מילוליים ומספריים של הבקשה להיתר, חתום בחותמת מים של עיריית תל אביב) ותכנית הבקשה להיתר (תכניות, חתכים, חזיתות וכד').

2) לאחר שתפתח בקשת רישוי במחלקת רישוי בניה תשלח אליך הודעה עם מספר הבקשה להיתר. לאחר קבלתה, עליך להכנס לתיק הבניין בגנזך ההנדסה האינטרנטי באתר עיריית תל אביב ולוודא שהתכנית הנוכחית עליה חתמת כאן זהה למסמכי הבקשה להיתר כפי שהם מופיעים בתיק הבניין האינטרנטי.

הסכמת בעלי זכות בנכס לבקשה להיתר בניה כנדרש בחוק התכנון והבניה אנו מסכימים לבקשה להיתר אשר על תכניתה אנו חותמים כאן:

מספר סידורי	גוש	חלקה	חלקת משנה	שם רחוב	מספר בית	מספר דירה	קומה	שם פרטי	שם משפחה	מספר זהות	חתימה	תאריך חתימה
1												
2												
עיריית תל־אביב־יפו
מינהל הנדסה
אגף רישוי ופיקוח על הבנייה

חוק התכנון והבניה התשכ"ה- 1965
תקנות התכנון והבניה (בקשה להיתר תנאיו ואגרות) התש"ל - 1970
על פי טופס 1 תקנה 2(א)

א. פרטי הנכס והמבקשים

בקשת מידע: 23-00684
תיק בניין: 3843-039

כתובת
תרדיון
בית 22
גוש/חלקה: 71/6135
שטח מגרש/חלקה: 101.00 מ"ר
שטח בניה מבוקש: 243.86 מ"ר
אחוז בניה: 241.45

תכניות החלות על המקום והן מקור לשטחים מבוקשים
2215
2215א1
ג3
ע1
ע1א
תמ"א23/א4

פרטים אישיים	שם משפחה שם פרטי שם חברה או תאגיד	רחוב / מספר בית ישוב מיקוד
מבקש	שגיא אליגון	סיוון 6 תל אביב - יפו 6762006
בעל זכות בנכס	שגיא אליגון	סיוון 6 תל אביב - יפו 6762006
עורך ראשי	זאב אלפרוביץ	שפרינצק 12 כפר סבא 4441224
מתכנן שלד	אתי בוחניק	משעול גיל 1 כפר סבא 4428144

ב. מהות הבקשה

סוג הבקשה
בניה חדשה בניין מגורים לא גבוה (עד 13 מ')

שימוש
מגורים

ג. מפרט תאור הבקשה

הריסה
מספר קומות להריסה (סה"כ הקומות במבנה או מספר מבנים על המגרש): 1
שטח הריסה (מ"ר): 54.02

פירוט המבוקש במרתפים
מרתף אחד בלבד
מחסן
חדרי עזר

פירוט המבוקש בקומת הקרקע
אולם כניסה
חדר אשפה

פירוט המבוקש בקומות
כמות קומות מגורים: 3
כמות יח"ד מבוקשות: 2

פירוט המבוקש על הגג
חדרי יציאה
קולטי שמש
חדר מדרגות כללי

פירוט המבוקש בחצר
גינה
שטחים מרוצפים
גדר בגבולות מגרש בגובה (מטר): 28.00

פירוט נוסף
בית למגורים בן 2 יח"ד המורכבות קומת קרקע עם מרתף לאחסון ומשחקים וקומה ראשונה עם חדר יציאה לגג מרפסת זיזית. שתי היח"ד כוללות ממ"ד וכניסות מחדר מדרגות משותף. חצר משק לאצירת פסולת ביתית ופילר חשמל. חיבור לרשת המים בצמוד לחיבור קיים.

חפירה
נפח חפירה (מ"ק): 276.00

גן ילדים
קיים ממ"ד: לא

צובר גז
העבודות המבוקשות בהיתר כוללות הוספת צובר גז חדש או העתקה של צובר קיים: לא

הגורם עבורו מתבצעת העבודה
גורם פרטי

ד. חומרי הבנייה

סוג הבניה
רגילה

קירות חיצוניים
בלוקים

חומרי גימור
טיח

תקרות
בטון מזוין

גג
בטון מזוין

גדרות
בטון
רשת

אורך גדר
קיים: 6.5 מ"א
מוצע: 70 מ"א
סה"כ: 76.5 מ"א

מקרא חומרים (צבעים)
בטון או בטון מזוין: כחול
בלוקים או לבנים: אדום
עץ: חום
זכוכית: סגול
הריסה: צהוב
בניה קיימת: אפור

ו. קווי בנייה

לרחוב חנינא בן תרדיון קומה 1 מוצע: 0
לצד מוצע: 0

ז. מספר יחידות דיור

מספר יחידות הדיור הקיימות:
מספר יחידות הדיור לביטול/הריסה: 2
מספר יחידות הדיור המבוקשות ששטחן עד 120 מ"ר: 2
מספר יחידות הדיור המבוקשות ששטחן מעל 120 מ"ר:
מספר יחידות הדיור המותרות: 2

ח. פרטי הבנייה - לשימוש הלשכה המרכזית לסטטיסטיקה

שטח הבניה ברוטו לפי היעוד
למגורים: מגורים בקומות קרקע 1 וחדר יציאה לגג שטח: 154.94
למקלט או למרתף: שטח: 74.79
למבני עזר: שטח: 25.73
סך כל שטחי הבניה: 255.46

גודל הדירות לפי מספר חדרים
חדר 5: מספר דירות: 1 מספר מגורים: 5
מעל 6: מספר מגורים: 3
סה"כ מספר דירות: 2
סה"כ מספר מגורים: 8

ט. הבקשה מוגשת לאישור

פירוט הבקשה להקלה	נימוקי הבקשה להקלה
7.5% על הריסה	שיפור דיור
תוספת עד 6% משטח המגרש מעל ל % 100 מותרים, לצורך שיפור תכנון	שיפור דיור

ה. השטחים המבוקשים (על-פי תכני תכנית הבנייה) והמותרים לבנייה

(על-פי "אסמכתא": חוק, תקנות, תכניות) בכל מפלס בנפרד ולפי שימוש

מבנה	הקומה	מפלס	מגורים מבוקש	ממ"ד/ממ"ק/מקלט שטח שירות לשמוש מגורים מבוקש	מעברים מבואות וחדרי מדרגות לשמוש מגורים מבוקש	עובי קירות ממ"ד/ממ"ק/מקלט לשימוש מגורים מבוקש	שטח תת קרקעי נלווה מבוקש	עיקרי: סה"כ	עיקרי: % משטח המגרש	אסמכתא: תכנית ראשית/אחר	שירות: סה"כ	שירות: % משטח המגרש	סה"כ קומה: עיקרי+שירות	סה"כ קומה: % משטח המגרש	סה"כ קומה: שטחים לא מקורים
1	מרתף -1	-3.05					69.3375			עוא	69.3375	68.65	69.3375	68.65	
1	קומה 1	0.00	57.4652	9.1800		3.5173		57.4652	56.90	2215א1	12.6973	12.57	70.1625	69.47	
1	קומה 2	3.20	49.0800	9.1800	8.3632	3.5173		49.0800	48.59	2215א1	21.0605	20.85	70.1405	69.45	
1	קומה 3	6.40	34.2205					34.2205	33.88	ג3			34.2205	33.88	
1	קומה 4	9.60													34.2205
	מתחת לקרקע						69.34				69.34		69.34		
	מעל הקרקע		140.77	18.36	8.36	7.03		140.77			33.76		174.52		34.22
	סה"כ		140.77	18.36	8.36	7.03	69.34	140.77			103.10		243.86		34.22

י. הצהרת עורך הבקשה הראשי

אני מצהיר על נכונות הפרטים בסעיפים א עד ט

תאריך 18 / 05 /2024 שם: זאב אלפרוביץ חתימה

זאב אלפרוביץ, אדריכל
מ.ר. 6492526
דה האז 3 ת"א
zeevalp@gmail.co

יא. חתימות נוספות

תפקיד	שם	תאריך	חתימה
מבקש	שגיא אליגון	18.05.24	שגיא
בעל זכות בנכס	שגיא אליגון	18.05.24	שגיא
מתכנן שלד	אתי בוחניק	18.05.24	

לתשומת לב החותם על תכנית הבקשה להיתר:

1) אין לחתום על תכנית הבקשה להיתר, אלא אם היא חלק מהדפסה רציפה (גרמוקשה / הרמוניקה) בנייר הכוללת את טופס1(פרטים ונתונים מילוליים ומספריים של הבקשה להיתר, חתום בחותמת מים של עיריית תל אביב) ותכנית הבקשה להיתר (תכניות, חתכים, חזיתות וכד').

2) לאחר שתפתח בקשת רישוי במחלקת רישוי בניה תשלח אליך הודעה עם מספר הבקשה להיתר. לאחר קבלתה, עליך להכנס לתיק הבניין בגנזך ההנדסה האינטרנטי באתר עיריית תל אביב ולוודא שהתכנית הנוכחית עליה חתמת כאן זהה למסמכי הבקשה להיתר כפי שהם מופיעים בתיק הבניין האינטרנטי.

יב. מינויים מטעם מבקש ההיתר

מינוי עורך הבקשה הראשי

אני ממנה בזה את זאב אלפרוביץ בעל/ת מס' זהות 065121402 הרשום בסעיף א להיות עורך הבקשה הראשי להיתר, ולייצגני לפני מוסדות התיכנון והרשויות המוסמכות בכל הנוגע לטיפול בבקשה להיתר ולקבלתו, לרבות התיקונים ככל שידרשו הרשויות המוסמכות.

מינוי עורכי בקשה לפי תחומים

אני ממנה את הרשומים להלן להיות עורכי הבקשה להיתר בתחום הפעולה כרשום ליד שמם, ולייצגני בתחום פעולתם לפני מוסדות התכנון והרשויות המוסמכות בכל הנוגע לטיפול בבקשה להיתר ולקבלתו, לרבות התיקונים ככל שידרשו הרשויות המוסמכות.

	שם משפחה שם פרטי	תחום פעילות	המען	פרטי התקשרות
1.	זאב אלפרוביץ	אדריכל	דה האז 3 ת"א	zeevalp@gmail.com
2.	אתי בוחניק	מהנדסת	סוקולוב 97 הרצליה	[illegible]
3.				

מינוי מתכנן שלד הבניין

אני ממנה בזה את אתי בוחניק בעל/ת מס' זהות 022377741 הרשום בסעיף א להיות אחראי לתכנון שלד הבניין שבעבורו מבוקש ההיתר, להגיש לוועדה המקומית לרשות הרישוי המקומית את החישובים לגבי הבניין שבעבורו מבוקש היתר ולפקח פיקוח עליון על הקמת השלד.

מינוי הקבלן האחראי לבנייה

☐ אני ממנה בזה את ____ בעל/ת מס' זהות ____ ובעל תעודת רישום בפנקס קבלנים מספר ____ במדור ____ ובעל רישיון לביצוע עבודה בתוקף עד ____ לבצע את העבודה הנדונה בהיתר כמתחייב לפי כל דין.

☐ אני מצהיר, כי טרם מסרתי את ביצוע העבודה הנדונה בהיתר לידי קבלן, ומתחייב למסור אותה לידי קבלן רשום בפנקס הקבלנים, כמתחייב על פי כל דין, ולהודיע על כך לרשות הרישוי המקומית טרם התחלת ביצוע העבודה, וחתימתו של הקבלן תצורף להודעה המפרטת את פרטי רישומו של הקבלן.

מינוי האחראי לבניית שלד הבניין

☐ אני ממנה בזה את ____ בעל/ת מס' זהות ____ כתובת ____ טלפון ____ מייל ____ הרשום לעיל להיות אחראי לביצוע שלד הבניין.

☐ אני מצהיר, כי טרם מיניתי אחראי/ת לביצוע עבודות הבנייה בתחומים אלה: ____ ומתחייב לעשות זאת כמפורט בתקנות, ולהודיע על כך לרשות הרישוי המקומית טרם התחלת ביצוע העבודה.

מינוי אחראים לביקורת

☐ אני ממנה בזה את הרשומים להלן להיות אחראים לביקורת על ביצוע עבודות בתחום הפעולה כרשום ליד שמם

	שם משפחה שם פרטי	תחום פעילות	המען	פרטי התקשרות
1.	אתי בוחניק	קונסטרוקציה	סוקולוב [illegible]	[illegible]
2.	זאב אלפרוביץ	אדריכלות	דה האז 3 ת"א	0545455559
3.				

אני מצהיר כי טרם מיניתי אחראי/ם לביקורת על ביצוע עבודות הבנייה את כולם או את חלקם בתחומים האלה: ____
ומתחייב לעשות זאת כמפורט בתקנות, ולהודיע על כך לרשות הרישוי המקומית טרם התחלת ביצוע העבודה.

חתימת המבקש על המינויים שגיא

יג. הצהרות

הצהרות עורכי הבקשה כולל הצהרות עורך הבקשה על לחץ המים

אנו החתומים מטה מצהירים בזה:
1) כל אחד מאתנו מאשר שהאמור בנוגע לרשימה שבסעיף י"ב לעיל הוא נכון.
2) כל אחד מאתנו מסכים לקבל עליו את התפקיד המיועד לו בסעיף י"ב לעיל.
3) אנו מצהירים, כל אחד בנוגע לתחום פעולתו, שיש לנו כישורים מקצועיים לערוך בקשה זו וכי בדקנו את המסמכים הנודעים לבקשה, לרבות כל תכנית הנוגעת לבקשה, וידוע לנו כי אם הצהרה זו אינה נכונה, הרי היא תיחשב מסירת ידיעה שהיא כוזבת או מטעה בפרט חשוב, כמשמעותה בסעיף 214 לחוק, וצפויים לנו העונשים הקבועים לפי כל דין.

אני זאב אלפרוביץ (עורך בקשה ראשי) אחרי/ת לכך שהבקשה, ובכלל זה נספחיה, נערכה לפי מיטב הידיעה המקצועית ובהתאם לכל חיקוק החל על הבניין או העבודה המוצעת, שכל הנתונים שנמסרו על ידי בבקשה זו נכונים ושהתכנון המוצע תואם את כל התכניות, פרט לסטיות שפורטו לעיל.

☐ אני עורך הבקשה מתכנן האינסטלציה הסניטרית, מצהיר בזאת ואחרי לכך שתכניות הבקשה בכל הנוגע לסידורים הסניטריים נערכו כדין וכי קויימו בהן הוראות החוק וההוראות למתקני תברואה התש"ל 1970 (הל"ת) לעניין זה, לרבות בדיקת לחץ המים הקיים בבניין ותיכנון בהתאם.

	תאריך	שם משפחה שם פרטי	מספר רישיון	חתימה
עורך ראשי		זאב אלפרוביץ	6492526	זאב אלפרוביץ, אדריכל מ.ר. 6492526 דה האז 3 ת"א zeevalp@gmail.co

הצהרת מתכנן שלד הבניין

אני החתום מטה אתי בוחניק מס' זהות 022377741
מהנדס רשוי מס' 73416
או הנדסאי בעל רישוי מס' ____ (ל"מבנה פשוט") מצהיר בזאת כדלקמן:
1) אני מסכים להיות מתכנן שלד הבניין הנדון בבקשה ולפקח פיקוח עליון על הקמת השלד.
2) כל אחד מאתנו מסכים לקבל עליו את התפקיד המיועד לו בסעיף י"ב לעיל.
3) ידוע לי, שאם אחרי הגשת הנתונים הסטטיים יתגלה צורך בשינוי מהותי בהם, אני מתחייב להגיש חישובים סטטיים מתוקנים מיד עם גילוי הצורך בכך.
4) אני מצהיר, כי יש לי כישורים מקצועיים לערוך בקשה זו וכי בדקתי את כל המסמכים הנוגעים לבקשה, לרבות כל תכנית הנוגעת לבקשה, וידוע לי כי אם הצהרה זו אינה נכונה, הרי היא תיחשב מסירת ידיעה שהיא כוזבת או מטעה בפרט חשוב, כמשמעותה בסעיף 214 לחוק, וצפויים לי העונשים הקבועים לפי כל דין.
5) ידוע לי כי עלי לשמור את תכנית הקונסטרוקציה לתקופה של לא פחות מ5 שנים לאחר גמר הבניה.

תאריך 18.05.24 חתימה ____

הצהרת האחראי לביצוע שלד הבניין (כאשר מונה)

אני החתום מטה (שם משפחה ושם פרטי) ____ מס' זהות ____
מהנדס רשוי מס' ____ או הנדסאי בעל רישוי מס' ____ (ל"מבנה פשוט")
מצהיר בזאת כדלקמן:
1) אני מסכים להיות האחראי לבצוע שלד הבניין.
הבניין על פי תוכניות והוראות של מתכנן השלד כפי שייתנו בכתב וכן למלא את תפקידי על פי שנקבע בכל חיקוק הנוגע להן.
2) אני מצהיר, כי יש לי כישורים מקצועיים להיות אחראי לבצוע שלד הבניין, ואני מתחייב לדאוג לביצוע שלד

תאריך ____ חתימה ____

הצהרת אחראים לביקורת (כאשר מונו)

אנו החתומים מטה מצהירים בזה:
1) כל אחד מאיתנו מאשר שהאמור בנוגע לו ברשימה שבסעיף י"ב לעיל הוא נכון.
2) כל אחד מאיתנו מסכים לקבל עליו את התפקיד המיועד לו בסעיף י"ב.
3) אנו מצהירים כל אחד בנוגע לתחום פעולתו, שיש לנו כישורים מקצועיים לערוך את הביקורת כהלכה ולדווח על תוצאותיה לרשות הרישוי המקומית, כמתחייב כל פי כל דין.
אני זאב אלפרוביץ (עורך הביקורת הראשי) אחראי/ת לכך שהביקורת תיערך על פי מיטב הידיעה המקצועית, ושכל הדיווחים לרשות הרישוי המקומית ייערכו על פי כל דין.

תאריך	שם משפחה שם פרטי	מספר רישיון	חתימה
18/ 05 24	אלפרוביץ זאב	64922526	זאב אלפרוביץ, אדריכל מ.ר. 6492526 דה האז 3 ת"א zeevalp@gmail.co
20/ 5 /2024	אתי בוחניק	73416	ת.ז. 516631132 73416
/ /			
/ /			

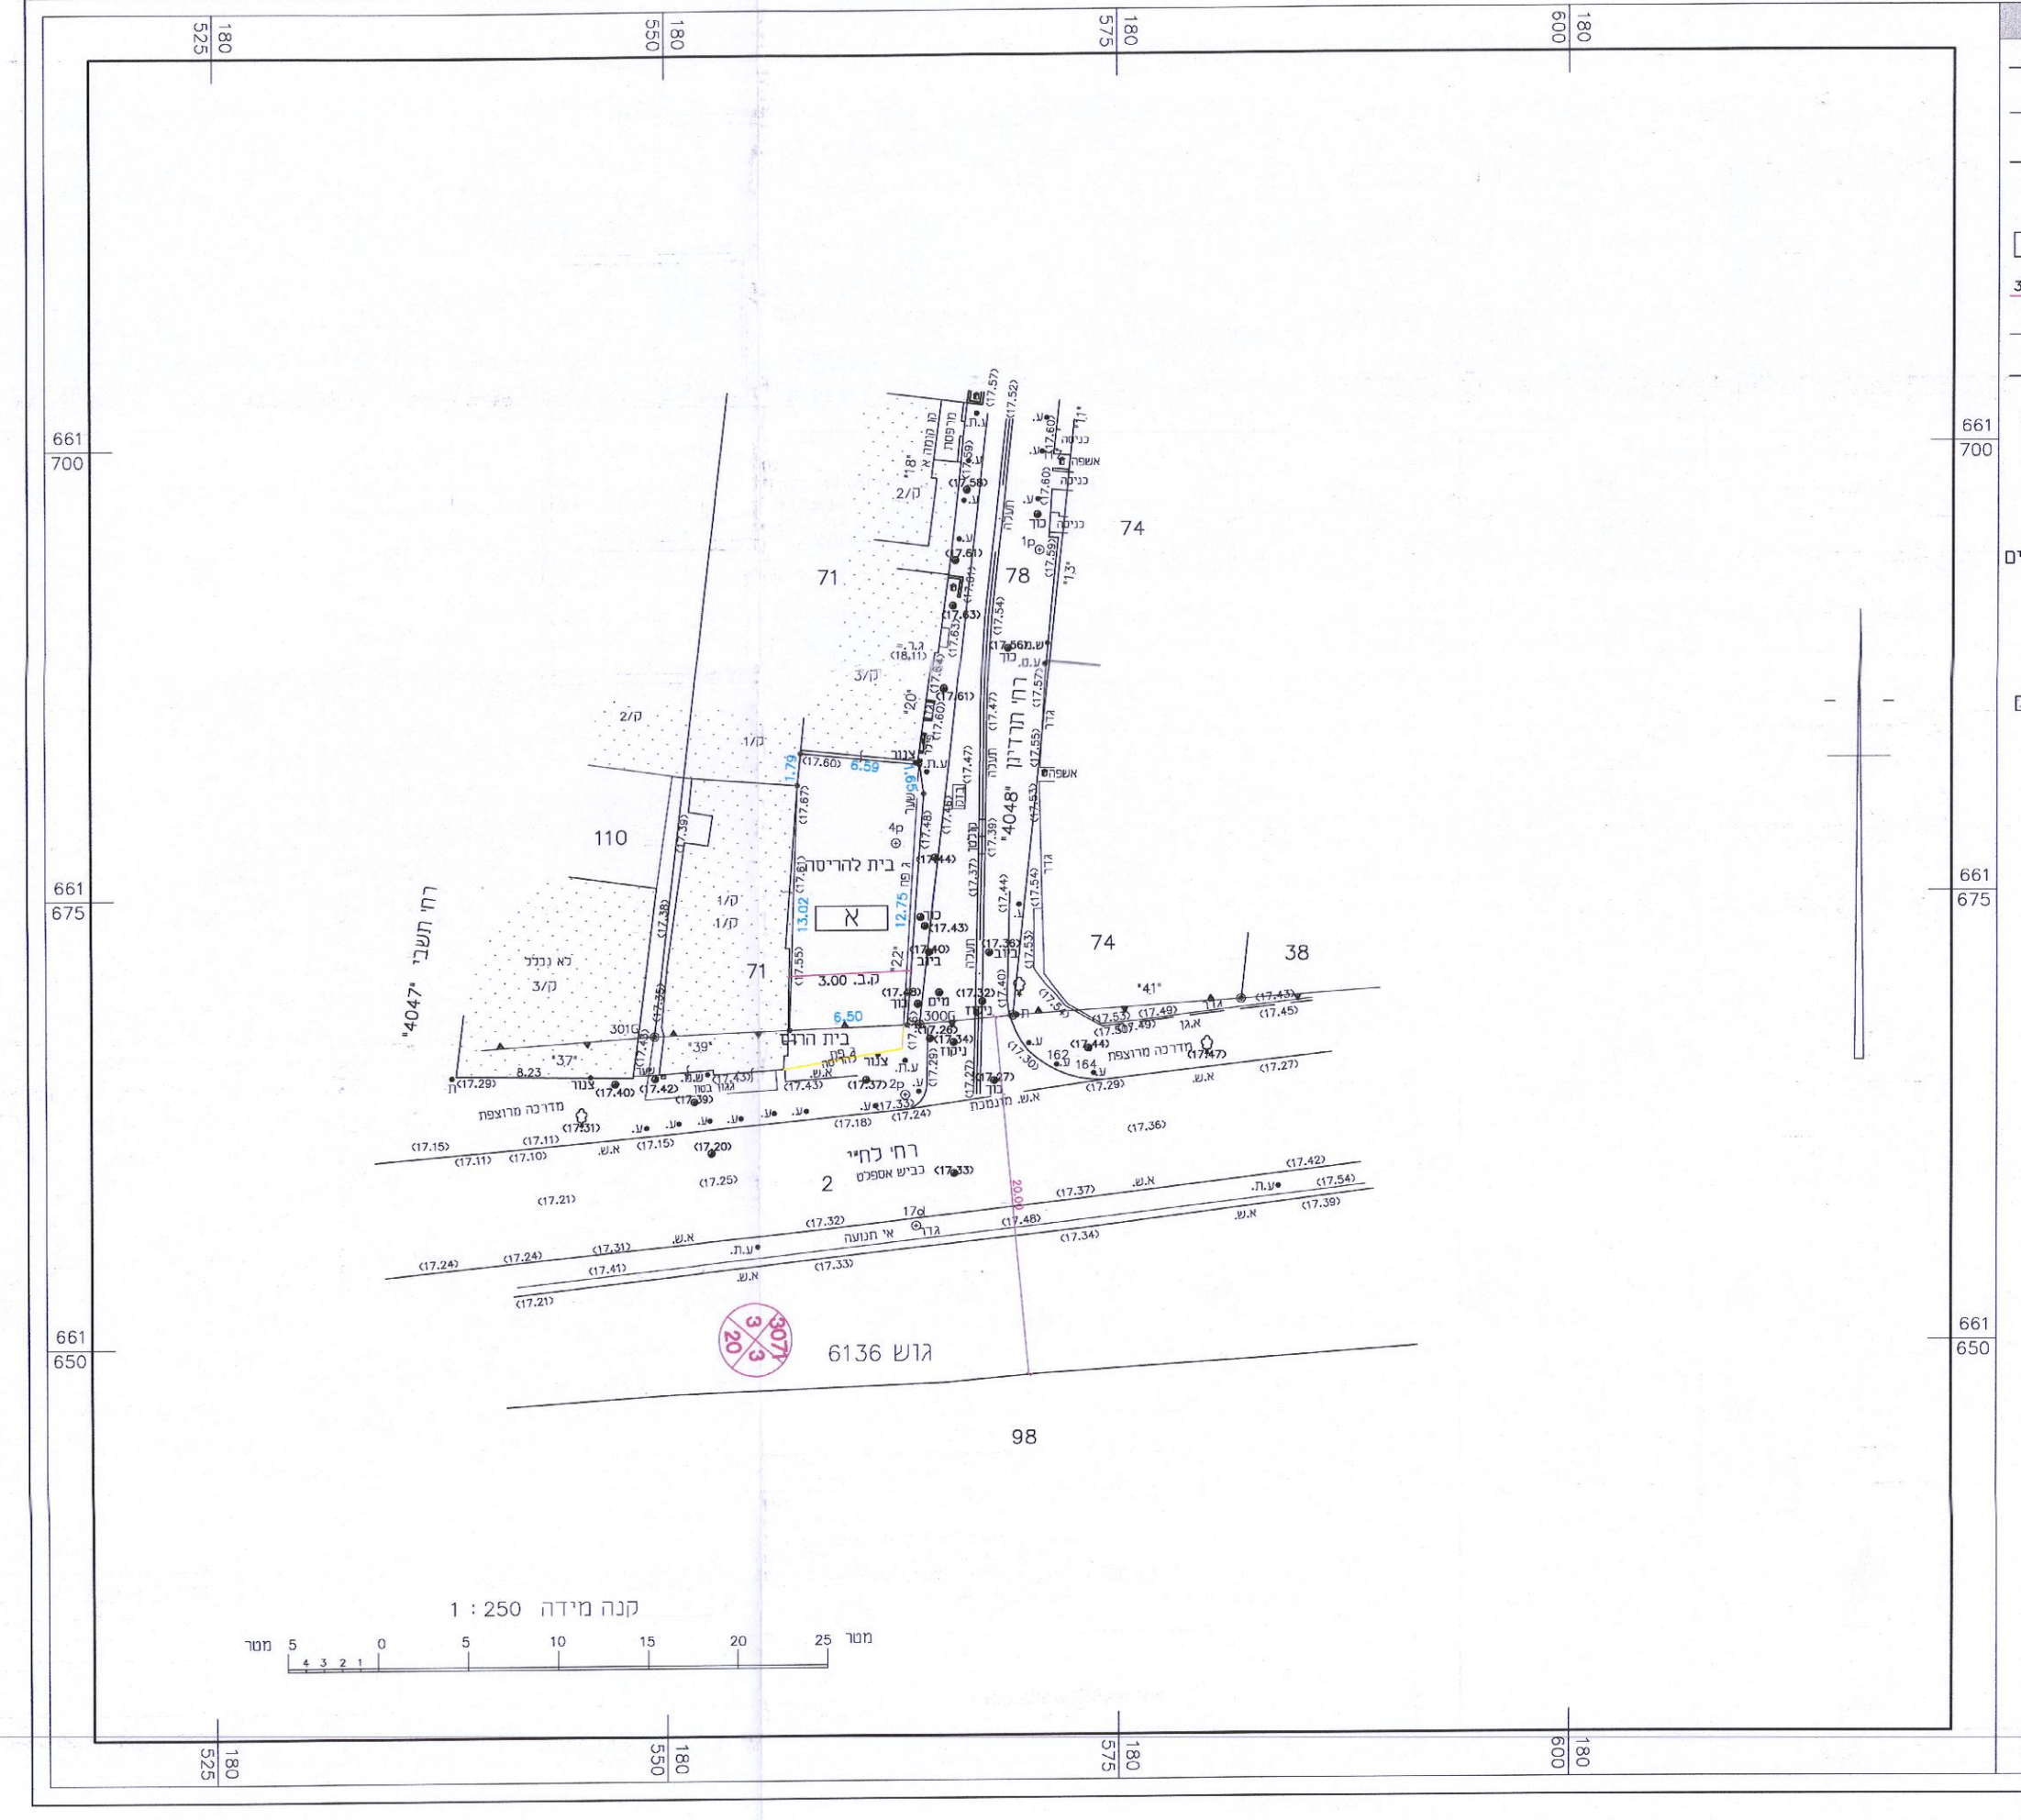

מפה להיתר בניה

ישוב	: K. TCHC	כתובת	רח' תרדיון 22 פינת רח' לחי 39
הוכן עבור	: אליגון שגיא פוליפ	מספר סידורי	: 6135-71

גוש	חלקה	בשלמות	שטח רשום(מ"ר)	תכנית מפורטת	מגרש	שטח מגרש(מ"ר)
6135	71	לא	1991	תא/2215	א	101 מדוד

הערות

1. קווי הבנין הותוו כפי שהתקבלו מעורך הבקשה, והם יאושרו על ידי מהנדס הוועדה בעת הכנת תיק המידע.
2. מס' פרויקט 1101484
בעלות : אליגון שגיא פוליפ ת.ז. 04833612 חלקים 112/1991

1. המדידה בוצעה ברשת : ישראל 2005\12
2. נקודות הבקרה שעליהן מבוססת המדידה הן : נק' 188 שגובהה (17.530)
3. גבולות החלקות חושבו מ :תצ'יר מספר 433/1941

תרשים סביבה קנה מידה 1 : 1250

מס' נקודה	קואורדינטת מזרח-מערב	קואורדינטת צפון-דרום
300G	180564.10	661667.83
301G	180549.33	661667.27

נקודות גבול מגרש או חלקה

מקרא

גבול גוש	
גבול חלקה נקודת גבול	
גבול מגרש	
מספר חלקה	80
מספר מגרש	8
קו בנין	ק.ב. 3.00
אבן שפה	א.ש.
גדר רשת	ג.ר.
גובה גדר	54.00 ג.גדר
עמוד חשמל	ע.ח.
עמוד טלפון	ע.ט.
שעון מים	שעון מים
תא ביוב	ביוב
תא מים	מים
בית קיים	

הצהרת המודד

אני מאשר כי מפה זו הוכנה ונערכה בקנה מידה 1:250 והיא העתקה נכון של המפה הטופוגרפית על סמך מדידה שהסתיימה ביום 17.04.2016
בהסתמך על בקרת איכות שביצעתי למפה זו אני מאשר את כל הפרטים ומאפייניהם שצוינו במפה, מדויקים לפי האמור :דרגת דיוק אופקי היא : 3 דרגת דיוק אנכי היא : 3
המפה הוכנה לפי תקנות המדידות (מדידות ומיפוי), התשע"ו-2016. תאריך גמר התכנית: 10.01.2023

דניאל שמוקלר — שם המודד ומענו
374 — מספר רשיון
חתימה

דניאל שמוקלר
רח' פרופי שור 19 ת"א — שם המודד ומענו
052-2563049 — טלפון
zafrira5@walla.com — דוא"ל

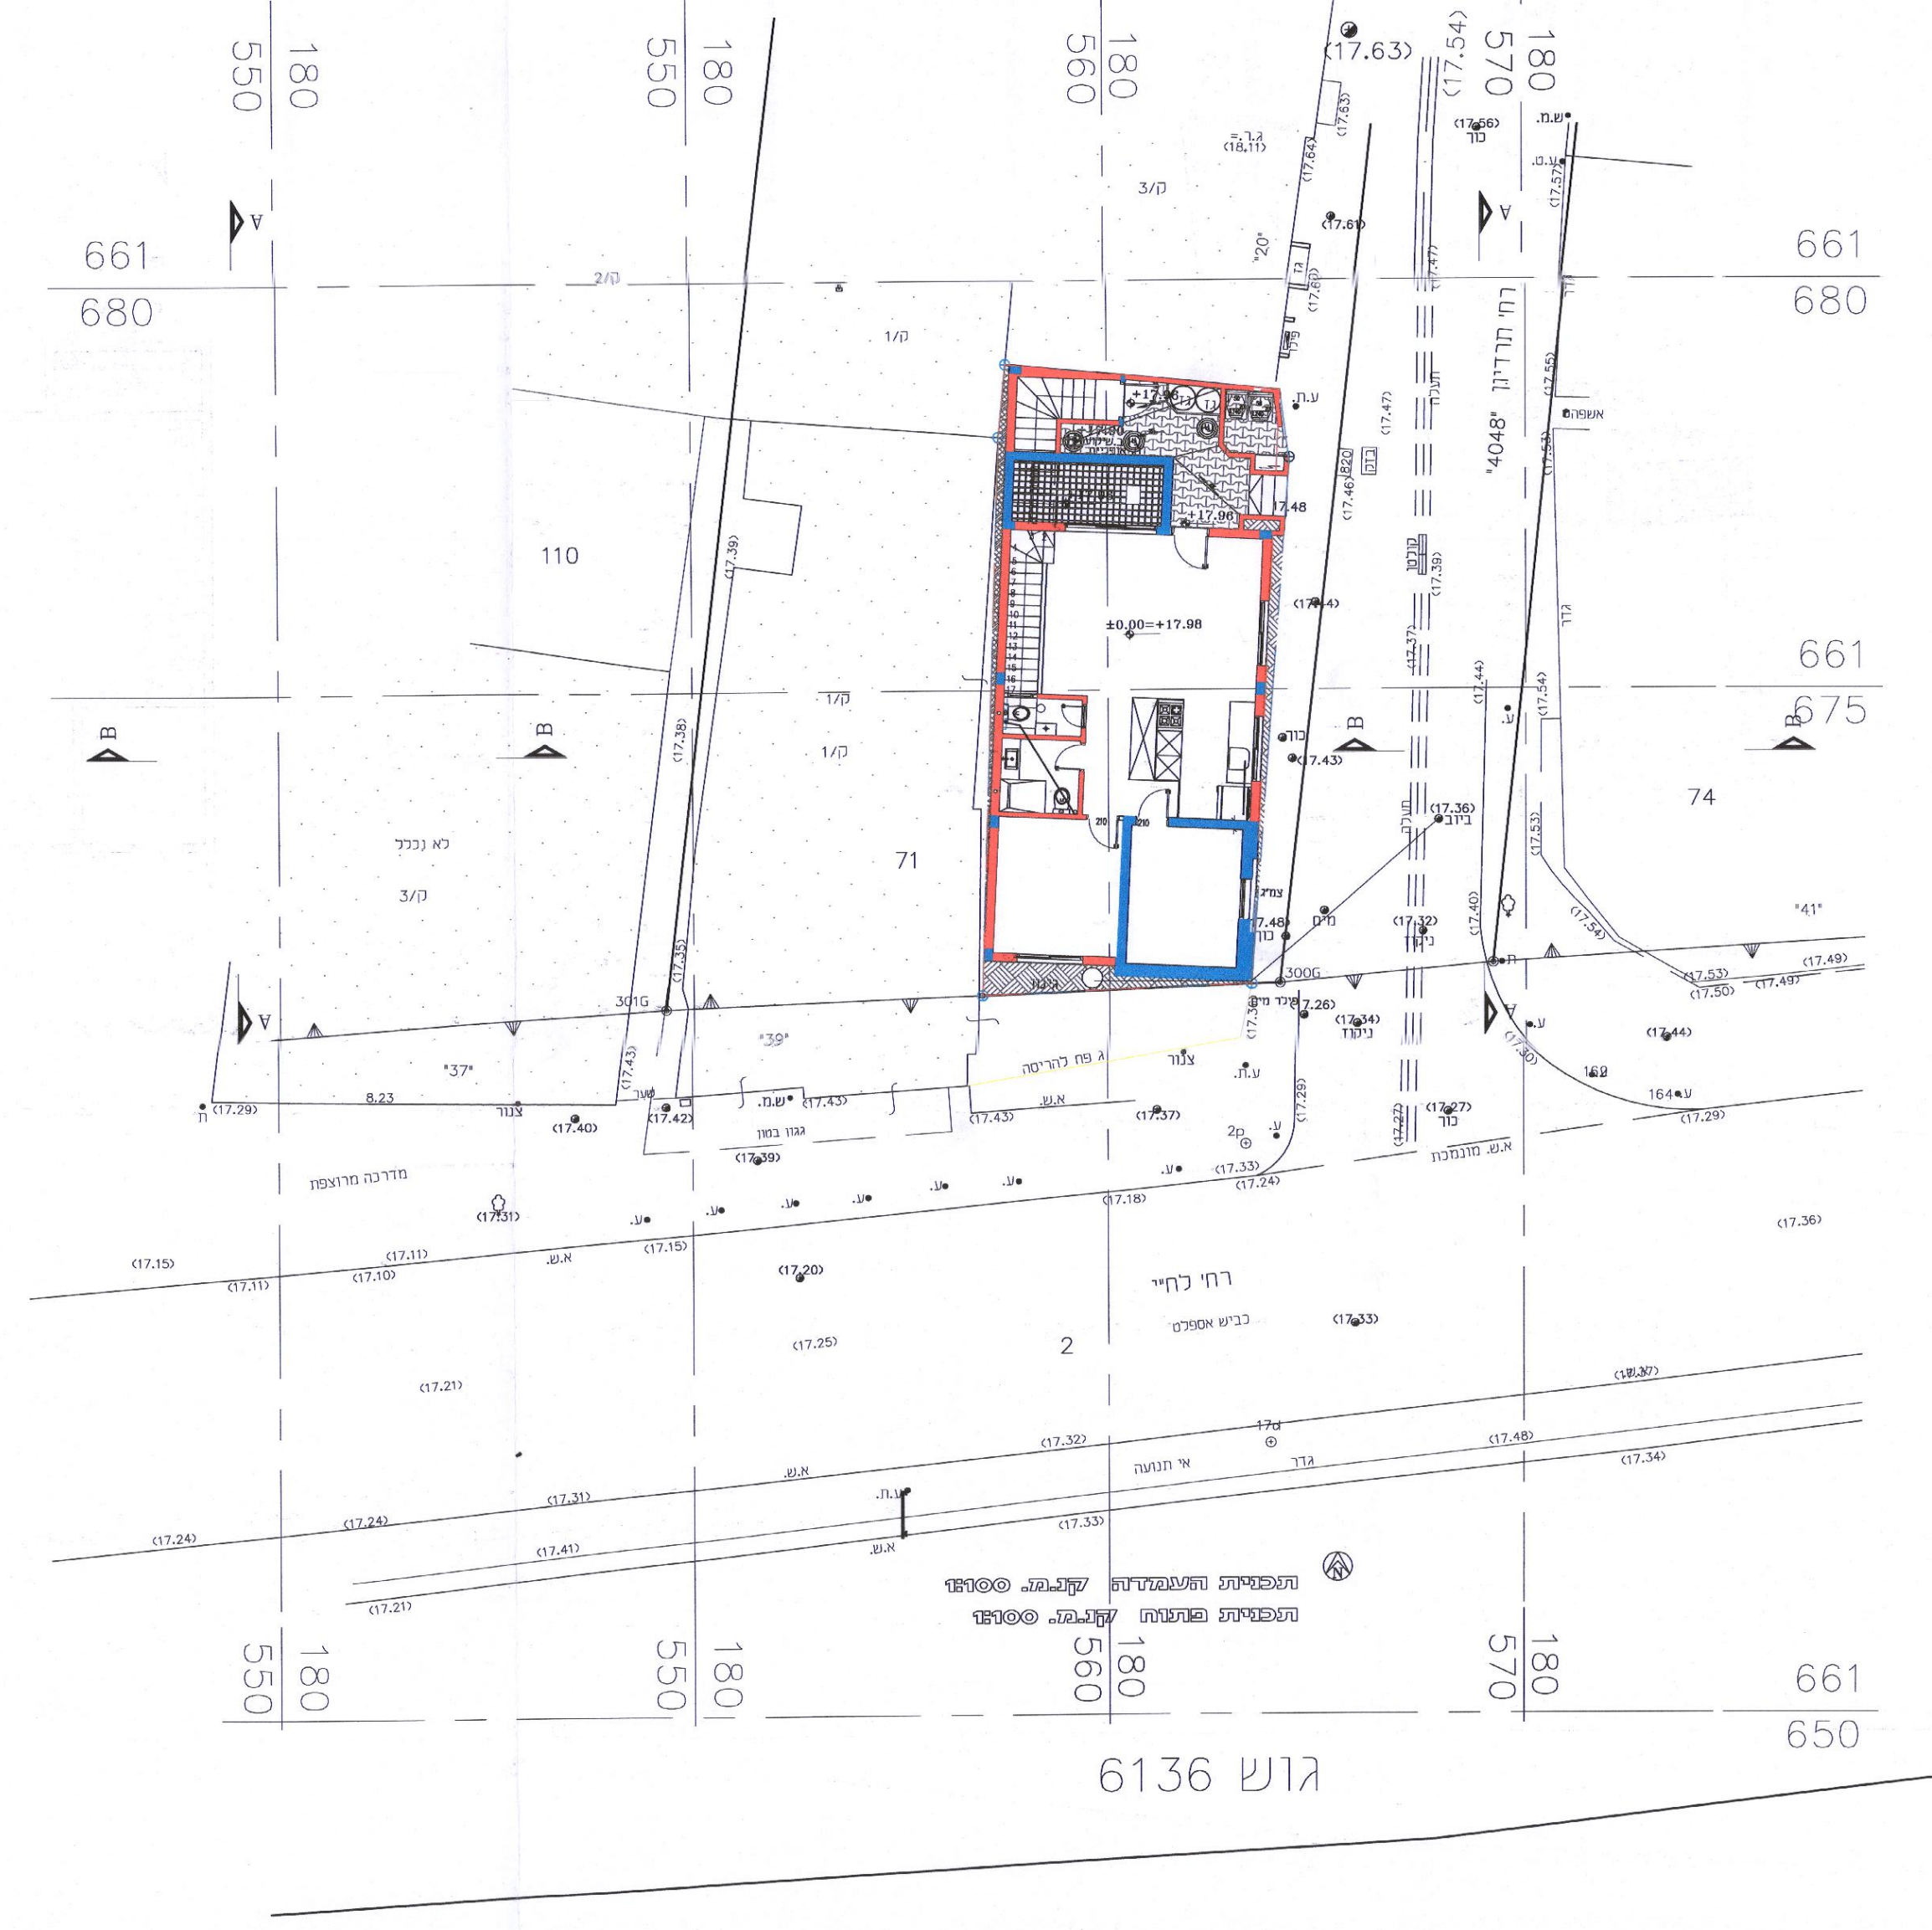

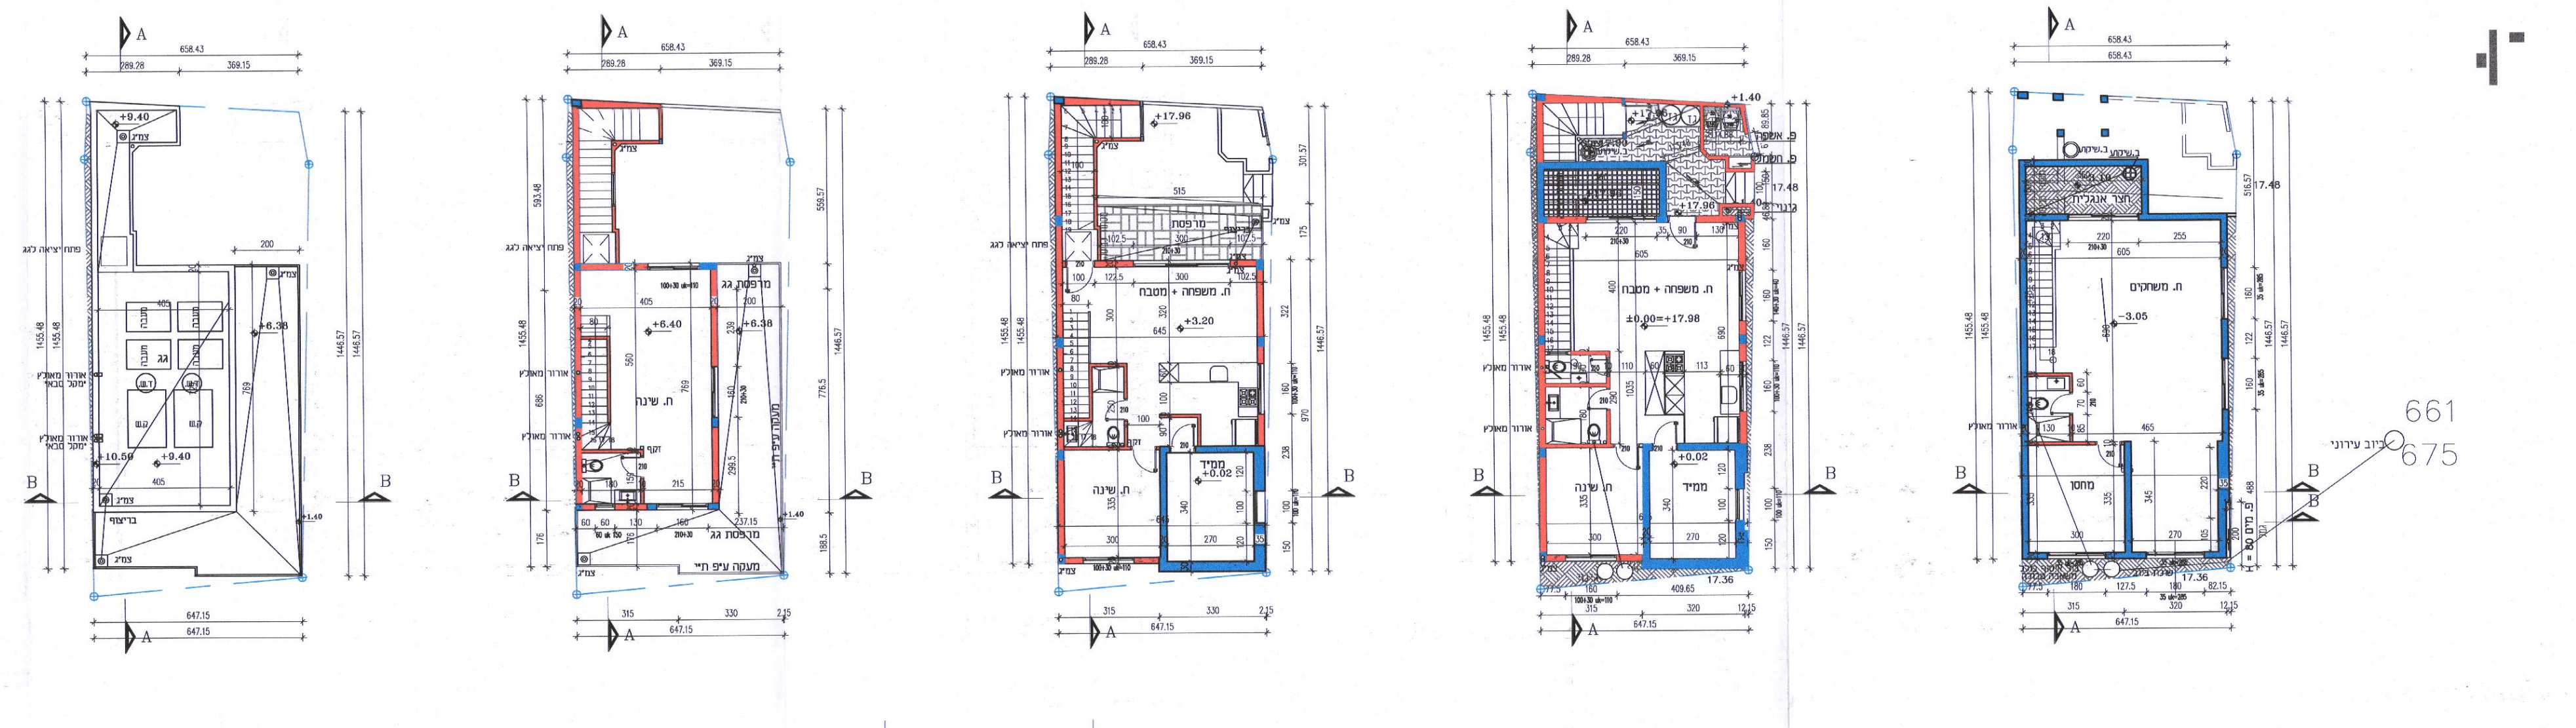

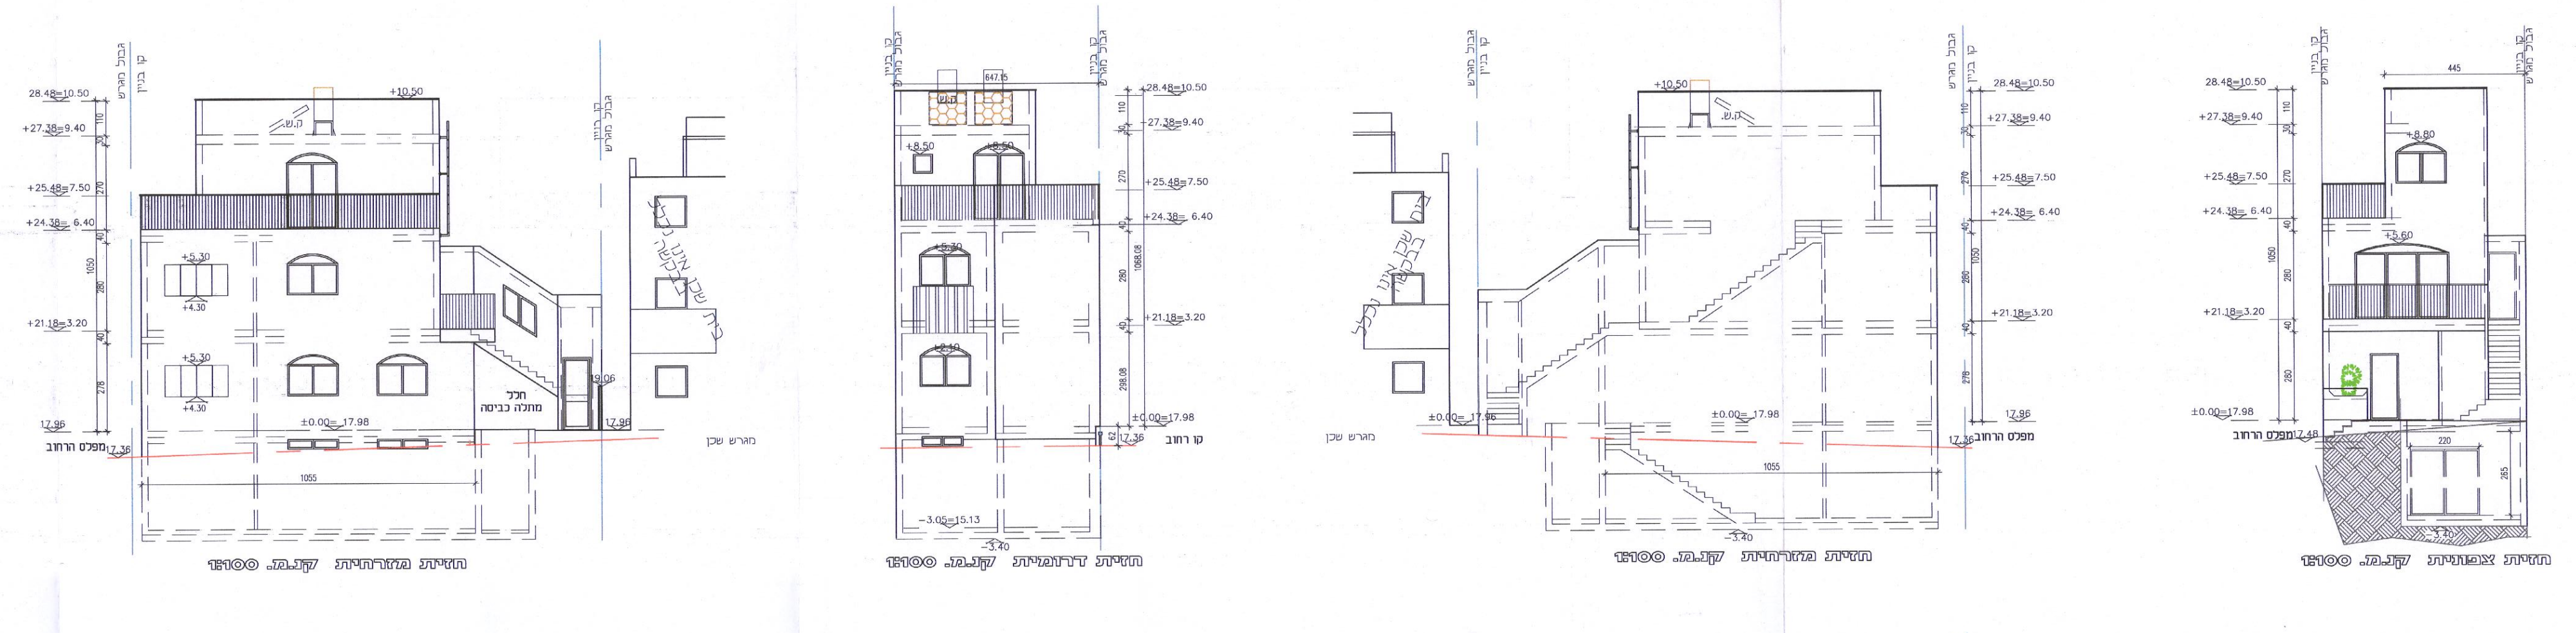

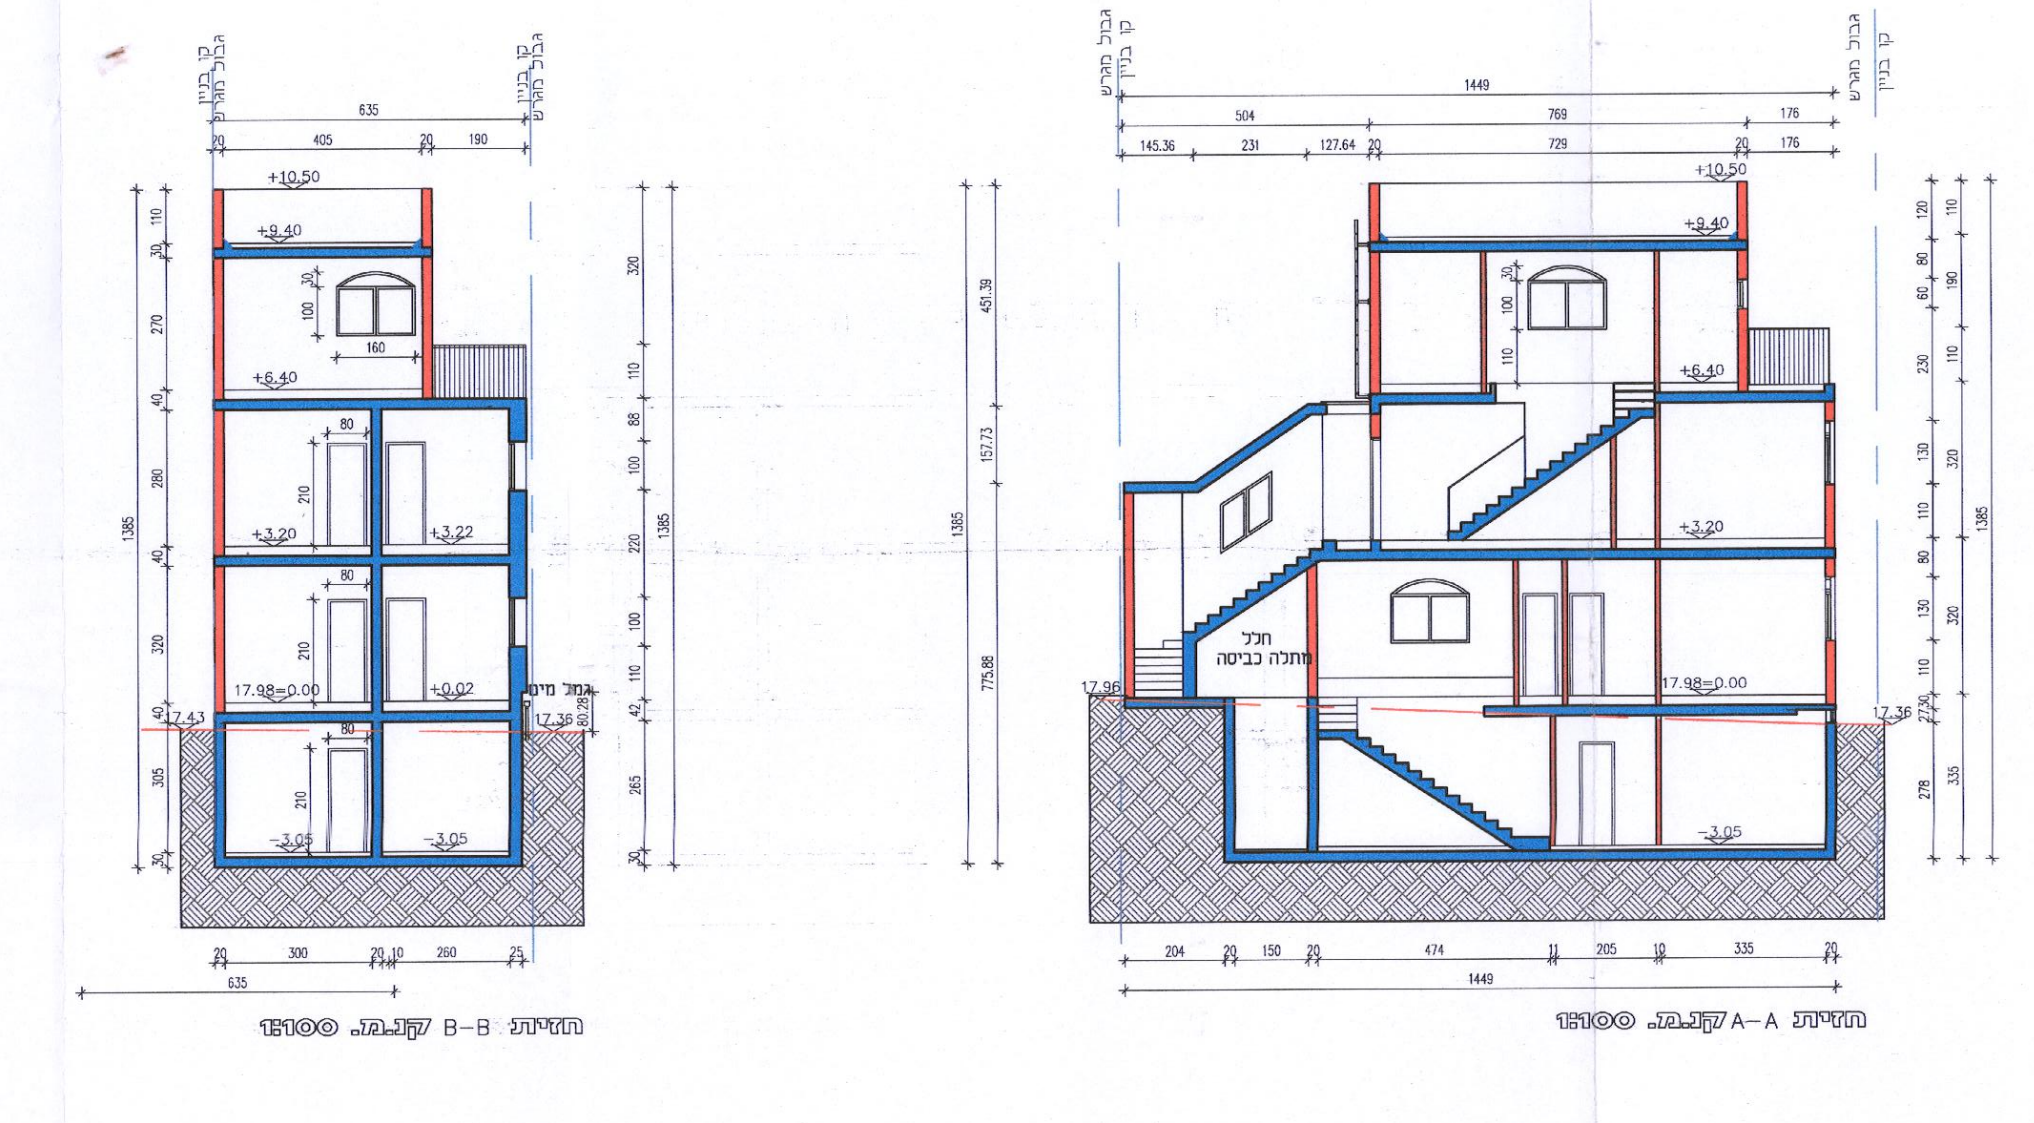

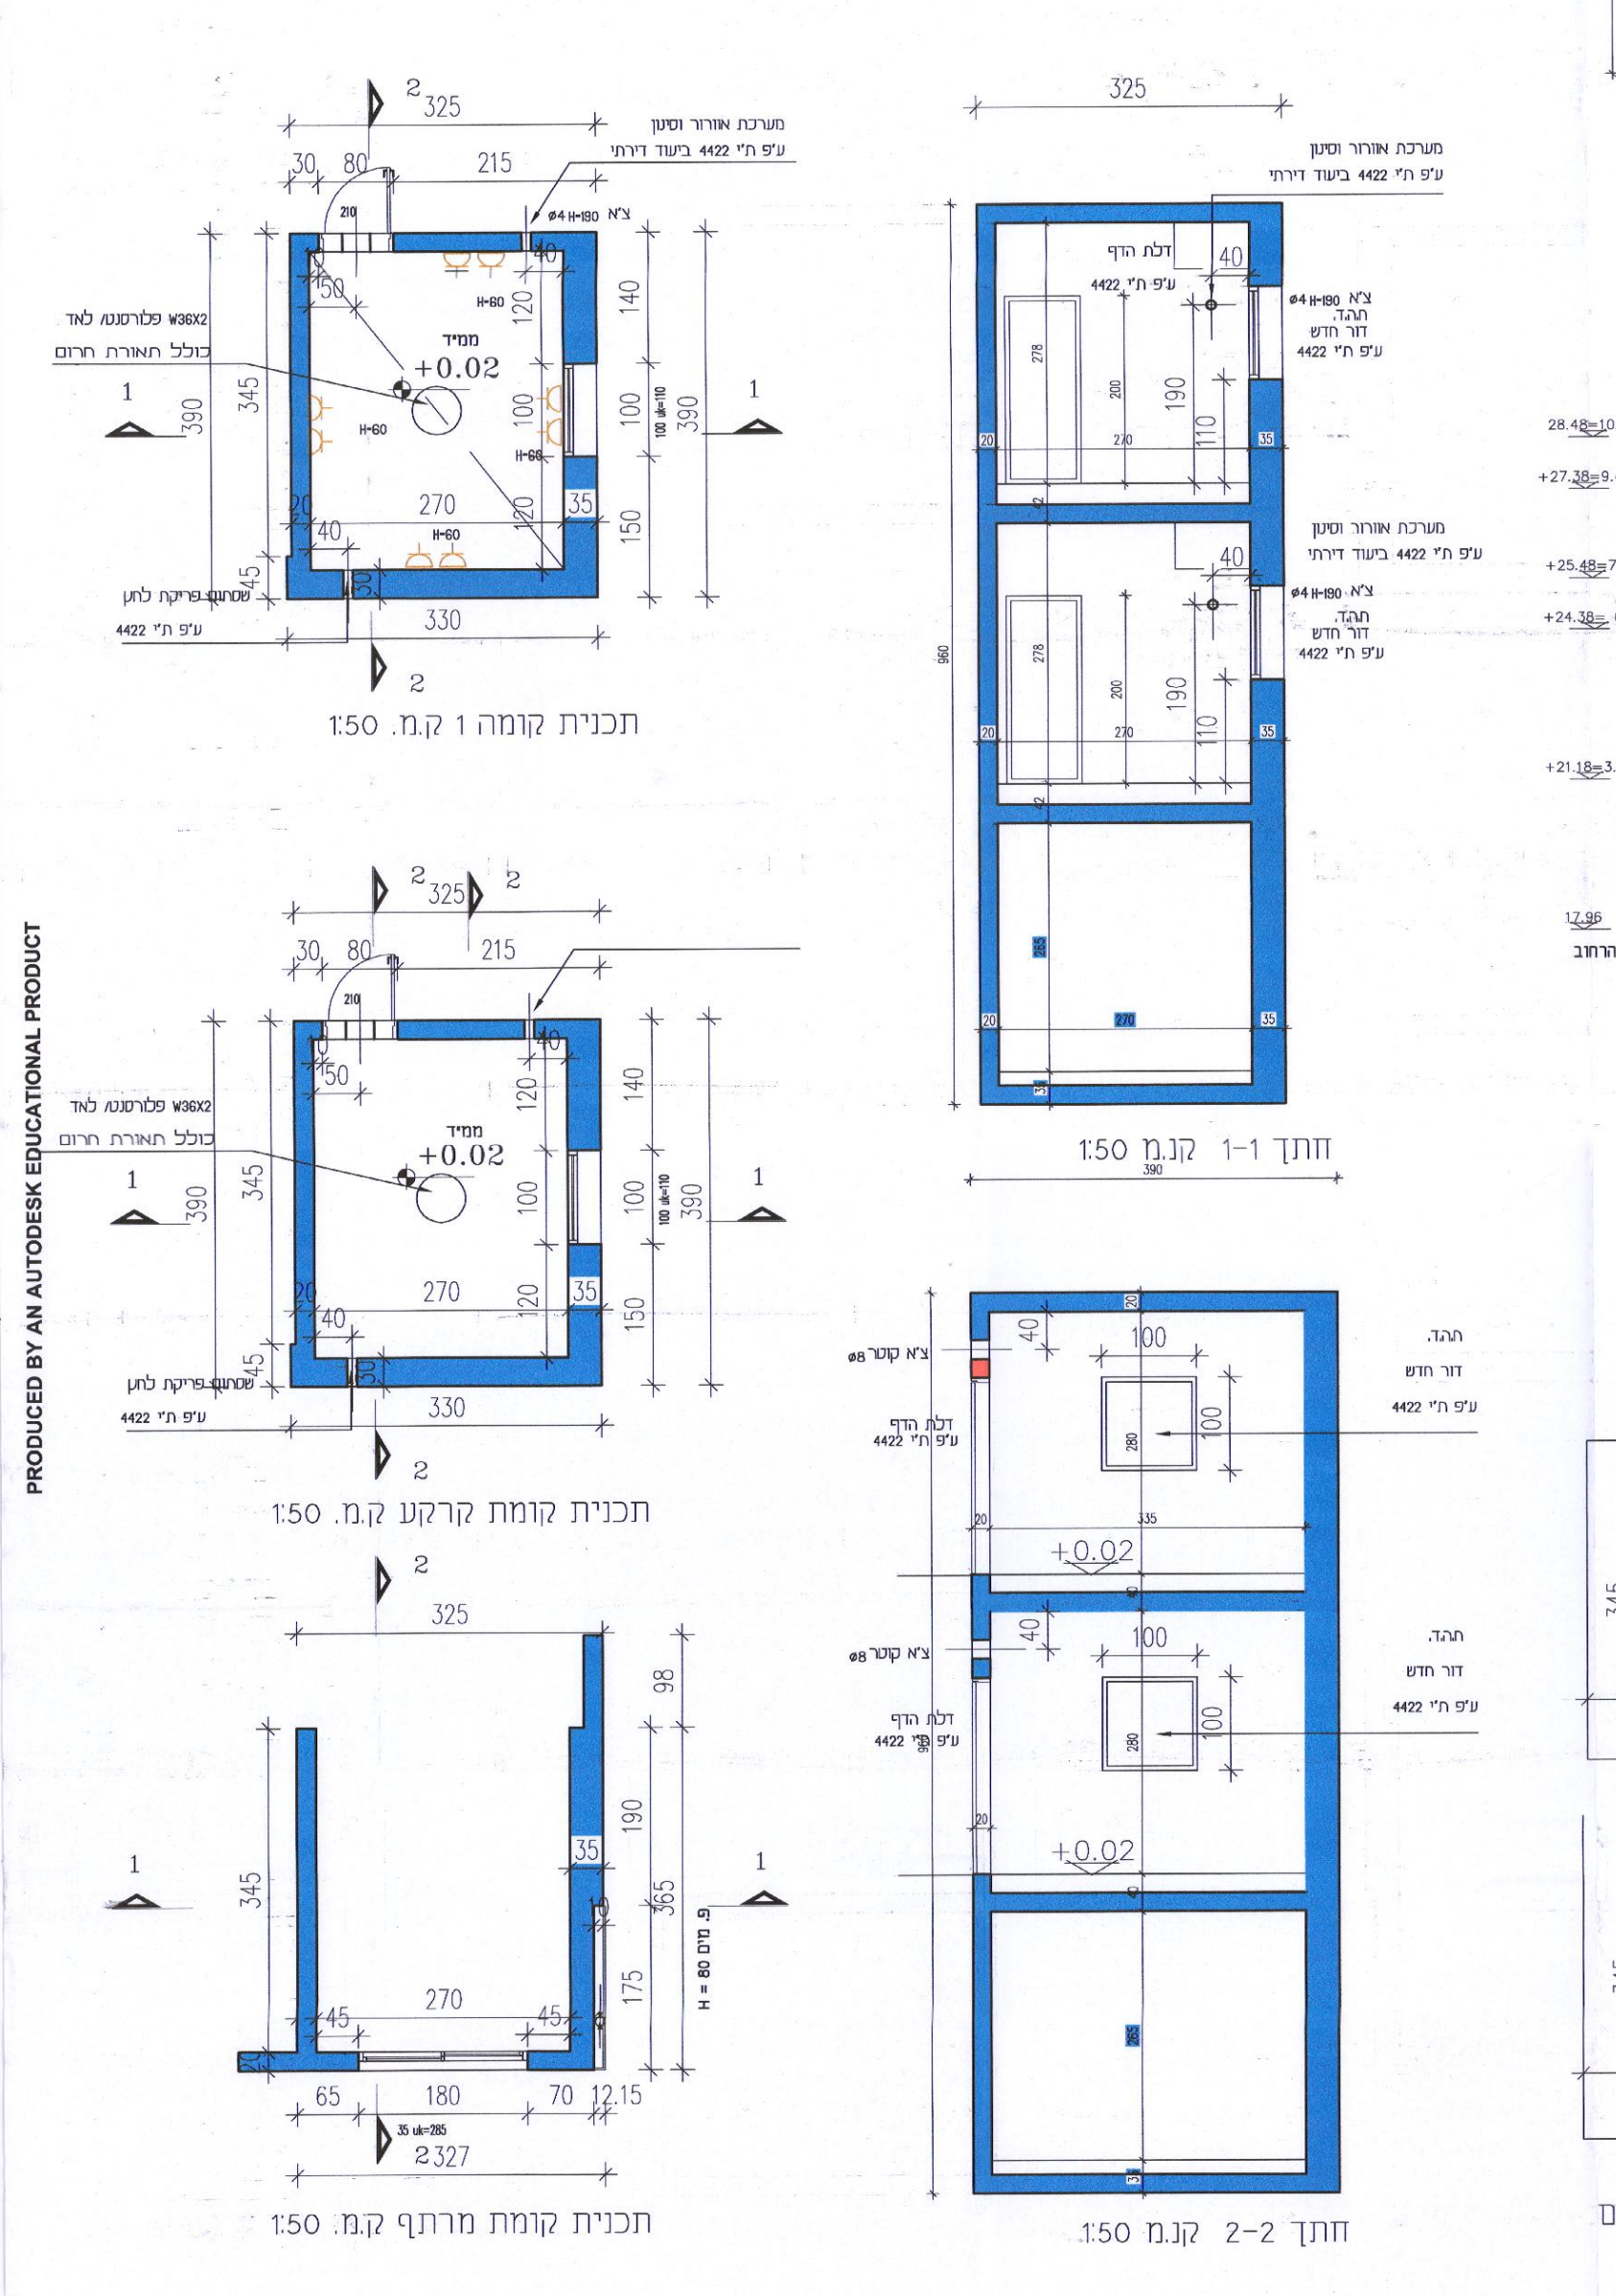

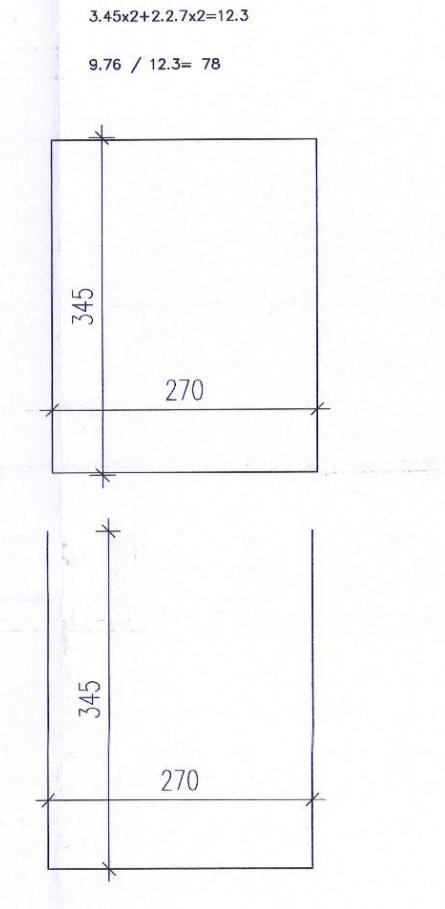

חישוב יחס היקפים

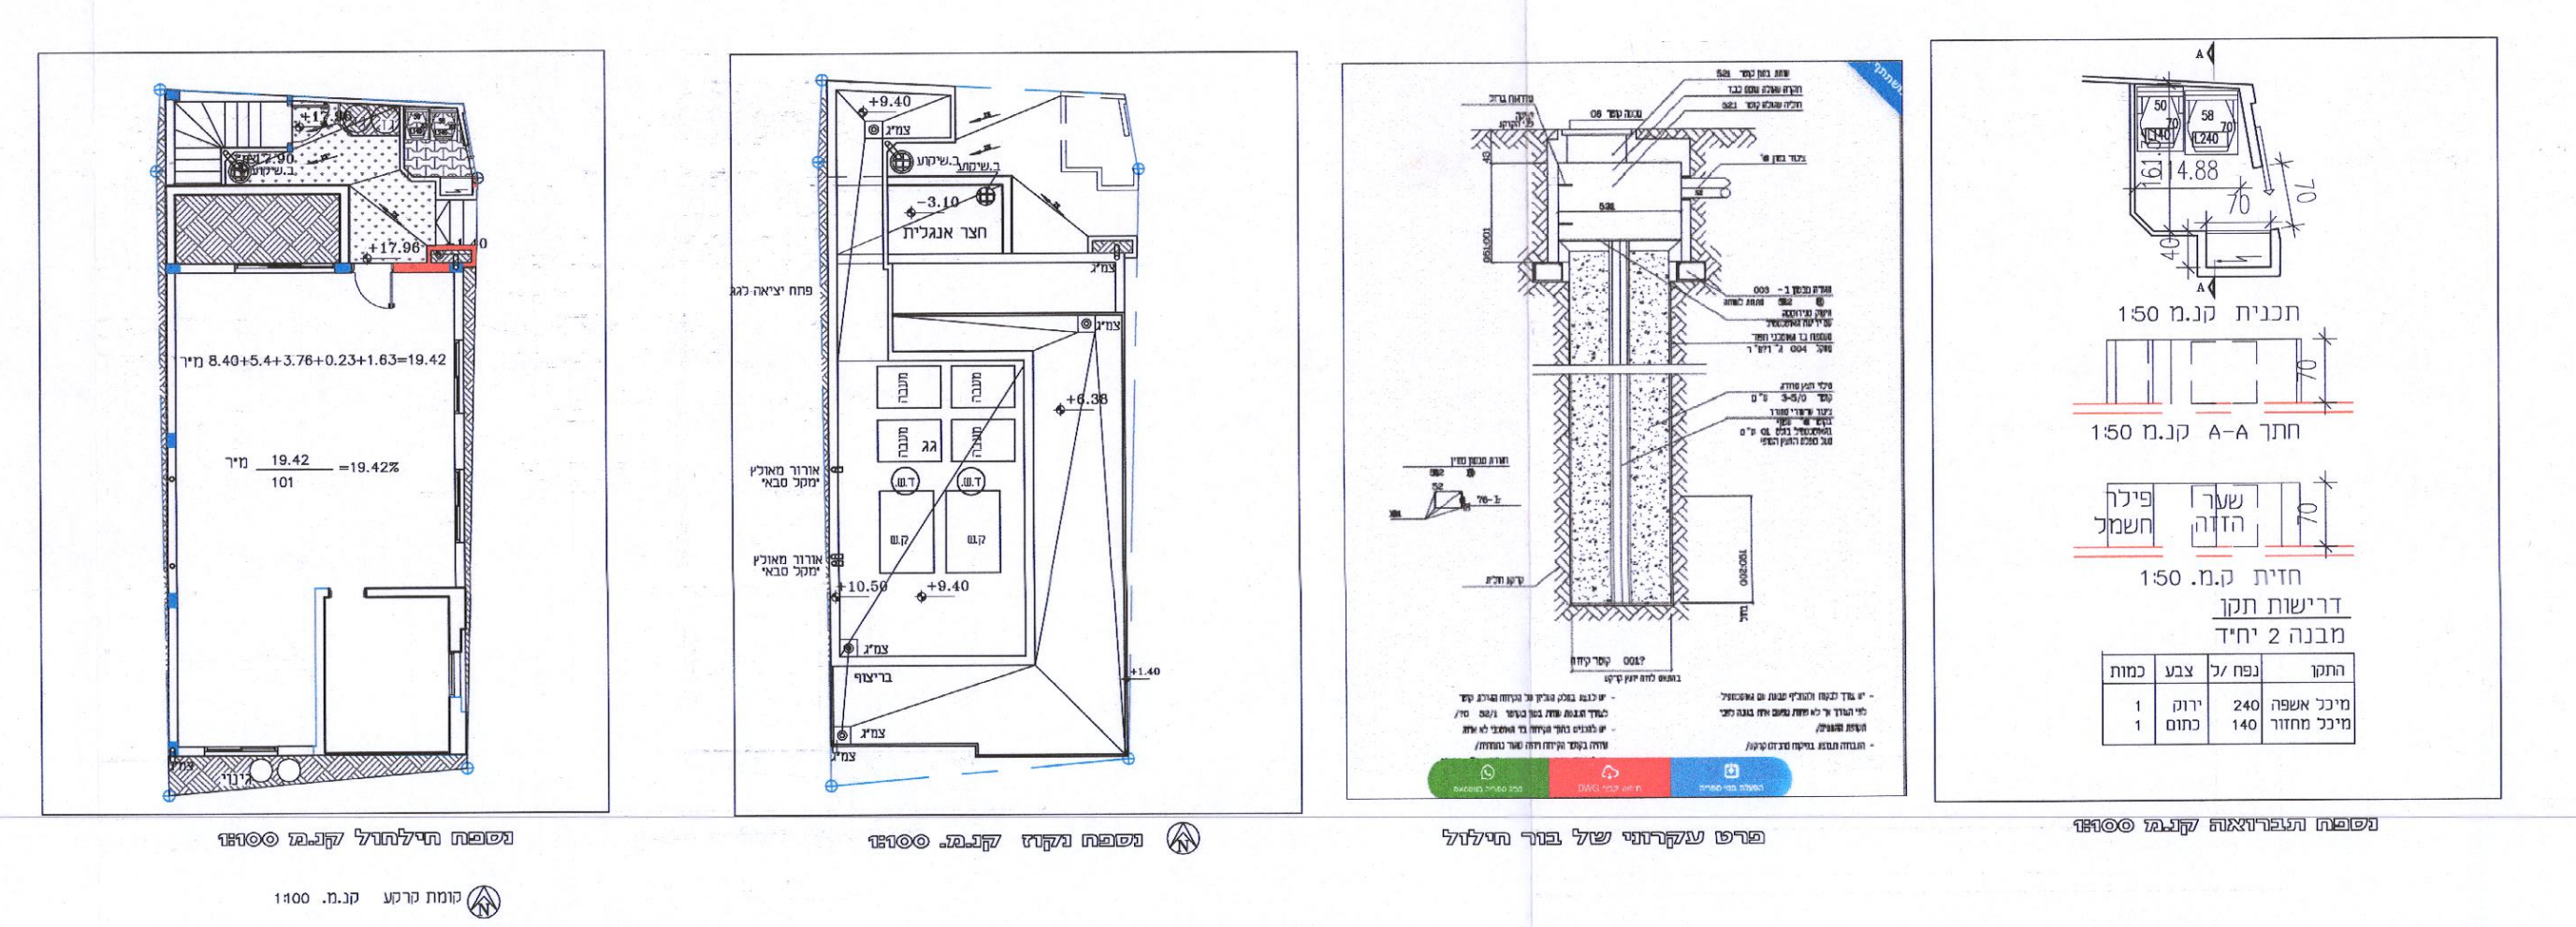

נספח חנייה

בנין חדש בן 2 יח"ד
שטח יח"ד צמודת קרקע כולל מרתף 140 מ"ר
דרישת תקן חנייה 1.33
שטח יח"ד קומה ראשונה כולל חדר יציאה לגג 106 מ"ר
דרישת תקן חנייה 1.

ע"פ הודעת המכון אין לתכנן חניות בחלקה זו