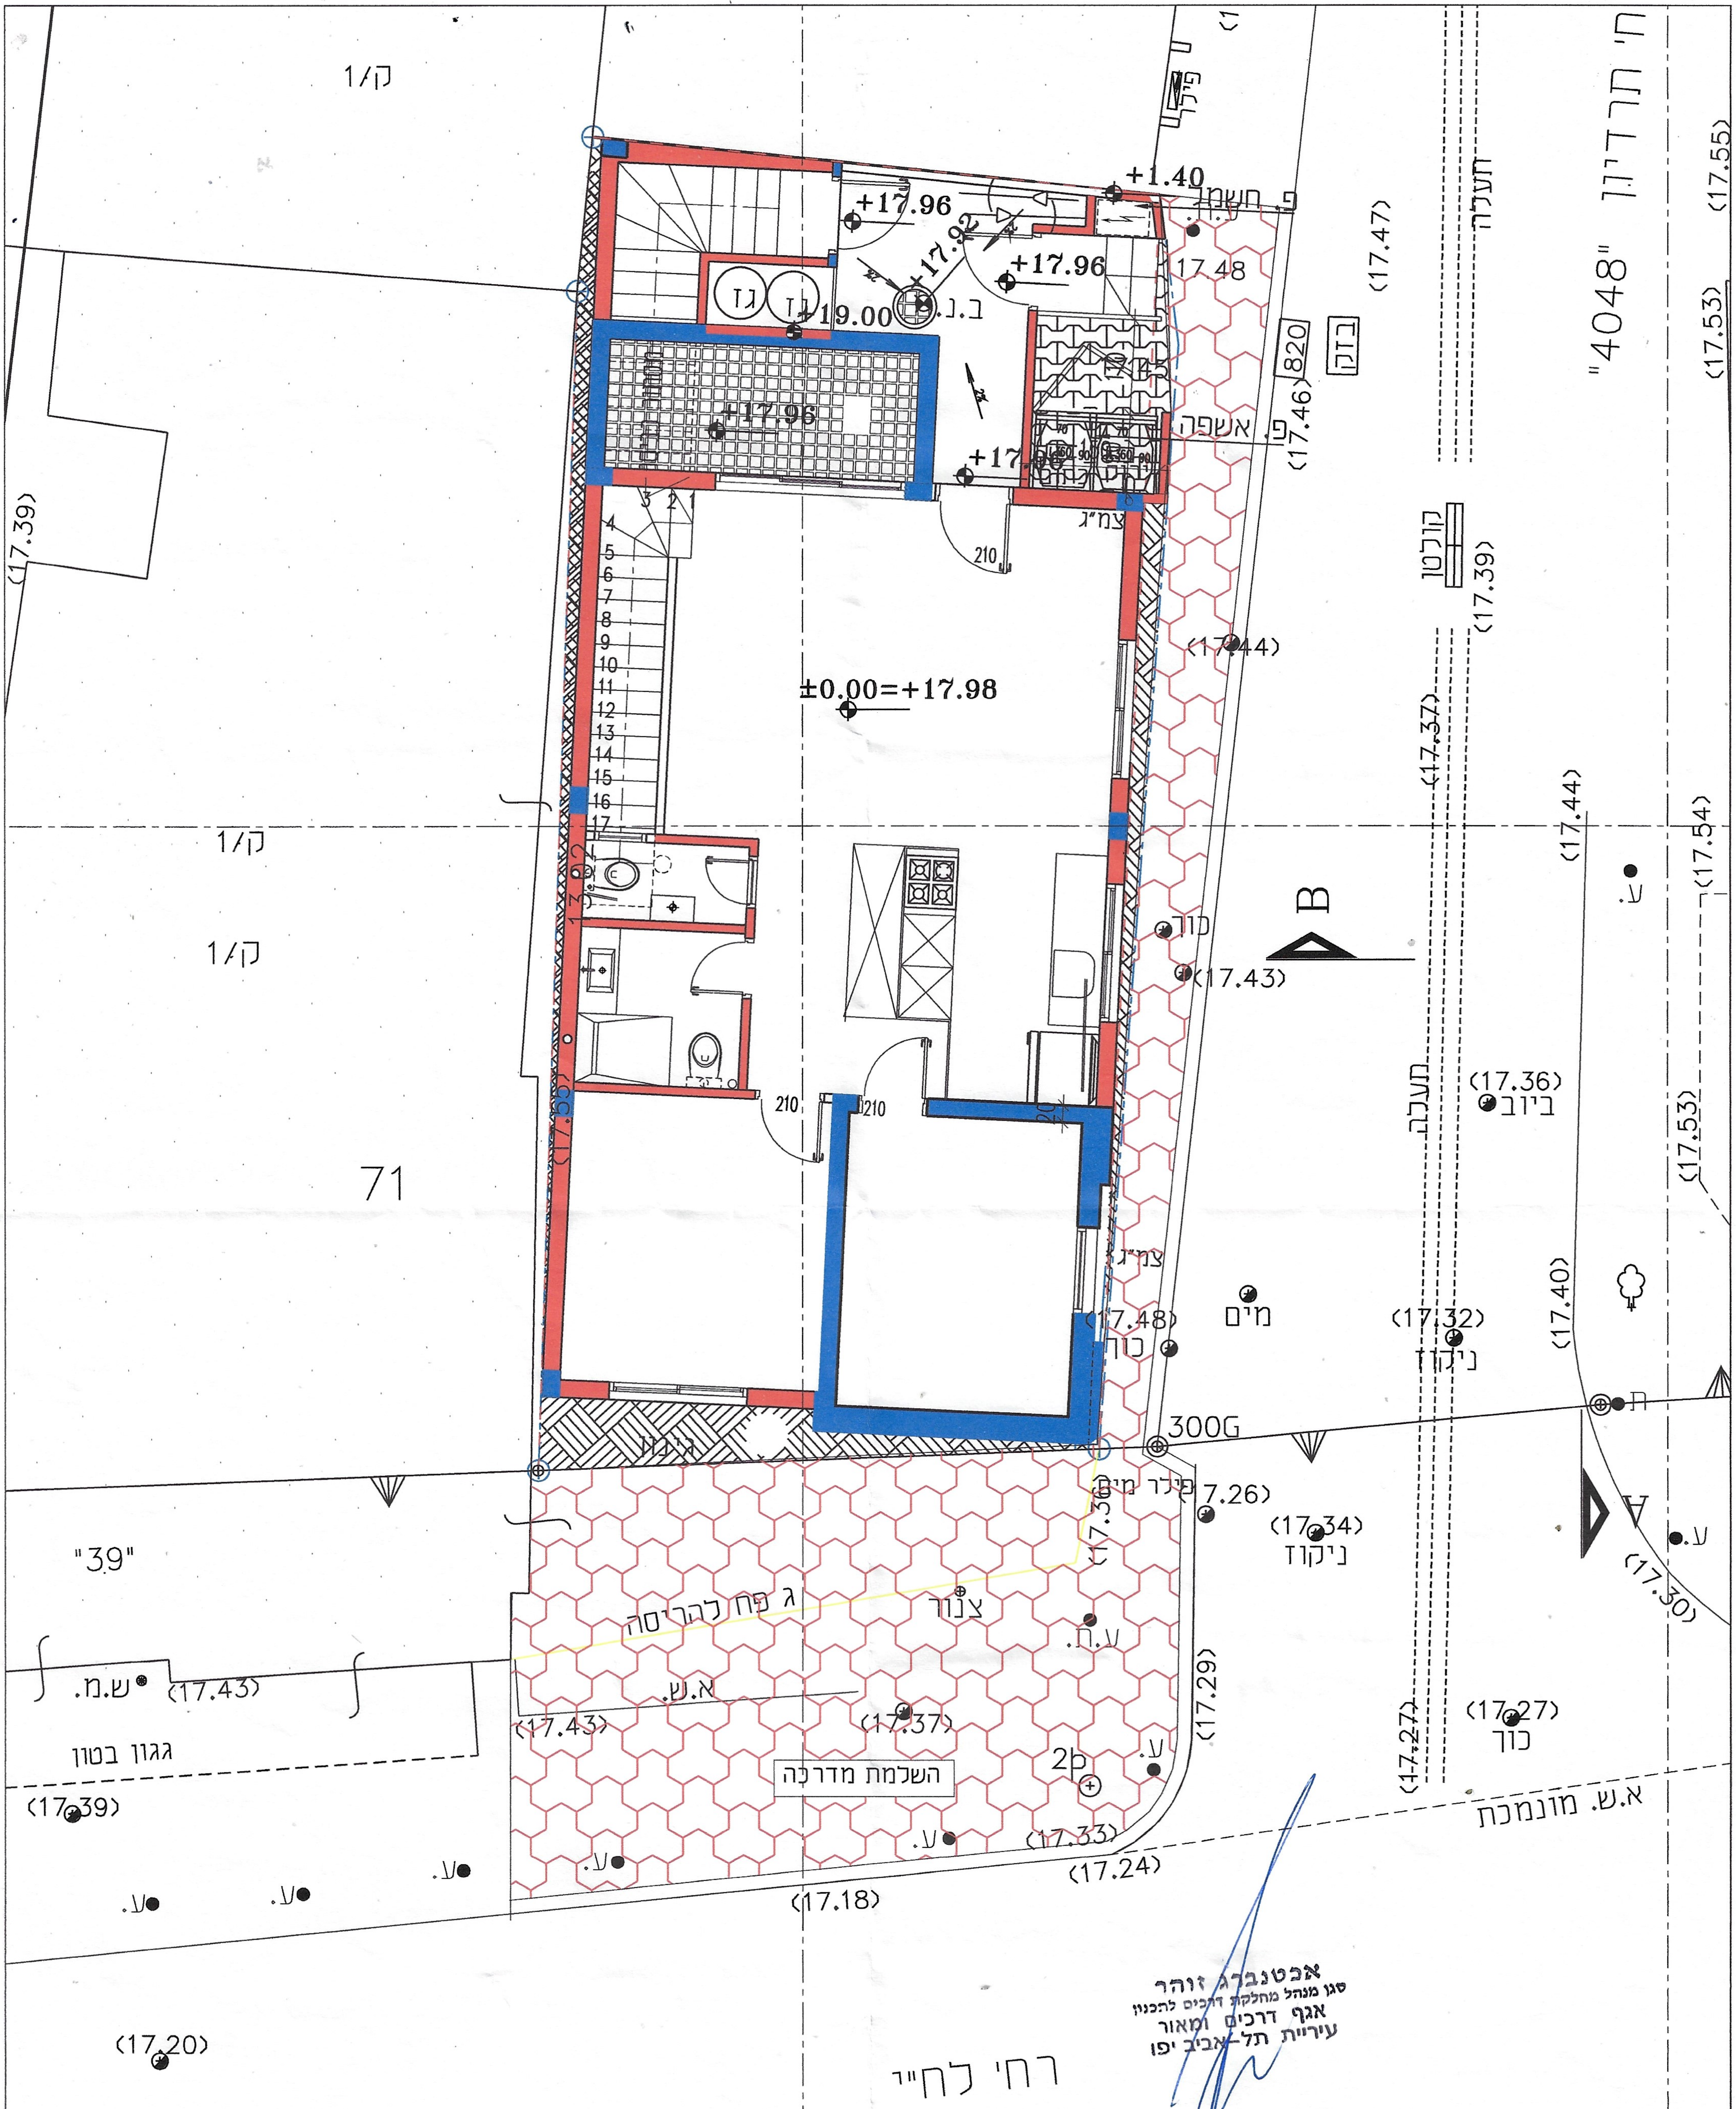
ח' תרדיון
"4048"
(17.55)
(17.53)
(17.54)
(17.44)
(17.47)
(17.46)
(17.39)
(17.37)
תעלה
קורנס
בזק
820
פ. חשמל
+1.40
ע.ח.
17.48
פ. אשפה
+17.96
+17.92
+17.96
ב.נ.
+19.00
גז
גז
+17.96
+17.96
צמ"ג
210
±0.00=+17.98
1
2
3
4
5
6
7
8
9
10
11
12
13
14
15
16
17
(17.44)
כוך
(17.43)
B
210
210
20
(17.36)
ביוב
(17.53)
צמ"ג
(17.48)
כוך
מים
(17.32)
ניקוז
(17.40)
ת
300G
גינון
פילר מים
7.26
(17.34)
ניקוז
A
ע.
(17.30)
(17.36)
ג פח להריסה
צנור
ע.ח.
א.ש.
(17.37)
(17.29)
(17.27)
כוך
(17.27)
(17.43)
השלמת מדרכה
2p
ע.
ע.
(17.33)
(17.24)
(17.18)
א.ש. מונמכת
ק/1
ק/1
ק/1
(17.39)
71
(17.55)
"39"
ש.מ.
(17.43)
גגון בטון
(17.39)
ע.
ע.
ע.
(17.20)
רחי לח"י
כביש אספלט
(17.33)
(17.25)
2

אכטנברג זוהר
סגן מנהל מחלקת דרכים לתכנון
אגף דרכים ומאור
עיריית תל-אביב יפו

**ZEEV ALPEROVITCH ARCHITECT**
**זאב אלפרוביץ אדריכל**
3 De Hass st — דה האז 3
Tel Aviv 6266605 תל אביב
TEL. 0545455559 טל.
zeevalp@gmail.com

הערות

המבצע אחראי לבדיקת התכניות ולהתאמתן במקום ; על המבצע לבקר כל המדות ועל כל טעות או אי התאמה עליו להודיע למתכנן . אין לקבוע מידות על - ידי מדידה בשרטוט ;
מהנדס ו או יועץ אשר שמו רשום מעל שם האדריכל בתכנית זו, נושא לבדו באחריות המקצועית והחוקית לתכנית .
אין לעשות כל שימוש בתכנית זו או ברעיונות הגלומים בה ללא אישור בכתב מאת המתכנן .
(17.32)

☐ לביצוע ☐ למכרז ☐ לאישור ☐ לעיון

BAR 900 WD
קנ.מ ±0.00 מפלס

**משפ אליגון**
**תרדיון 22**
**תל אביב**

**תכנית**

(17.48)