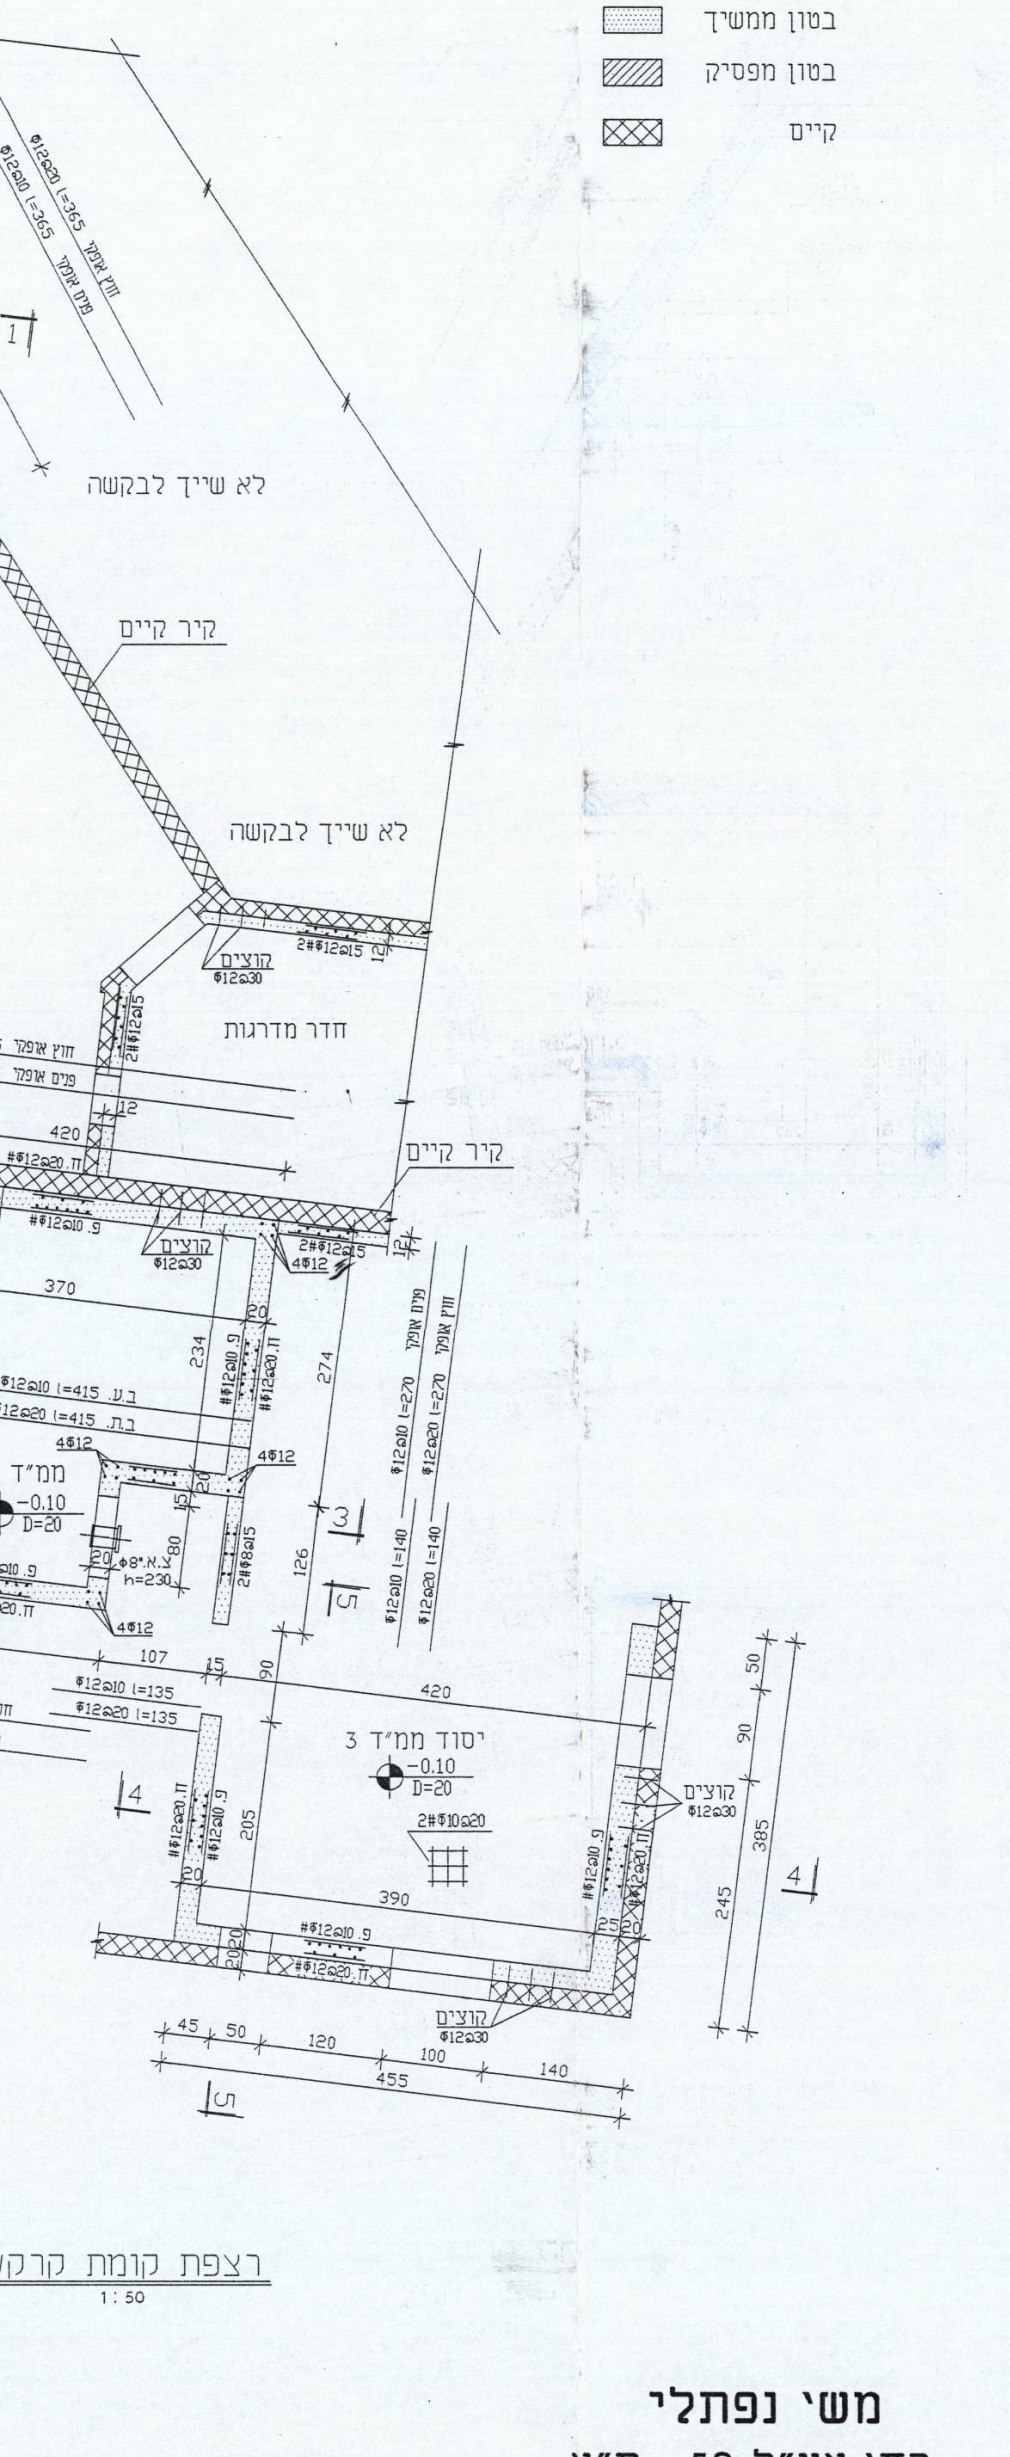

מיקרא:

▤ בטון ממשיך

▨ בטון מפסיק

☒ קיים

משי נפתלי

רח' אצ"ל 58, ת"א

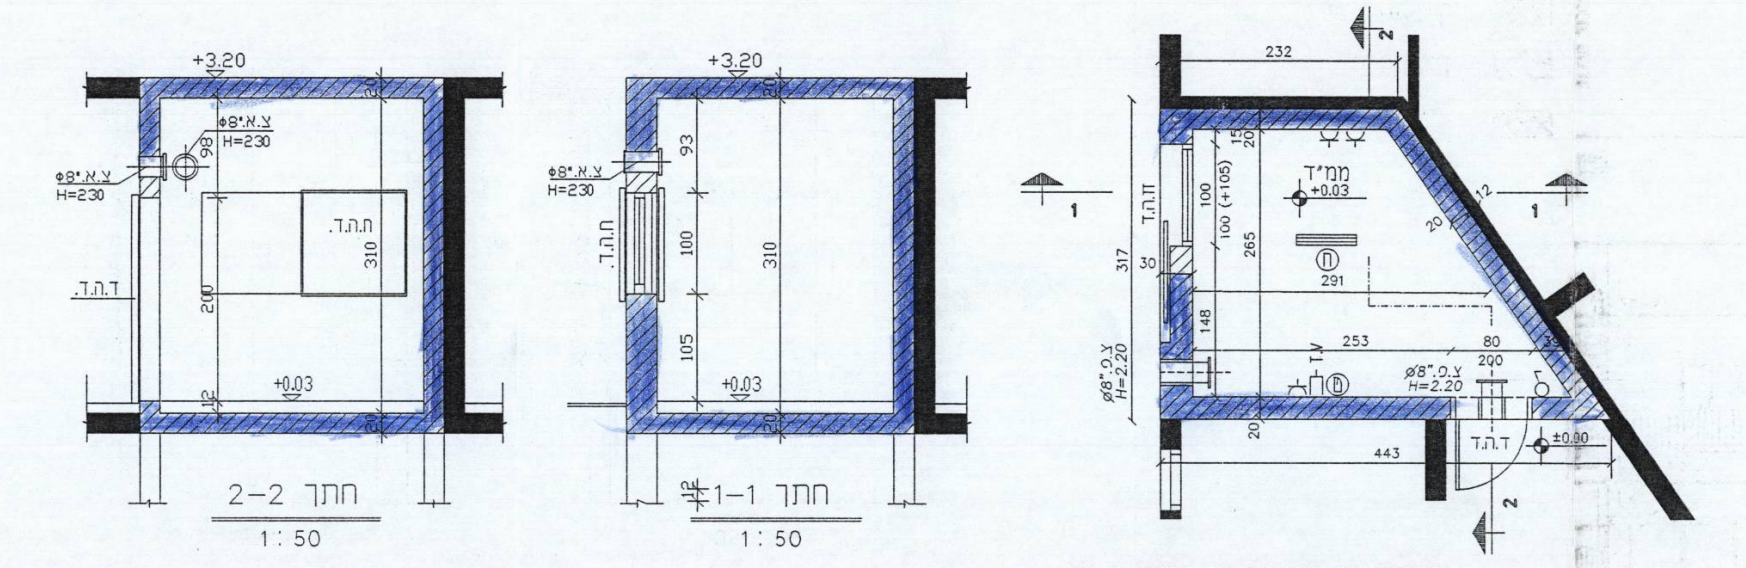

חתך 2-2
1:50

חתך 1-1
1:50

ממ"ד דירה מס' 5
קנ"מ: 1:50

מקרא
- שקע
- טלויזיה
- טלפון
- נ.ת. חרום 40w
- נ.ת. פלורסנט 2×40w
- מפסק בודד

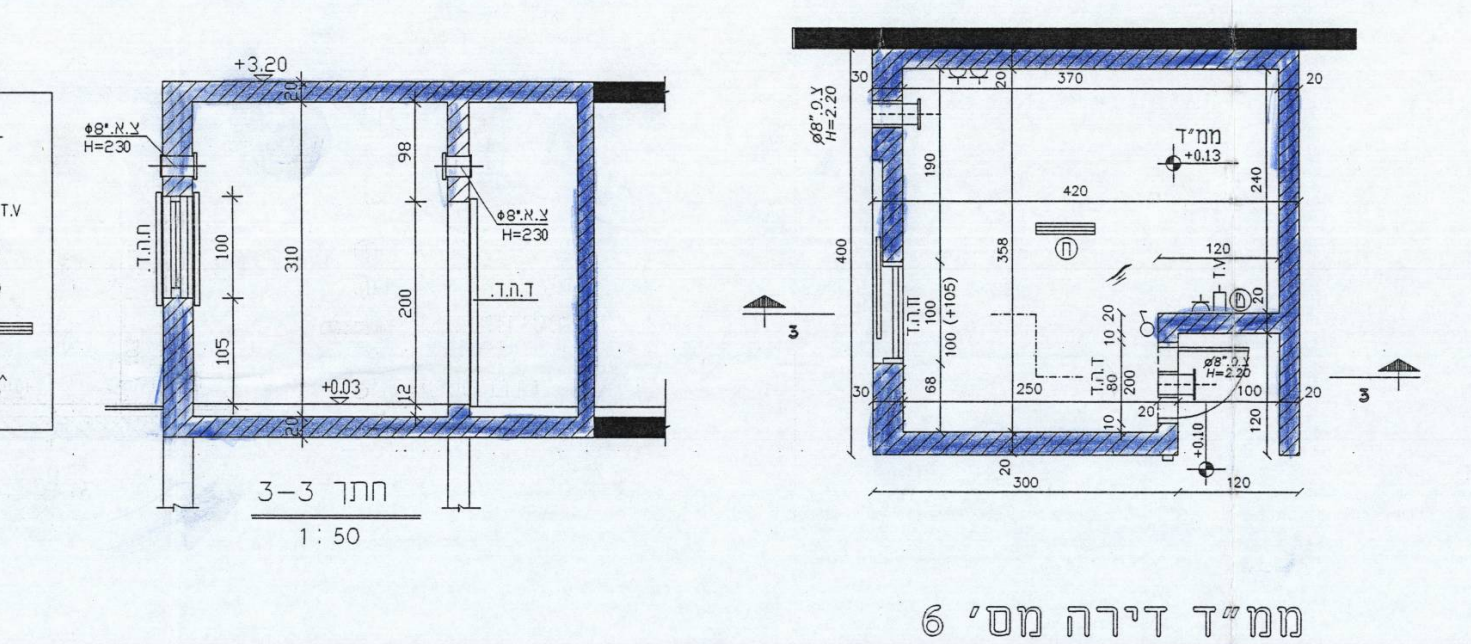

חתך 3-3
1:50

ממ"ד דירה מס' 6
קנ"מ: 1:50

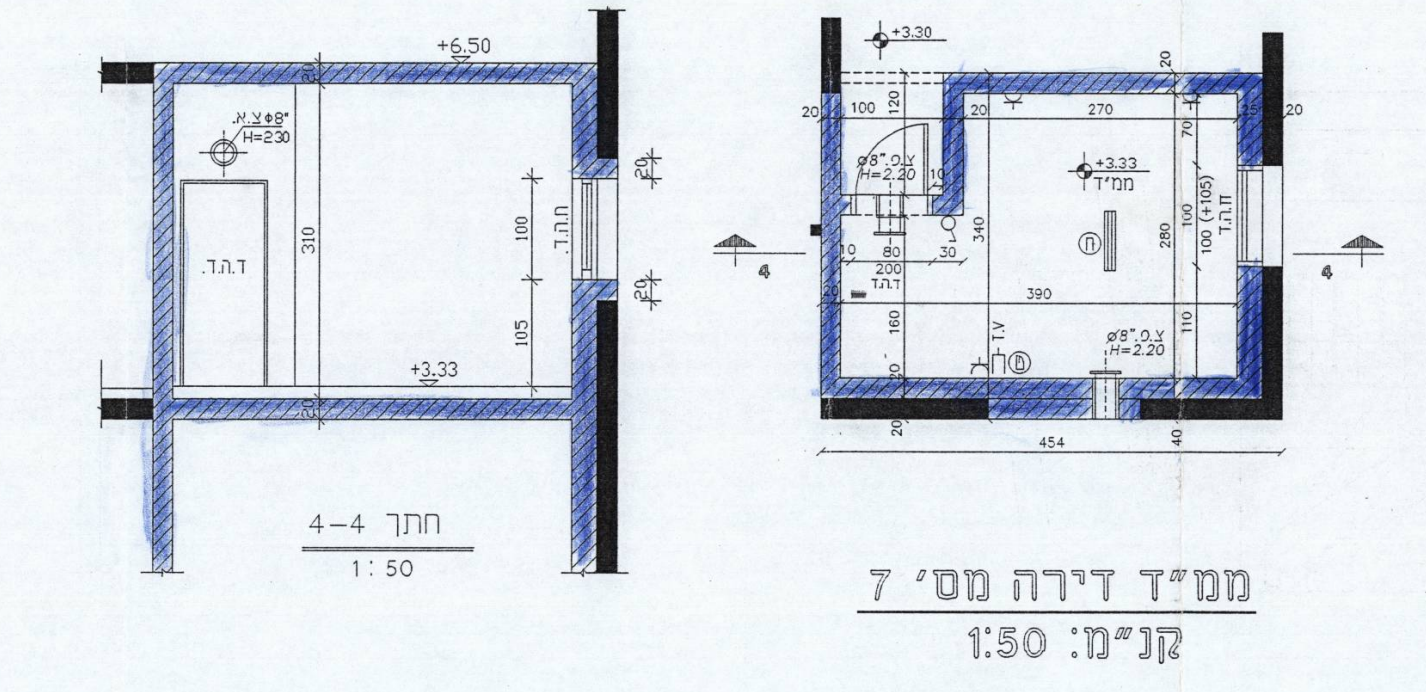

חתך 4-4
1:50

ממ"ד דירה מס' 7
קנ"מ: 1:50

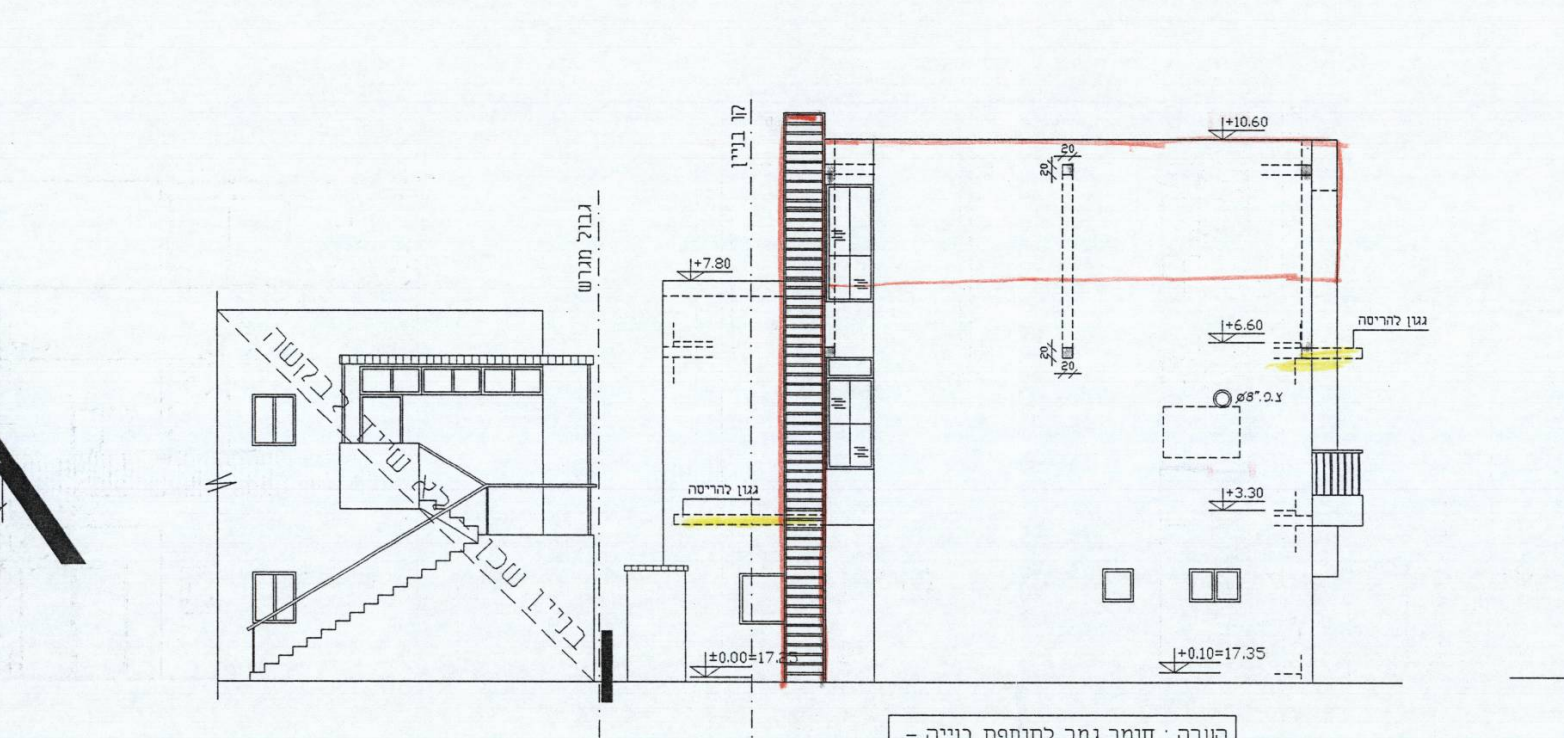

הערה: חומר גמר לתוספת בנייה – טיח בצבע כדוגמת הקיים

חזית דרומית
קנ"מ: 1:100

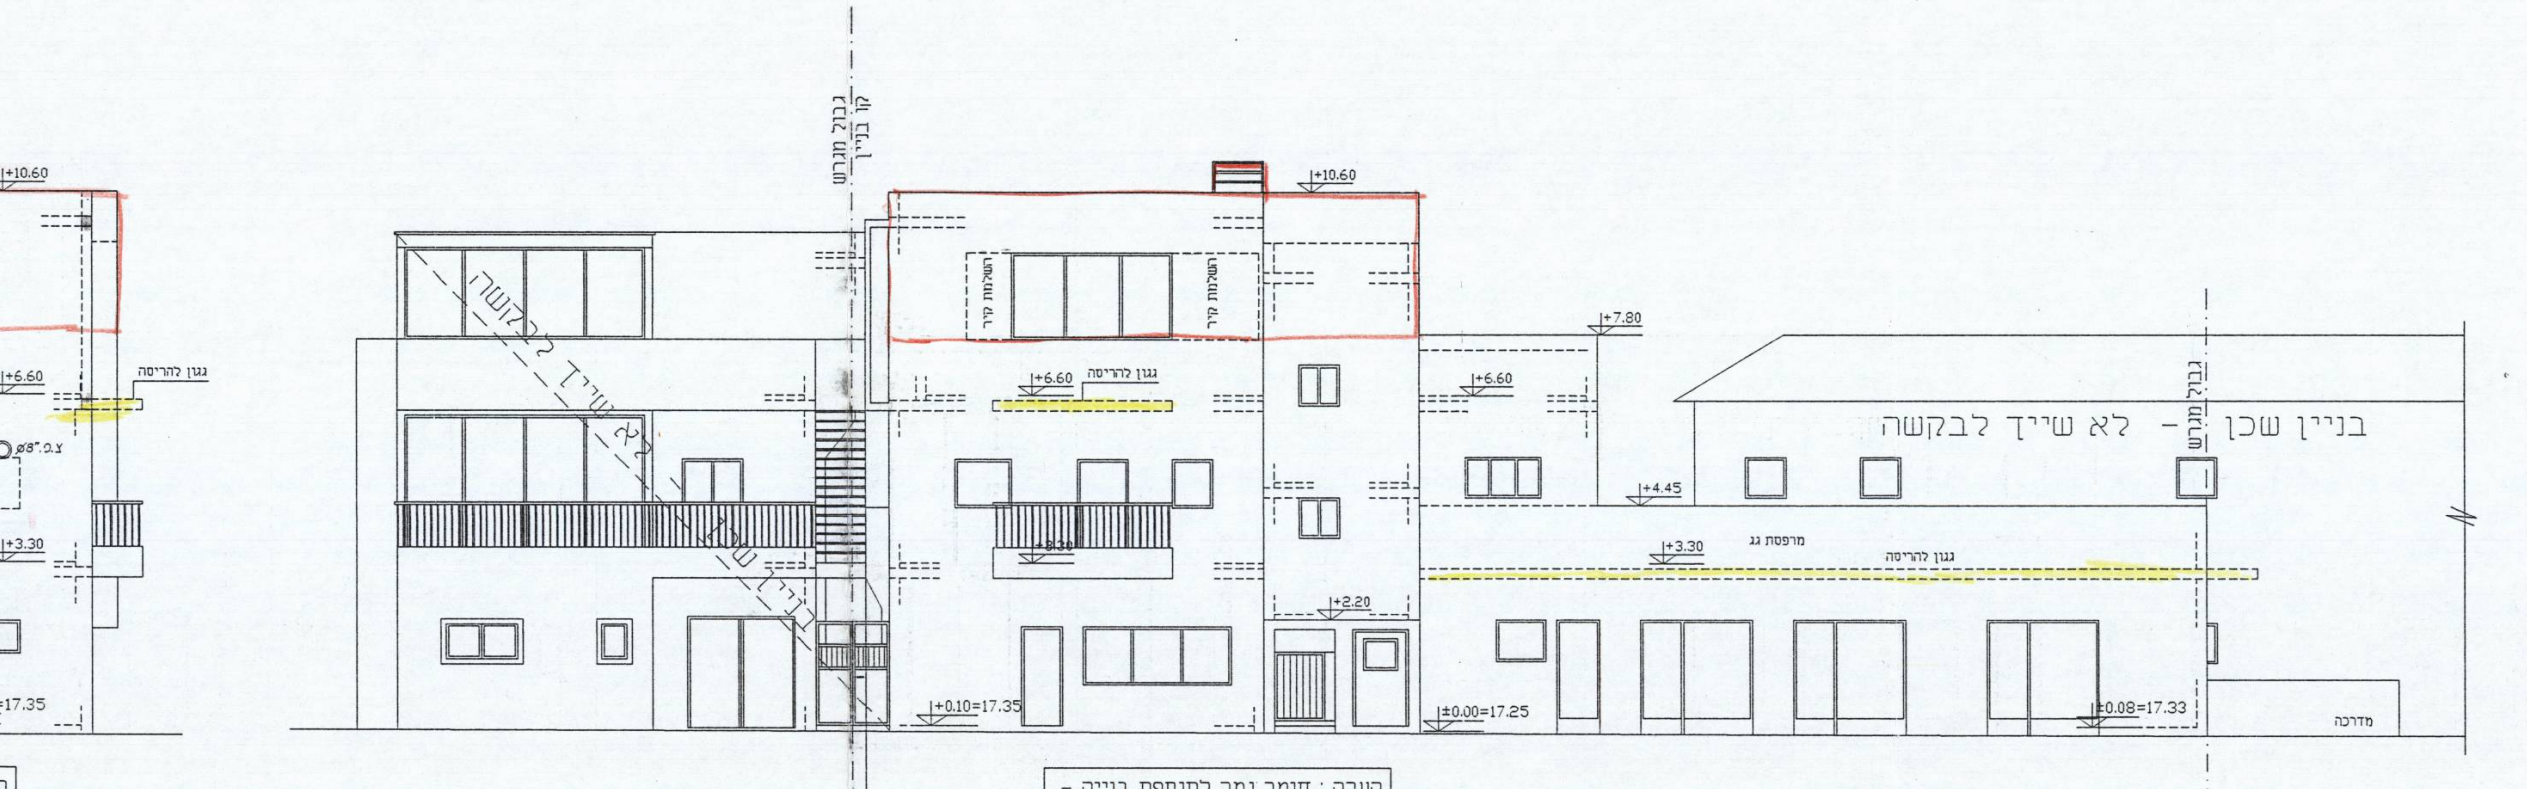

הערה: חומר גמר לתוספת בנייה – טיח בצבע כדוגמת הקיים

חזית מזרחית
קנ"מ: 1:100

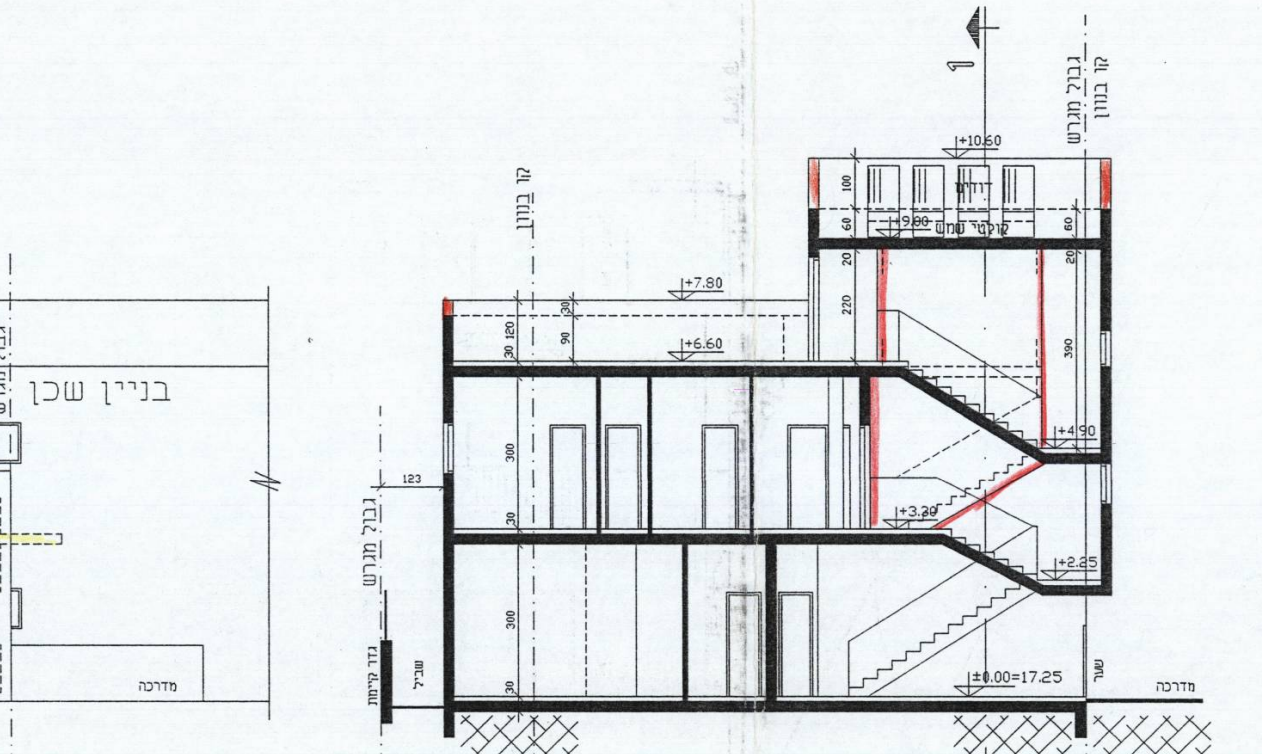

חתך א-א
קנ"מ: 1:100

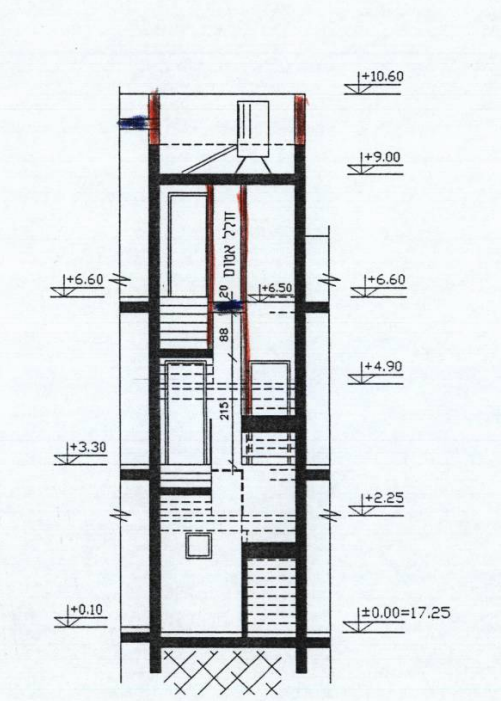

חתך 1-1
(מקומי)
קנ"מ: 1:100

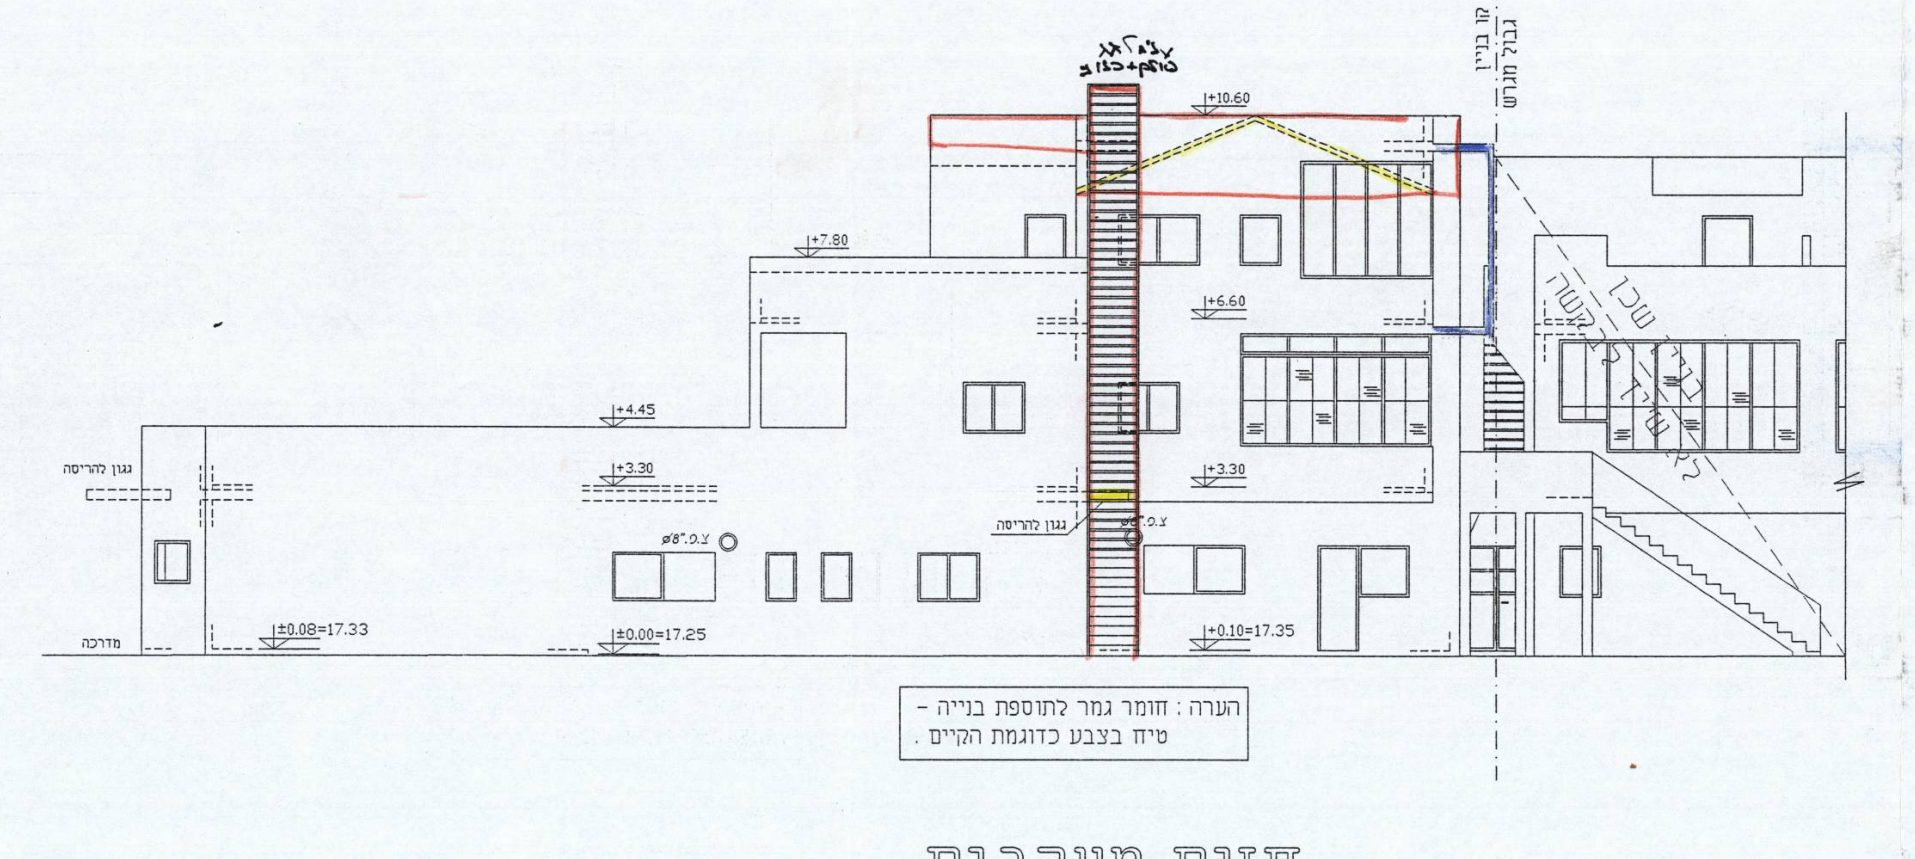

הערה: חומר גמר לתוספת בנייה – טיח בצבע כדוגמת הקיים

חזית מערבית
קנ"מ: 1:100

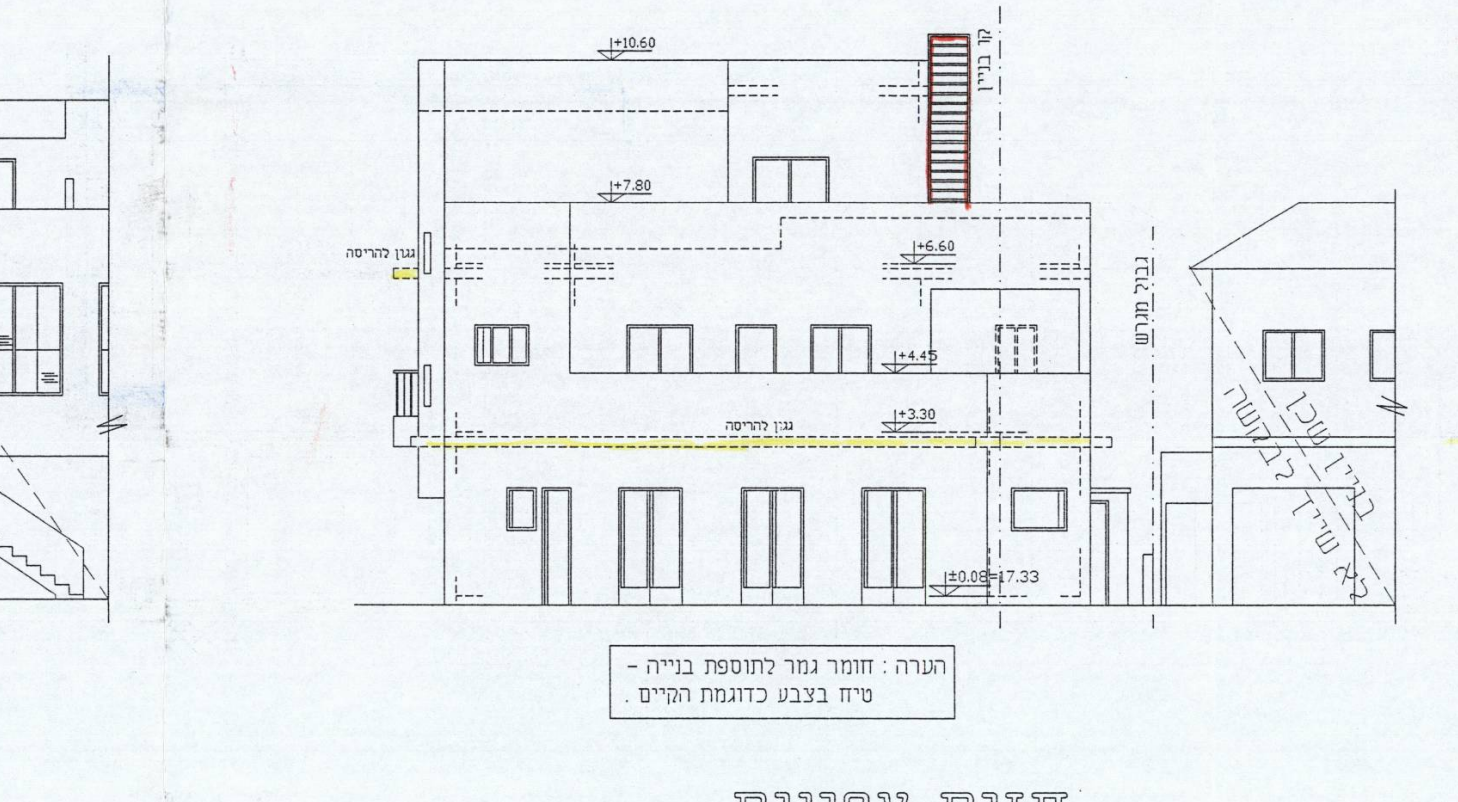

הערה: חומר גמר לתוספת בנייה – טיח בצבע כדוגמת הקיים

חזית צפונית
קנ"מ: 1:100

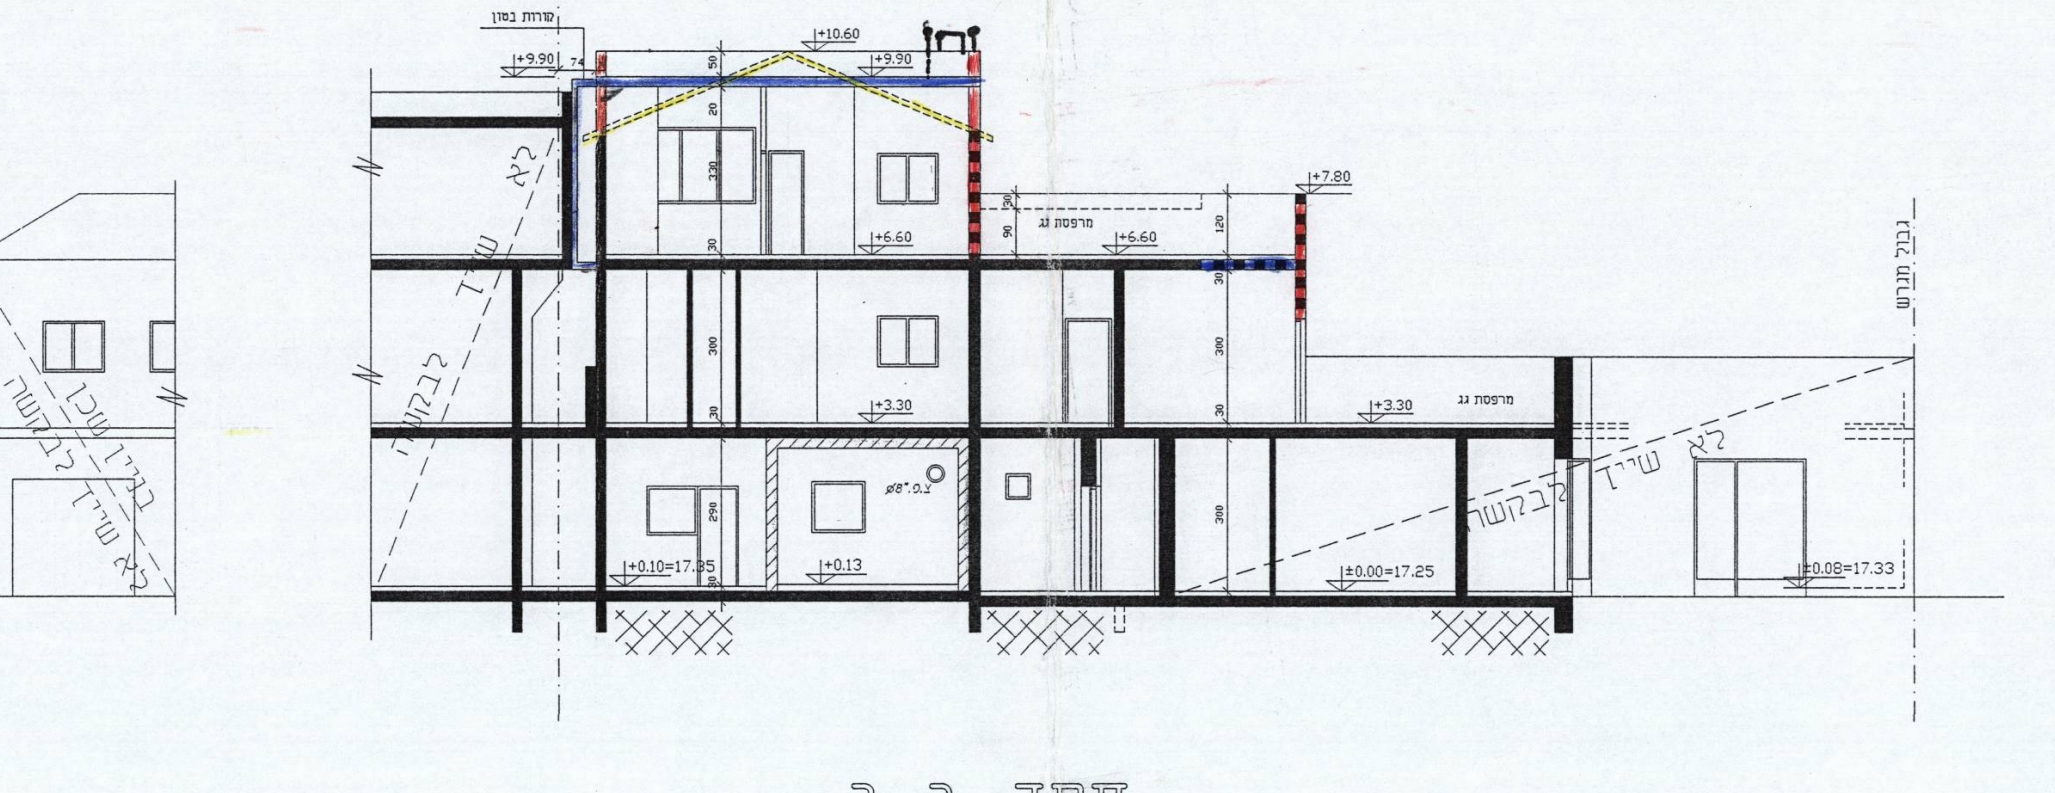

חתך ב-ב
קנ"מ: 1:100

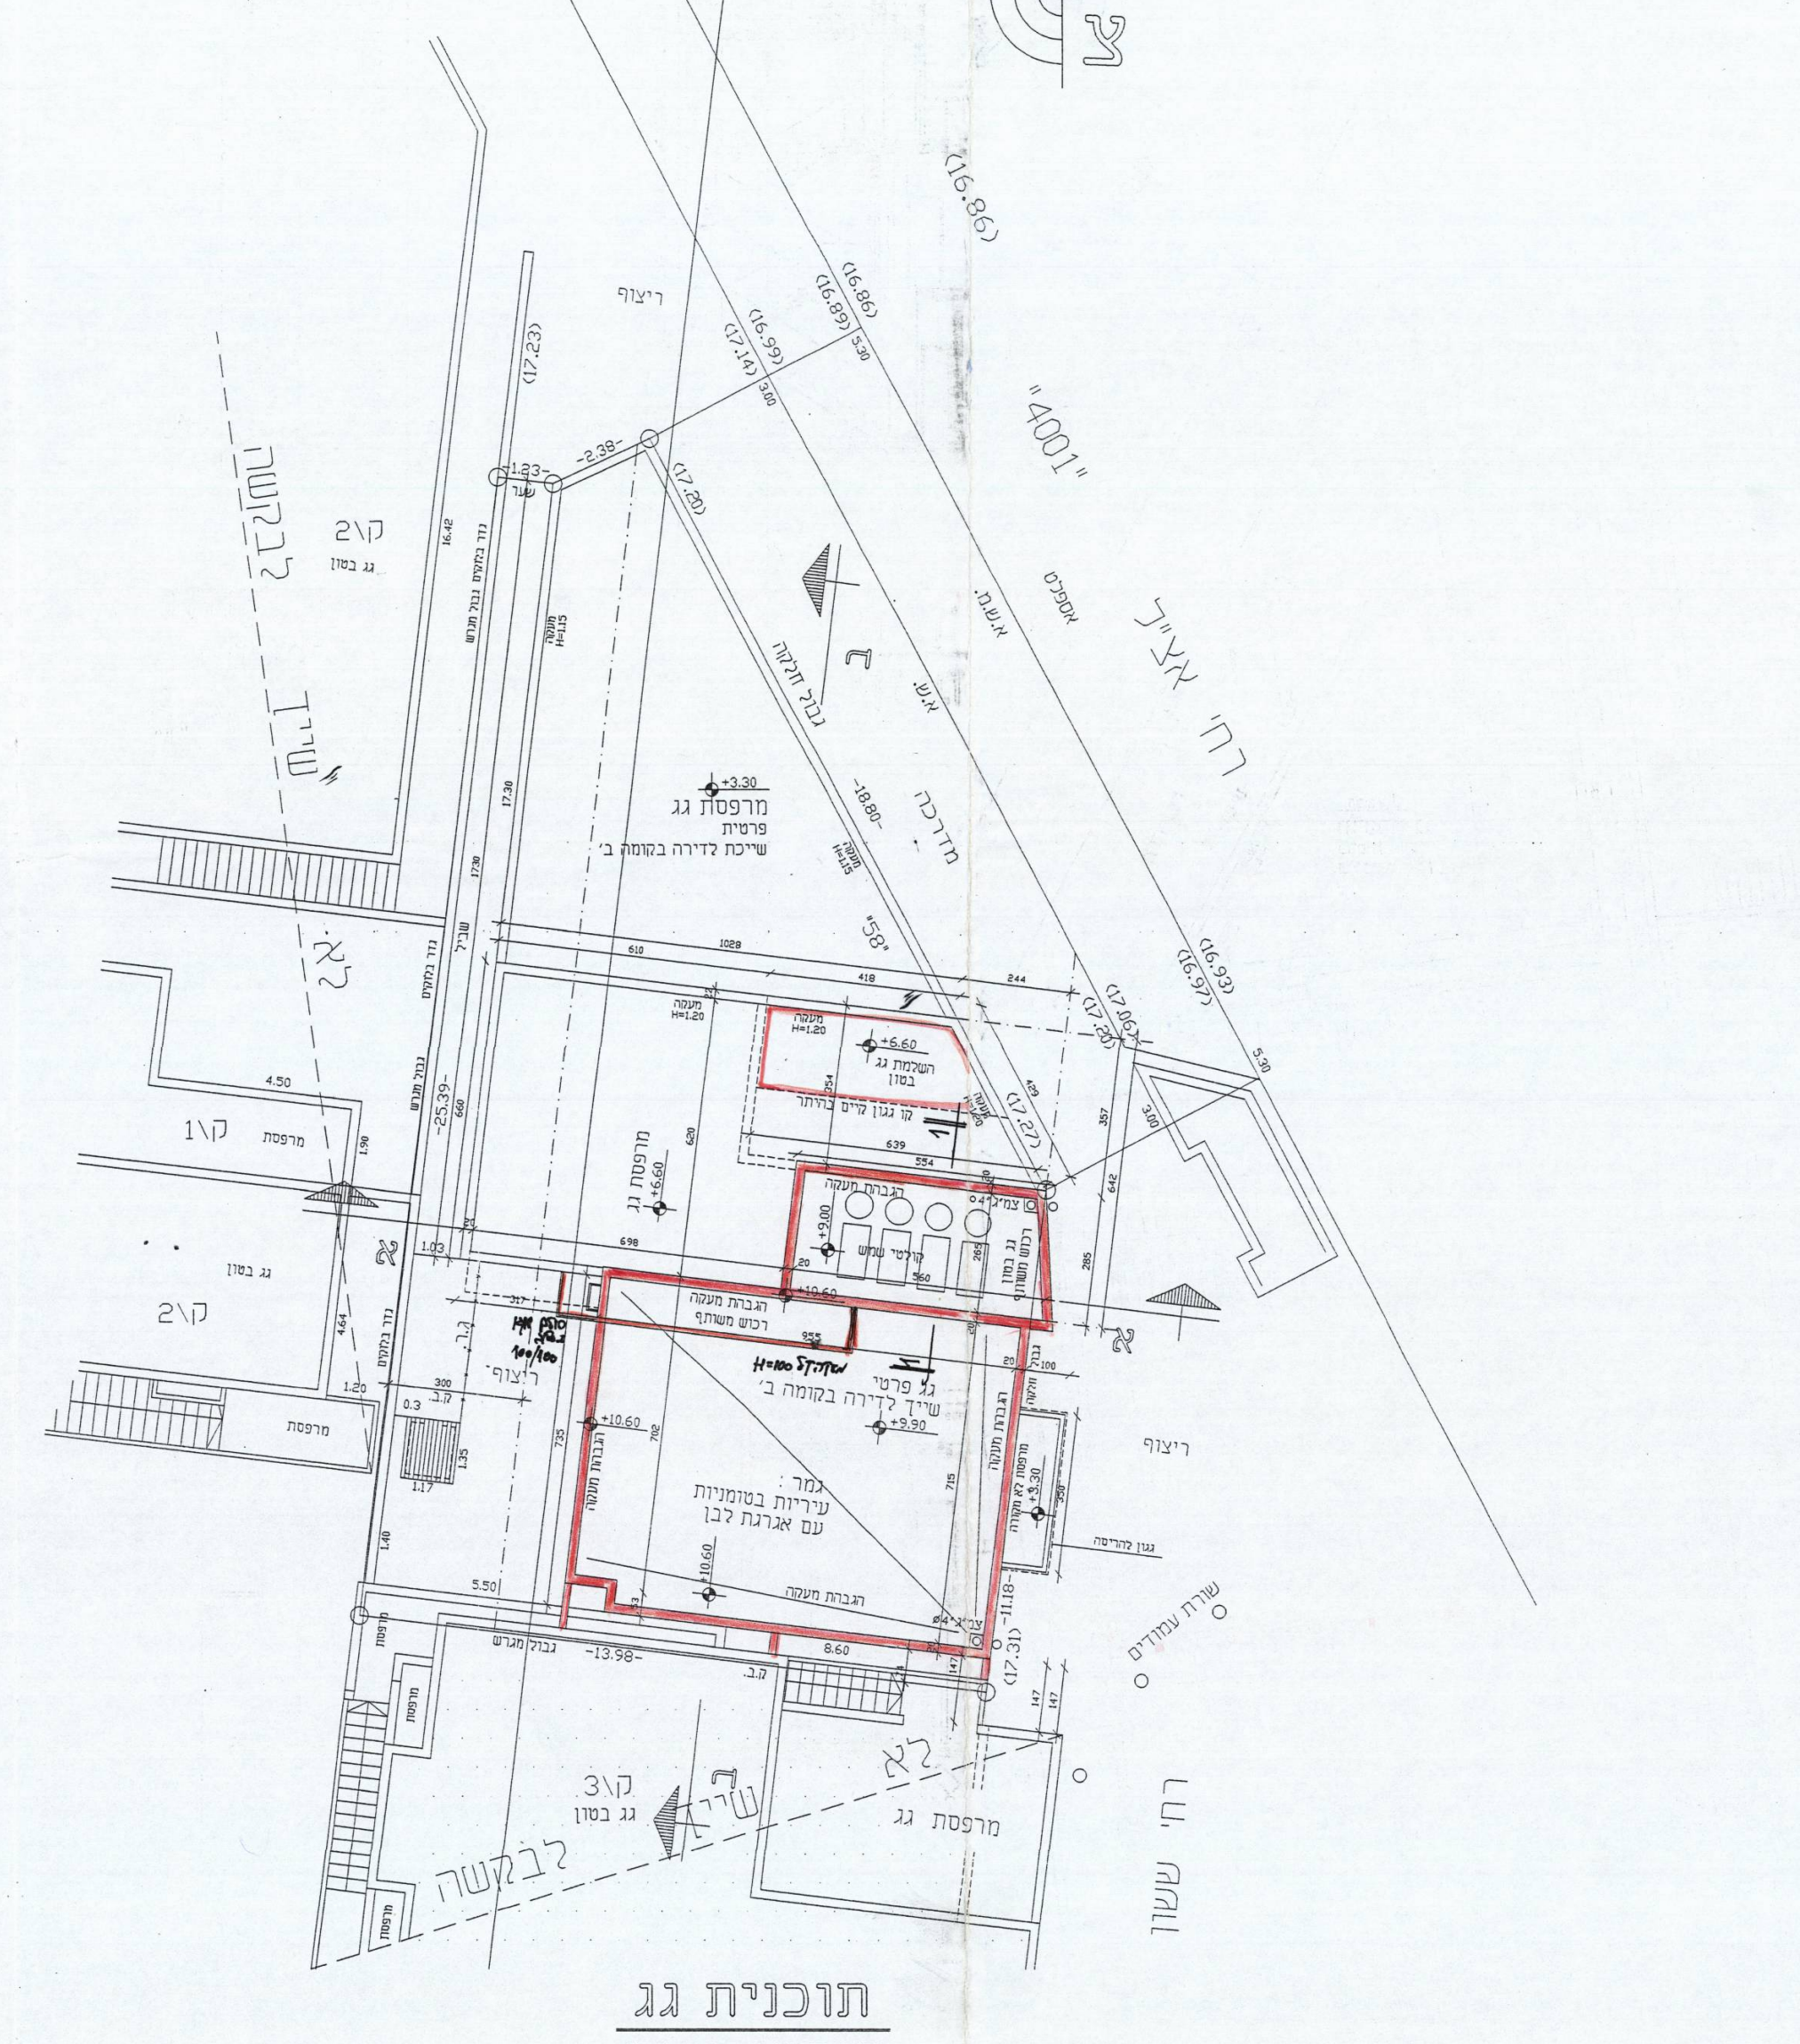

תוכנית גג
קנ"מ: 1:100

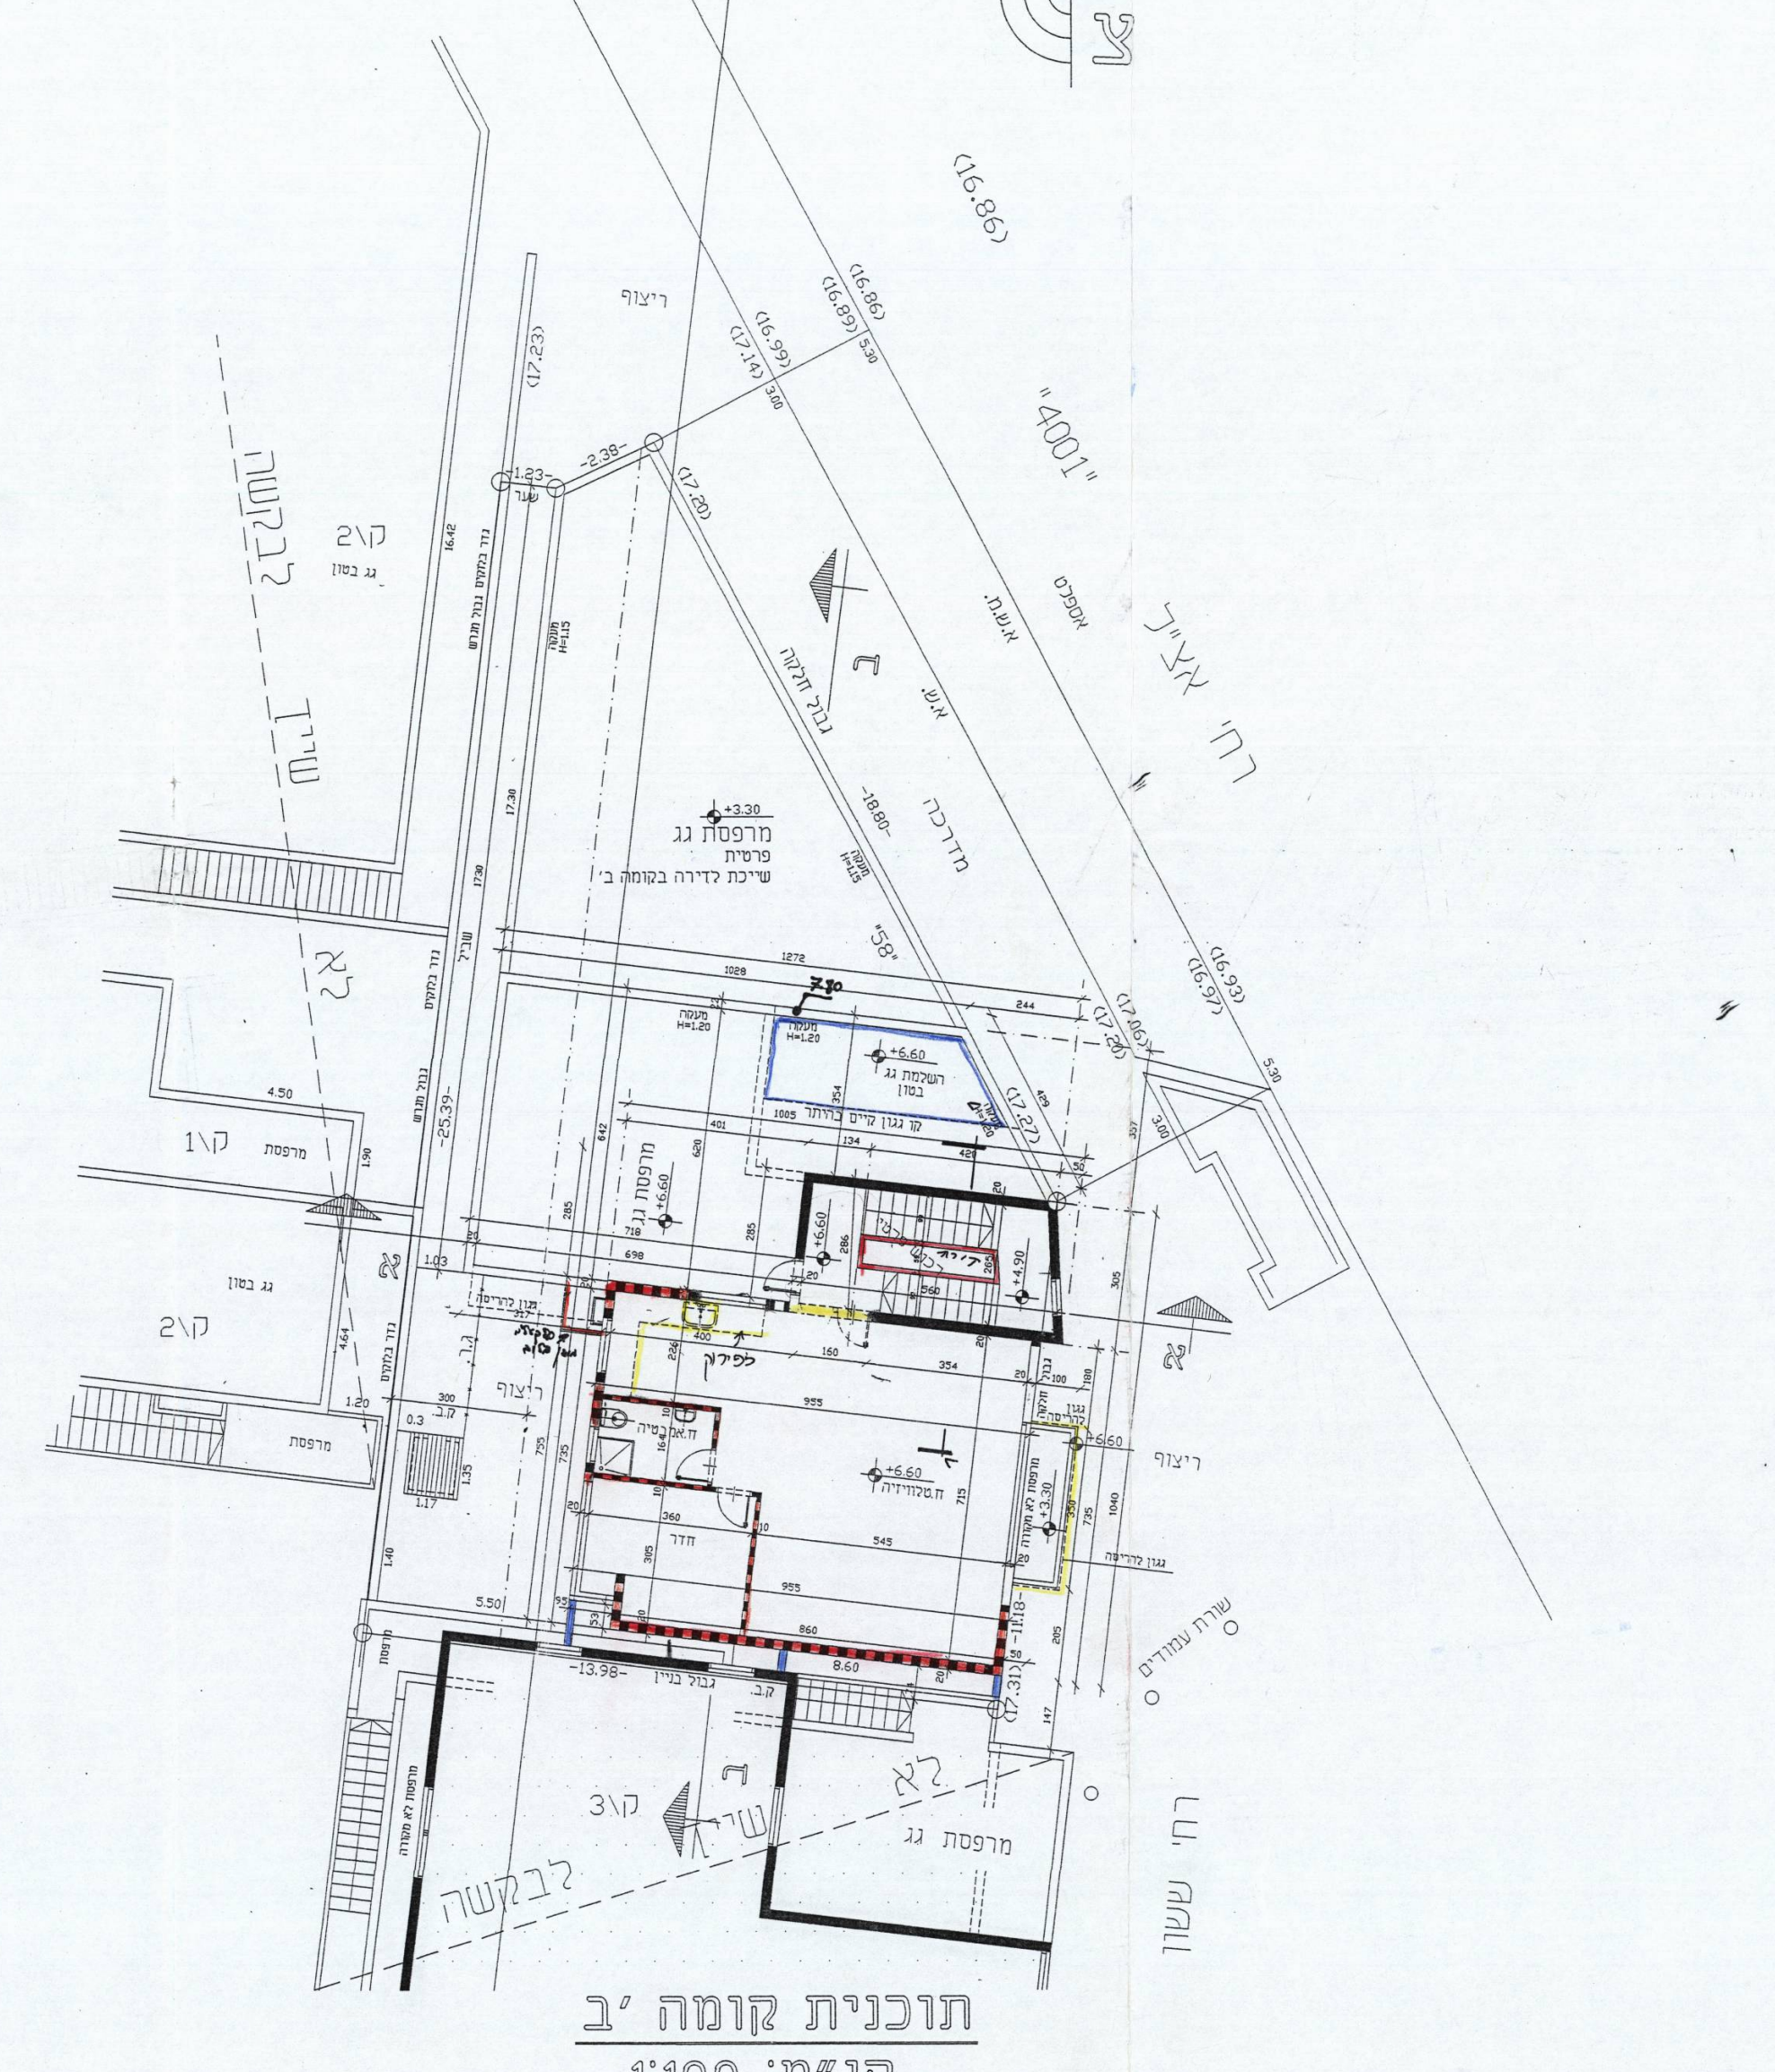

תוכנית קומה ב'
קנ"מ: 1:100

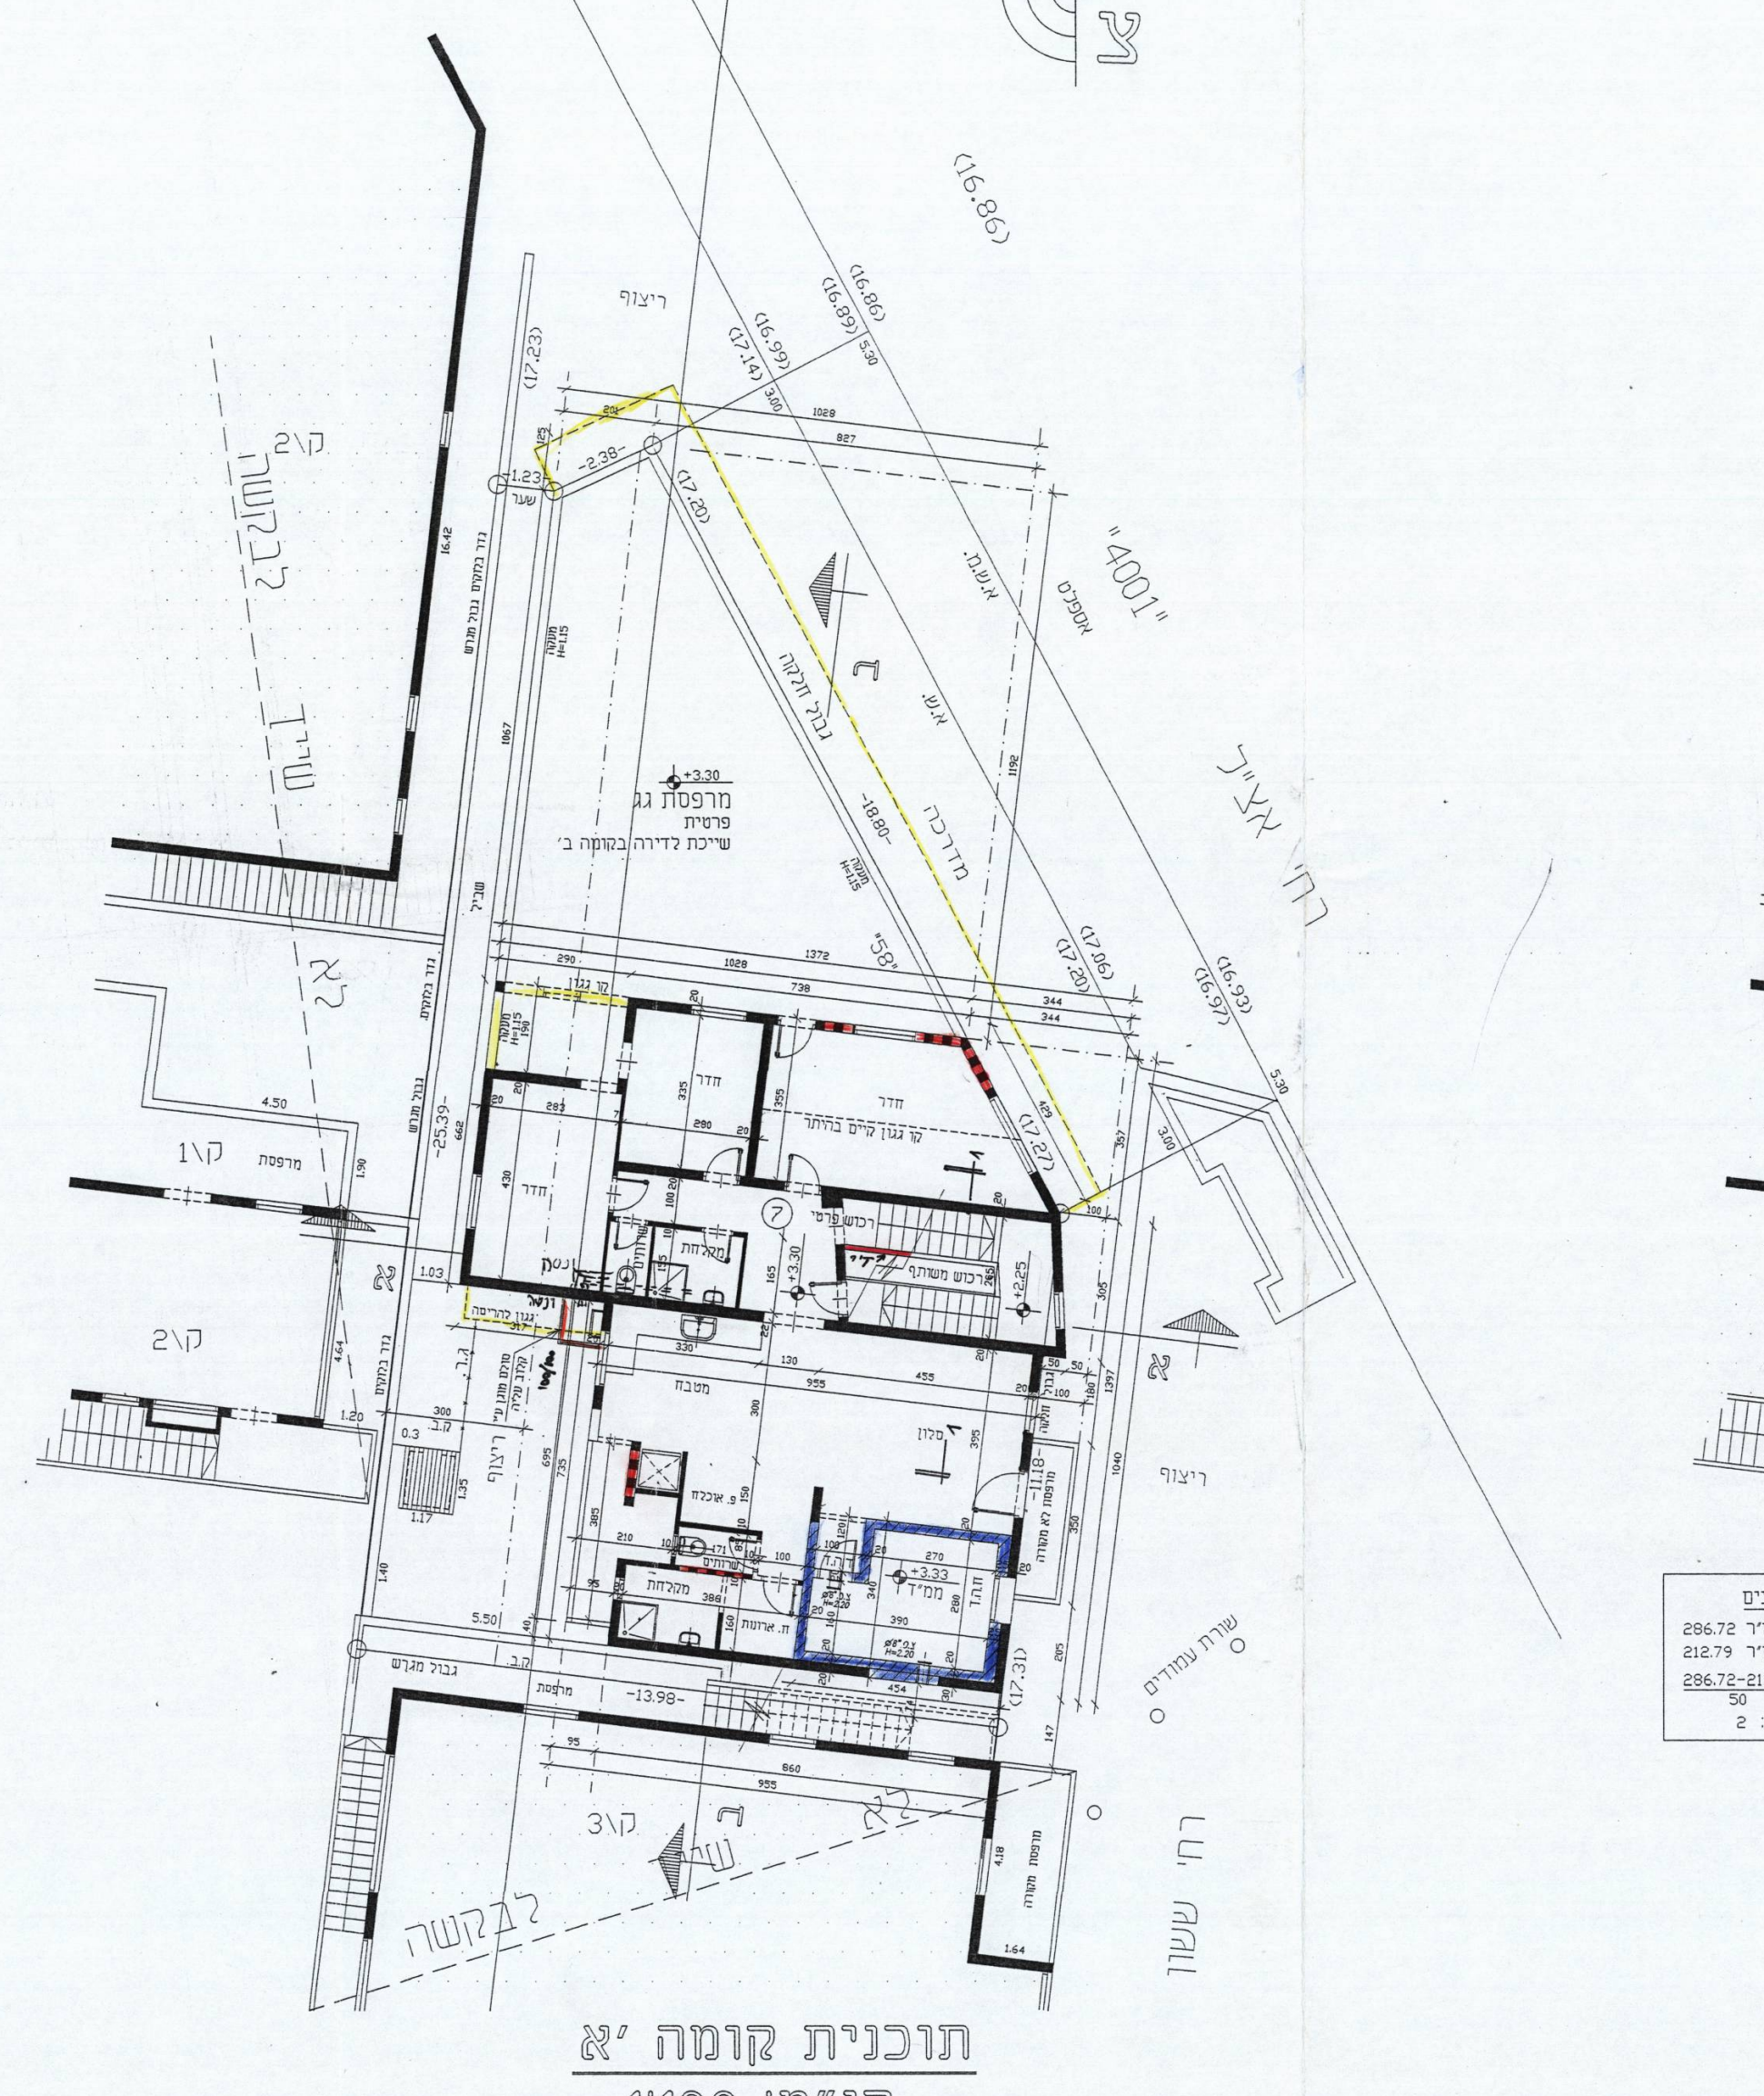

תוכנית קומה א'
קנ"מ: 1:100

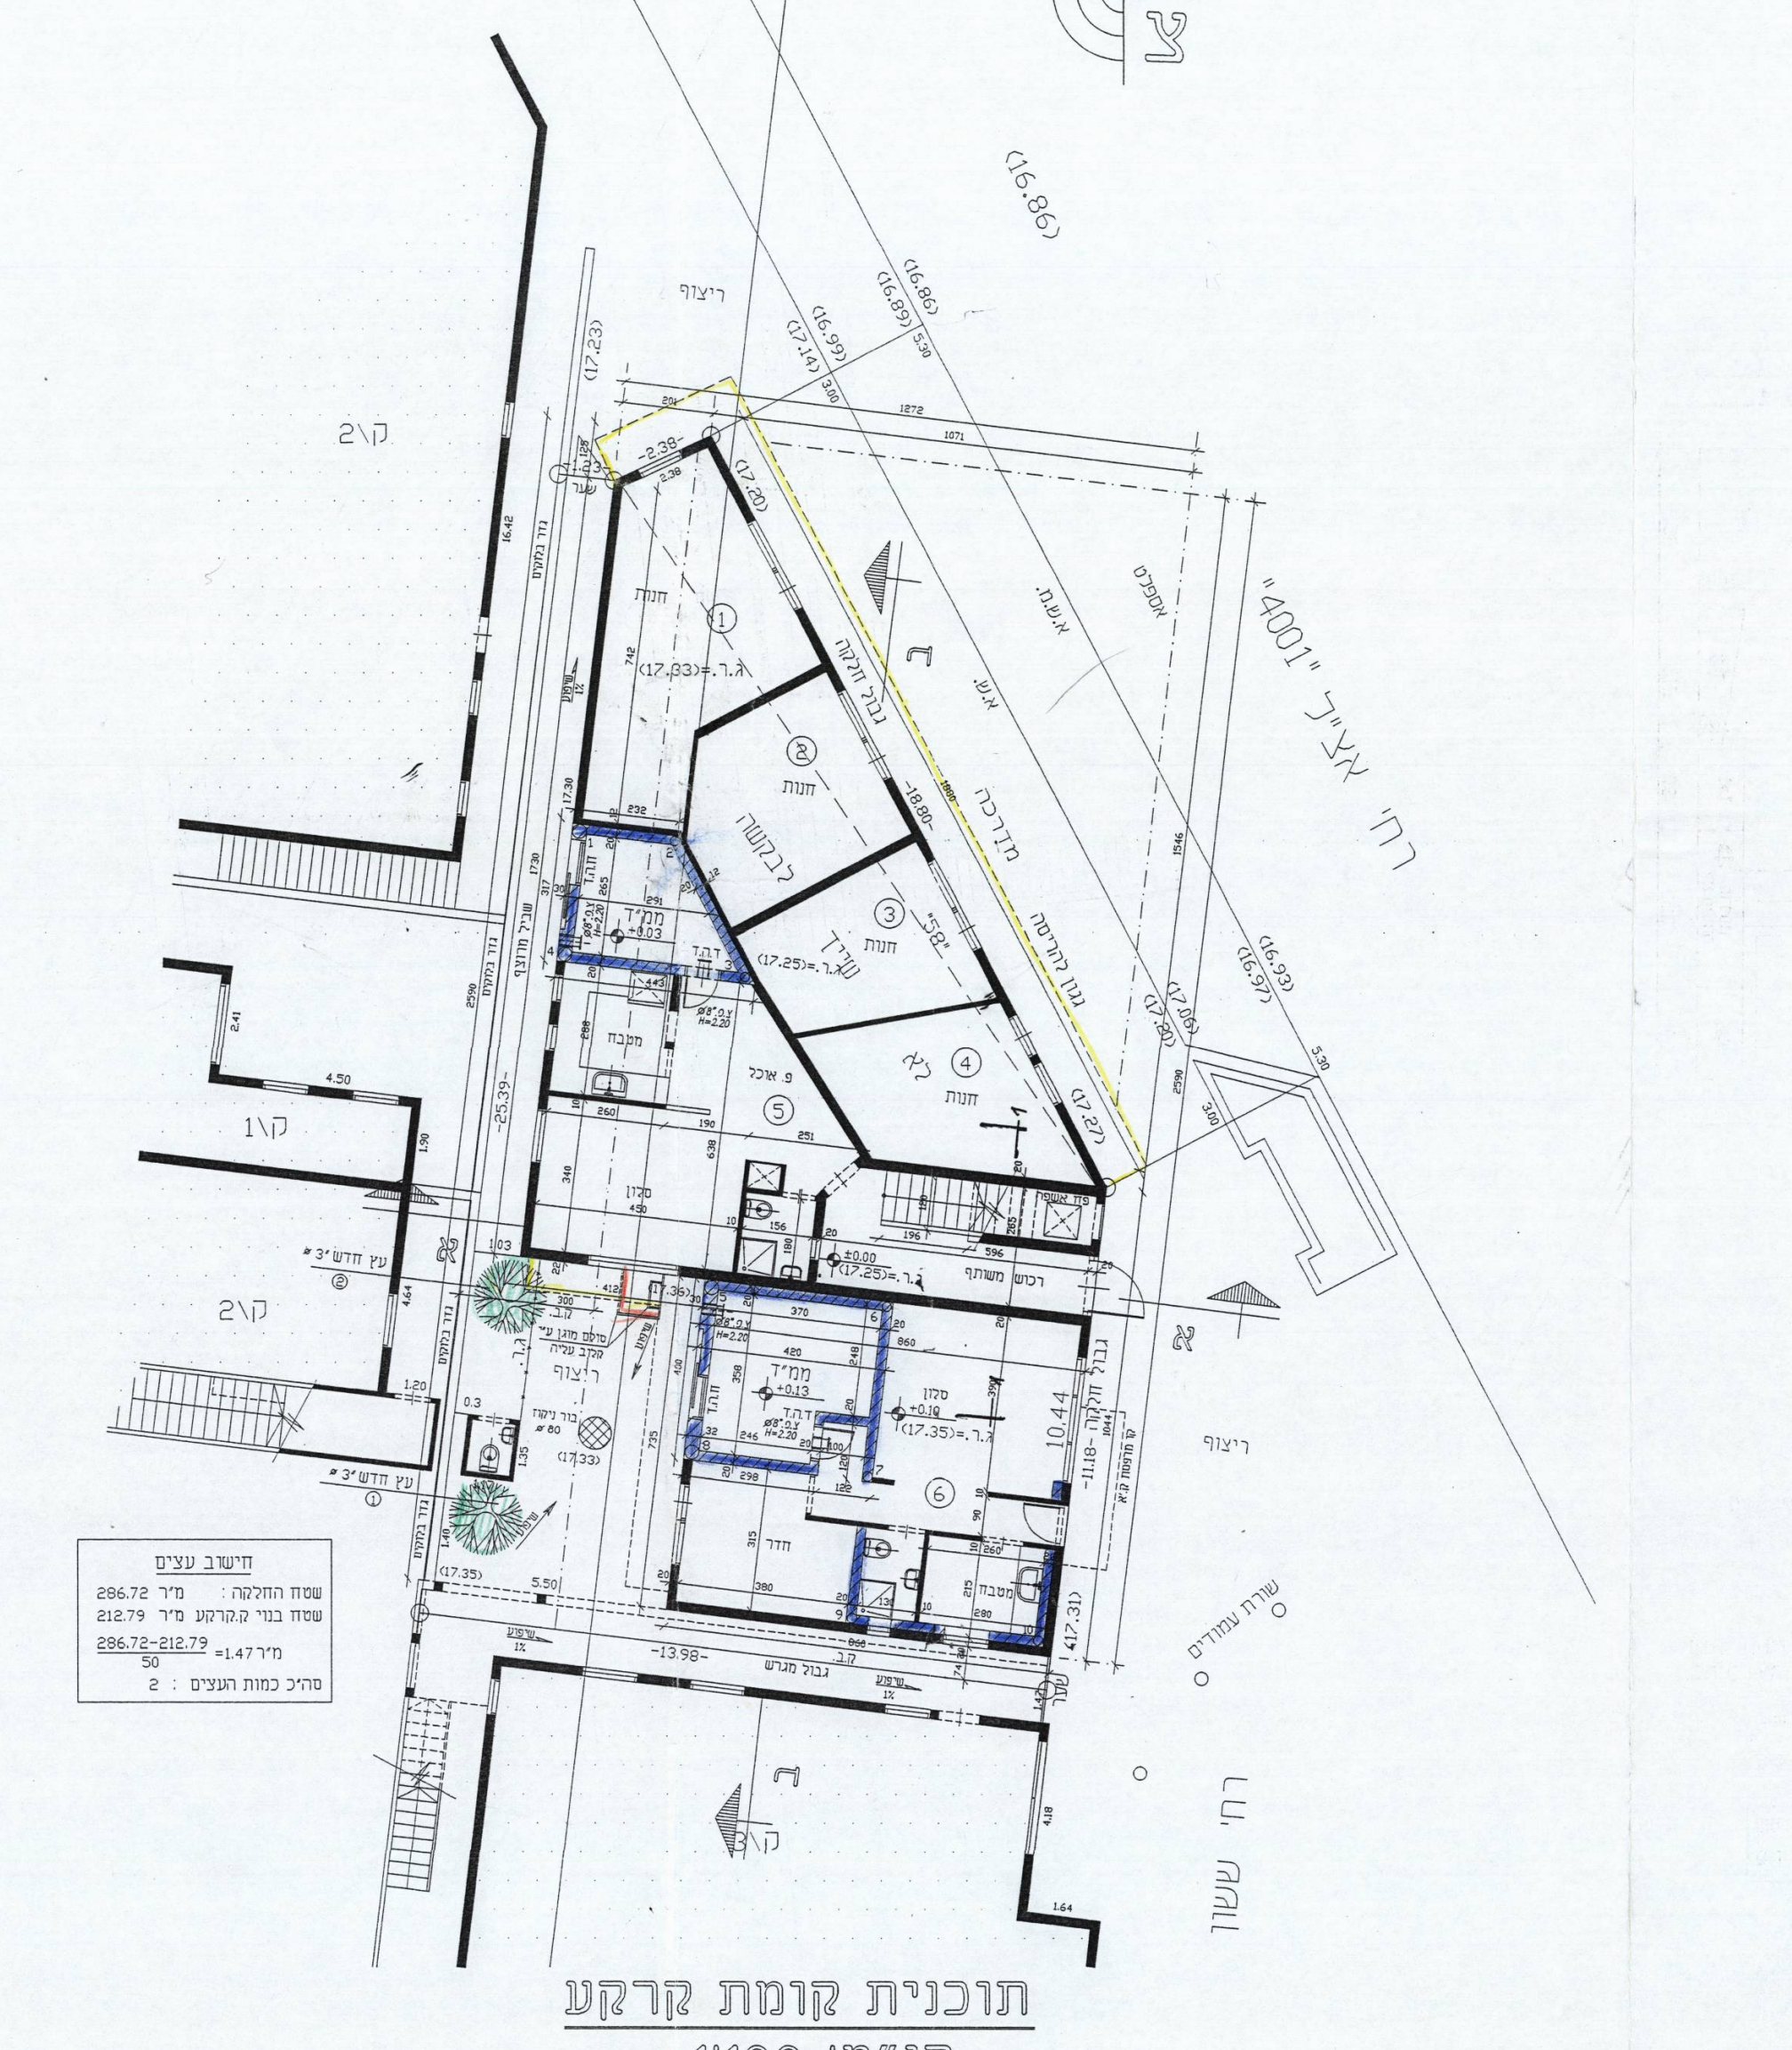

תוכנית קומת קרקע
קנ"מ: 1:100

חישוב שטחים

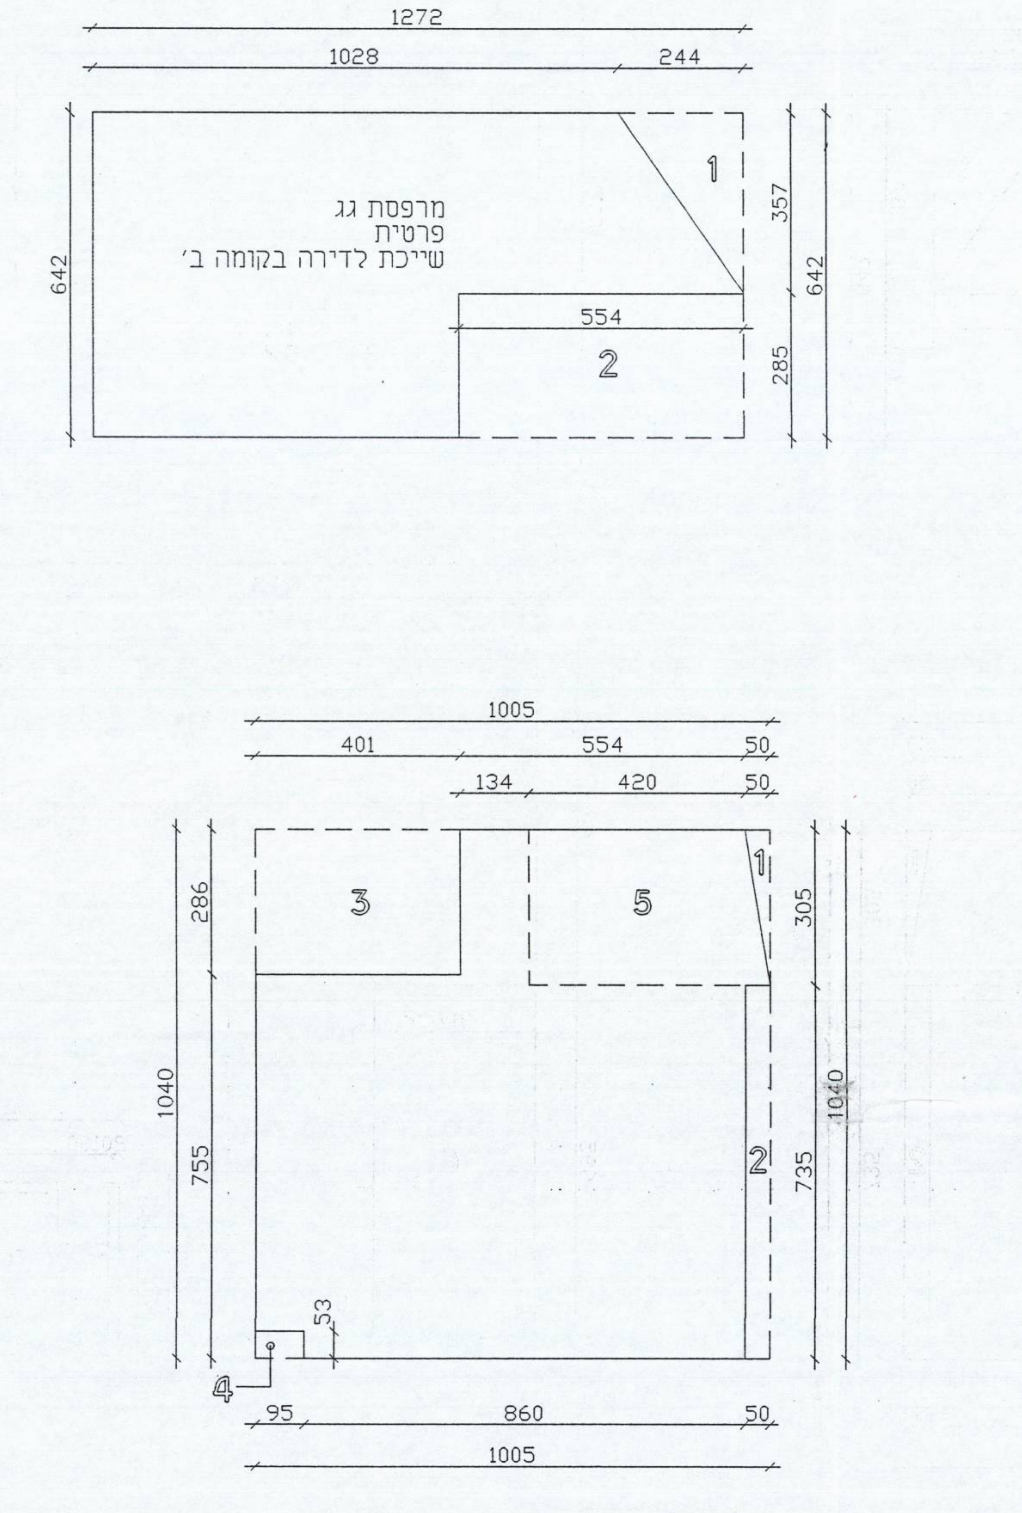

קומה ב'

שטח מסגרת: 10.05 × 10.40 = 104.52

הורדות:
1) 0.5 × 3.05/2 = 0.77
2) 0.5 × 7.35 = 3.68
3) 2.85 × 4.01 = 11.43
4) 0.95 × 0.53 = 0.50
חדר מדרגות: 5) (4.20+4.70)/2X3.07 = 13.66

סה"כ הורדות: 30.04

סה"כ שטח עיקרי: 104.72 - 30.08 = 74.48

שטח מרפסת גג ק.'ב

שטח מסגרת: 12.72 × 6.42 = 81.66

הורדות:
1) 2.44 × 3.57/2 = 4.36
2) 5.54 × 2.87 = 15.79

סה"כ שטח מרפסת: 61.51

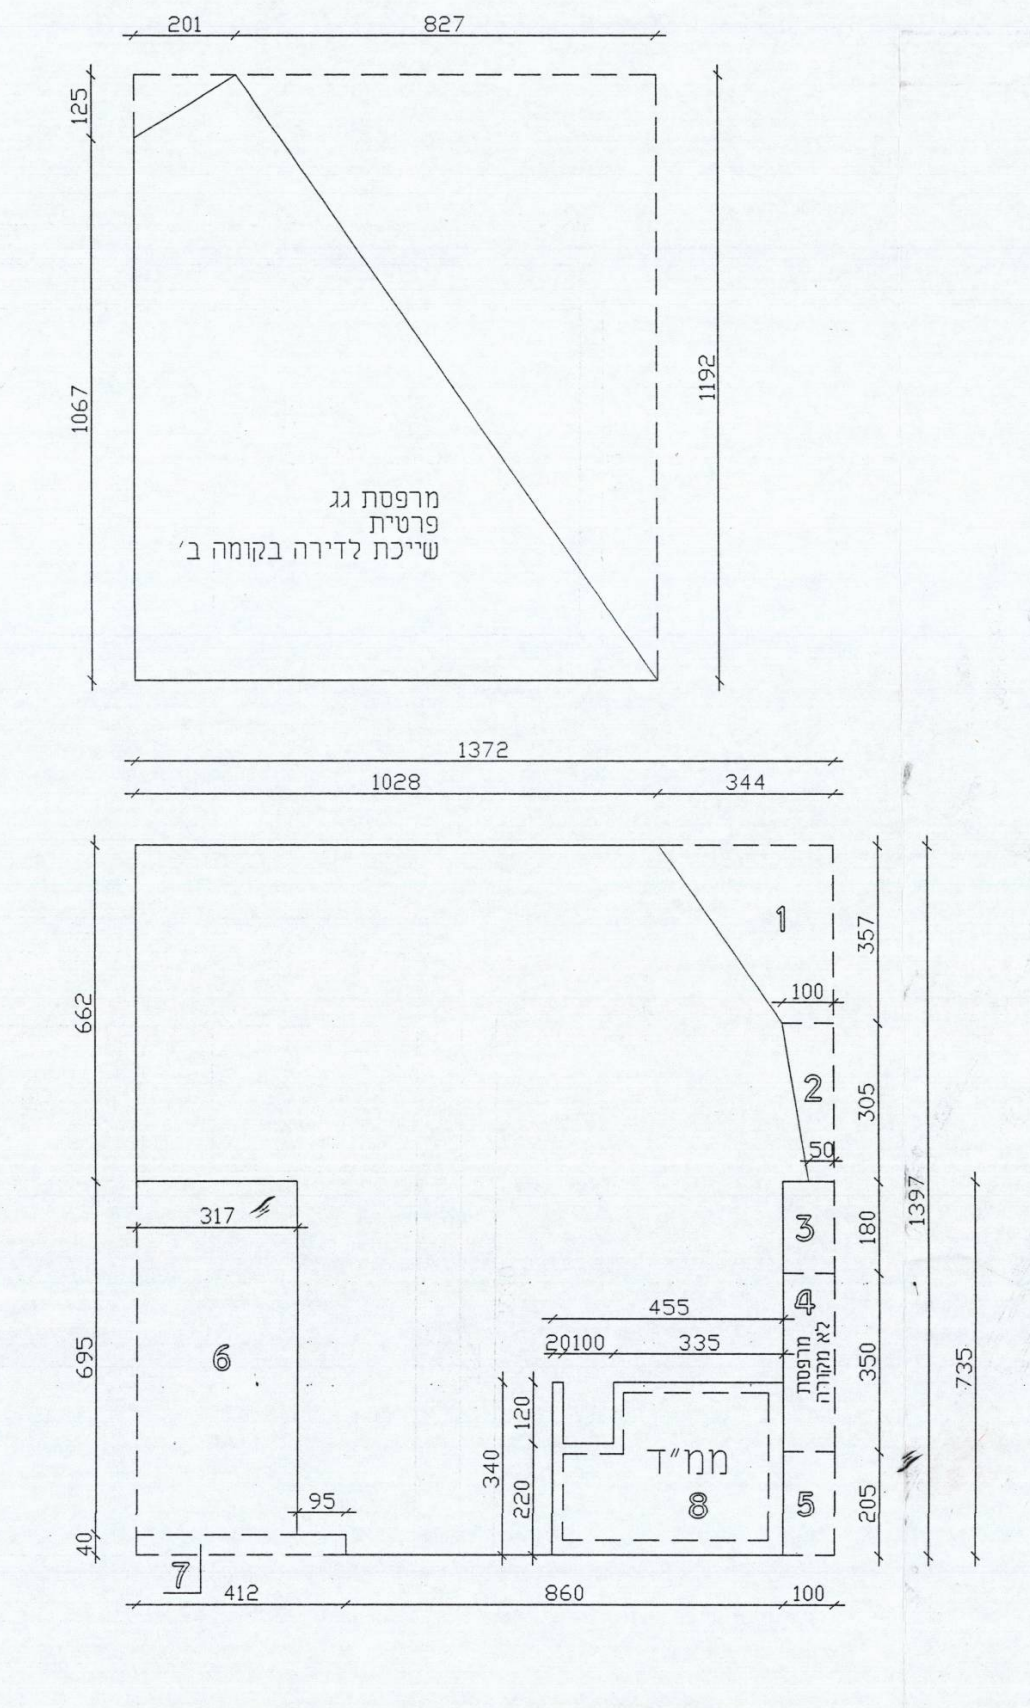

קומה 'א

שטח מסגרת: 13.72 × 13.97 = 191.67

הורדות:
1) (3.44+1.00)/2 × 3.57 = 7.91
2) (1.00+0.50)/2 × 3.05 = 2.27
3) 1.80 × 1.00 = 1.80
מרפסת לא מקורה: 4) 3.50 × 1.00 = 3.50
5) 2.05 × 1.00 = 2.05
6) 3.17 × 6.95 = 22.03
7) 0.4 × 4.12 = 1.65
שטח ממ"ד: 8) 4.55X3.40-1.20X1.00 =14.27
סה"כ שטח להורדה: 7.50

סה"כ הורדות: 48.71

סה"כ שטח עיקרי: 191.67 - 48.71 = 142.96

שטח קיים לפי היתר: 103.89
סה"כ שטח תוספת החדשה: 142.96 - 103.89 = 39.07

שטח מרפסת גג ק.'א

שטח מסגרת: 10.28 × 11.92 = 122.54

הורדות:
1) 8.27 × 11.92/2 = 49.29
2) 2.01 × 1.25/2 = 1.26

סה"כ שטח מרפסת: 71.99

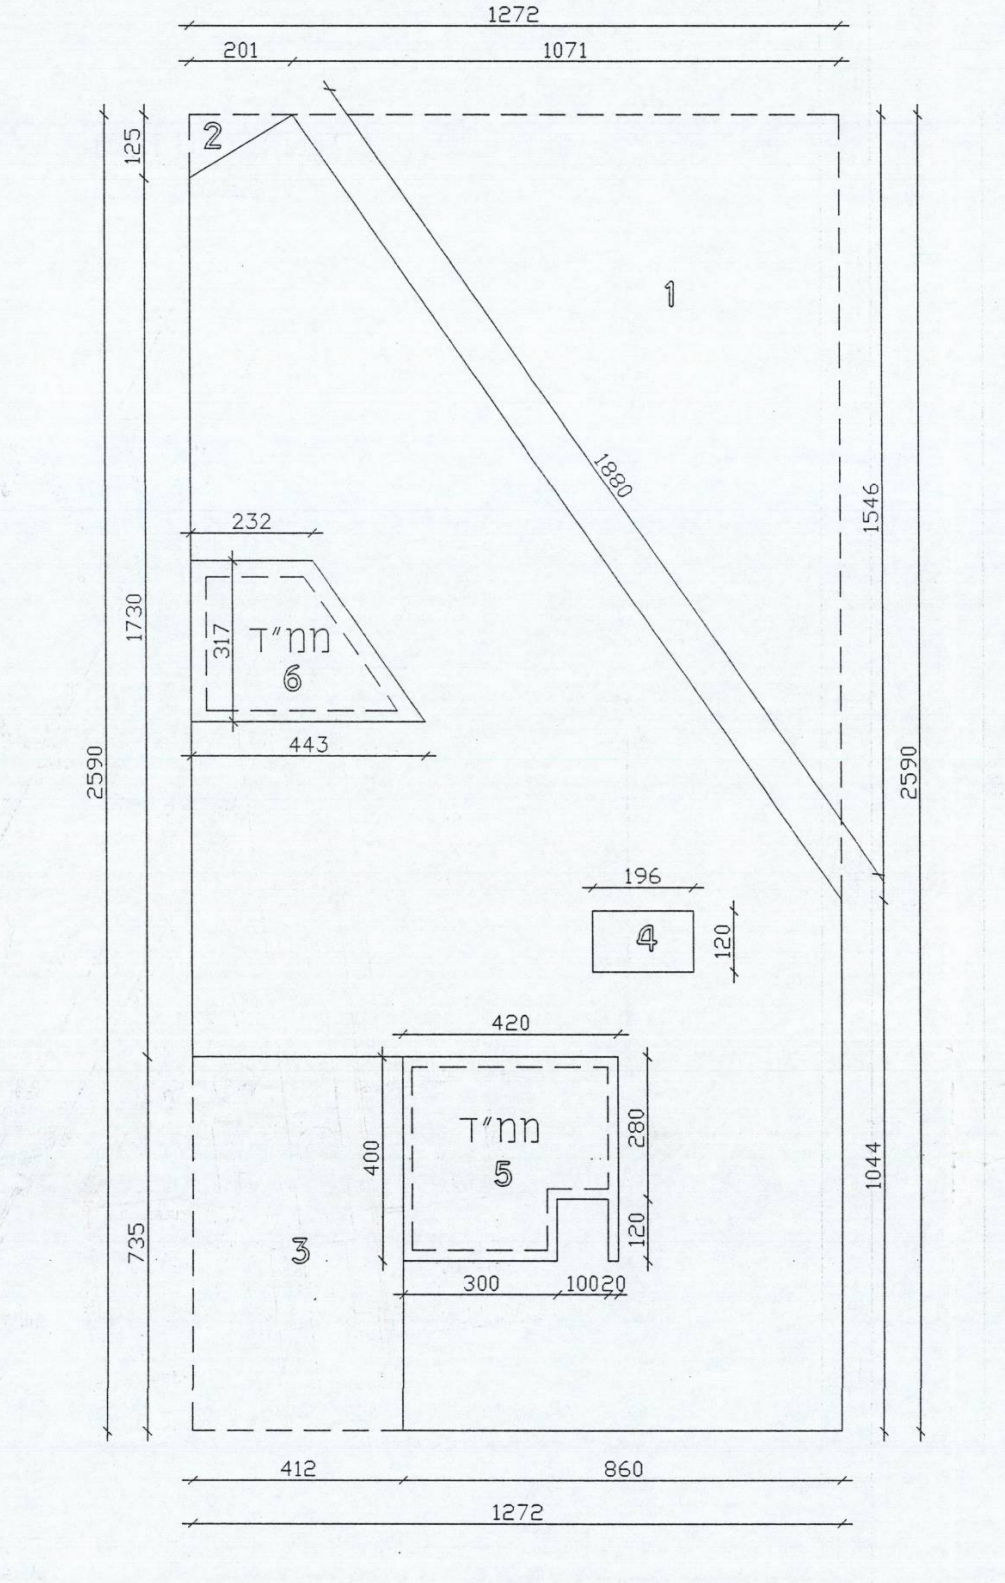

קומת קרקע

שטח מסגרת: 12.72 × 25.90 = 329.49

הורדות:
1) 10.71 × 15.46 /2 = 82.79
2) 1.25 × 2.01 /2 =1.26
3) 7.35 × 4.12 = 30.28
שטח מדרגות מתחת לגובה (H=+1.20): 4) 1.96 × 1.20 =- 2.35
שטח ממ"ד: 5) 4.00×4.20-1.00X1.20 = 15.60
סה"כ שטח להורדה: 7.50
שטח ממ"ד: 6) (2.32+4.43)/2 × 3.17 = 10.70
סה"כ שטח להורדה: 7.50

סה"כ הורדות: 131.70

סה"כ שטח עיקרי: 329.49 - 131.70 = 197.79

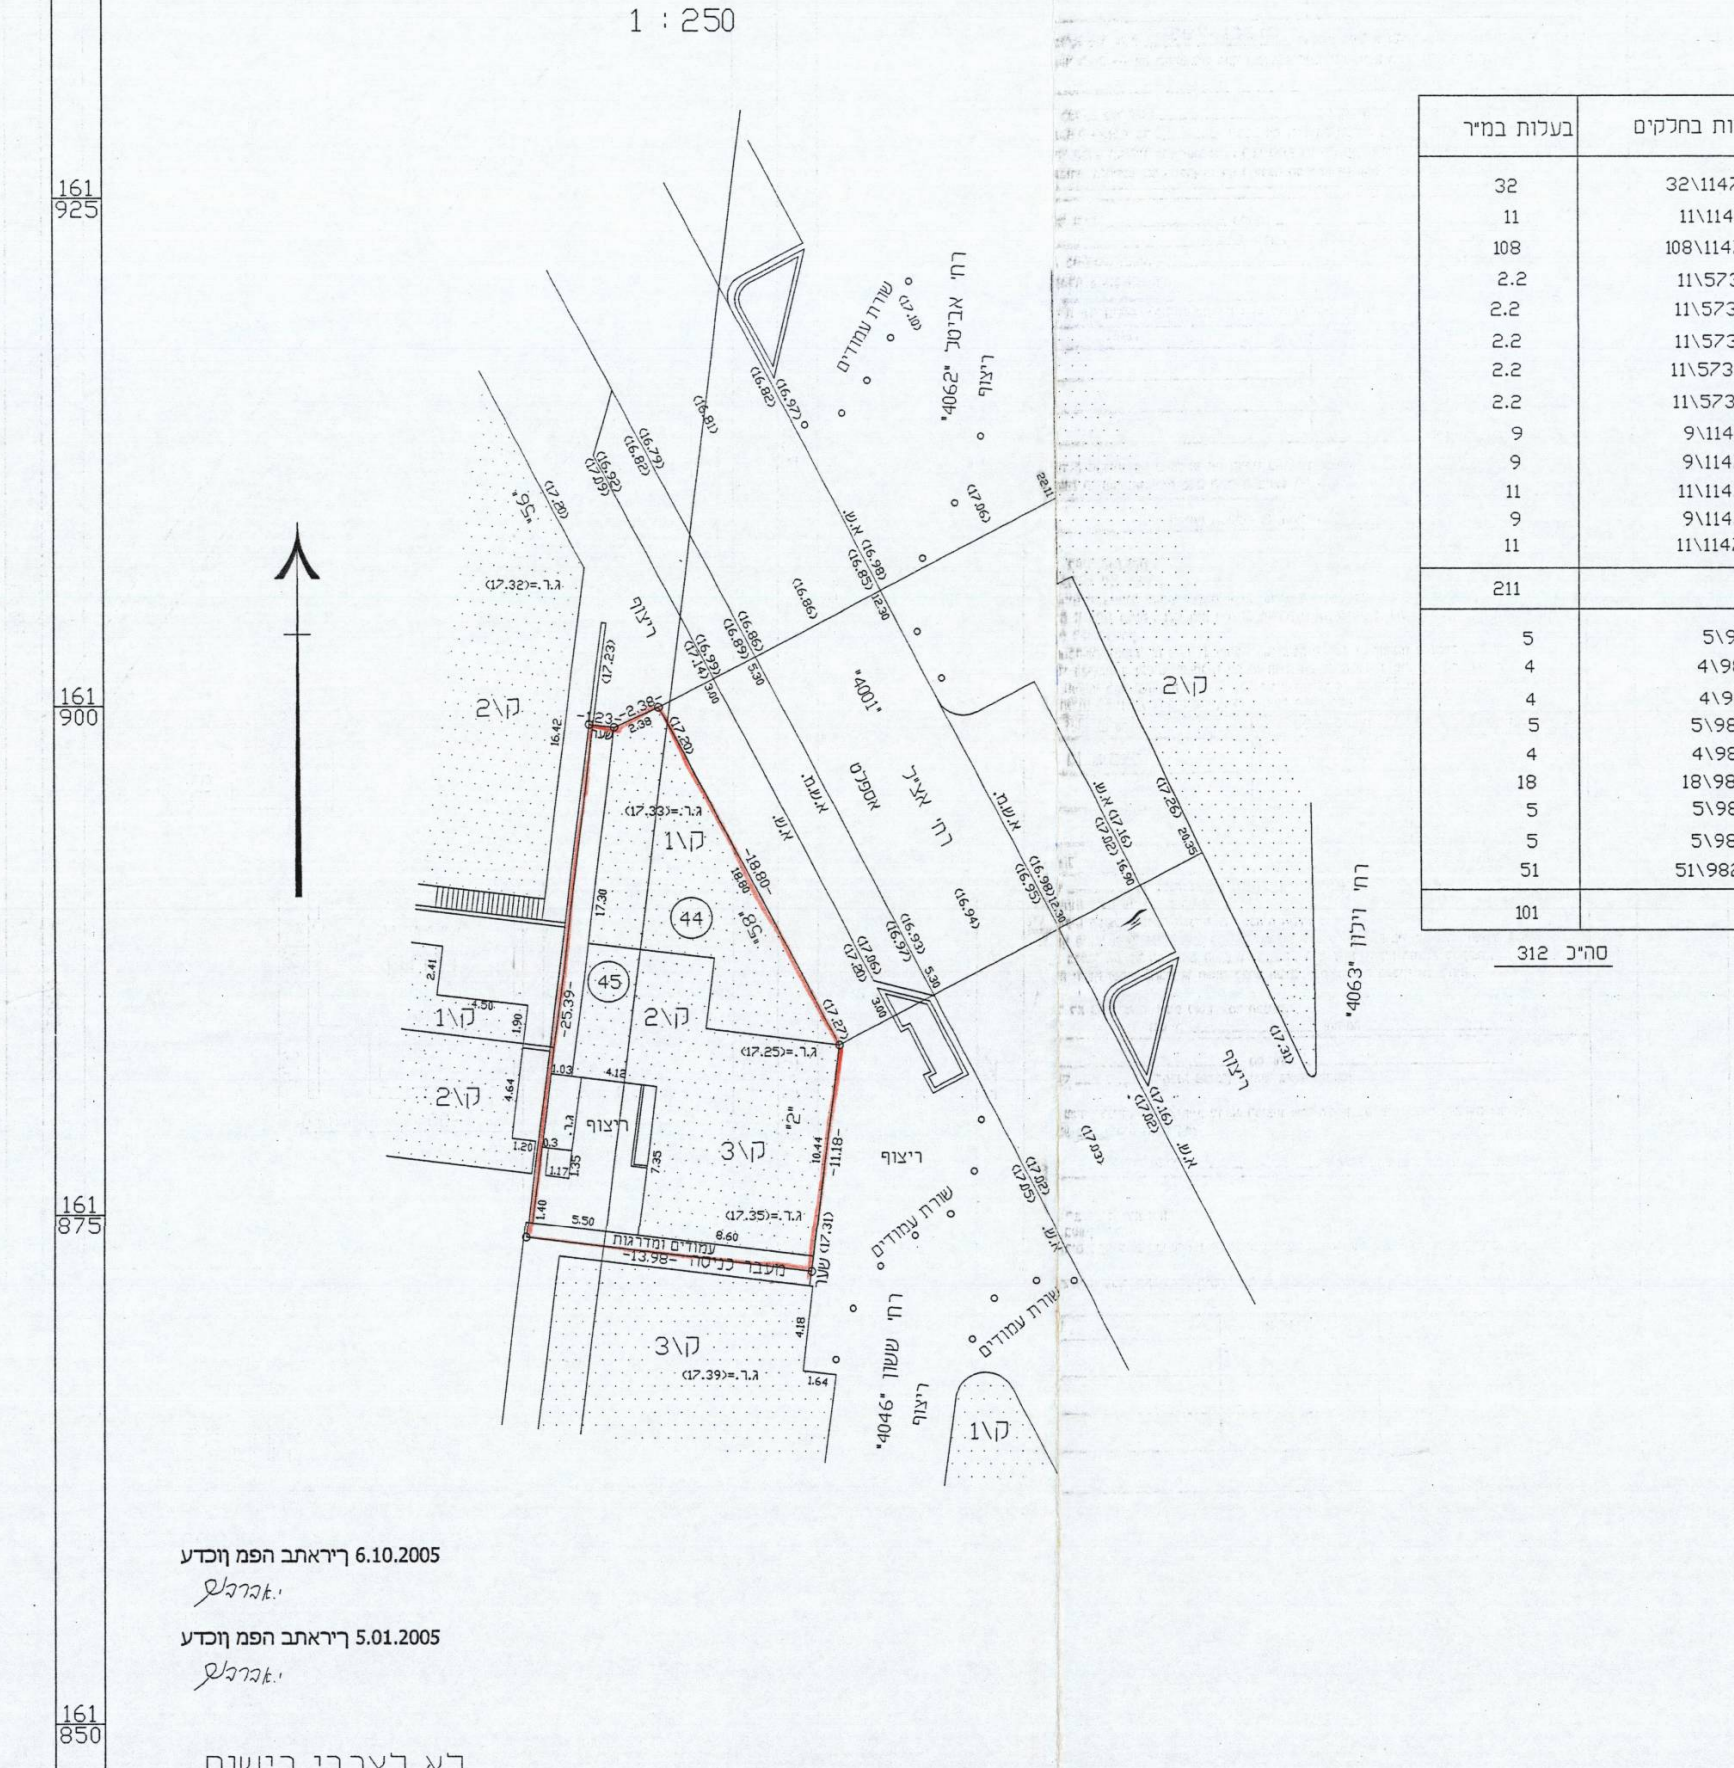

מפה טופוגרפית
1 : 250

עדכון מפה בתאריך 6.10.2005

עדכון מפה בתאריך 5.01.2005

לא לצרכי רישום

תל אביב
תאריך: 1.12.2003
י.אברבוך מודד מוסמך
רשיון מס' "461"

אברבוך ושותי מודדים מוסמכים בע"מ
דיזנגוף 190, תל-אביב טל 5235891, 03-5226791

תל-אביב
גוש: 6135
כתובת: רח' אצ"ל, 58 פינת רח' שושן, 2
הוכן עבור: משפ' יצחקי
מטרת המדידה: היתר בניה
חלקות: 45,44 (חלק)

חלקה	שם הבעלים	מסי ת.ז.	שטח חלקה כולה	בעלות בחלקים	בעלות במ"ר
44	יצחקי שושנה	0481321\8	11,476.00	32\11476	32
	יצחקי זהבה	0481322\6		11\11476	11
	יצחקי נפתלי	0481318		108\11476	108
	בן אברהם יאיר	5119051		11\57380	2.2
	דייכובסקי אביגיל	478999		11\57380	2.2
	יצחקי חנה	04449625		11\57380	2.2
	בן אברהם יונתן	004790002		11\57380	2.2
	טסה נאוה	58907663		11\57380	2.2
	מדני מזל	0479542		9\11476	9
	אריאל רחל	0481317		9\11476	9
	ורון נעמי	0481319		11\11476	11
	ורון צפורה	0481320		9\11476	9
	מזרחי חרותה	0481323		11\11476	11
					211
45	בן אברהם מירים	0478998	9,821.00	5\9821	5
	מדני מזל	0479542		4\9821	4
	אריאל רחל	0481317		4\9821	4
	ירון נעמי	0481319		5\9821	5
	ירון ציפורה	0481320		4\9821	4
	יצחקי שושנה	0481321\8		18\9821	18
	יצחקי זהבה	0481322\6		5\9821	5
	מזרחי חרותה	0481323		5\9821	5
	יצחקי נפתלי	0481318		51\9821	51
					101
					סה"כ 312

בעלות במ"ר: 312
שטח מדוד (מ"ר): 286.72 (188.50+98.22)
חלקה44 188.50מ"ר
חלקה45 98.22 מ"ר

שטח מגרש משני: ________

שטח להפקעה: ________

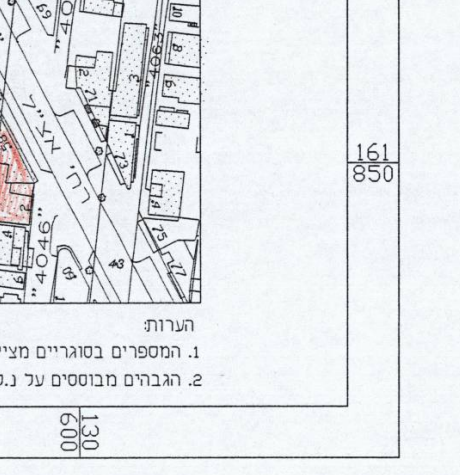

תשריט הסביבה 1:1250

עיריית תל - אביב - יפו
מינהל ההנדסה, אגף רישוי ופיקוח על הבנייה

20

לכבוד
☒ הועדה המקומית לתכנון ולבנייה
☐ רשות הרישוי המקומית

706-0027

חוק התכנון והבניה, התשכ"ה-1965
תקנות התכנון והבניה (בקשה להיתר תנאיו ואגרות) התש"ל-1970
בקשה להיתר בנייה או לשימוש במקרקעין

מס' תיק הבניין	מס' בקשה קודמת להיתר בנייה	מס' הבקשה למידע	מתאריך
4001-058		מ-2004-	

א. פרטי הנכס והמבקשים

הכתובת	רחוב	מס' בית	גוש	חלקה
	אצ"ל	58	6135	44,45

	שם משפחה / שם פרטי	מס' זהות/חברה	רחוב ומספר בית / ישוב ומיקוד	מספר טלפון
מבקש 1	נפתלי בן יהודה	02355164-1	רח' אצ"ל 58 תל-אביב	058-631247
מבקש 2	נפתלי יצחק נפתלי ציונה	00481318-4 0046932-4	רח' אצ"ל 58 תל-אביב	03-6874166
מבקש 3				
בעל הזכות בנכס	נפתלי יצחק	00481318-4	רח' אצ"ל 58 תל-אביב	03-6874166
החוכר				
עורך הבקשה הראשי	דוד בן מיכאל	313616799	רח' משה דיין 66 חולון	03-5530617
מתכנן שלד הבניין	דוד בן מיכאל	313616799	רח' משה דיין 66 חולון	03-5530617

ב. מהות הבקשה

☒ בקשה לתוספת בנייה
תוספת 1 קומות לבניין
הכוללות: 2 יחידות דיור
☒ תוספת בנייה בקומה א', ב' ☒ רחוית ☒ לאחור ☒ לצד
בשטח של 121.21 מ"ר
☒ שינויים פנימיים הכוללים: שינוים בקומת קרקע וקומה א' וקומת גג + ביצוע ממ"דים
☒ אישור מצב קיים
קיים בניין בן-2 קומות + בניה על הגג
המקום משמש כיום ל- מגורים
☒ בהיתר ☐ בלי היתר

ג. מפרט - תיאור הבקשה

תיאור הקיים על המגרש: קיים בניין בן-2 קומות + בניה על הגג. סה"כ 7 יח' דיור.

שימוש עיקרי: ☒ מגורים

סוג העבודה או השימושים המוצעים: ☒ תוספת לבניין

הגורם שבהוצאת בעבודת הבנייה: ☒ גורם פרטי

שטחים: 286.72 מ"ר, 439.03 מ"ר, 153.13 %

ד. חומרי הבנייה

יב. מינויים מטעם מבקש ההיתר

דוד בן מיכאל 313616799

דוד בן מיכאל 83824

נספח בתיחום זה
הוכן על תוכנית זהה
לתוכנית שהוגשה לרשויות
....
חתימת האדריכל

נסרק

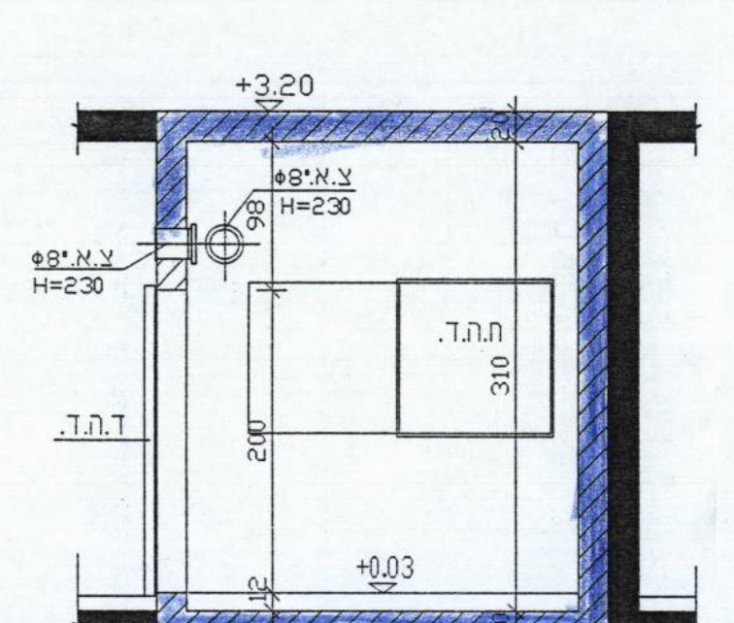

חתך 2-2
1:50

+3.20
צ.א.*Φ8
H=230
ת.ה.ד.
ד.ה.ד.
310
200
+0.03

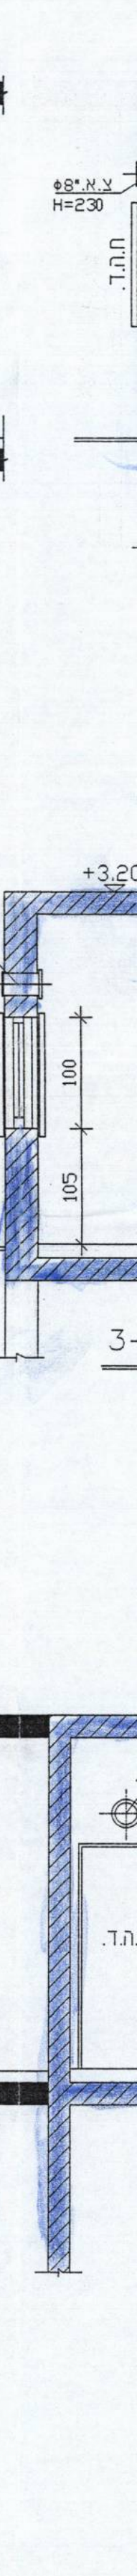

+3.20
צ.א.*Φ8
H=230
ת.ה.ד.
100
105

מקרא

⅄	שקע
T.V	טלויזיה
Ⓣ	טלפון
Ⓗ	ג.ת. חרום 40w
═	ג.ת. פלוריסנט 2*40w
♂	מפסק בודד

מיקרא:

░	בטון ממשיך
▨	בטון מפסיק
☒	קיים

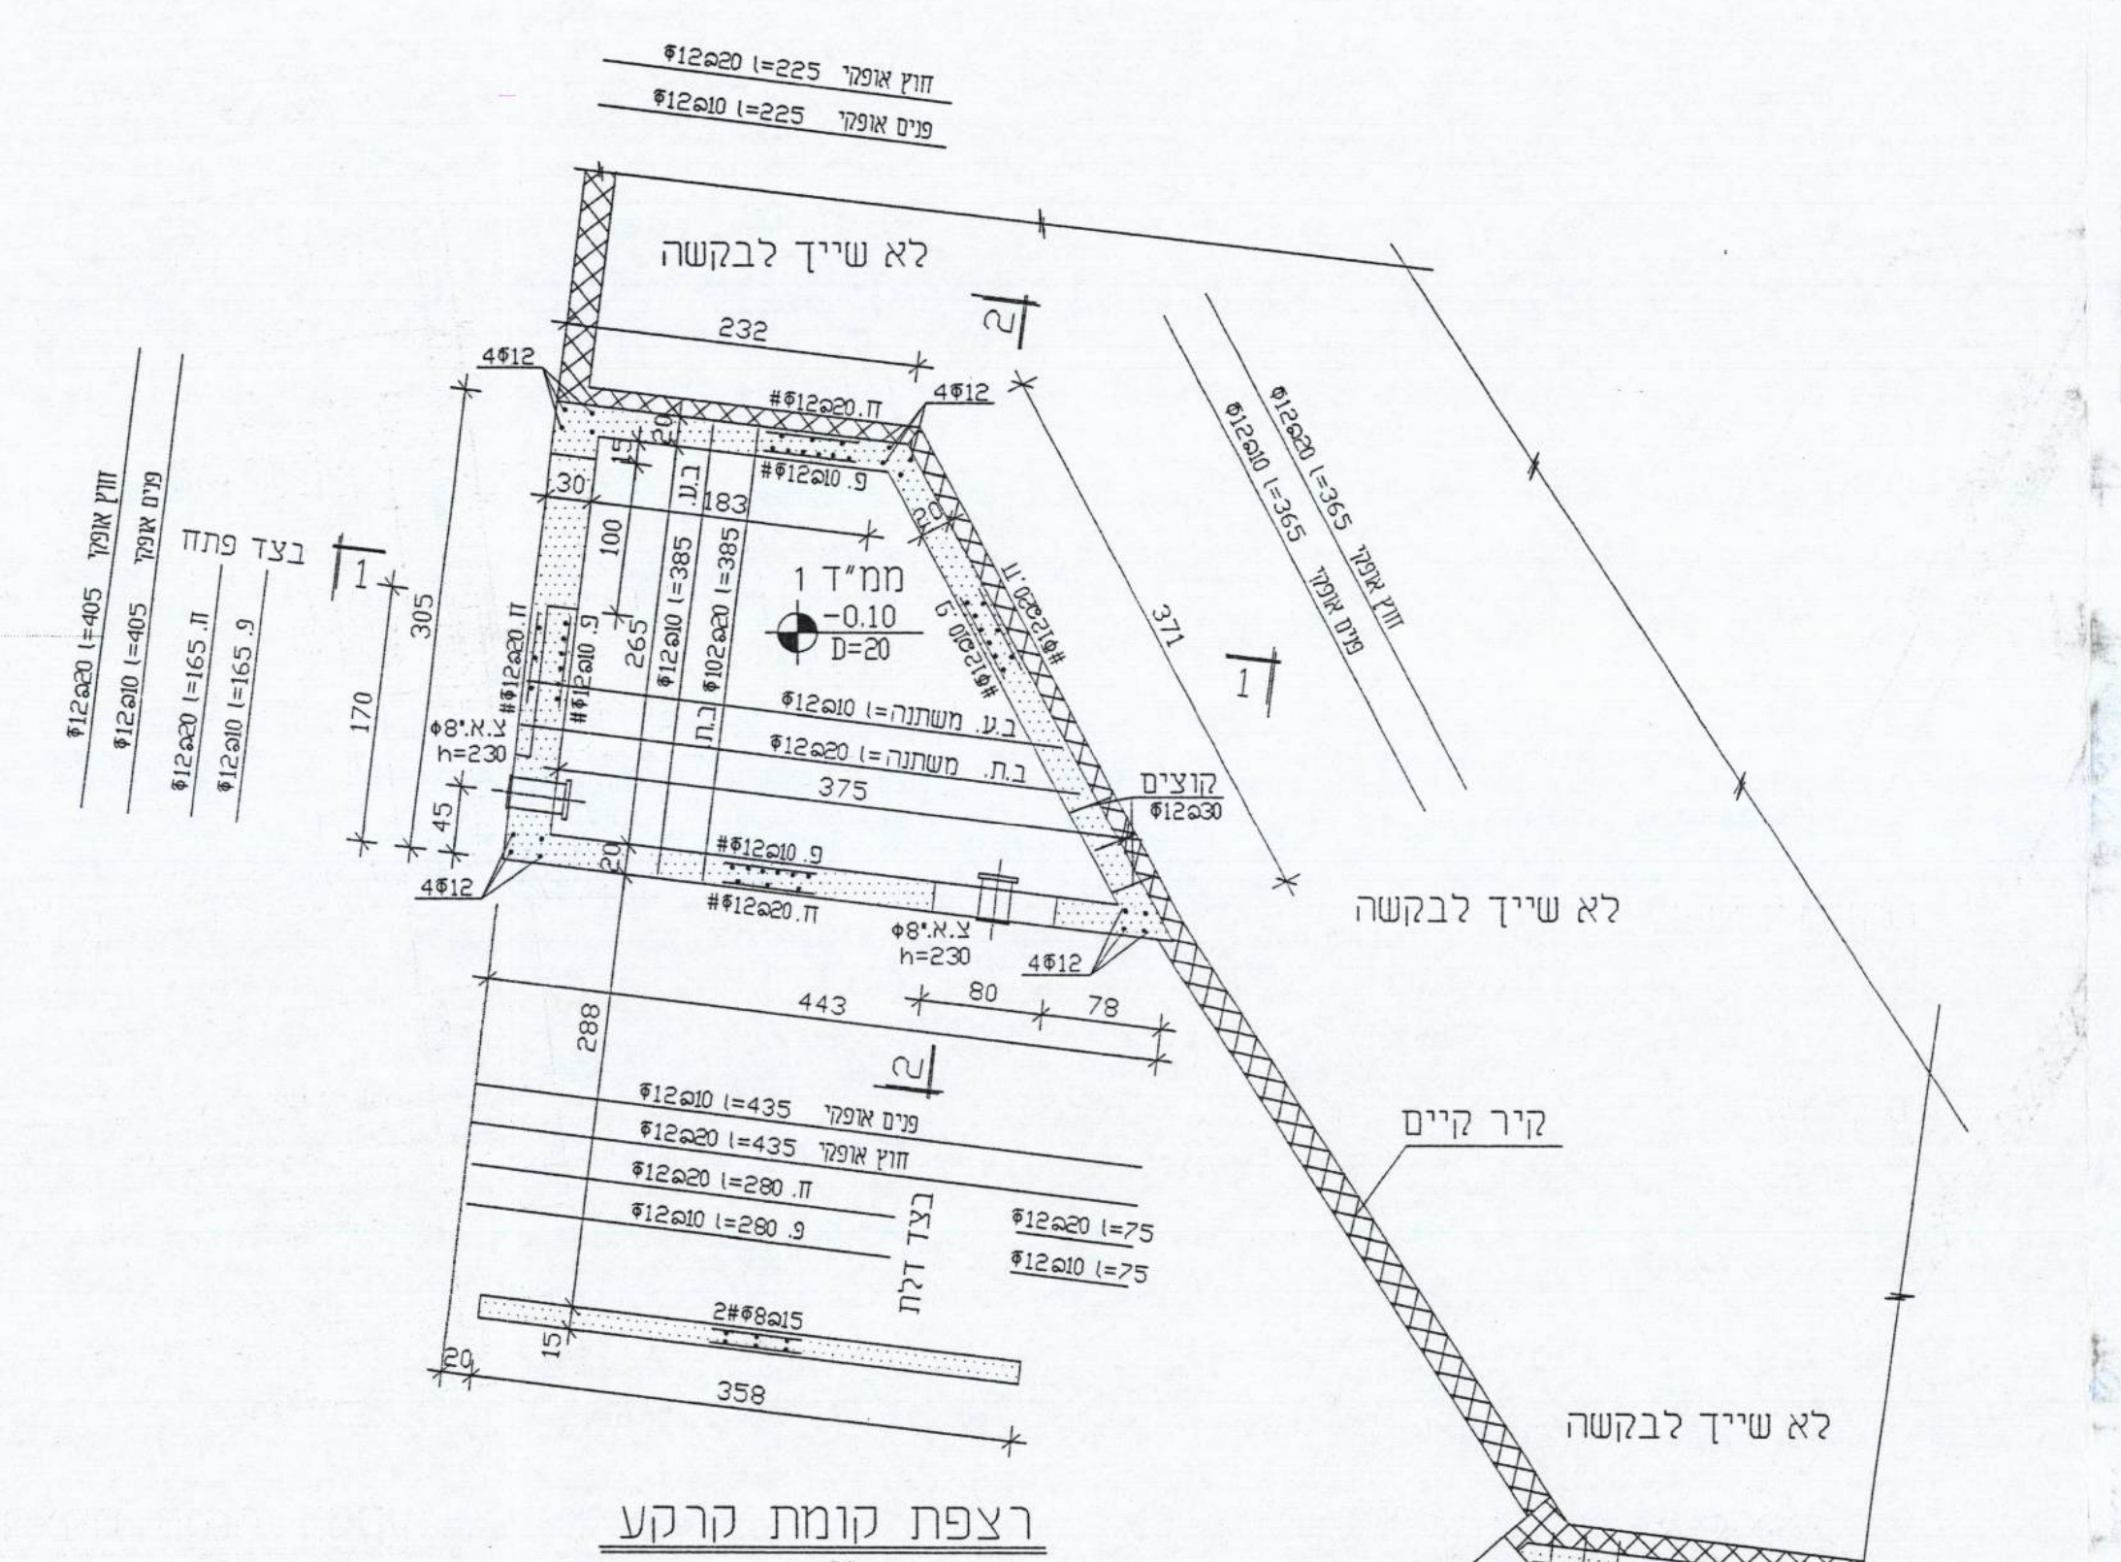

רצפת קומת קרקע
1:50

Φ12@20 l=225 חוץ אופקי
Φ12@10 l=225 פנים אופקי
לא שייך לבקשה
232
4Φ12
ממ"ד 1
-0.10
D=20
בצד פתח
Φ12@20 l=405
Φ12@10 l=405
Φ12@20 l=165 .ח
Φ12@10 l=165 .פ
Φ12@20 l=365
Φ12@10 l=365
371
375
443
288
Φ12@10 l=435
Φ12@20 l=435
Φ12@20 l=280 .ח
Φ12@10 l=280 .פ
Φ12@20 l=75
Φ12@10 l=75
בצד דלת
2#Φ8@15
358
קוצים Φ12@30
קיר קיים
לא שייך לבקשה

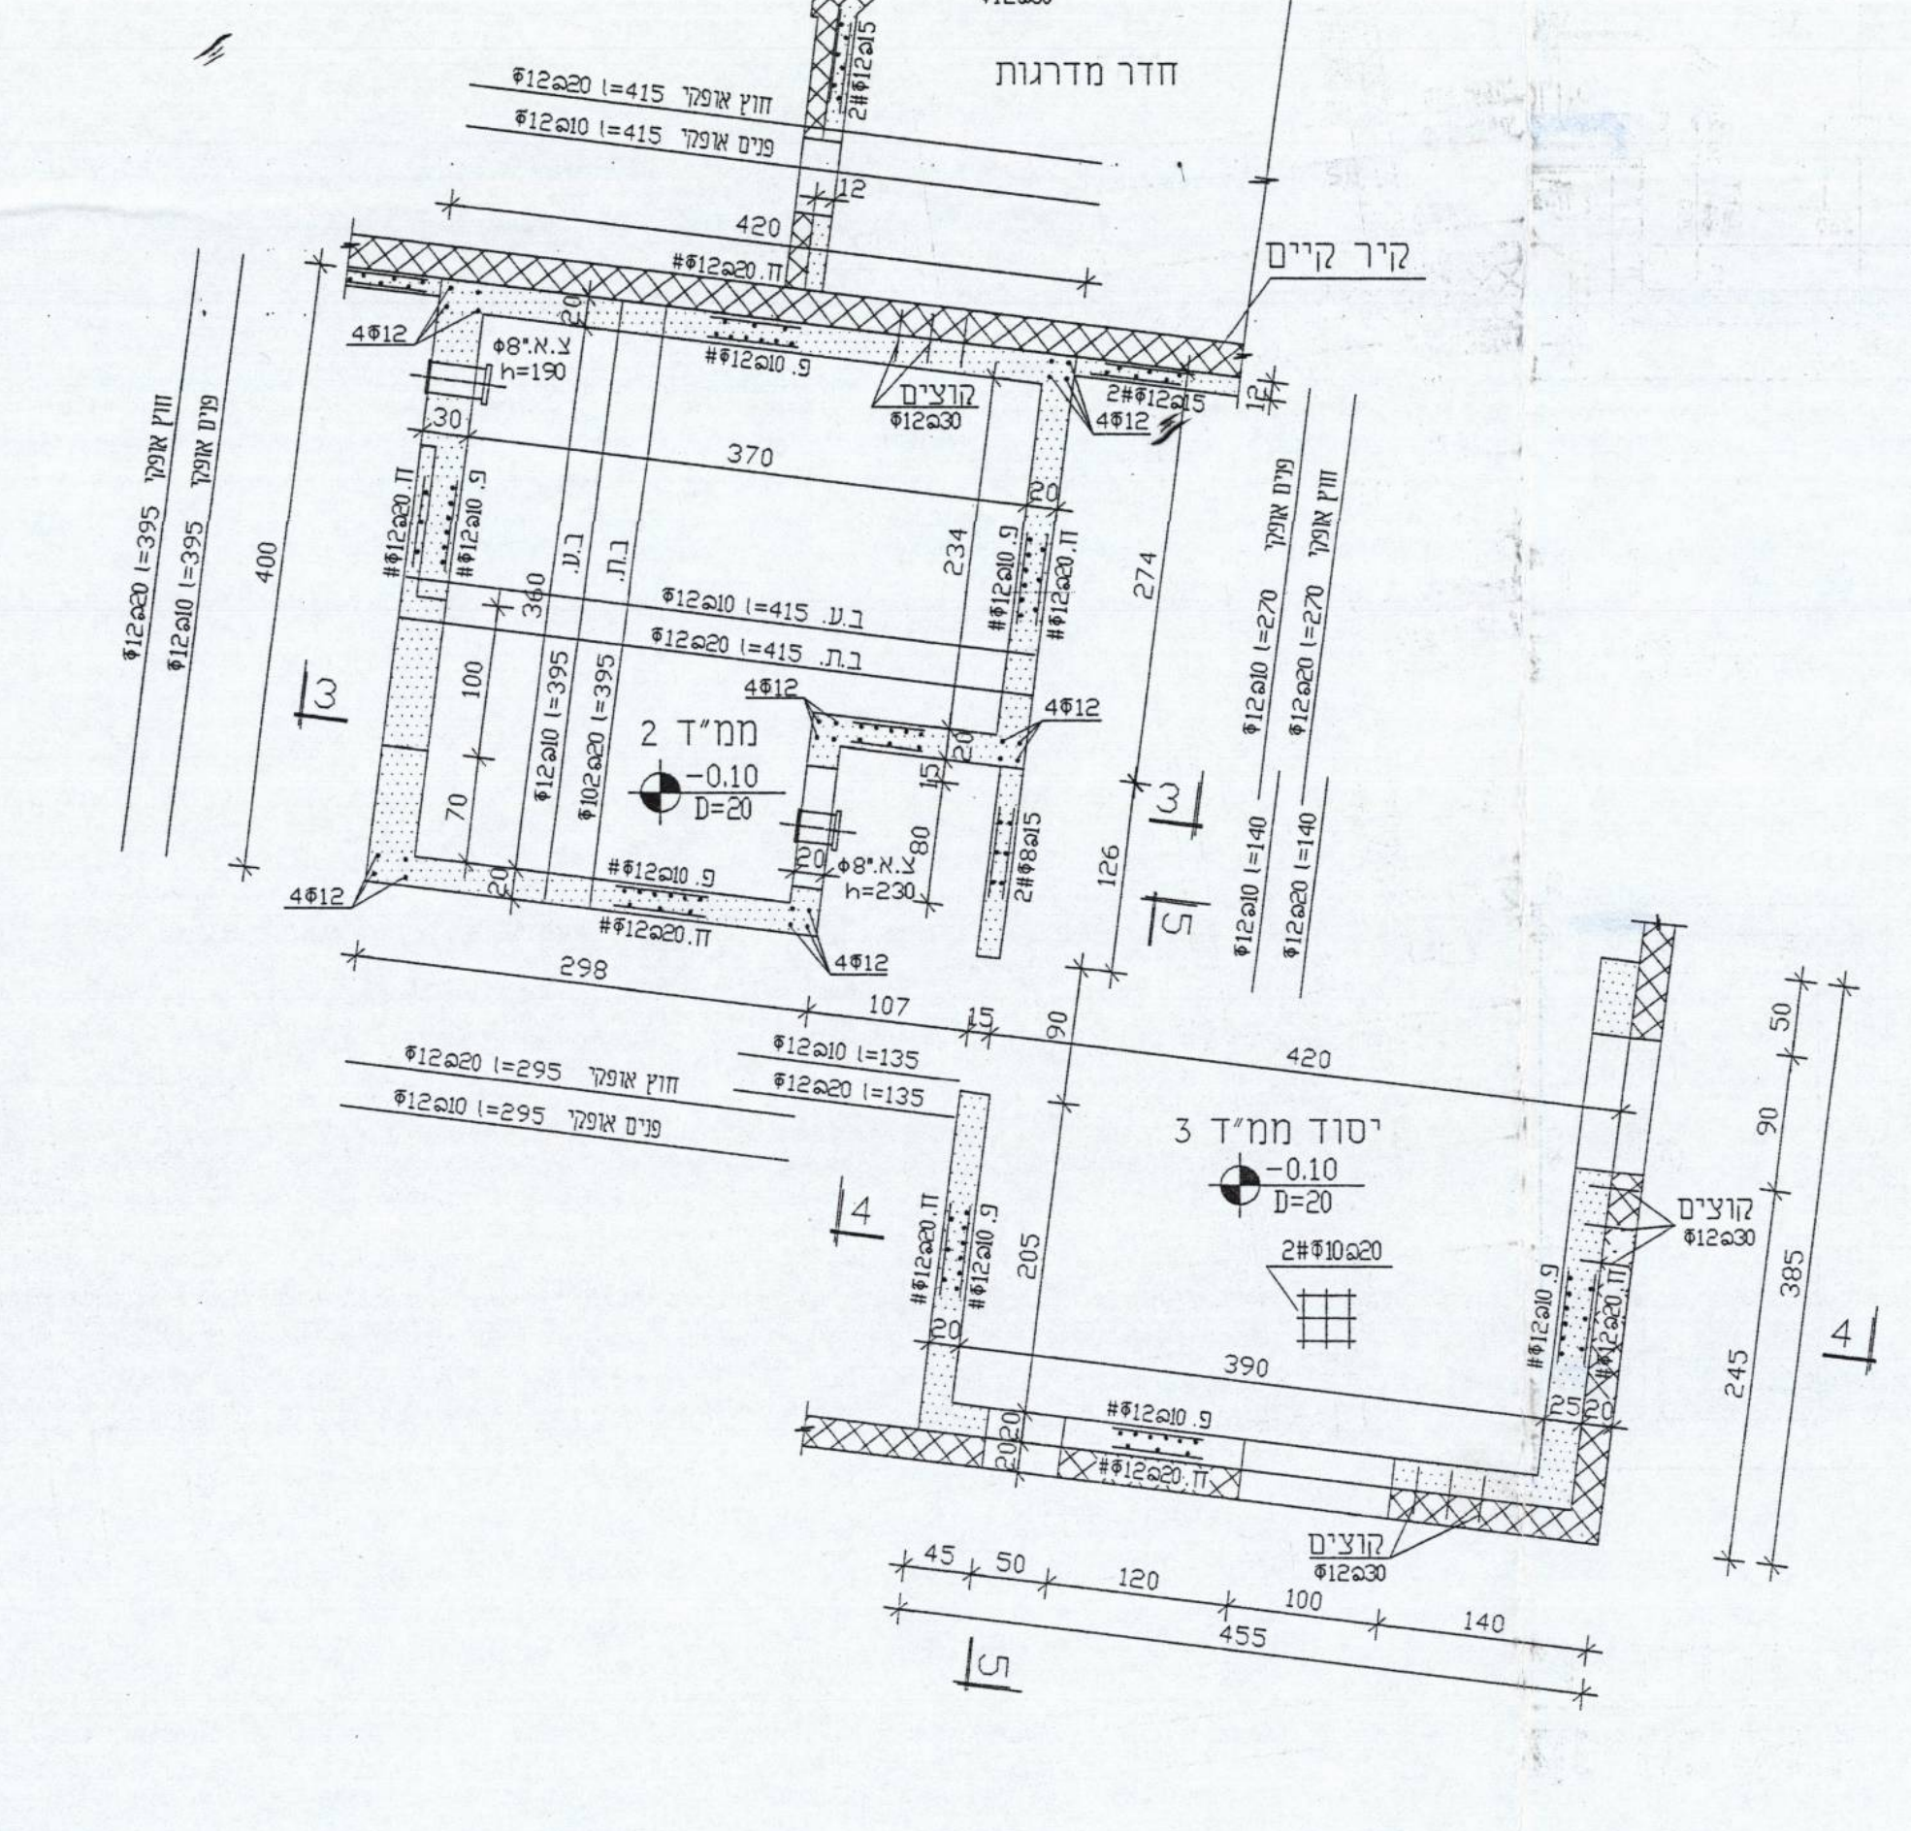

רצפת קומת קרקע
1:50

חדר מדרגות
קוצים Φ12@30
Φ12@20 l=415 חוץ אופקי
Φ12@10 l=415 פנים אופקי
420
קיר קיים
4Φ12
צ.א.*Φ8 h=190
370
ממ"ד 2
-0.10
D=20
Φ12@10 l=415 .ב.ע
Φ12@20 l=415 .ב.ת
Φ12@20 l=395
Φ12@10 l=395
400
274
126
298
107
Φ12@10 l=135
Φ12@20 l=135
Φ12@20 l=295 חוץ אופקי
Φ12@10 l=295 פנים אופקי
יסוד ממ"ד 3
-0.10
D=20
2#Φ10@20
420
390
205
385
245
45 50 120 100 140
455

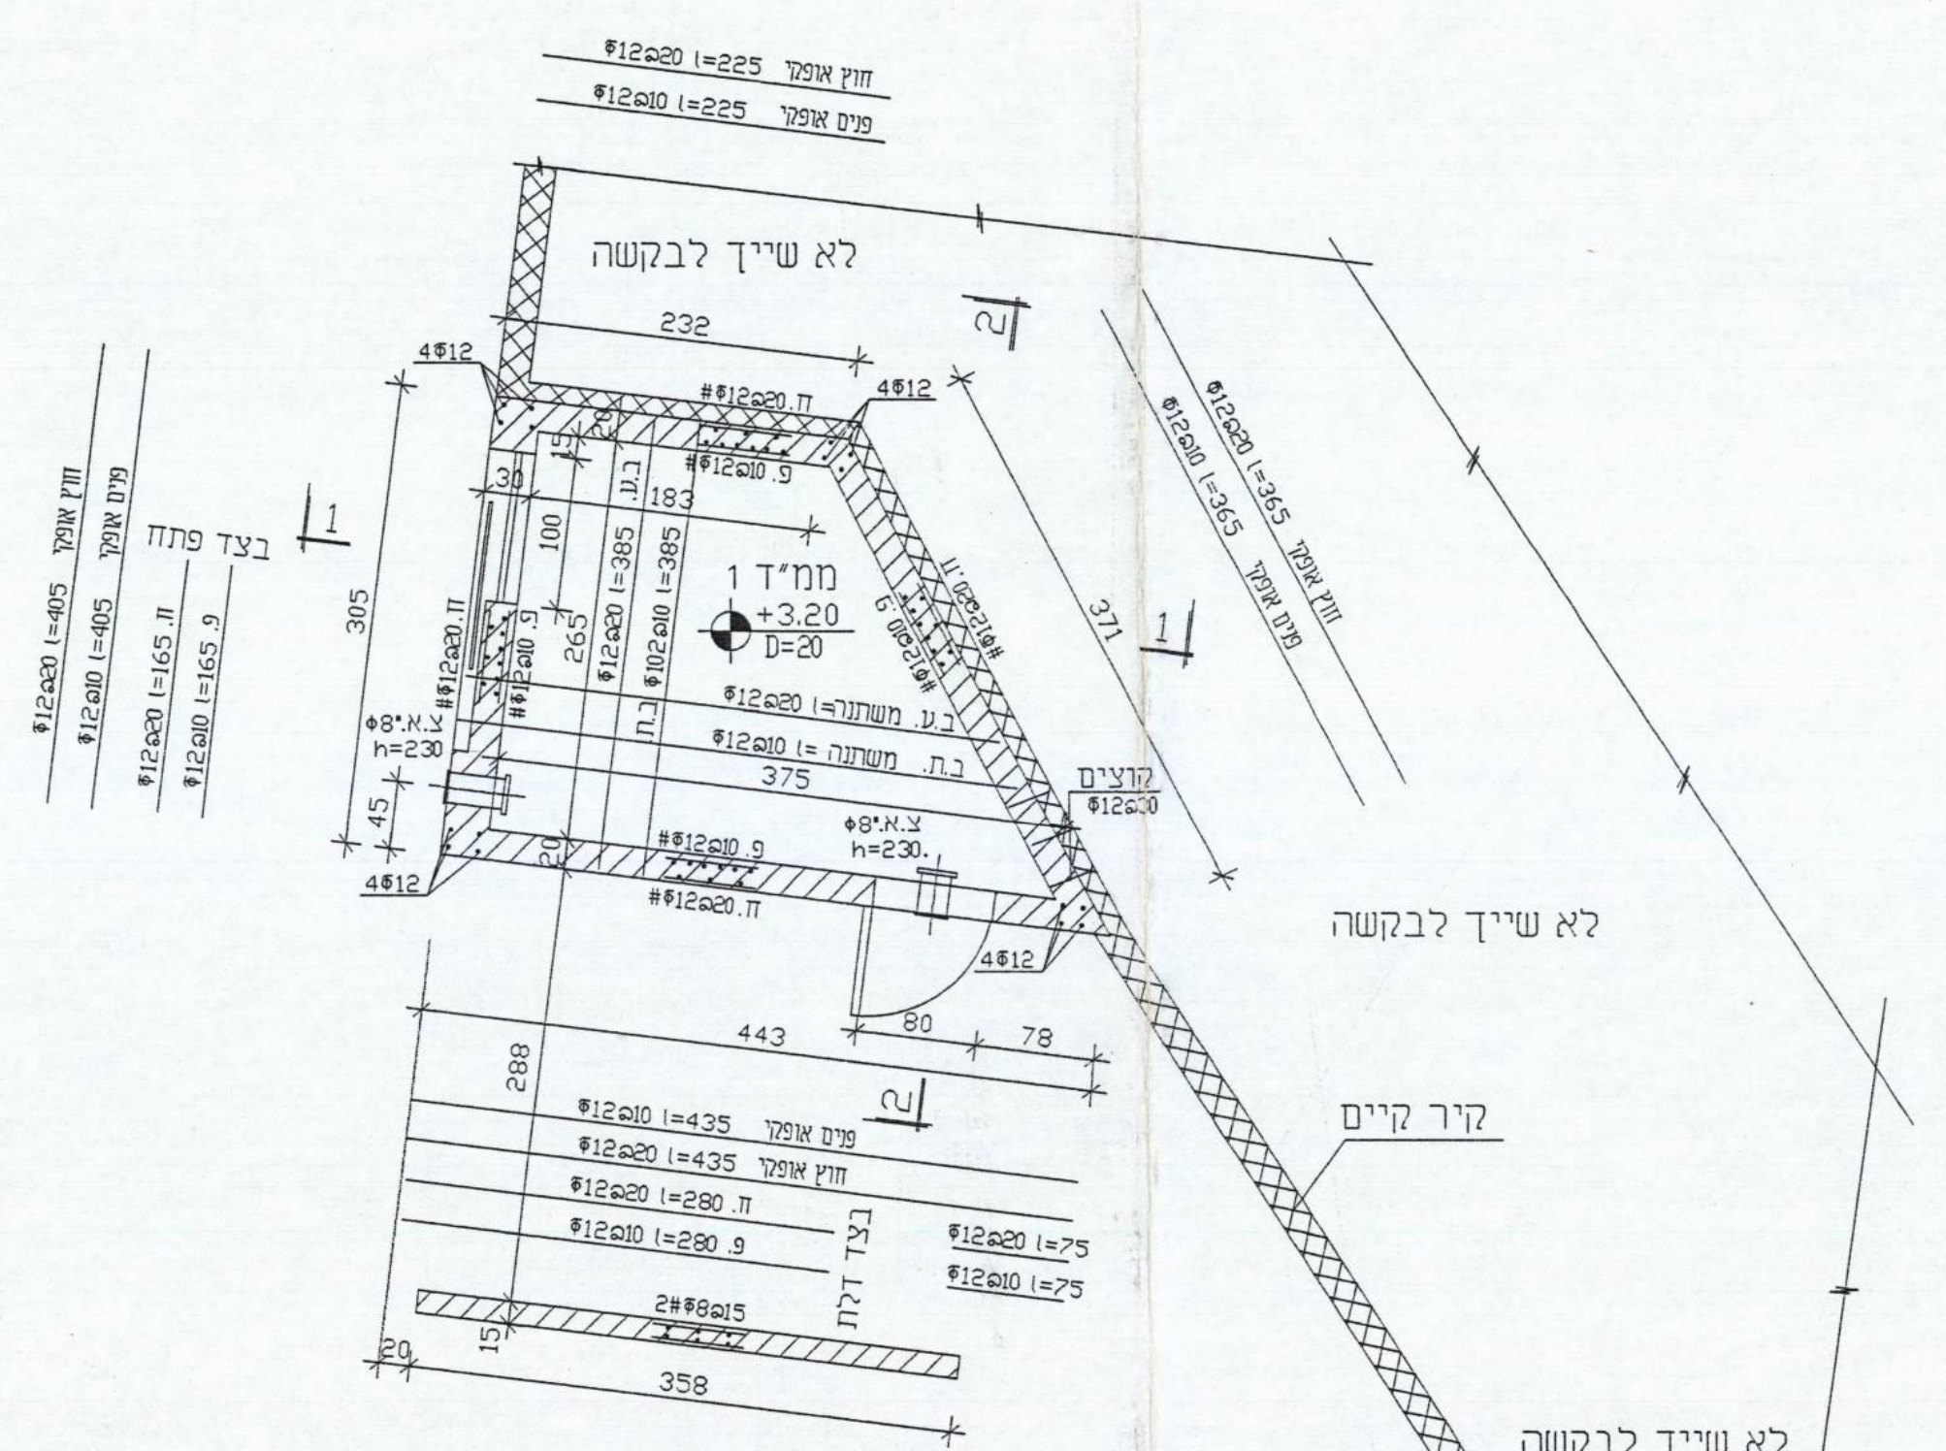

תקרת קומת קרקע
(רצפת קומה א')
1:50

Φ12@20 l=225 חוץ אופקי
Φ12@10 l=225 פנים אופקי
לא שייך לבקשה
232
4Φ12
ממ"ד 1
+3.20
D=20
בצד פתח
Φ12@20 l=405
Φ12@10 l=405
Φ12@20 l=165 .ח
Φ12@10 l=165 .פ
Φ12@20 l=365
Φ12@10 l=365
371
375
Φ12@20 l= משתנה .ב.ע
Φ12@10 l= משתנה .ב.ת
443
288
Φ12@10 l=435 פנים אופקי
Φ12@20 l=435 חוץ אופקי
Φ12@20 l=280 .ח
Φ12@10 l=280 .פ
Φ12@20 l=75
Φ12@10 l=75
בצד דלת
2#Φ8@15
358
קוצים Φ12@30
קיר קיים
לא שייך לבקשה

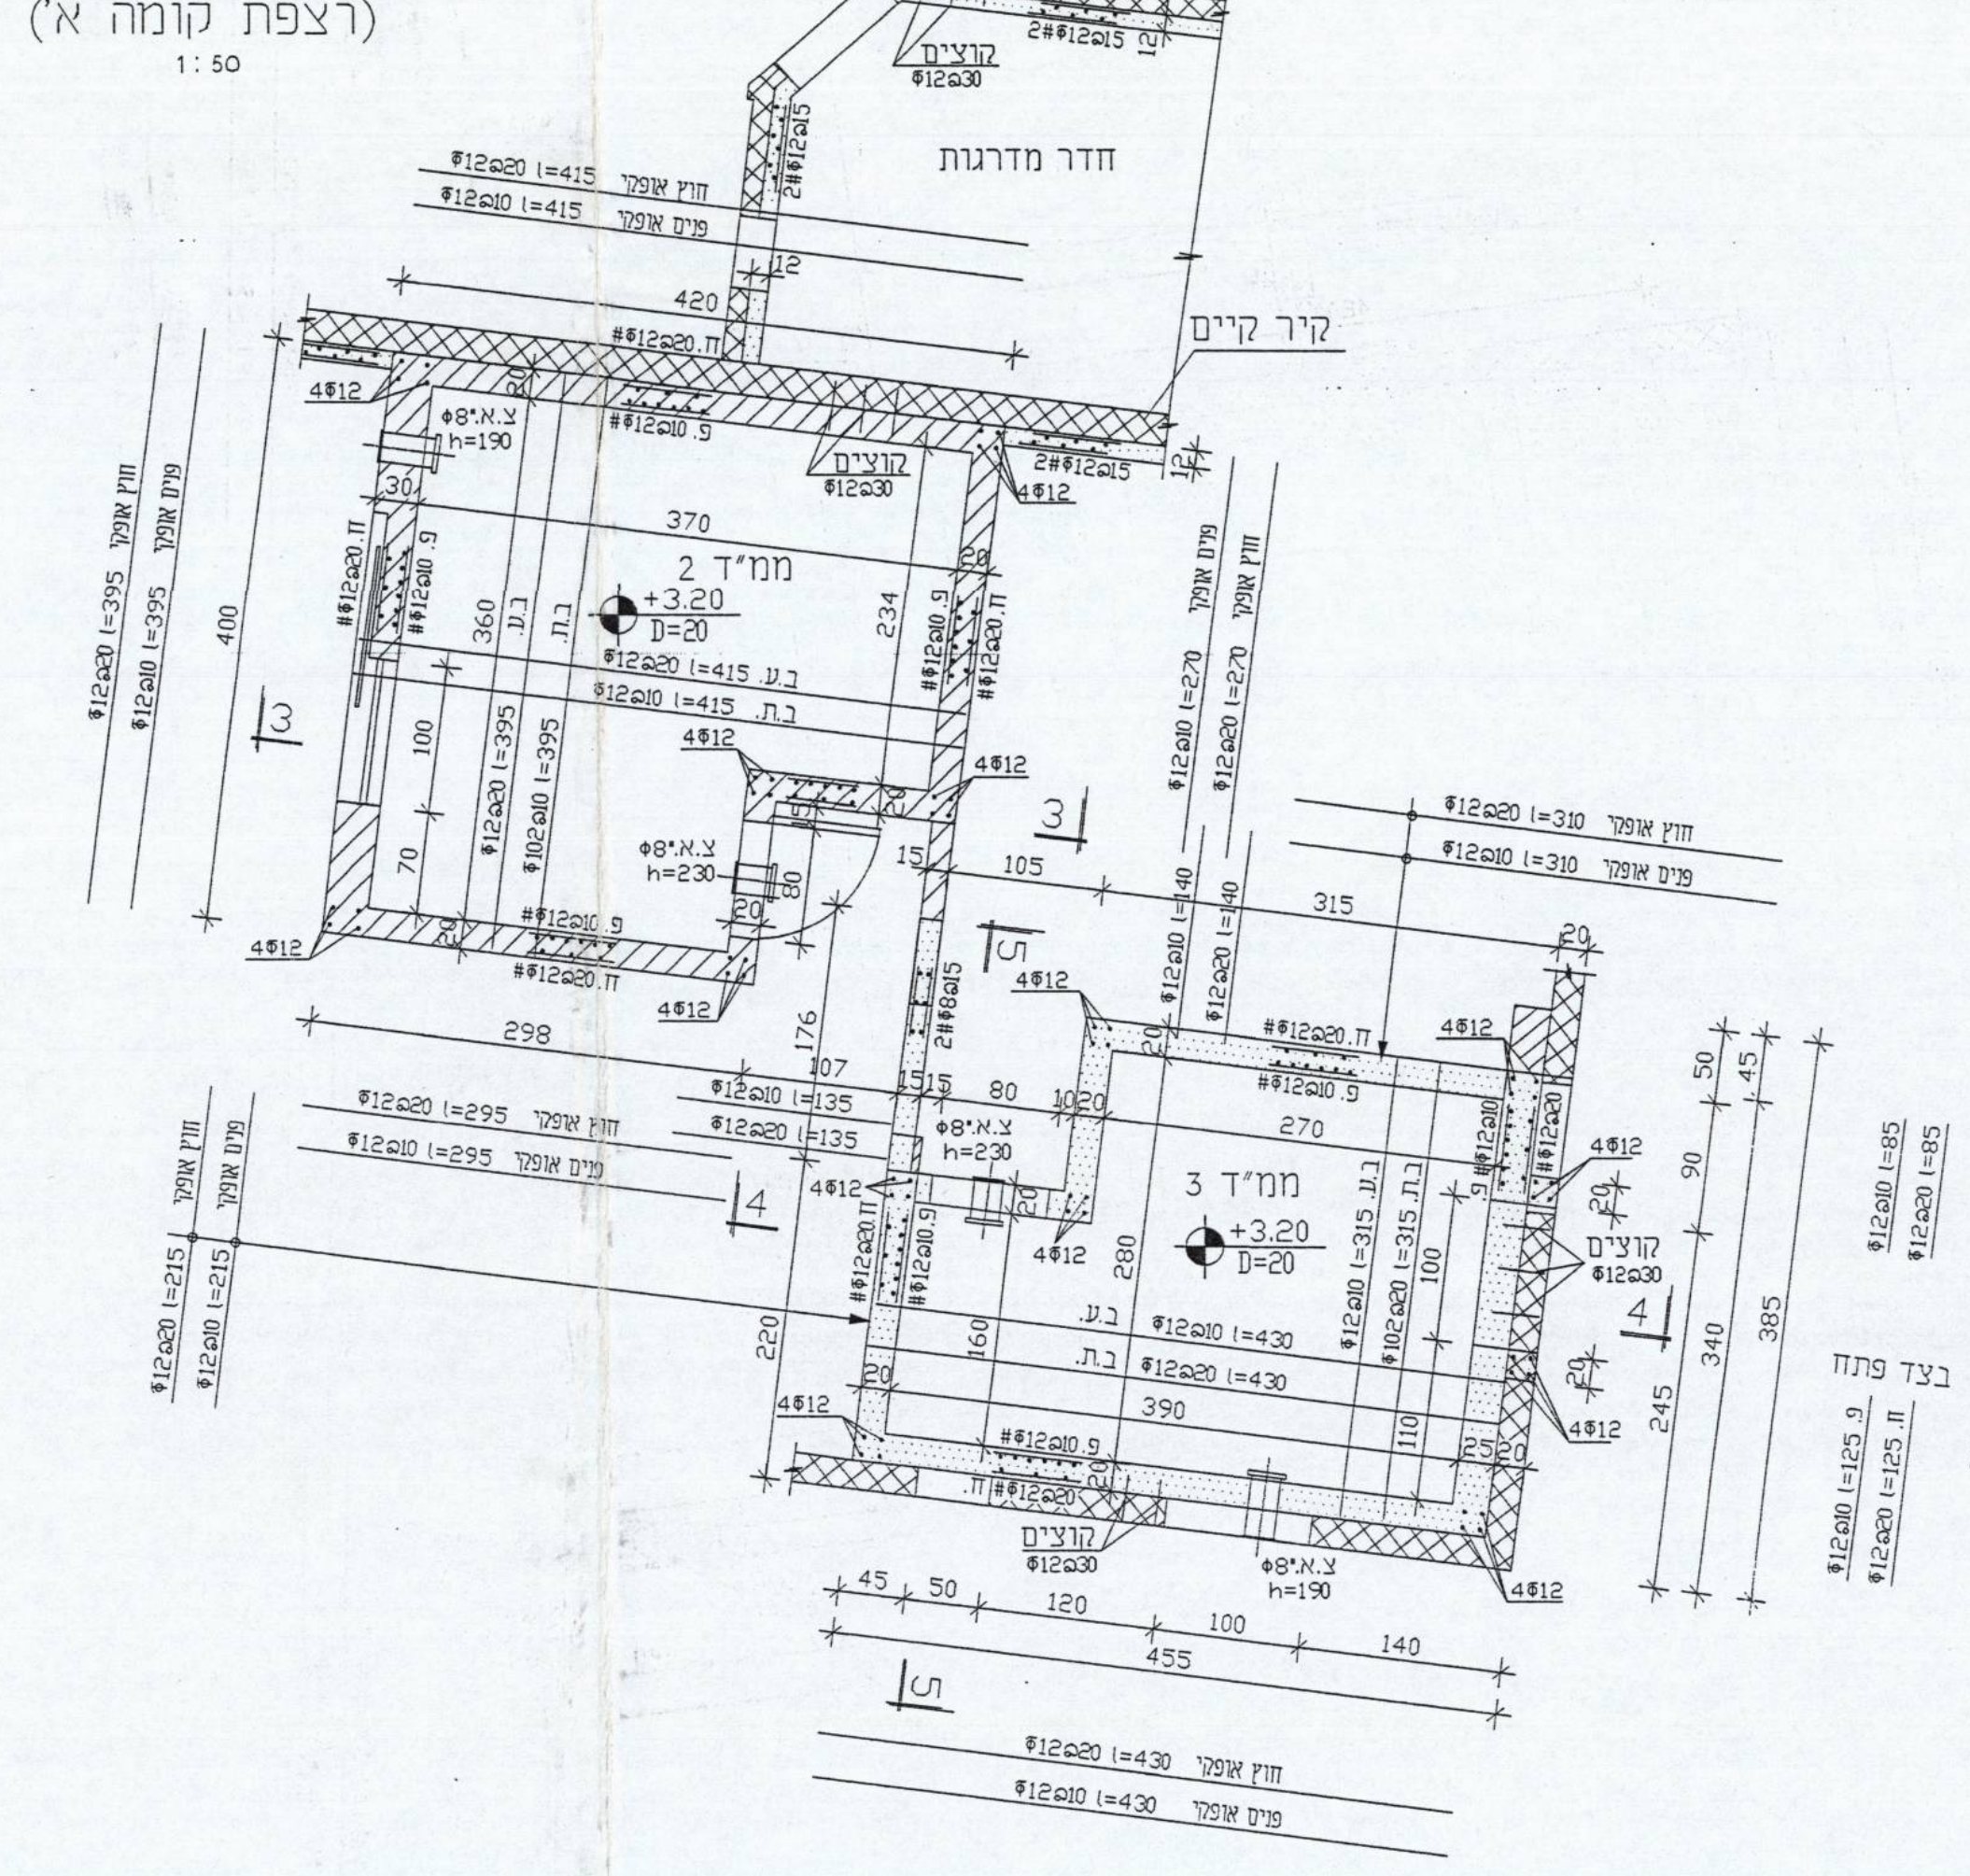

תקרת קומת קרקע
(רצפת קומה א')
1:50

חדר מדרגות
Φ12@20 l=415 חוץ אופקי
Φ12@10 l=415 פנים אופקי
420
קיר קיים
4Φ12
צ.א.*Φ8 h=190
370
ממ"ד 2
+3.20
D=20
Φ12@20 l=395
Φ12@10 l=395
400
360
298
107
ממ"ד 3
+3.20
D=20
Φ12@20 l=430 .ב.ע
Φ12@20 l=430 .ב.ת
390
Φ12@20 l=310 חוץ אופקי
Φ12@10 l=310 פנים אופקי
315
270
Φ12@10 l=85
Φ12@20 l=85
בצד פתח
Φ12@10 l=125 .פ
Φ12@20 l=125 .ח
Φ12@10 l=315
Φ12@20 l=315
385
340
245
45 50 120 100 140
455
Φ12@20 l=430 חוץ אופקי
Φ12@10 l=430 פנים אופקי
קוצים Φ12@30

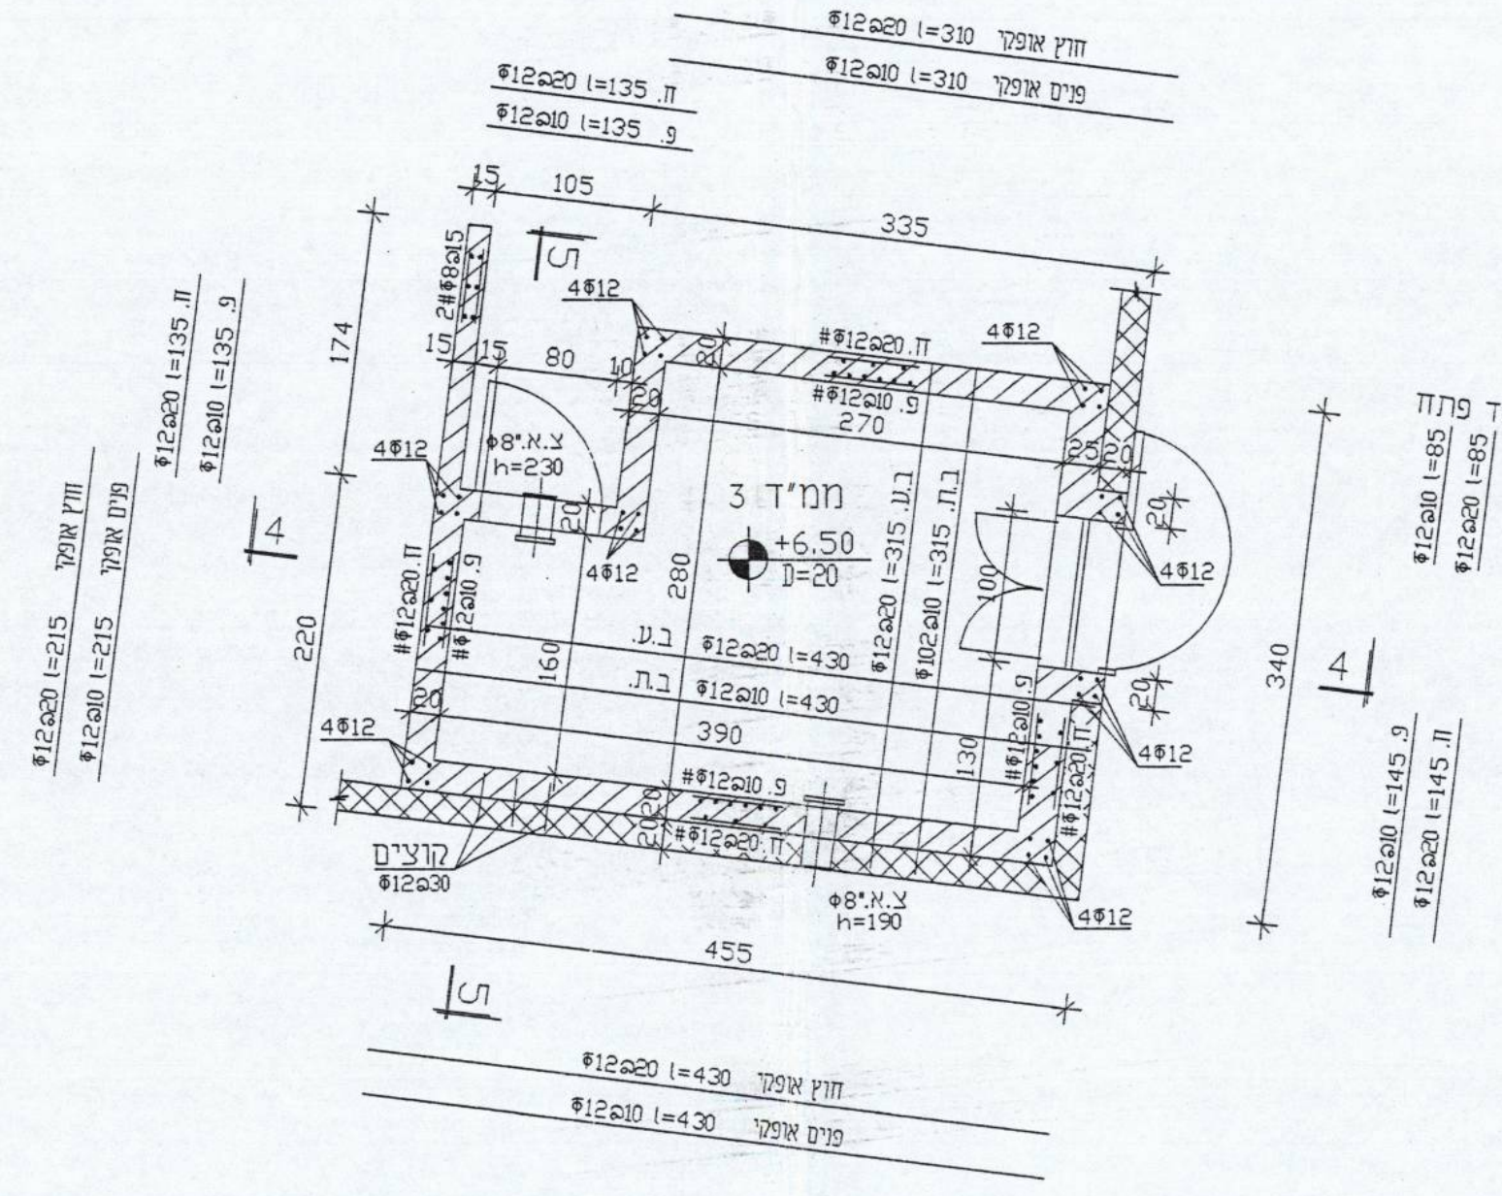

תקרת קומה א'
(רצפת קומה ב')
1:50

Φ12@20 l=310 חוץ אופקי
Φ12@10 l=310 פנים אופקי
Φ12@20 l=135 .ח
Φ12@10 l=135 .פ
105
335
174
4Φ12
ממ"ד 3
+6.50
D=20
270
280
Φ12@20 l=430 .ב.ע
Φ12@10 l=430 .ב.ת
390
220
340
בצד פתח
Φ12@20 l=85
Φ12@10 l=85
Φ12@10 l=145 .פ
Φ12@20 l=145 .ח
Φ12@10 l=315
Φ12@20 l=315
Φ12@20 l=215
Φ12@10 l=215
קוצים Φ12@30
צ.א.*Φ8 h=190
455
Φ12@20 l=430 חוץ אופקי
Φ12@10 l=430 פנים אופקי

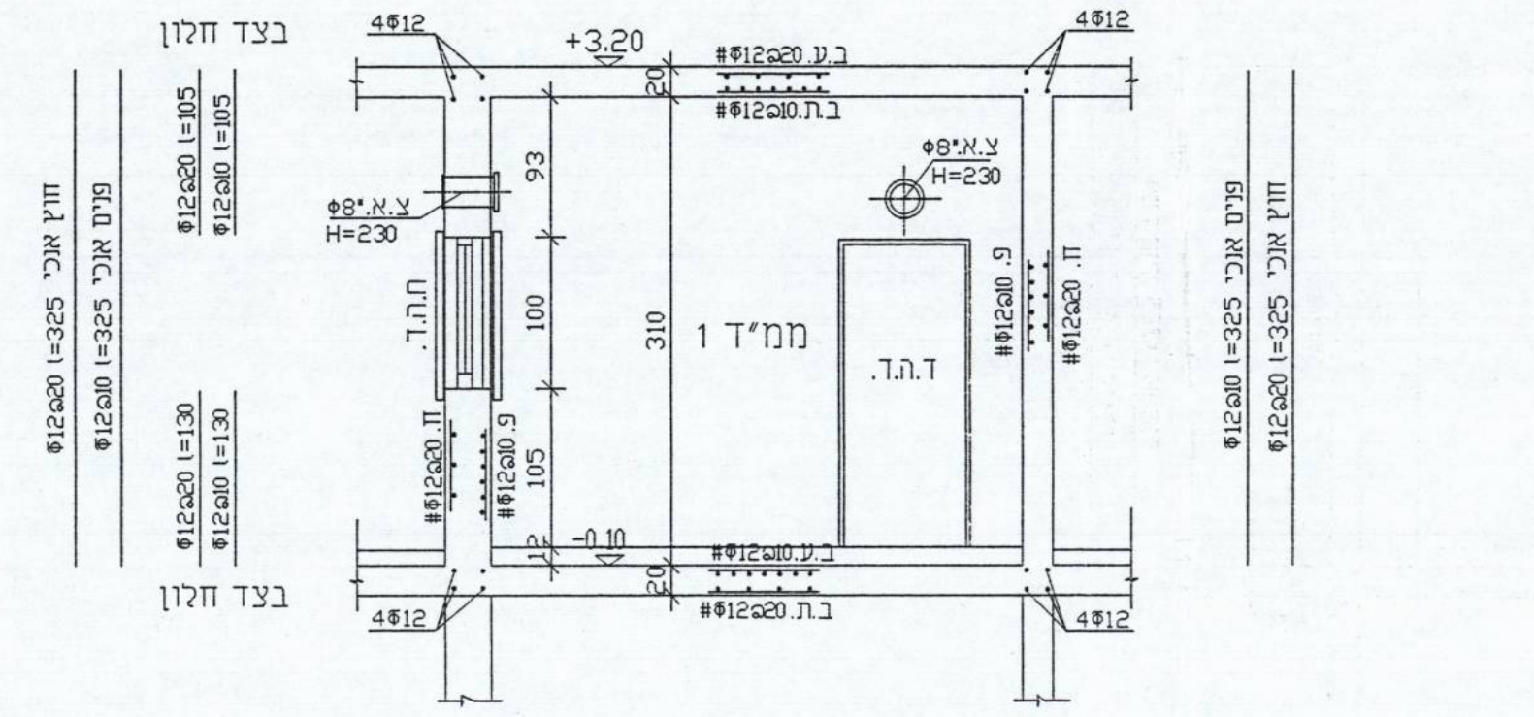

חתך 1-1
1:50

בצד חלון
4Φ12
+3.20
#Φ12@20 .ב.ע
#Φ12@10 .ב.ת
צ.א.*Φ8
H=230
ת.ה.ד.
ממ"ד 1
ד.ה.ד.
310
100
93
105
-0.10
Φ12@20 l=105
Φ12@10 l=105
Φ12@20 l=325 חוץ אנכי
Φ12@10 l=325 פנים אנכי
Φ12@20 l=130
Φ12@10 l=130

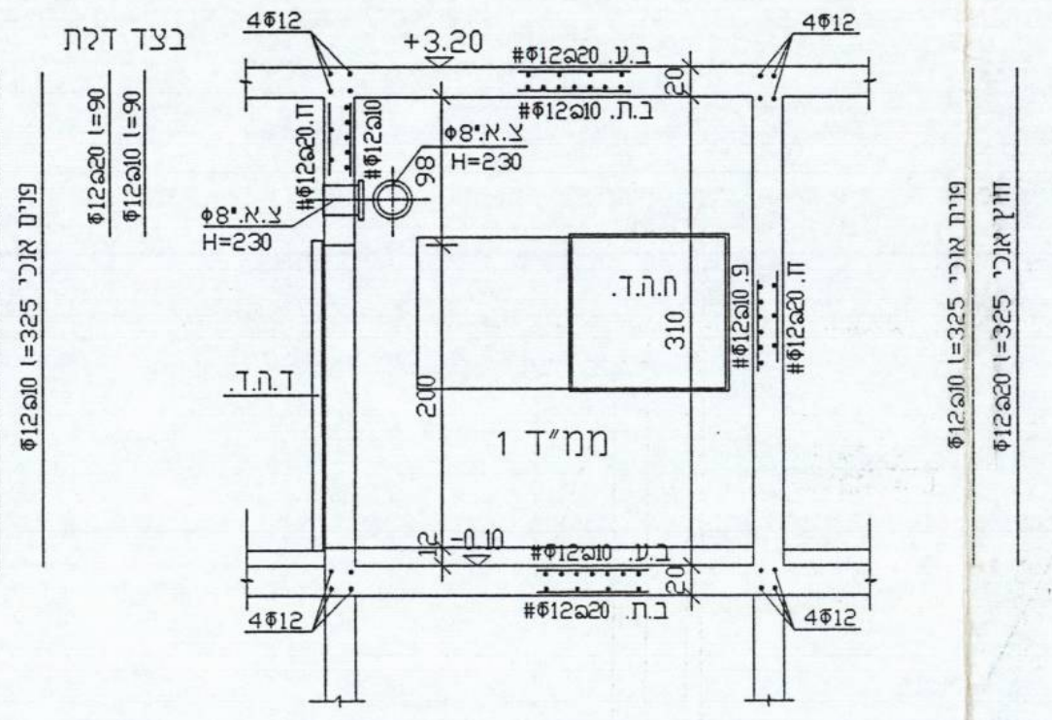

חתך 2-2
1:50

בצד דלת
4Φ12
+3.20
#Φ12@20 .ב.ע
#Φ12@10 .ב.ת
צ.א.*Φ8
H=230
ת.ה.ד.
ד.ה.ד.
ממ"ד 1
310
200
-0.10
Φ12@20 l=90
Φ12@10 l=90
Φ12@20 l=325 חוץ אנכי
Φ12@10 l=325 פנים אנכי

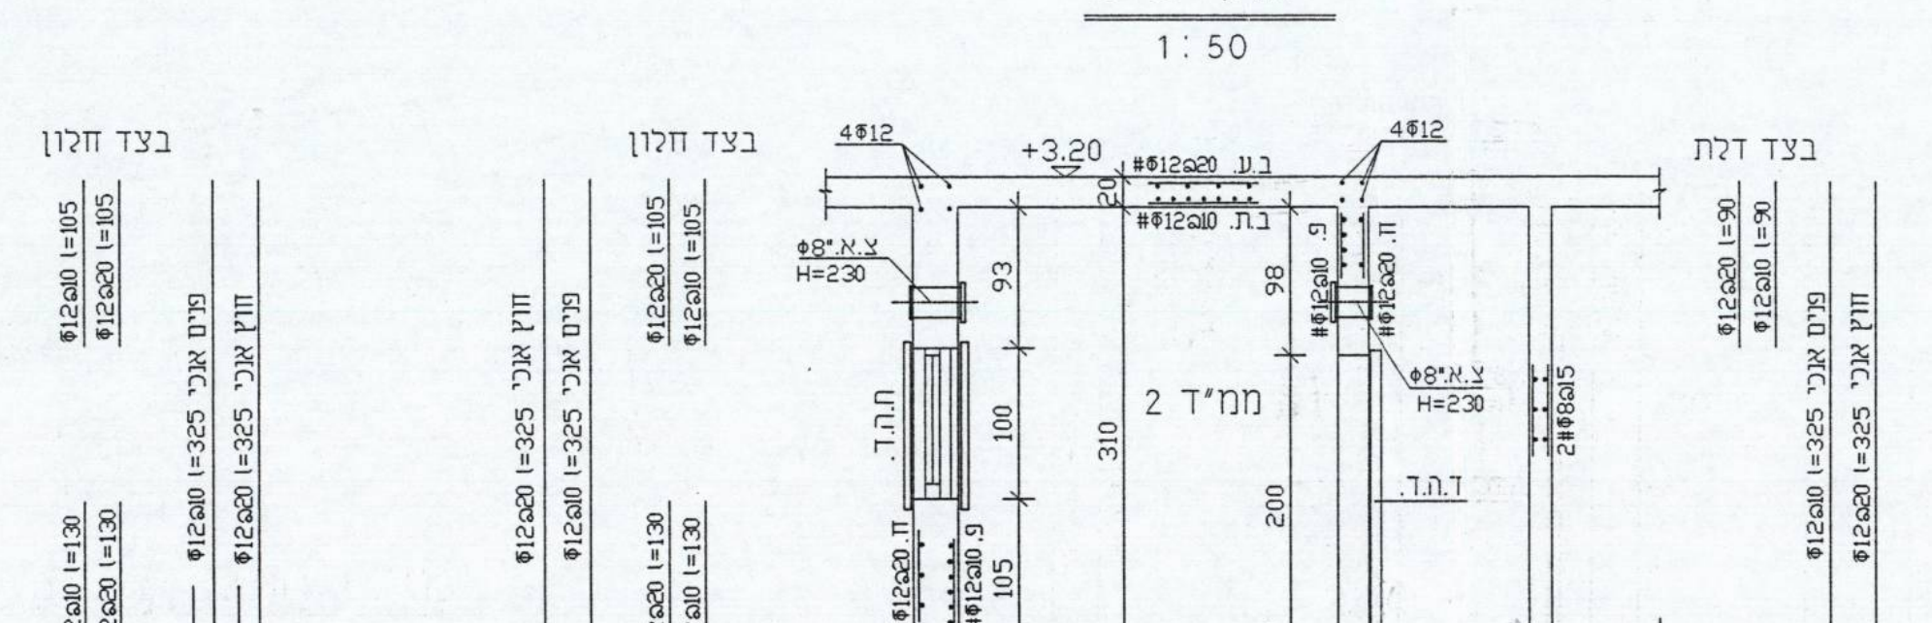

חתך 3-3
1:50

בצד חלון
בצד דלת
4Φ12
+3.20
צ.א.*Φ8
H=230
ת.ה.ד.
ממ"ד 2
ד.ה.ד.
310
200
100
93
105
-0.10
2#Φ8@15
Φ12@20 l=105
Φ12@10 l=105
Φ12@20 l=130
Φ12@10 l=130
Φ12@20 l=90
Φ12@10 l=90
Φ12@20 l=325 חוץ אנכי
Φ12@10 l=325 פנים אנכי

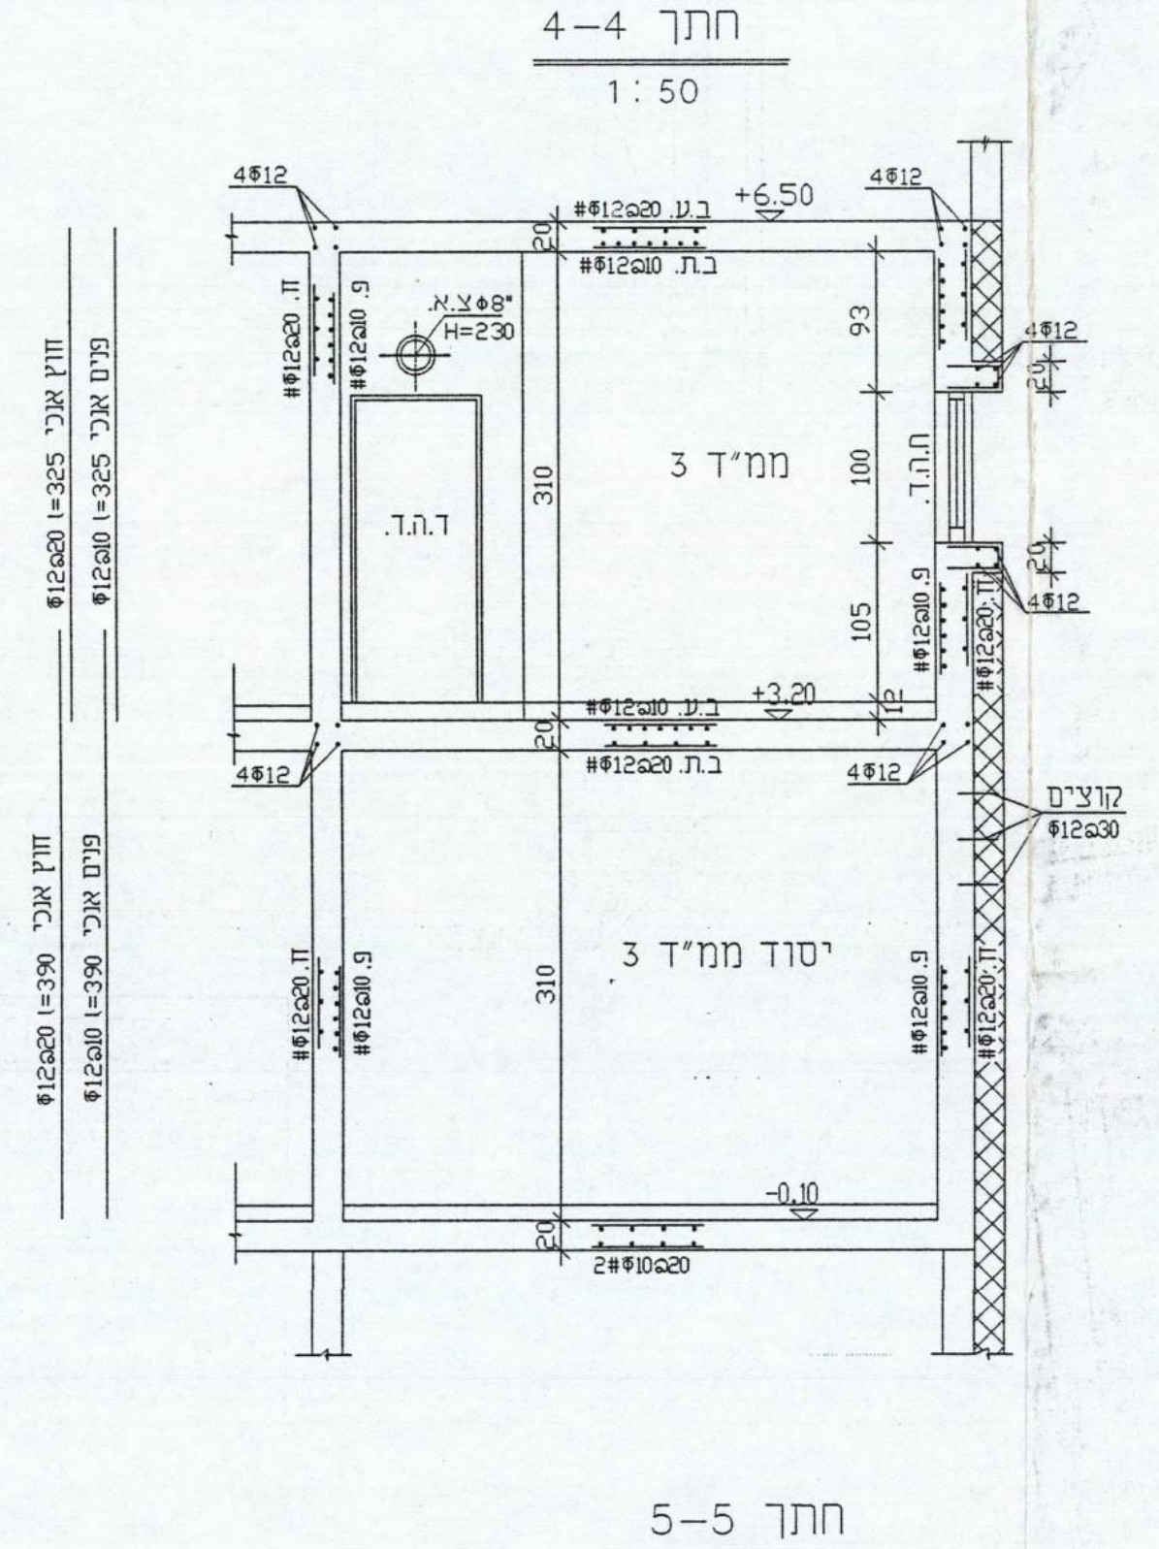

חתך 4-4
1:50

4Φ12
+6.50
+3.20
-0.10
צ.א.*Φ8
H=230
ממ"ד 3
ד.ה.ד.
ת.ה.ד.
יסוד ממ"ד 3
310
100
93
105
קוצים Φ12@30
2#Φ10@20
בצד חלון
Φ12@20 l=105
Φ12@10 l=105
Φ12@20 l=130
Φ12@10 l=130
Φ12@20 l=325 חוץ אנכי
Φ12@10 l=325 פנים אנכי
Φ12@20 l=390 חוץ אנכי
Φ12@10 l=390 פנים אנכי

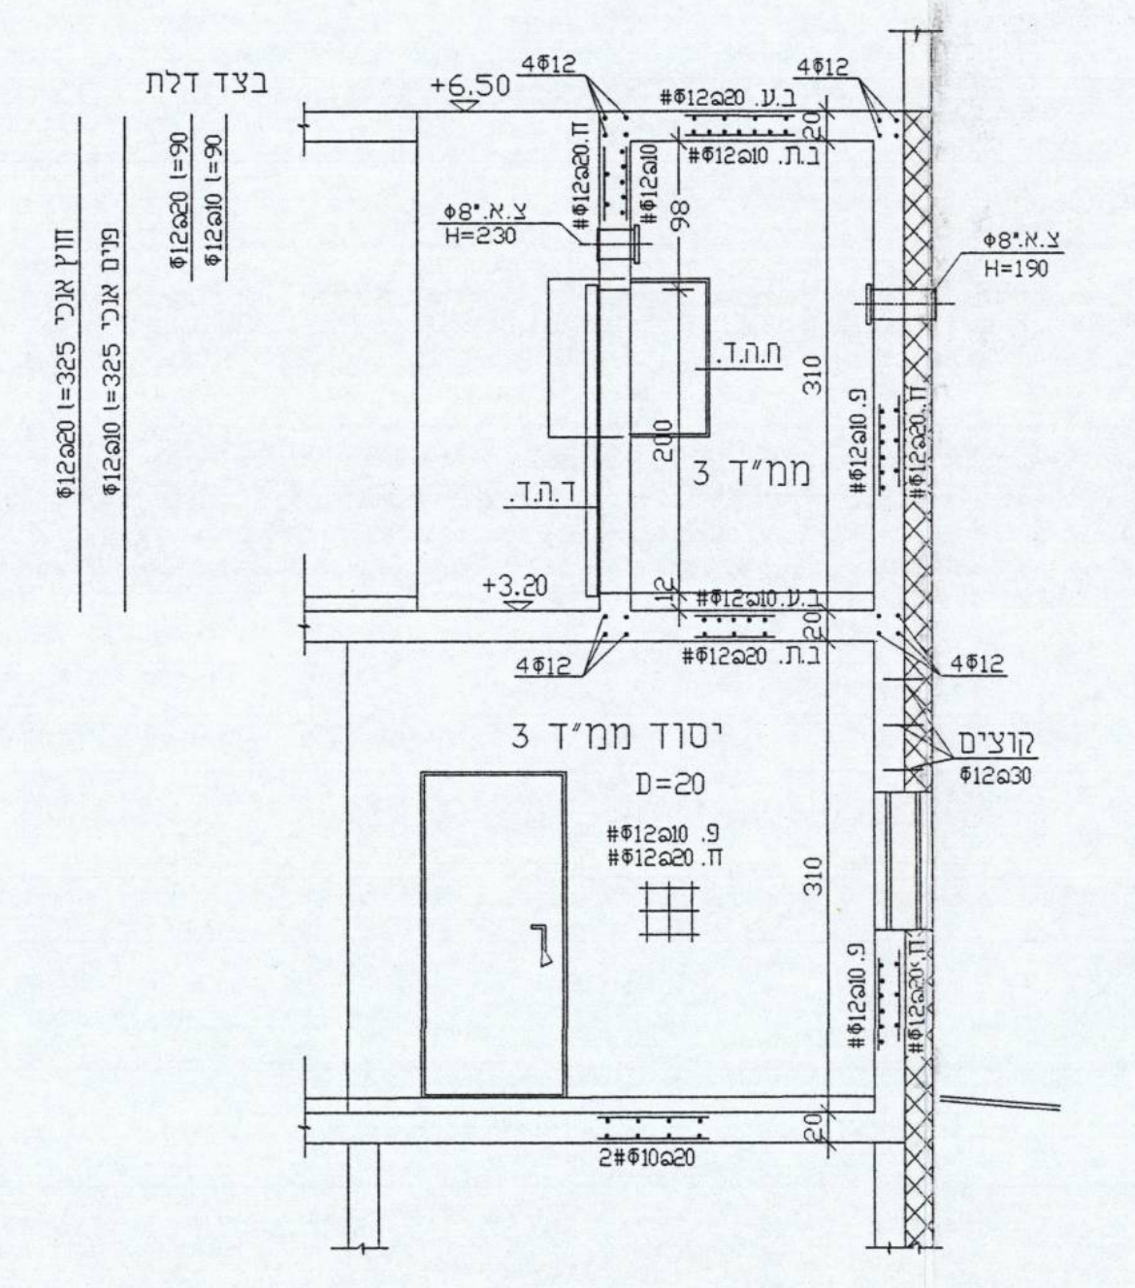

חתך 5-5
1:50

בצד דלת
4Φ12
+6.50
+3.20
צ.א.*Φ8
H=230
צ.א.*Φ8
H=190
ת.ה.ד.
ד.ה.ד.
ממ"ד 3
יסוד ממ"ד 3
D=20
#Φ12@10 .פ
#Φ12@20 .ח
310
קוצים Φ12@30
2#Φ10@20
Φ12@20 l=90
Φ12@10 l=90
Φ12@20 l=325 חוץ אנכי
Φ12@10 l=325 פנים אנכי
Φ12@10 l=390 חוץ אנכי
Φ12@20 l=390 פנים אנכי

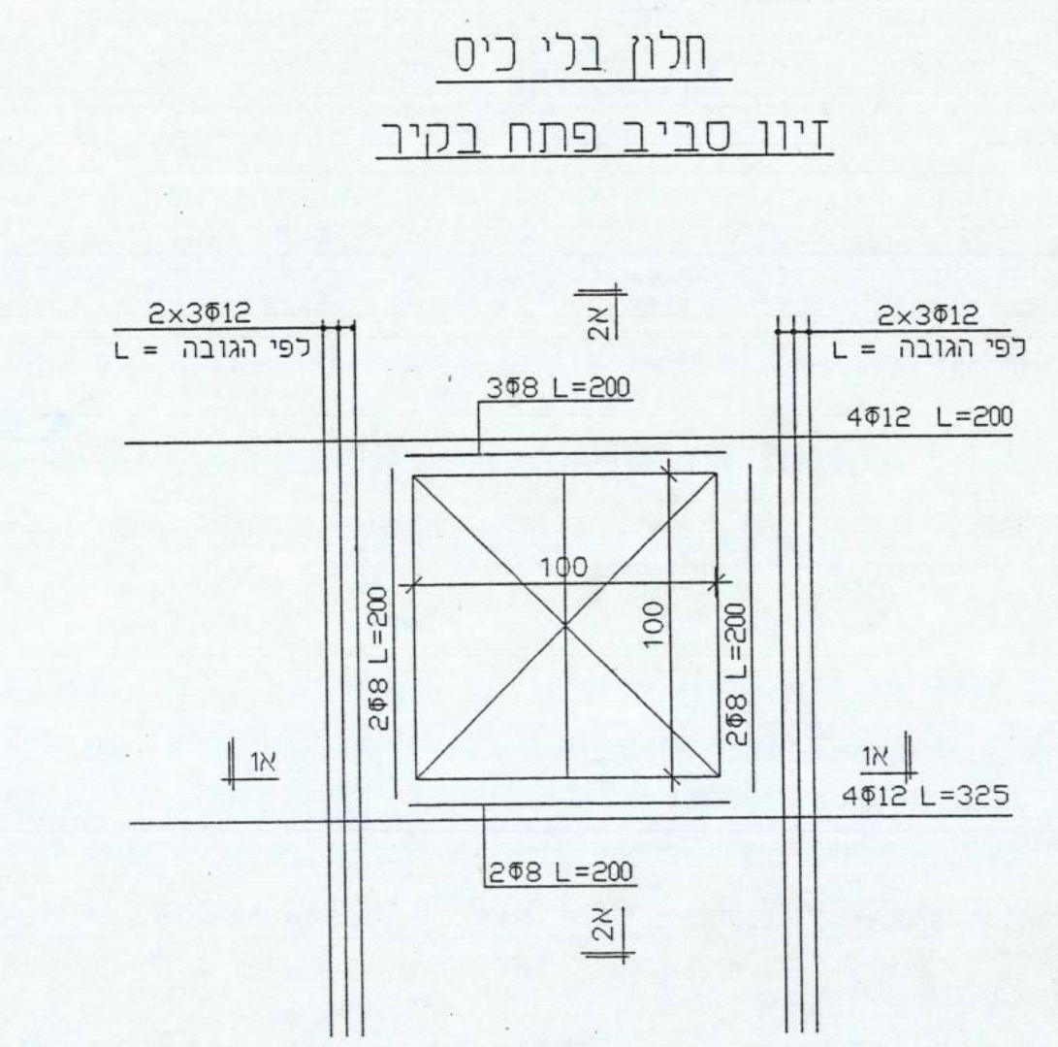

חלון בלי כיס
זיון סביב פתח בקיר

2x3Φ12
L = לפי הגובה
3Φ8 L=200
4Φ12 L=200
100
2Φ8 L=200
א1
4Φ12 L=325
2Φ8 L=200
א2

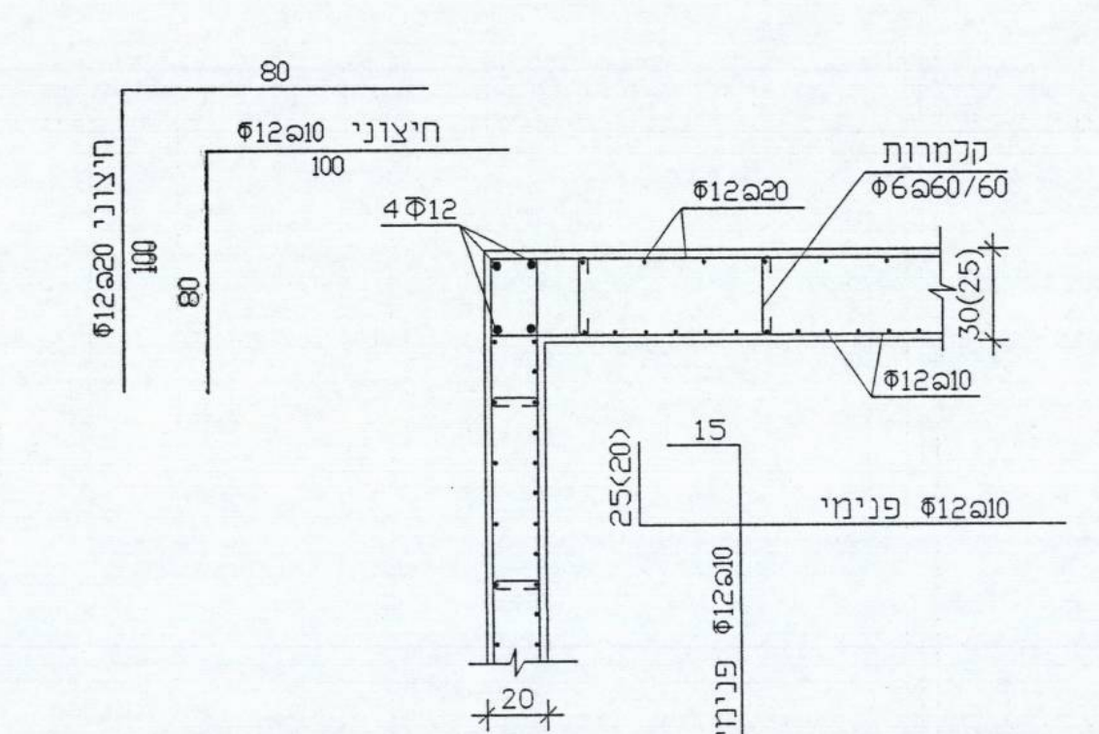

① חתך אופקי בקיר מרחב מוגן

80
חיצוני Φ12@10
100
חיצוני Φ12@20
4Φ12
Φ12@20
קלמרות Φ6@60/60
30(25)
Φ12@10
15
25(20)
פנימי Φ12@10
פנימי Φ12@10
20

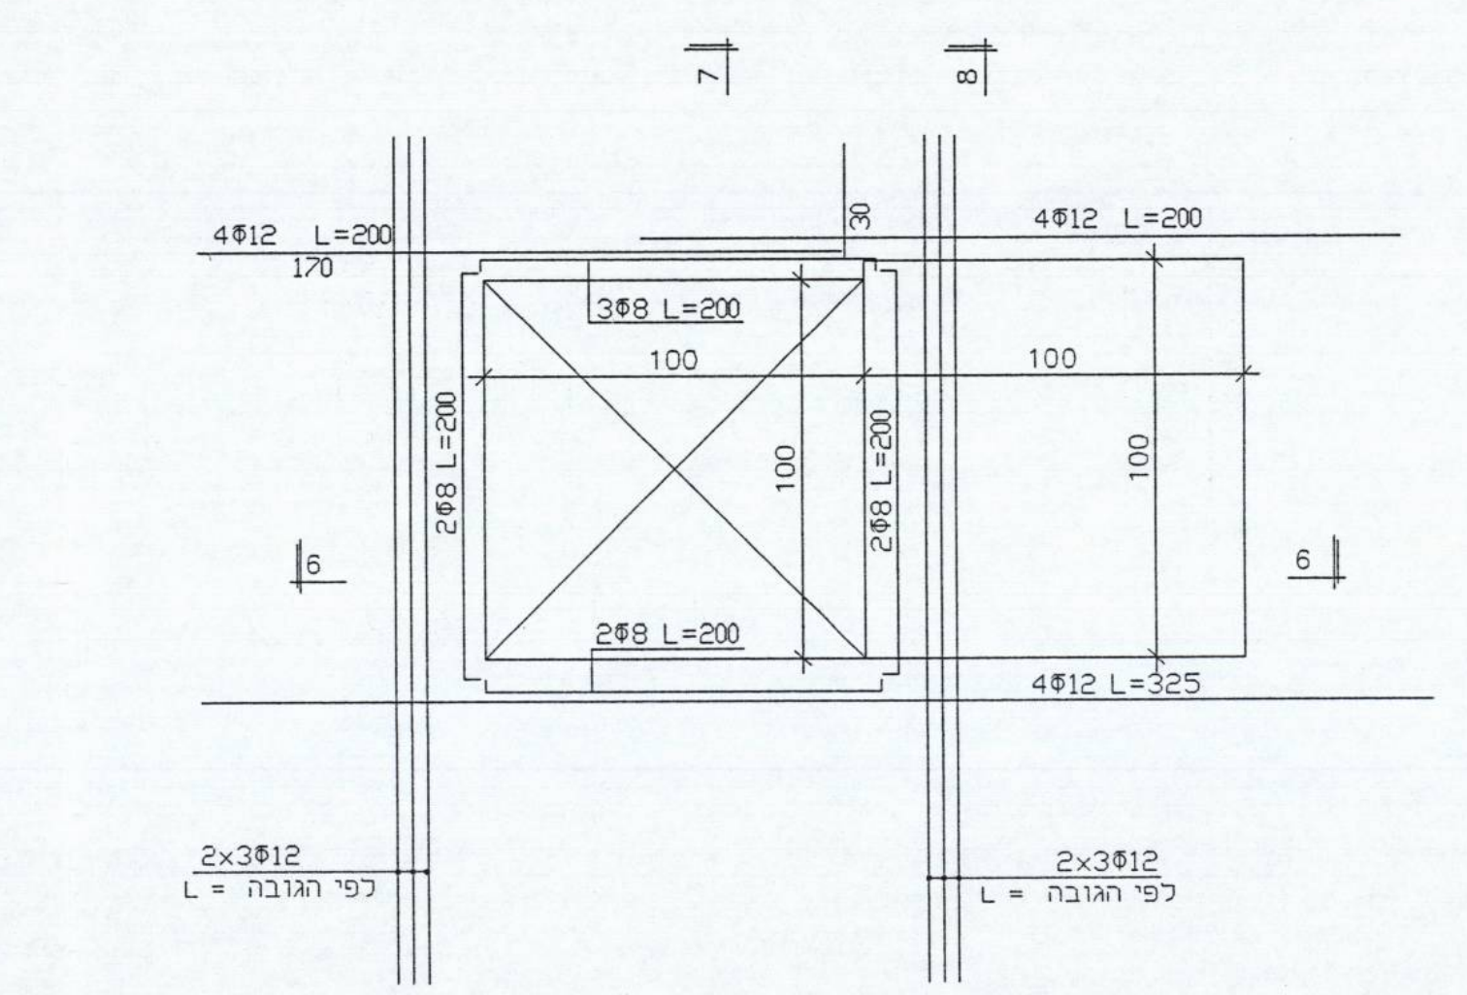

חלון עם כיס
זיון סביב פתח בקיר

7
8
4Φ12 L=200
170
3Φ8 L=200
4Φ12 L=200
30
100
2Φ8 L=200
6
2Φ8 L=200
4Φ12 L=325
2x3Φ12
L = לפי הגובה

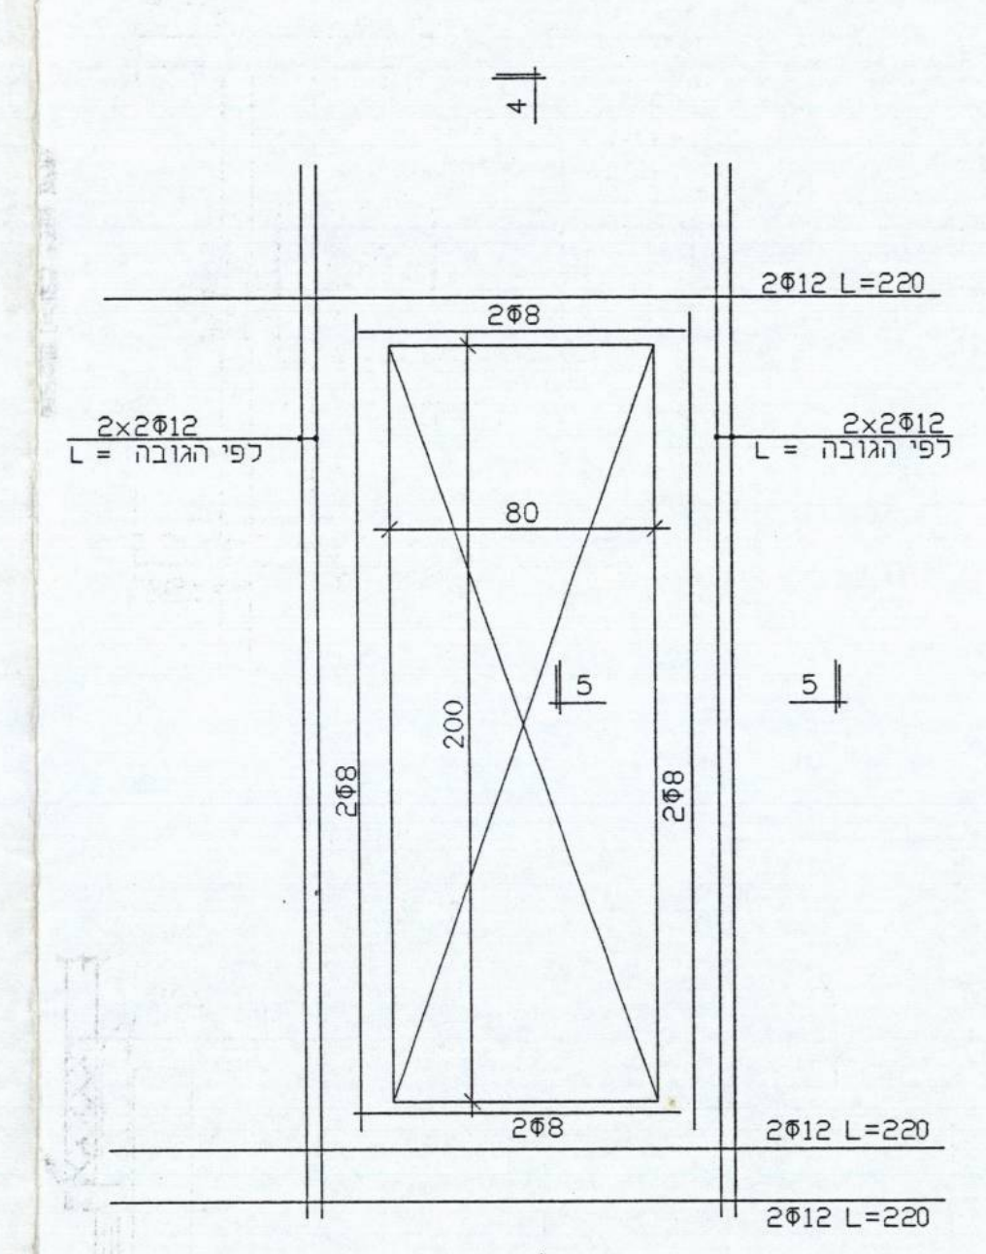

דלת
זיון סביב פתח בקיר

4
2Φ12 L=220
2Φ8
2x2Φ12
L = לפי הגובה
80
200
5
2Φ8
2Φ12 L=220
2Φ12 L=220

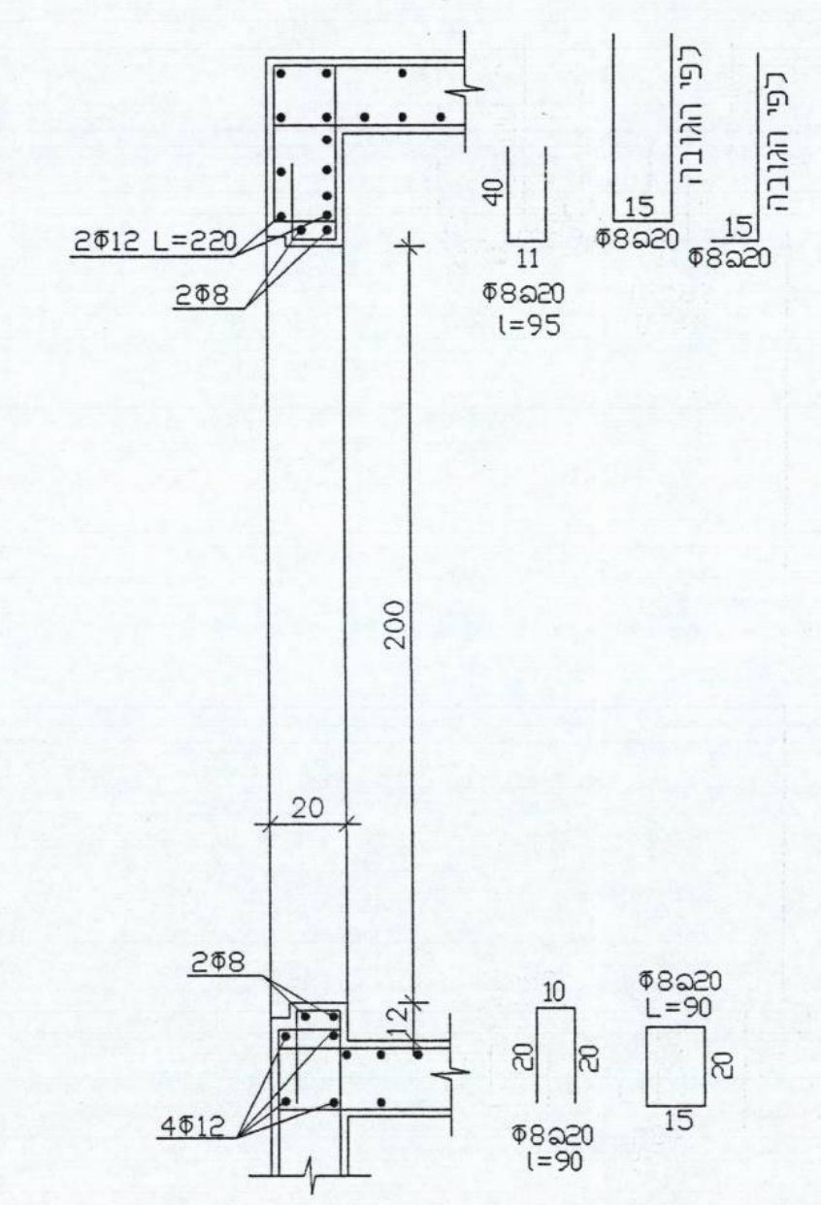

חתך 4-4

2Φ12 L=220
2Φ8
40
11
Φ8@20
l=95
15
Φ8@20
לפי הגובה
200
20
2Φ8
4Φ12
10
20
Φ8@20
l=90
Φ8@20
L=90
15

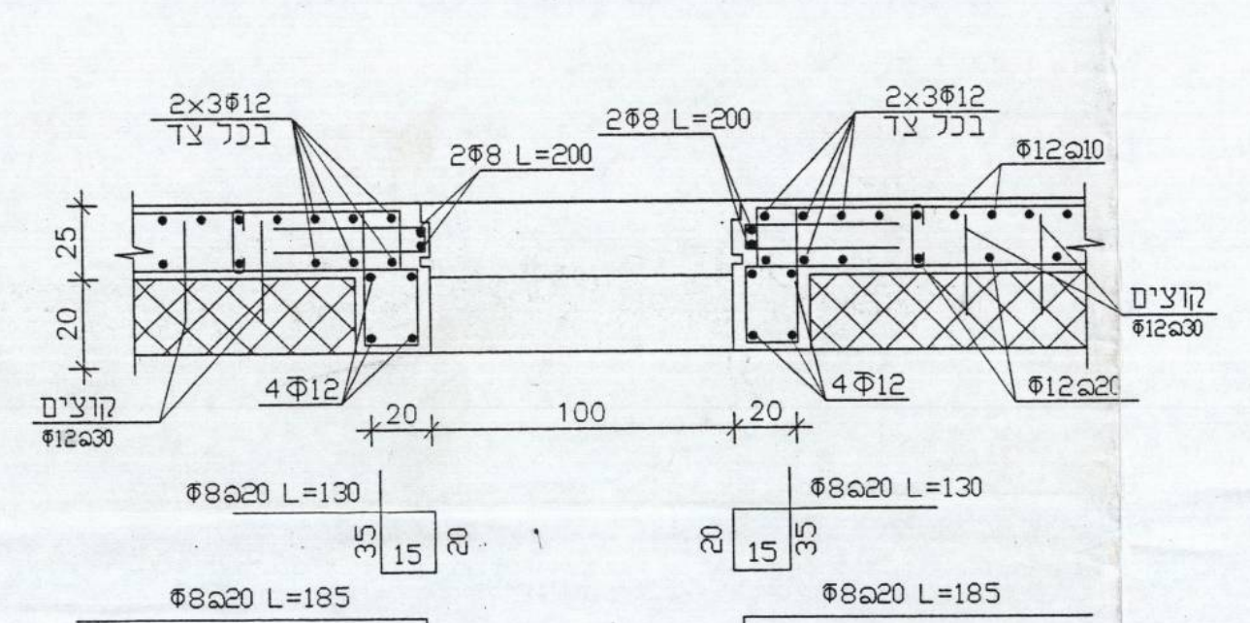

חתך א1-א1

2x3Φ12
בכל צד
2Φ8 L=200
2Φ8 L=200
Φ12@10
קוצים Φ12@30
4Φ12
20 100 20
Φ8@20 L=130
Φ8@20 L=185
80
Φ8@20 L=90
40

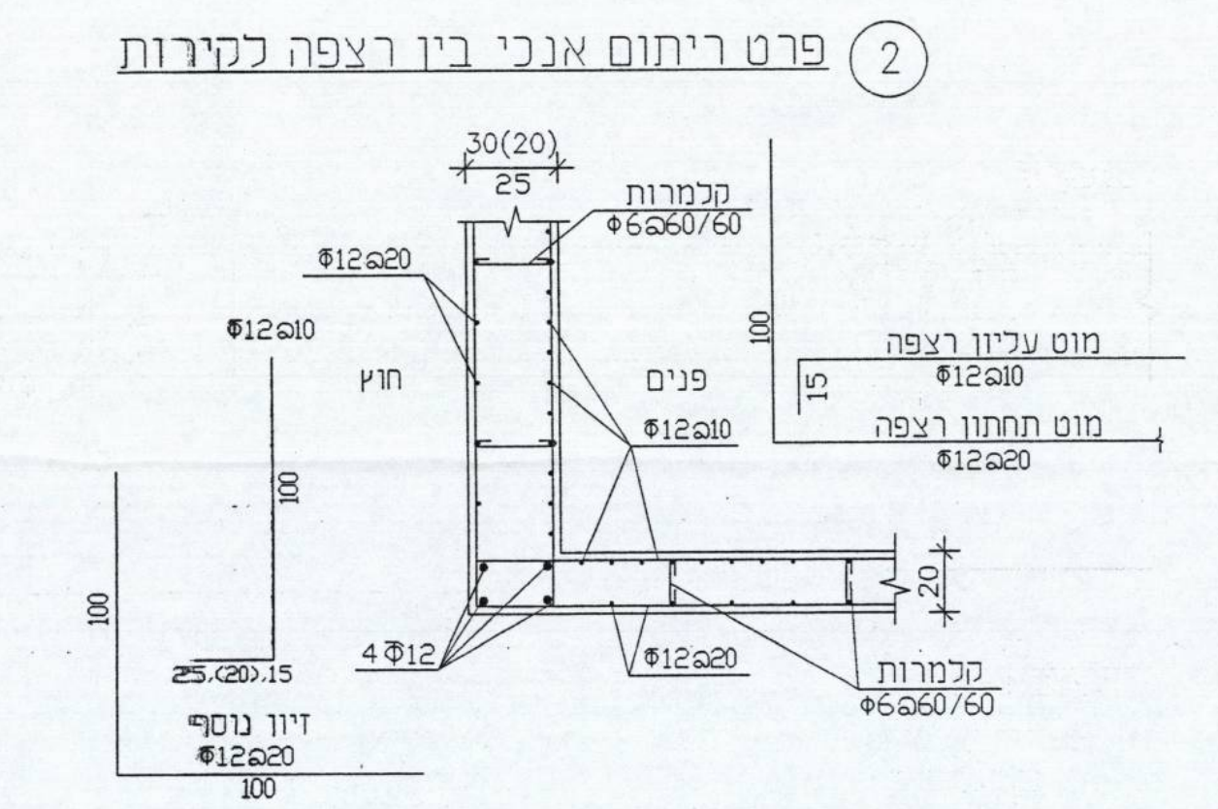

② פרט ריתום אנכי בין רצפה לקירות

30(20)
25
קלמרות Φ6@60/60
Φ12@20
Φ12@10
חוץ
פנים
Φ12@10
מוט עליון רצפה Φ12@10
מוט תחתון רצפה Φ12@20
100
4Φ12
Φ12@20
קלמרות Φ6@60/60
25.(20).15
זיון נוסף Φ12@20
100

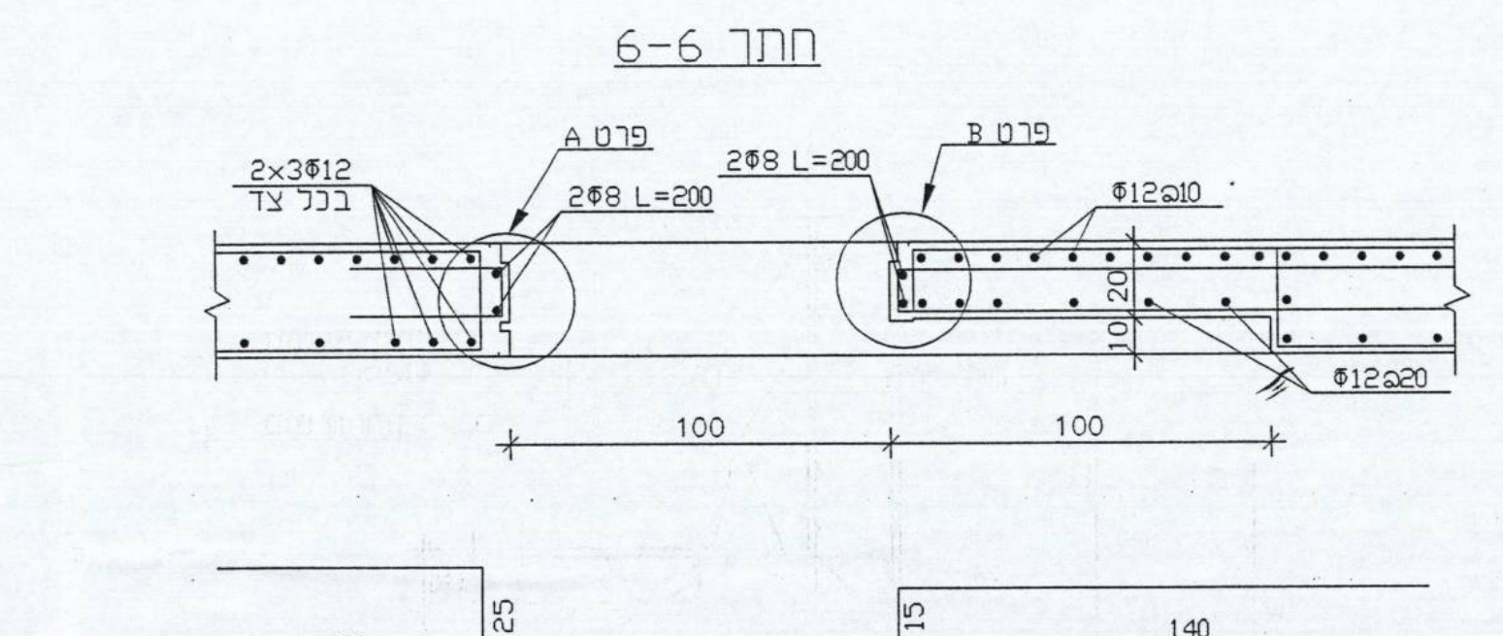

חתך 6-6

2x3Φ12
בכל צד
פרט A
2Φ8 L=200
2Φ8 L=200
פרט B
Φ12@10
Φ12@20
100 100
80
Φ8@20 L=185
140
Φ8@20 L=295
40
Φ8@20 L=90

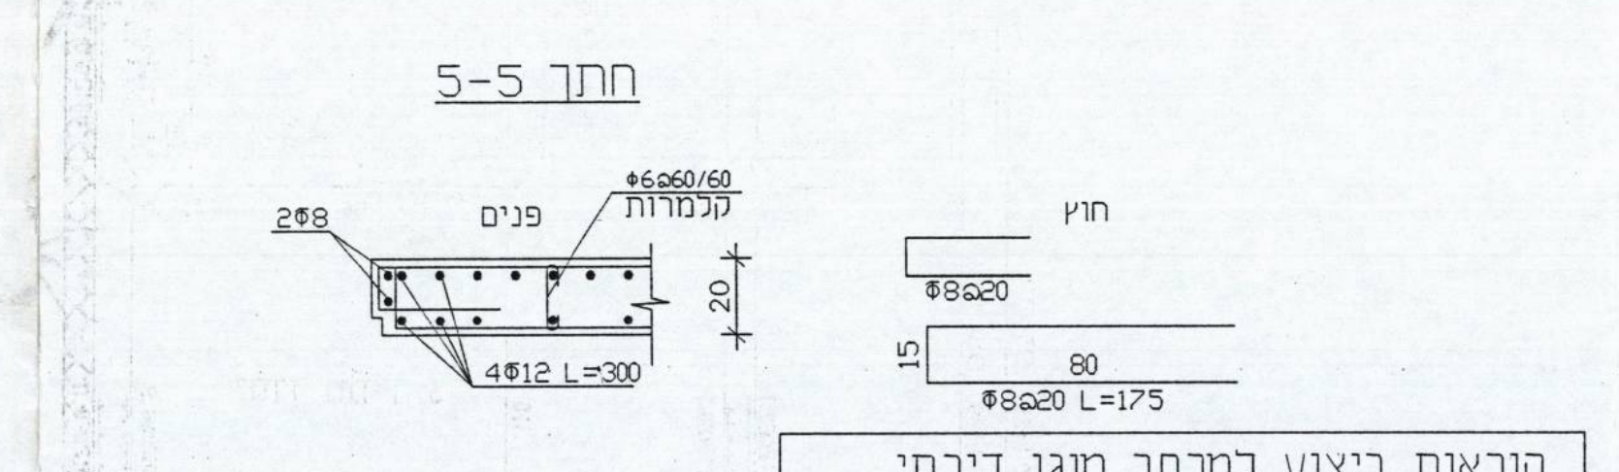

חתך 5-5

2Φ8
פנים
קלמרות Φ6@60/60
20
4Φ12 L=300
חוץ
Φ8@20
15
80
Φ8@20 L=175

הוראות ביצוע למרחב מוגן דירתי

המרחב המוגן הדירתי יבנה בהתאם לתקנות ההתגוננות האזרחית,במרחב המוגן יתקיימו עקרונות יסוד אלו:

1.המ.מ.ד יבנה מבטון כמבנה דמוי תיבה,עשוי מקשה אחת ורתום בכל חלקיו.
2.ריצפת המ.מ.ד,קירותיו ותיקרתו יהיו מישוריים וחלקים.
3.קירות המ.מ.ד יעבירו העומסים עד ליסודות ויהיו רציפים לכל גובה הבניין, ליצירת מיגדל מוגן.
4.סוג הבטון ב-30 בכל חלקי המ.מ.ד. לפי דרישות ת"י 118,החוזק לפי ת"י 466.
5.יציבות המיגדל תובטח מפני כוחות אופקיים.
6.מידות פתח לדלת כניסה יהיה 80/200 או 70/200. סוג דלת הכניסה (דלת הדף דירתית),דלת בטחון הג"א.
7.מידות פתח לחלון 110/110 או לפי אישור רשות מוסמכת,גובה תחתית חלון מריצפת החדר לא יהיה קטן מ-1.20 מ"א.
8.במידה ולא קיים פתח לחלון יש להתקין צינורות איוורור "18 Φ * 2 .
9.הכנת המ.מ.ד למערכות חשמל ותיקשורת לפי פרטים מצורפים.
10.פני הדופן הפנימית של המ.מ.ד יהיו חלקים עם גמר יציקת הבטון:
א.קירות להחלקה "שליכט בגר" עובי 2 מ"מ.
ב.טיח פנים פולימרי יעמוד בדרישות ת"י 1731,דרישות לעמידות ברטיבות בחדירת מים בתנאי גשם,אדי מים ובליה.
ג.טיח גבס יעמוד בדרישות מיפרט מיוחד פיקוד העורף.
ד.טיח טרמי מסוג "תרמוקיר 400" על בסיס פוליסטירן מותפח, כולל שכבת "הרבצה צמנטית",שכבת בידוד טיח טרמי "תרמוקיר 400",שכבת מגן ושכבת גמר "שליכט גמר".
11.הקבלן חייב להחזיק תוכנית מאושרת של המ.מ.ד באתר הבניה עד לסיום הקמתו.

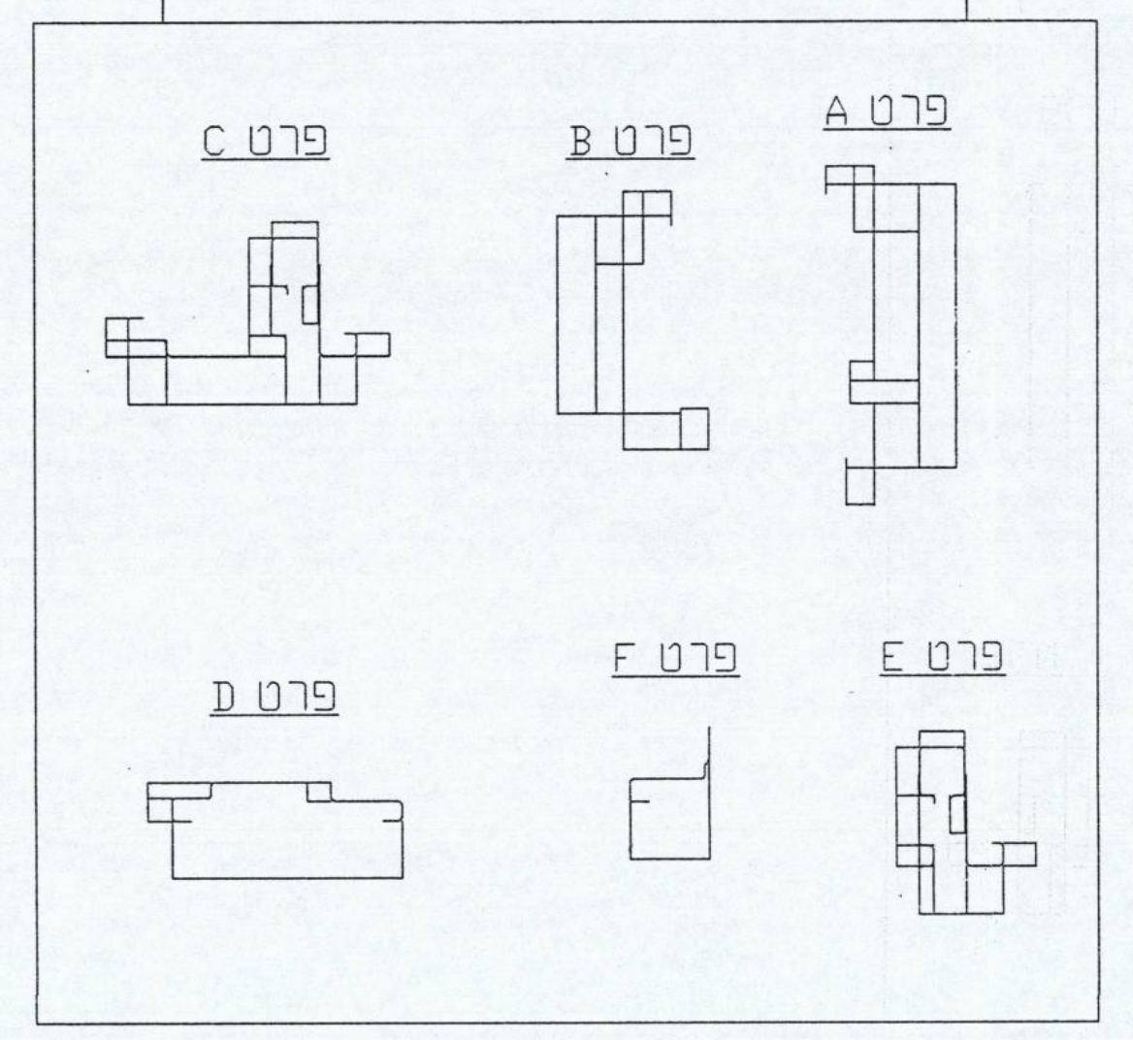

פרט C
פרט B
פרט A
פרט D
פרט F
פרט E

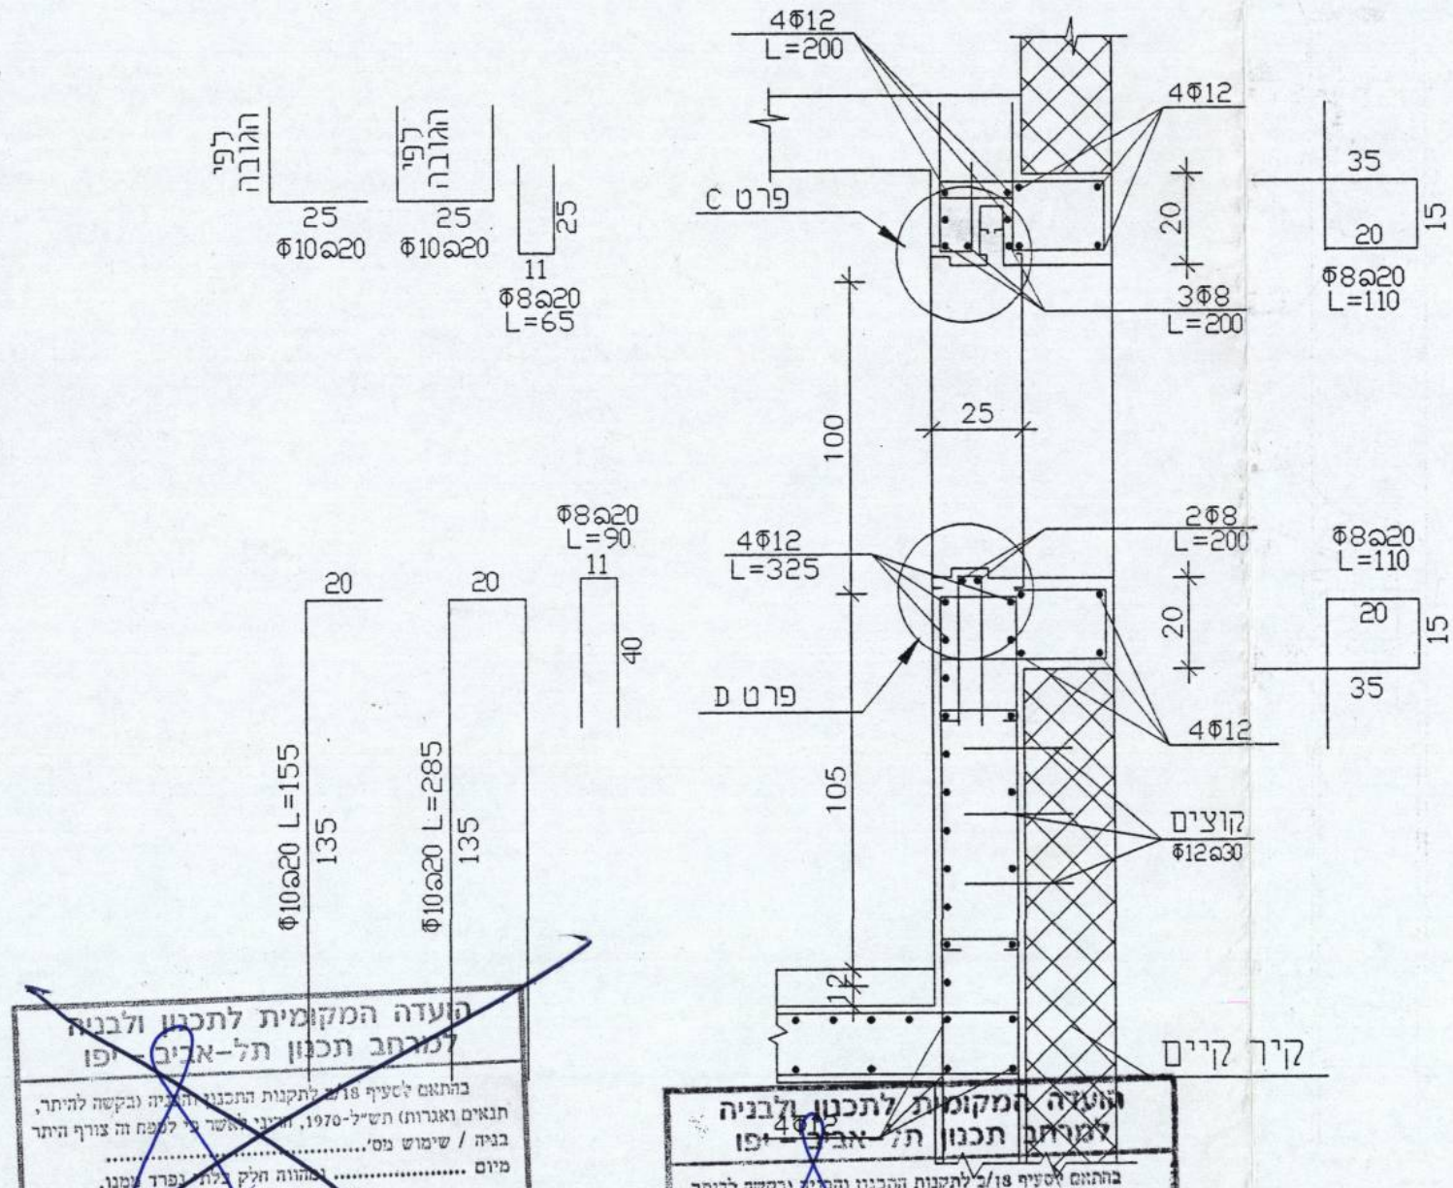

חתך א2-א2

4Φ12
L=200
4Φ12
פרט C
3Φ8
L=200
35
20
Φ8@20
L=110
25
לפי הגובה
Φ10@20
Φ8@20
L=65
100
4Φ12
L=325
2Φ8
L=200
Φ8@20
L=90
פרט D
105
4Φ12
קוצים Φ12@30
Φ10@20 L=155
Φ10@20 L=285
135
קיר קיים

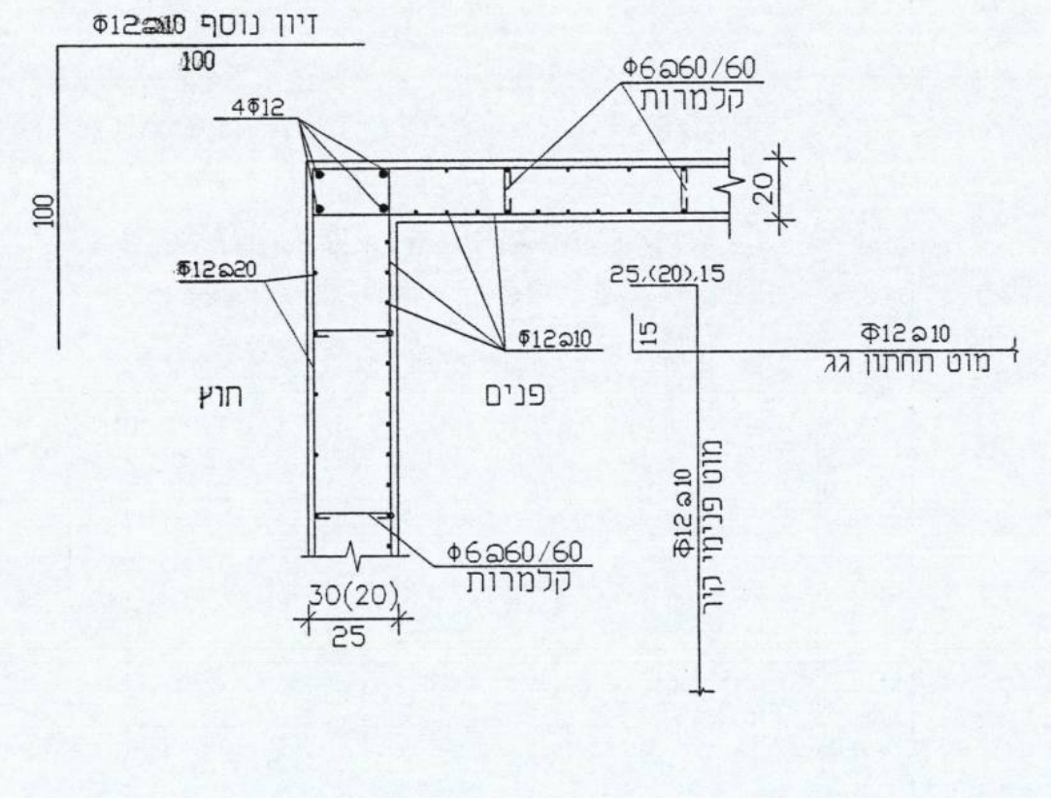

③ פרט ריתום אנכי בין קיר לגג

זיון נוסף Φ12@10
100
4Φ12
קלמרות Φ6@60/60
Φ12@20
Φ12@10
25.(20).15
Φ12@10
מוט תחתון גג
חוץ
פנים
Φ12@10
מוט פנימי קיר
קלמרות Φ6@60/60
30(20)
25

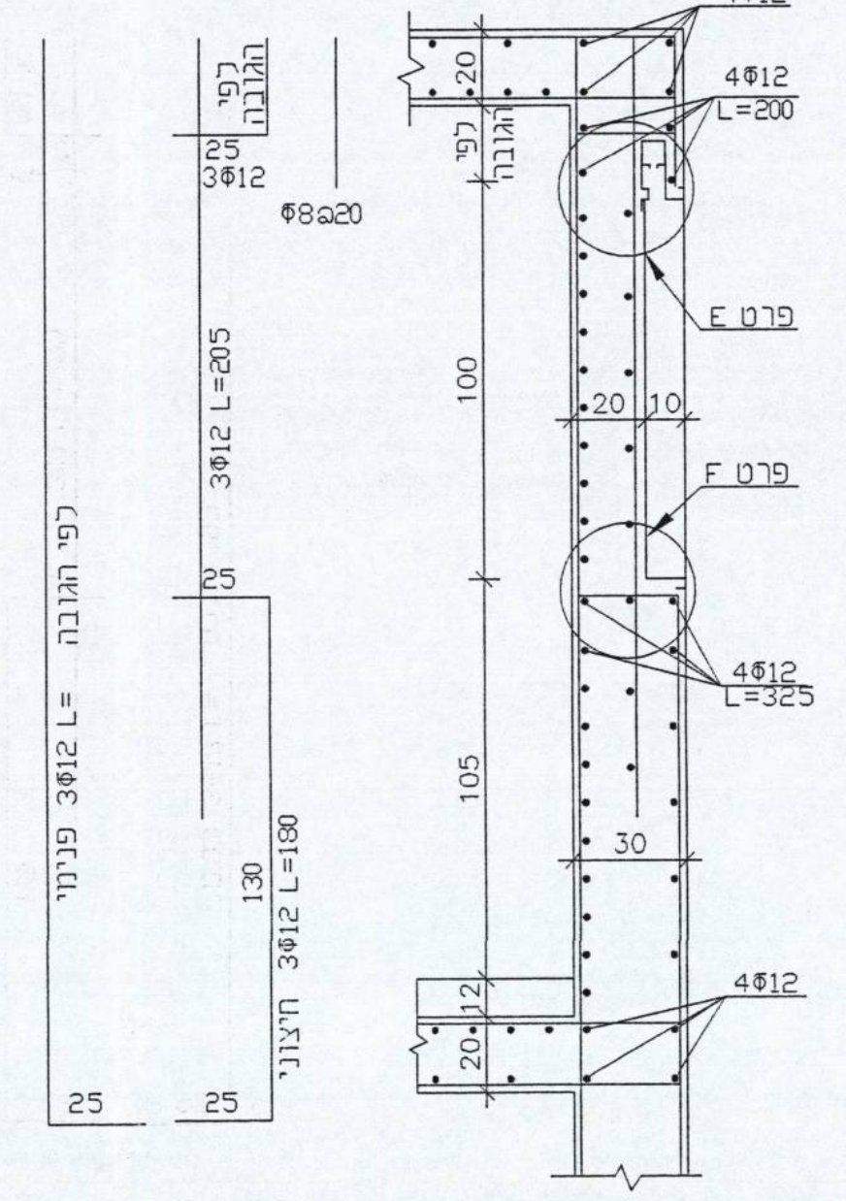

חתך 8-8

לפי הגובה
3Φ12
Φ8@20
4Φ12
4Φ12
L=200
פרט E
100
20 10
פרט F
4Φ12
L=325
105
30
3Φ12 L=205
3Φ12 L=180
130
חיצוני
פנימי
4Φ12
25 25

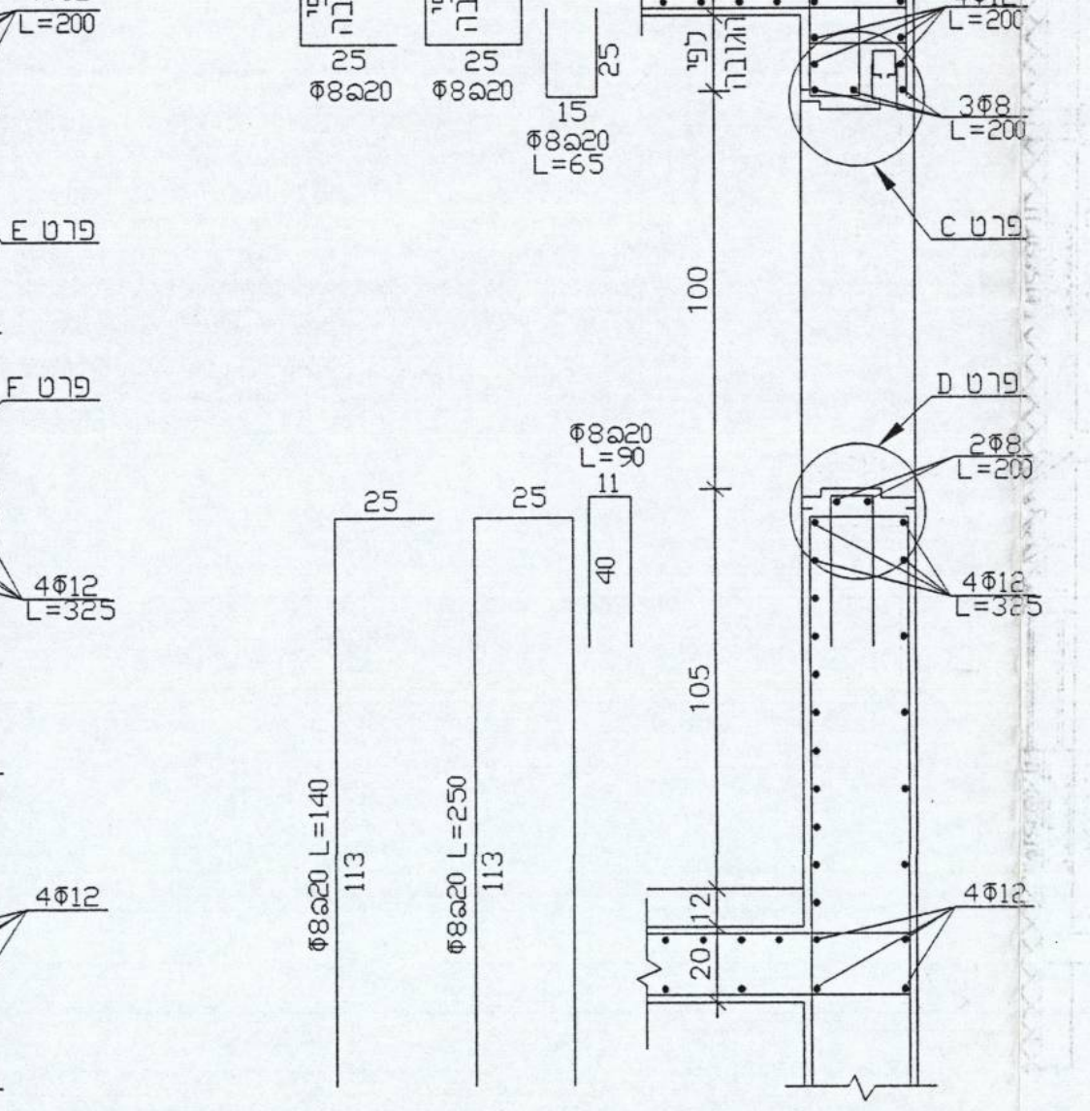

חתך 7-7

לפי הגובה
Φ8@20
15
Φ8@20
L=65
4Φ12
4Φ12
L=200
3Φ8
L=200
פרט C
100
פרט D
2Φ8
L=200
Φ8@20
L=90
4Φ12
L=325
105
Φ8@20 L=140
Φ8@20 L=250
113
25 25
4Φ12

סוף מסמך

~~הועדה המקומית לתכנון ולבניה~~
~~למרחב תכנון תל-אביב-יפו~~
~~בהתאם לסעיף 18/ב לתקנות התכנון והבניה (בקשה להיתר, תנאים ואגרות) תש"ל-1970, הריני לאשר כי לטפח זה צורף היתר בניה / שימוש מס'..........~~
~~מיום .... ומהווה חלק בלתי נפרד ממנו.~~
~~מהנדס העיר~~
~~תאריך 09-01-2007~~

~~06-0027~~

עירית תל-אביב-יפו
מינהל ההנדסה / היתרי בניה
לפי תוכנית מאושרת זו מיום ______
מותר להגיש השבון.
להגיש תוכנית סניטרית ______
אחראי לאזור ______

הועדה המקומית לתכנון ולבניה
למרחב תכנון תל-אביב-יפו
בהתאם לסעיף 18/ב לתקנות התכנון והבניה (בקשה להיתר, תנאים ואגרות) תש"ל-1970, הריני לאשר כי לטפח זה צורף היתר בניה / שימוש מס' 080292
מיום 14-04-2008 ומהווה חלק בלתי נפרד ממנו.
מהנדס העיר
תאריך..........

07-0660

משי נפתלי
רחי אצ"ל 58 , ת"א