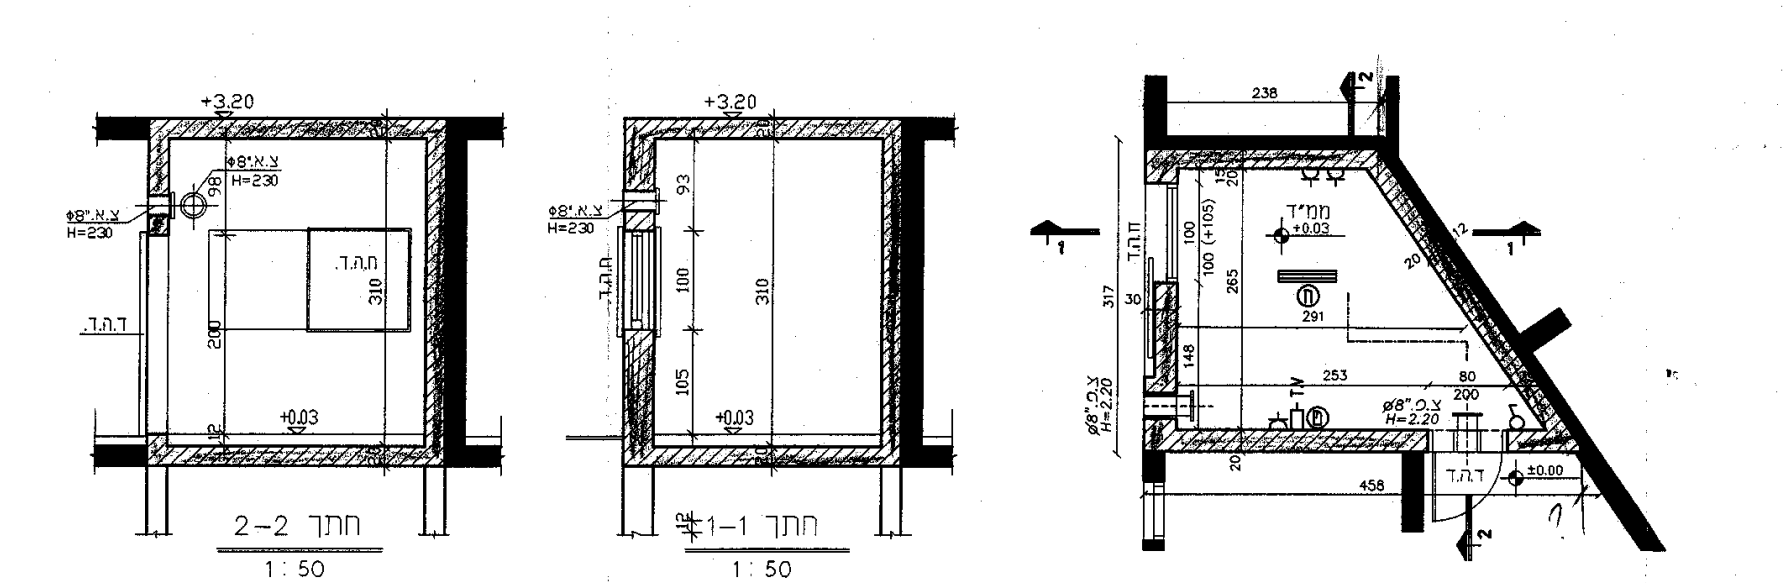
חתך 2-2
1:50
חתך 1-1
1:50

ממ"ד דירה מס' 5
קנ"מ: 1:50

מקרא

○	שקע
ט.ע	טלויזיה
⊕	טלפון
	נ.ת. חורום 40w
▬	נ.ת. פלורוסנט 2×40w
♂	מפסק בודד

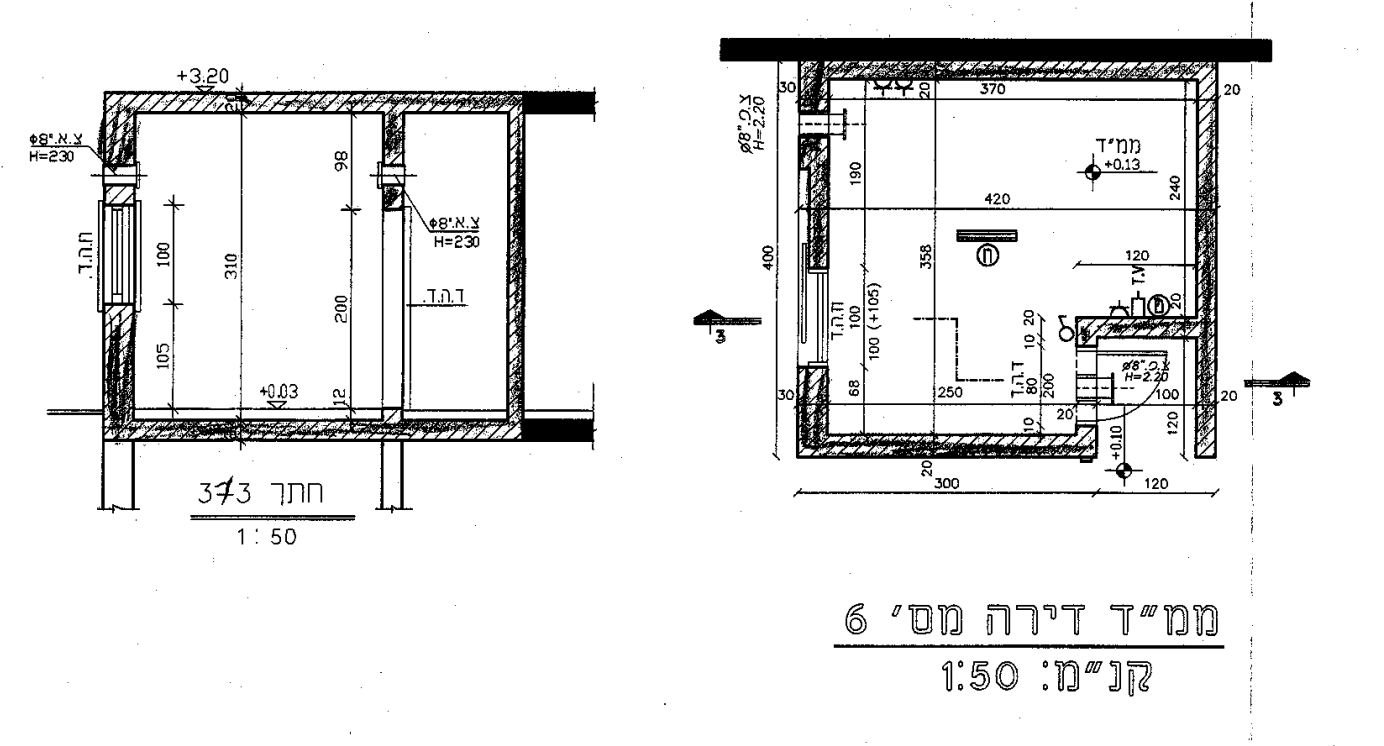

ממ"ד דירה מס' 6
קנ"מ: 1:50

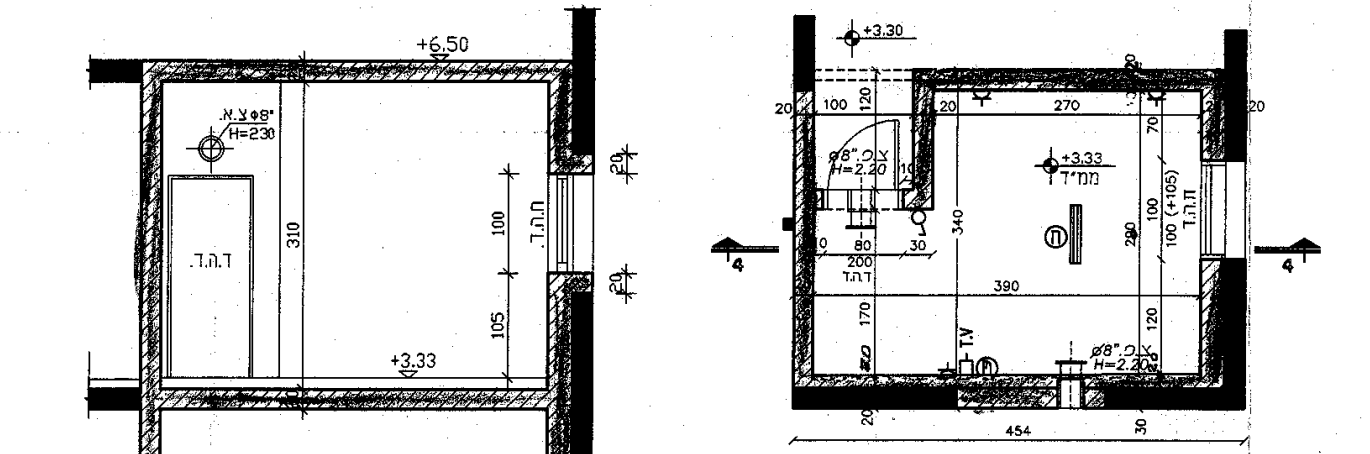

ממ"ד דירה מס' 7
קנ"מ: 1:50

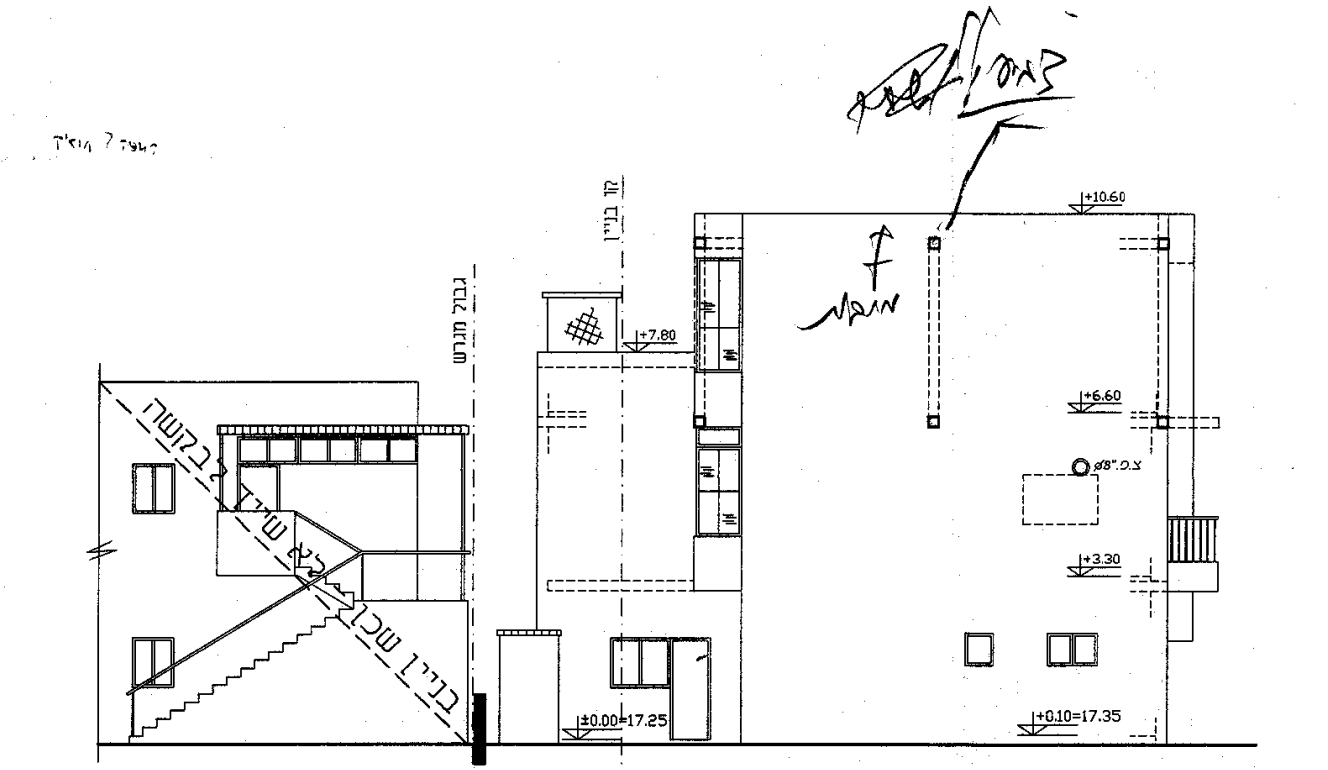
בניין שכן לא שייך לבקשה
קיים להריסה

חזית דרומית
קנ"מ: 1:100

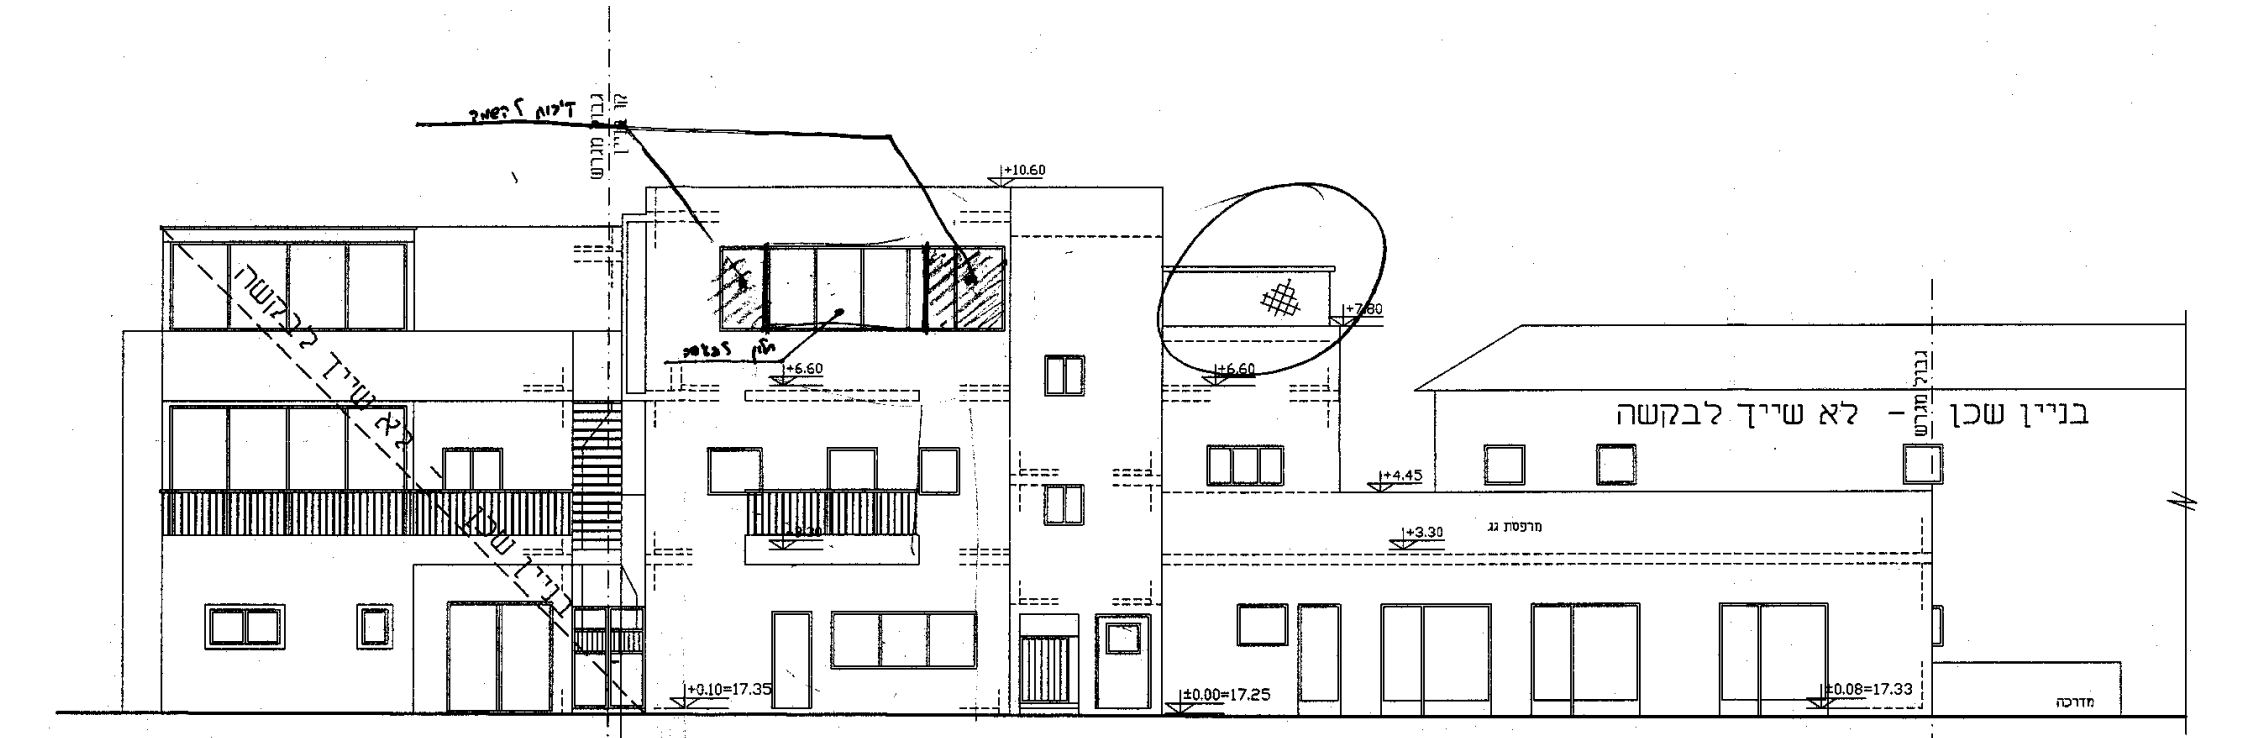
בניין שכן לא שייך לבקשה
לא שייך לבקשה

חזית מזרחית
קנ"מ: 1:100

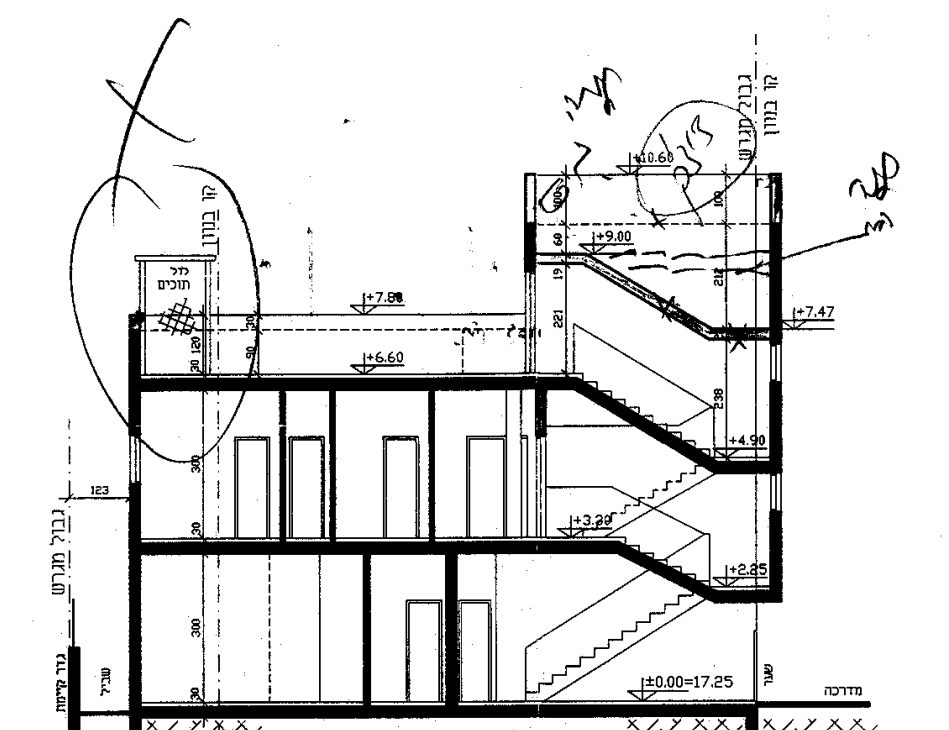

חתך א-א
קנ"מ: 1:100

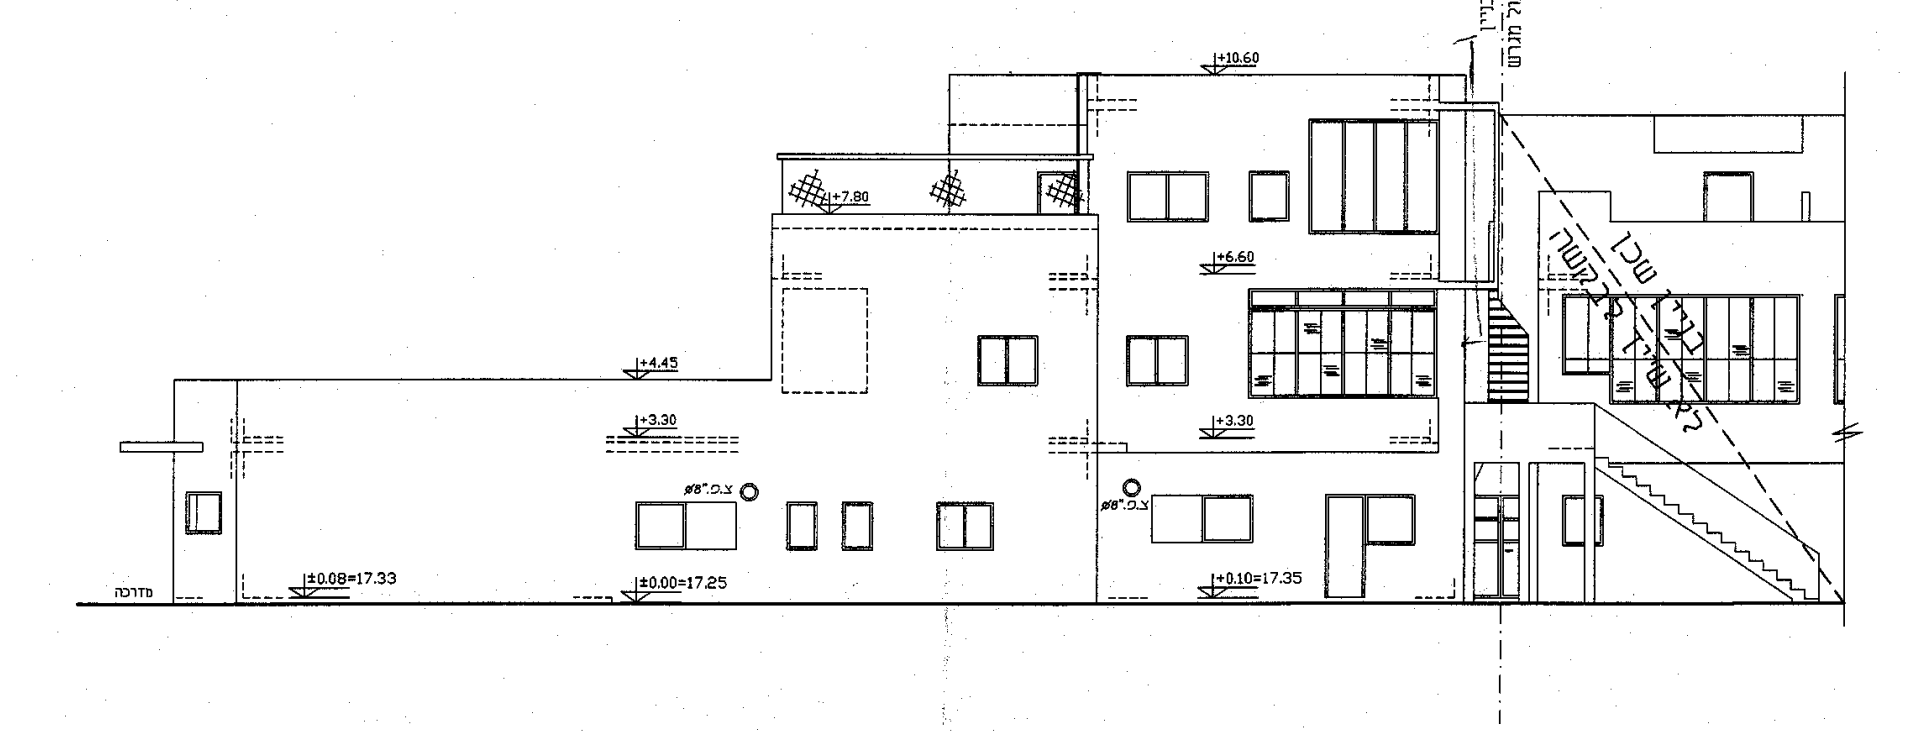
בניין שכן לא שייך לבקשה

חזית מערבית
קנ"מ: 1:100

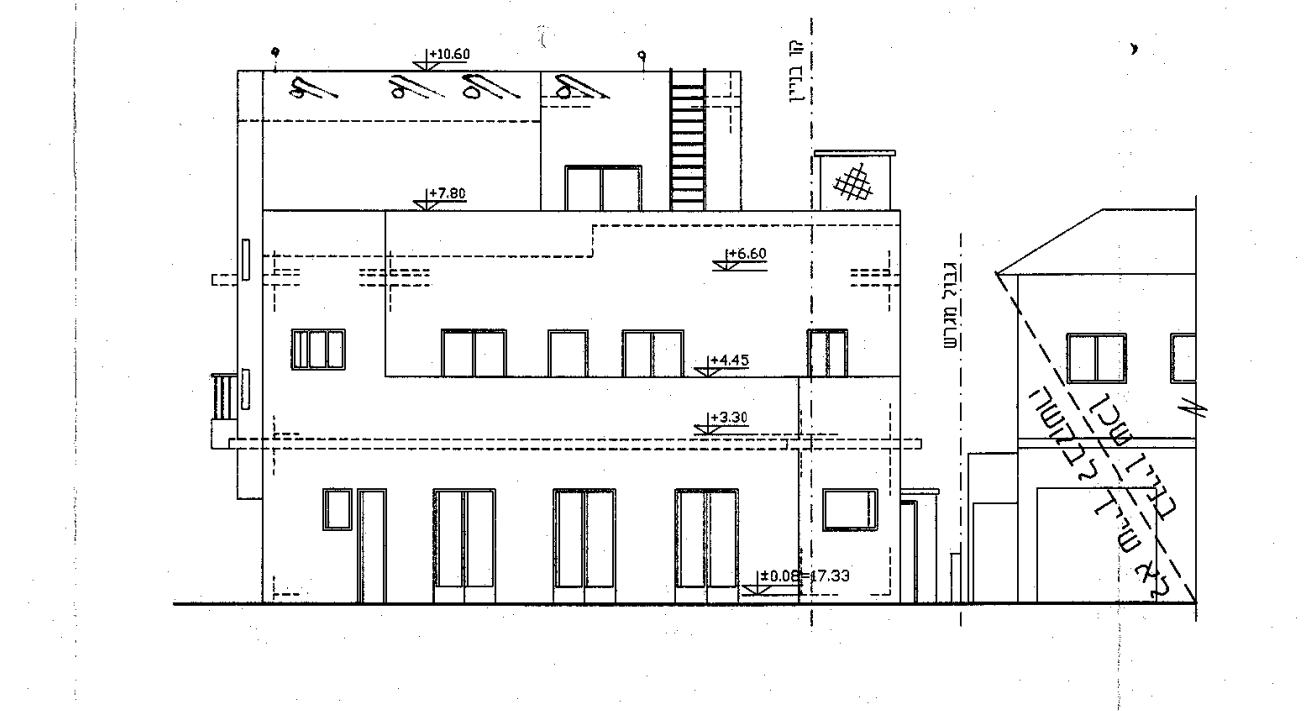
בניין שכן לא שייך לבקשה

חזית צפונית
קנ"מ: 1:100

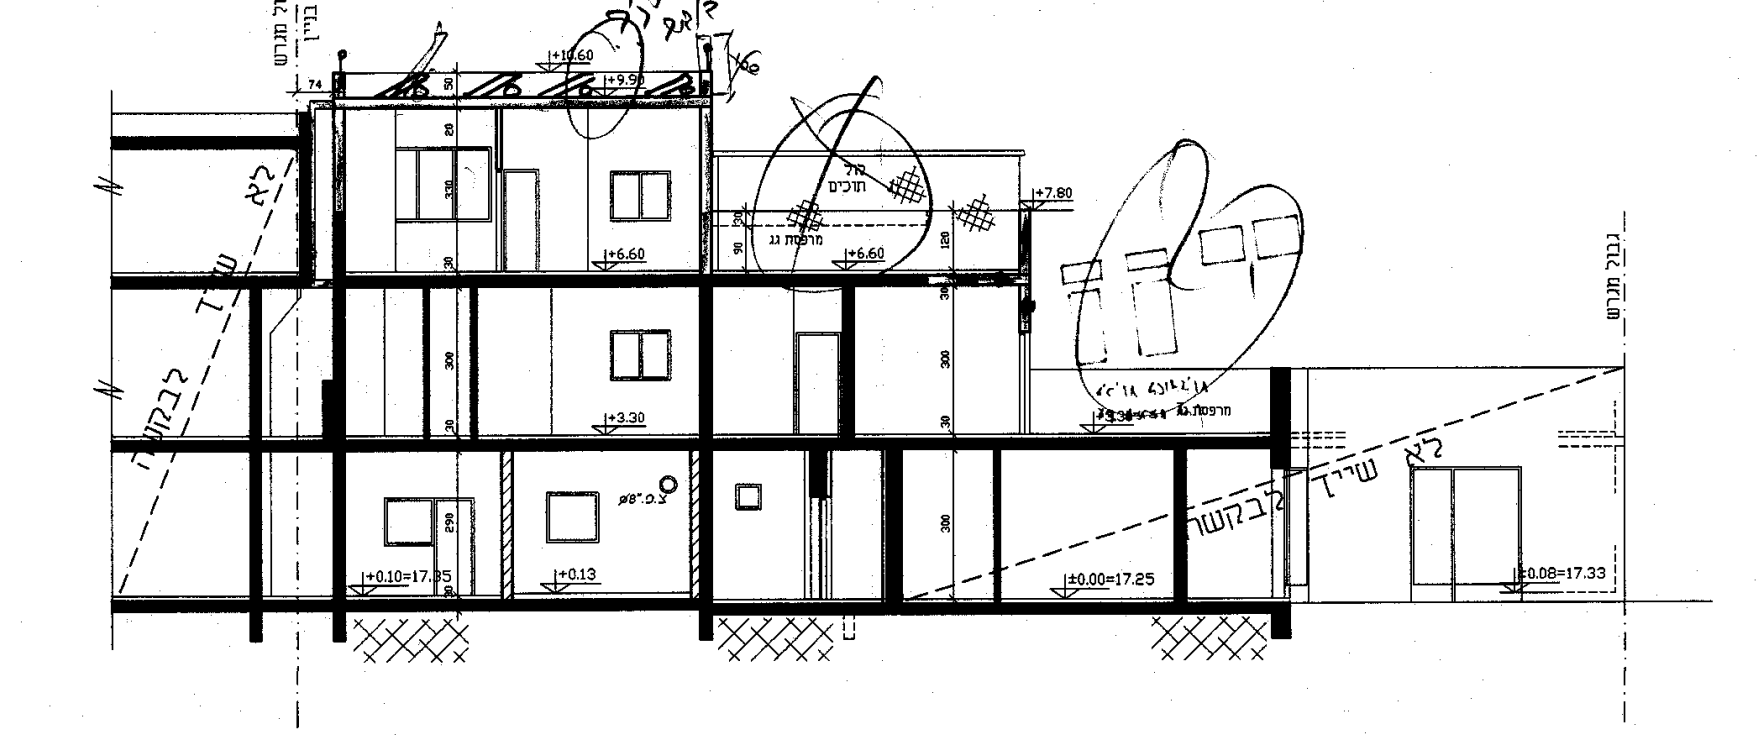
לא שייך לבקשה

חתך ב-ב
קנ"מ: 1:100

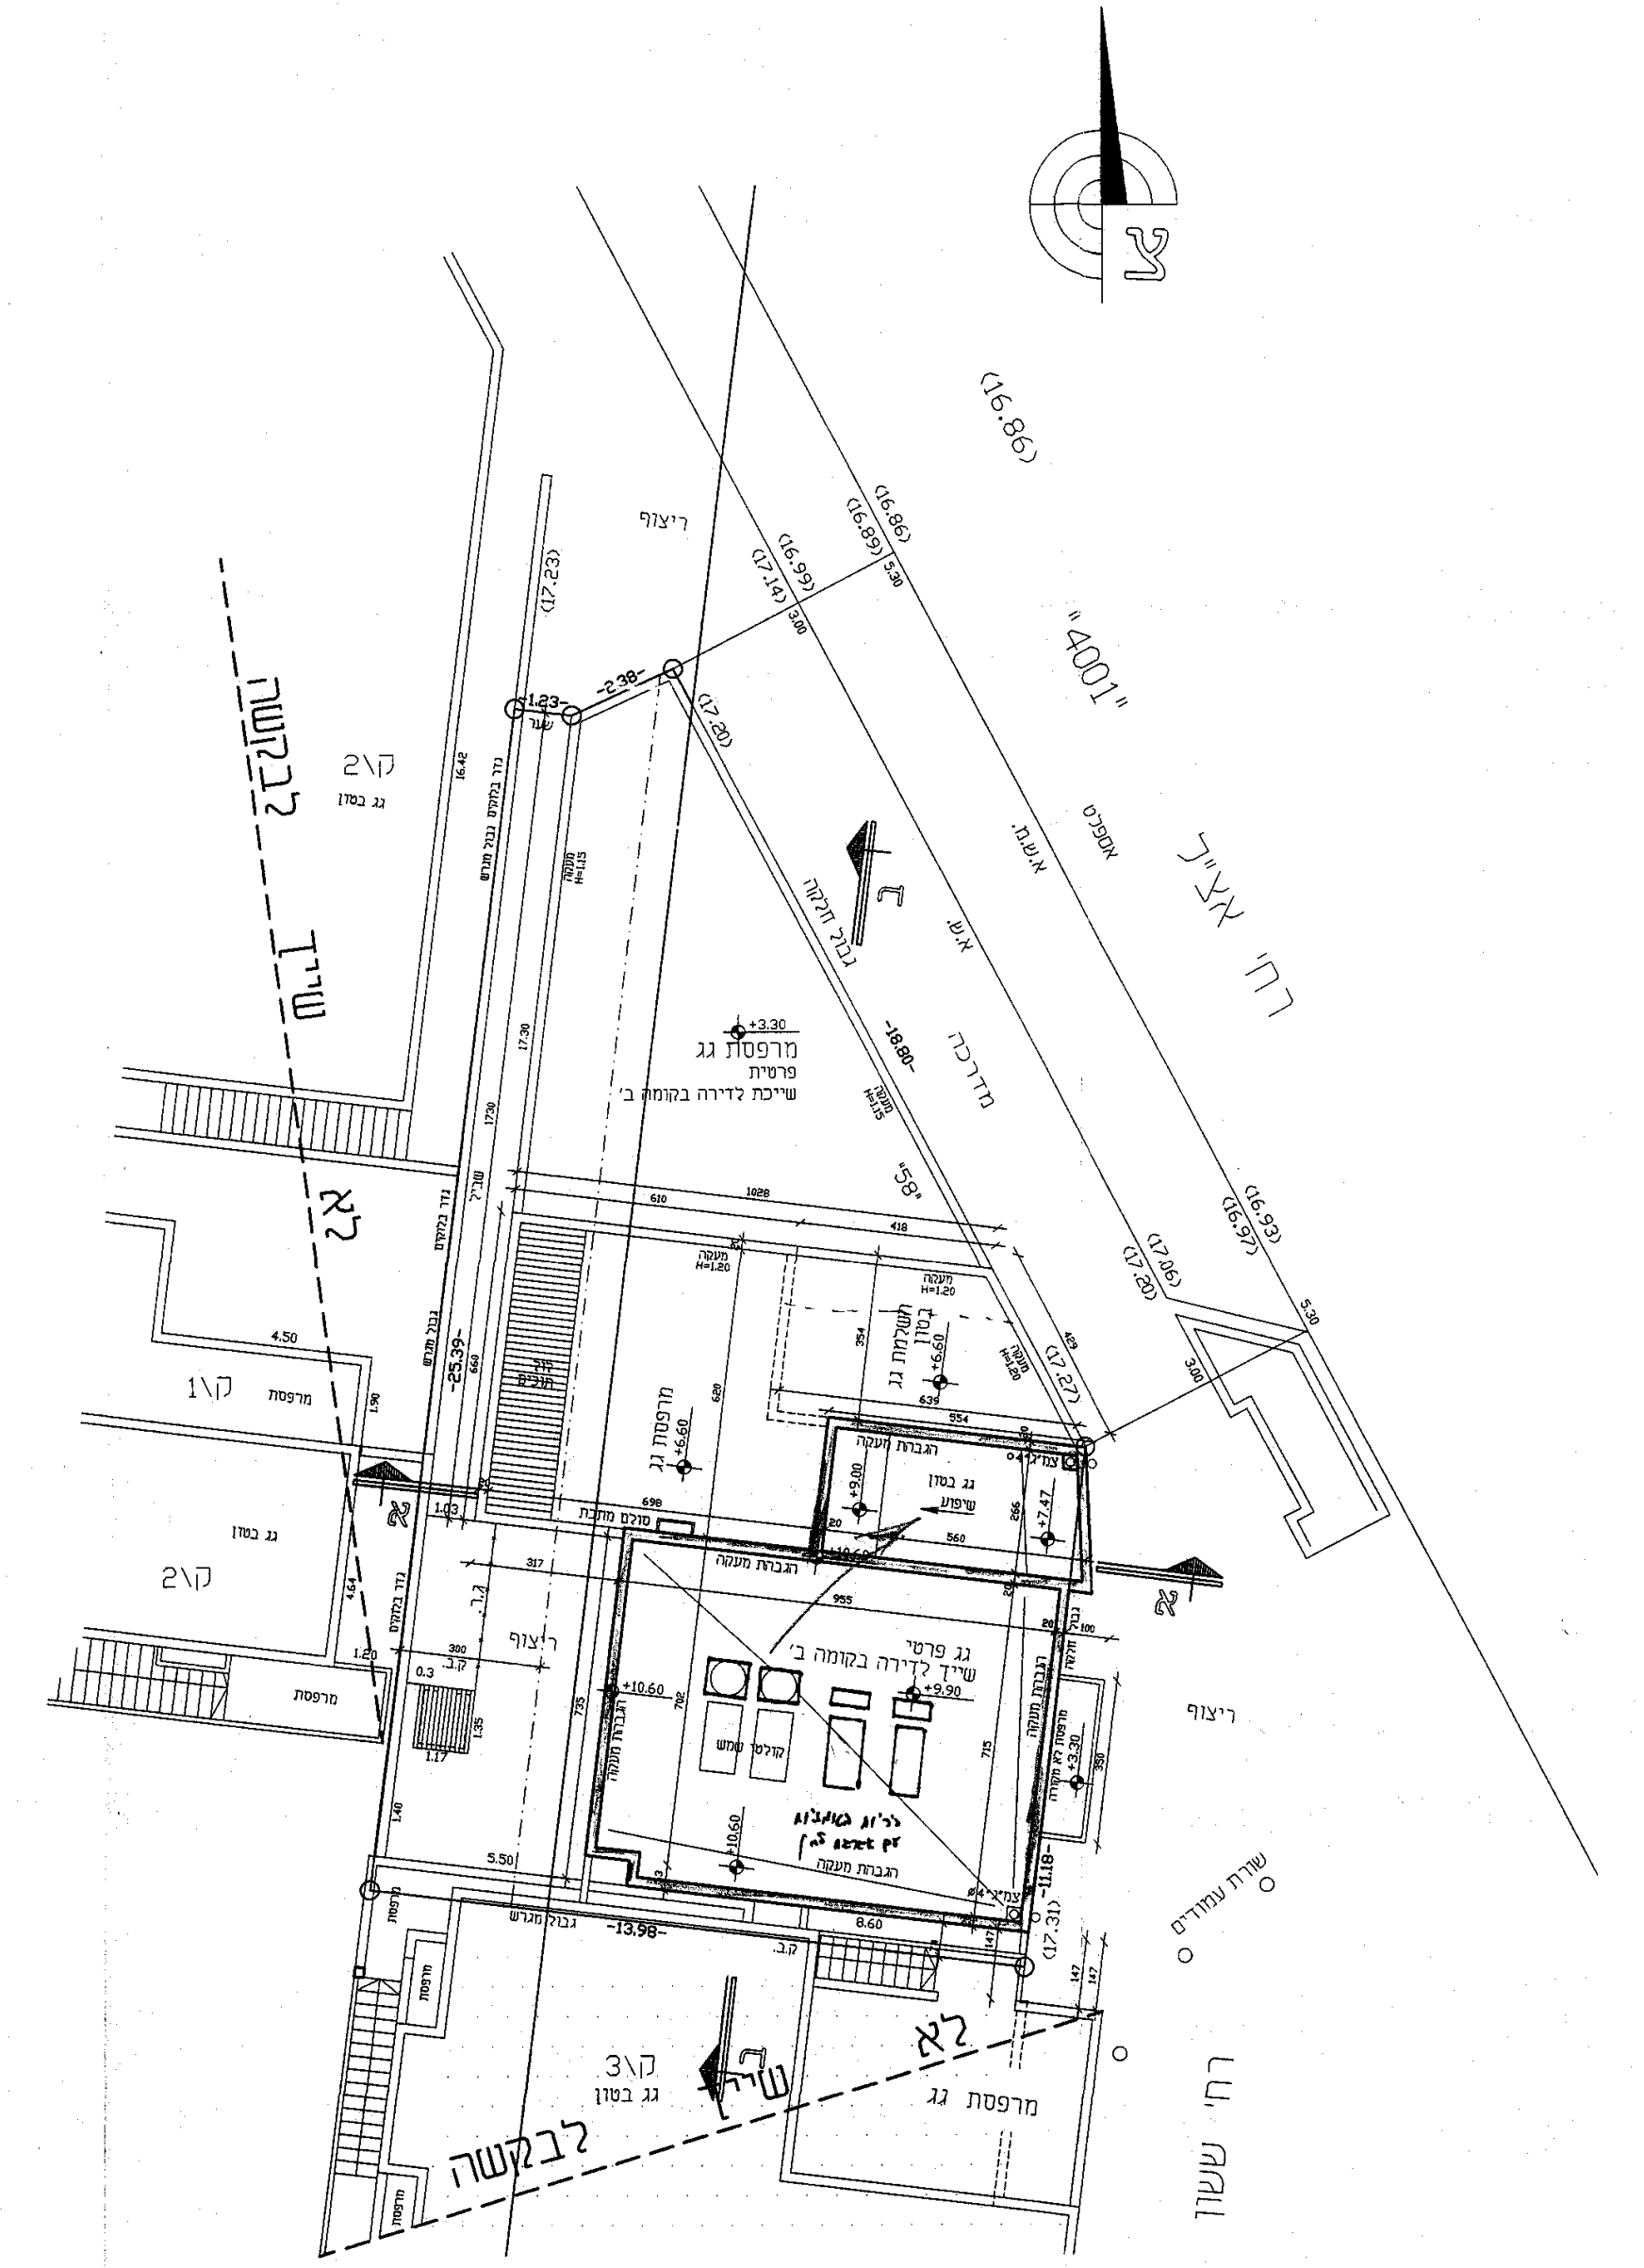
צ
רח' אצ"ל
"4001"
(16.86)
ריצוף
מדרכה
מרפסת גג
פרטית
שייכת לדירה בקומה ב'
לא שייך לבקשה
רח' ששון
שדרת עמודים
ק\2
ק\3
ק\1

תוכנית גג
קנ"מ: 1:100

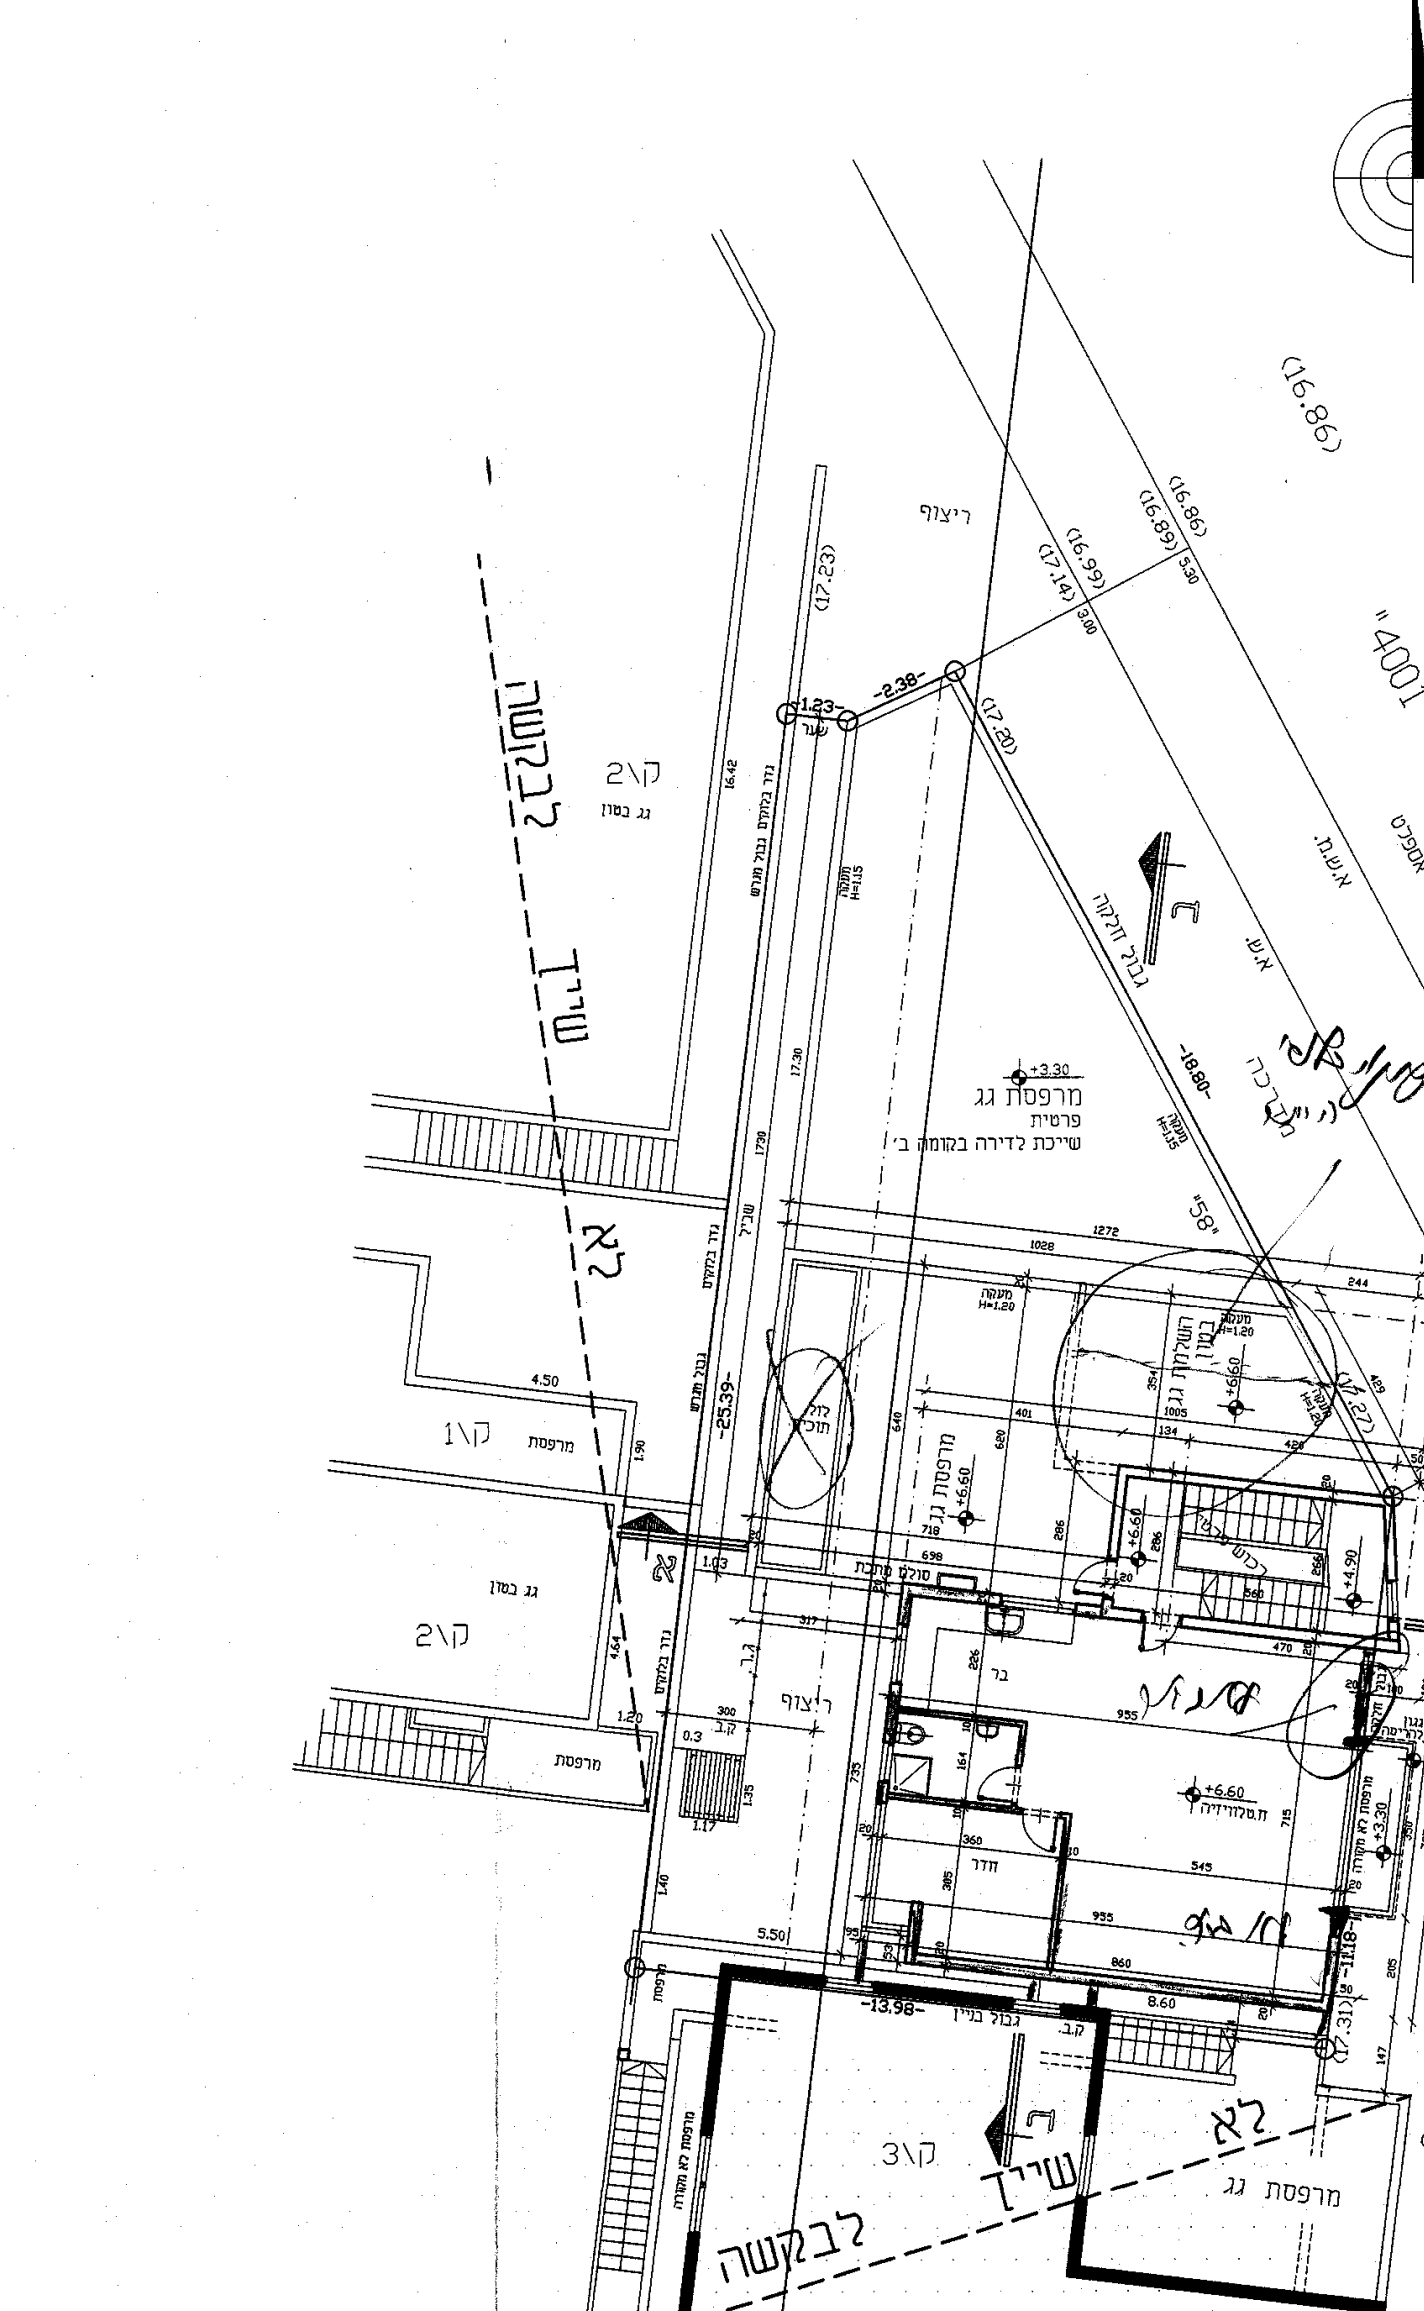
צ
רח' אצ"ל
"4001"
(16.86)
ריצוף
מדרכה
מרפסת גג
פרטית
שייכת לדירה בקומה ב'
לא שייך לבקשה
רח' ששון
שדרת עמודים
ק\1
ק\2
ק\3

תוכנית קומה ב'
קנ"מ: 1:100

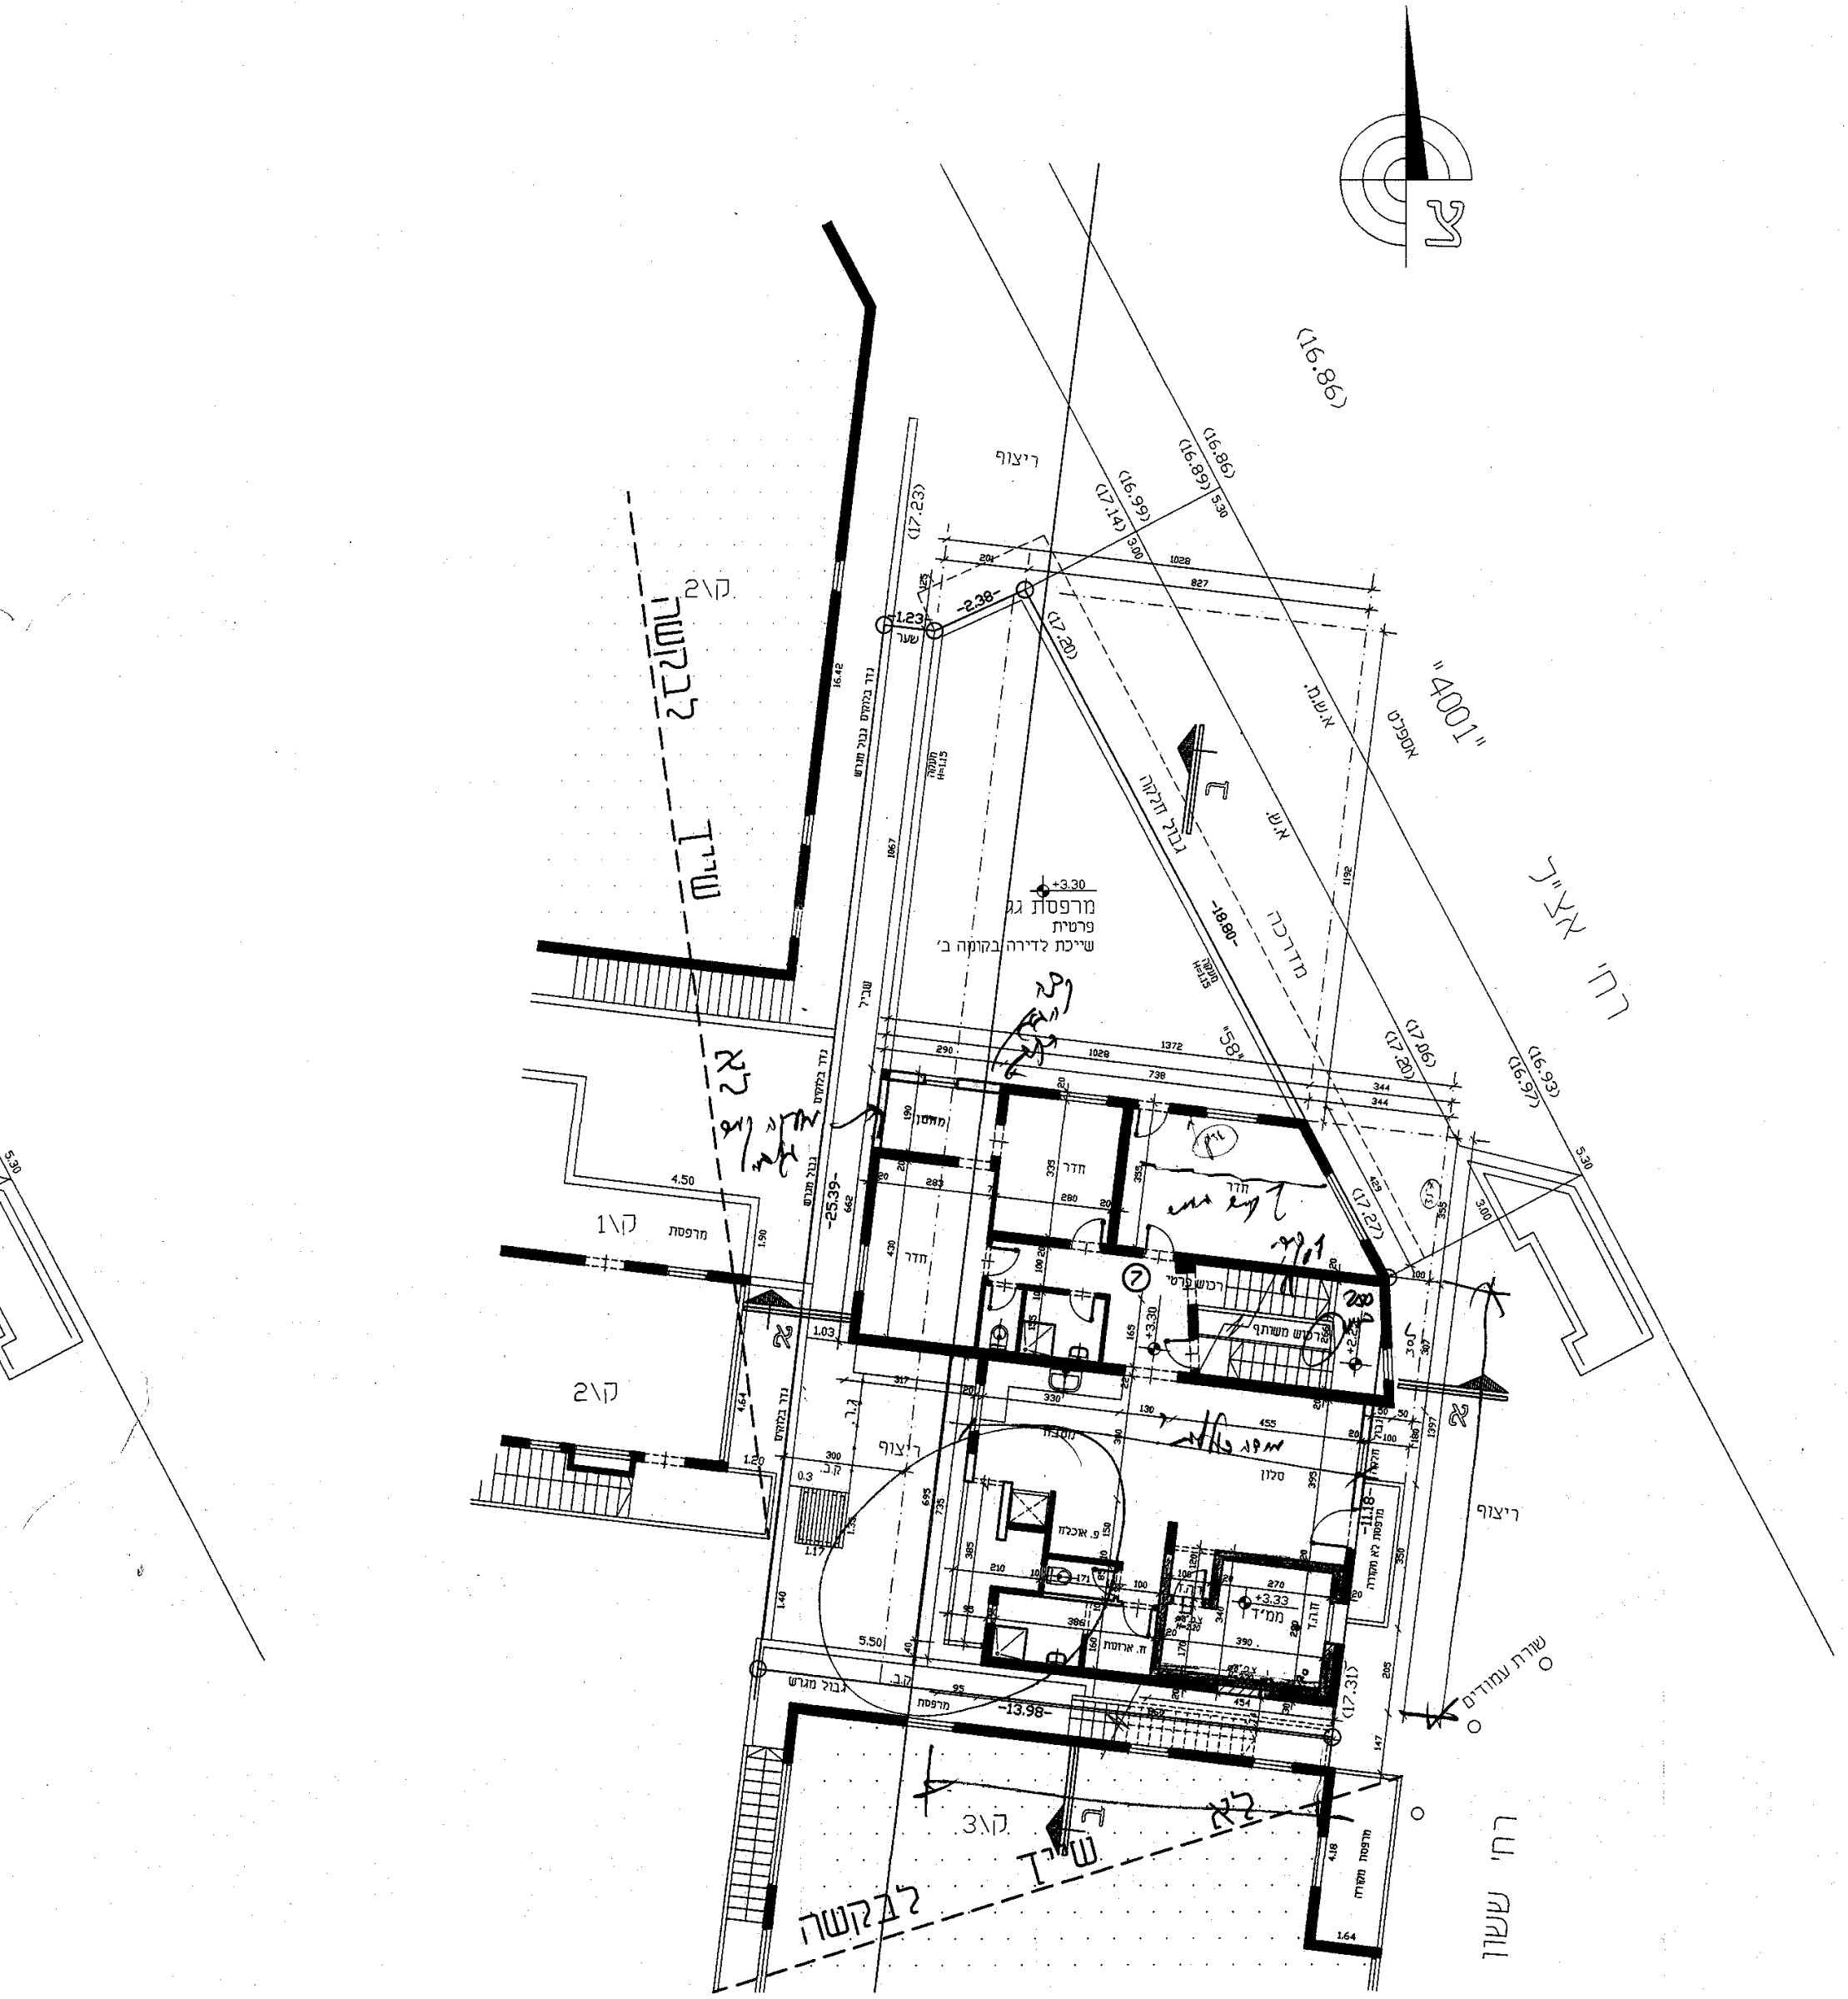
צ
רח' אצ"ל
"4001"
(16.86)
ריצוף
מדרכה
לא שייך לבקשה
רח' ששון
שדרת עמודים
ק\1
ק\2
ק\3

תוכנית קומה א'
קנ"מ: 1:100

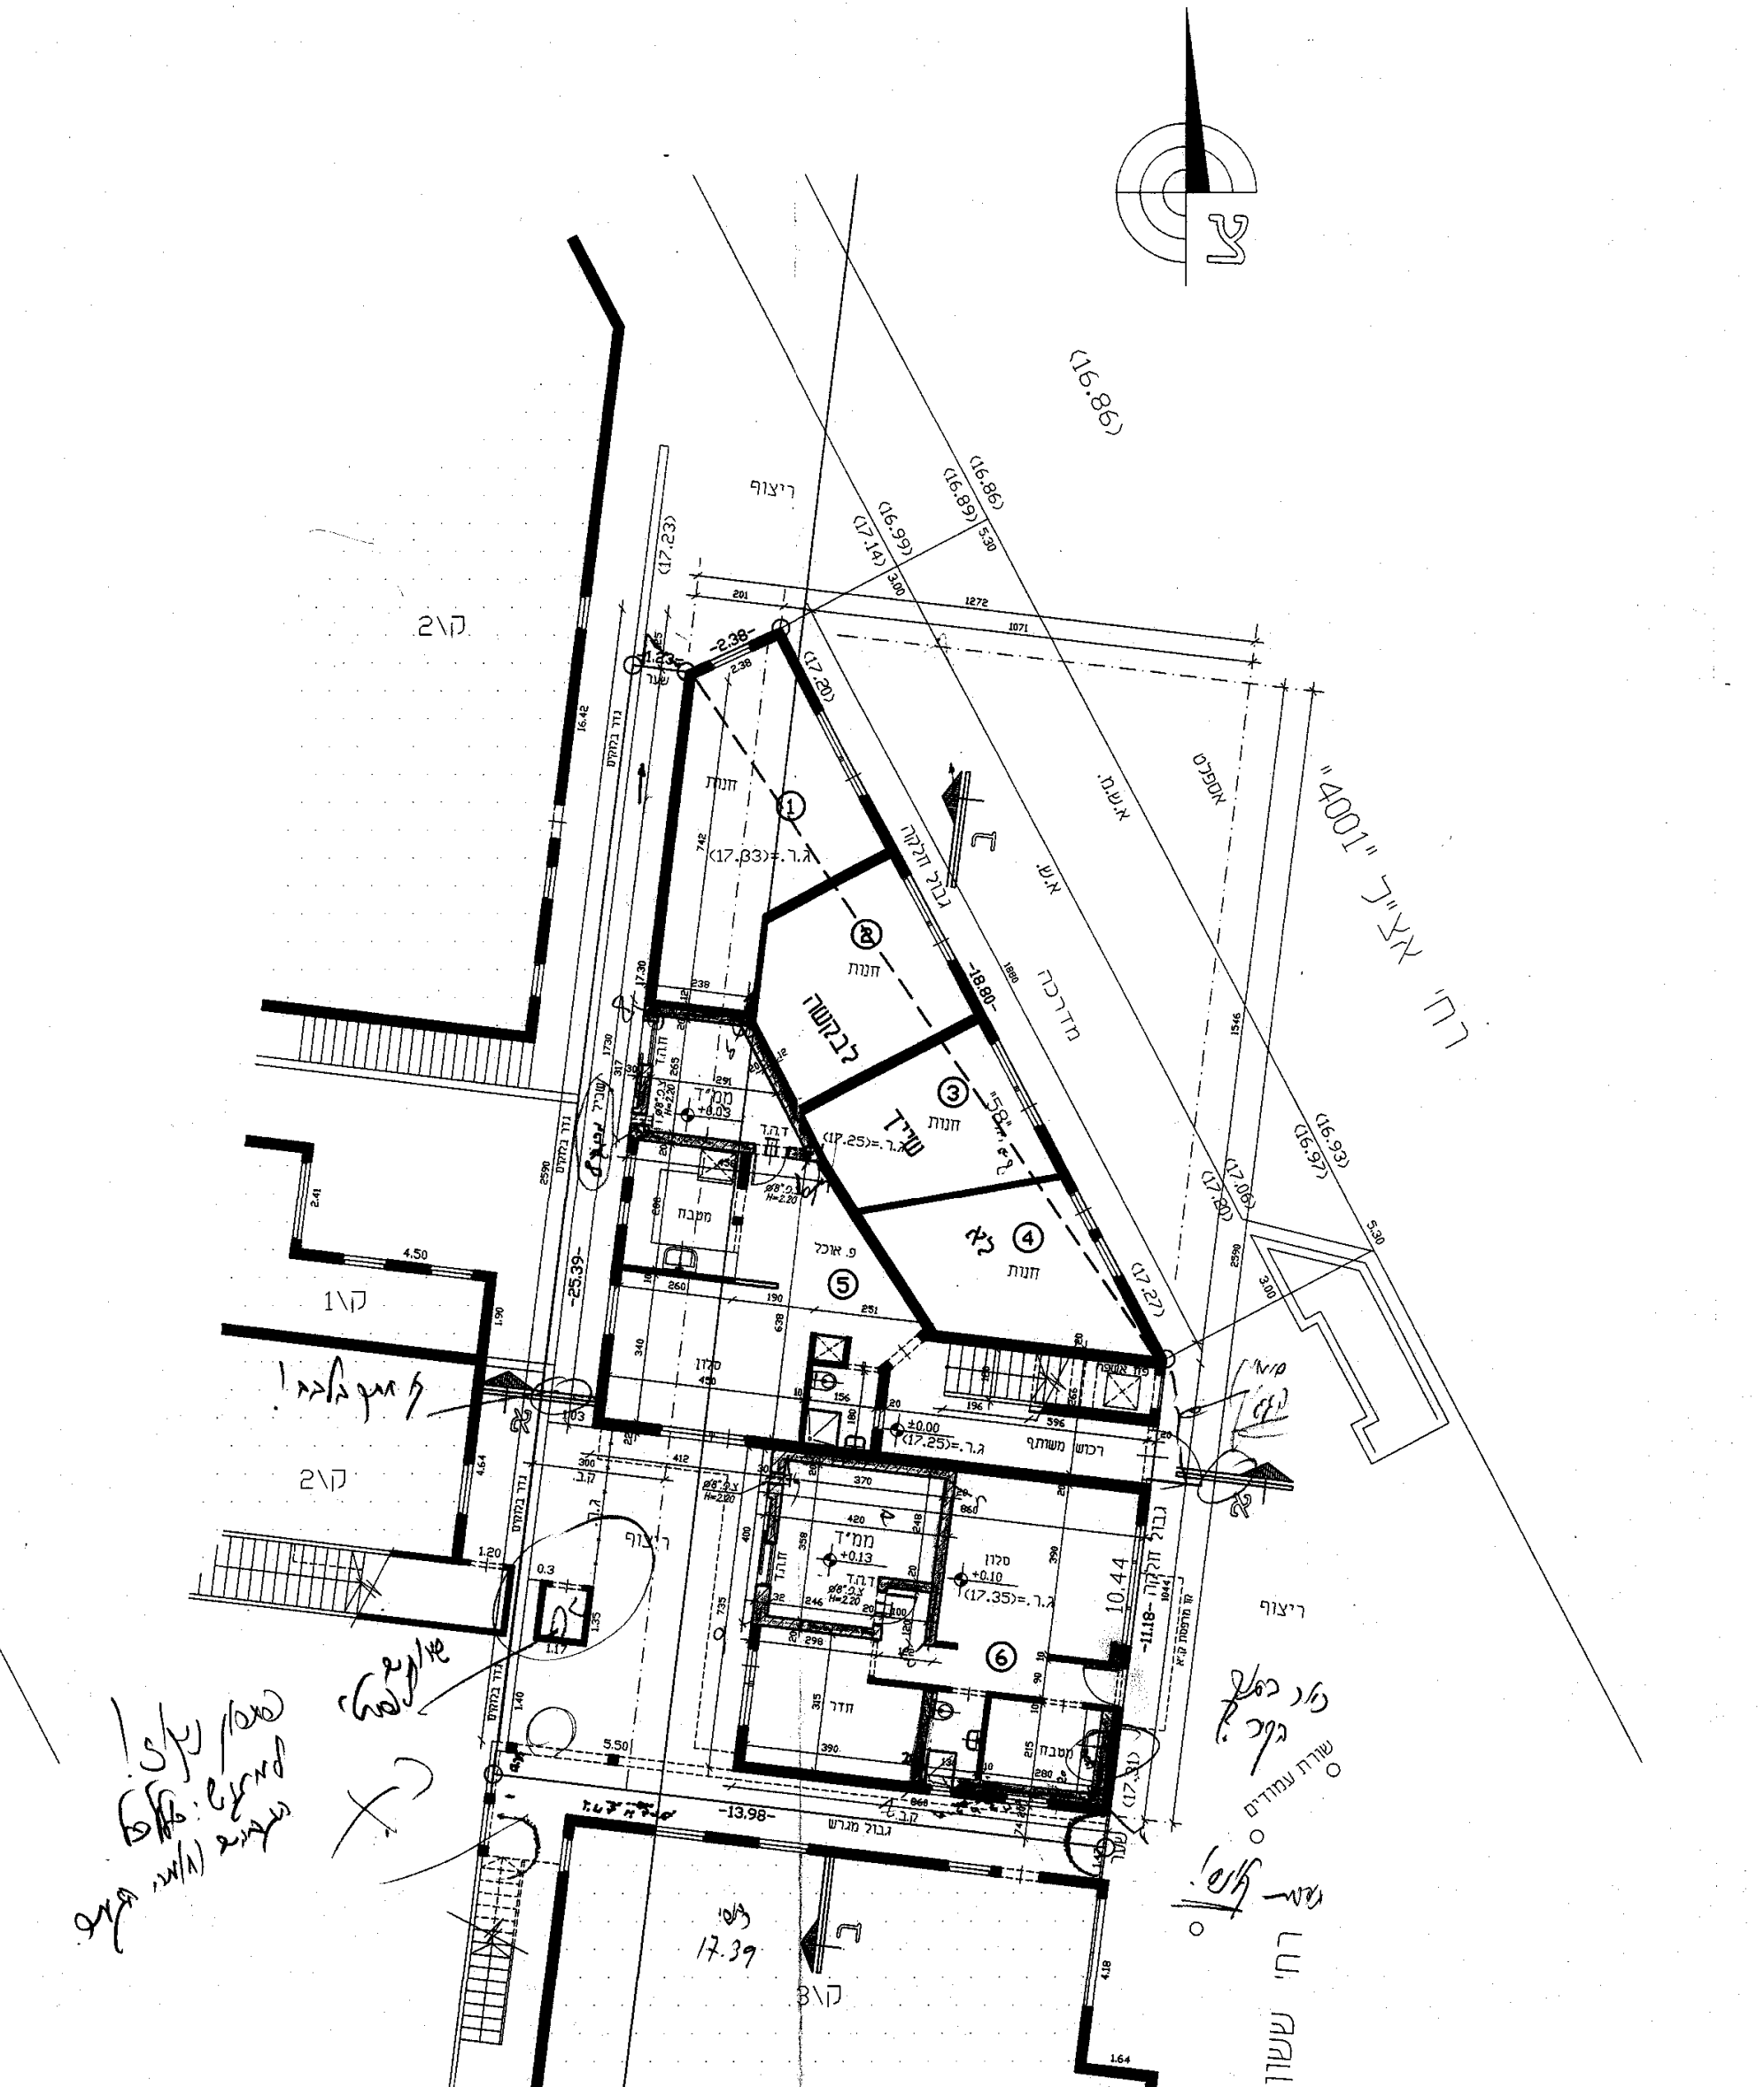
צ
רח' אצ"ל
"4001"
(16.86)
ריצוף
מדרכה
לבקשה
רח' ששון
שדרת עמודים
ק\1
ק\2
ק\3

תוכנית קומת קרקע
קנ"מ: 1:100

חישוב שטחים

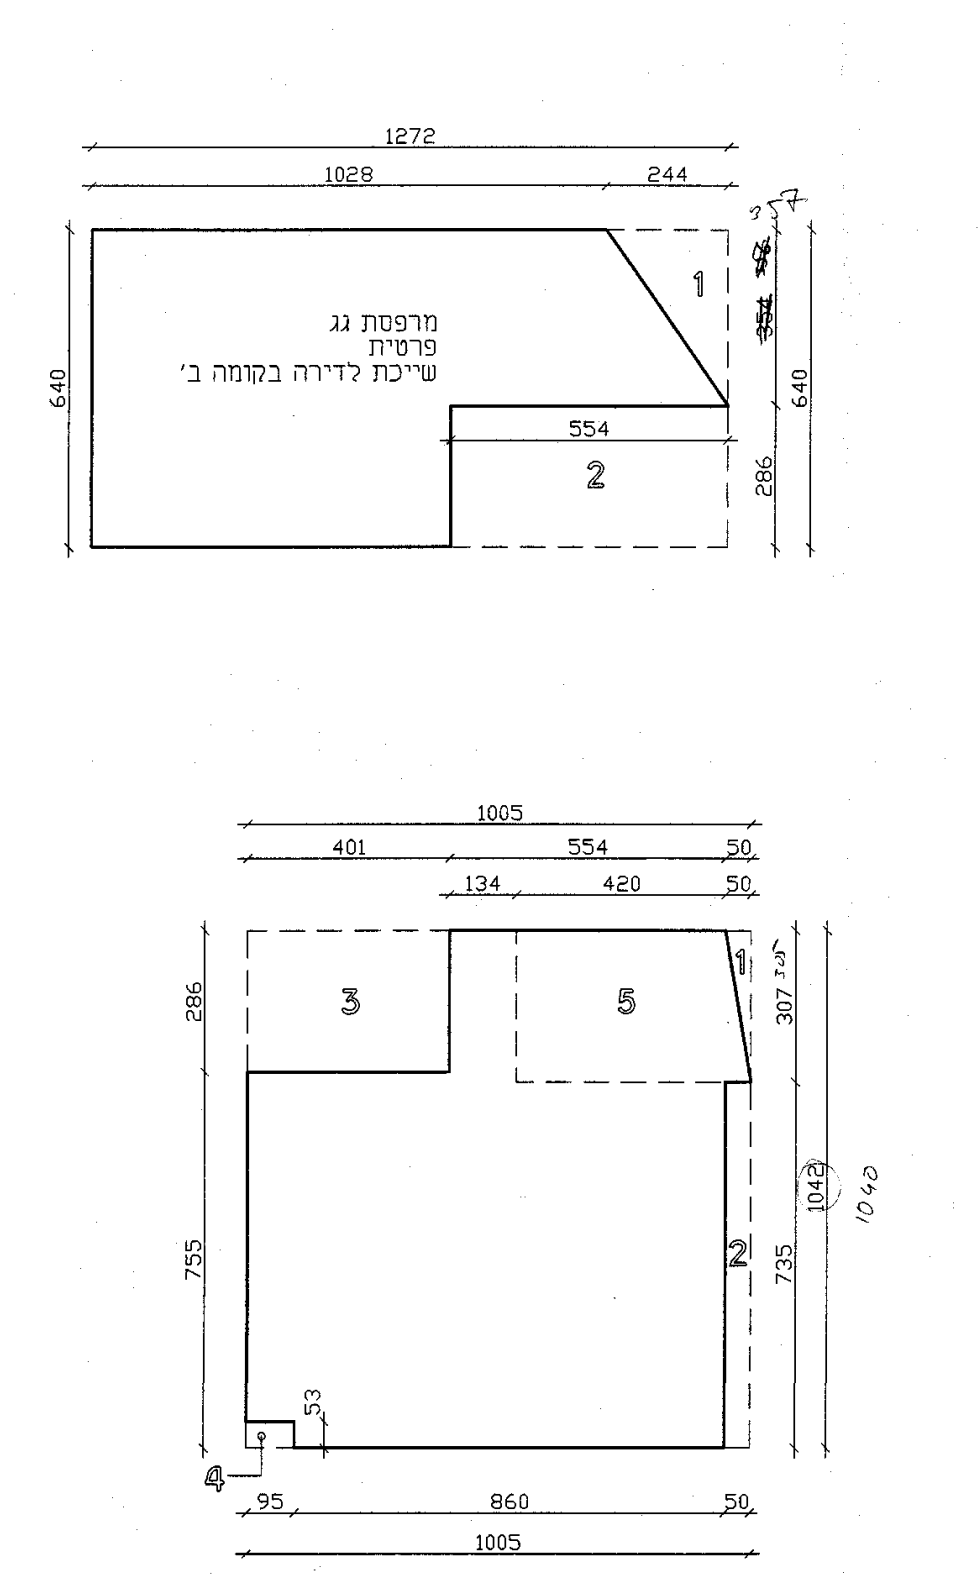
1272
1028
244
מרפסת גג
פרטית
שייכת לדירה בקומה ב'
1
2
554
640
286
1005
401
554
50
134
420
3
5
286
307
755
735
1042
95
860
1005
4

קומה ב'

שטח מסגרת : 10.05 × 10.40 = 104.72

הורדות :
1) 0.5 × 3.07/2 = 0.77
2) 0.5 × 7.35 = 3.68
3) 2.86 × 4.01 = 11.47
4) 0.95 × 0.53 = 0.50
חדר מדרגות : 5) (4.20+4.70)/2X3.07 = 13.66

סה"כ הורדות : 30.08

סה"כ שטח עיקרי : 104.72 − 30.08 = 74.64

74.48

7.93 7.91
2.29 2.27
10.8

שטח מרפסת גג ק.ב'

שטח מסגרת : 12.72 × 6.62 = 84.21

הורדות :
1) 2.44 × ~~3.53~~ 3.56/2 = 4.31
2) 5.54 × 2.87 = 15.90
3) 9.55 × 0.22 = 2.10

סה"כ שטח מרפסת : ~~61.90~~

61.9

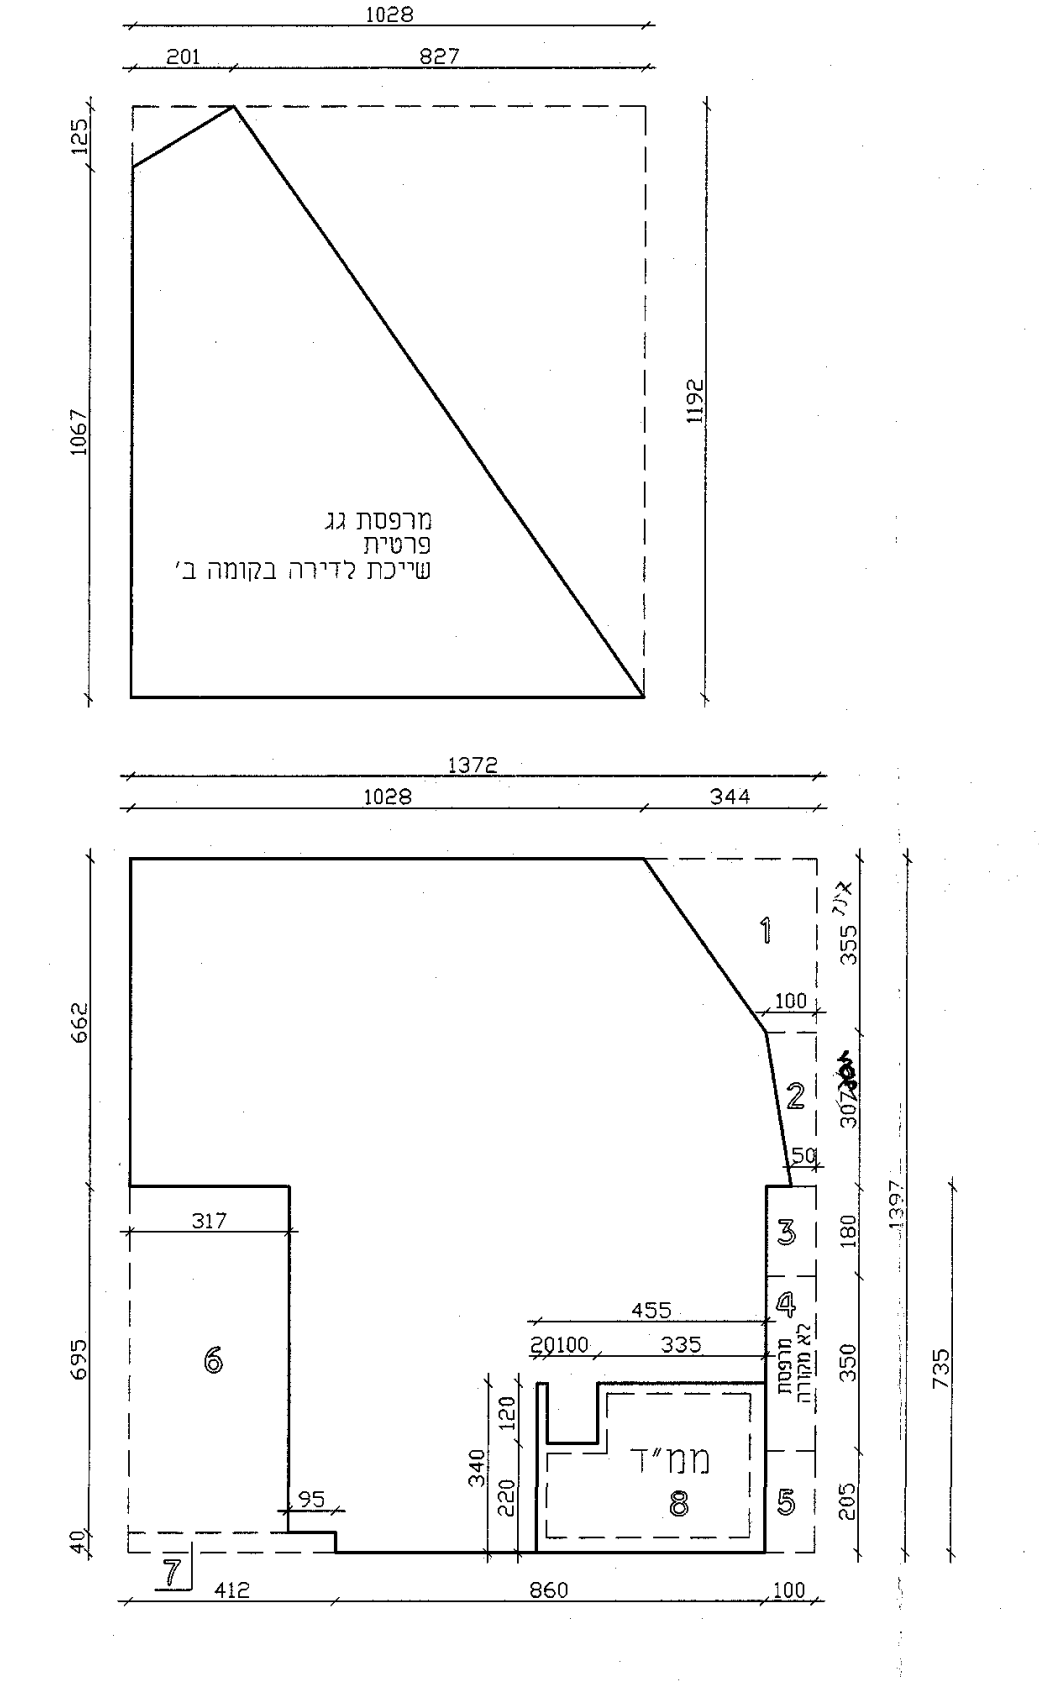
1028
1067
1192
מרפסת גג
פרטית
שייכת לדירה בקומה ב'
1372
1028
344
1
2
3
4
5
6
7
ממ"ד
8
מרפסת לא מקורה
662
695
317
455
335
412
860
100

קומה א'

שטח מסגרת : 13.72 × 13.97 = 191.67

הורדות :
1) (3.44+1.00)/2 × 3.55 = 7.88
2) (1.00+0.50)/2 × 3.07 = 2.30
3) 1.80 × 1.00 = 1.80
מרפסת לא מקורה : 4) 3.50 × 1.00 = 3.50
5) 2.05 × 1.00 = 2.05
6) 3.17 × 6.95 = 22.03
7) 0.4 × 4.12 = 1.65
שטח ממ"ד : 8) 4.55X3.40−1.20X1.00 =14.27
סה"כ שטח להורדה : 7.50

סה"כ הורדות : 48.71

סה"כ שטח עיקרי : 191.67 − 48.71 = 142.96

שטח קיים לפי היתר : 103.89
סה"כ שטח תוספת החדשה : 142.96 − 103.89 = 39.07

שטח מרפסת גג ק.א'

שטח מסגרת : 10.28 × 11.92 = 122.54

הורדות :
1) 8.27 × 11.92/2 = 49.29
2) 2.01 × 1.25/2 = 1.26

סה"כ שטח מרפסת : 71.99

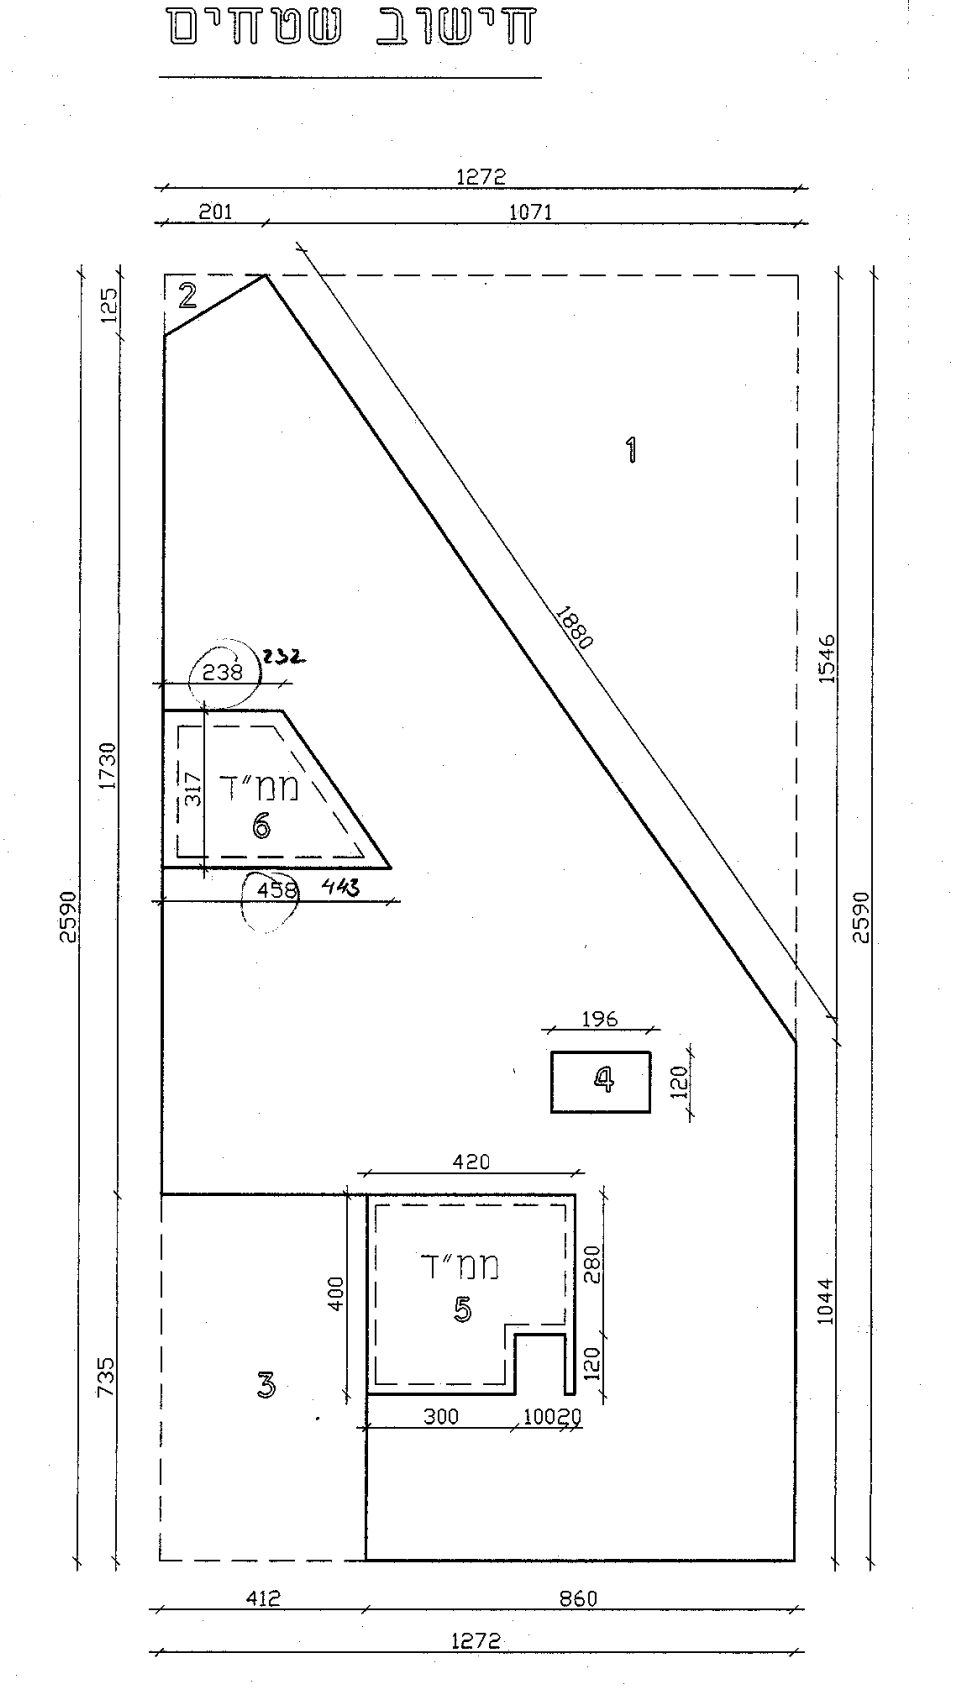
1272
201
1071
2
1
1880
1546
2590
1730
238
232
ממ"ד
6
317
458
443
196
4
120
420
ממ"ד
5
400
280
3
735
300
100
20
1044
412
860
1272

קומת קרקע

שטח מסגרת : 12.72 × 25.90 = 329.49

הורדות :
1) 10.71 × 15.46 /2 = 82.79
2) 1.25 × 2.01 /2 =1.26
3) 7.35 × 4.12 = 30.28
שטח מדרגות מתחת לגובה (H=+1.20) : 4) 1.96 × 1.20 =− 2.35
שטח ממ"ד : 5) 4.00×4.20−1.00X1.20 = 15.60
סה"כ שטח להורדה : 7.50
שטח ממ"ד : 6) (2.38+4.58)/2 × 3.17 = 11.03
סה"כ שטח להורדה : 7.50

להתאים! לפי המידות בתוכניות!

סה"כ הורדות : 131.70

סה"כ שטח עיקרי : 329.49 − 131.70 = 197.79

מפה טופוגרפית
1 : 250

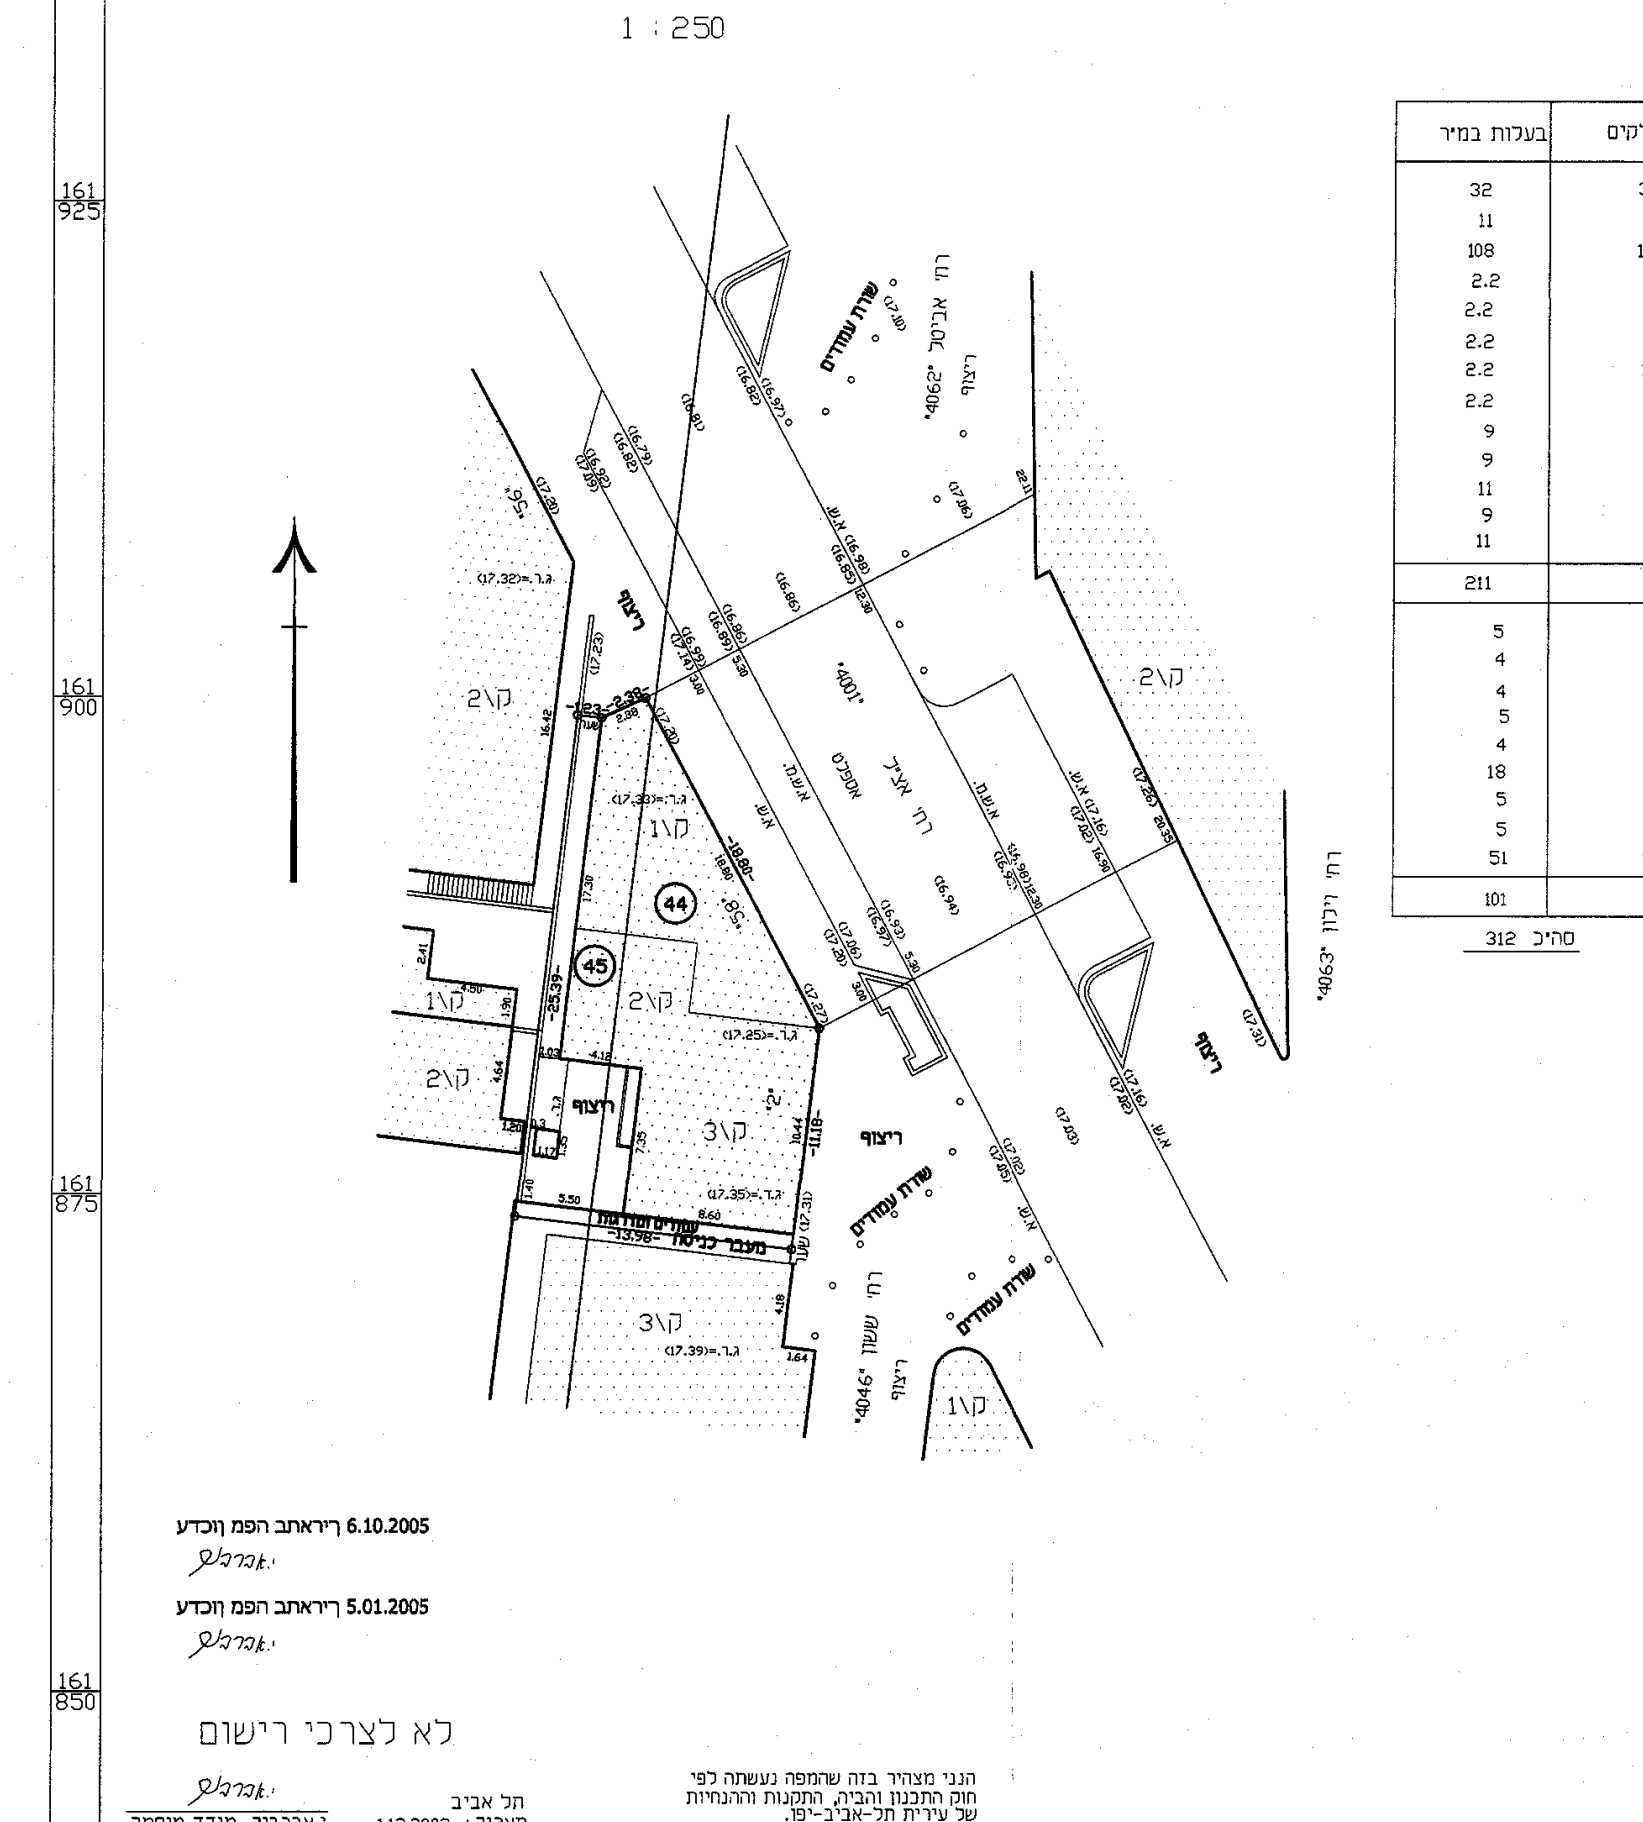
רח' אצ"ל
"4001"
"4062"
"4063"
"4046"
רח' ויזל
רח' ששון
שדרת עמודים
ריצוף
44
45
ק\1
ק\2
ק\3
161/925
161/900
161/875
161/850
130/525
130/550
130/575
130/600

עודכן ריאתבא הפמ ונכדע 6.10.2005

עודכן ריאתבא הפמ ונכדע 5.01.2005

לא לצרכי רישום

תל אביב
תאריך : 1.12.2003
י.אברבוך מודד מוסמך
רשיון מס' "461"
י. אברבוך ושותי מודדים מוסמכים בעים
רח' דיזנגוף, 190, תל-אביב טל5235891, 03-5226791

הנני מצהיר בזה שהמפה נעשתה לפי חוק התכנון והבניה, התקנות וההנחיות של עירית תל-אביב-יפו.

תל-אביב
גוש : 6135
כתובת : רח' אצ"ל 58 פינת רח' ששון 2
הוכן עבור : משפ' יצחקי
מטרת המדידה : היתר בניה
חלקות : 45,44 (חלק)

חלקה	שם הבעלים	מס' ת.ז.	שטח חלקה כולה	בעלות בחלקים	בעלות במ"ר
44	יצחקי שושנה	0481321\8	11.476.00	32\11476	32
	יצחקי זהבה	0481322\6		11\11476	11
	יצחקי נפתלי	0481318		108\11476	108
	בן אברהם יאיר	5119051		11\57380	2.2
	דייכובסקי אביגיל	478999		11\57380	2.2
	יצחקי חנה	04449625		11\57380	2.2
	בן אברהם יונתן	004790002		11\57380	2.2
	טסה נאוה	58907663		11\57380	2.2
	מדני מזל	0479542		9\11476	9
	אריאל רחל	0481317		9\11476	9
	ורון נעמי	0481319		11\11476	11
	ורון צפורה	0481320		9\11476	9
	מזרחי חרותה	0481323		11\11476	11
					211
45	בן אברהם מירים	0478998	9.821.00	5\9821	5
	מדני מזל	0479542		4\9821	4
	אריאל רחל	0481317		4\9821	4
	ירון נעמי	0481319		5\9821	5
	ירון ציפורה	0481320		4\9821	4
	יצחקי שושנה	0481321\8		18\9821	18
	יצחקי זהבה	0481322\6		5\9821	5
	מזרחי חרותה	0481323		5\9821	5
	יצחקי נפתלי	0481318		51\9821	51
					101

סה"כ 312

בעלות במ"ר : 312

שטח מדוד (מ"ר) : 286.72 (188.50+98.22)

חלקה44 188.50מ"ר
חלקה45 98.22 מ"ר

שטח מגרש משני : ______

שטח להפקעה : ______

תרשים הסביבה 1:1250

"4001"
"4062"
"4045"
"4046"
רח' אצ"ל

הערות:
1. המספרים בסוגריים מציינים גבהים.
2. הגבהים מבוססים על נ.ק. עירונית מס' 188 שגובהה 17.530 מ.'

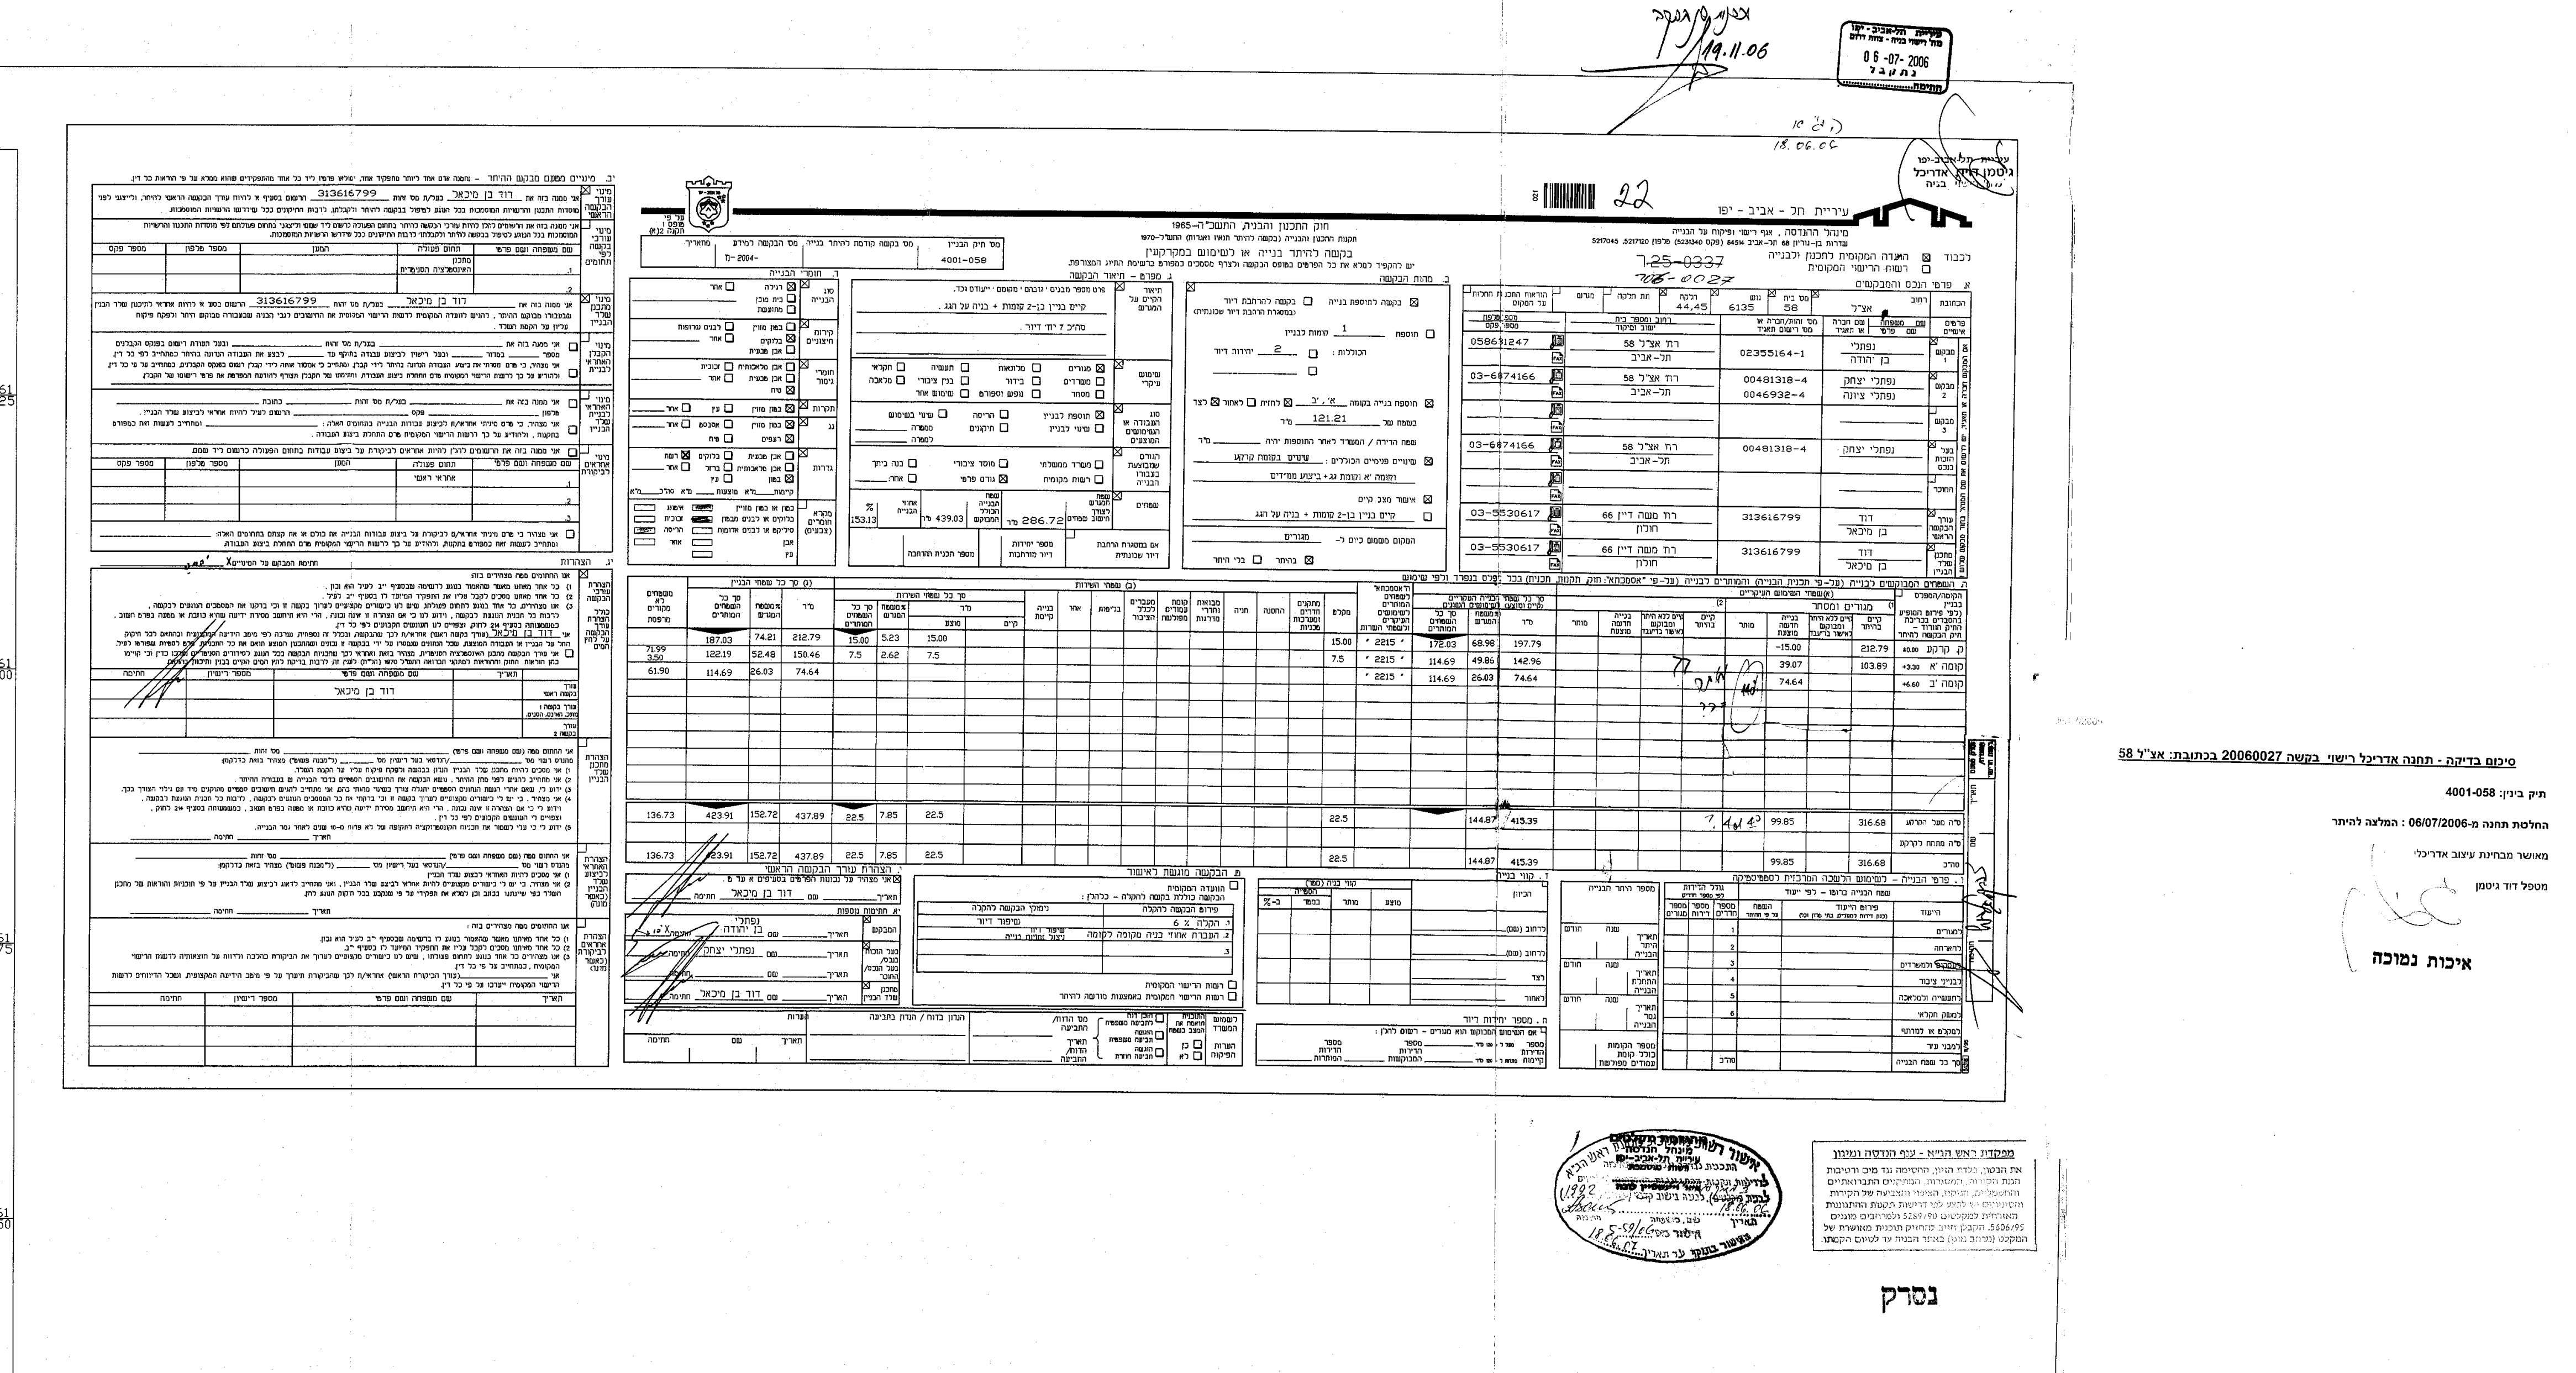

צגווע אן גנצגב 19.11.06

עיריית תל-אביב - יפו
מנהל רישוי בנייה - צוות דרום
06-07-2006
נתקבל

18.06.06

עיריית תל-אביב-יפו
גיטמן דוד אדריכל
מנהל רישוי בניה

22

עיריית תל - אביב - יפו
מינהל ההנדסה, אגף רישוי ופיקוח על הבנייה

חוק התכנון והבניה, התשכ"ה-1965
תקנות התכנון והבנייה (בקשה להיתר תנאיו ואגרות) התש"ל-1970
בקשה להיתר בנייה או לשימוש במקרקעין

לכבוד
☒ הוועדה המקומית לתכנון ולבנייה
☐ רשות הרישוי המקומית

~~7-25-0337~~
706-0027

מס' תיק הבניין: 4001-058

א. פרטי הנכס והמבקשים

הכתובת	רחוב	מס' בית	גוש	חלקה	תת חלקה	מגרש
	אצ"ל	58	6135	44,45		

	שם משפחה / שם פרטי	מס' זהות	רחוב ומספר בית / ישוב	מס' טלפון
מבקש 1	נפתלי בן יהודה	02355164-1	רח' אצ"ל 58 תל-אביב	05863124 7
מבקש 2	נפתלי יצחק נפתלי ציונה	00481318-4 0046932-4	רח' אצ"ל 58 תל-אביב	03-6874166
מבקש 3				
בעל הזכות בנכס	נפתלי יצחק	00481318-4	רח' אצ"ל 58 תל-אביב	03-6874166
מתכנן שלד הבניין	דוד בן מיכאל	313616799	רח' משה דיין 66 חולון	03-5520617
עורך הבקשה	דוד בן מיכאל	313616799	רח' משה דיין 66 חולון	03-5520617

ב. מהות הבקשה
☒ בקשה לתוספת בנייה
תוספת 1 קומות לבניין
הכוללות: 2 יחידות דיור
☒ תוספת בנייה בקומה א', ב' ☒ לצד ☒ לאחור ☐ לחזית
בשטח של 121.21 מ"ר
☒ שינויים פנימיים הכוללים : שינויים בקומת קרקע

ג. מפרט - תיאור הבקשה
קיים בניין בן-2 קומות + בניה על הגג.
סה"כ 7 יח' דיור.
שימוש עיקרי: ☒ מגורים

אני ממנה בזה את דוד בן מיכאל בעל/ת מס' זהות 313616799

ה. השטחים המבוקשים לבנייה

הקומה	קיים בהיתר	בנייה חדשה מוצעת	מ"ר	%	סך כל השטחים המותרים	מקלט
ק. קרקע ±0.00	212.79	−15.00	197.79	68.98	172.03	15.00
קומה א' +3.30	103.89	39.07	142.96	49.86	114.69	7.5
קומה ב' +6.60		74.64	74.64	26.03	114.69	
סה"כ מעל הקרקע	316.68	99.85	415.39	144.87		22.5
סה"כ	316.68	99.85	415.39	144.87		22.5

ט. הבקשה מוגשת לאישור
1. הקלה 6 % — שיפור דיור
2. העברת אחוזי בניה מקומה לקומה — שיפור דיור ניצול זכויות בנייה

מפקדת ראש הג"א - ענף הנדסה ומיגון

אשור רשות ההתגוננות האזרחית
מינהל הנדסה
עיריית תל-אביב-יפו
18.06.06

נסרק

סיכום בדיקה - תחנה אדריכל רישוי בקשה 20060027 בכתובת: אצ"ל 58

תיק בינין: 4001-058

החלטת תחנה מ-06/07/2006 : המלצה להיתר

מאושר מבחינת עיצוב אדריכלי

מטפל דוד גיטמן

איכות נמוכה

חלון בלי כיס

זיון סביב פתח בקיר

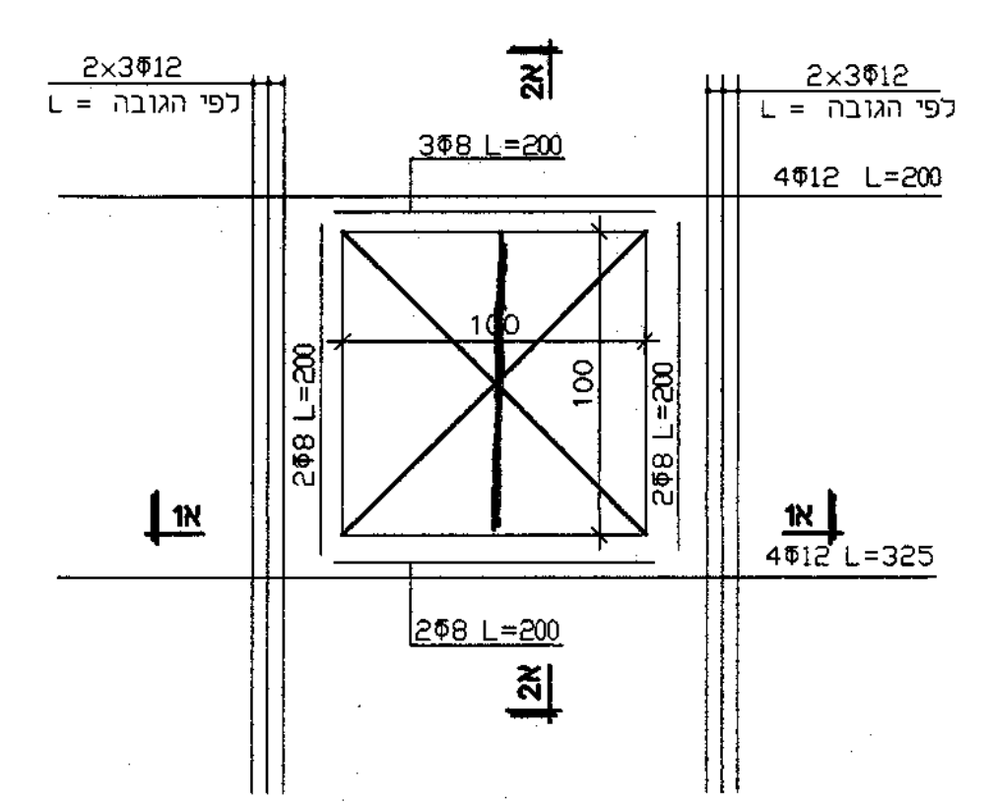

2×3Φ12
לפי הגובה = L
3Φ8 L=200
4Φ12 L=200
100
100
2Φ8 L=200
4Φ12 L=325
א1
א2

① חתך אופקי בקיר מרחב מוגן

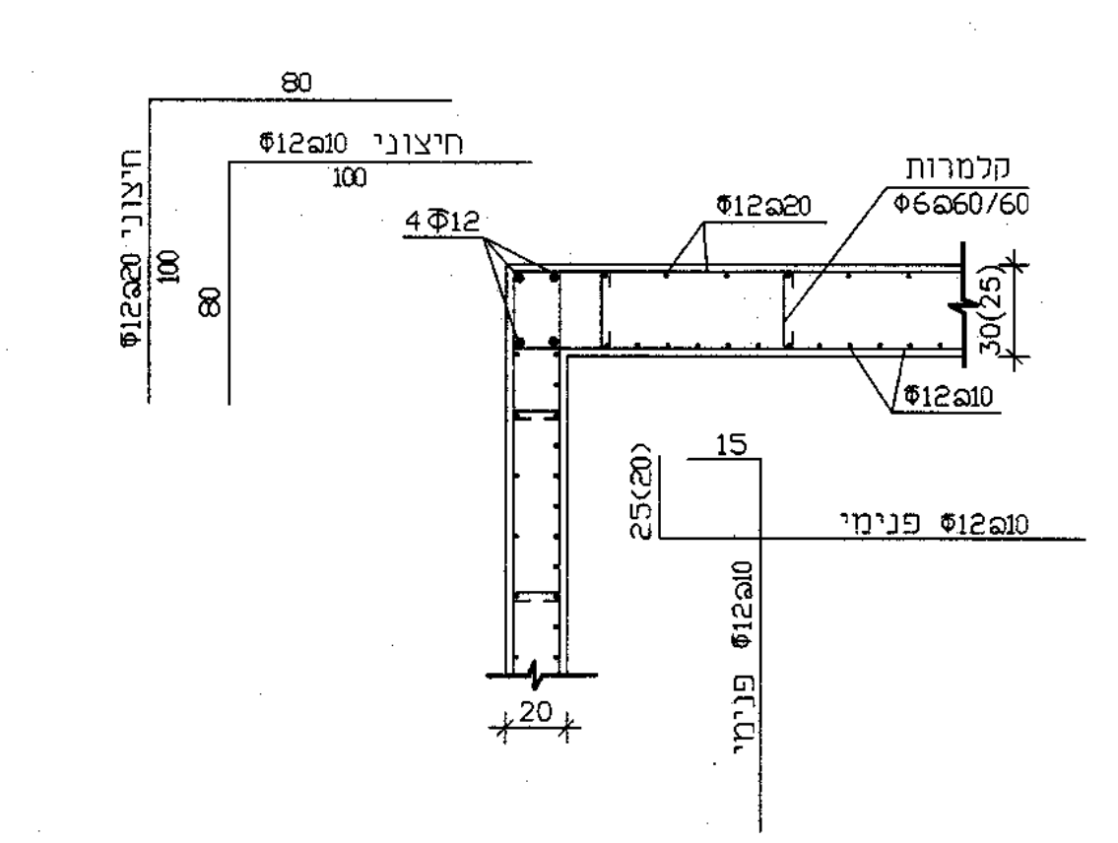

80
Φ12a10 חיצוני
100
Φ12a10 חיצוני
4Φ12
Φ12a20
קלמרות
Φ6a60/60
30(25)
Φ12a10
15
25(20)
Φ12a10 פנימי
פנימי
20

חלון עם כיס

זיון סביב פתח בקיר

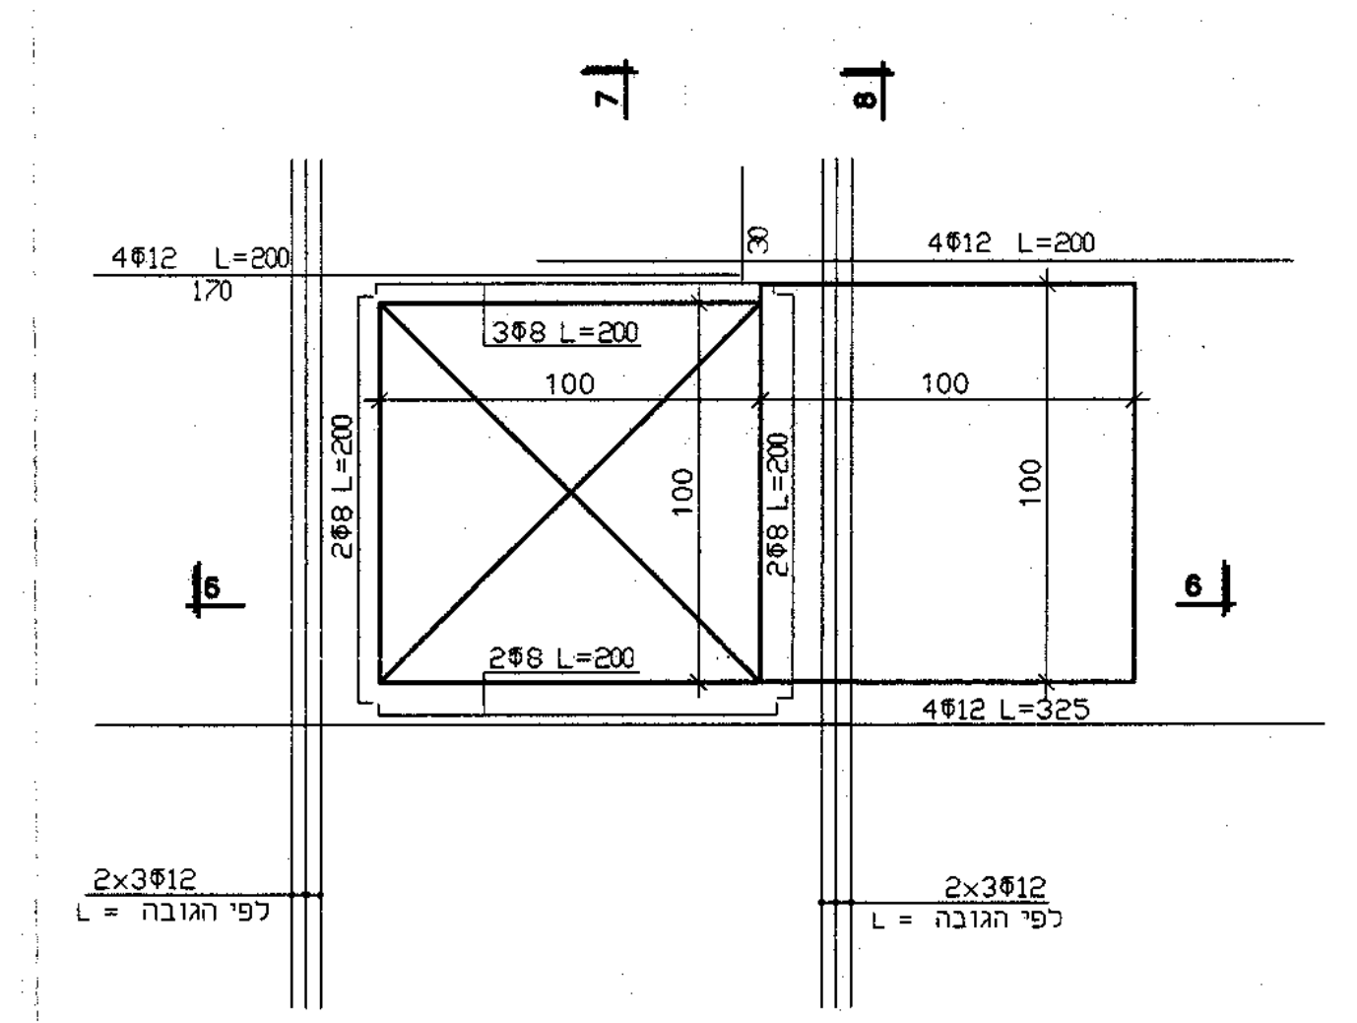

4Φ12 L=200
170
3Φ8 L=200
100
100
4Φ12 L=200
2Φ8 L=200
2Φ8 L=200
4Φ12 L=325
2×3Φ12
לפי הגובה = L
6
7
8

דלת

זיון סביב פתח בקיר

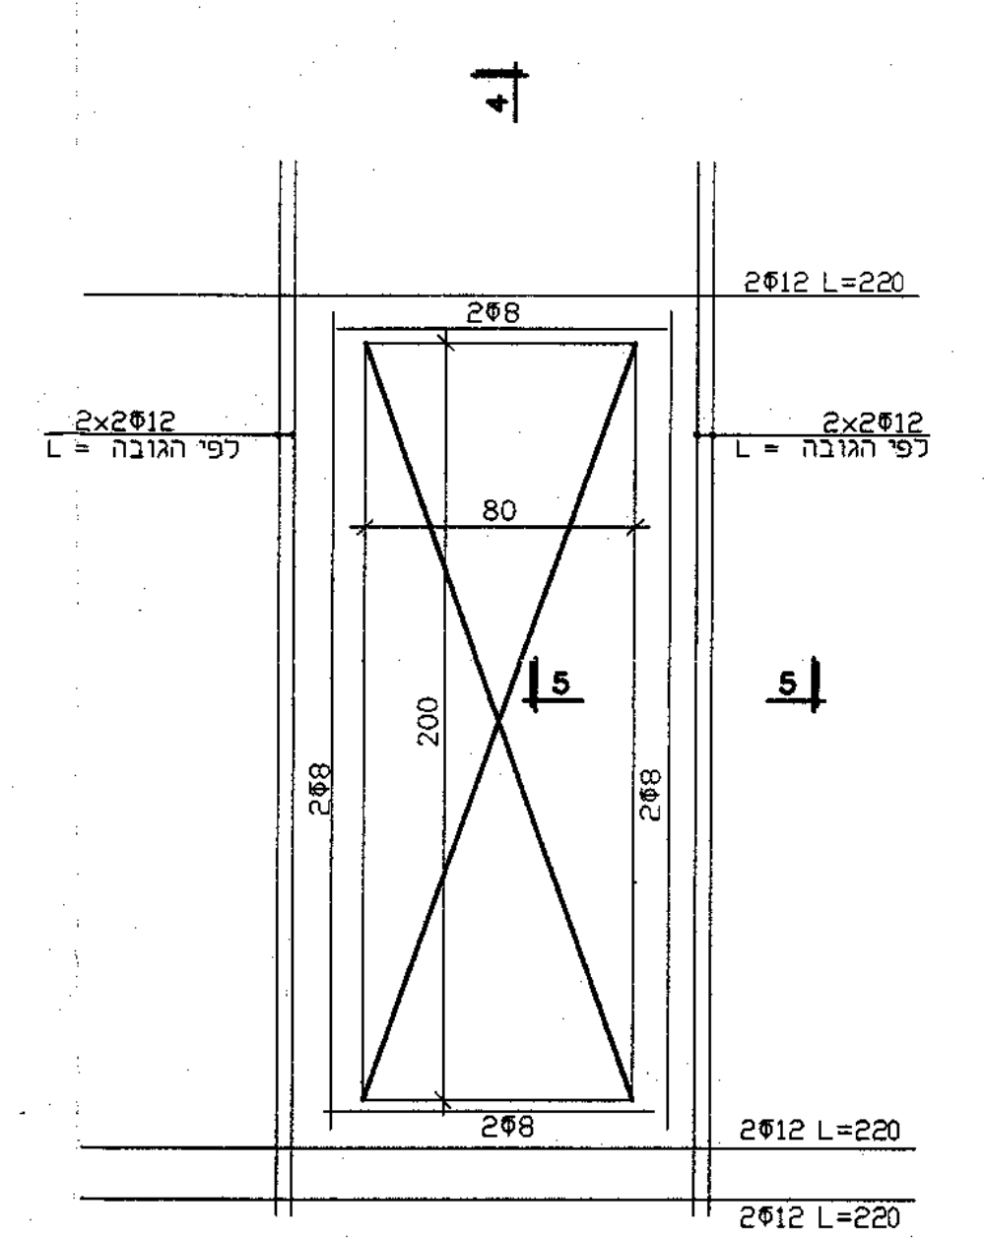

2Φ12 L=220
2Φ8
2×2Φ12
לפי הגובה = L
80
200
2Φ8
5
4

חתך 4-4

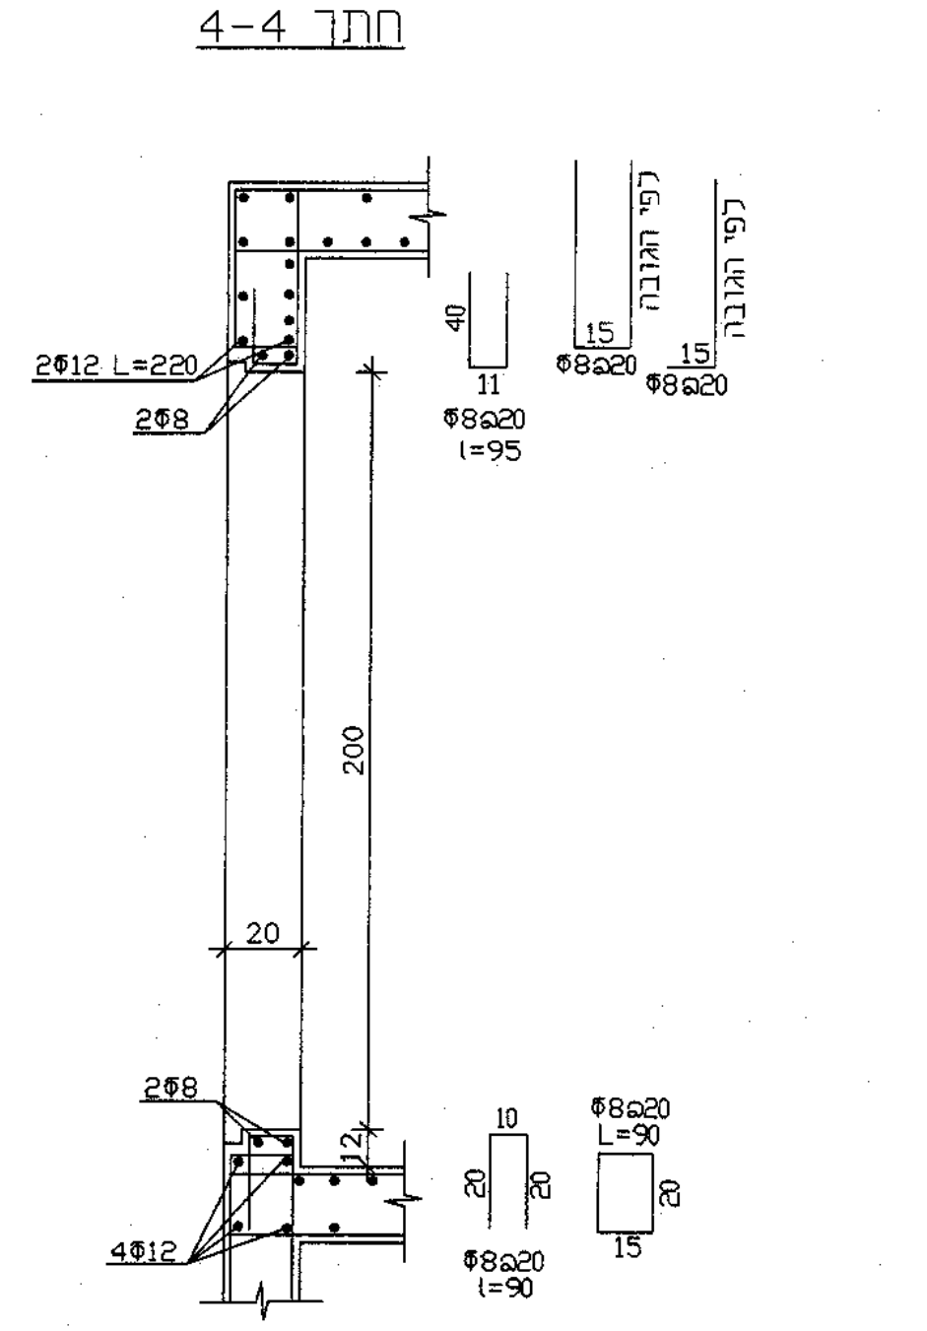

2Φ12 L=220
2Φ8
200
20
4Φ12
Φ8a20
l=95
Φ8a20
לפי הגובה
Φ8a20
l=90

חתך א1-א1

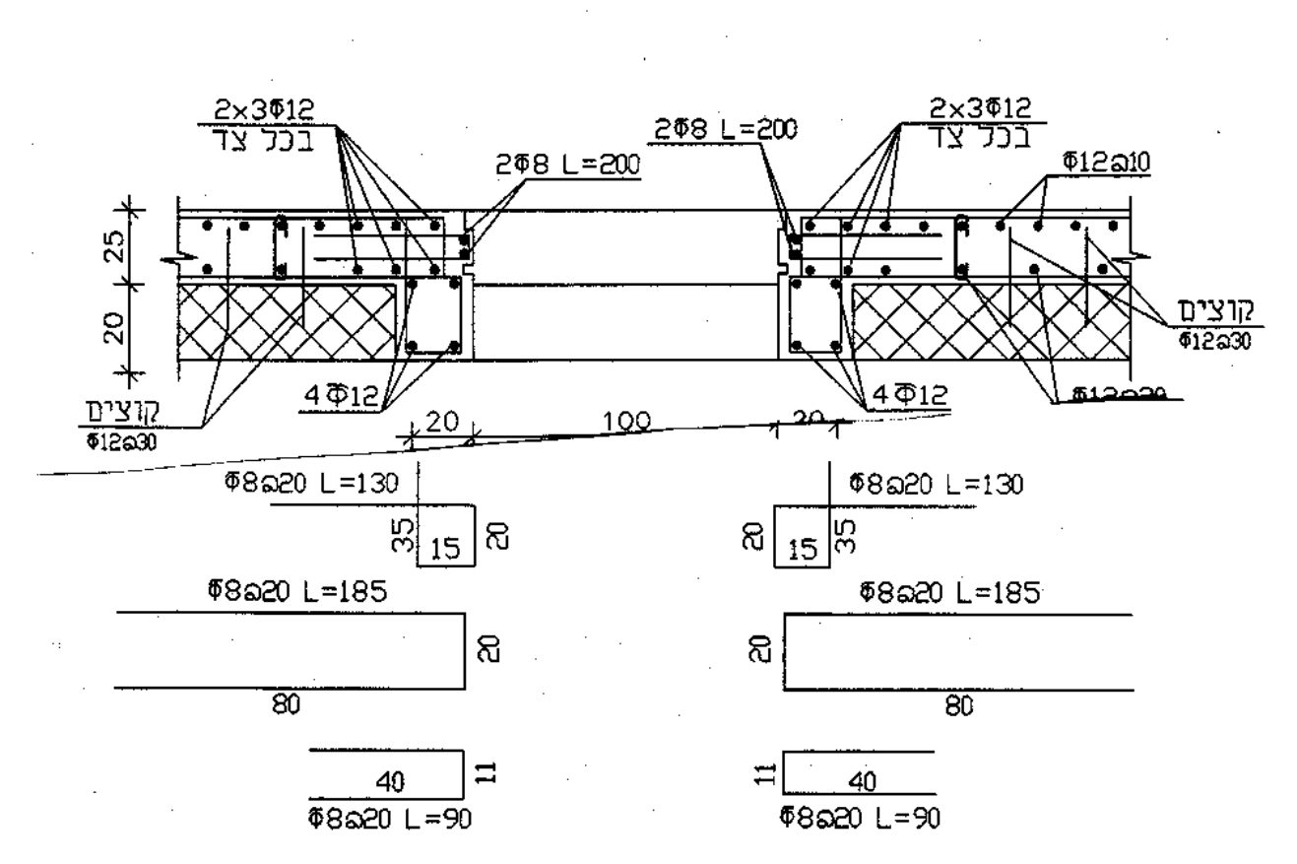

2×3Φ12
בכל צד
2Φ8 L=200
Φ12a10
קוצים
Φ12a30
4Φ12
100
Φ8a20 L=130
Φ8a20 L=185
80
Φ8a20 L=90

② פרט ריתום אנכי בין רצפה לקירות

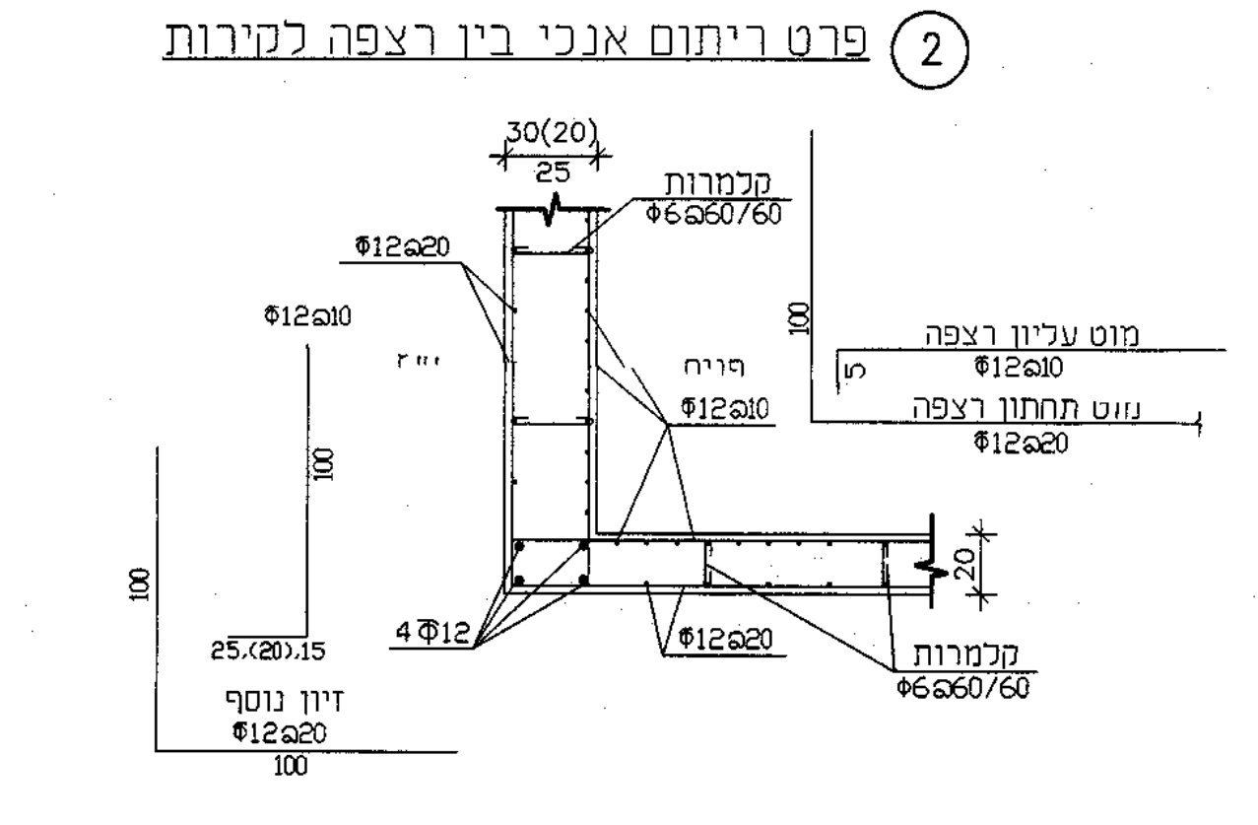

30(20)
25
קלמרות
Φ6a60/60
Φ12a20
Φ12a10
מוט עליון רצפה
Φ12a10
מוט תחתון רצפה
Φ12a20
4Φ12
זיון נוסף
Φ12a20
100
25.(20).15

חתך 6-6

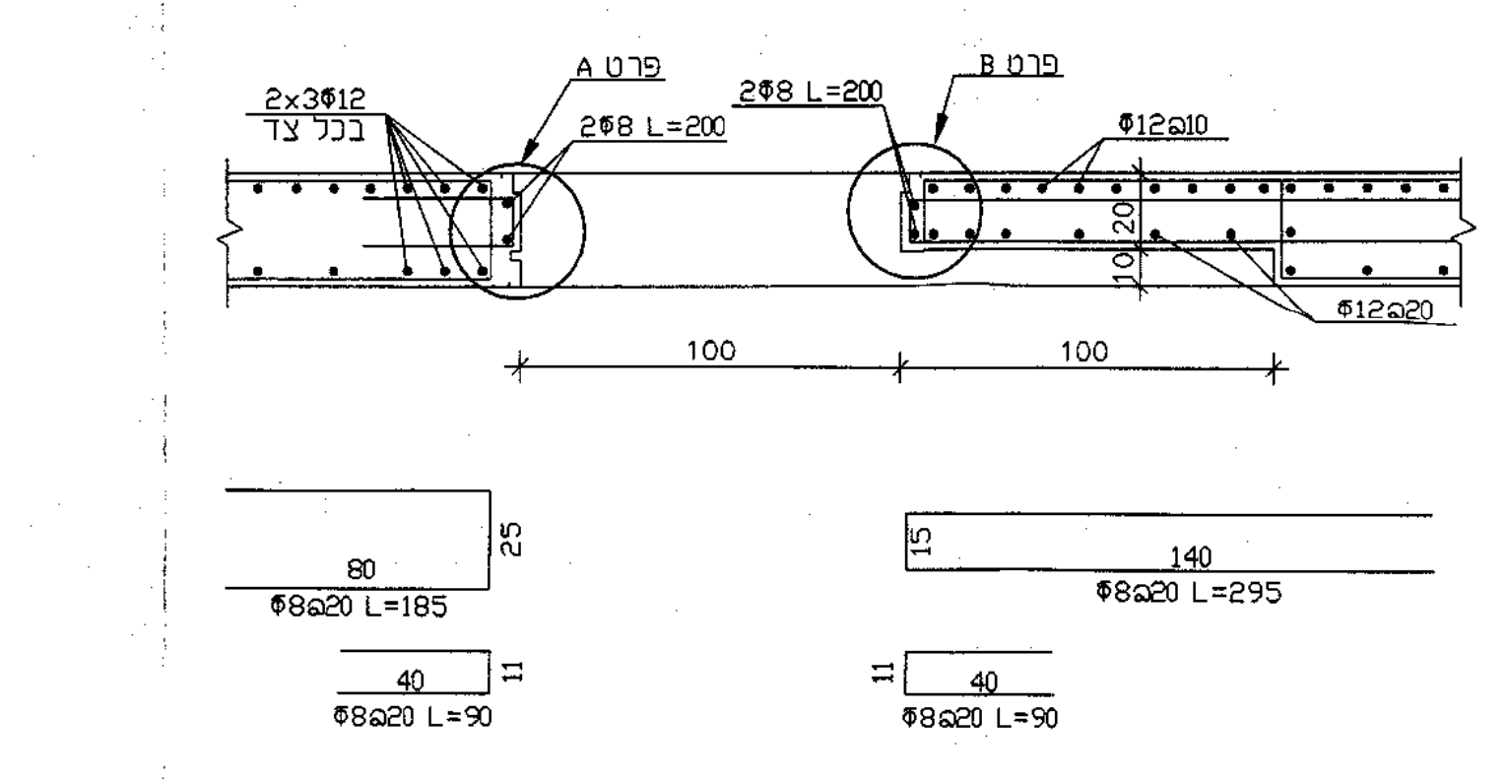

2×3Φ12
בכל צד
פרט A
2Φ8 L=200
פרט B
Φ12a10
Φ12a20
100
100
80
Φ8a20 L=185
140
Φ8a20 L=295
Φ8a20 L=90

חתך 5-5

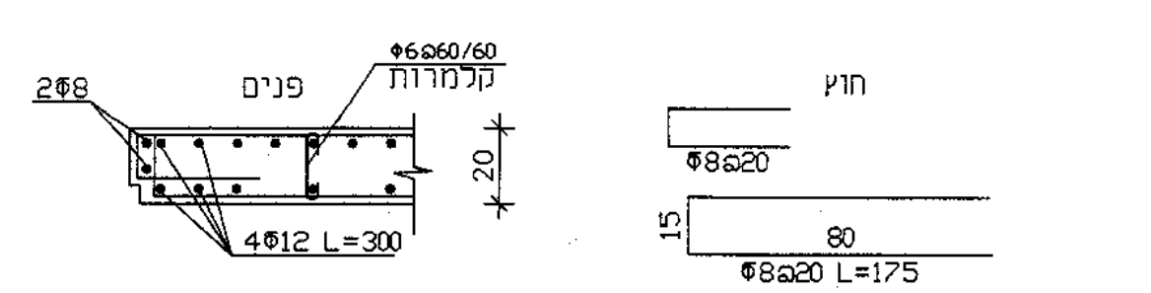

2Φ8
פנים
Φ6a60/60
קלמרות
4Φ12 L=300
חוץ
Φ8a20
80
Φ8a20 L=175

חתך א2-א2

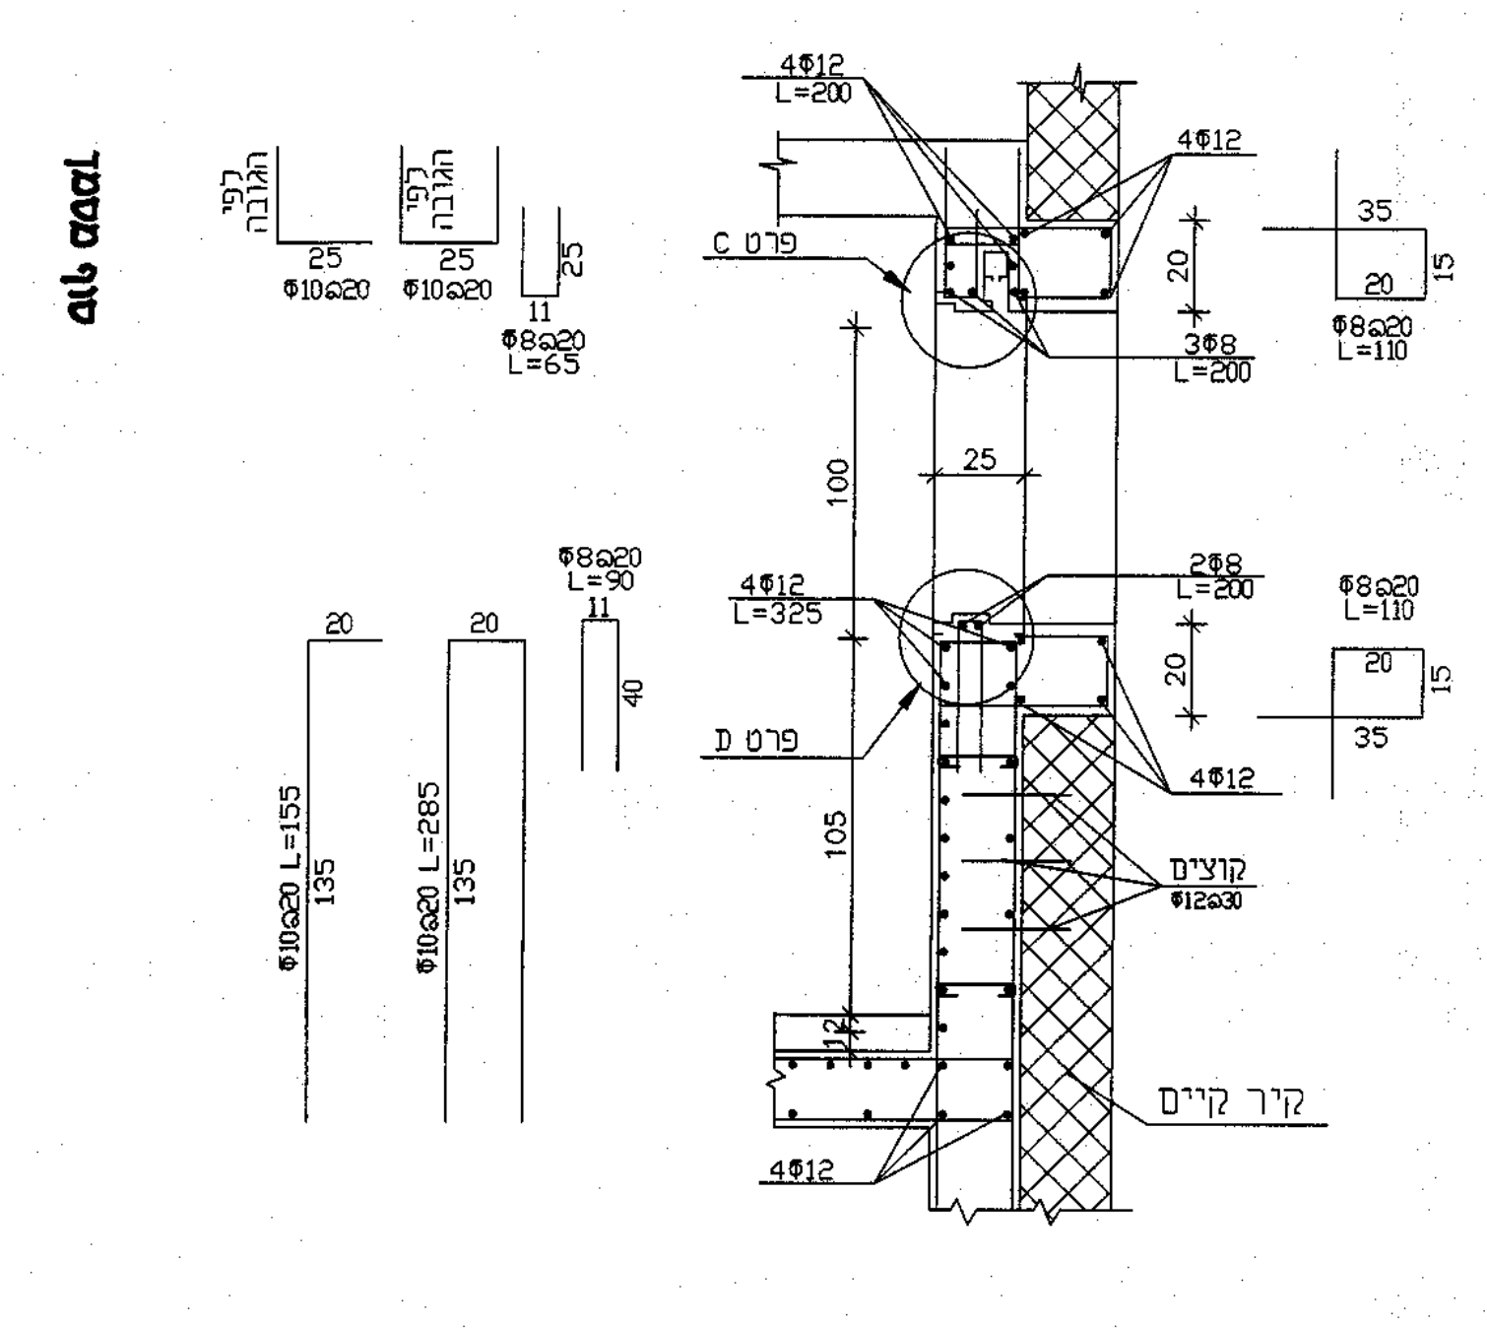

4Φ12
L=200
פרט C
3Φ8
L=200
4Φ12
L=325
פרט D
2Φ8
L=200
קוצים
Φ12a30
קיר קיים
Φ10a20 L=155
Φ10a20 L=285
Φ8a20 L=65
Φ8a20 L=110

③ פרט ריתום אנכי בין קיר לגג

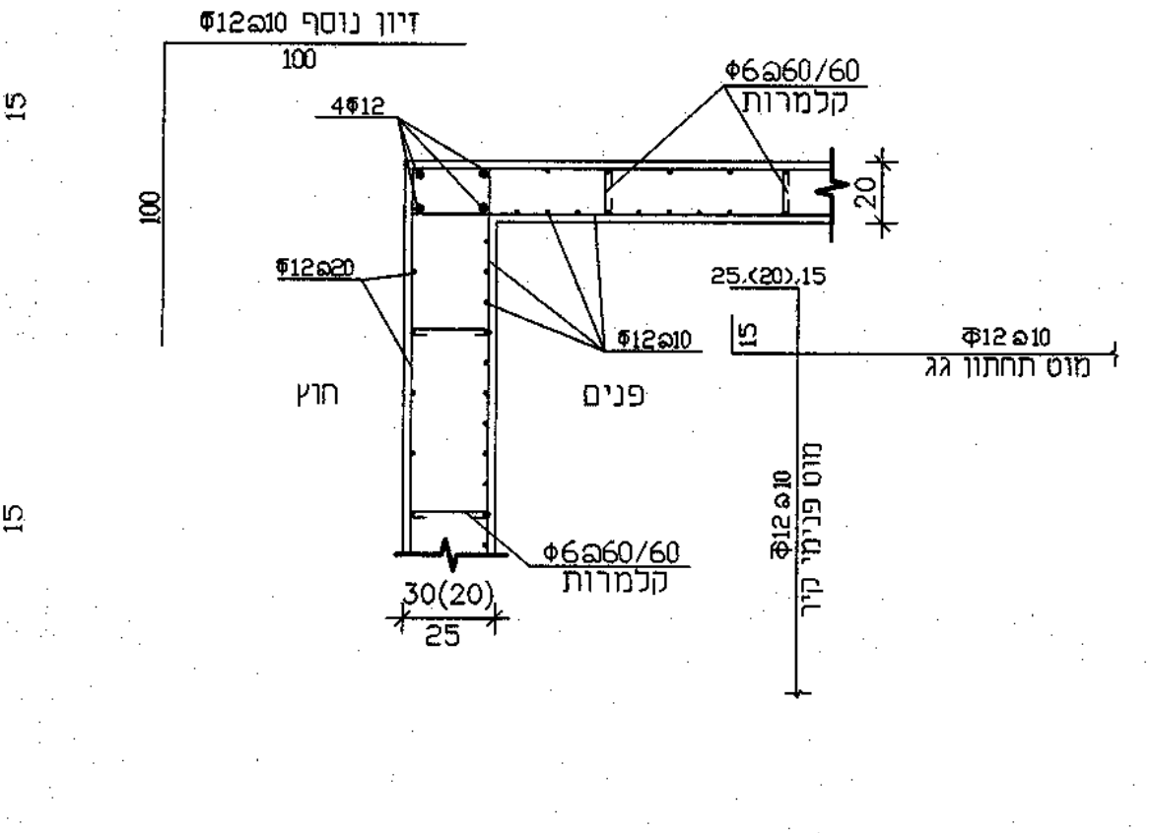

זיון נוסף Φ12a10
4Φ12
Φ6a60/60
קלמרות
Φ12a20
Φ12a10
חוץ
פנים
מוט תחתון גג
מוט פנימי קיר
30(20)
25

חתך 8-8

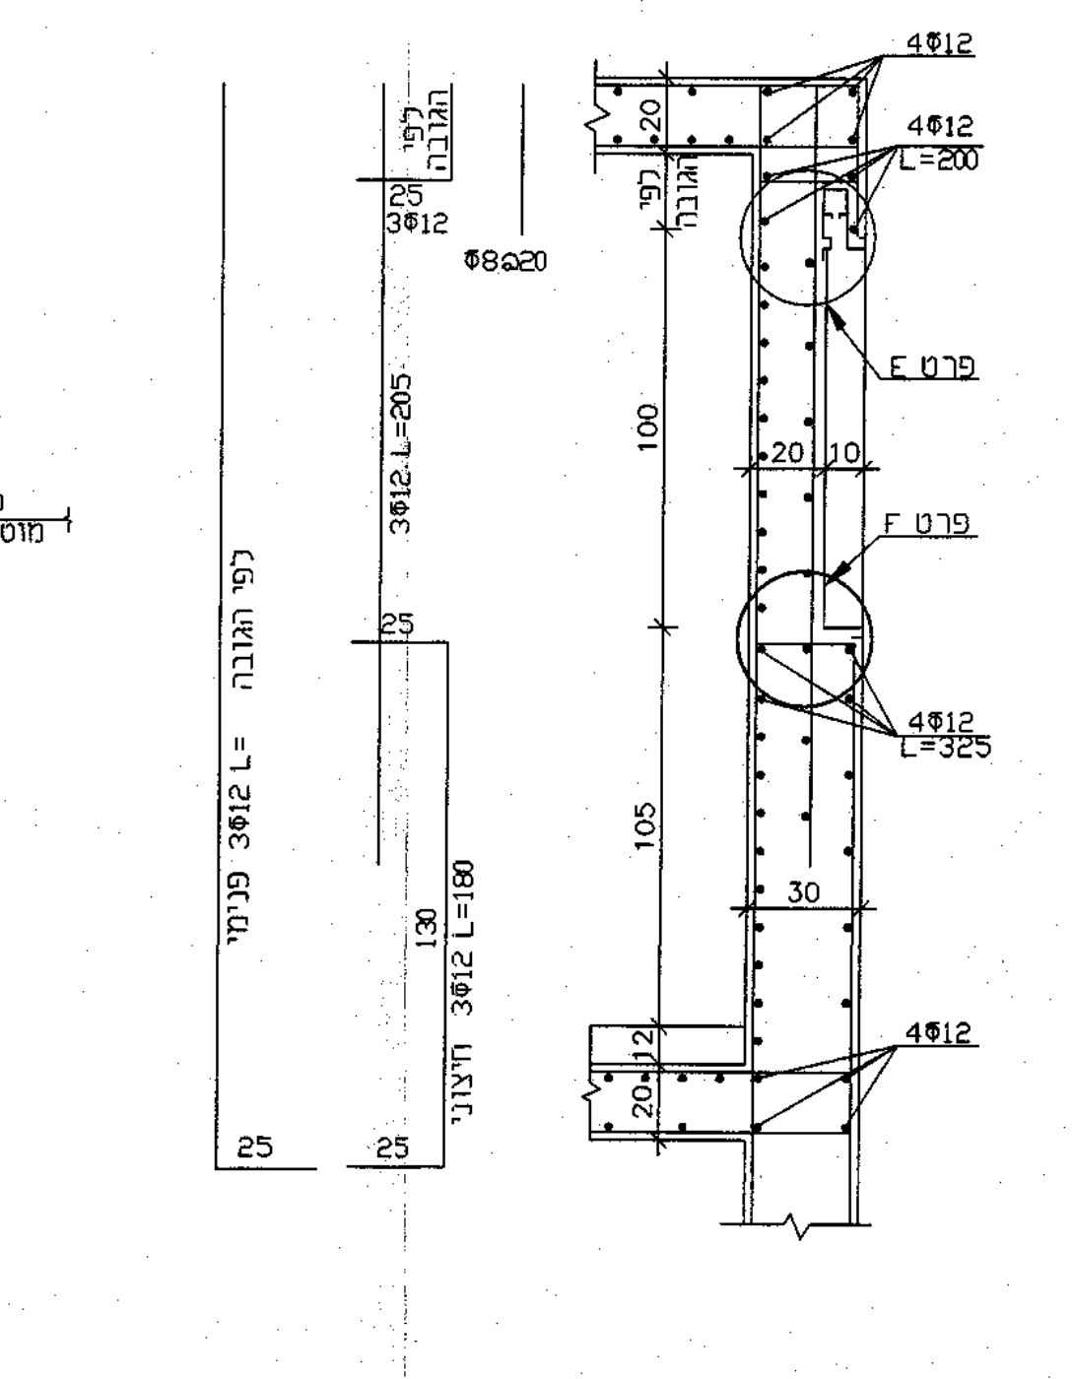

4Φ12
L=200
פרט E
פרט F
4Φ12
L=325
3Φ12 L=205
3Φ12 L=180
לפי הגובה
100
105

חתך 7-7

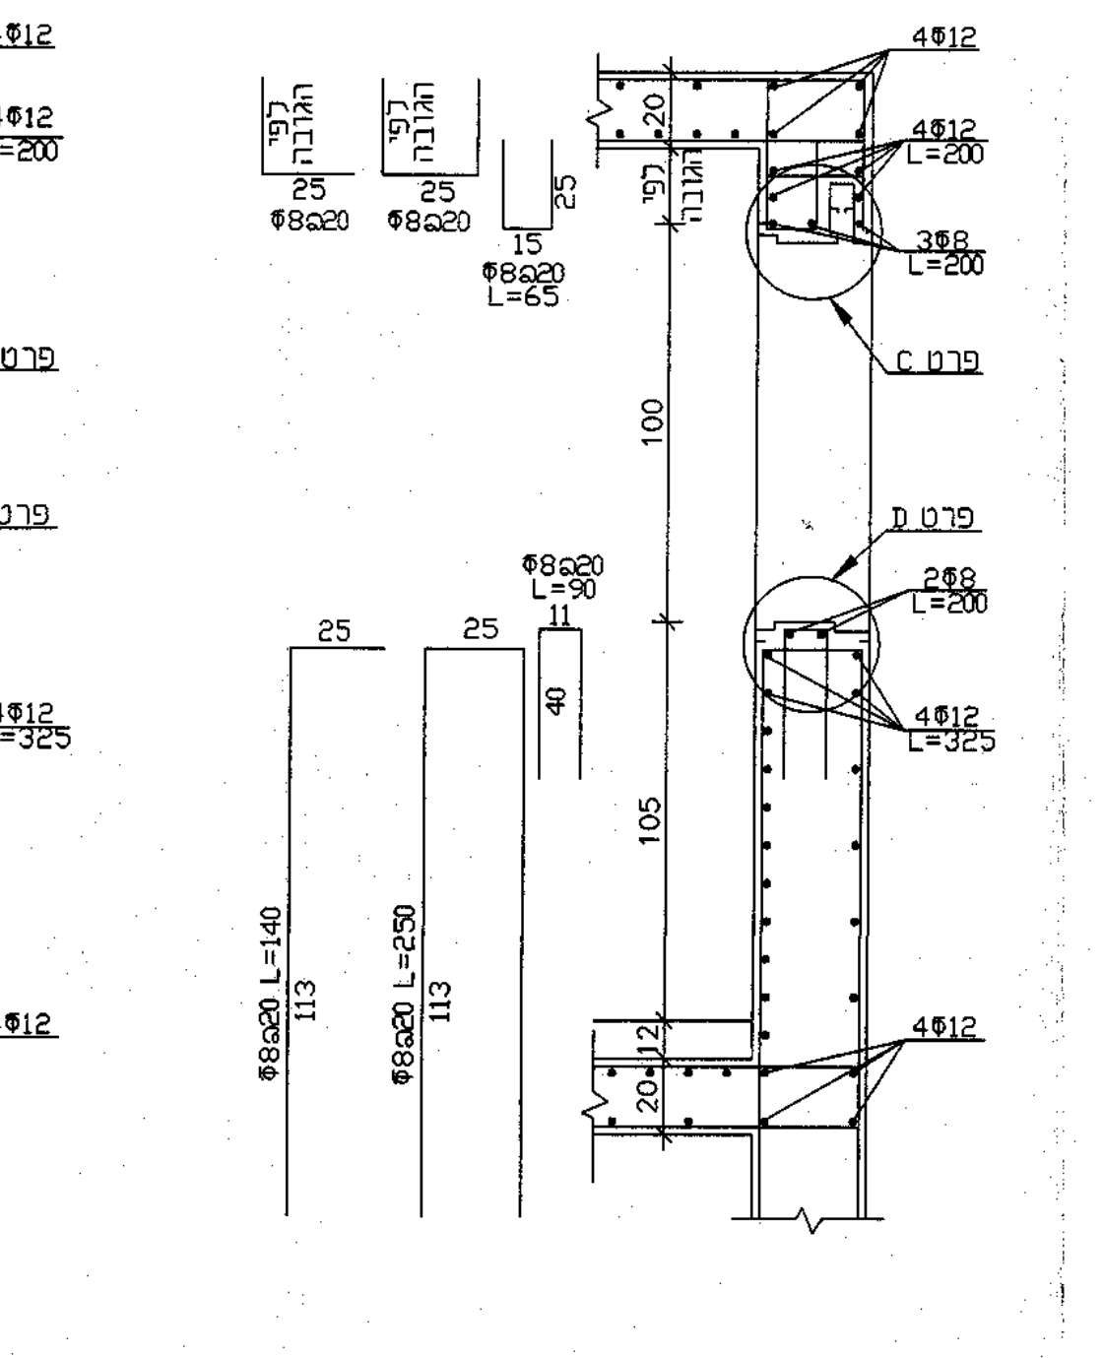

4Φ12
L=200
3Φ8
L=200
פרט C
פרט D
2Φ8
L=200
4Φ12
L=325
Φ8a20 L=140
Φ8a20 L=250
Φ8a20
L=90

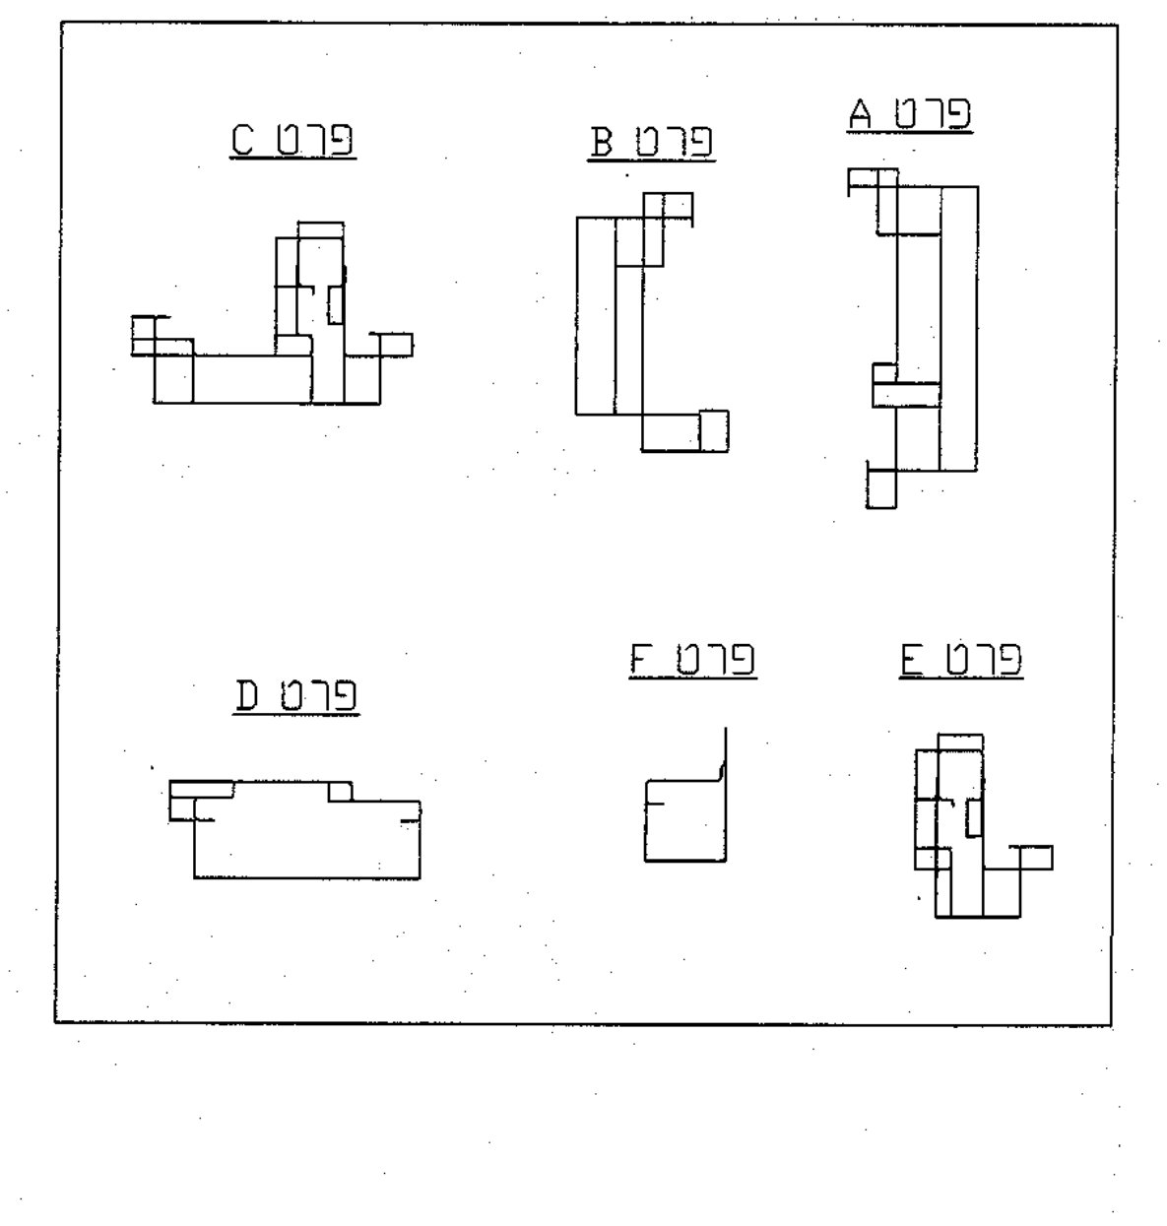

פרט C
פרט B
פרט A
פרט D
פרט F
פרט E

חתך 2-2

1:50

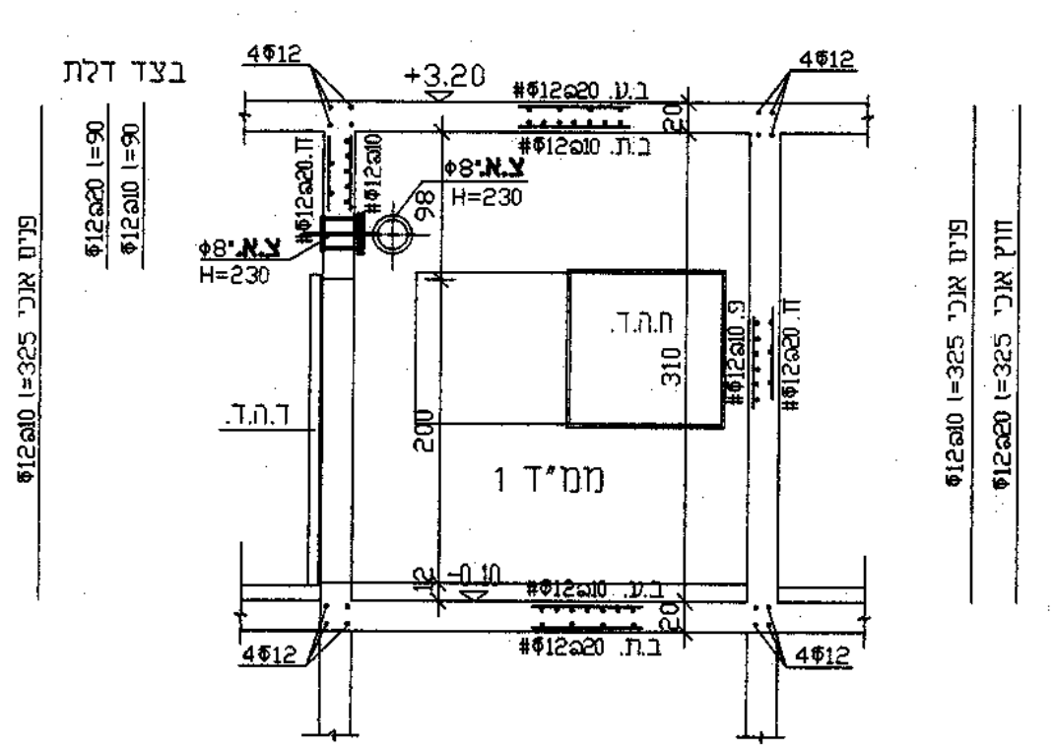

בצד דלת
+3.20
4Φ12
ממ"ד 1
ד.ה.ד.
ח.ה.ד.
-0.10
חוץ אנכי Φ12a20 l=325
פנים אנכי Φ12a10 l=325

חתך 1-1

1:50

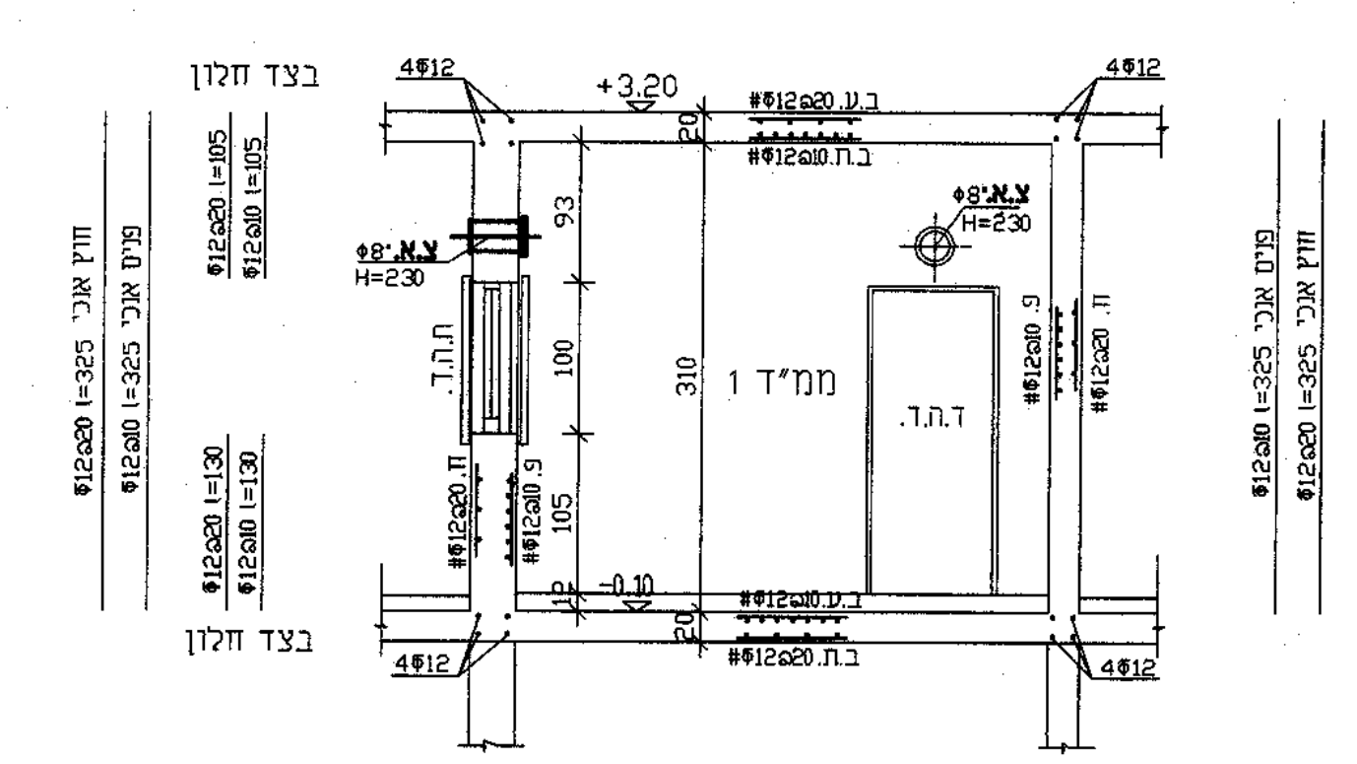

בצד חלון
+3.20
4Φ12
ממ"ד 1
ח.ה.ד.
ד.ה.ד.
-0.10

חתך 4-4

1:50

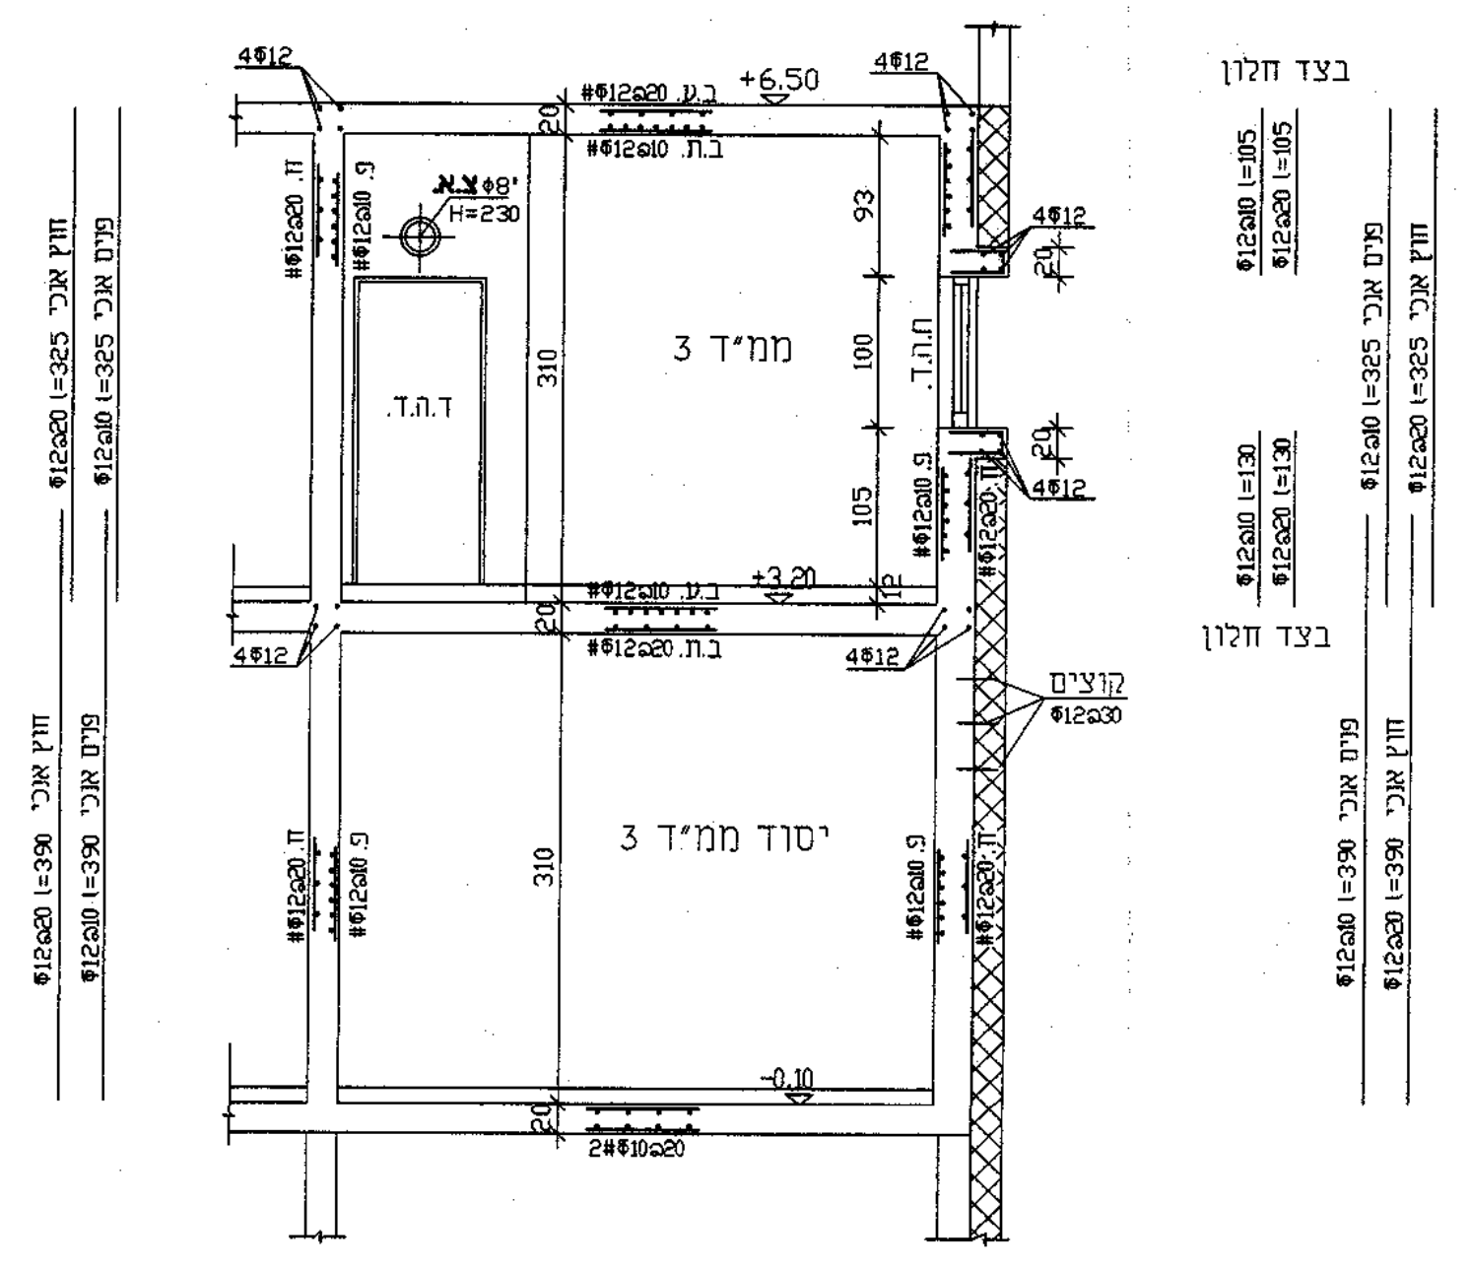

+6.50
+3.20
ממ"ד 3
יסוד ממ"ד 3
ד.ה.ד.
ח.ה.ד.
קוצים
Φ12a30
בצד חלון
-0.10

חתך 3-3

1:50

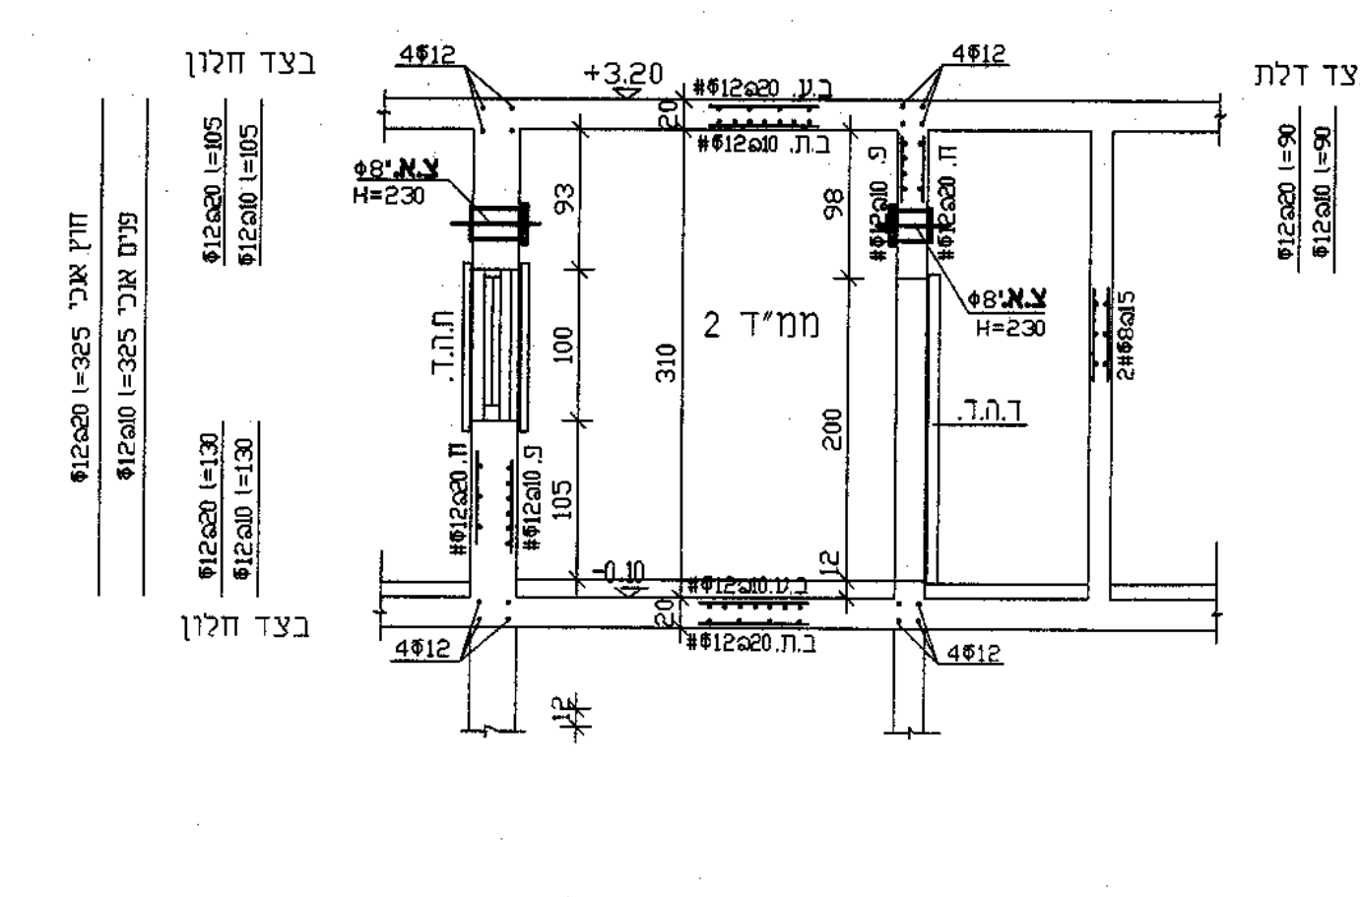

בצד חלון
בצד דלת
+3.20
ממ"ד 2
ח.ה.ד.
ד.ה.ד.
-0.10

חתך 5-5

1:50

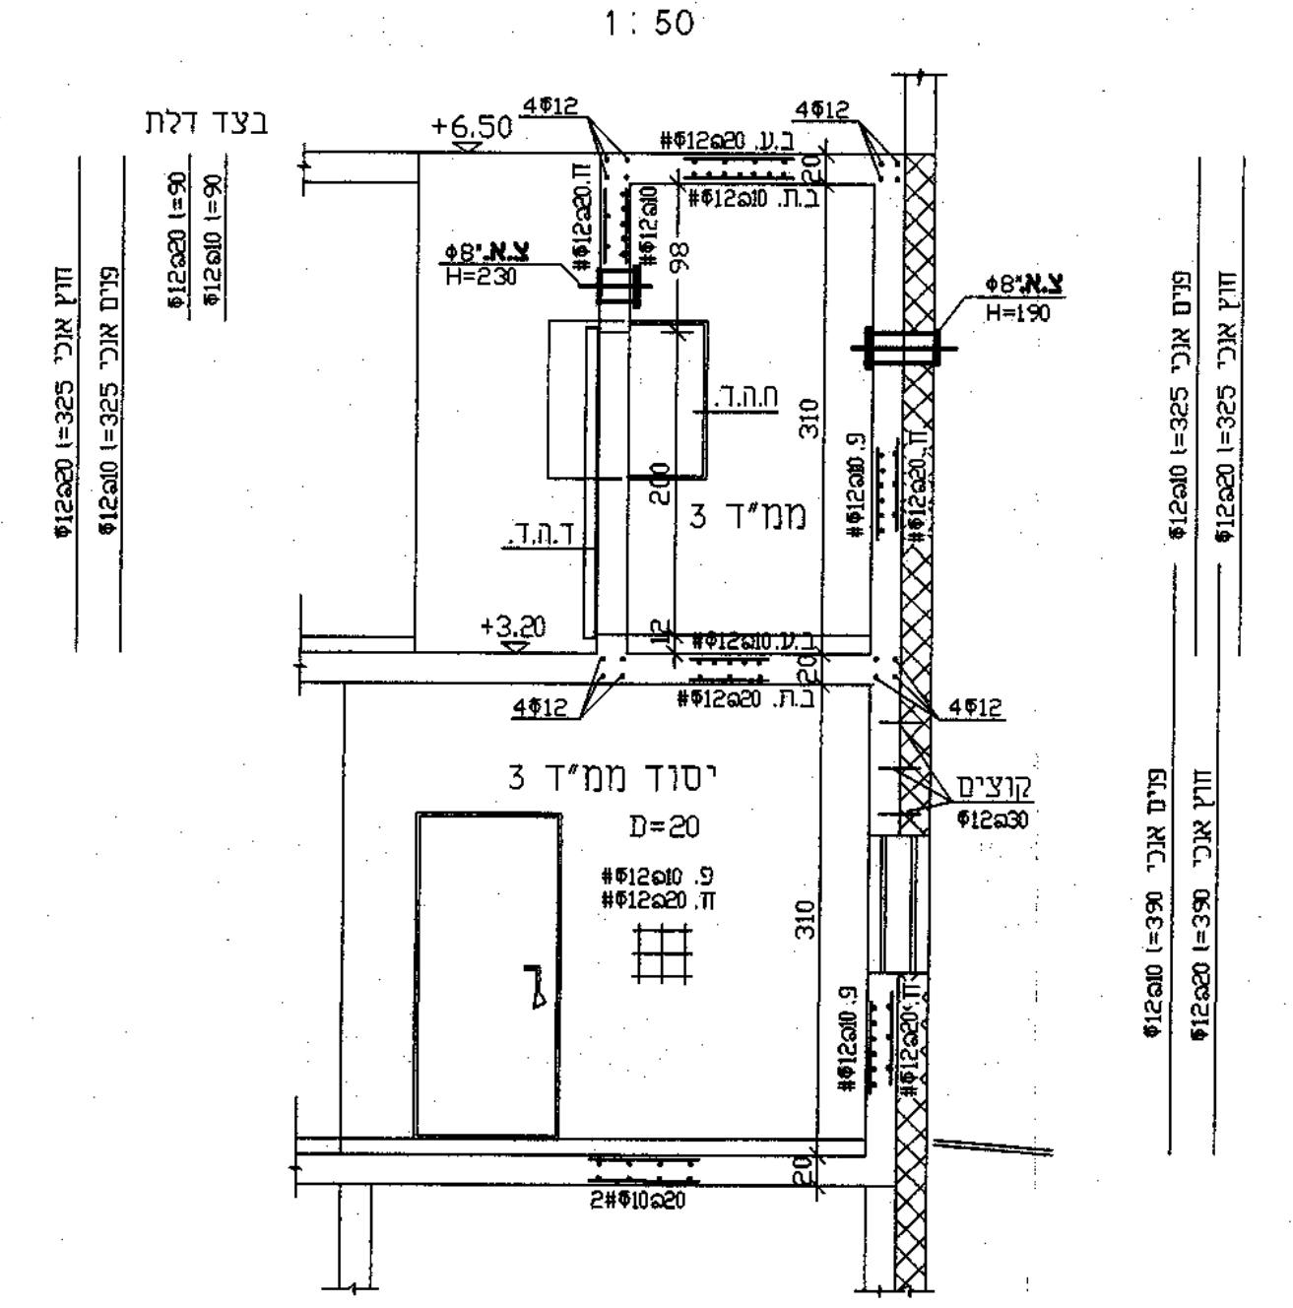

בצד דלת
+6.50
+3.20
ממ"ד 3
יסוד ממ"ד 3
D=20
קוצים
Φ12a30
2#Φ10a20

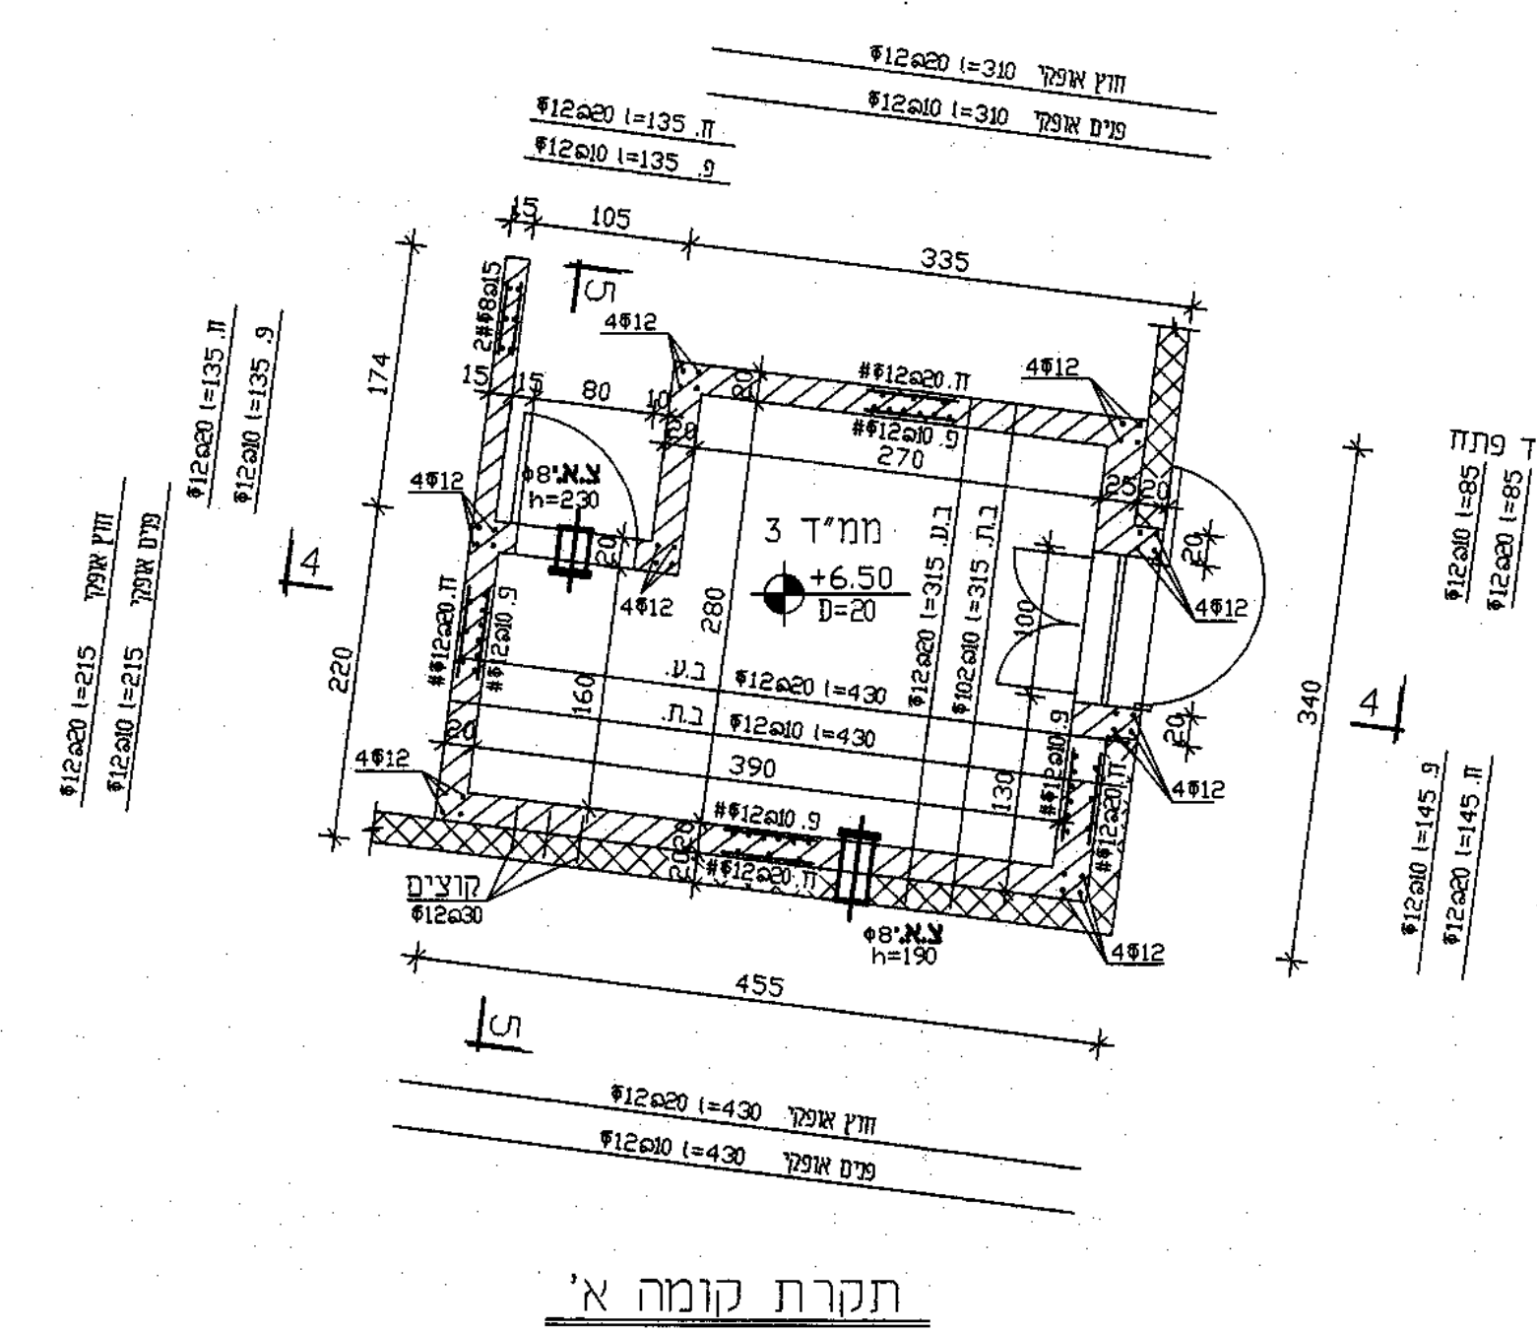

ממ"ד 3
+6.50
D=20
בצד פתח
455
390
335
קוצים
Φ12a30

תקרת קומה א'
(רצפת קומה ב')
1:50

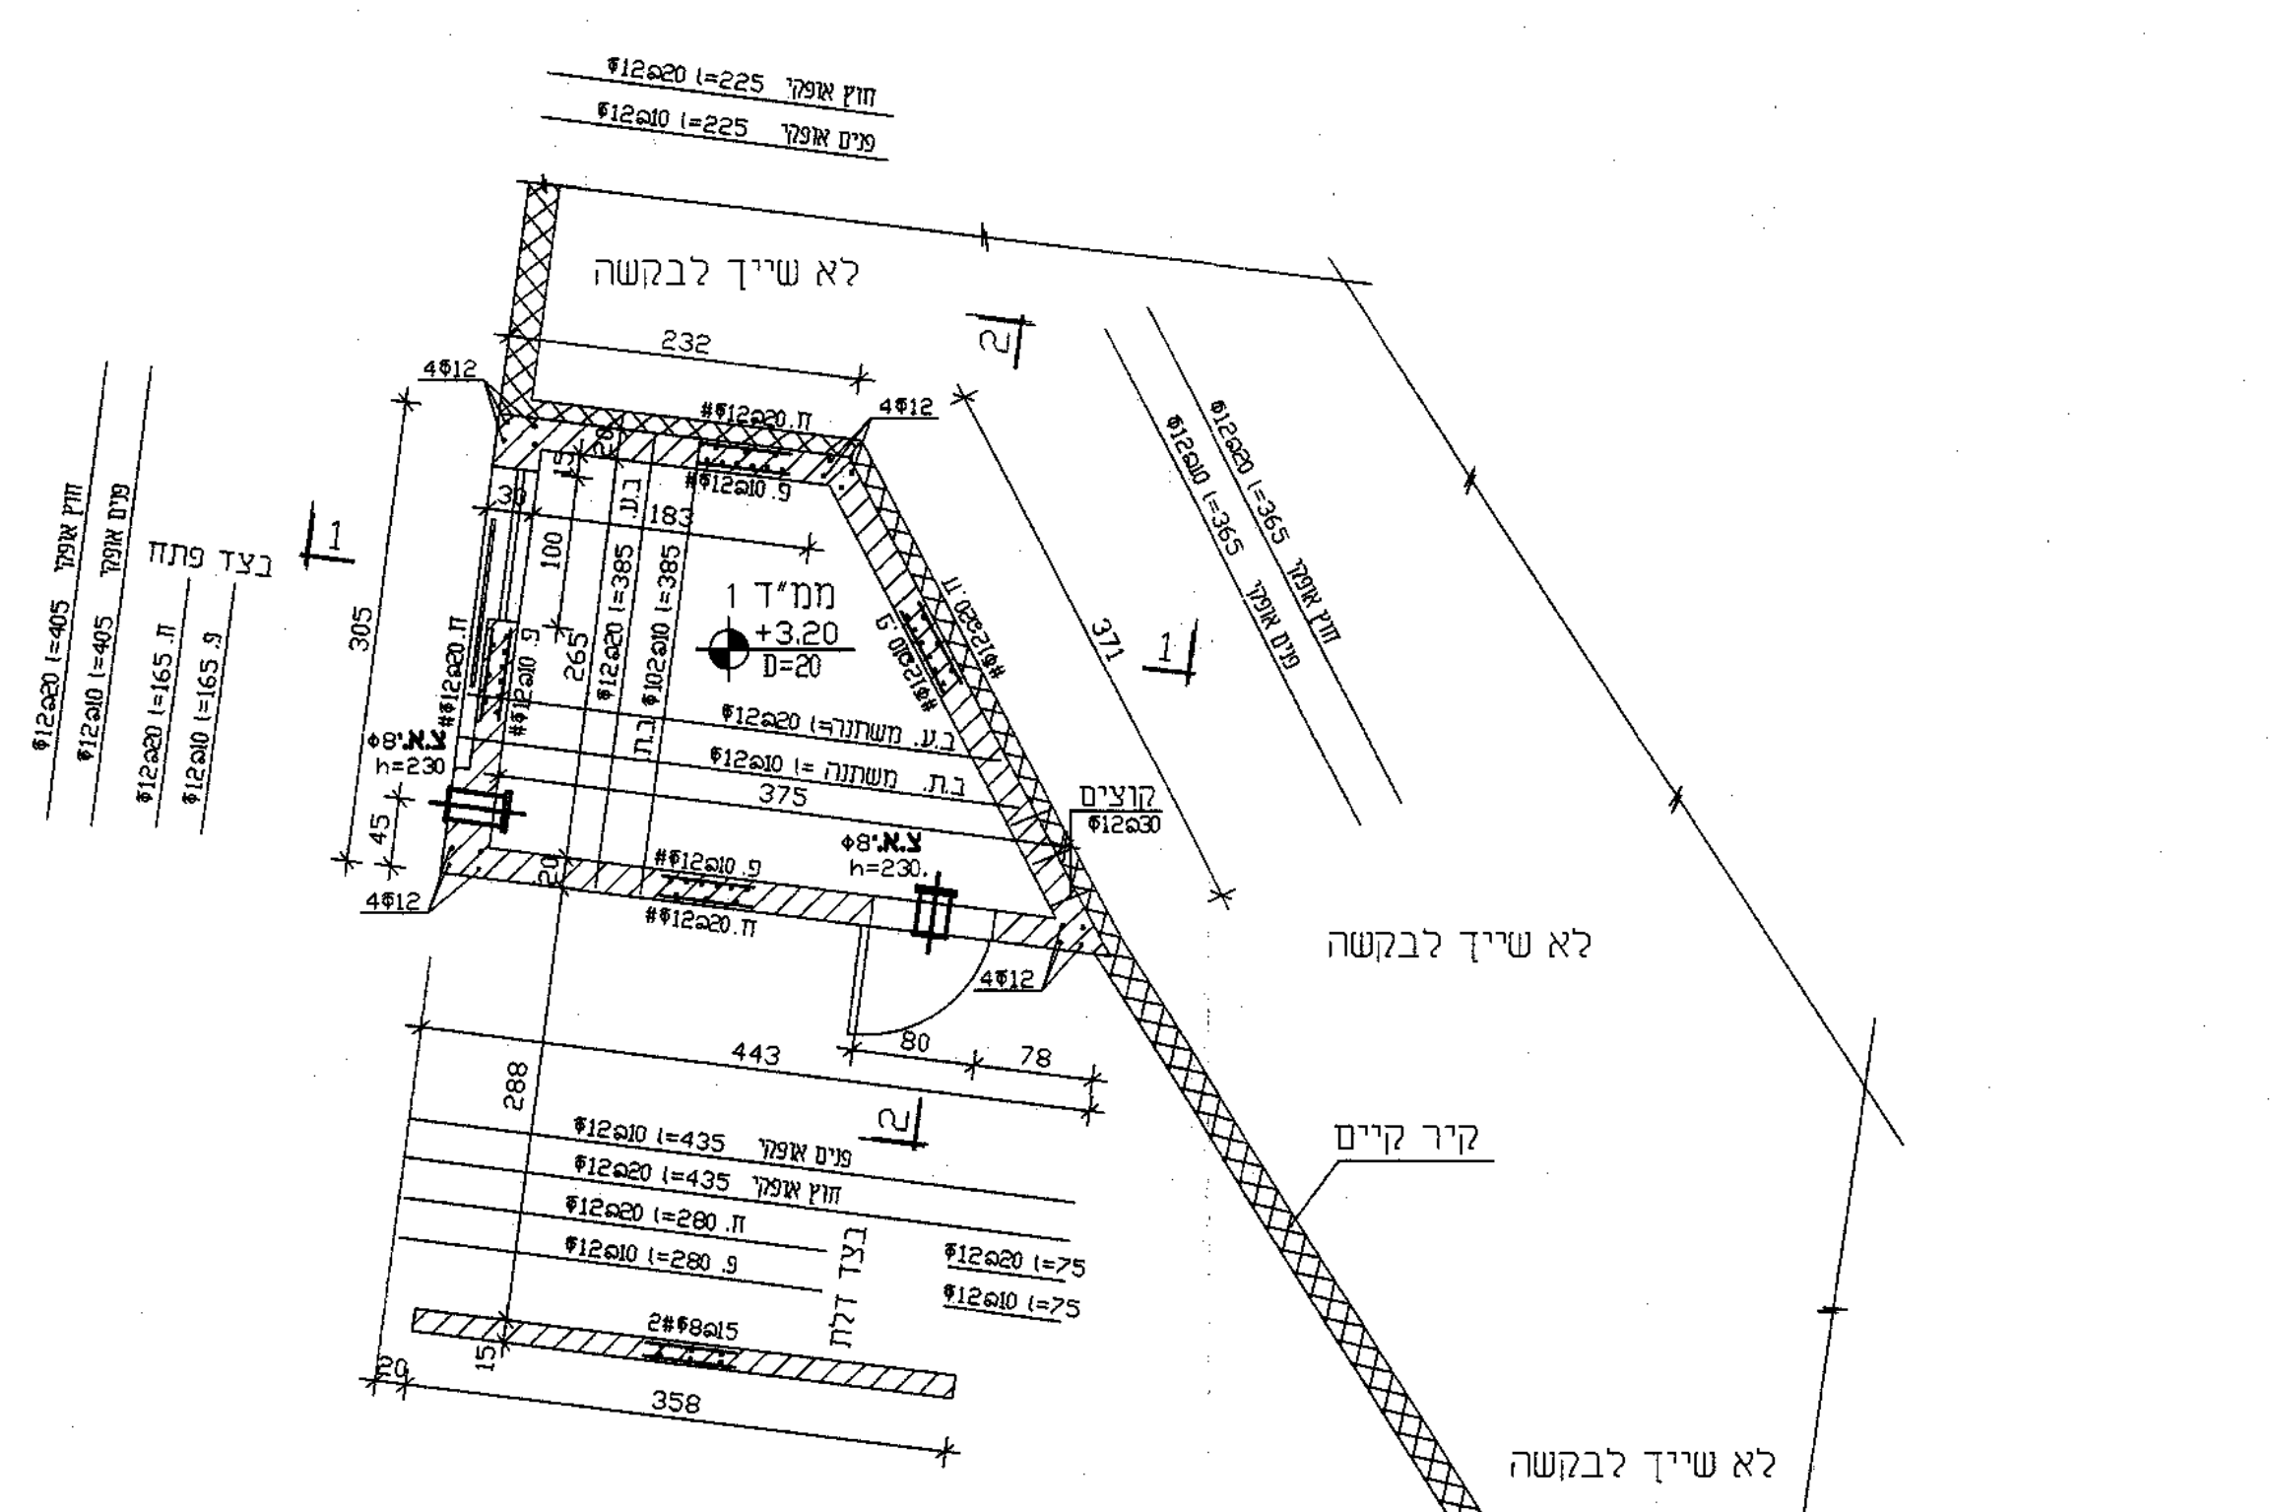

לא שייך לבקשה
ממ"ד 1
+3.20
D=20
קיר קיים
קוצים
Φ12a30
232
375
443
358
בצד פתח
בצד דלת

תקרת קומת קרקע
(רצפת קומה א')
1:50

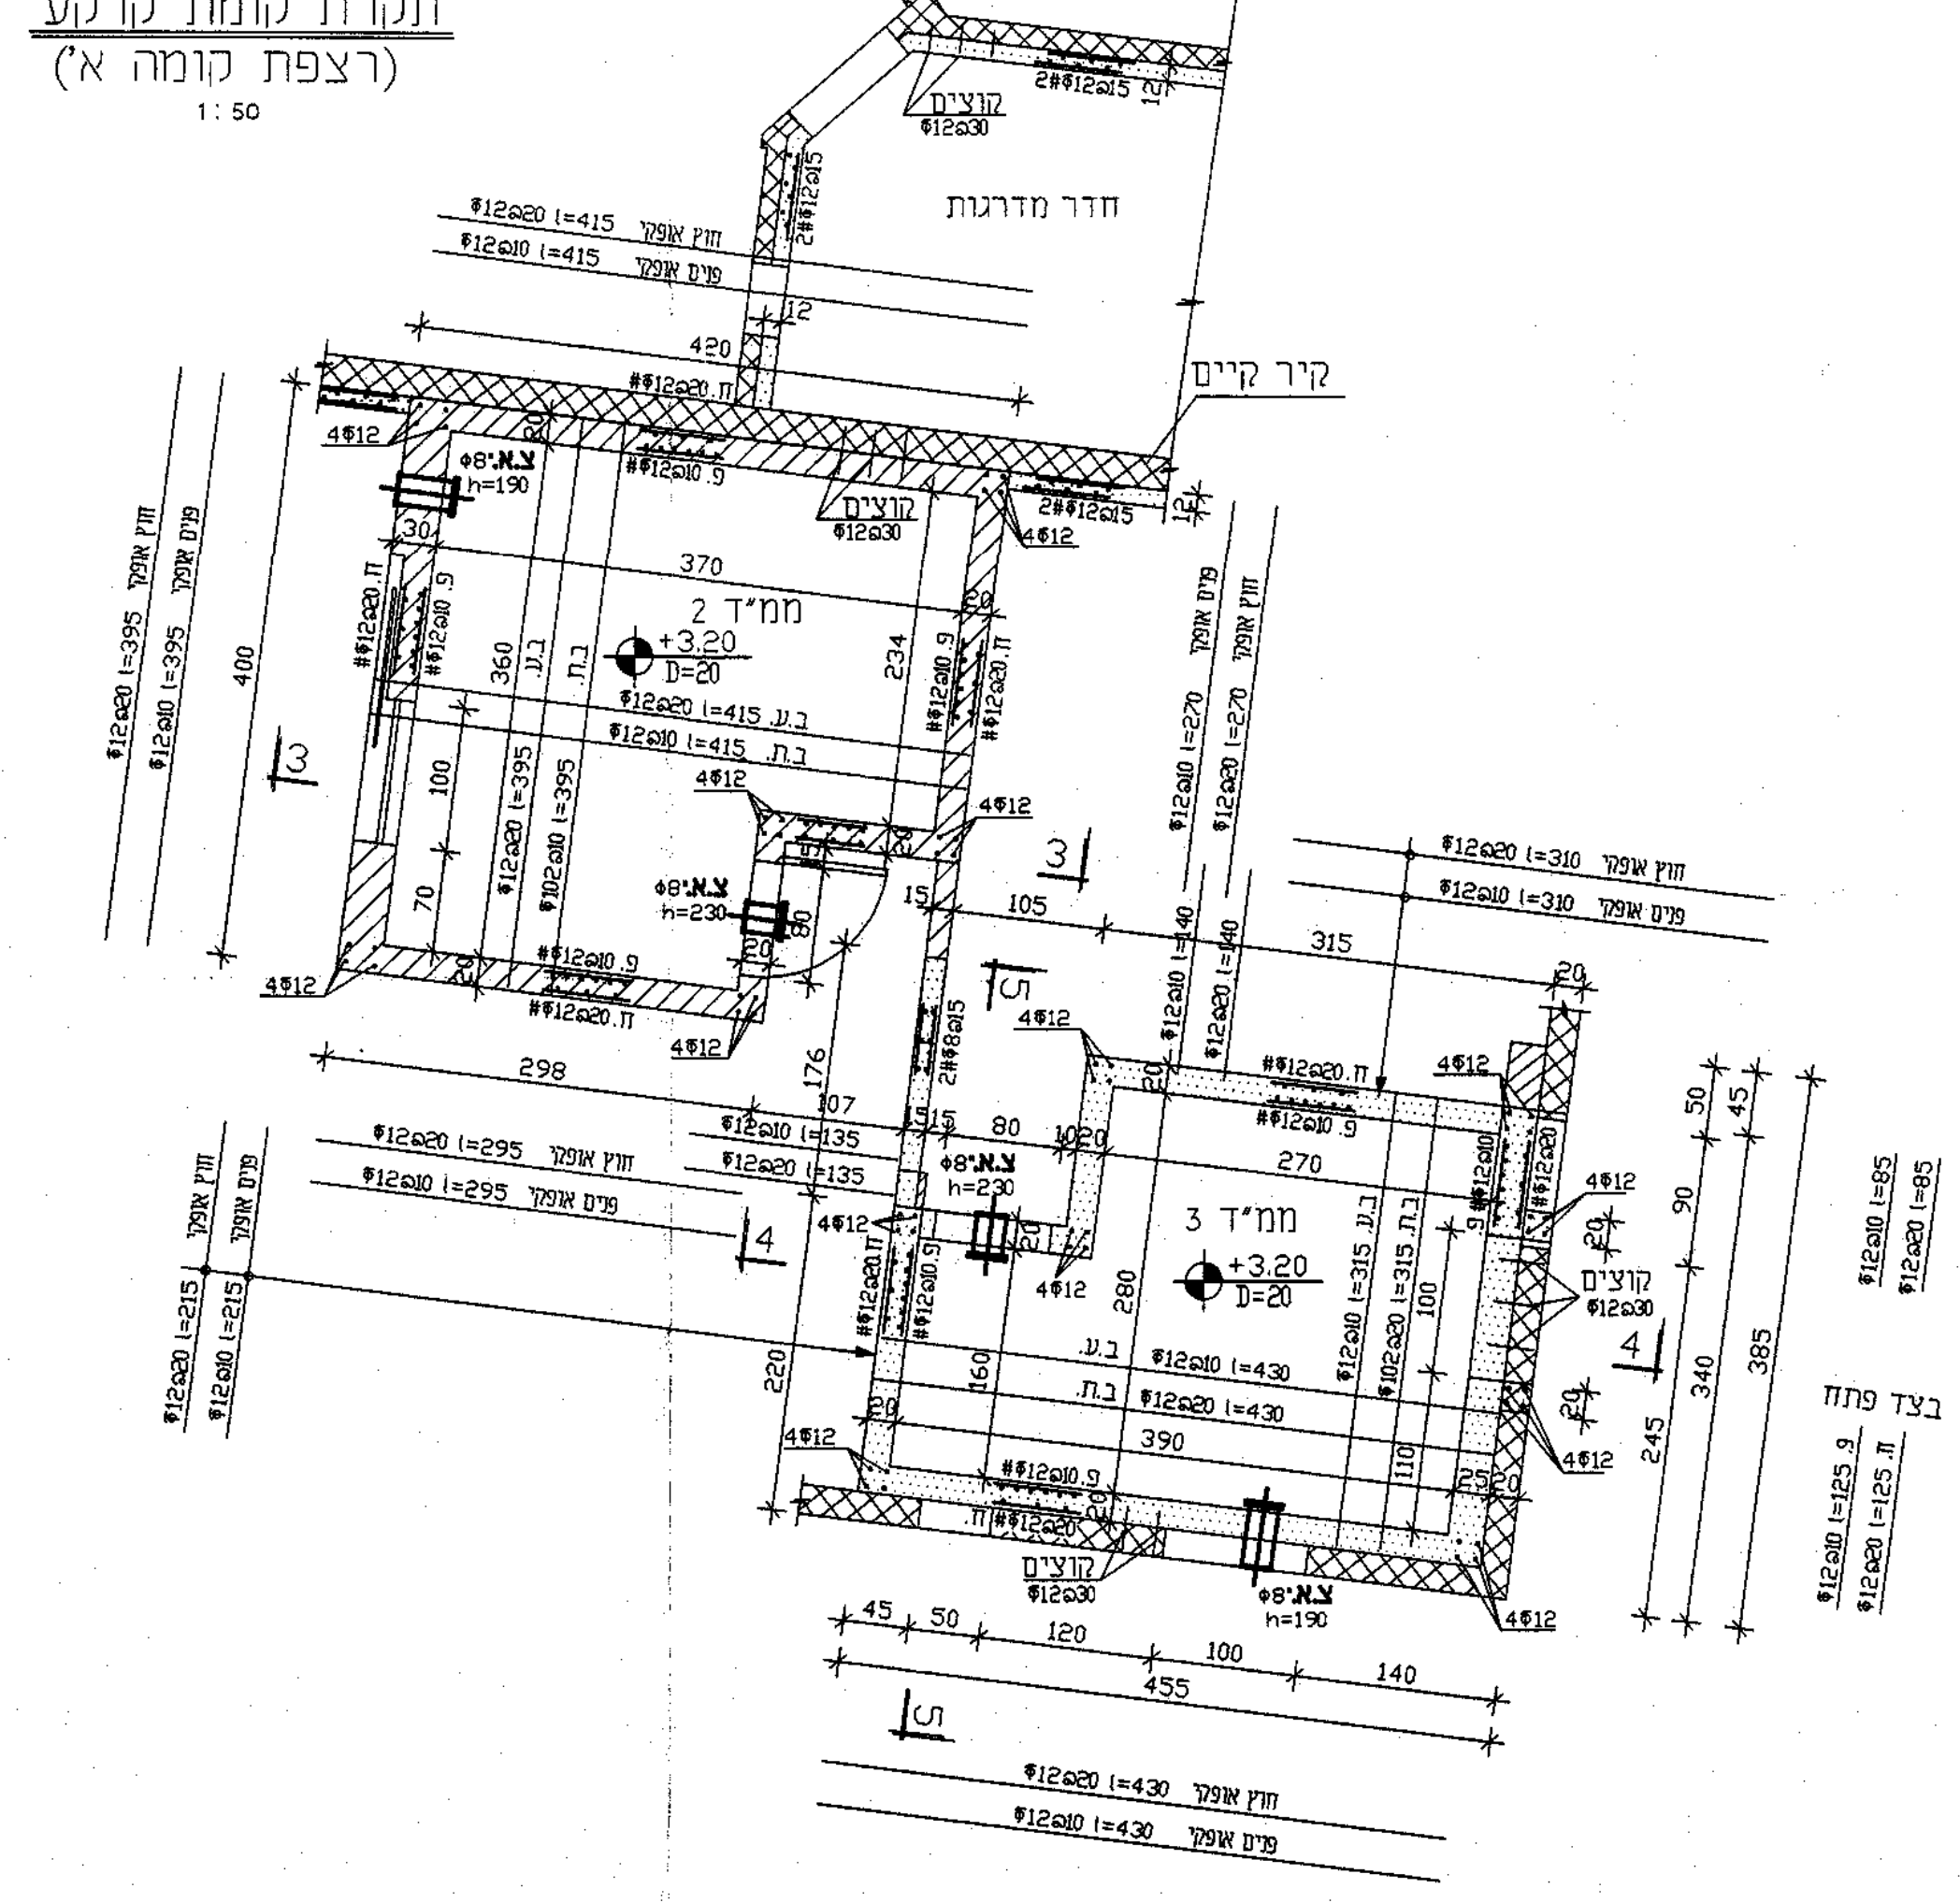

חדר מדרגות
קיר קיים
ממ"ד 2
+3.20
ממ"ד 3
+3.20
D=20
קוצים
Φ12a30
בצד פתח
370
420
455

תקרת קומת קרקע
(רצפת קומה א')
1:50

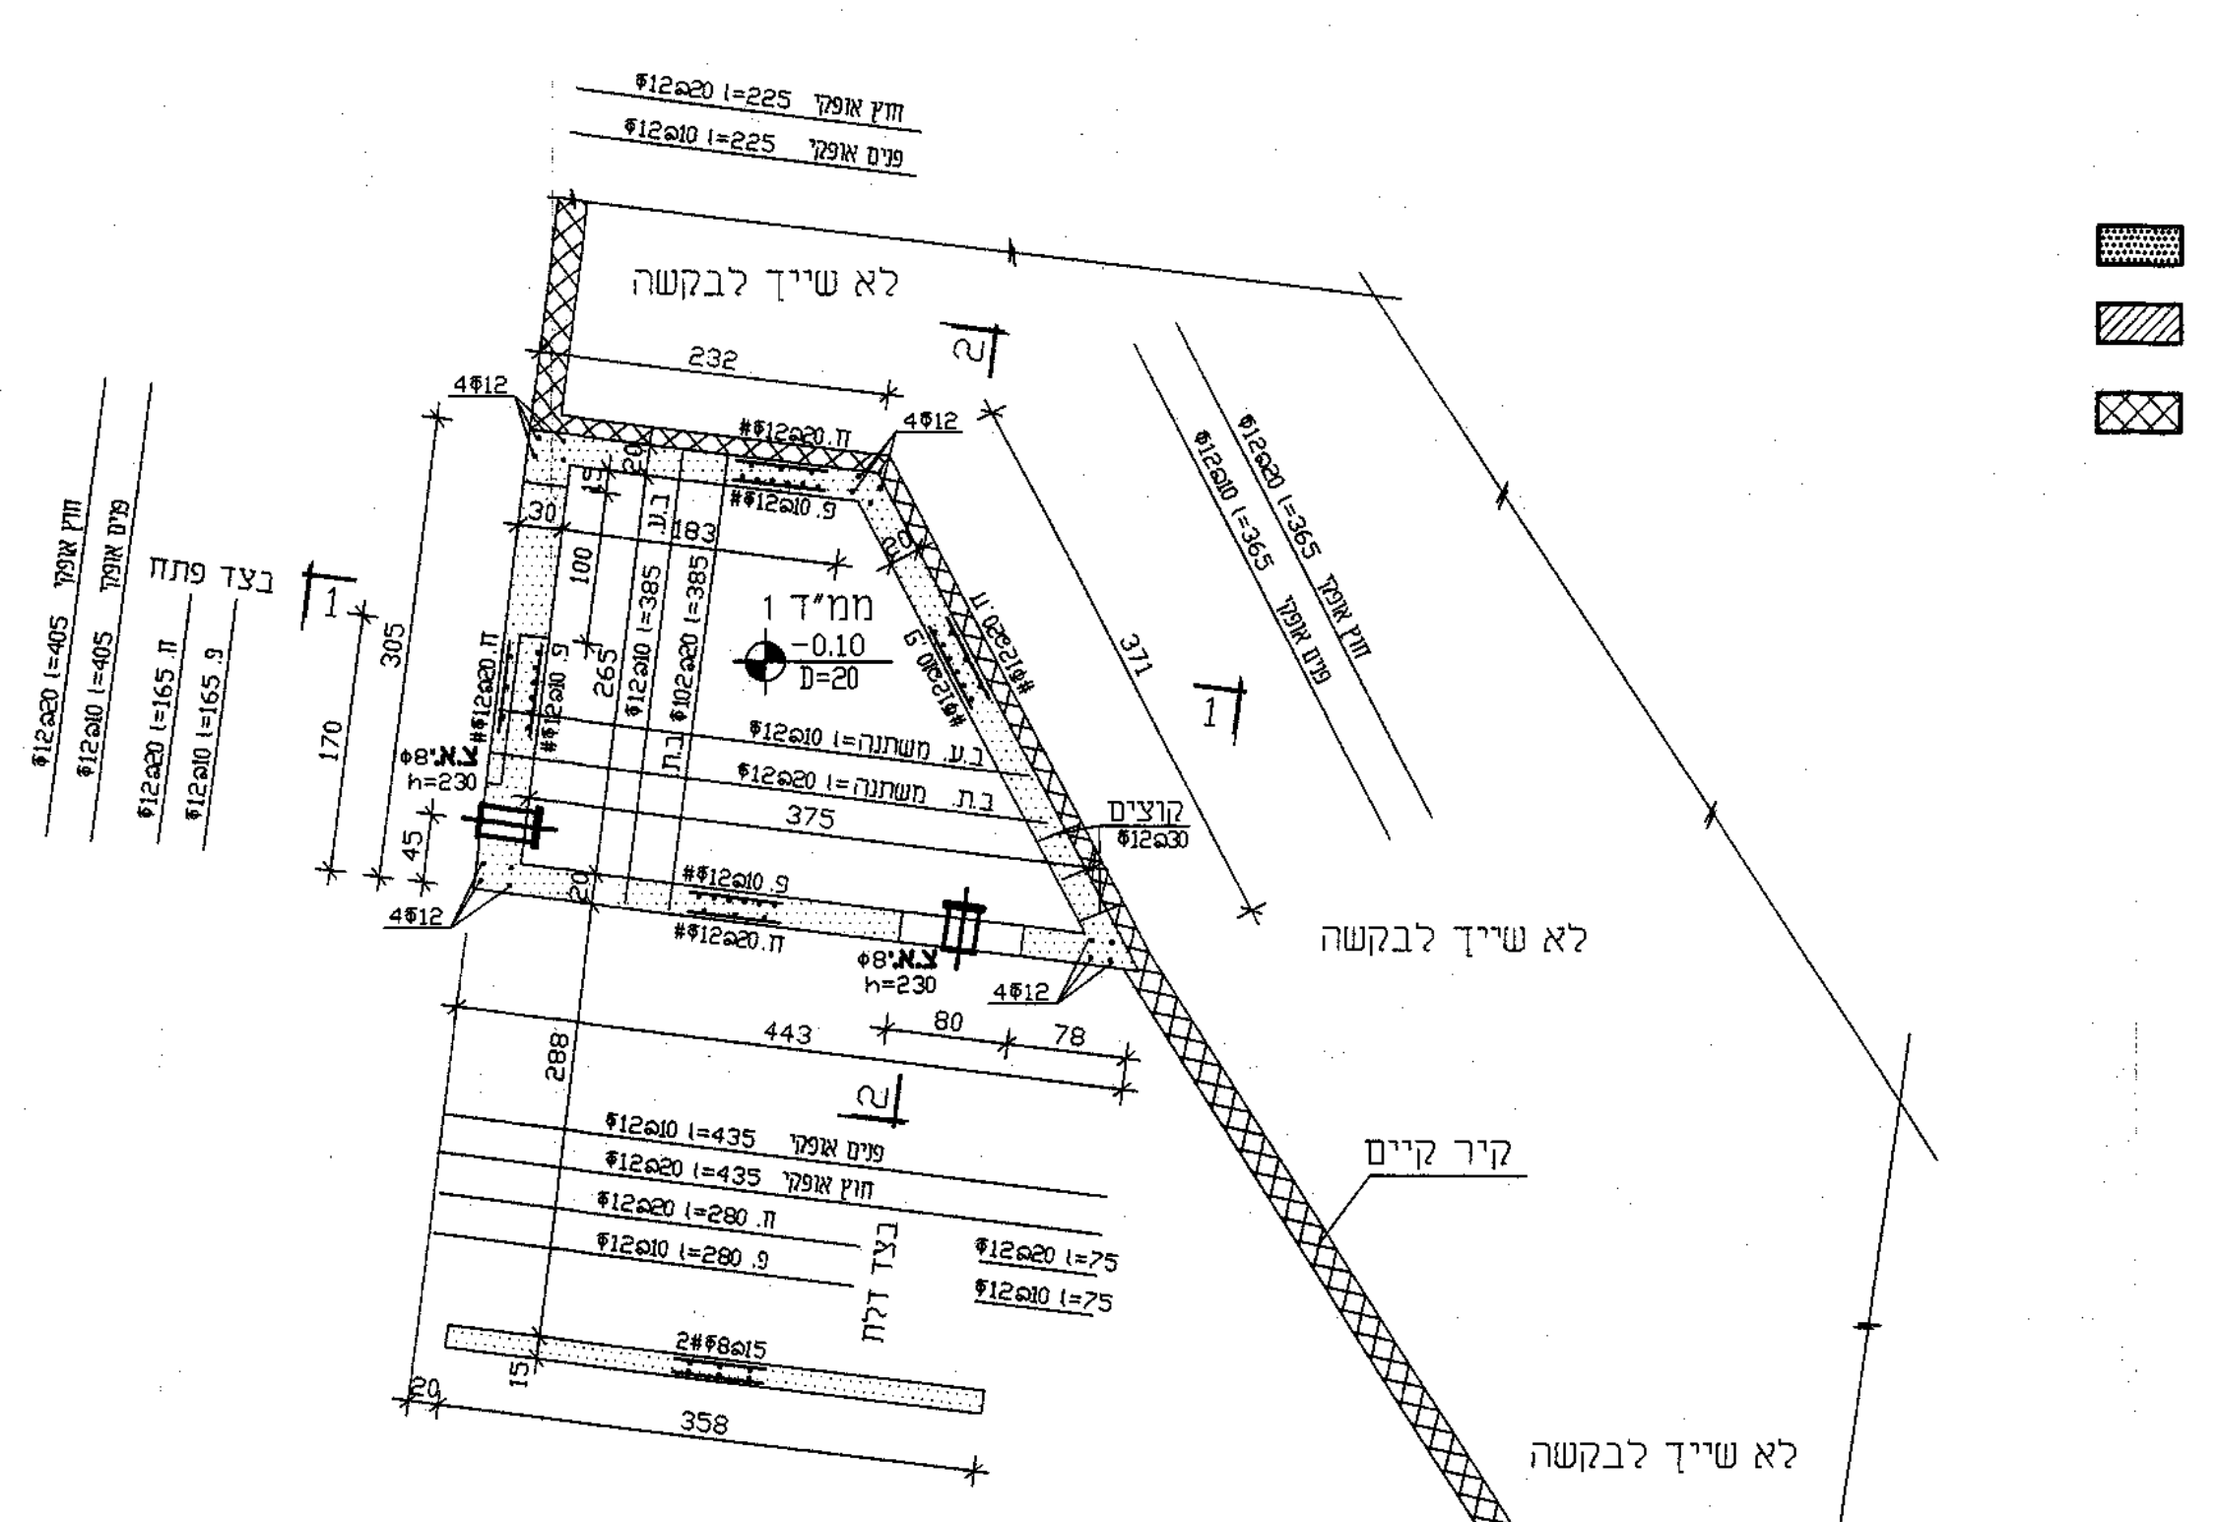

לא שייך לבקשה
ממ"ד 1
-0.10
D=20
קיר קיים
קוצים
Φ12a30
232
375
443
358
בצד פתח
בצד דלת

מיקרא:
▩ בטון ממשיך
▨ בטון מפסיק
☒ קיים

רצפת קומת קרקע
1:50

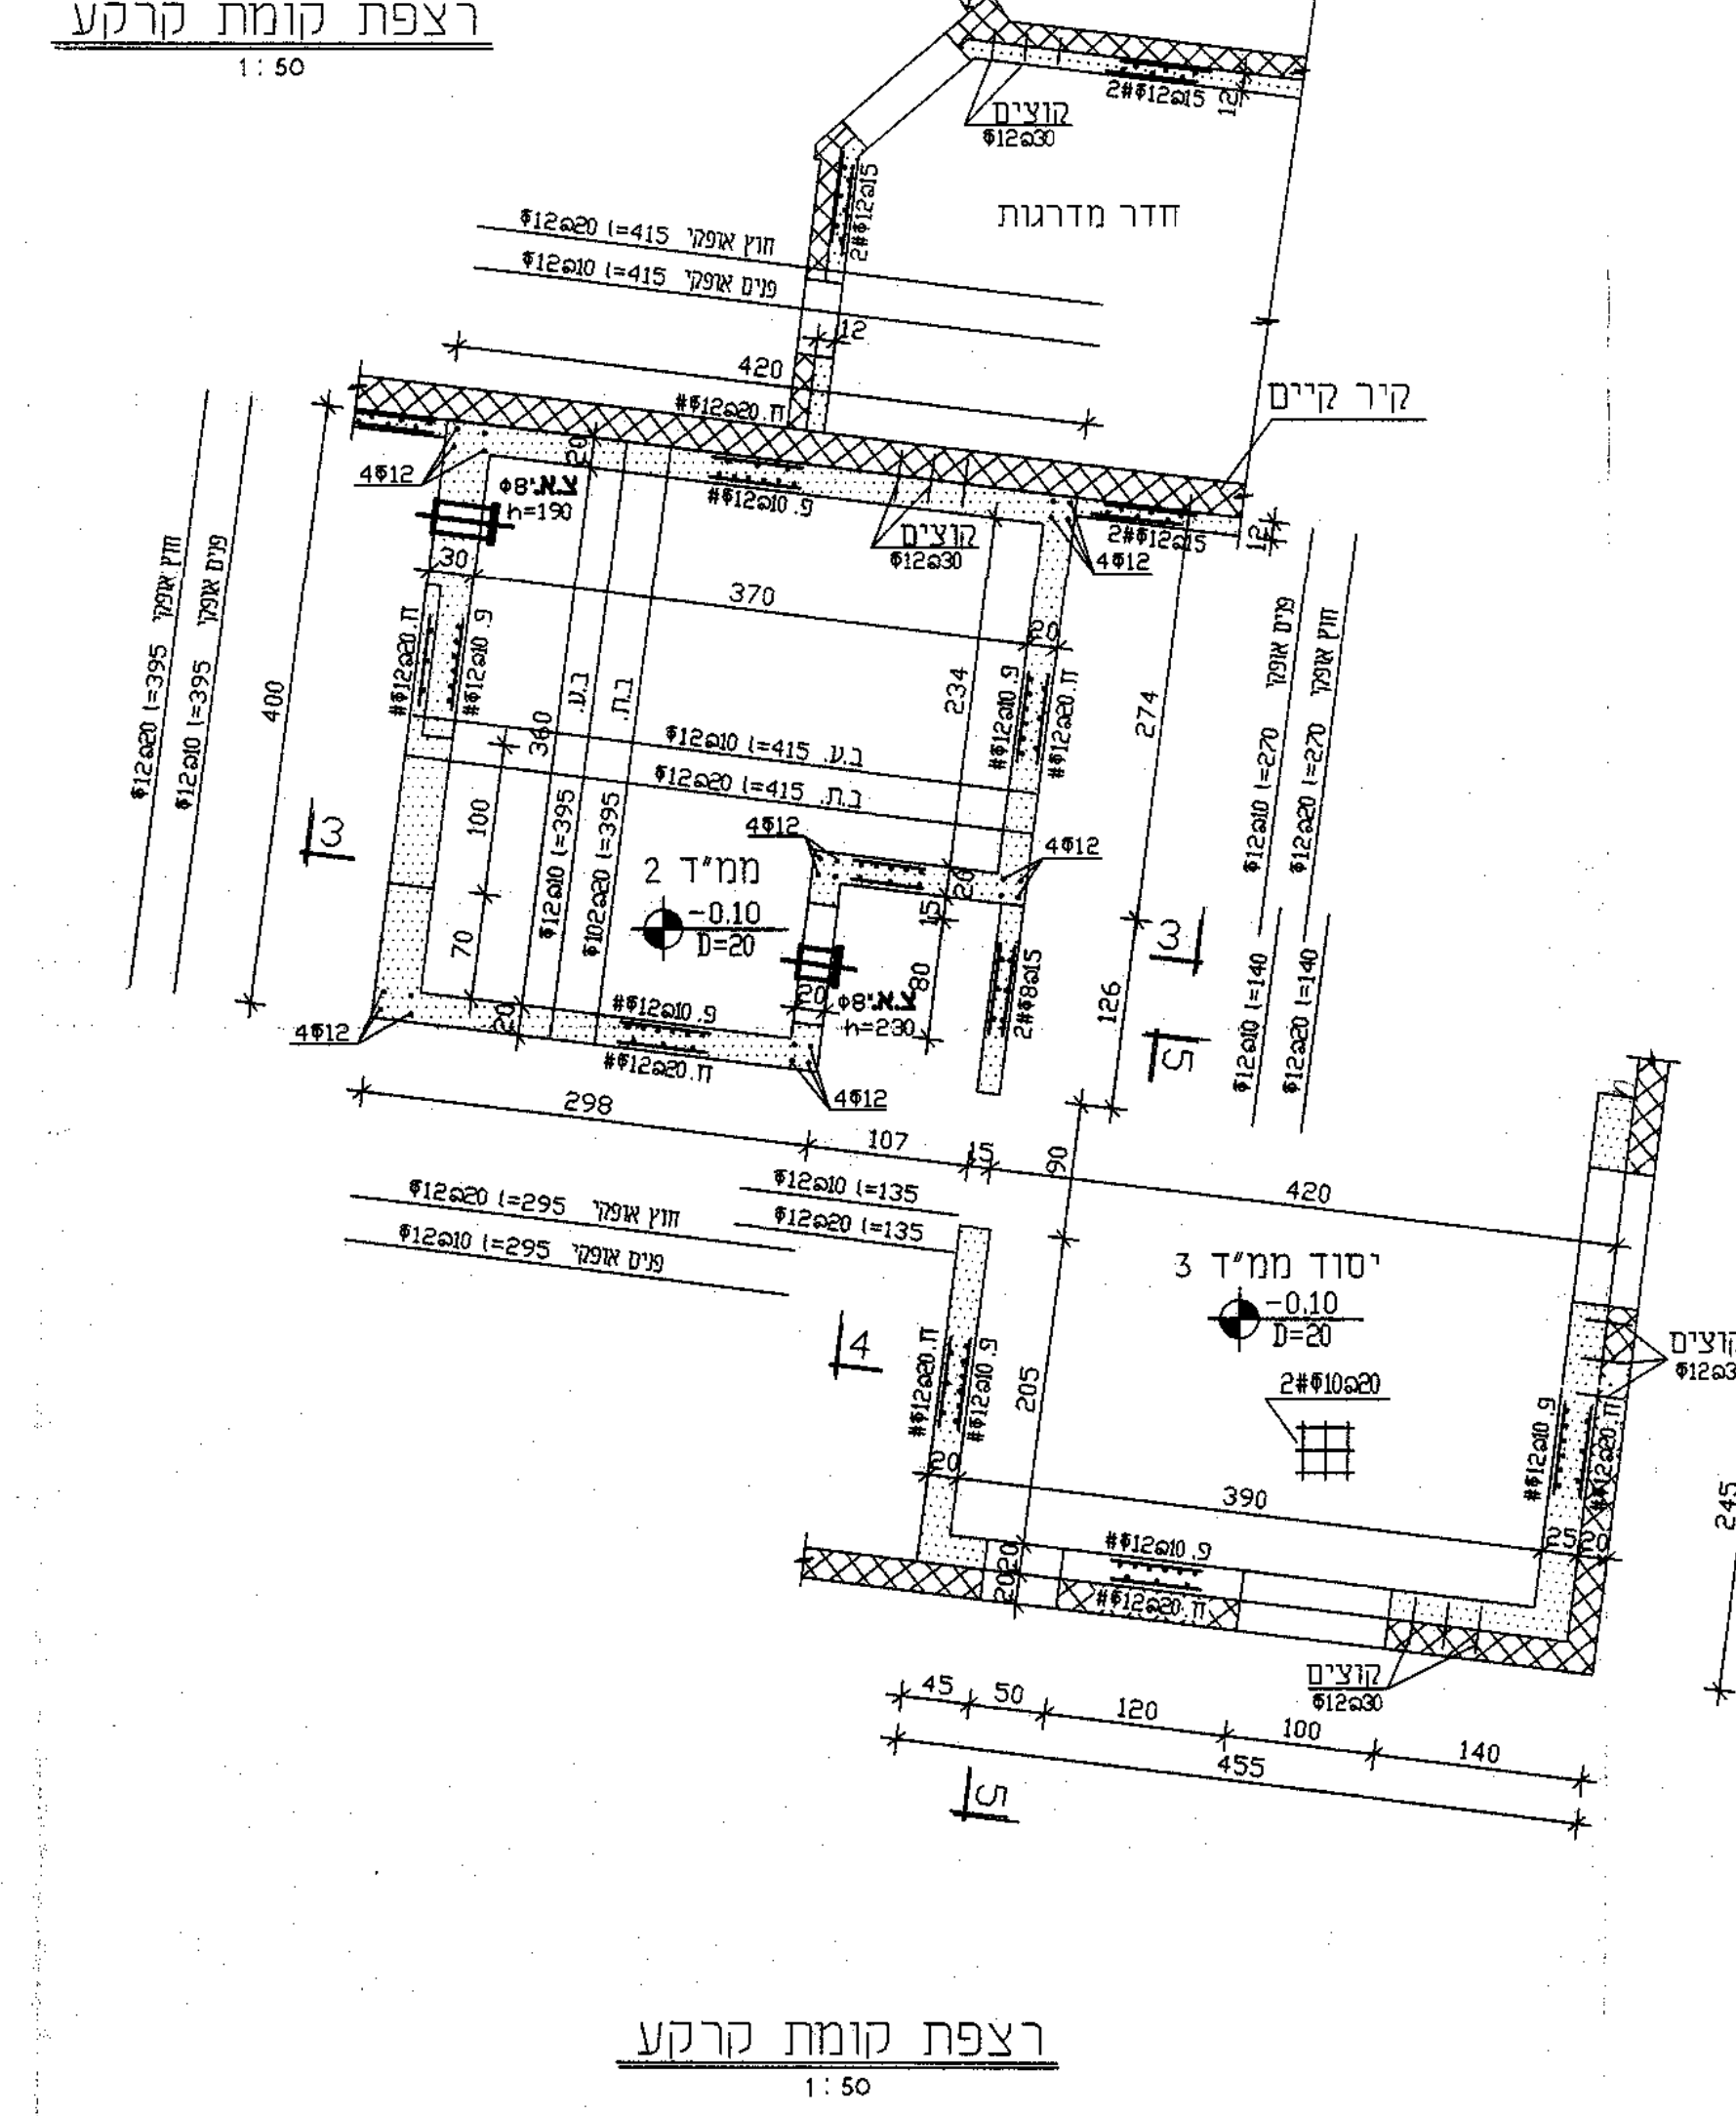

חדר מדרגות
קיר קיים
ממ"ד 2
-0.10
D=20
יסוד ממ"ד 3
-0.10
D=20
קוצים
Φ12a30
420
390
455

רצפת קומת קרקע
1:50

משי נפתלי

רחי אצ"ל 58 , ת"א

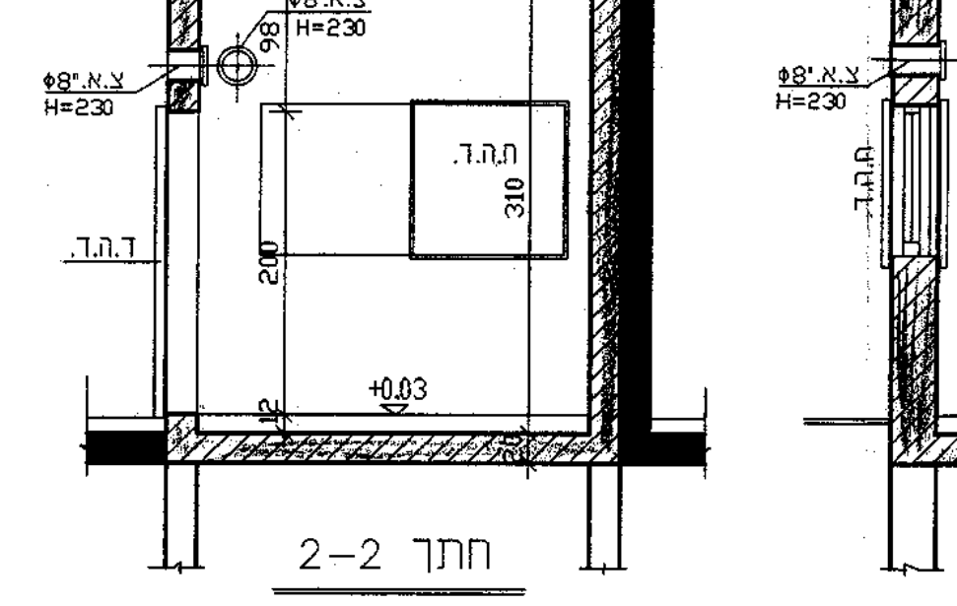

+3.20
צ.א.Φ8
H=230
ד.ה.ד.
ח.ה.ד.
310
+0.03

חתך 2-2

1:50

מקרא
שקע
טלויזיה T.V
טלפון
40w ג.ת. חרום
ג.ת. פלוריסנט 2*40w
מפסק בודד

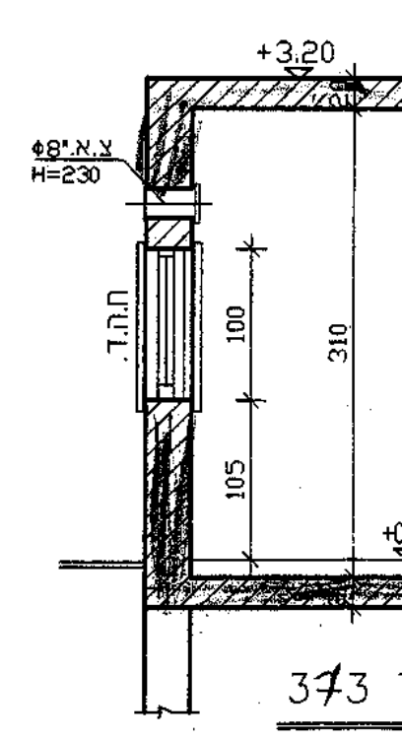

+3.20
צ.א.Φ8
H=230
ח.ה.ד.
100
310
105

3₇3

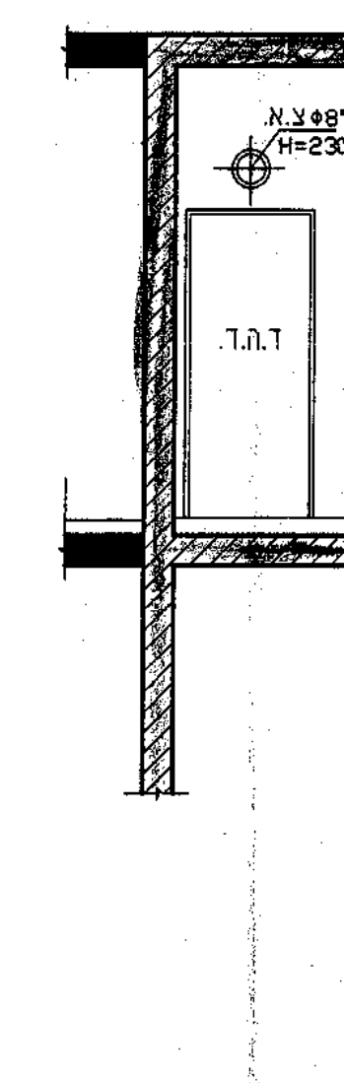

צ.א.Φ8
H=230
ד.ה.ד.