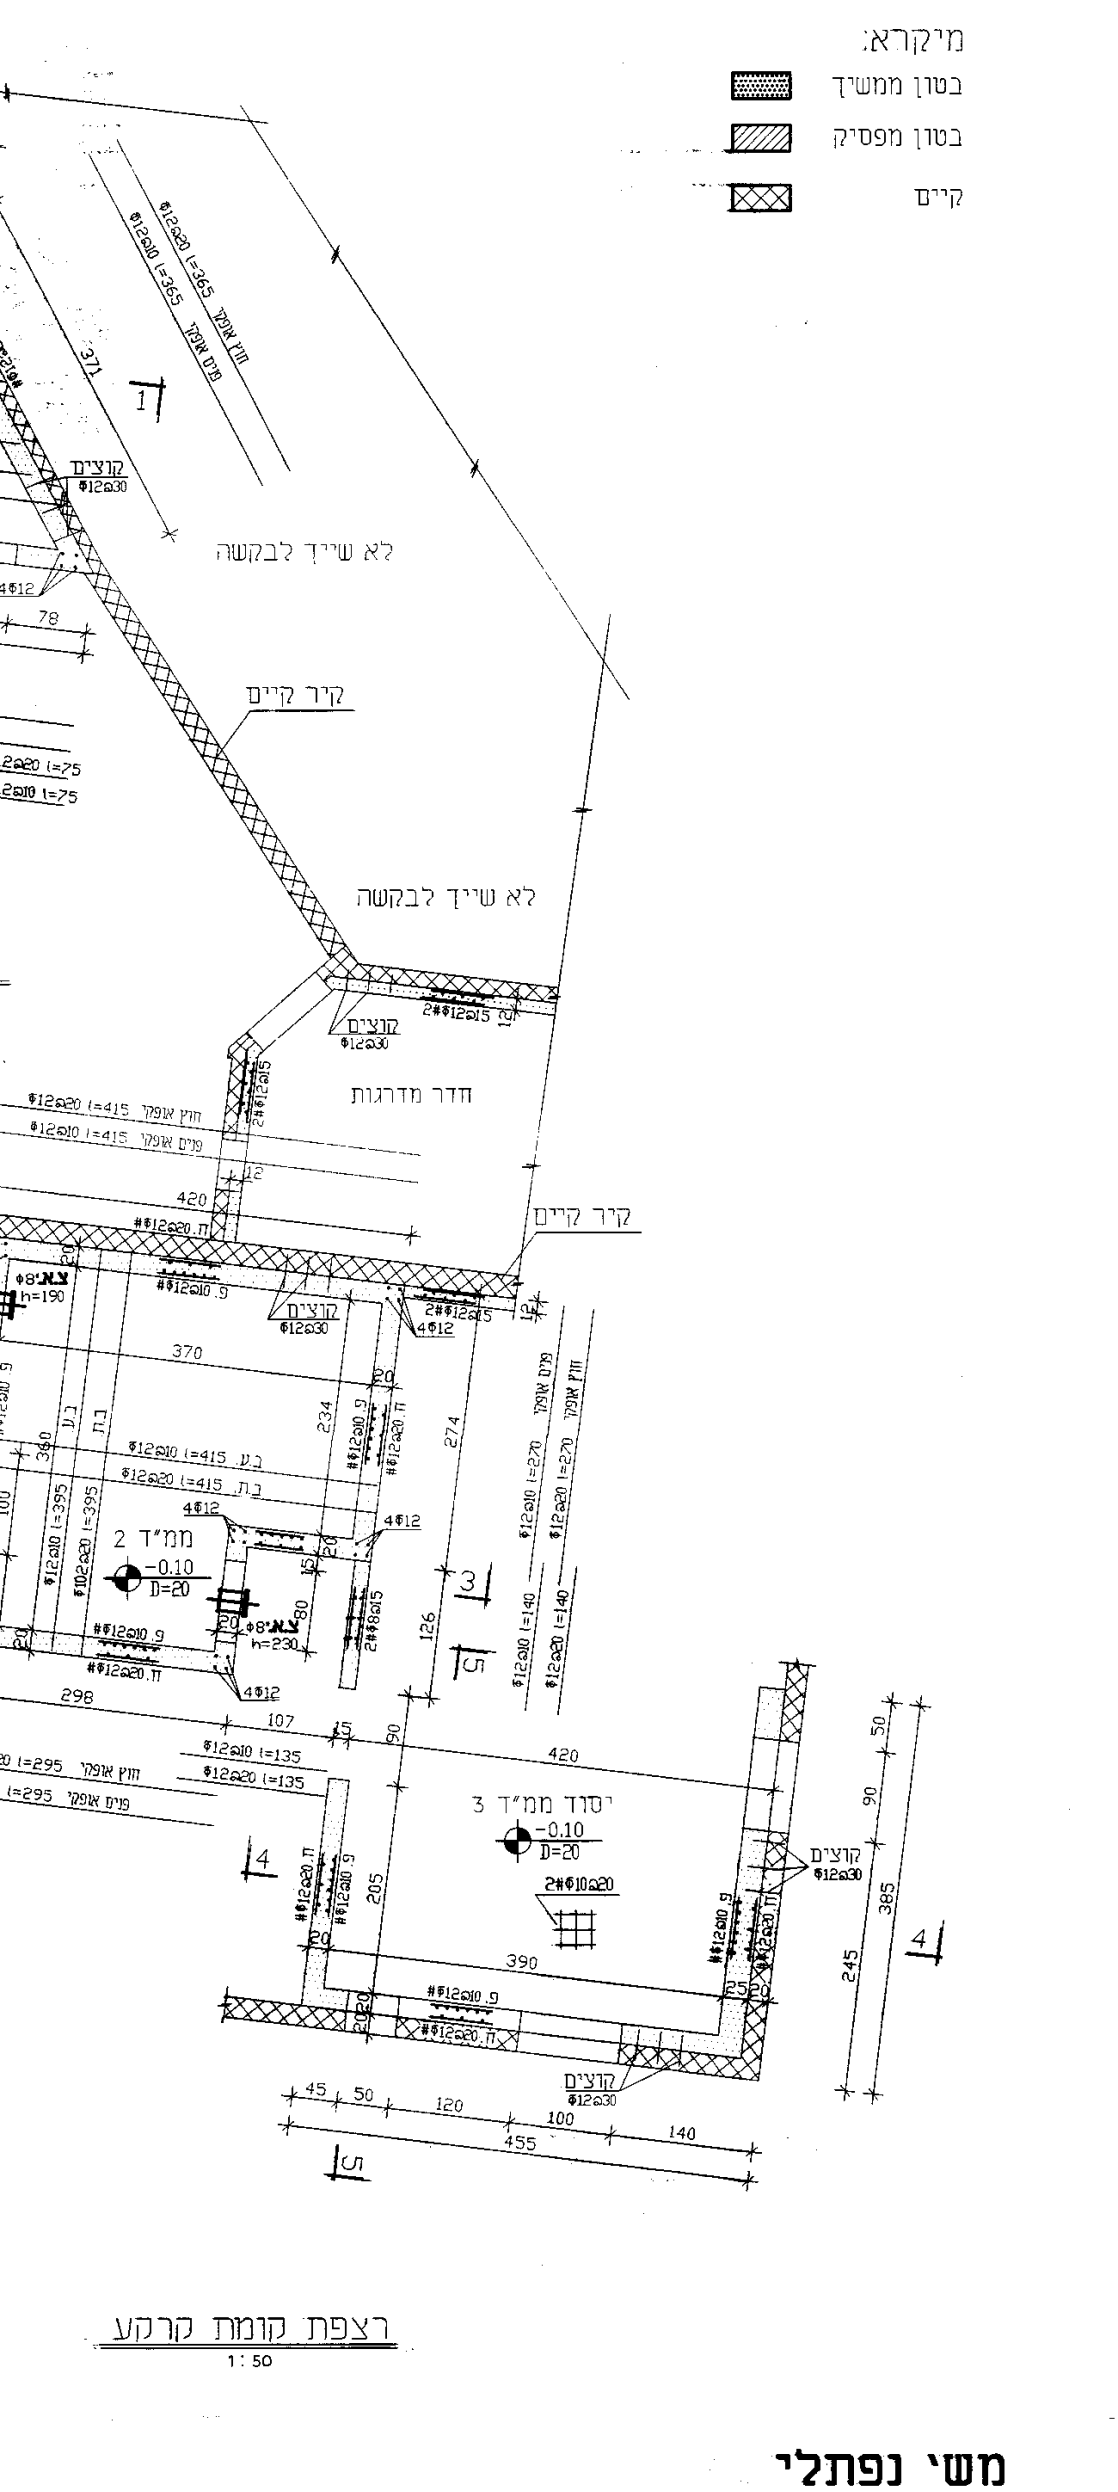

מיקרא:
בטון ממשיך
בטון מפסיק
קיים
לא שייך לבקשה
קיר קיים
ממ"ד 2
ממ"ד 3

רצפת קומת קרקע
1:50

משי נפתלי
רח' אצ"ל 58 , ת"א

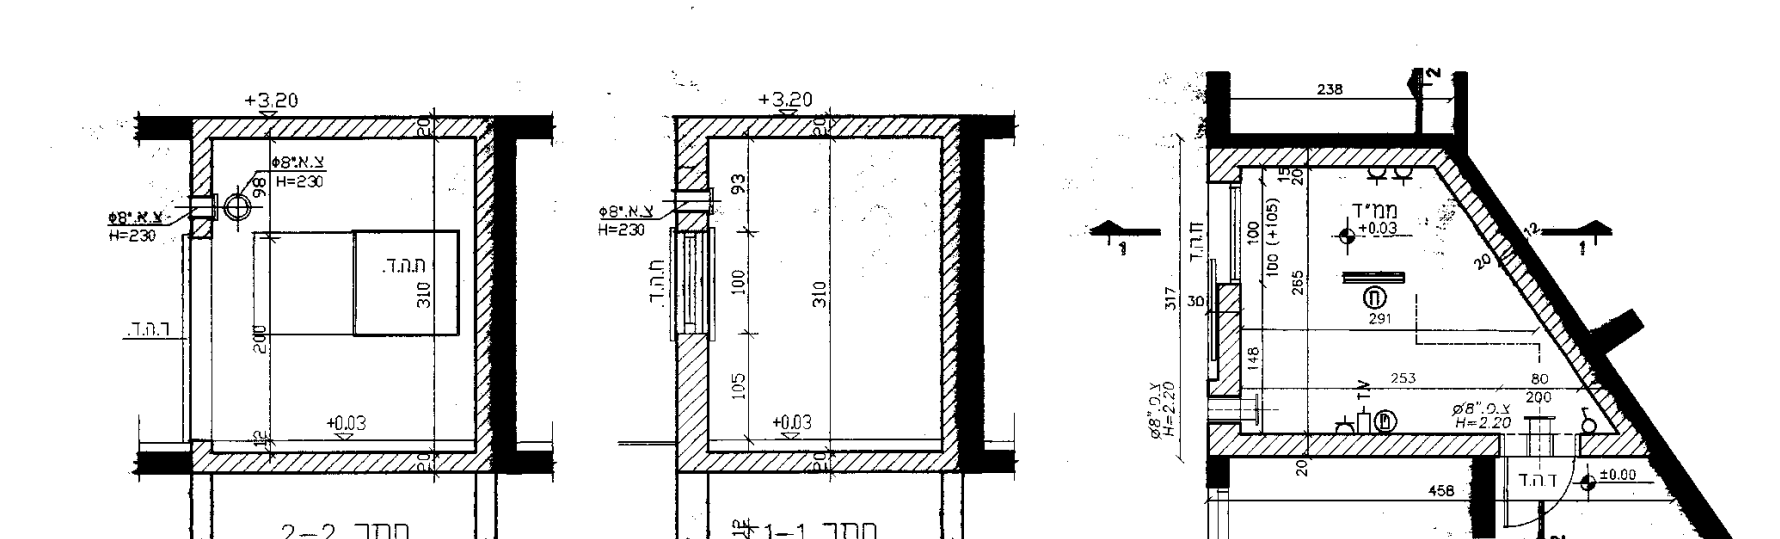

חתך 2-2
1:50
חתך 1-1
1:50

ממ"ד דירה מס' 5
קנ"מ: 1:50

מקרא
- שקע
- טלויזיה
- טלפון
- ג.ת. חדרוש 40w
- ג.ת. פלורסנט 2*40w
- מפסק בודד

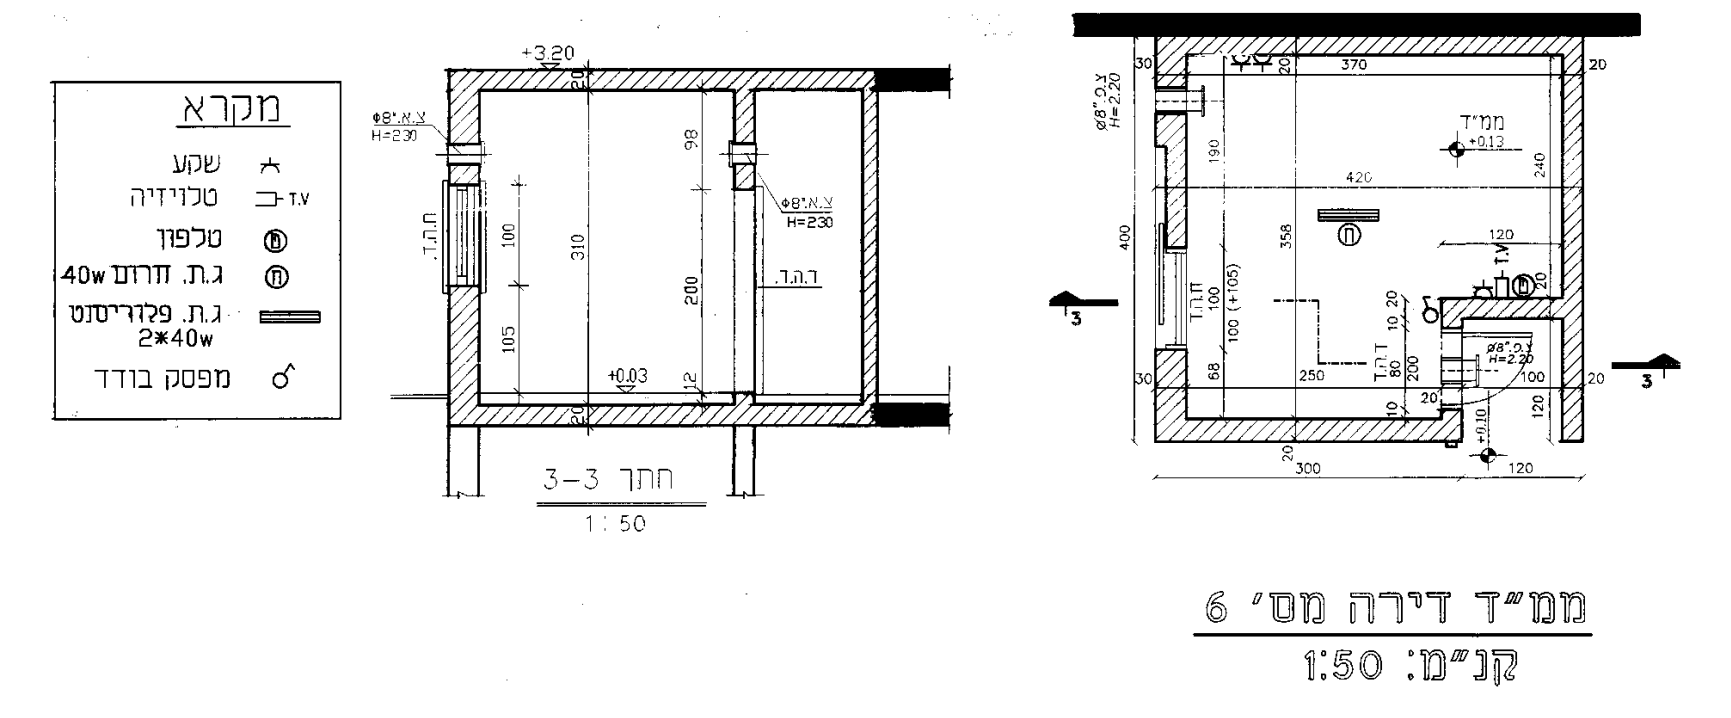

ממ"ד דירה מס' 6
קנ"מ: 1:50

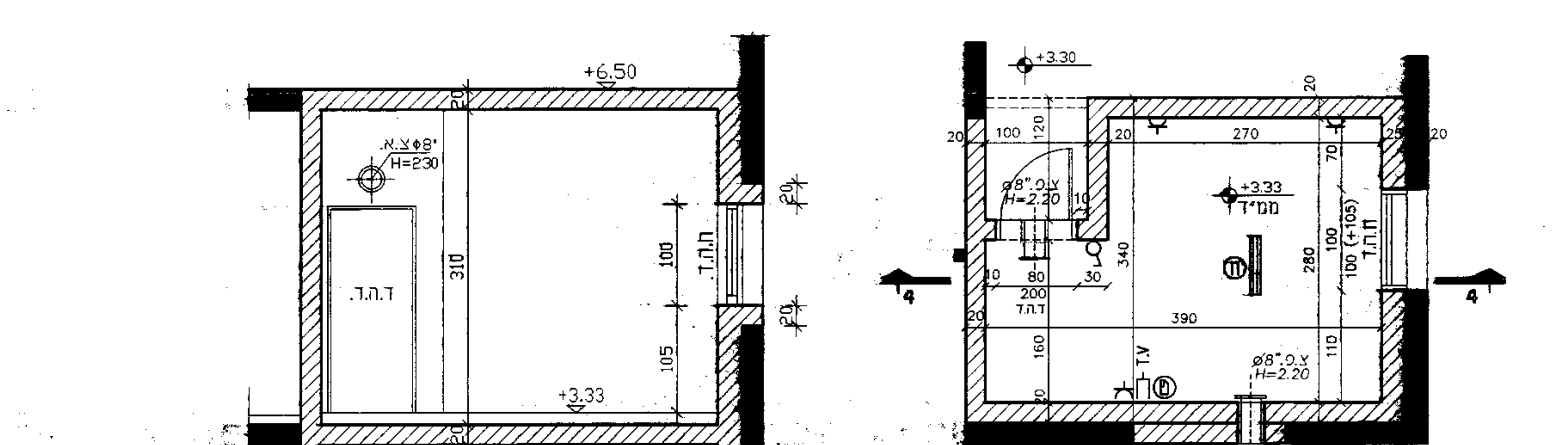

ממ"ד דירה מס' 7
קנ"מ: 1:50

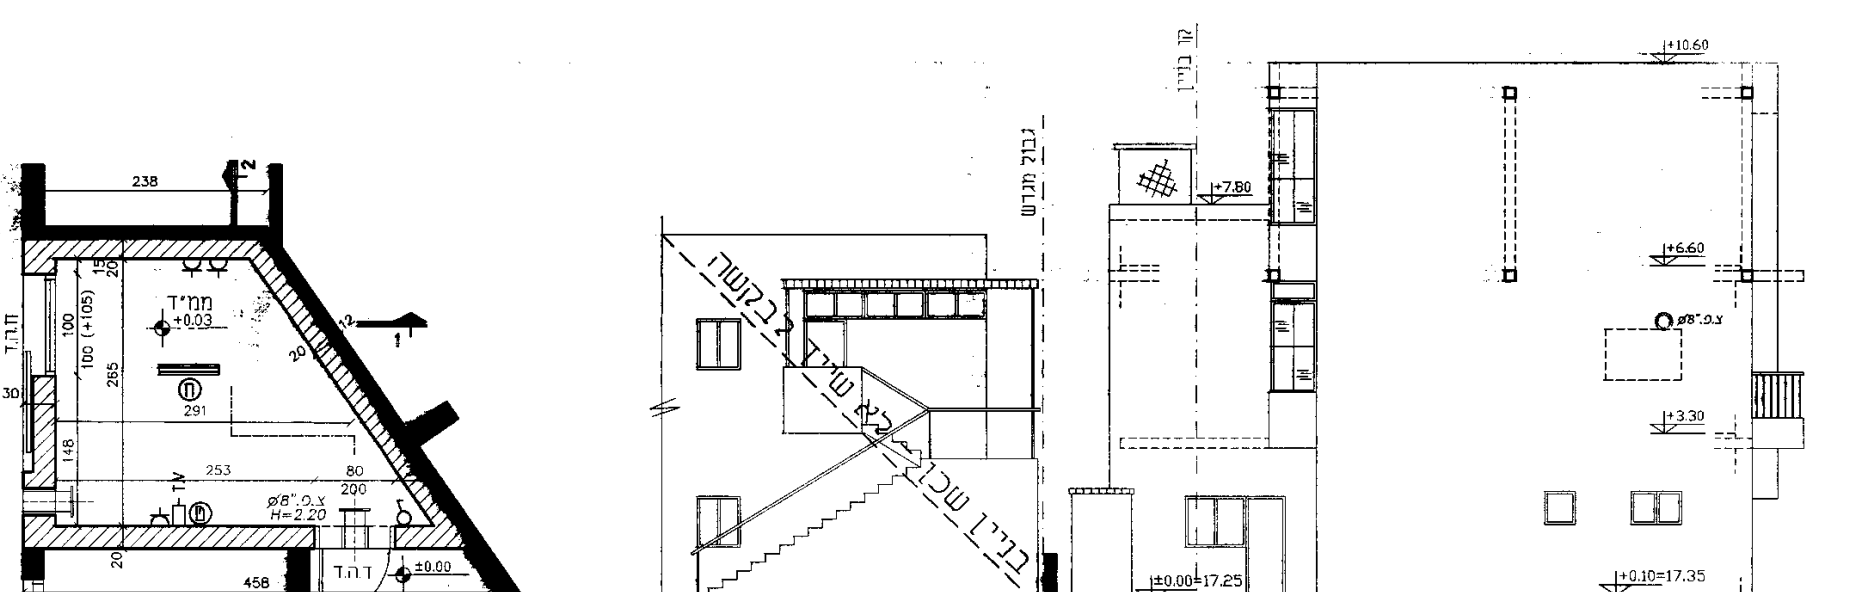

בניין שכן - לא שייך לבקשה

חזית דרומית
קנ"מ: 1:100

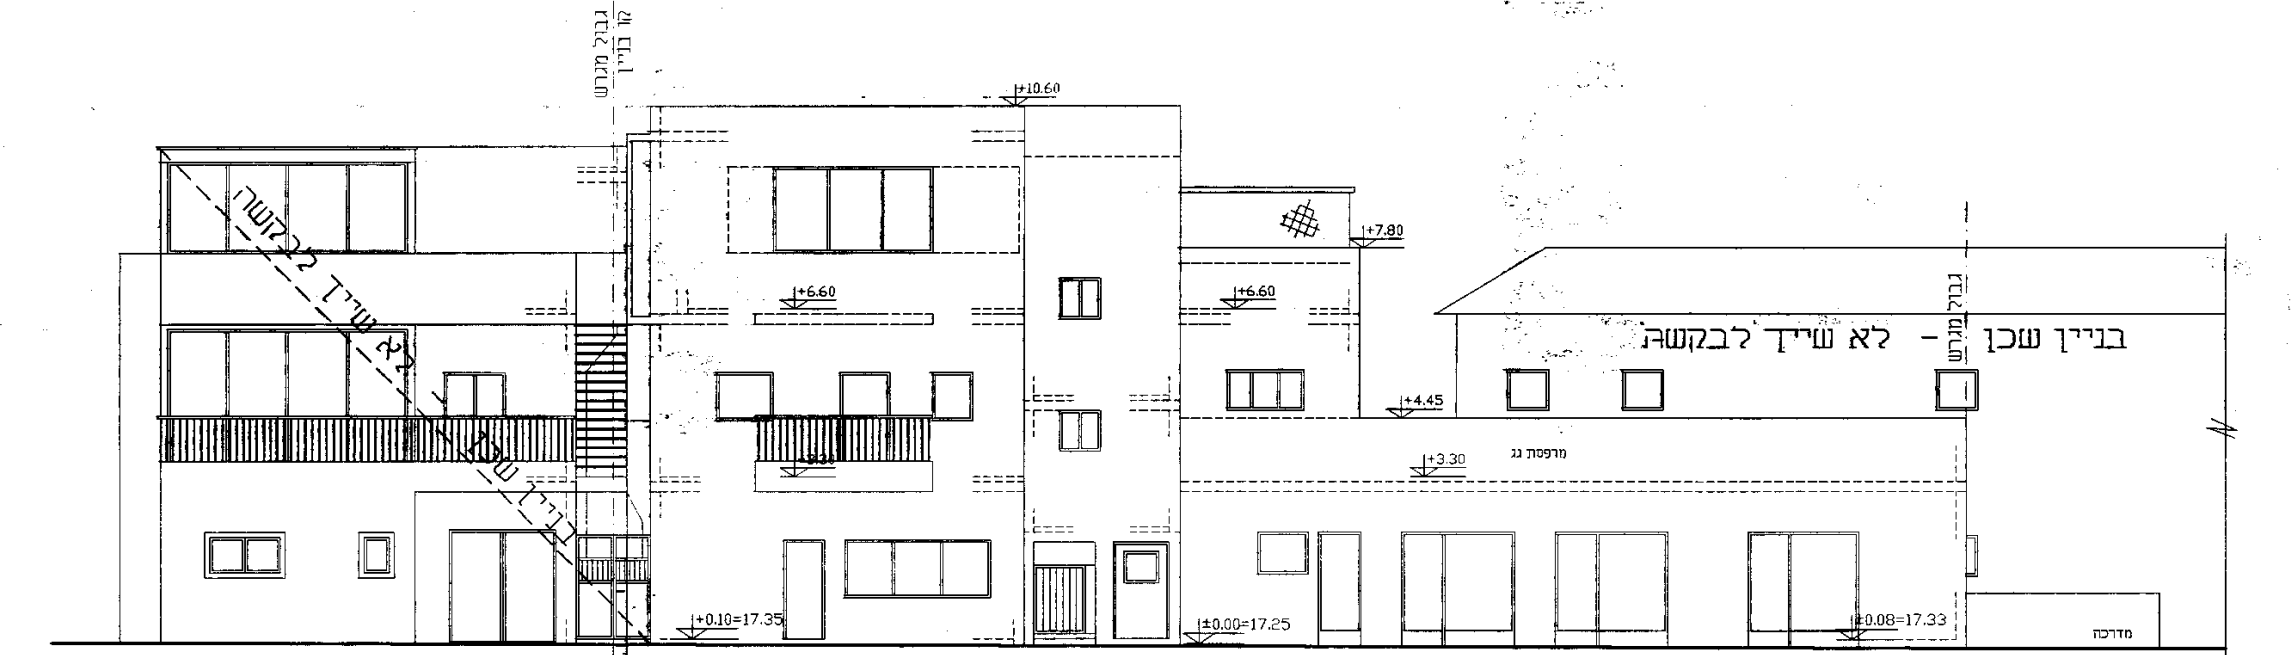

בניין שכן - לא שייך לבקשה

חזית מזרחית
קנ"מ: 1:100

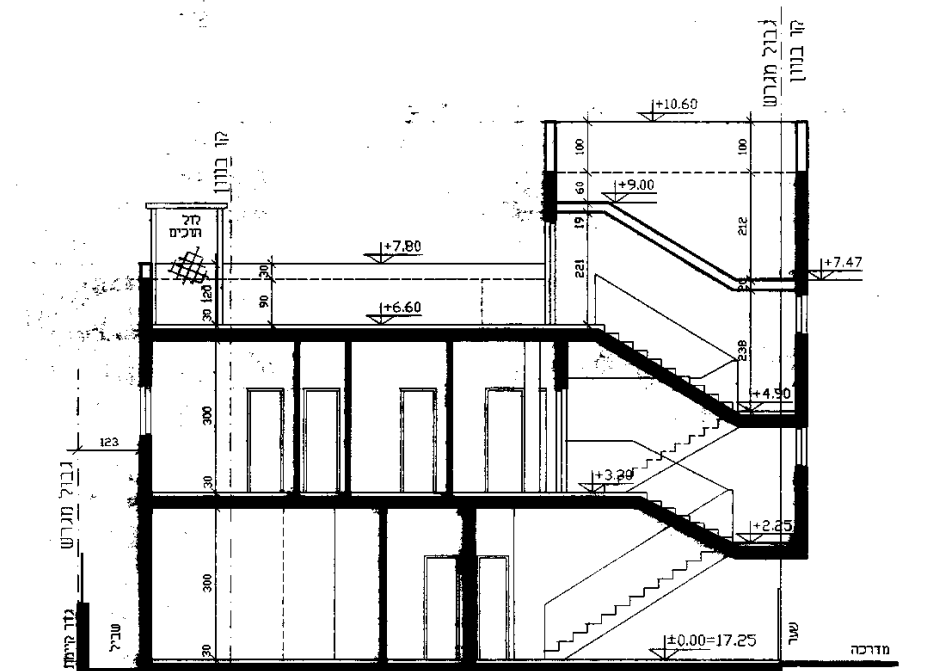

חתך א-א
קנ"מ: 1:100

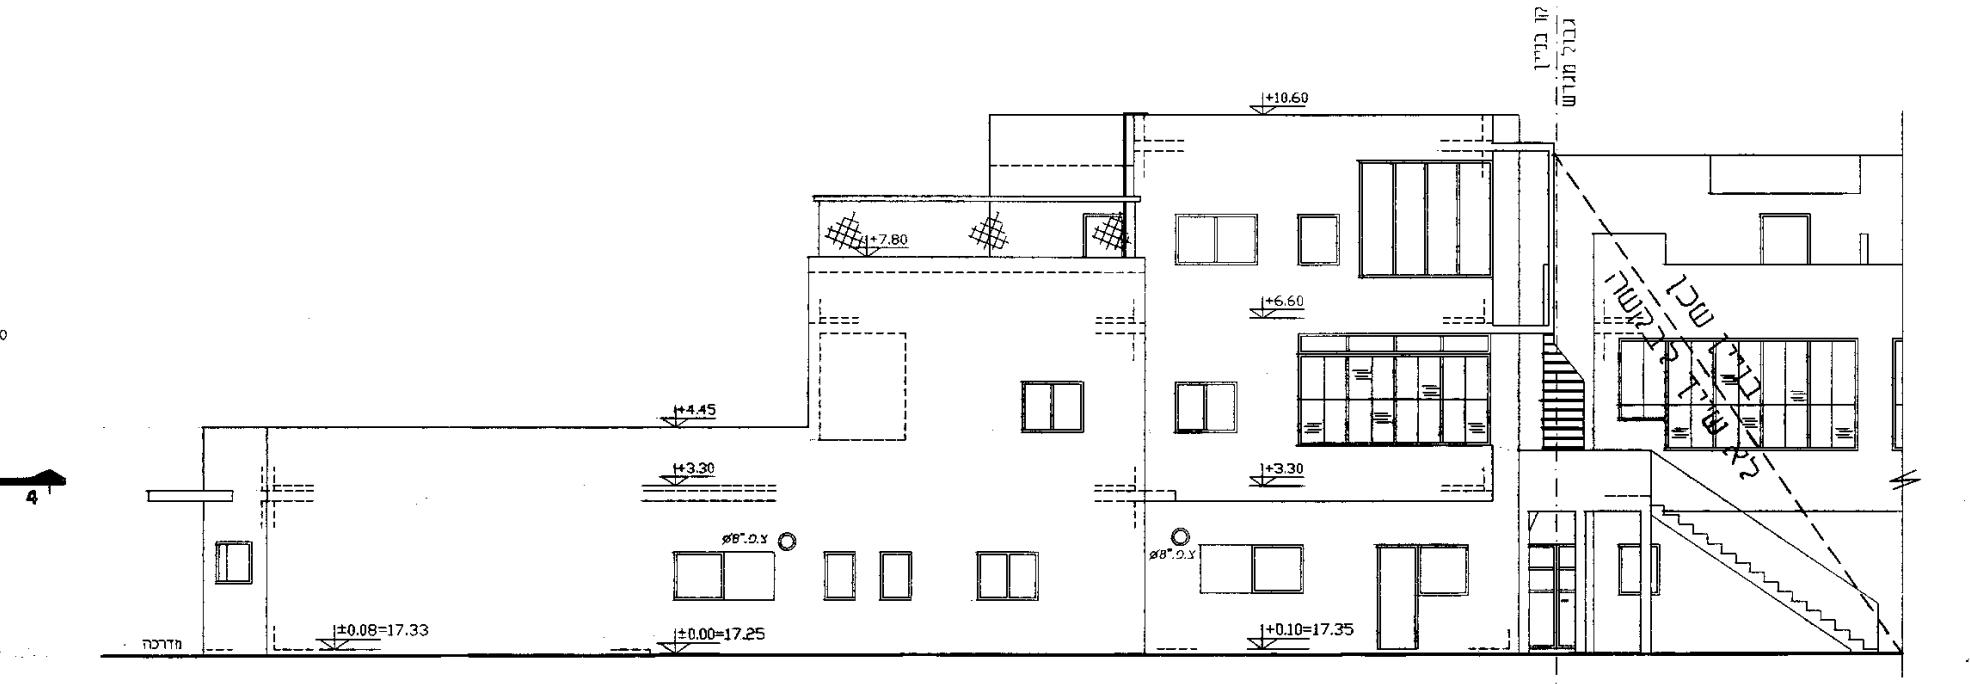

בניין שכן - לא שייך לבקשה

חזית מערבית
קנ"מ: 1:100

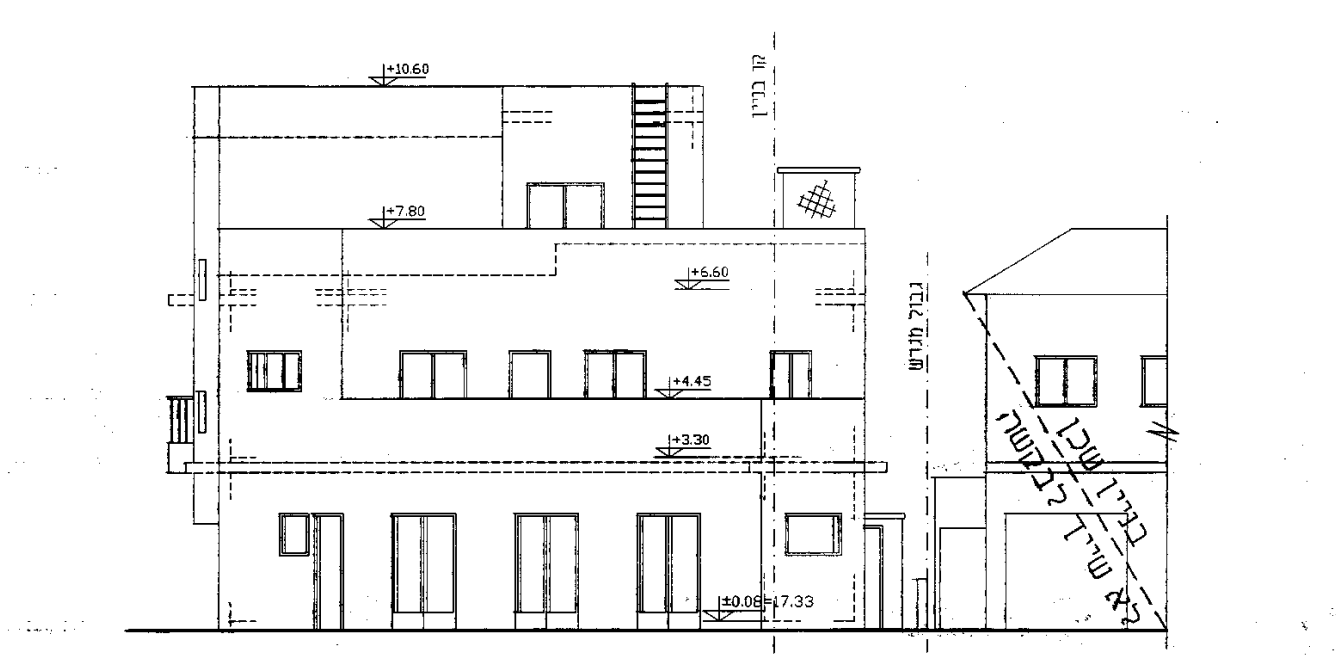

בניין שכן - לא שייך לבקשה

חזית צפונית
קנ"מ: 1:100

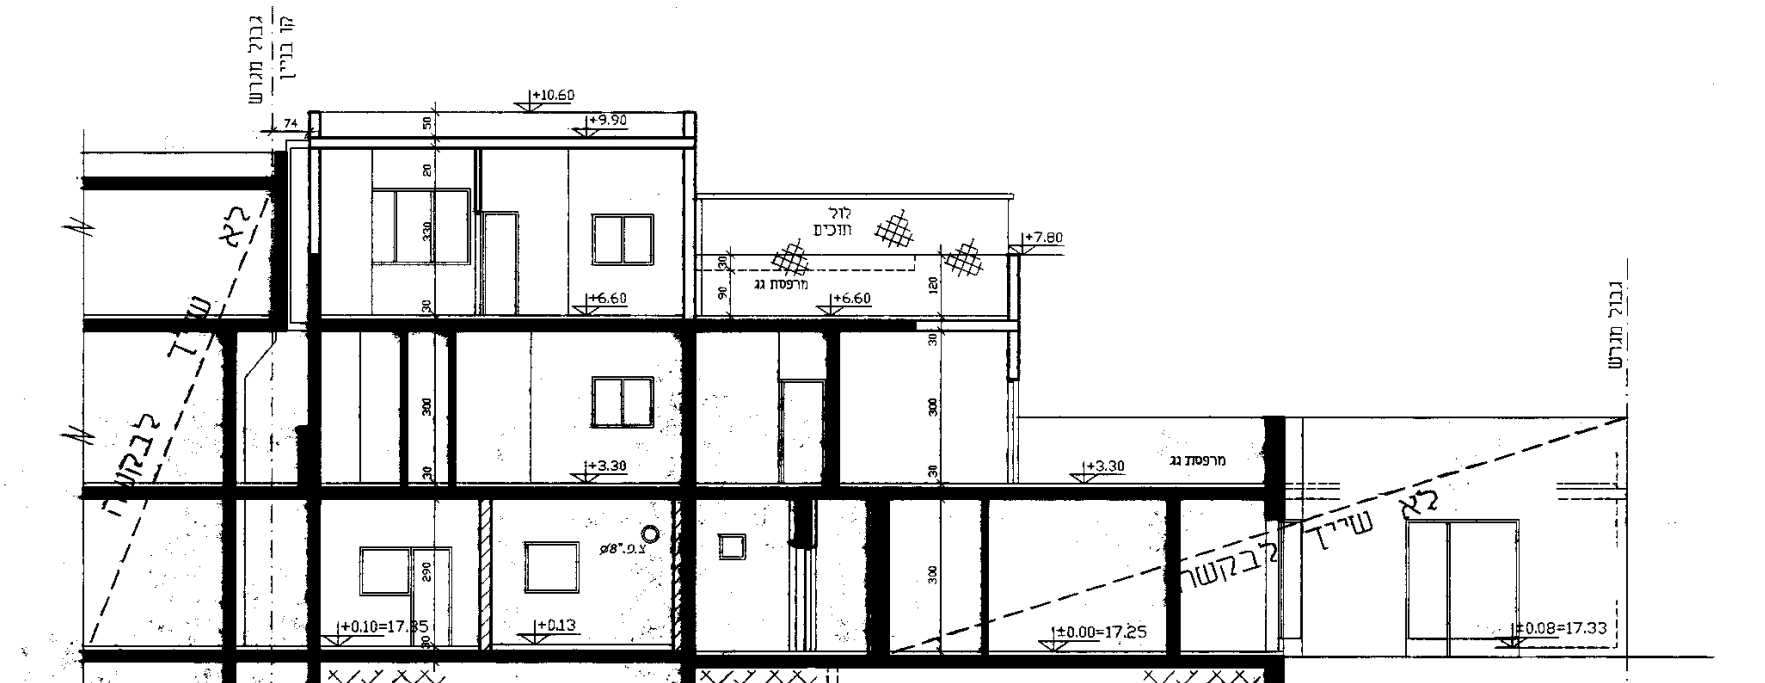

לא שייך לבקשה

חתך ב-ב
קנ"מ: 1:100

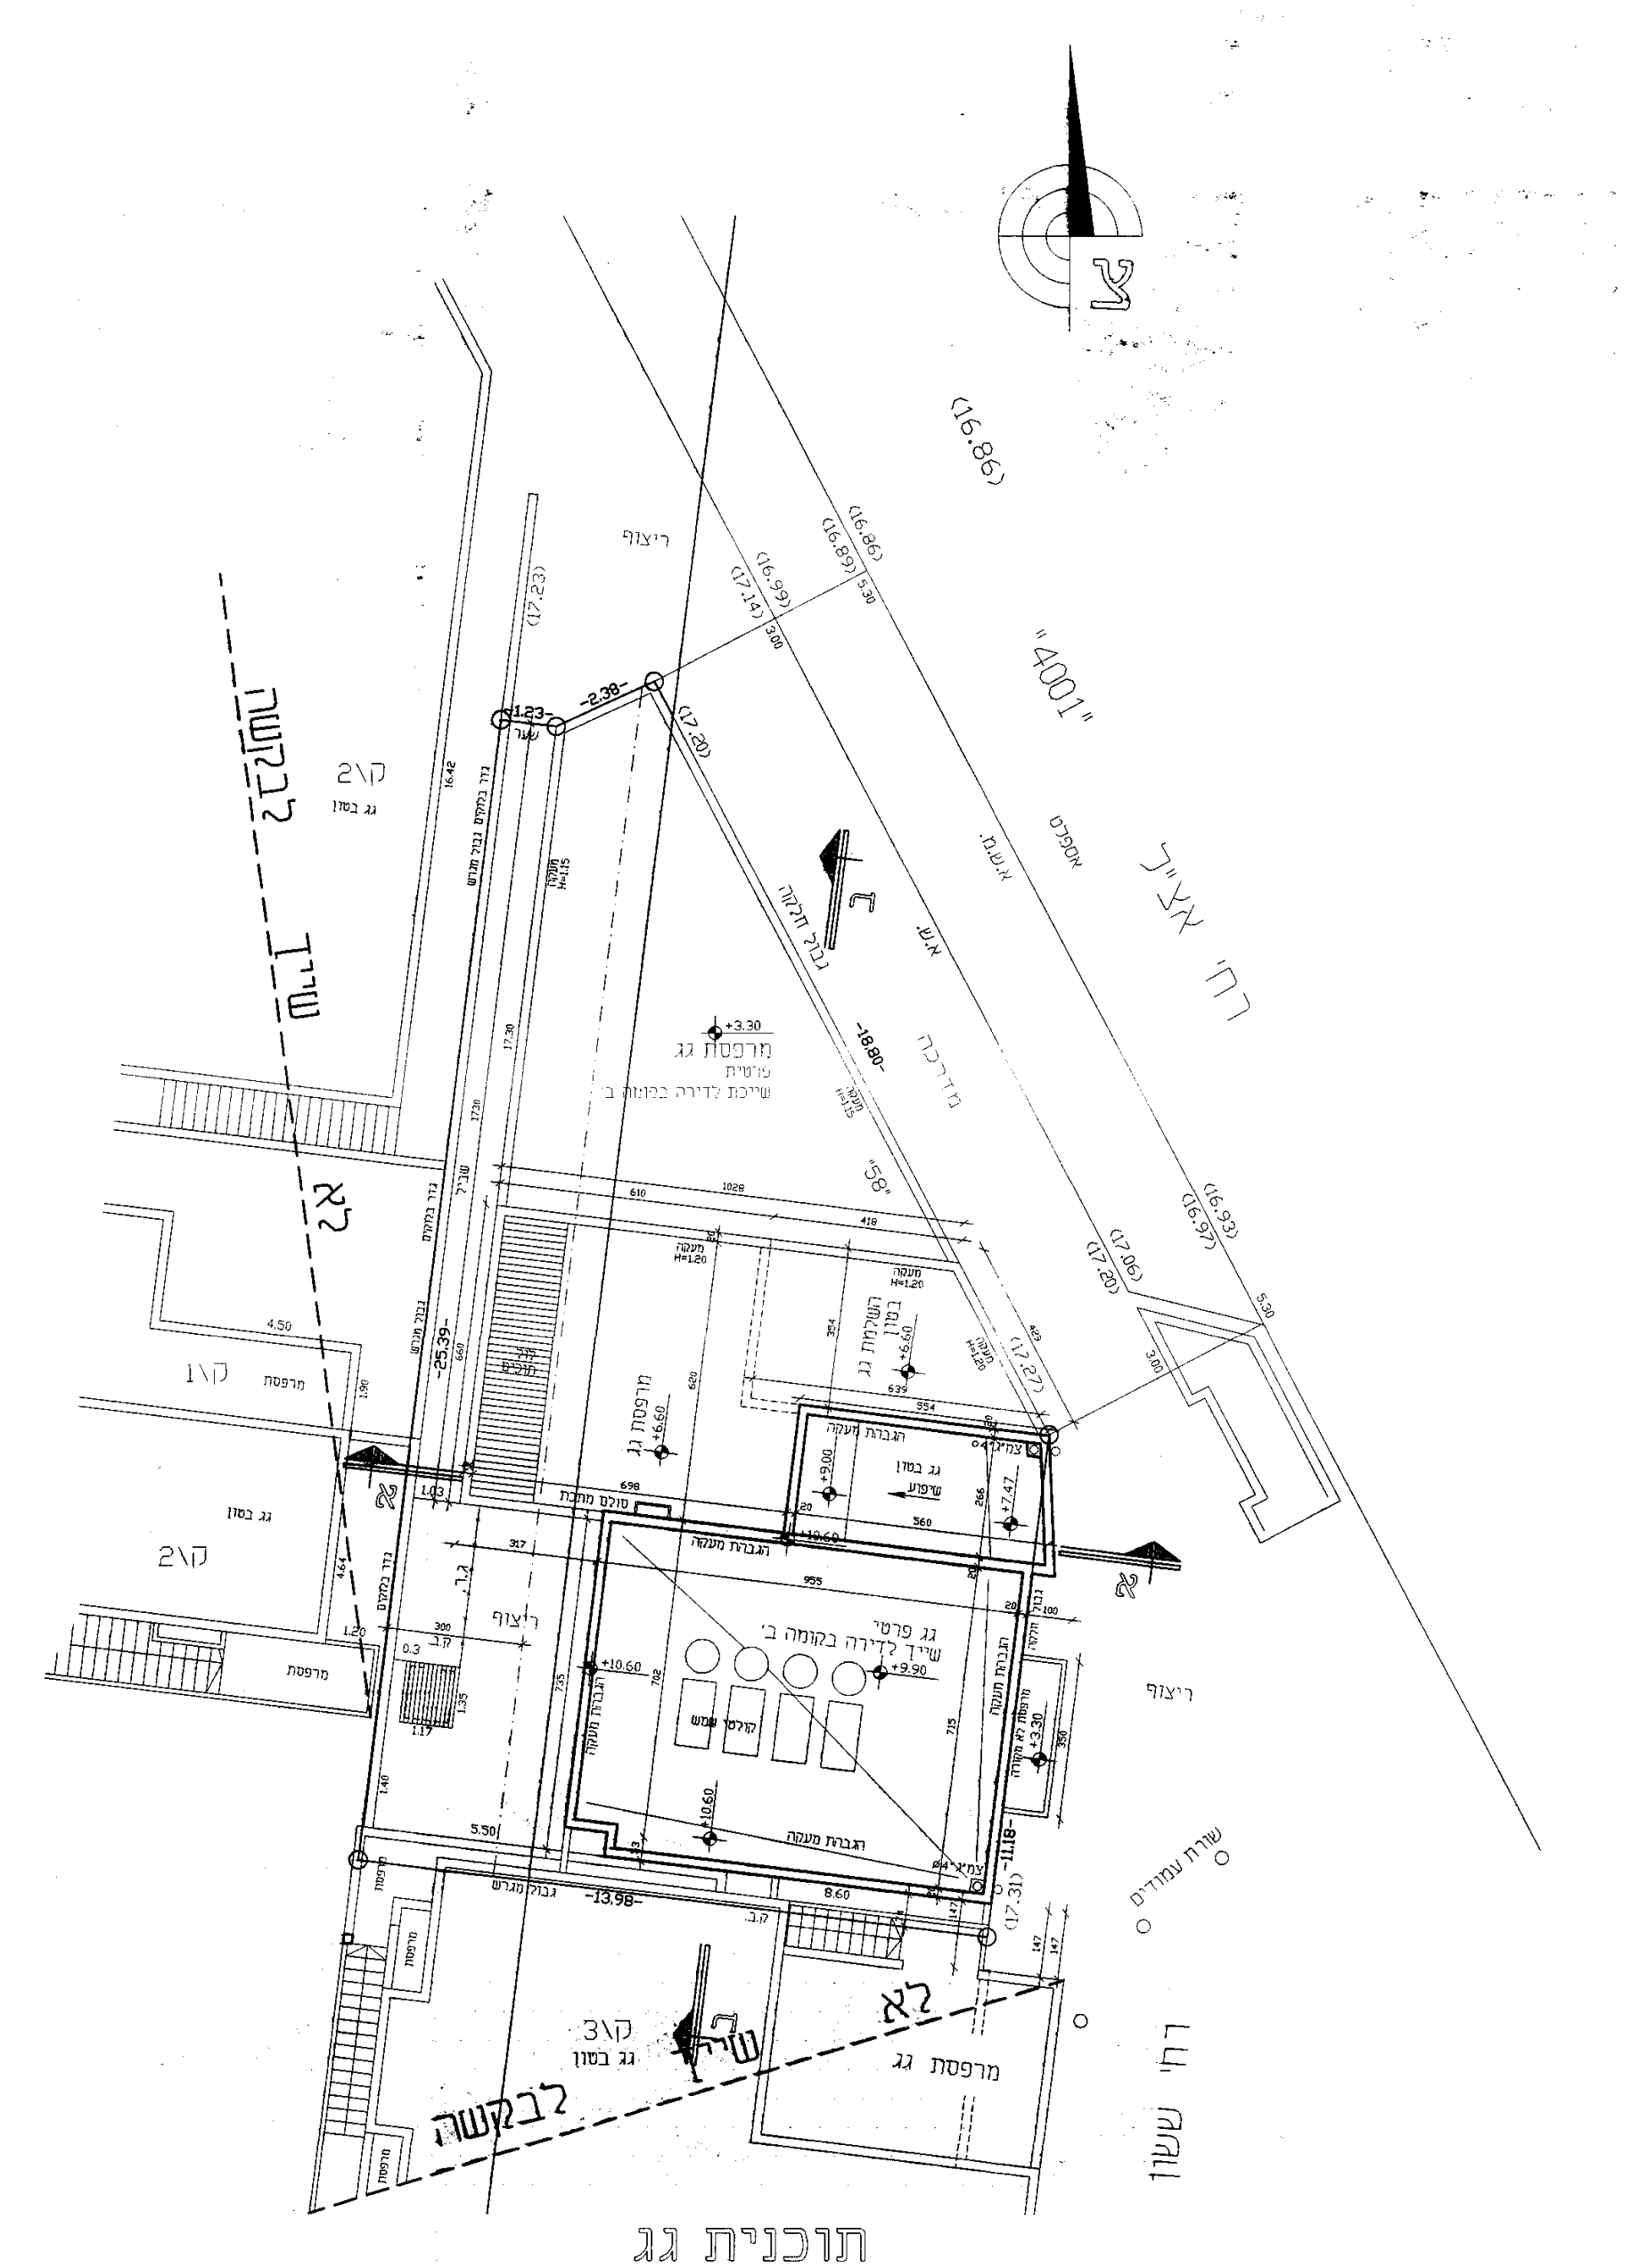

צ
(16.86)
"4001"
רח' אצ"ל
ק\2
ק\1
ק\3
לא שייך לבקשה
מרפסת גג פרטית שייכת לדירה בקומה ב'
רח' ששון

תוכנית גג
קנ"מ: 1:100

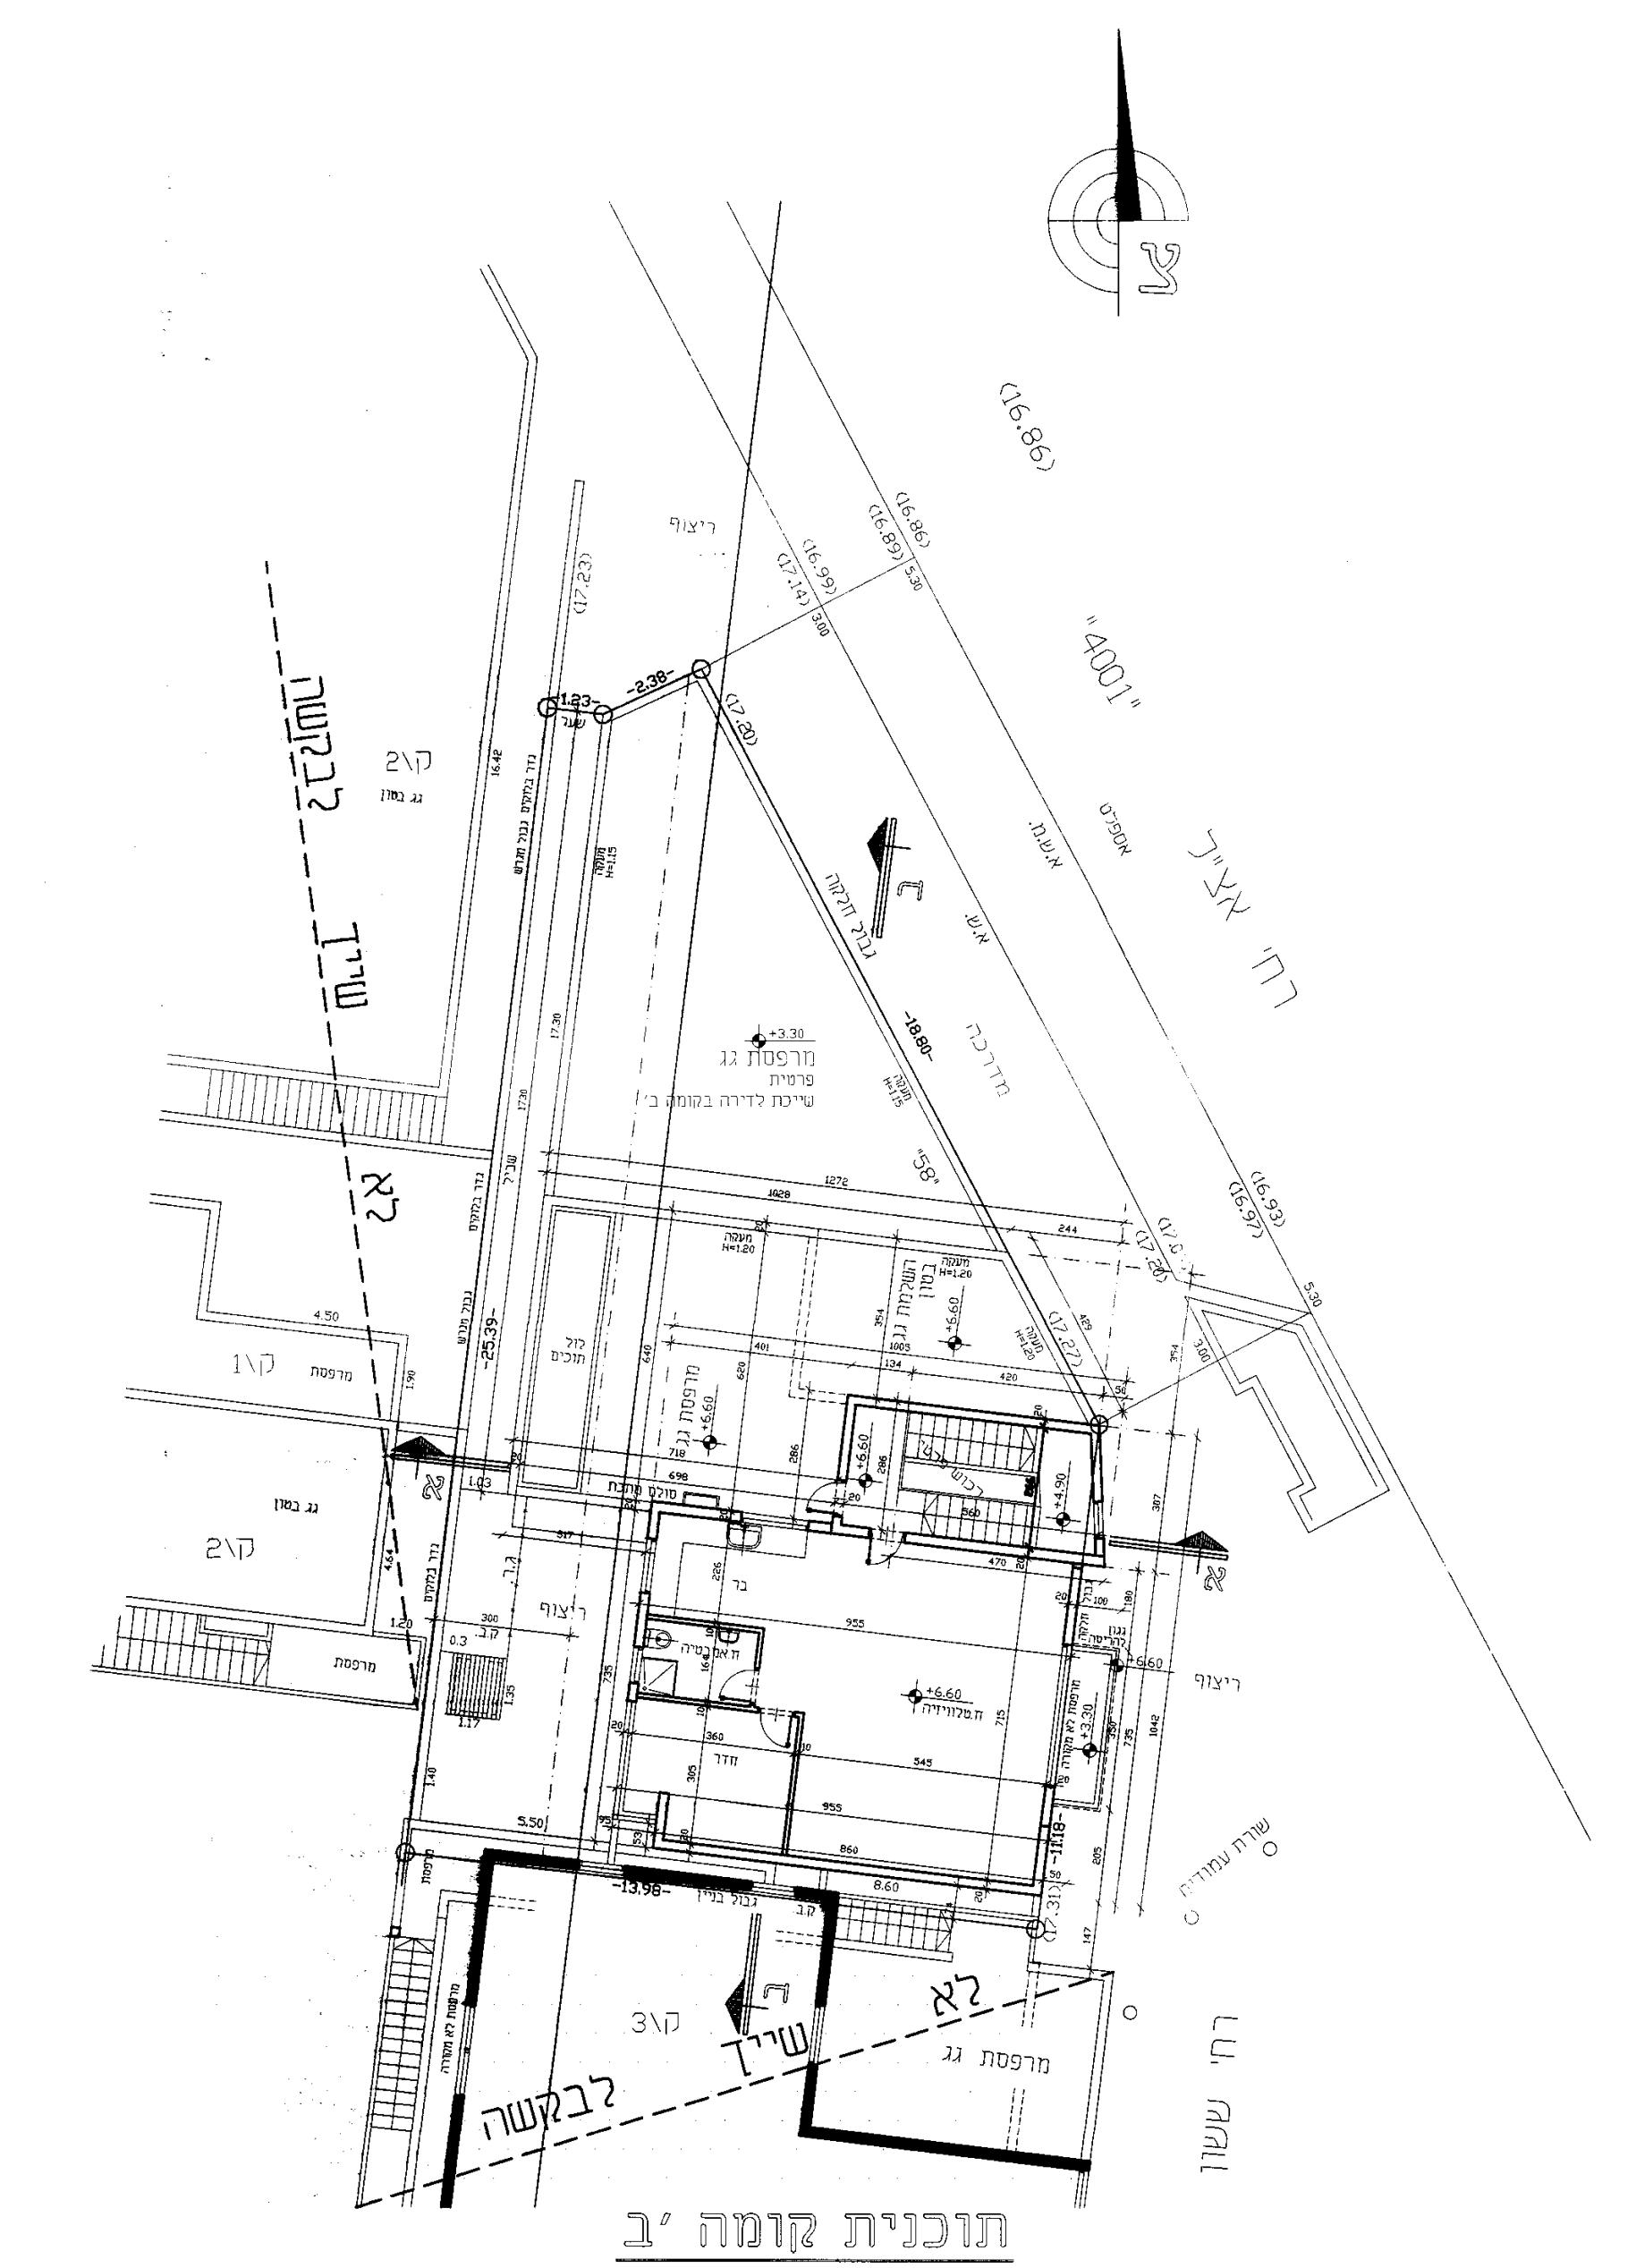

צ
(16.86)
"4001"
רח' אצ"ל
ק\2
ק\1
ק\3
לא שייך לבקשה
רח' ששון

תוכנית קומה 'ב
קנ"מ: 1:100

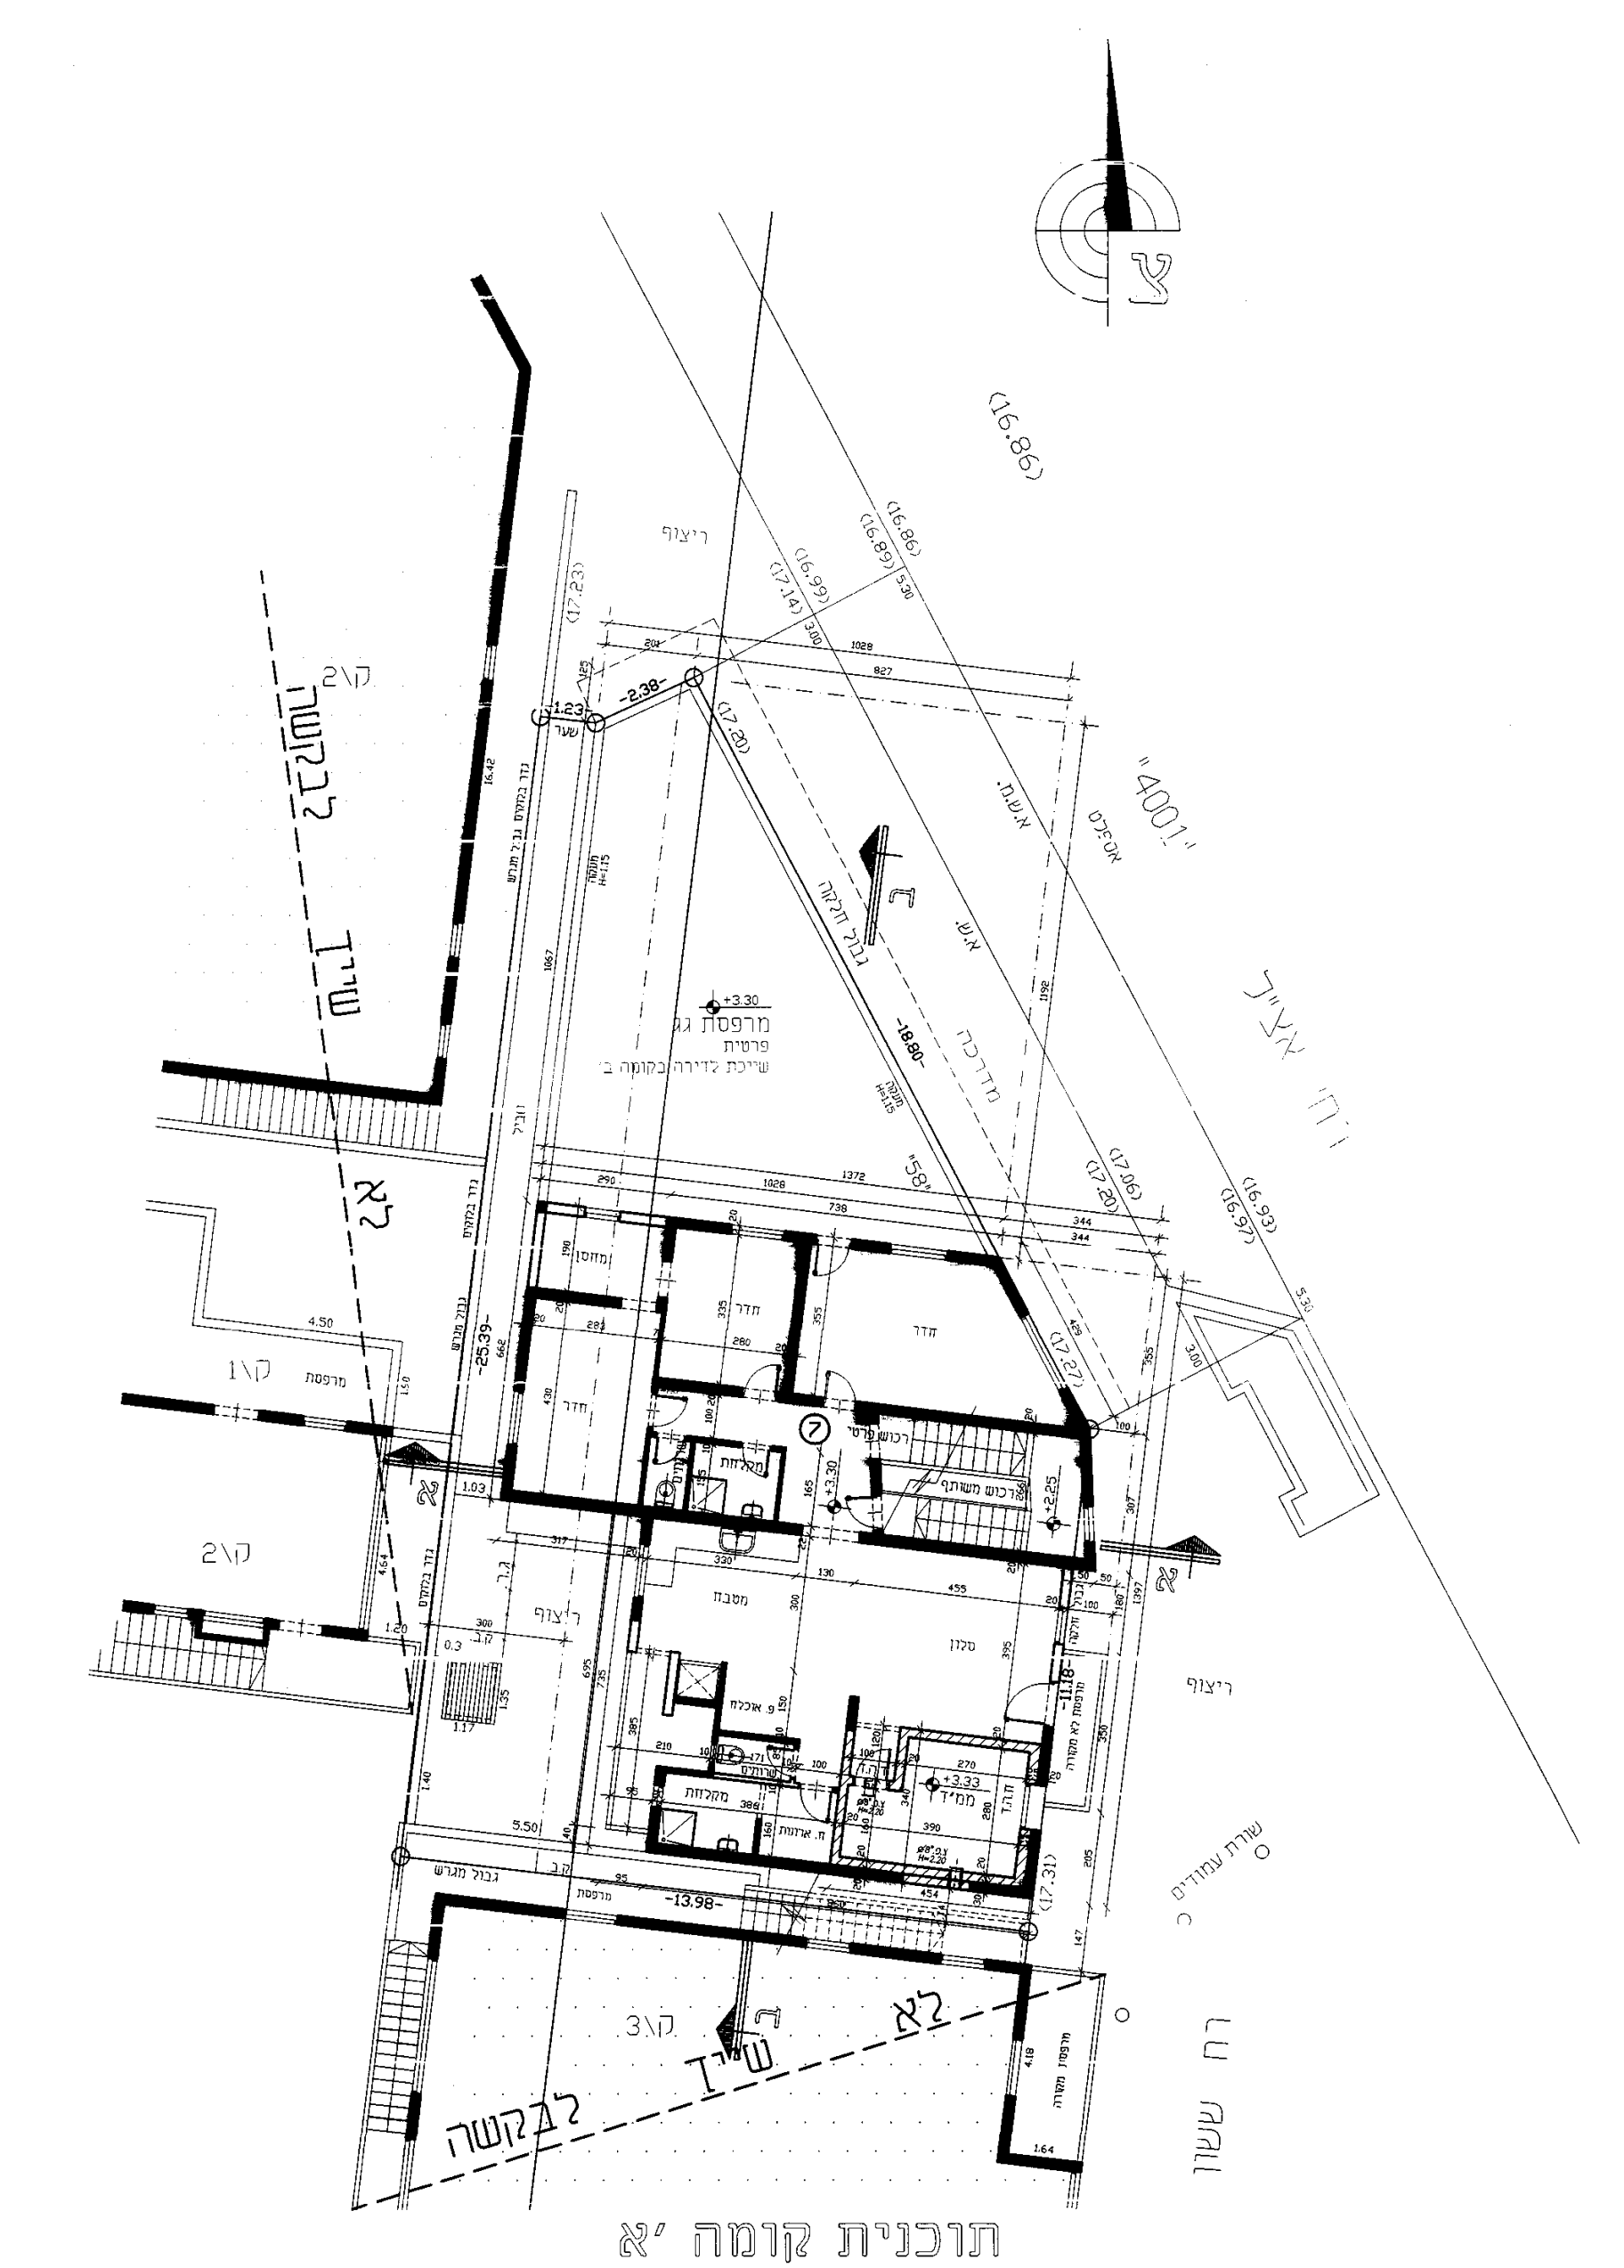

צ
(16.86)
"4001"
רח' אצ"ל
ק\2
ק\1
ק\3
לא שייך לבקשה
רח' ששון

תוכנית קומה 'א
קנ"מ: 1:100

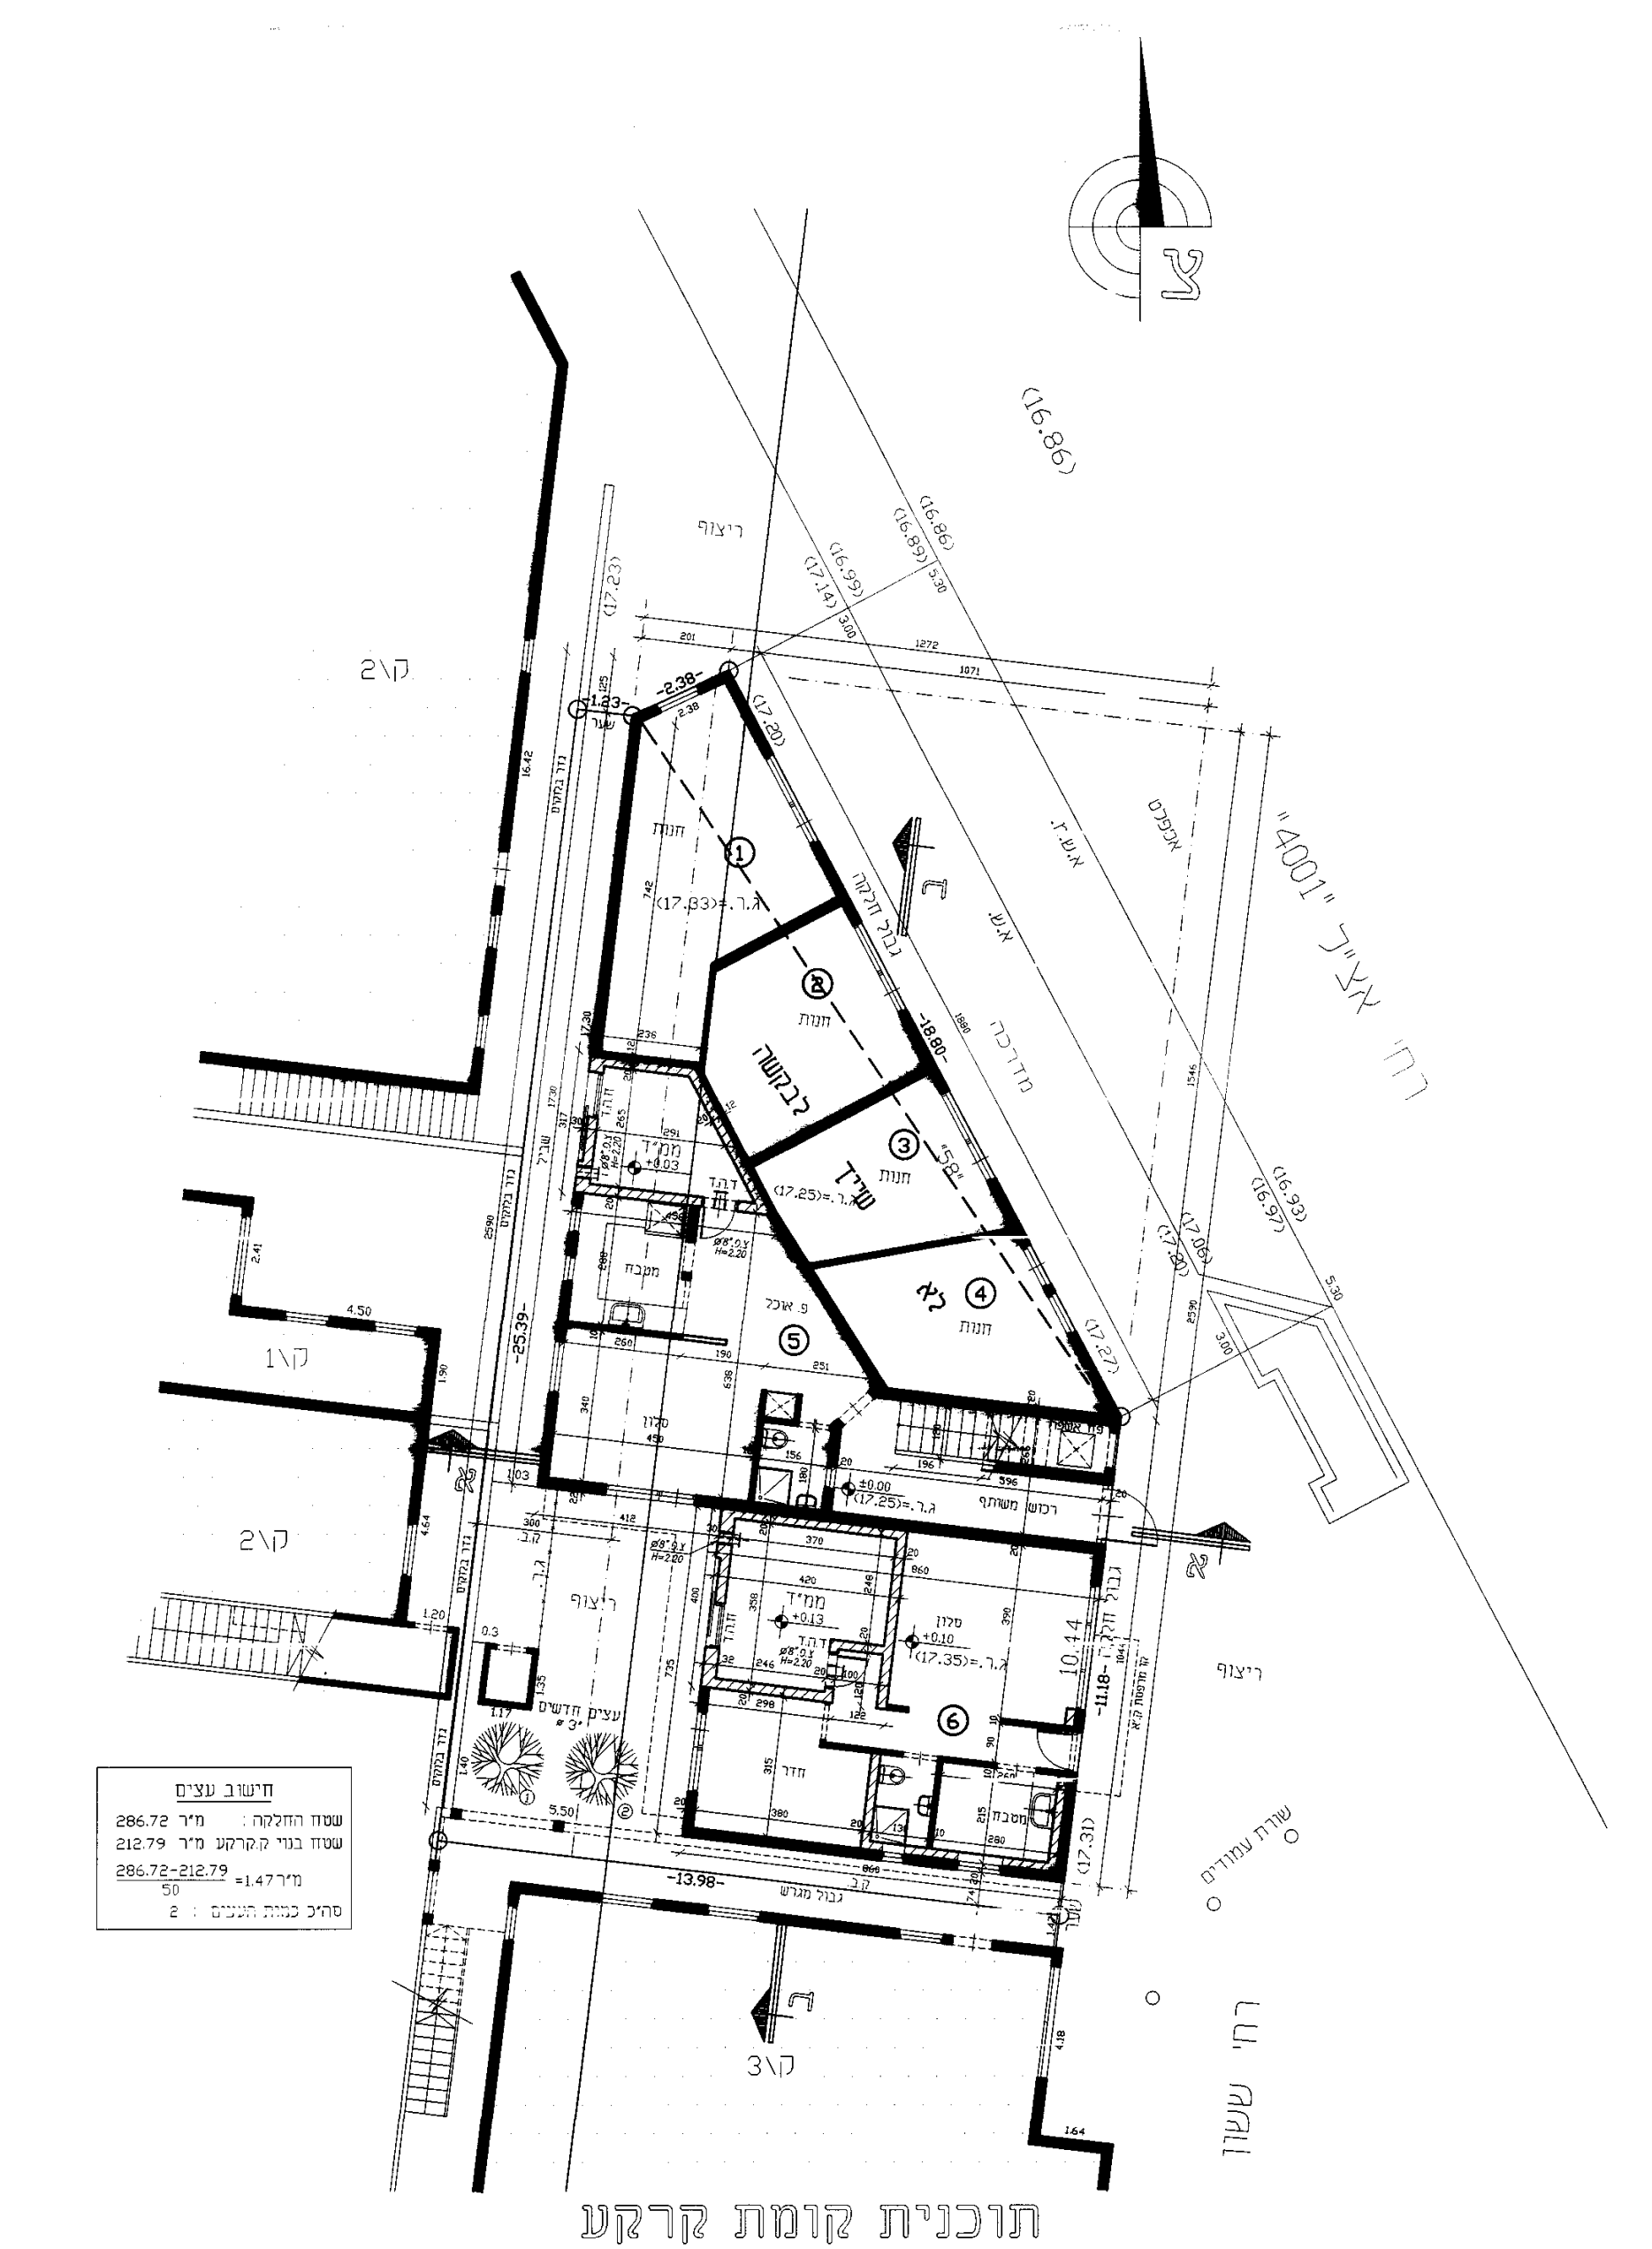

צ
(16.86)
"4001"
רח' אצ"ל
ק\2
ק\1
ק\3
לבקשה
שייך
רח' ששון

תוכנית קומת קרקע
קנ"מ: 1:100

חישוב שטחים

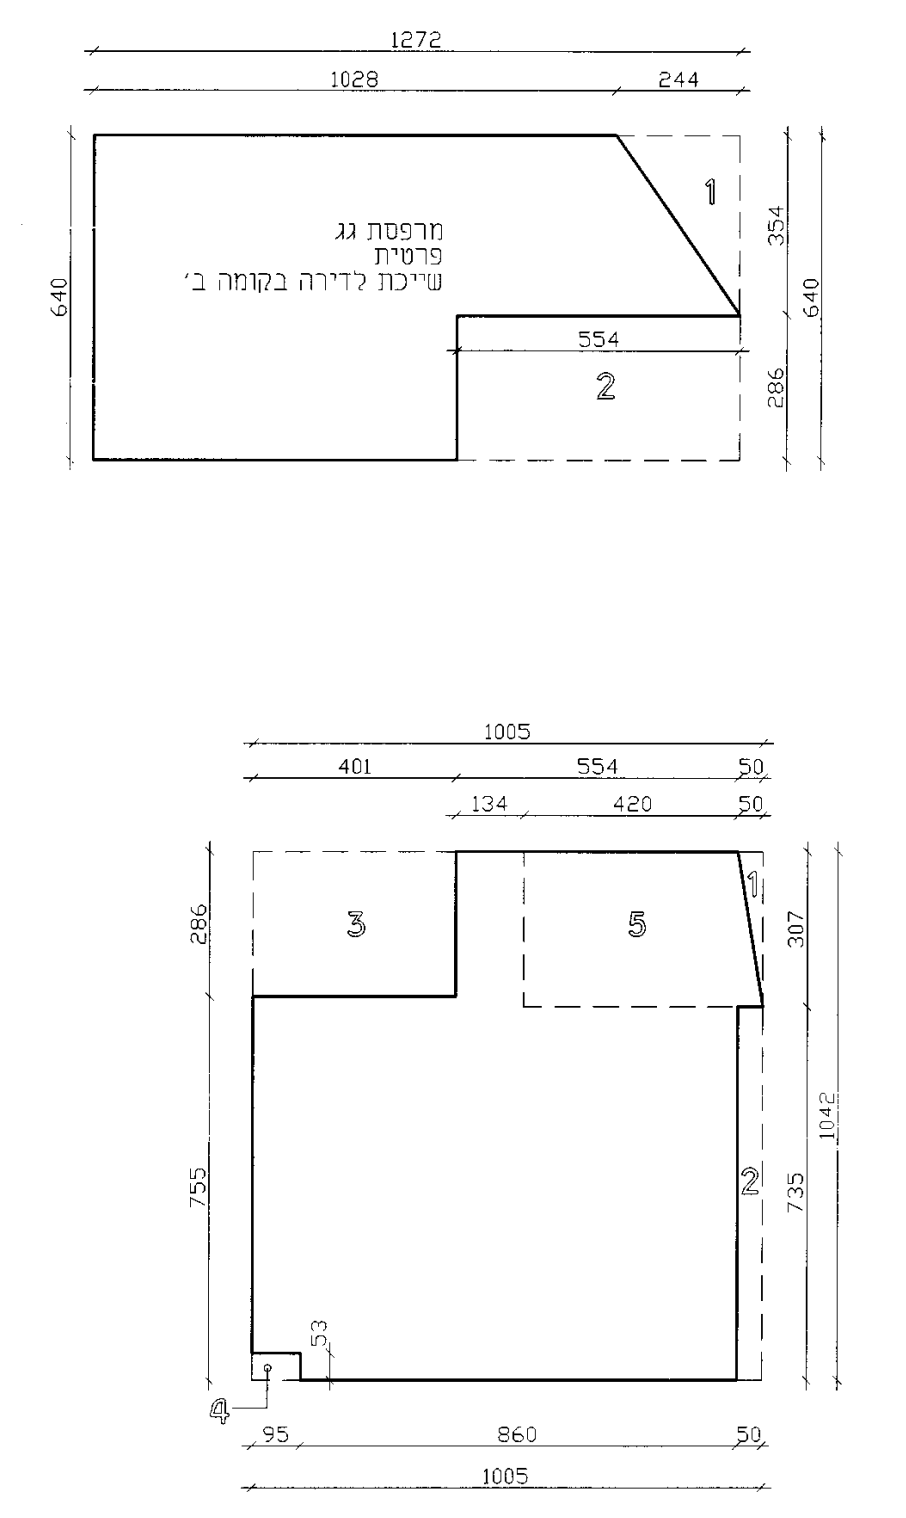

1272
1028
244
1
2
מרפסת גג פרטית שייכת לדירה בקומה ב'
554
1005
3
5
4
860

קומה 'ב

שטח מסגרת : 10.05 × 10.42 = 104.72

הורדות :
1) 0.5 × 3.07/2 = 0.77
2) 0.5 × 7.35 = 3.68
3) 2.86 × 4.01 = 11.47
4) 0.95 × 0.53 = 0.50
5) (4.20+4.70)/2X3.07 = 13.66 : חדר מדרגות

סה"כ הורדות : 30.08

סה"כ שטח עיקרי : 104.72 - 30.08 = 74.64

שטח מרפסת גג ק.'ב

שטח מסגרת : 12.72 × 6.62 = 84.21

הורדות :
1) 2.44 × 3.53/2 = 4.31
2) 5.54 × 2.87 = 15.90
3) 9.55 × 0.22 = 2.10

סה"כ שטח מרפסת : 61.90

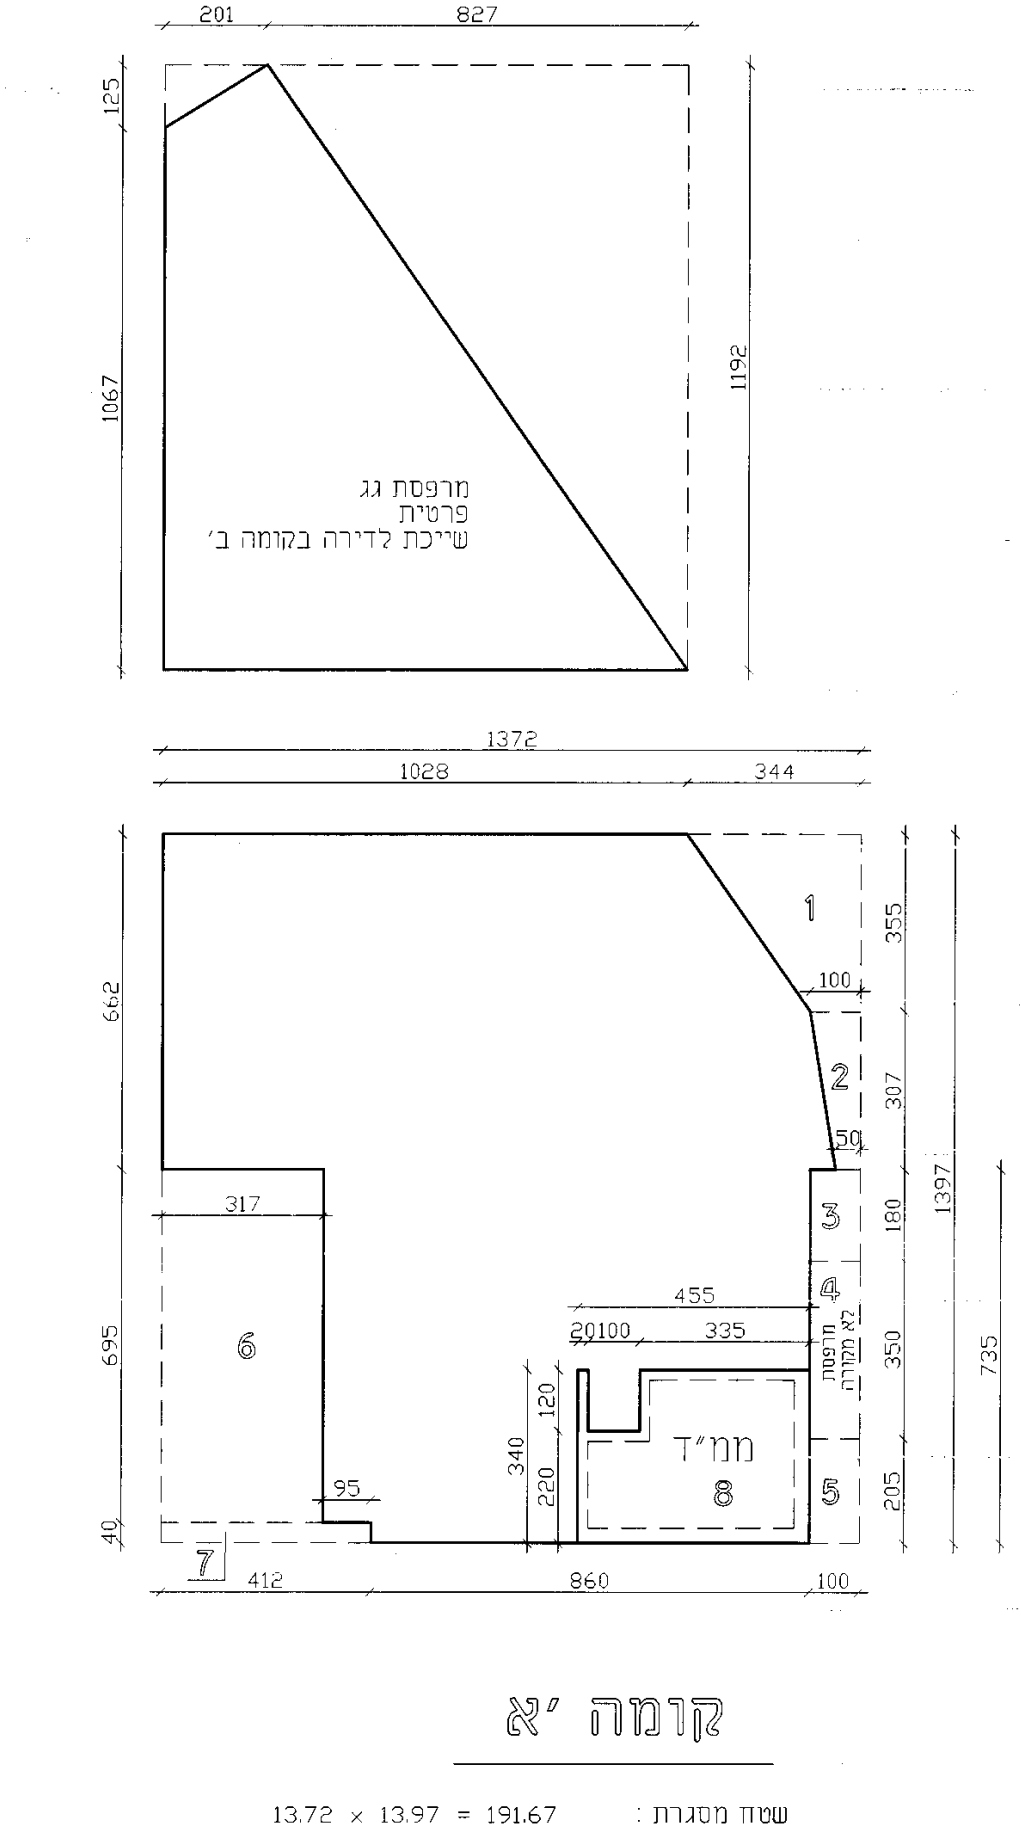

1028
201
827
מרפסת גג פרטית שייכת לדירה בקומה ב'
1372
1029
344
6
ממ"ד 8
7
412
860
100

קומה 'א

שטח מסגרת : 13.72 × 13.97 = 191.67

הורדות :
1) (3.44+1.00)/2 × 3.55 = 7.88
2) (1.00+0.50)/2 × 3.07 = 2.30
3) 1.80 × 1.00 = 1.80
4) 3.50 × 1.00 = 3.50 : מרפסת לא מקורה
5) 2.05 × 1.00 = 2.05
6) 3.17 × 6.95 = 22.03
7) 0.4 × 4.12 = 1.65
8) 4.55X3.40-1.20X1.00 =14.27 : שטח ממ"ד
7.50 : סה"כ שטח להורדה

סה"כ הורדות : 48.71

סה"כ שטח עיקרי : 191.67 - 48.71 = 142.96

שטח קיים לפי היתר : 103.89
סה"כ שטח תוספת החדשה : 142.96 - 103.89 = 39.07

שטח מרפסת גג ק.'א

שטח מסגרת : 10.28 × 11.92 = 122.54

הורדות :
1) 8.27 × 11.92/2 = 49.29
2) 2.01 × 1.25/2 = 1.26

סה"כ שטח מרפסת : 71.99

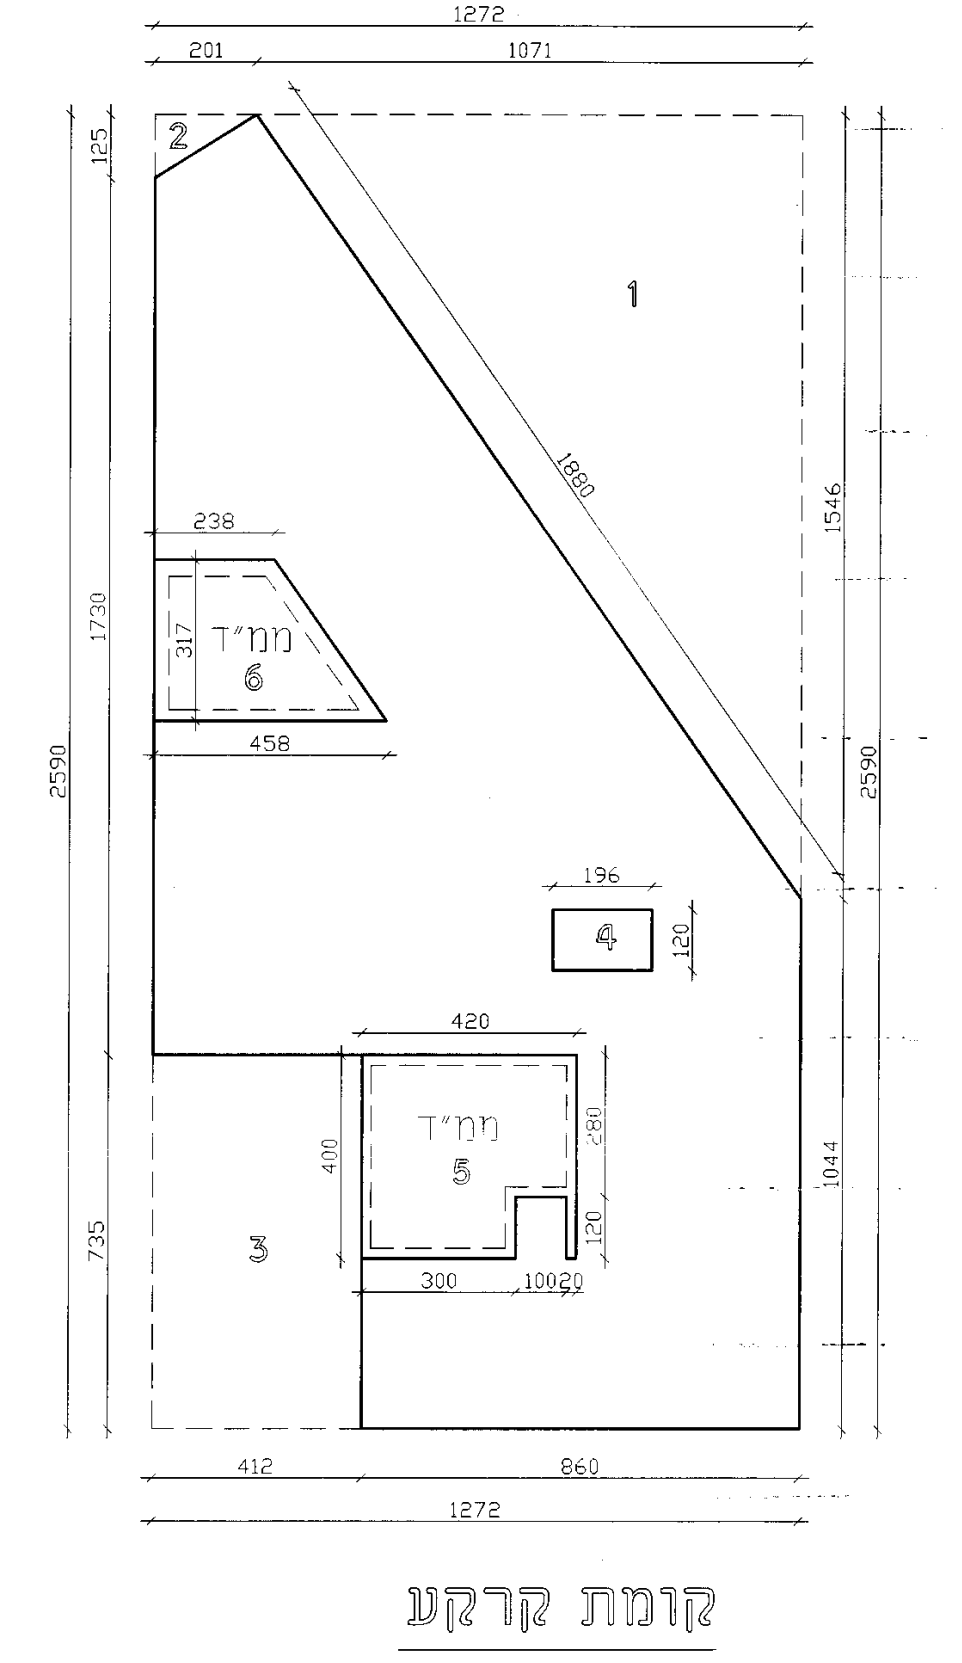

1272
201
1071
2
1
1880
6
ממ"ד 5
4
3
420
300
412
860
1272

קומת קרקע

שטח מסגרת : 12.72 × 25.90 = 329.49

הורדות :
1) 10.71 × 15.46 /2 = 82.79
2) 1.25 × 2.01 /2 =1.26
3) 7.35 × 4.12 = 30.28
4) 1.96 × 1.20 =- 2.35 : שטח מדרגות
מתחת לגובה (H=+1.20)
5) 4.00x4.20-1.00X1.20 = 15.60 : שטח ממ"ד
7.50 : סה"כ שטח להורדה
6) (2.38+4.58)/2 × 3.17 = 11.03 : שטח ממ"ד
7.50 : סה"כ שטח להורדה

סה"כ הורדות : 131.70

סה"כ שטח עיקרי : 329.49 - 131.70 = 197.79

תל-אביב
גוש : 6135
כתובת : רח' אצ"ל 58 פינת רח' ששון 2
הוכן עבור : משפי יצחקי
מטרת המדידה : היתר בניה
חלקות : 45,44 (חלק)

מפה טופוגרפית
1 : 250

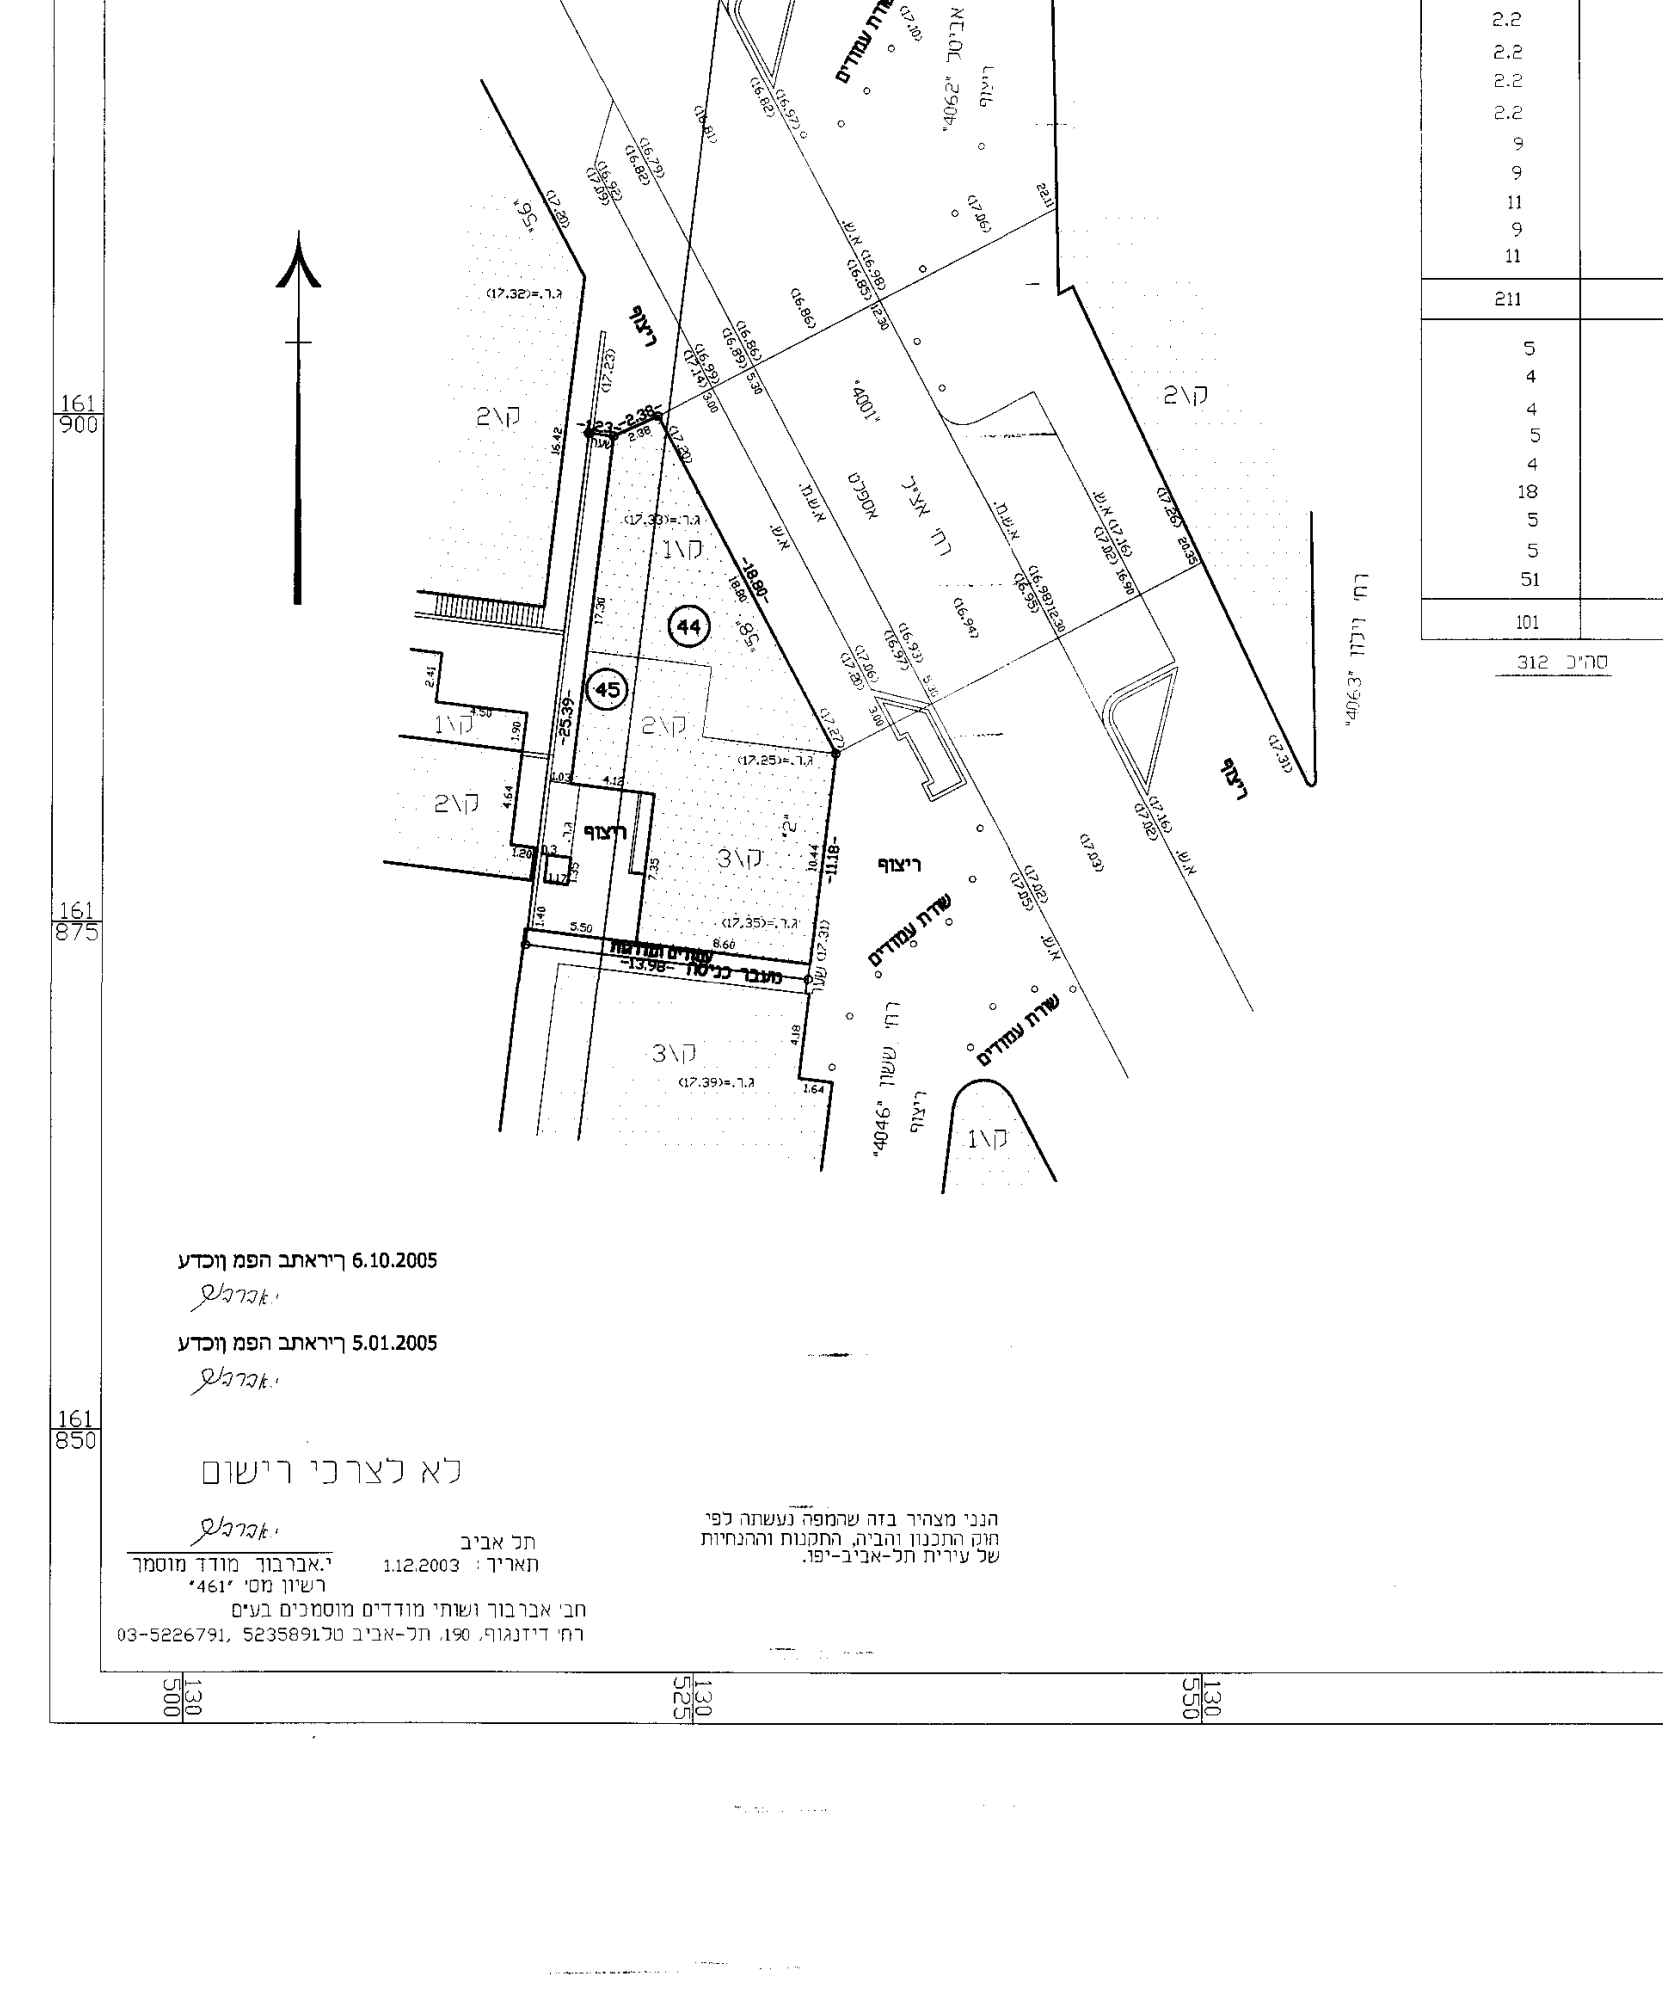

130 500
130 525
130 550
130 575
130 600
161 925
161 900
161 875
161 850
רח' אצ"ל
"4001"
"4062"
"4063"
"4046"
רח' ששון
רח' יונה
שדרת עמודים
ריצוף
ק\1
ק\2
ק\3
44
45

חלקה	שם הבעלים	מס' ת.ז.	שטח חלקה כולה	בעלות בחלקים	בעלות במ"ר
44	יצחקי שושנה	0481321\8	11.476.00	32\11476	32
	יצחקי זהבה	0481322\6		11\11476	11
	יצחקי נפתלי	0481318		108\11476	108
	בן אברהם יאיר	5119051		11\57380	2.2
	דייכובסקי אביגיל	478999		11\57380	2.2
	יצחקי חנה	04449625		11\57380	2.2
	בן אברהם יונתן	004790002		11\57380	2.2
	סטה נאוה	58907663		11\57380	2.2
	מדני מזל	0479542		9\11476	9
	אריאל רחל	0481317		9\11476	9
	ירון נעמי	0481319		11\11476	11
	ירון צפורה	0481320		9\11476	9
	מזרחי חרותה	0481323		11\11476	11
					211
45	בן אברהם מירים	0478998	9.821.00	5\9821	5
	מדני מזל	0479542		4\9821	4
	אריאל רחל	0481317		4\9821	4
	ירון נעמי	0481319		5\9821	5
	ירון צפורה	0481320		4\9821	4
	יצחקי שושנה	0481321\8		18\9821	18
	יצחקי זהבה	0481322\6		5\9821	5
	מזרחי חרותה	0481323		5\9821	5
	יצחקי נפתלי	0481318		51\9821	51
					101

סה"כ 312

בעלות במ"ר : 312
שטח מדוד (מ"ר) : 286.72 (188.50+98.22)
חלקה44 188.50מ"ר
חלקה45 98.22 מ"ר

שטח מגרש משני : ____
שטח להפקעה : ____

תרשים הסביבה 1:1250

6.10.2005 ריאתב הפמ ןוכדע
5.01.2005 ריאתב הפמ ןוכדע

לא לצרכי רישום

תל אביב
תאריך : 1.12.2003
י.אברבור מודד מוסמך
רשיון מס' "461"
חב' אברבור ושותי מודדים מוסמכים בעים
רח' דיזנגוף 190, תל-אביב טל5235891, 03-5226791

הנני מצהיר בזה שהמפה נעשתה לפי חוק התכנון והבניה, התקנות וההנחיות של עיריית תל-אביב-יפו.

הערות:
1. המספרים בסוגריים מציינים גבהים.
2. הגבהים מבוססים על נ.ק. עירונית מס' 188 שגובהה 17.530 מ'.

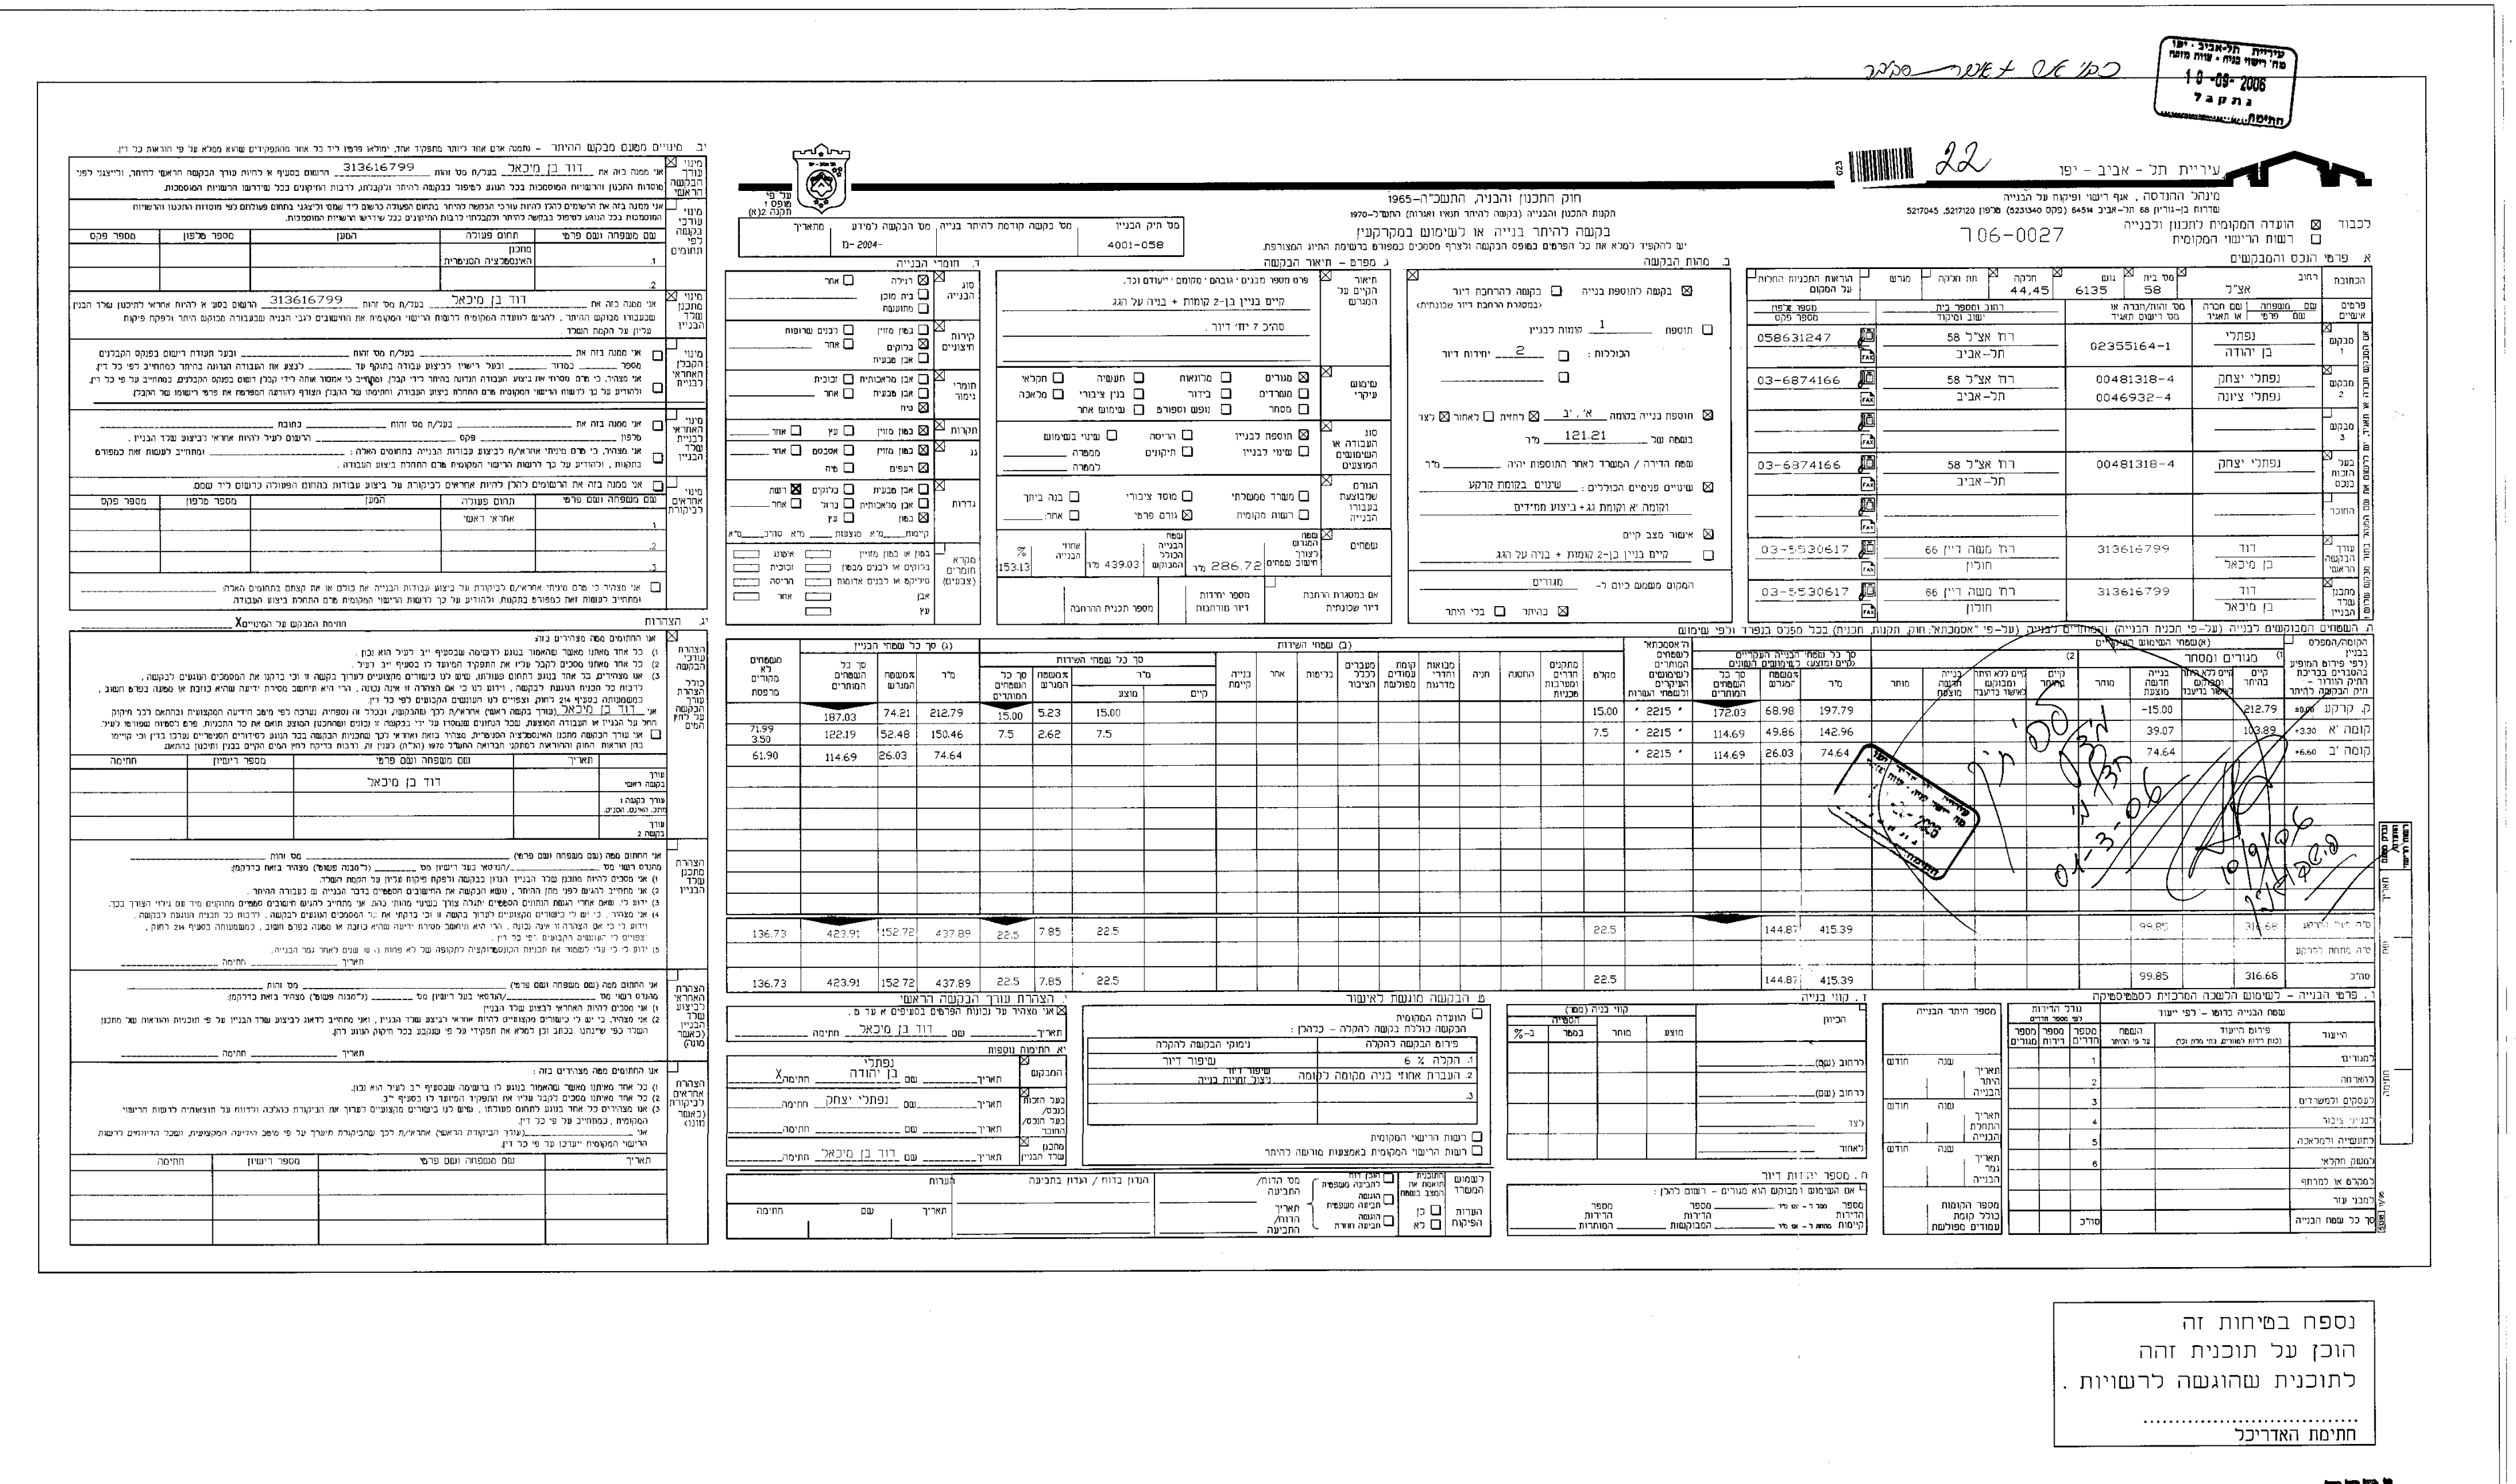

כמו אב + אשר סבלבר

עיריית תל-אביב - יפו
מח' רישוי בניה - שורת מזכה
10-09-2006
נתקבל
חתימה

22

עיריית תל - אביב - יפו
מינהל ההנדסה , אגף רישוי ופיקוח על הבנייה
שדרות בן-גוריון 68 תל-אביב 64514 (פקס 5231340) טלפון 5217120, 5217045

חוק התכנון והבניה, התשכ"ה-1965
תקנות התכנון והבניה (בקשה להיתר תנאיו ואגרות) התש"ל-1970
בקשה להיתר בנייה או לשימוש במקרקעין
יש להקפיד למלא את כל הפרטים בטופס הבקשה ולצרף מסמכים במפורט ברשימת התיוג המצורפת.

לכבוד ☒ הוועדה המקומית לתכנון ולבנייה
☐ רשות הרישוי המקומית

706-0027

מס' תיק הבניין	מס' בקשה קודמת להיתר בנייה	מס' הבקשה למידע	מתאריך
4001-058		מ- 2004-	

א. פרטי הנכס והמבקשים

	רחוב	מס' בית	גוש	חלקה	תת חלקה	מגרש	הוראות התכניות החלות על המקום
הכתובת	אצ"ל	58	6135	44,45			

	שם משפחה / שם פרטי	מס' זהות/חברה או מס' רישום תאגיד	רחוב ומספר בית / ישוב ומיקוד	מספר טלפון / מספר פקס
מבקש 1	נפתלי בן יהודה	02355164-1	רח' אצ"ל 58 תל-אביב	058631247
מבקש 2	נפתלי יצחק נפתלי ציונה	00481318-4 0046932-4	רח' אצ"ל 58 תל-אביב	03-6874166
מבקש 3				
בעל הזכות בנכס	נפתלי יצחק	00481318-4	רח' אצ"ל 58 תל-אביב	03-6874166
החוכר				
עורך	דוד	313616799	רח' משה דיין 66	03-5530617

ב. מהות הבקשה
☒ בקשה לתוספת בנייה ☐ בקשה להרחבת דיור (במסגרת הרחבת דיור שכונתית)
☐ תוספת 1 קומות לבניין
הכוללות : ☐ 2 יחידות דיור
☒ תוספת בנייה בקומה א', ב' ☒ לצד ☐ לאחור ☒ לחזית
בשטח של 121.21 מ"ר
שטח הדירה / המשרד לאחר התוספות יהיה ____ מ"ר
☒ שינויים פנימיים הכוללים : שינוים בקומת קרקע
וקומה א' וקומת גג + ביצוע ממ"דים
☒ אישור מצב קיים

ג. מפרט - תיאור הבקשה
תיאור הקיים על המגרש: קיים בניין בן-2 קומות + בניה על הגג
סה"כ 7 יח' דיור .
שימוש עיקרי: ☒ מגורים ☐ משרדים ☐ מסחר ☐ מלונאות ☐ בידור ☐ נופש וספורט ☐ תעשיה ☐ בנין ציבורי ☐ שימוש אחר ☐ חקלאי ☐ מלאכה
סוג העבודה או השימושים המוצעים: ☒ תוספת לבניין ☐ שינוי לבניין ☐ הריסה ☐ תיקונים ☐ שינוי בשימוש
הגורם שמבוצעת בעבורו הבנייה: ☐ משרד ממשלתי ☐ רשות מקומית ☐ מוסד ציבורי ☒ גורם פרטי ☐ בנה ביתך ☐ אחר

ד. חומרי הבנייה
סוג הבנייה: ☒ רגילה ☐ בית מוכן ☐ מתועשת ☐ אחר
קירות חיצוניים: ☐ בטון מזוין ☒ בלוקים ☐ אבן מבנית ☐ לבנים שרופות ☐ אחר
חומרי גימור: ☐ אבן מלאכותית ☐ אבן מבנית ☒ טיח ☐ זכוכית ☐ אחר
תקרות: ☒ בטון מזוין ☐ עץ ☐ אחר
גג: ☒ בטון מזוין ☐ אסבסט ☐ רעפים ☐ פח
גדרות: ☐ אבן מבנית ☐ אבן מלאכותית ☒ בטון ☐ בלוקים ☐ ברזל ☐ עץ

ט. הבקשה כוללת בקשה להקלה - כלהלן :

פירוט הבקשה להקלה	נימוקי הבקשה להקלה
1. הקלה 6 %	שיפור דיור
2. העברת אחוזי בניה מקומה לקומה	שיפור דיור ניצול זכויות בניה
3.	

☐ רשות הרישוי המקומית
☐ רשות הרישוי המקומית באמצעות מורשה להיתר

י. הצהרת עורך הבקשה הראשי
☒ אני מצהיר על נכונות הפרטים בסעיפים א עד ם .
תאריך ____ שם דוד בן מיכאל חתימה ____

יא. חתימות נוספות

	תאריך	שם	חתימה
המבקש		נפתלי בן יהודה	X
בעל הזכות בנכס/ בעל הנכס/ החוכר		נפתלי יצחק	
מתכנן שלד הבניין		דוד בן מיכאל	

נספח בטיחות זה
הוכן על תוכנית זהה
לתוכנית שהוגשה לרשויות .
....
חתימת האדריכל

נבדק

אצ"ל 58

יש לנקוט באמצעים ובקוסטיום להפרדה רעש אקוסטי והתבוננה על סמך הדוחות שלנו בקובץ ועדכני הבקשה פרק 40 .

נחמה עמירב
אחראית תכנון סביבתי
הרשות לאיכות הסביבה
10.9.06

חלון בלי כיס

זיון סביב פתח בקיר

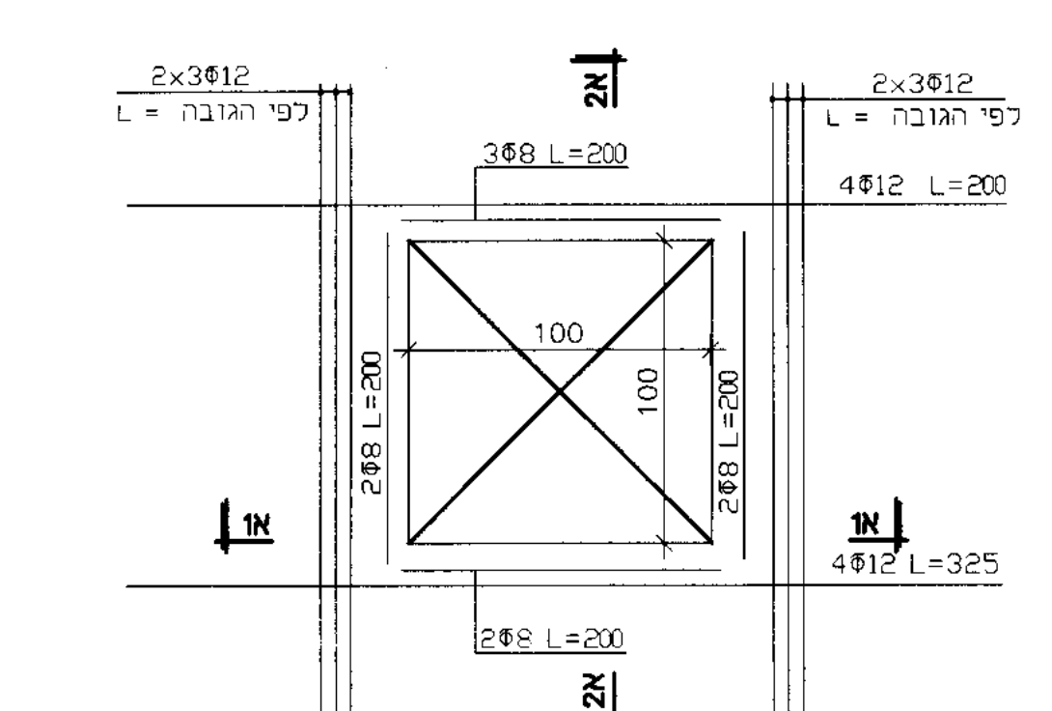
2×3Φ12
L = לפי הגובה
3Φ8 L=200
4Φ12 L=200
100
2Φ8 L=200
4Φ12 L=325
2Φ8 L=200
1א
2א

חתך א1–א1

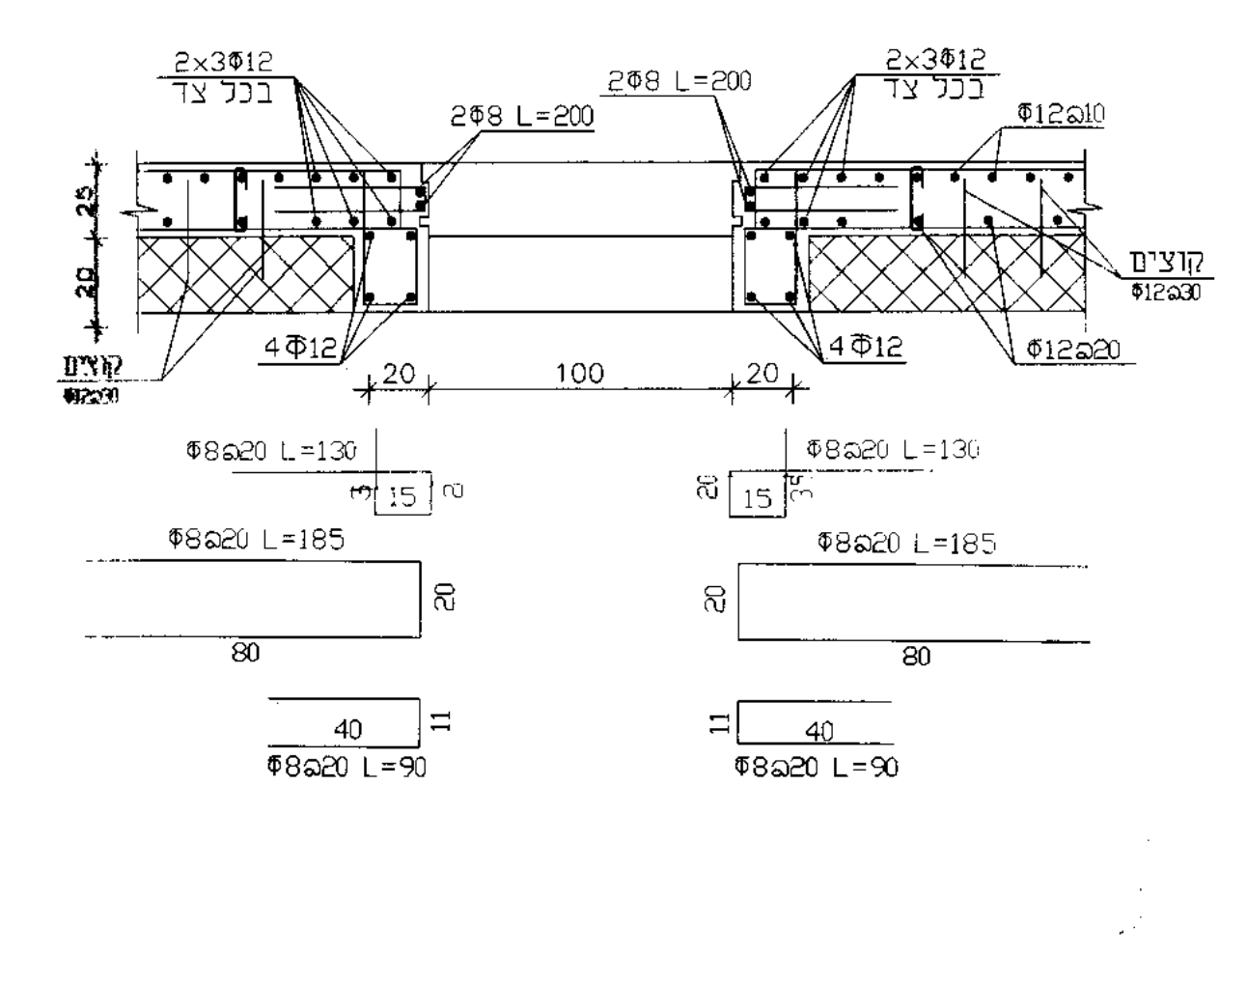
2×3Φ12
בכל צד
2Φ8 L=200
Φ12@10
קוצים
Φ12@30
4Φ12
Φ12@20
Φ8@20 L=130
Φ8@20 L=185
Φ8@20 L=90
20
100
80
40

① חתך אופקי בקיר מרחב מוגן

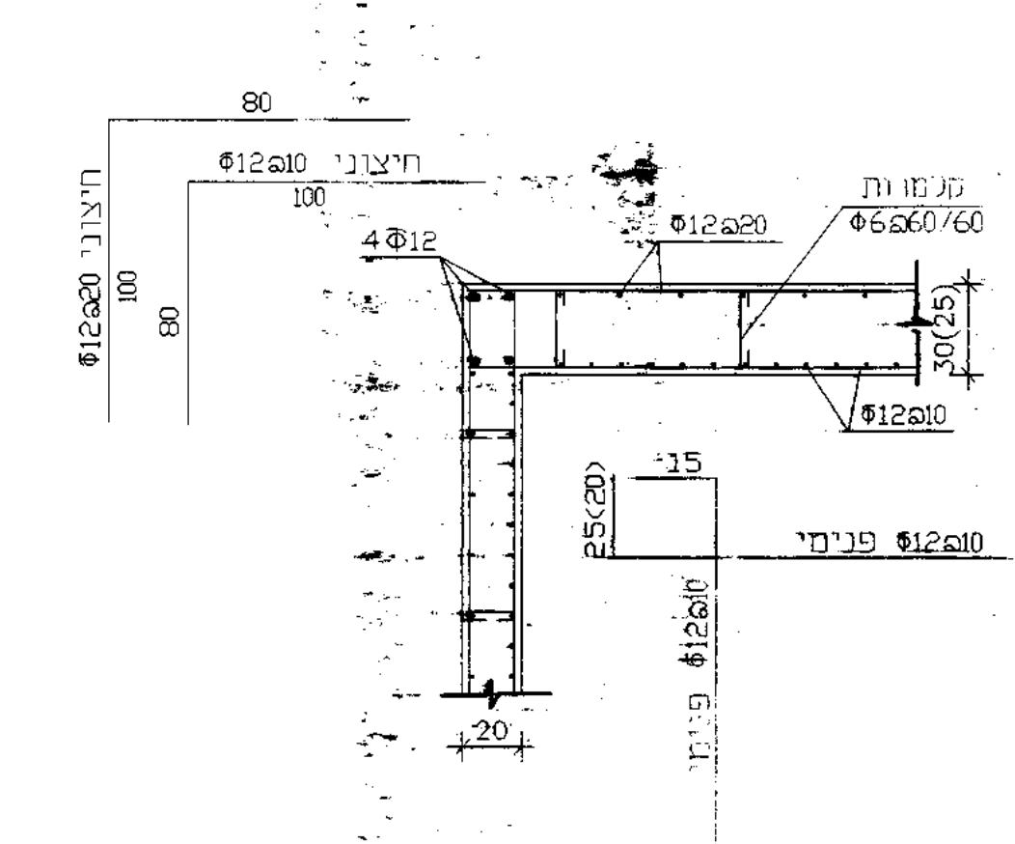
80
Φ12@10 חיצוני
Φ12@20 חיצוני
4Φ12
Φ12@20
קלמרות
Φ6@60/60
Φ12@10
פנימי Φ12@10
Φ12@10 פנימי
30(25)
25(20)
15
20

② פרט ריתום אנכי בין רצפה לקירות

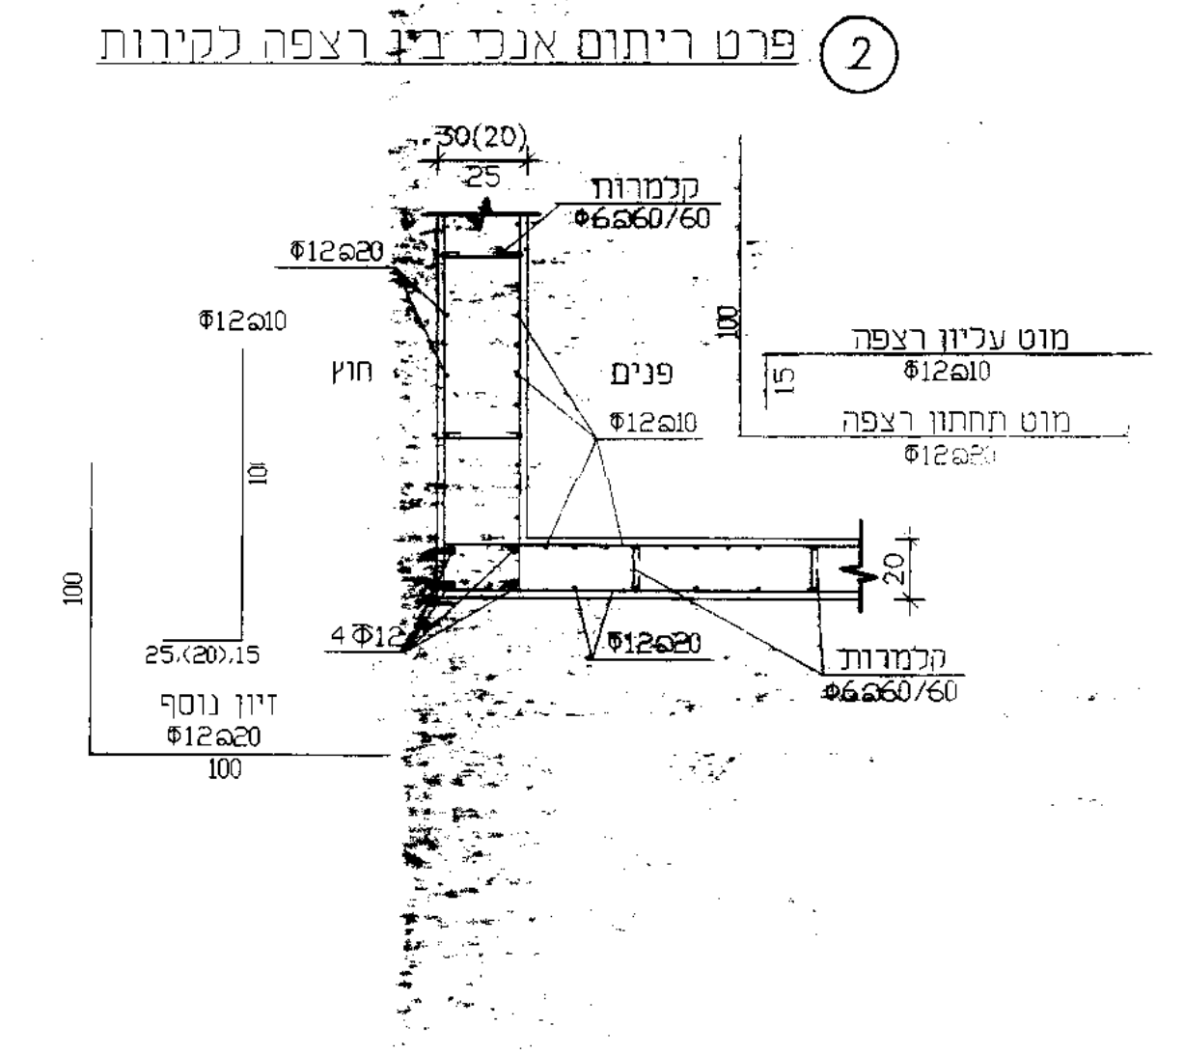
30(20)
25
קלמרות
Φ6@60/60
Φ12@20
Φ12@10
חוץ
פנים
מוט עליון רצפה
Φ12@10
מוט תחתון רצפה
Φ12@20
4Φ12
25.(20).15
זיון נוסף
Φ12@20
100

③ פרט ריתום אנכי בין קיר לגג

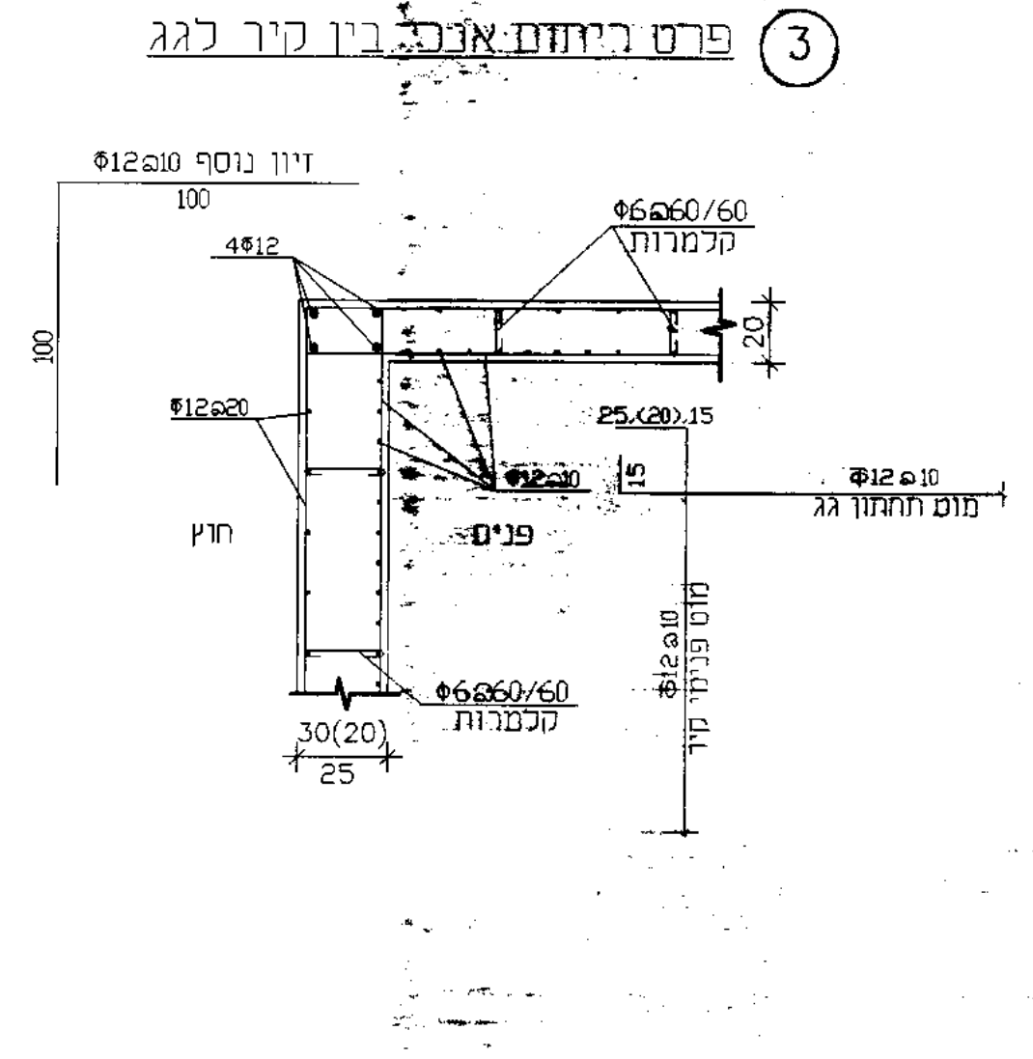
זיון נוסף Φ12@10
100
4Φ12
Φ6@60/60
קלמרות
Φ12@20
חוץ
25.(20).15
Φ12@10
מוט תחתון גג
פנים
מוט פנימי קיר
30(20)
25

חתך א2–א2

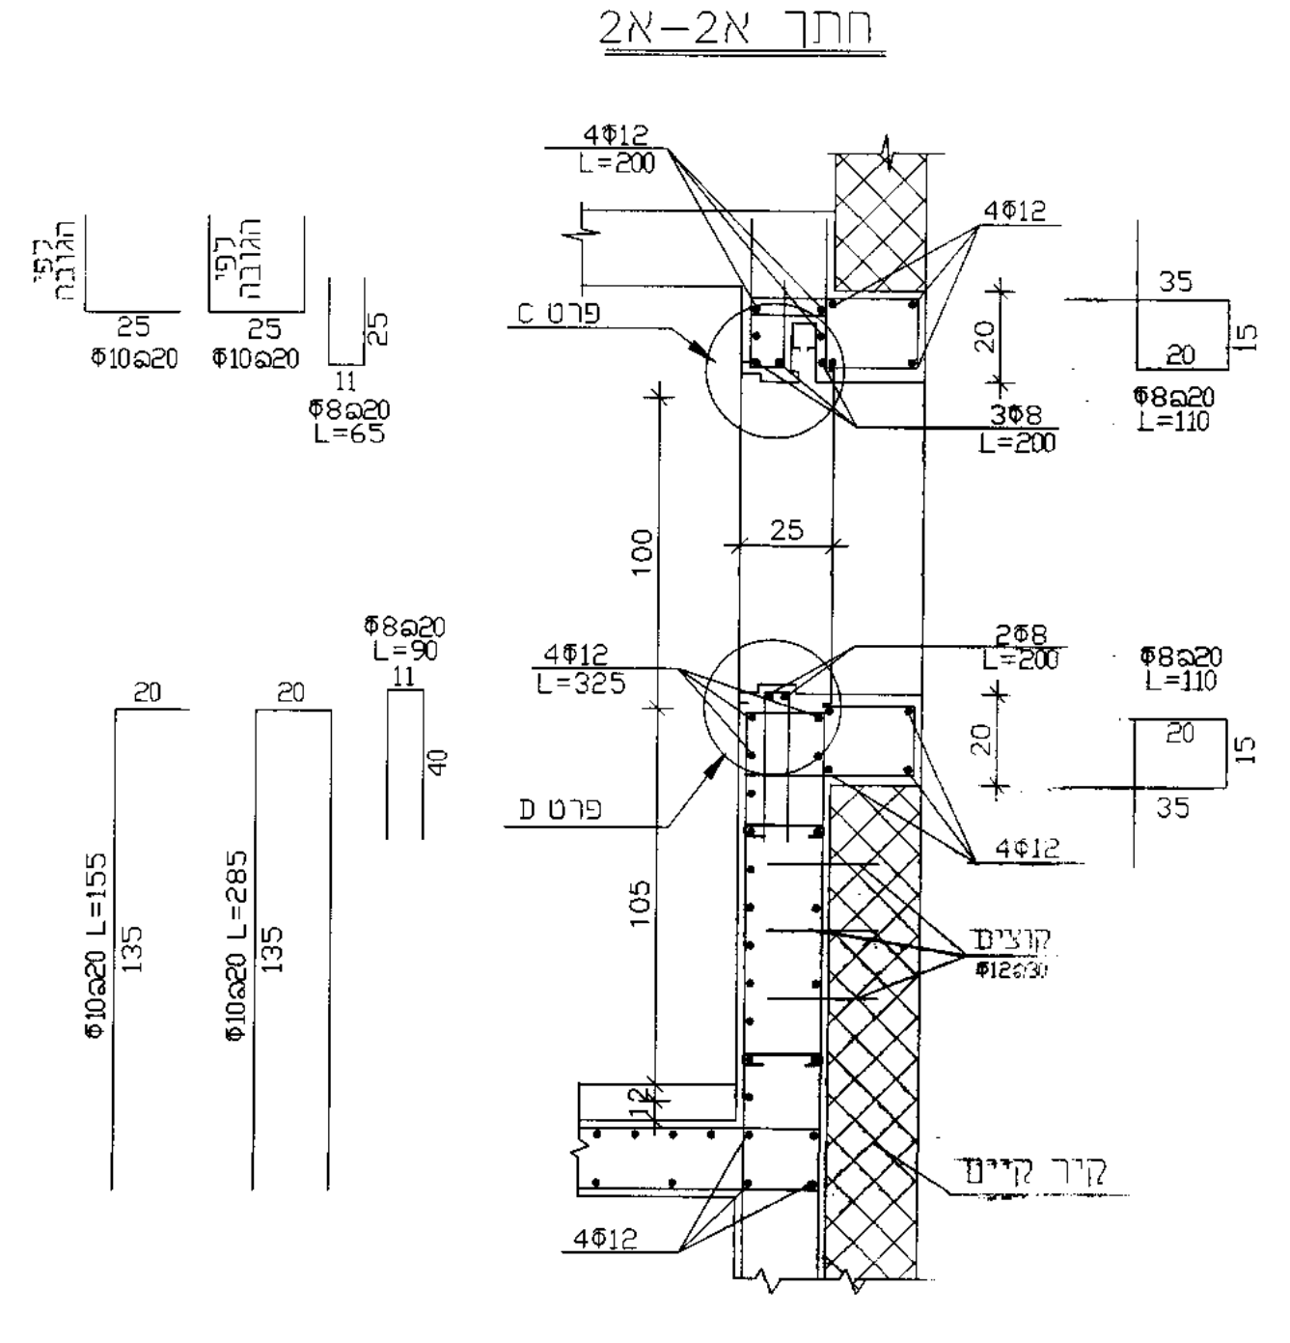
4Φ12 L=200
4Φ12
פרט C
3Φ8 L=200
4Φ12 L=325
2Φ8 L=200
פרט D
4Φ12
קוצים
Φ12@30
קיר קיים
לפי הגובה
Φ10@20
Φ8@20 L=65
Φ8@20 L=110
Φ8@20 L=90
Φ10@20 L=155
Φ10@20 L=285
100
105
25

חלון עם כיס

זיון סביב פתח בקיר

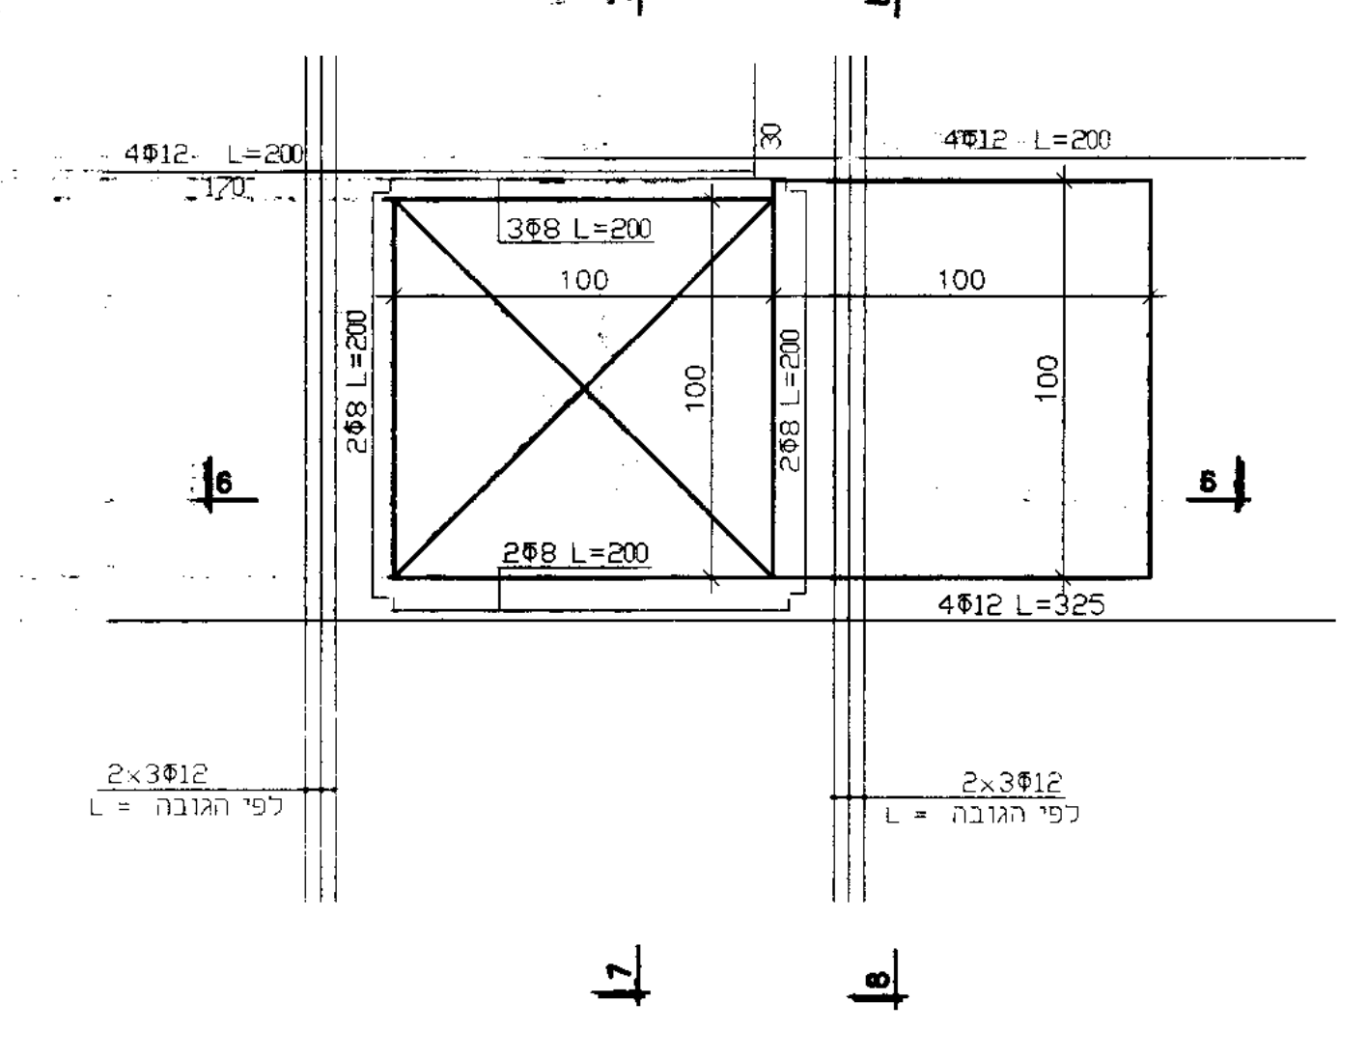
4Φ12 L=200
3Φ8 L=200
2Φ8 L=200
4Φ12 L=325
2×3Φ12
L = לפי הגובה
100
6
7
8

חתך 6–6

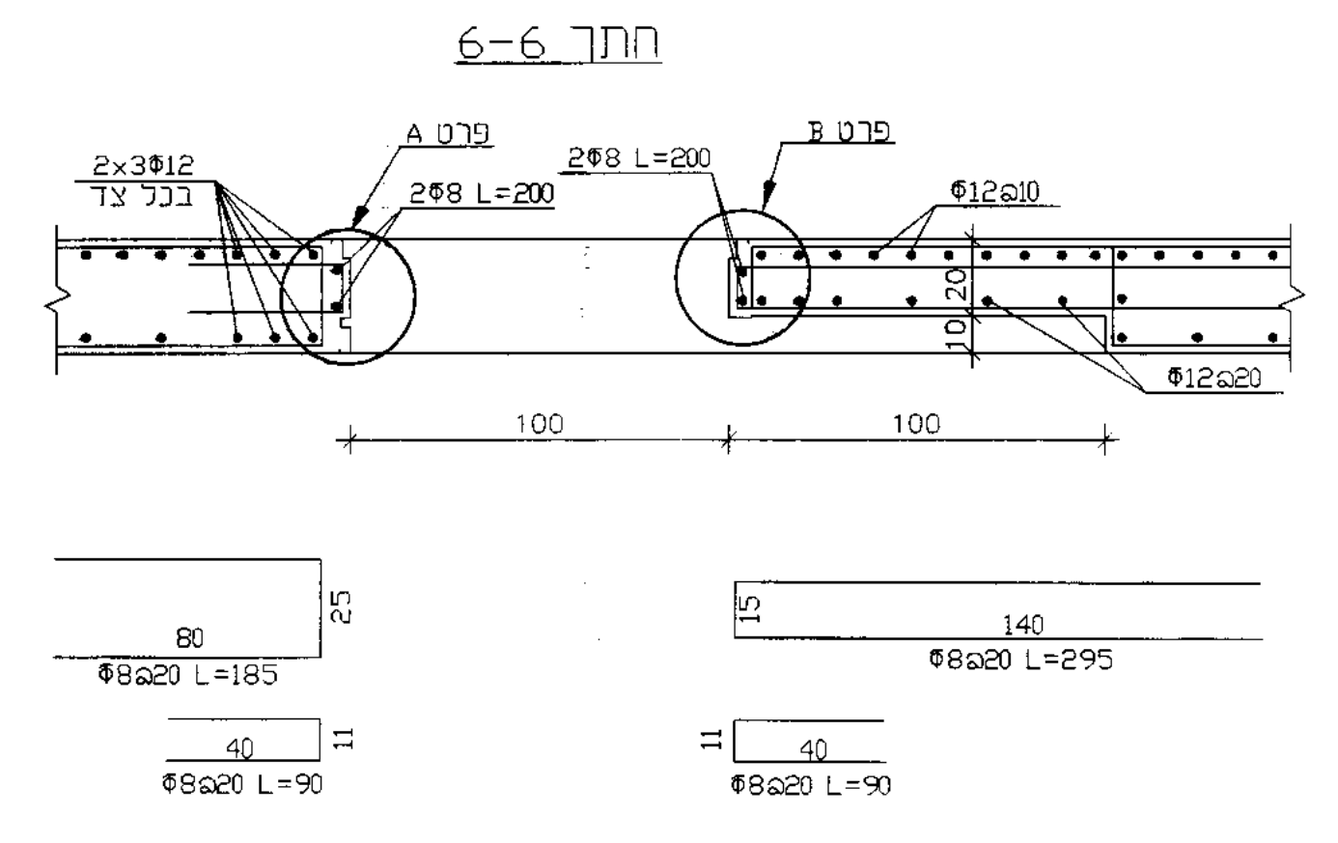
2×3Φ12
בכל צד
פרט A
2Φ8 L=200
פרט B
Φ12@10
Φ12@20
100
Φ8@20 L=185
Φ8@20 L=295
Φ8@20 L=90

חתך 8–8

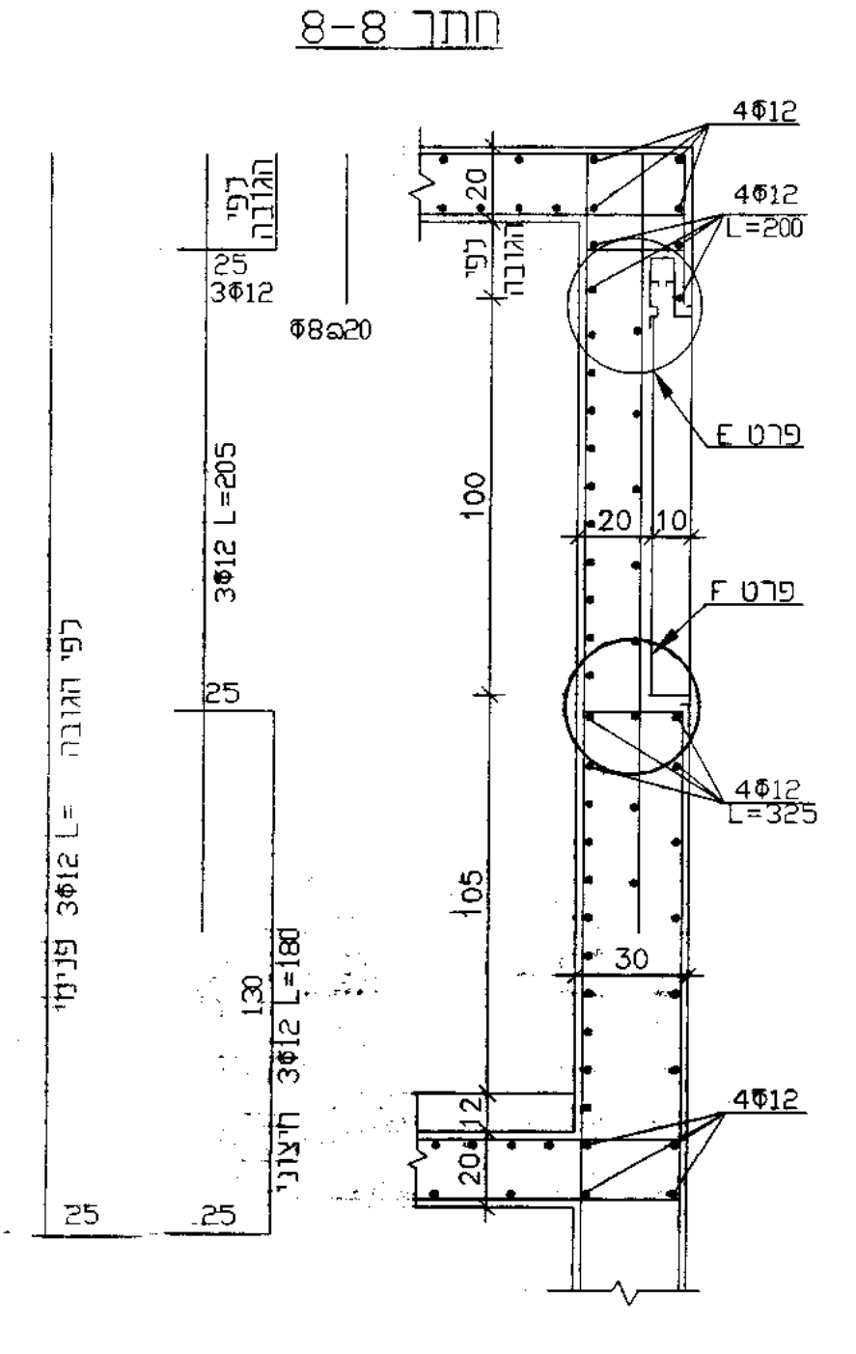
4Φ12
4Φ12 L=200
פרט E
פרט F
4Φ12 L=325
לפי הגובה
3Φ12
Φ8@20
3Φ12 L=205
3Φ12 L= לפי הגובה פנימי
3Φ12 L=180 חיצוני
100
105
30

חתך 7–7

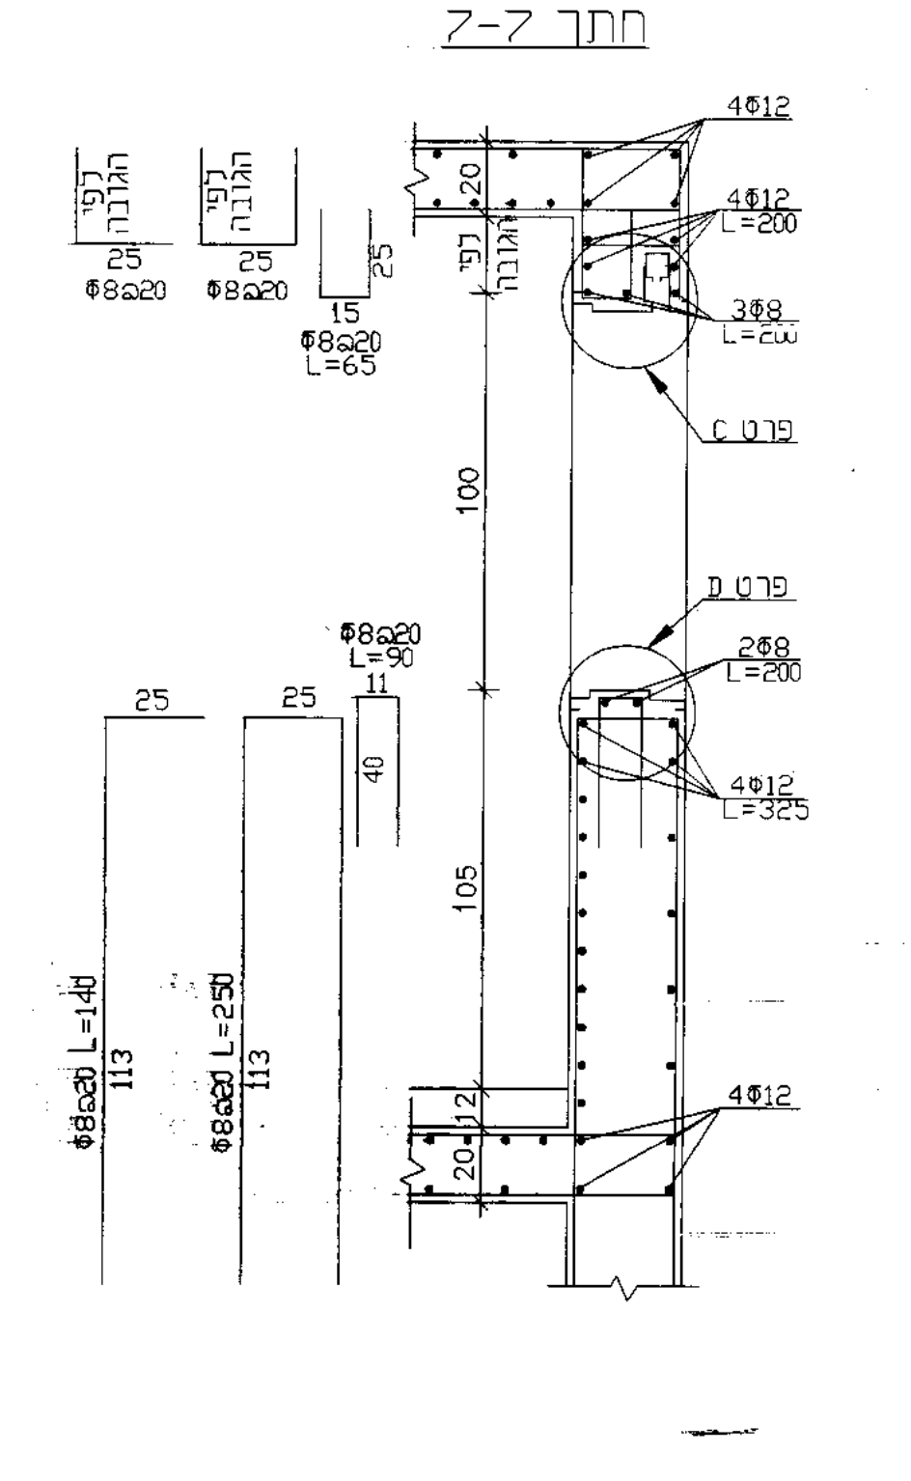
4Φ12
4Φ12 L=200
3Φ8 L=200
פרט C
פרט D
2Φ8 L=200
4Φ12 L=325
לפי הגובה
Φ8@20 L=65
Φ8@20 L=90
Φ8@20 L=140
Φ8@20 L=250
100
105

דלת

זיון סביב פתח בקיר

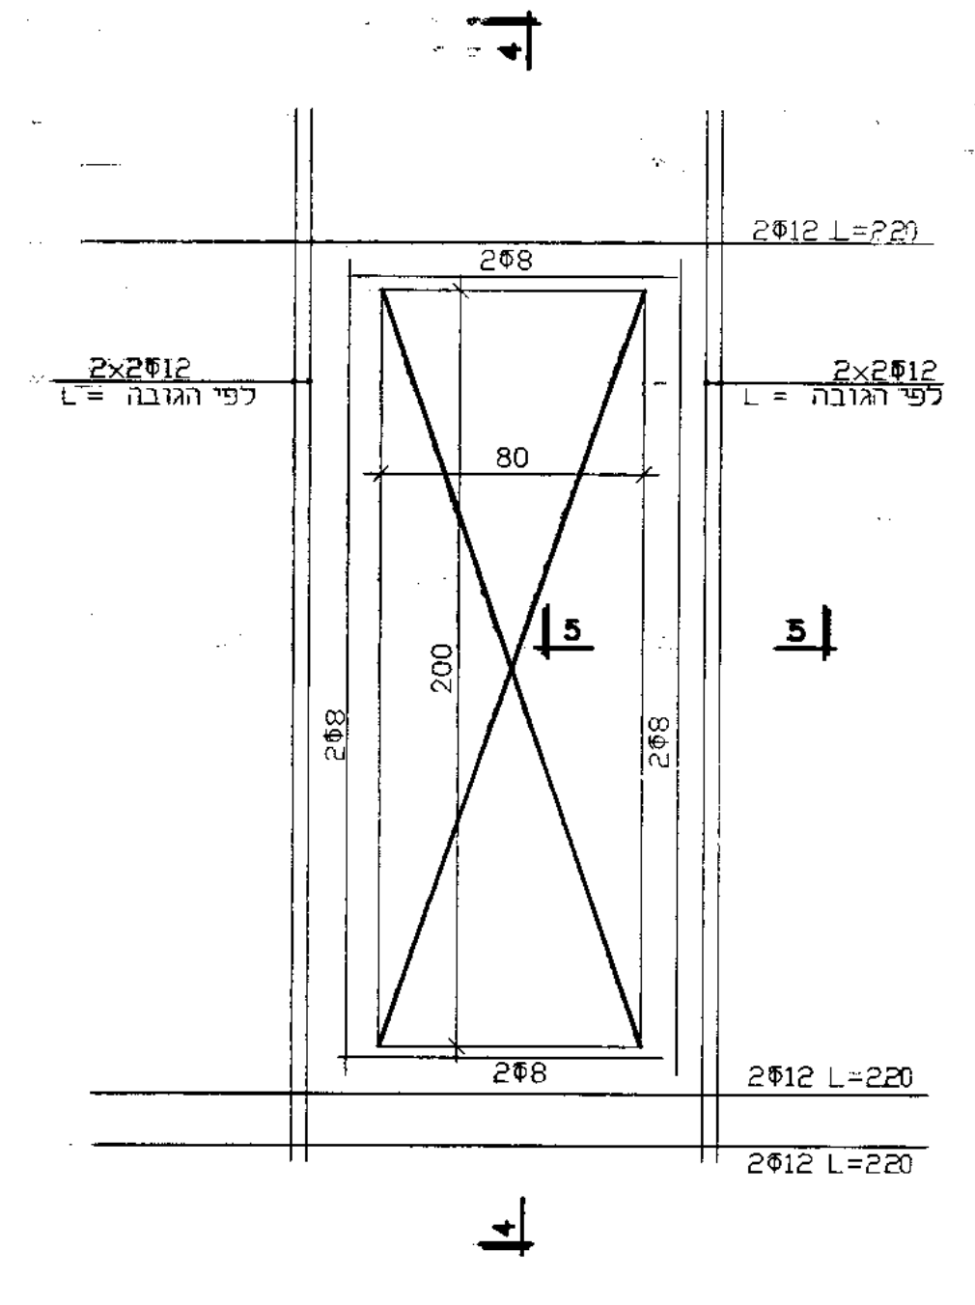
2Φ8
2Φ12 L=220
2×2Φ12
L = לפי הגובה
80
200
4
5

חתך 4–4

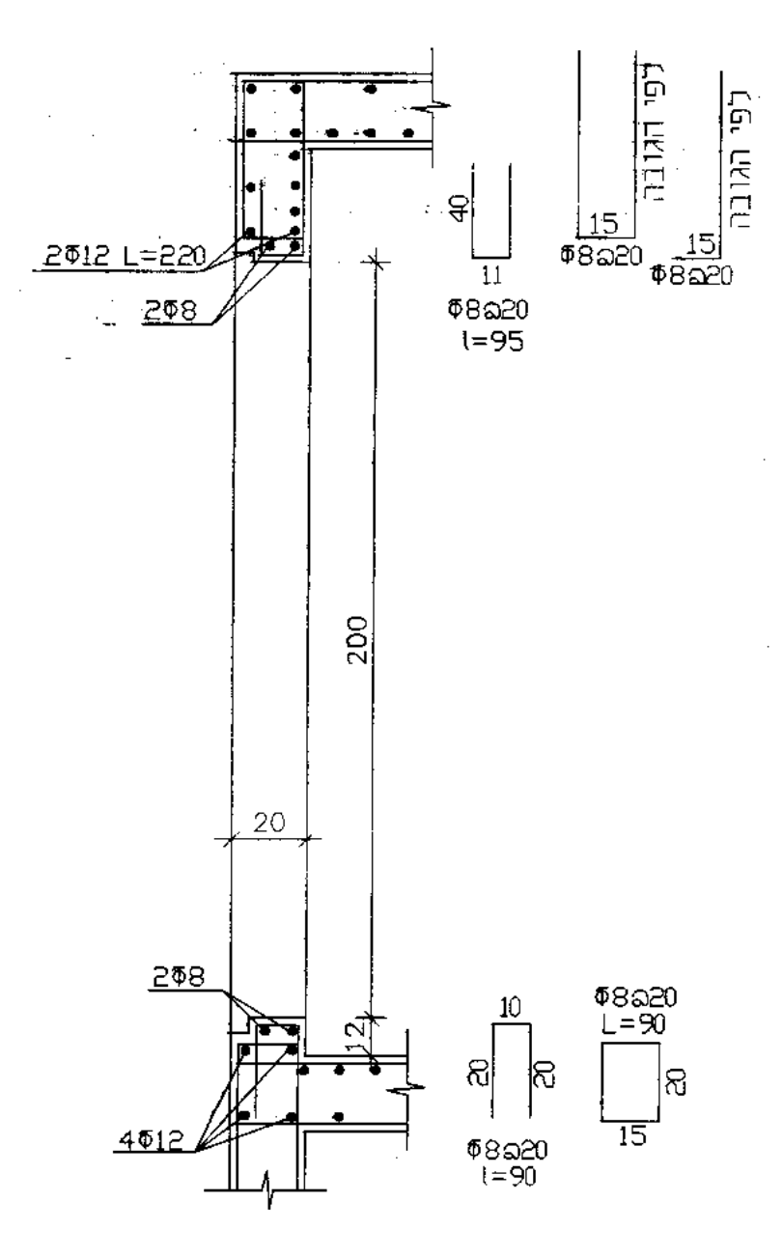
2Φ12 L=220
2Φ8
לפי הגובה
Φ8@20 l=95
Φ8@20 L=90
Φ8@20 l=90
4Φ12
200
20

חתך 5–5

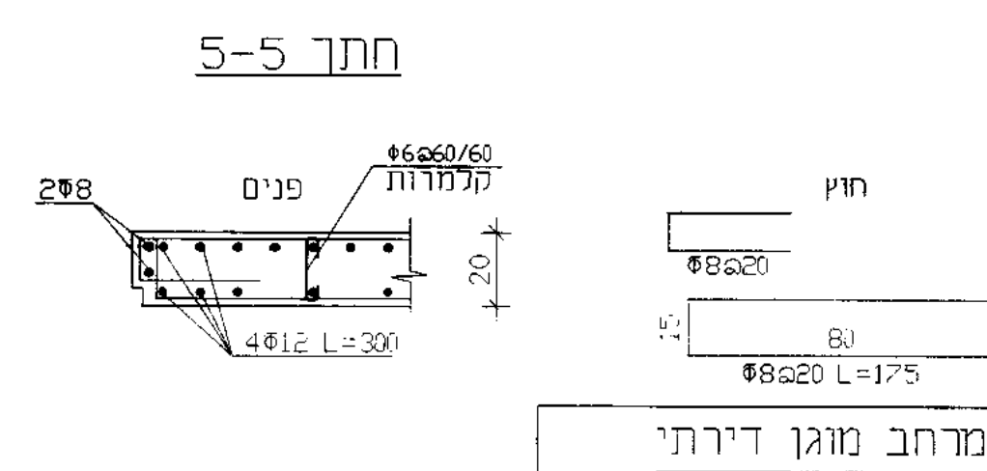
2Φ8
פנים
Φ6@60/60
קלמרות
4Φ12 L=300
חוץ
Φ8@20
Φ8@20 L=175

הוראות ביצוע למרחב מוגן דירתי

המרחב המוגן הדירתי יבנה בהתאם לתקנות ההתגוננות האזרחית, במרחב המוגן יתקיימו עקרונות יסוד אלו:

1. המ.מ.ד יבנה מבטון כמיבנה דמוי תיבה, עשוי מקשה אחת ורתום בכל חלקיו.
2. ריצפת המ.מ.ד, קירותיו ותיקרתו יהיו מישוריים וחלקים.
3. קירות המ.מ.ד יעבירו העומסים עד ליסודות ויהיו רציפים לכל גובה הבניין, ליצירת מיגדל מוגן.
4. סוג הבטון ב-30 בכל חלקי המ.מ.ד. לפי דרישות ת"י 118, החוזק לפי ת"י 466.
5. יציבות המיגדל תובטח מפני כוחות אופקיים.
6. מידות פתח לדלת כניסה יהיה 80/200 או 70/200. סוג דלת הכניסה (דלת הדף דירתית), דלת בטחון הג"א.
7. מידות פתח לחלון 110/110 או לפי אישור רשות מוסמכת, גובה תחתית חלון מריצפת החדר לא יהיה קטן מ-1.20 מ"א.
8. במידה ולא קיים פתח לחלון יש להתקין צינורות איוורור "18 Φ • 2.
9. הכנת המ.מ.ד למערכות חשמל ותיקשורת לפי פרטים מצורפים.
10. פני הדופן הפנימית של המ.מ.ד יהיו חלקים עם גמר יציקת הבטון:
  - א. קירות להחלקה "שליכט בגר" עובי 2 מ"מ.
  - ב. טיח פנים פולימרי יעמוד בדרישות ת"י 1731, דרישות לעמידות ברטיבות בחדירת מים בתנאי גשם, אדי מים ובליה.
  - ג. טיח גבס יעמוד בדרישות מיפרט מיוחד פיקוד העורף.
  - ד. טיח טרמי מסוג "תרמוקיר 400" על בסיס פוליסטירן מותפח, כולל שכבת "הרבצה צמנטית", שכבת בידוד טיח טרמי "תרמוקיר 400", שכבת מגן ושכבת גמר "שליכט גמר".
11. הקבלן חייב להחזיק תוכנית מאושרת של המ.מ.ד באתר הבניה עד לסיום הקמתו.

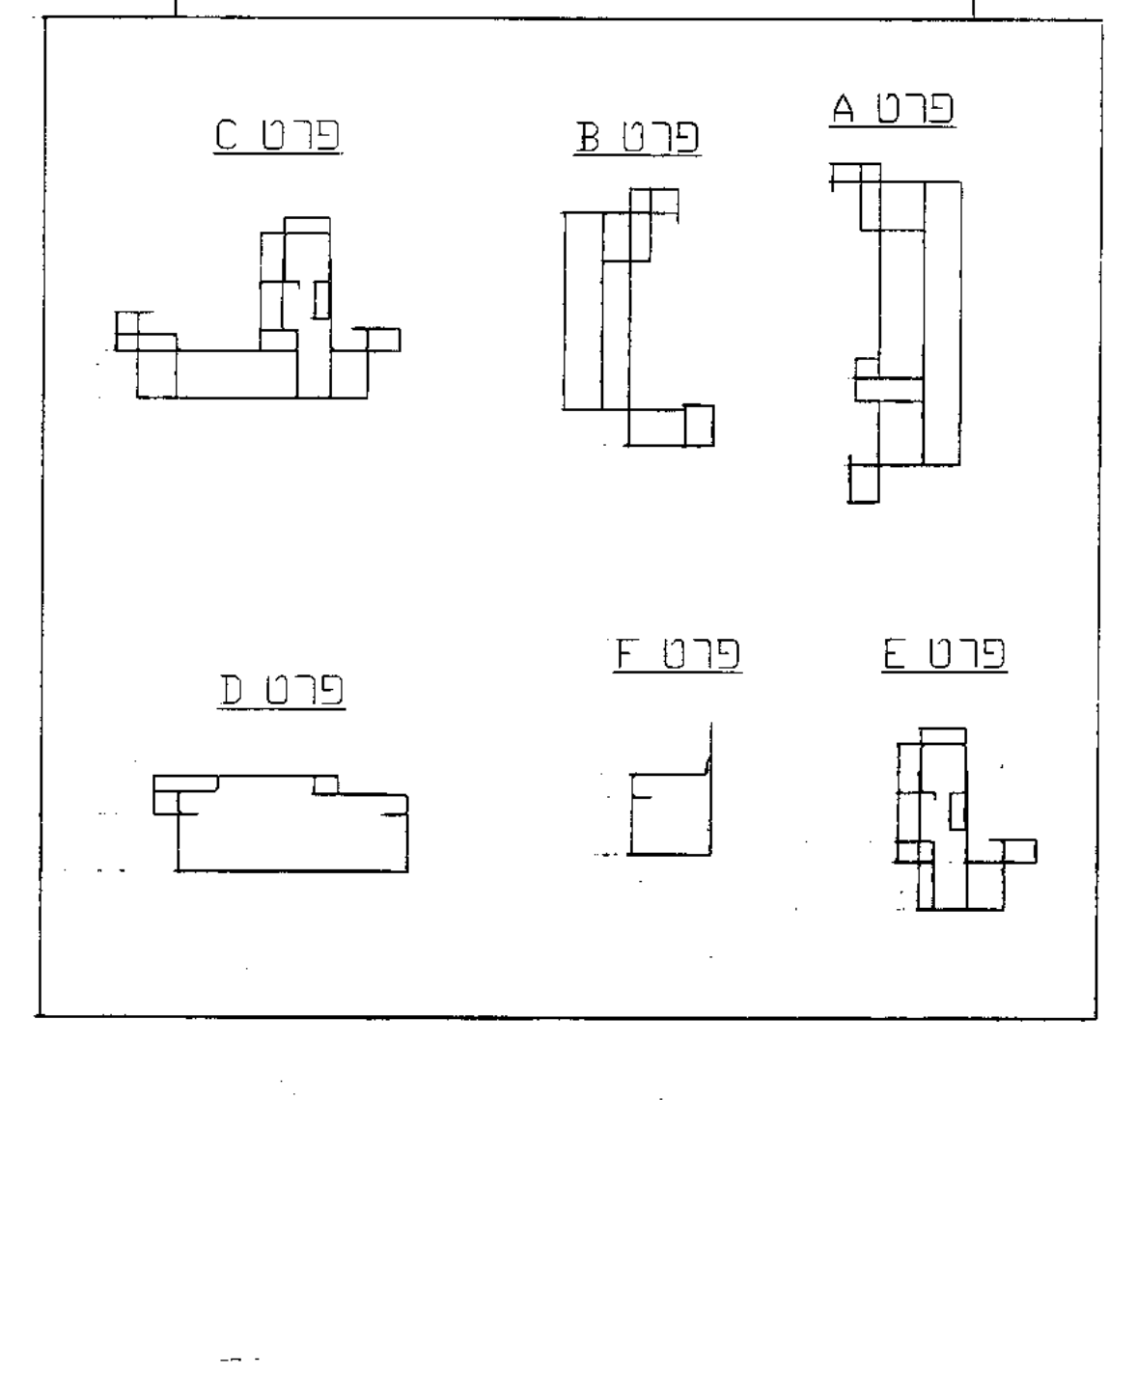
פרט A
פרט B
פרט C
פרט D
פרט E
פרט F

חתך 2–2

1:50

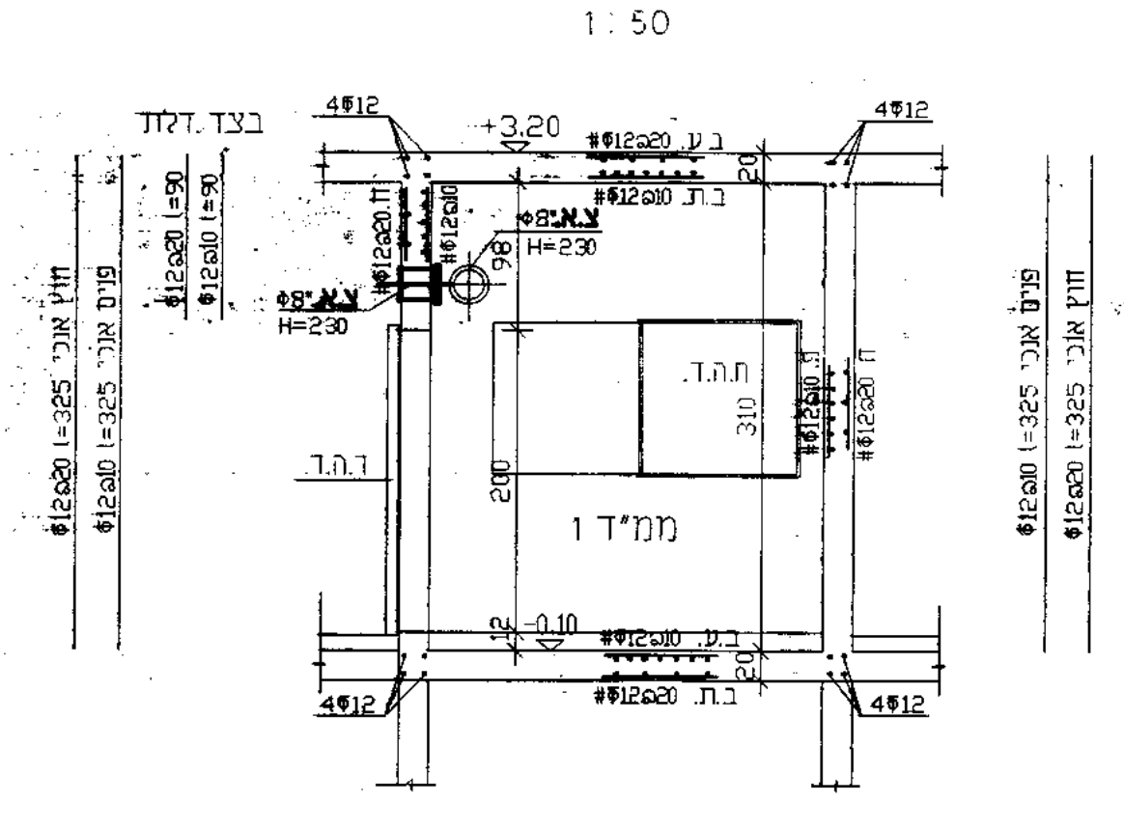
בצד דלת
4Φ12
+3.20
ב.ע. #Φ12@20
ב.ת. #Φ12@10
Φ8"צ.א.
H=230
ת.ה.ד.
ד.ה.ת.
ממ"ד 1
200
310
-0.10
חוץ אנכי Φ12@20 l=325
פנים אנכי Φ12@10 l=325
Φ12@20 l=90
Φ12@10 l=90

חתך 1–1

1:50

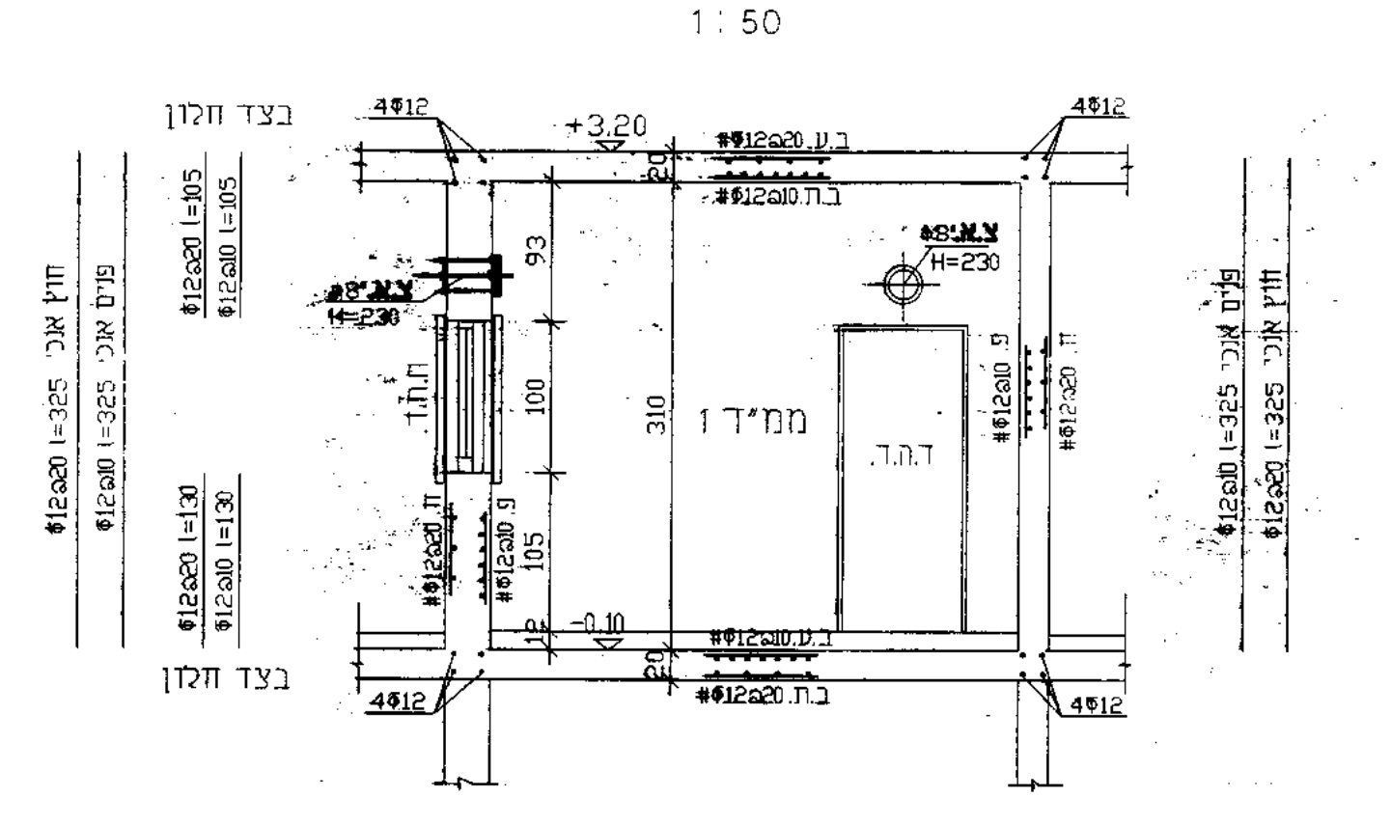
בצד חלון
4Φ12
+3.20
ב.ע. #Φ12@20
ב.ת. #Φ12@10
Φ8"צ.א.
H=230
ת.ה.ח.
ד.ה.ת.
ממ"ד 1
93
100
105
310
-0.10
Φ12@20 l=105
Φ12@10 l=105
Φ12@20 l=130
Φ12@10 l=130
חוץ אנכי Φ12@20 l=325
פנים אנכי Φ12@10 l=325

חתך 4–4

1:50

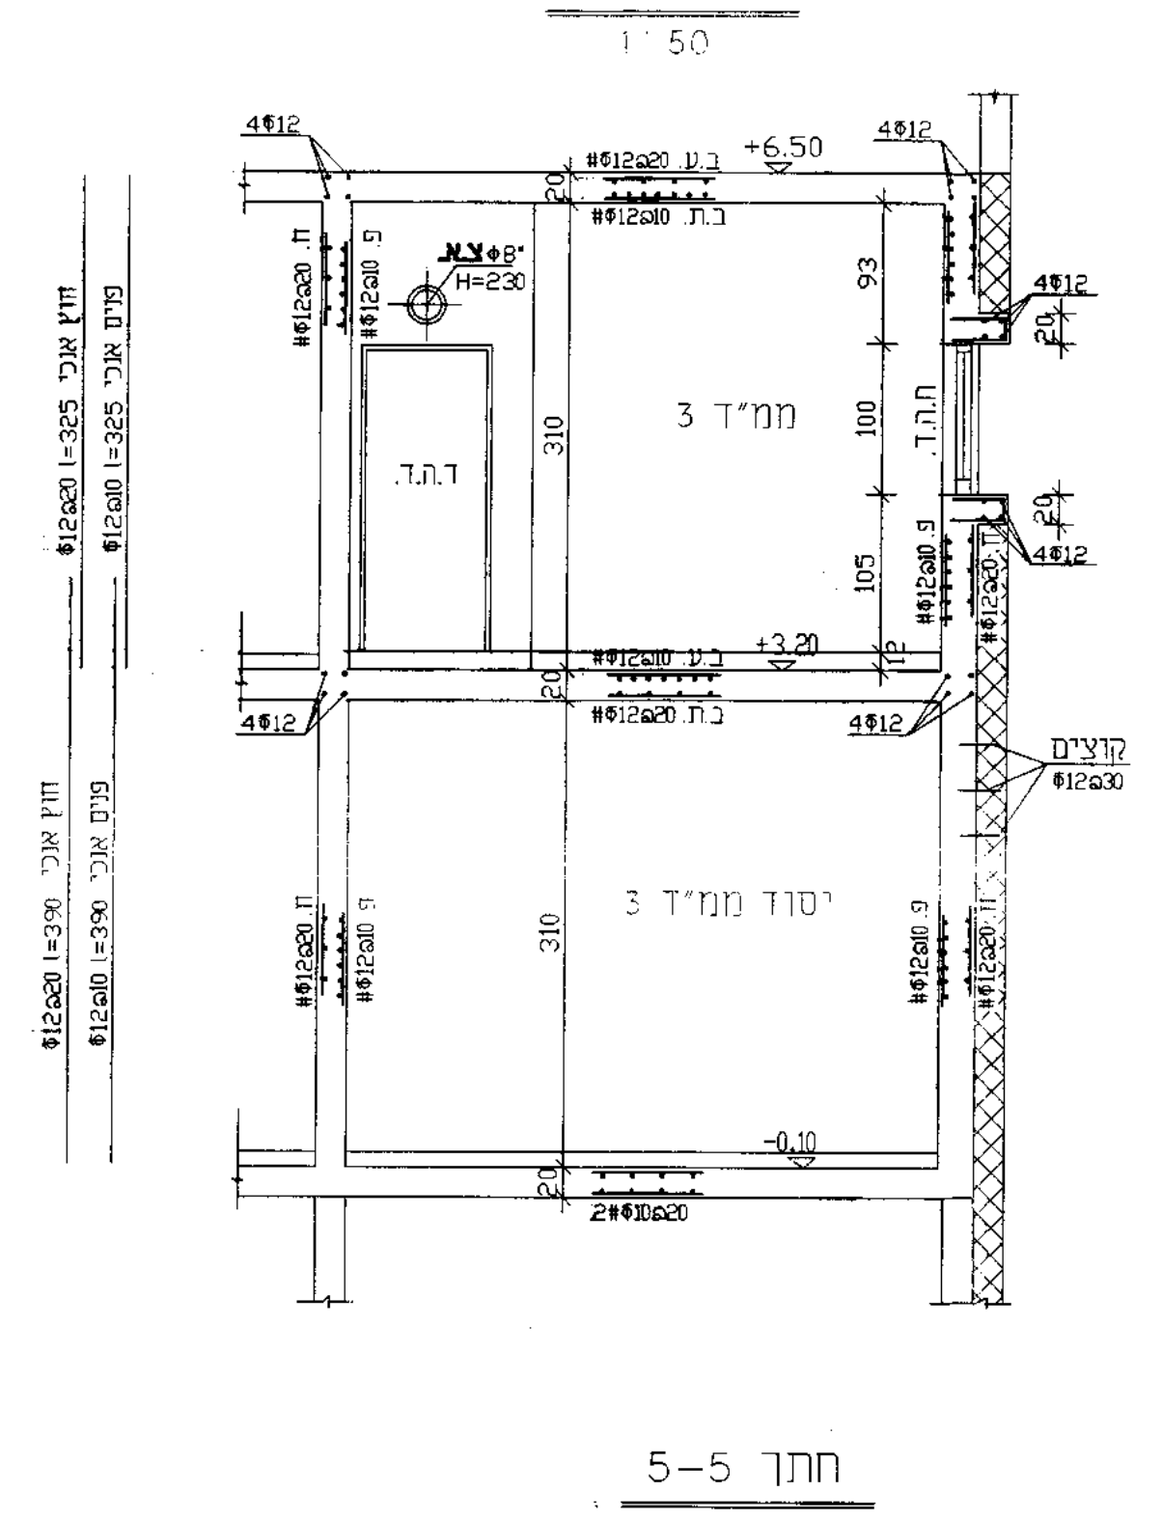
בצד חלון
4Φ12
+6.50
+3.20
ב.ע. #Φ12@20
ב.ת. #Φ12@10
Φ8"צ.א.
H=230
ד.ה.ת.
ת.ה.ח.
ממ"ד 3
יסוד ממ"ד 3
קוצים
Φ12@30
310
-0.10
2#Φ10@20
חוץ אנכי Φ12@20 l=325
פנים אנכי Φ12@10 l=325
חוץ אנכי Φ12@20 l=390
פנים אנכי Φ12@10 l=390
Φ12@20 l=105
Φ12@20 l=130

חתך 3–3

1:50

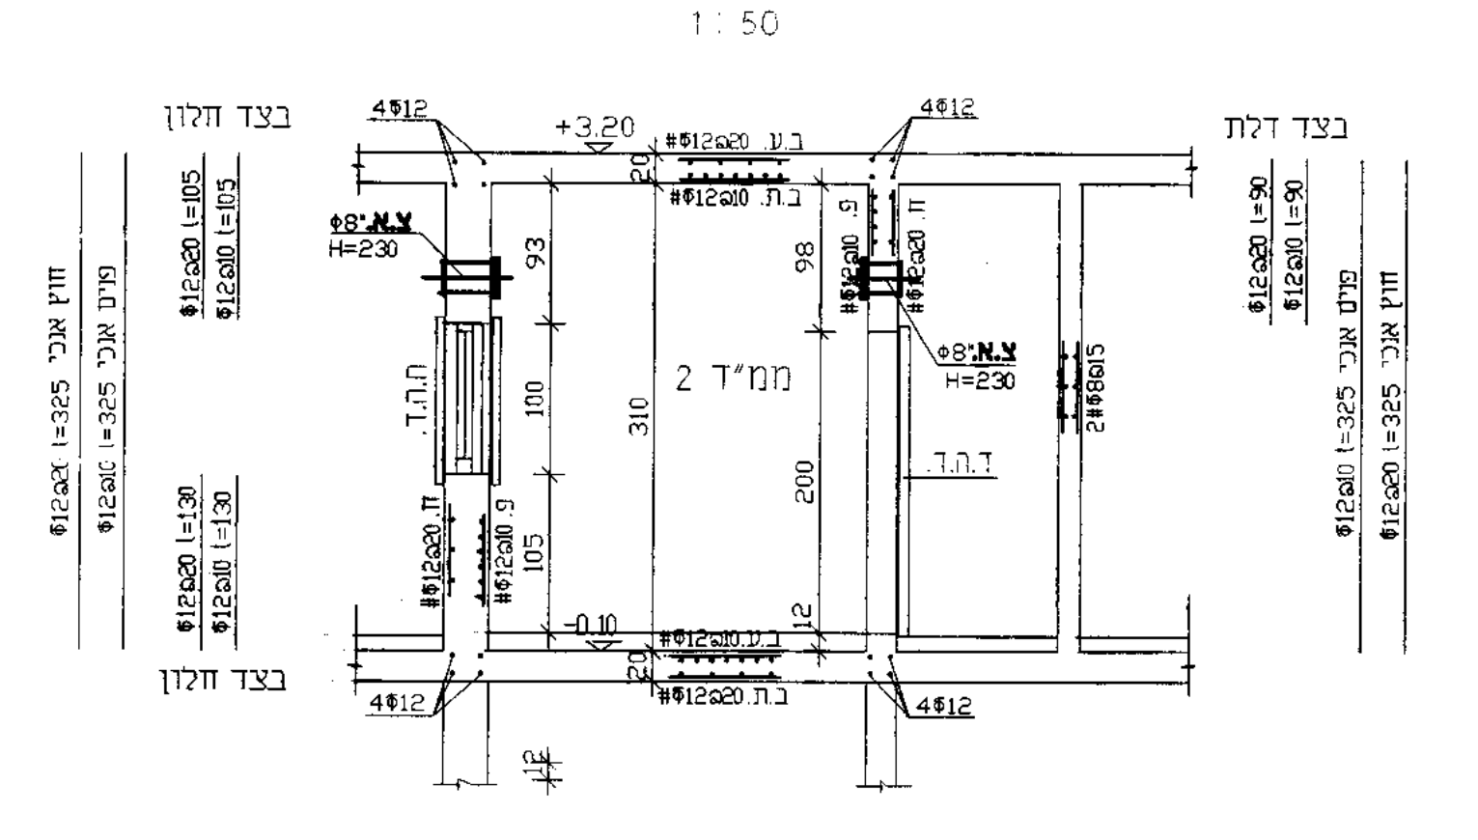
בצד חלון
בצד דלת
4Φ12
+3.20
ב.ע. #Φ12@20
ב.ת. #Φ12@10
Φ8"צ.א.
H=230
ת.ה.ח.
ד.ה.ת.
ממ"ד 2
2#Φ8@15
200
310
-0.10
חוץ אנכי Φ12@20 l=325
פנים אנכי Φ12@10 l=325
Φ12@20 l=90
Φ12@10 l=90

חתך 5–5

1:50

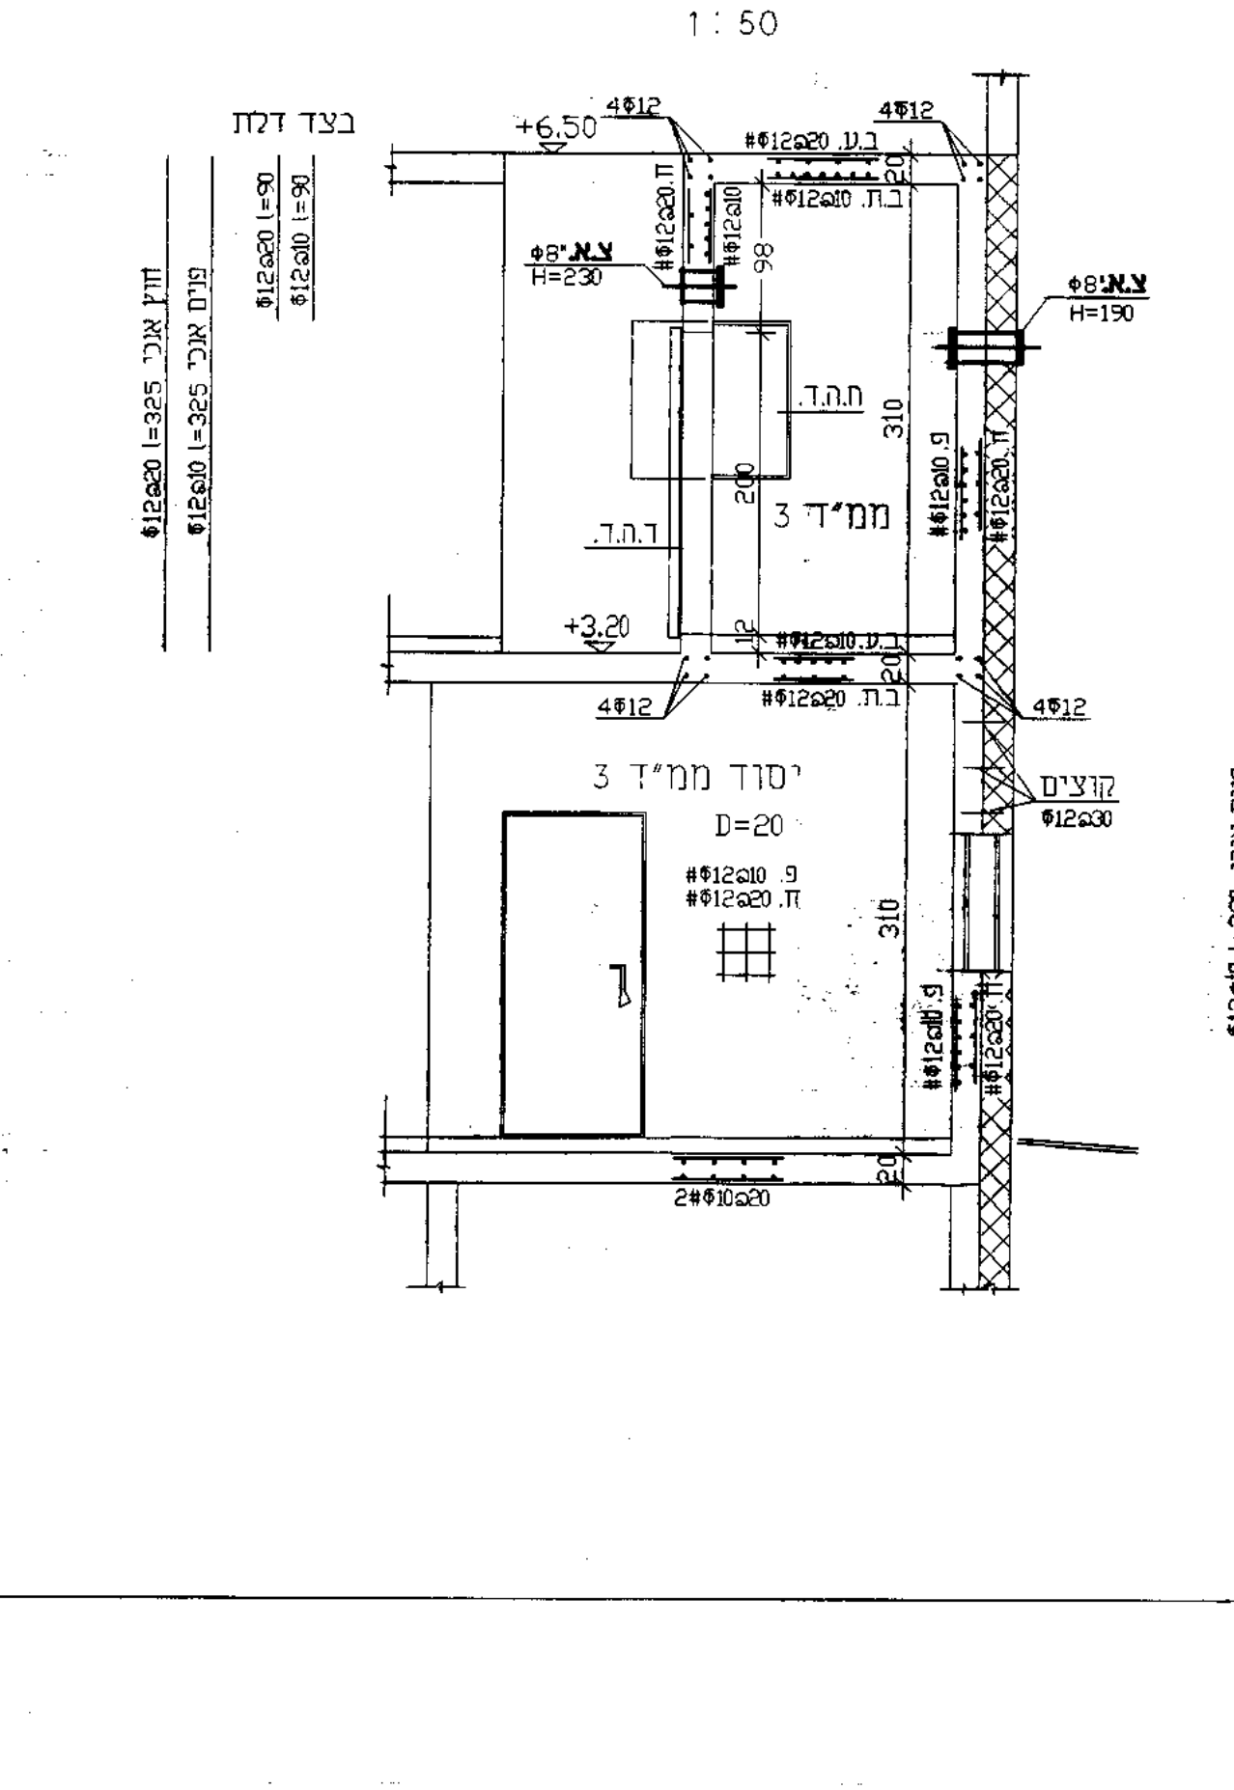
בצד דלת
+6.50
+3.20
4Φ12
ב.ע. #Φ12@20
ב.ת. #Φ12@10
Φ8"צ.א.
H=230
H=190
ת.ה.ד.
ד.ה.ת.
ממ"ד 3
יסוד ממ"ד 3
D=20
קוצים
Φ12@30
2#Φ10@20
310
חוץ אנכי Φ12@20 l=325
פנים אנכי Φ12@10 l=325
חוץ אנכי Φ12@20 l=390
פנים אנכי Φ12@10 l=390

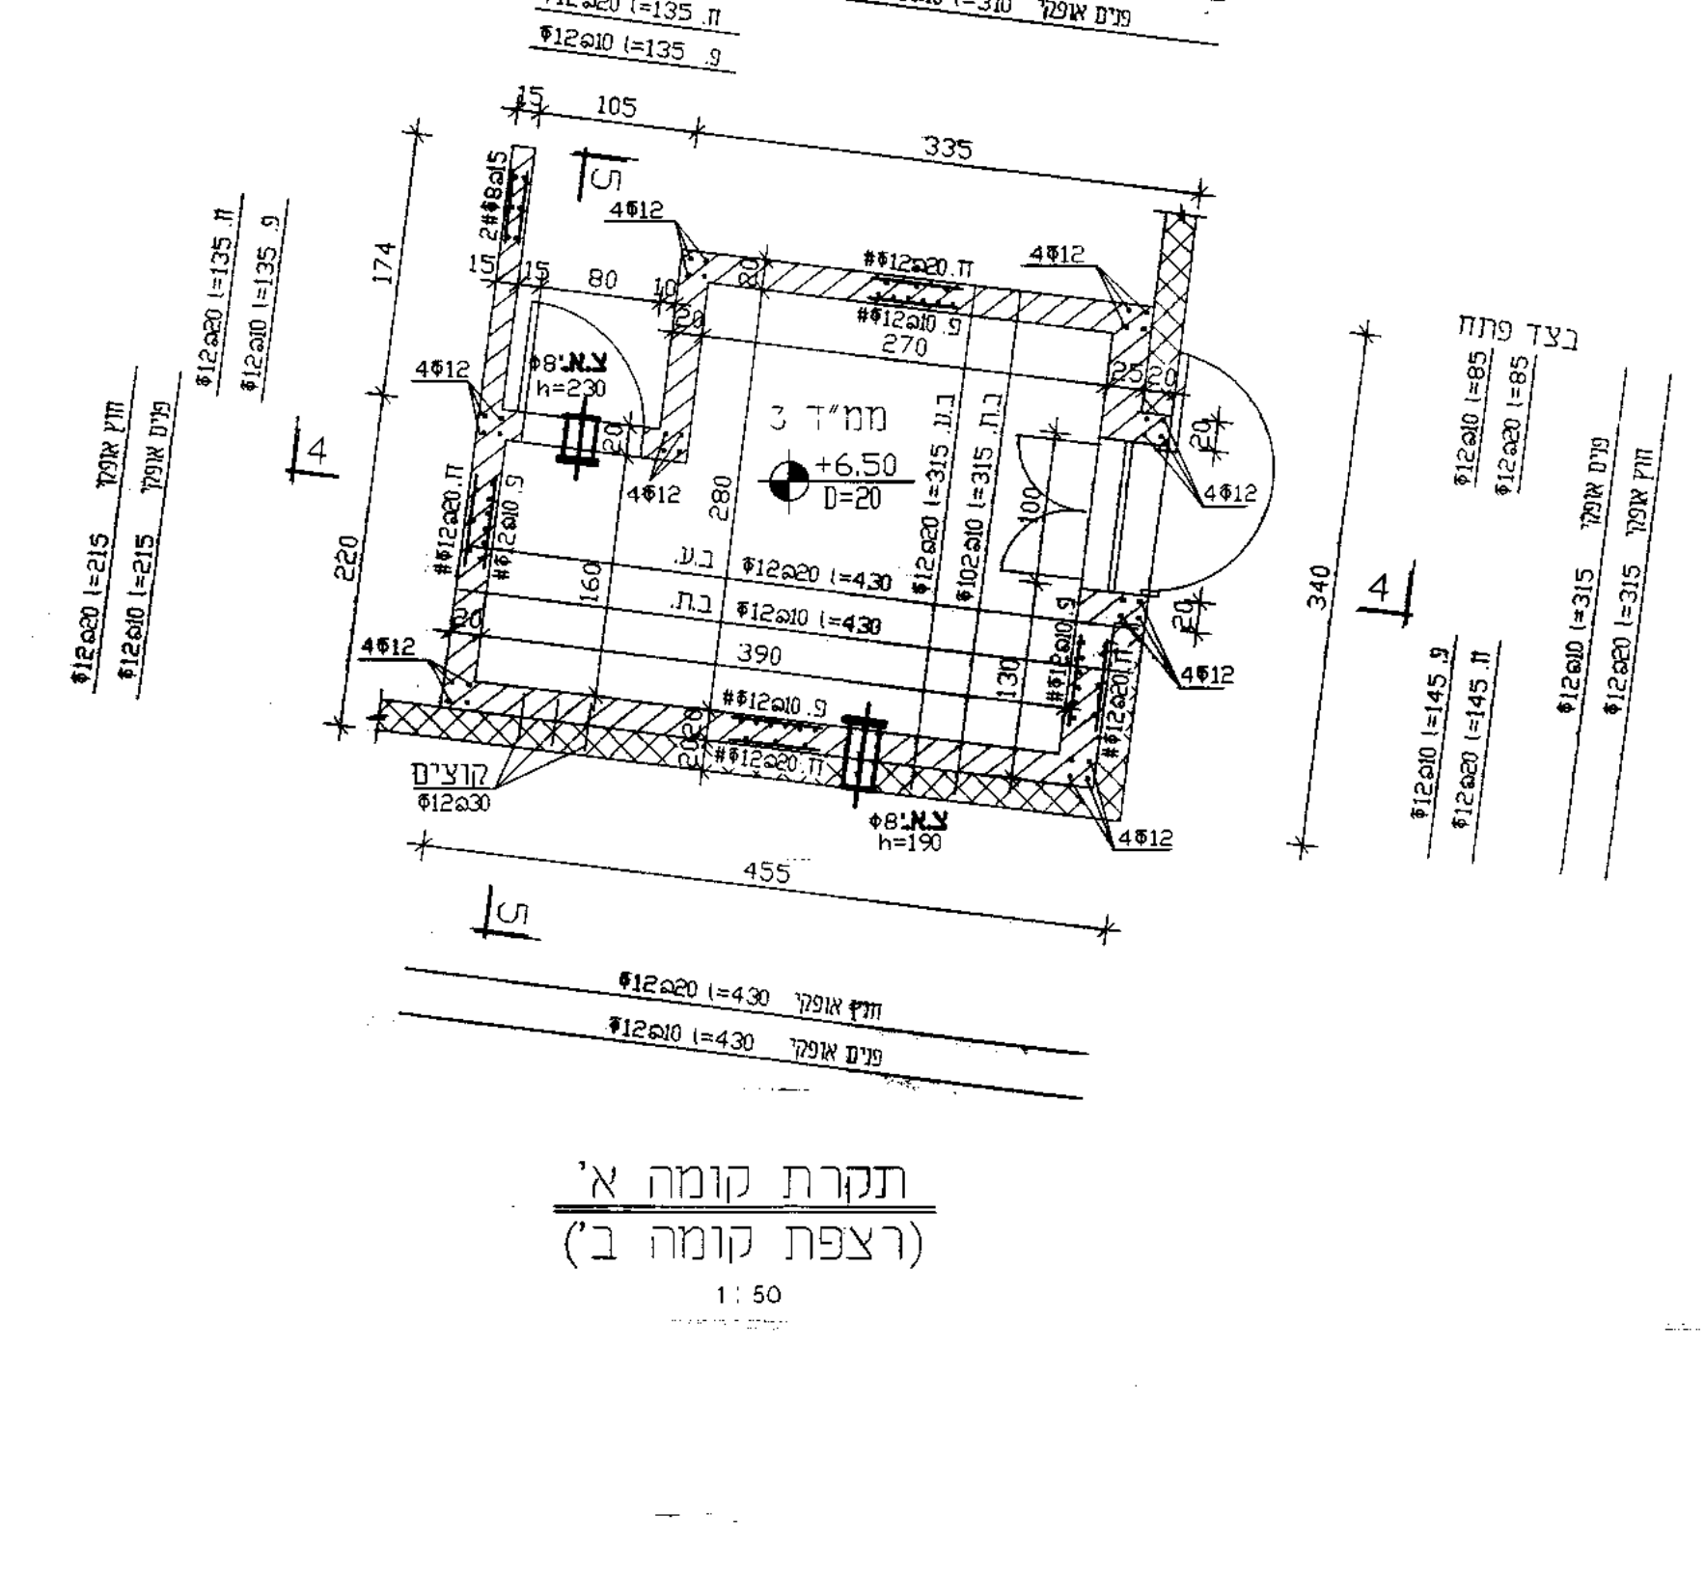
ממ"ד 3
+6.50
D=20
בצד פתח
ב.ע. Φ12@20 l=430
ב.ת. Φ12@10 l=430
חוץ אופקי Φ12@20 l=310
פנים אופקי Φ12@10 l=310
חוץ אופקי Φ12@20 l=430
פנים אופקי Φ12@10 l=430
Φ12@20 l=135
Φ12@10 l=135
Φ12@20 l=215
Φ12@10 l=215
Φ12@20 l=315
Φ12@10 l=315
Φ12@20 l=85
Φ12@10 l=145
קוצים
Φ12@30
Φ8"צ.א.
h=230
h=190
4Φ12
335
455
390
280
340
220
174

תקרת קומה א'

(רצפת קומה ב')

1:50

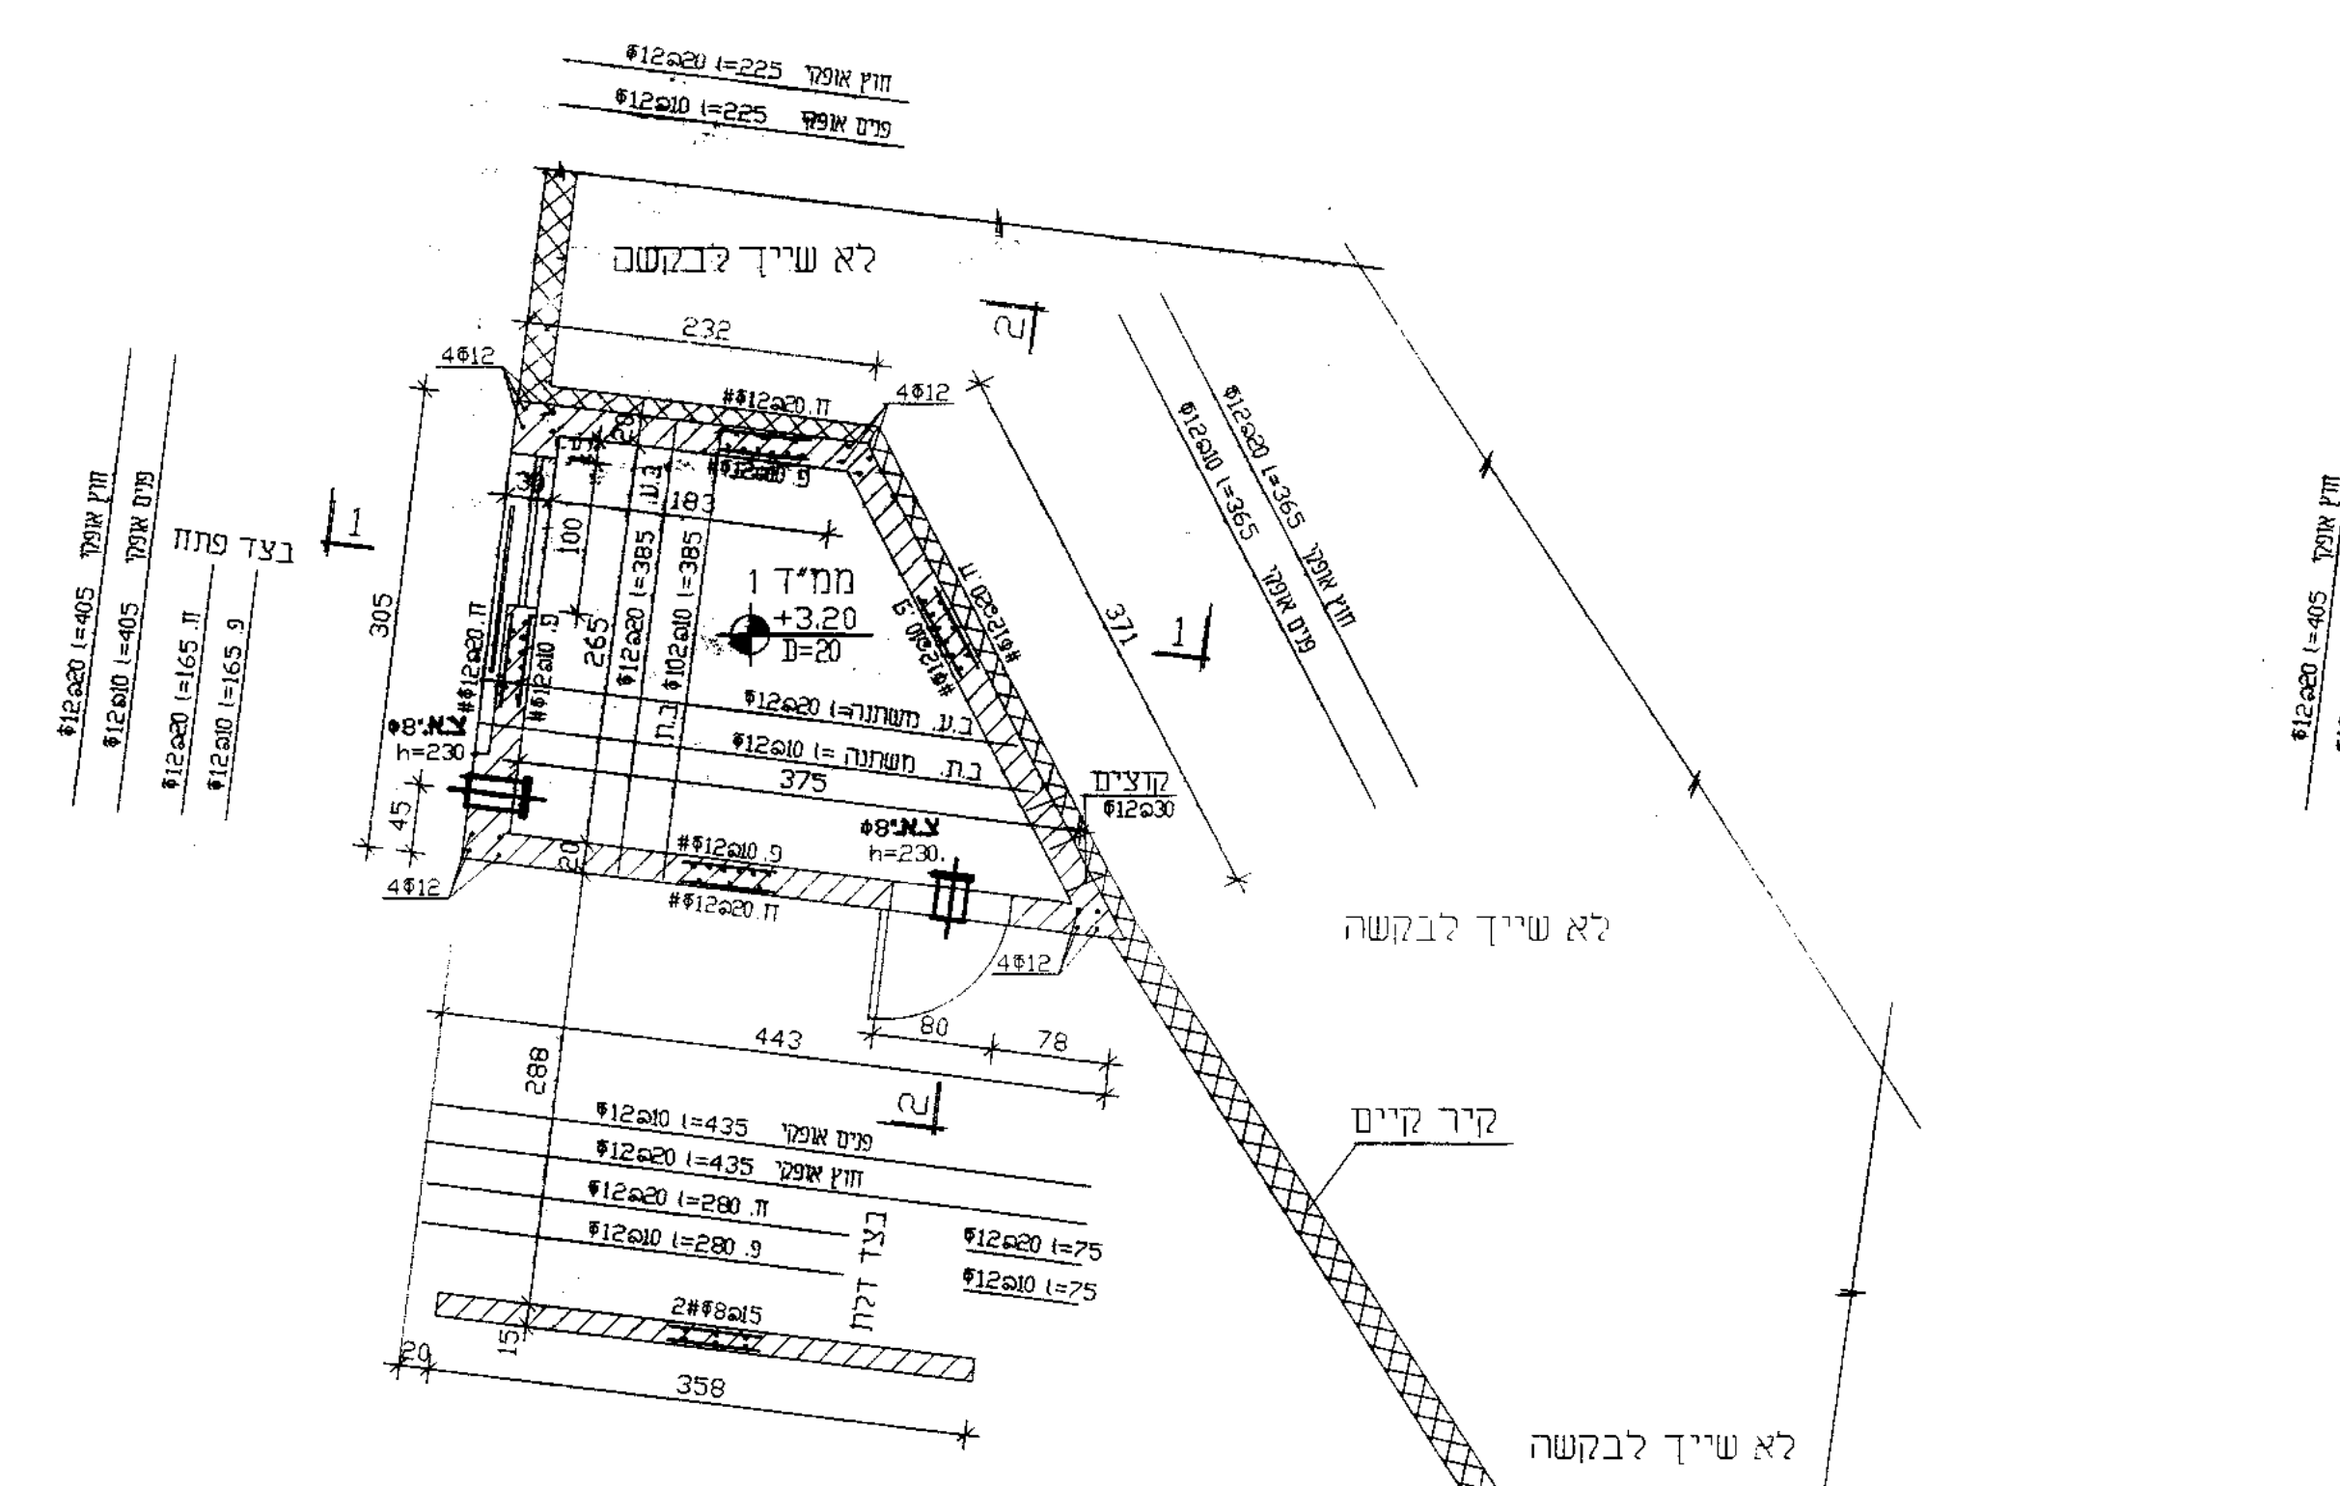
לא שייך לבקשה
קיר קיים
ממ"ד 1
+3.20
D=20
בצד פתח
בצד דלת
ב.ע. משתנה
ב.ת. משתנה
קוצים
Φ12@30
חוץ אופקי Φ12@20 l=225
פנים אופקי Φ12@10 l=225
Φ12@20 l=365
Φ12@10 l=365
Φ12@20 l=405
Φ12@10 l=405
Φ12@20 l=165
Φ12@10 l=165
Φ12@10 l=435
Φ12@20 l=435
Φ12@20 l=280
Φ12@10 l=280
Φ12@20 l=75
Φ12@10 l=75
2#Φ8@15
232
375
443
358
288
305
371

תקרת קומת קרקע

(רצפת קומה א')

1:50

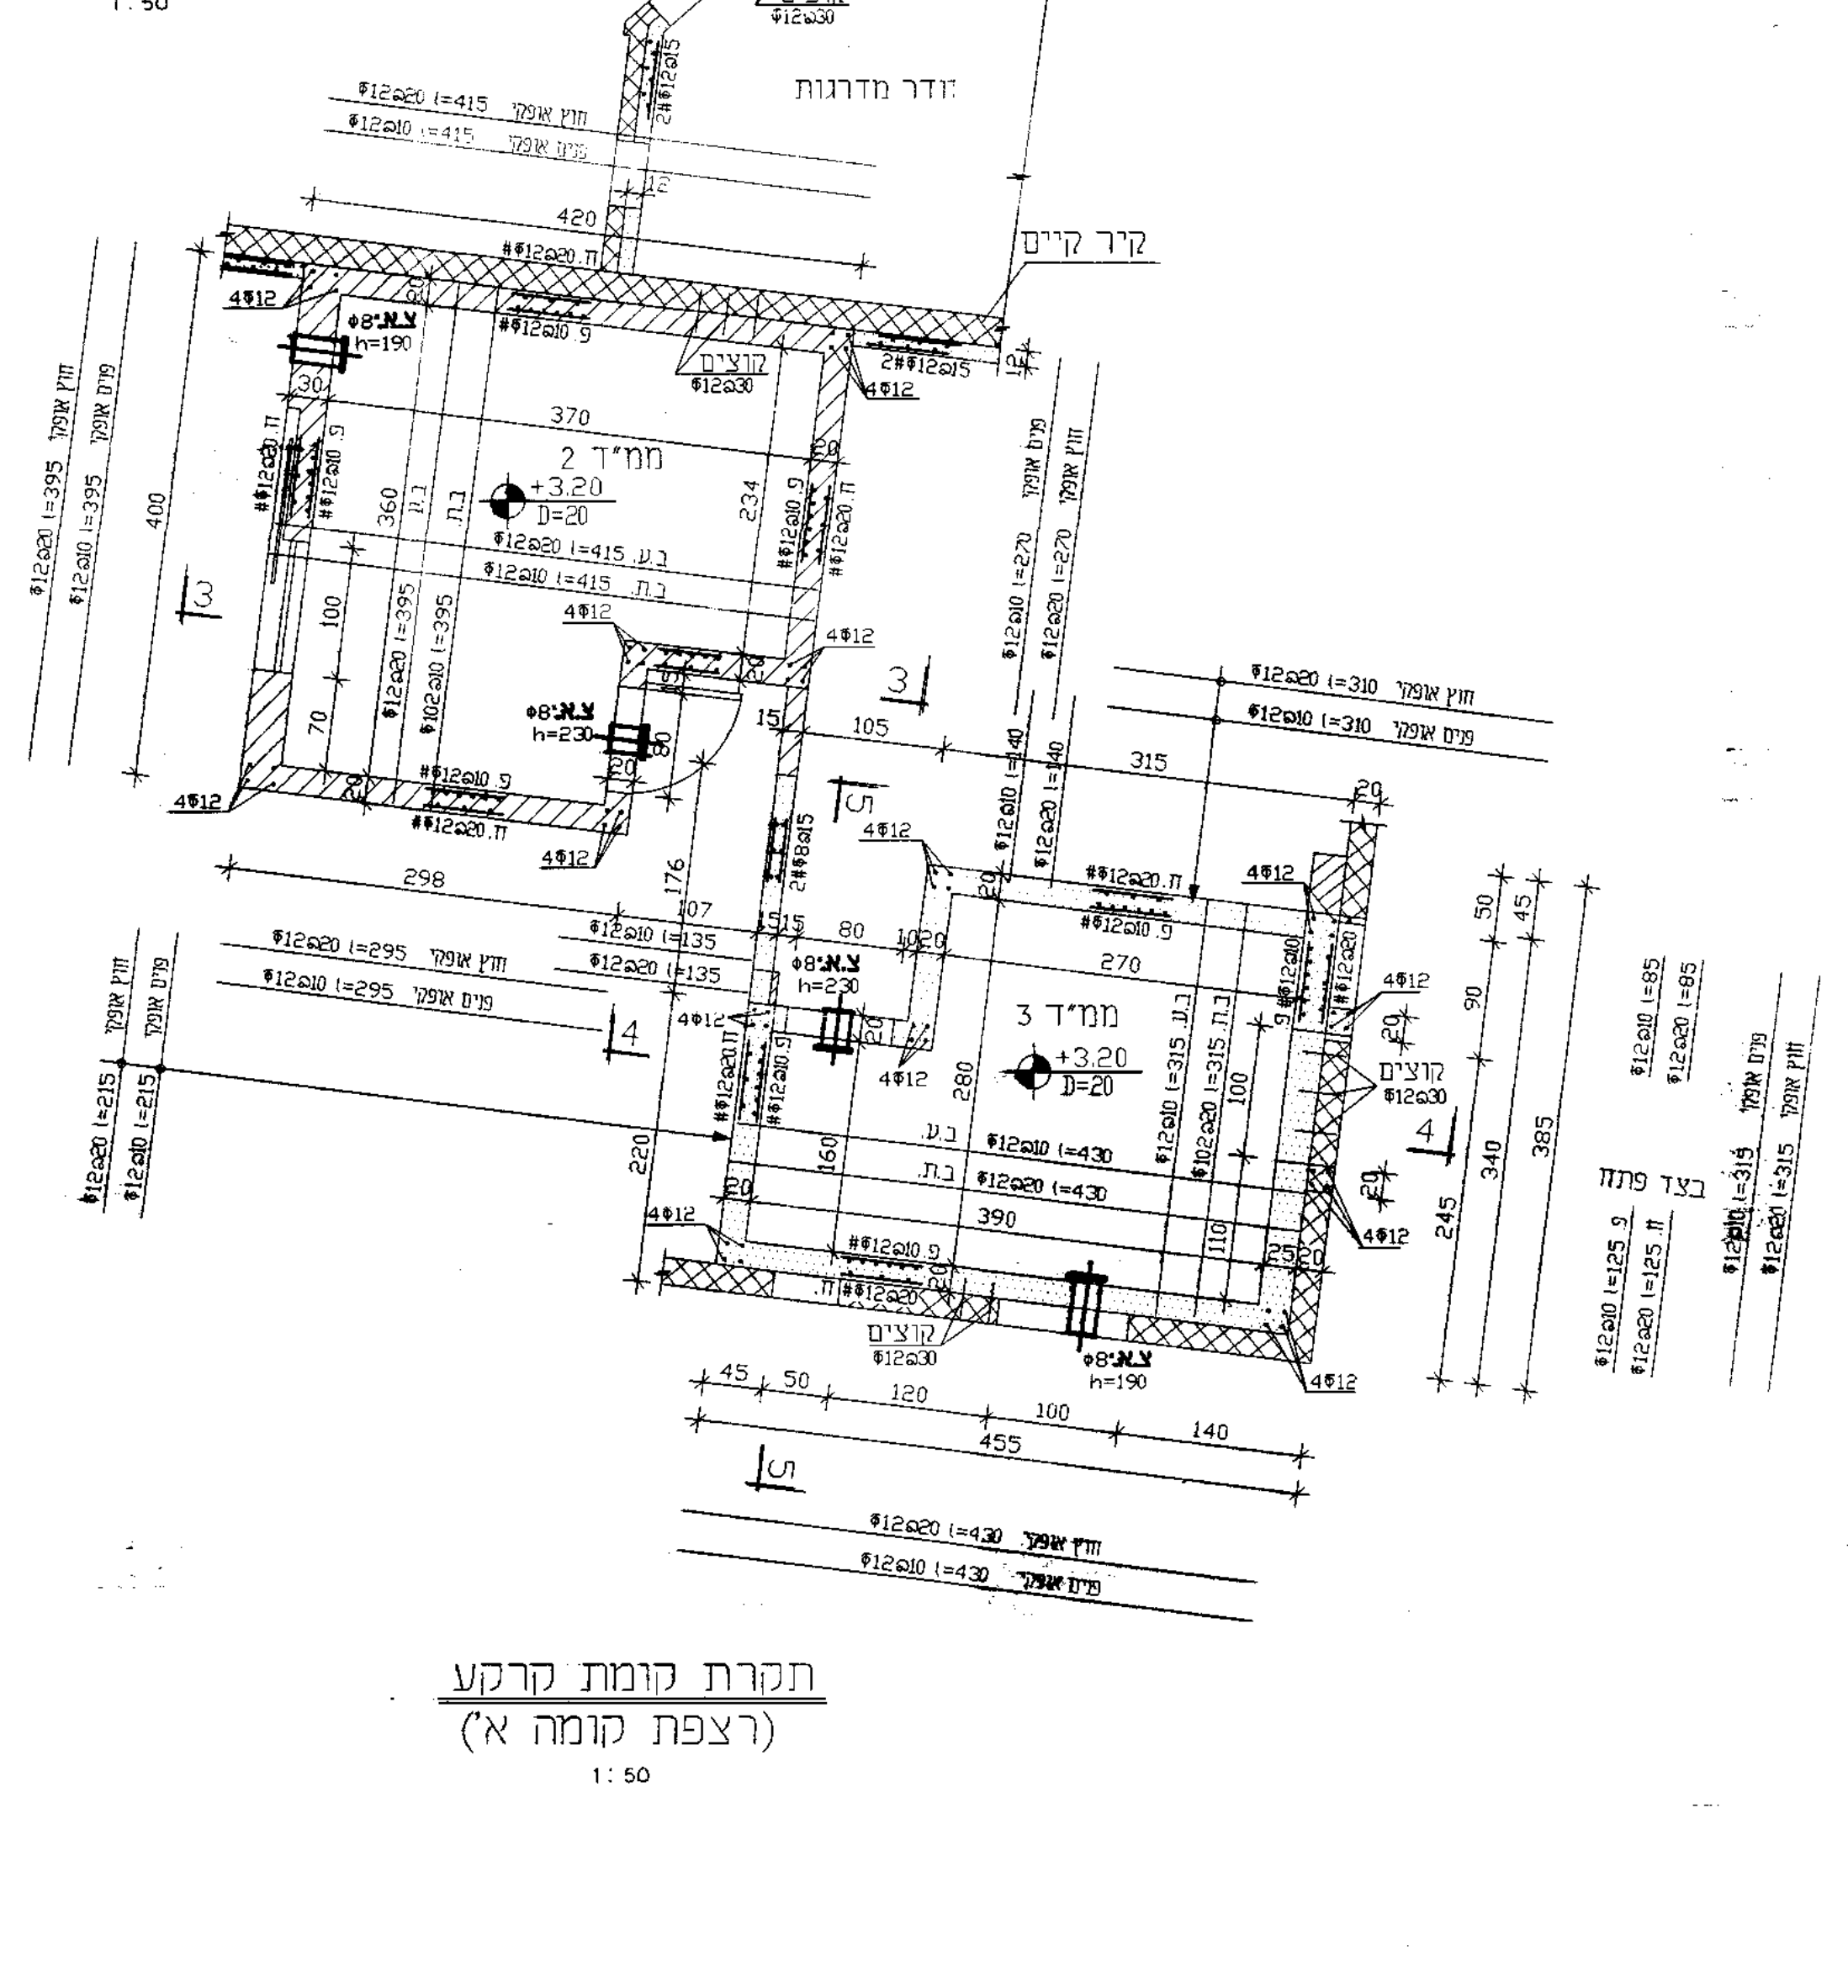
חדר מדרגות
קיר קיים
לא שייך לבקשה
ממ"ד 2
+3.20
ממ"ד 3
D=20
קוצים
Φ12@30
2#Φ12@15
חוץ אופקי Φ12@20 l=415
פנים אופקי Φ12@10 l=415
Φ12@20 l=395
Φ12@10 l=395
Φ12@20 l=295
Φ12@10 l=295
Φ12@20 l=215
Φ12@10 l=215
Φ12@20 l=270
Φ12@10 l=270
Φ12@20 l=135
Φ12@20 l=430
Φ12@10 l=430
Φ12@20 l=125
Φ12@10 l=125
Φ12@20 l=315
Φ12@10 l=315
בצד פתח
420
370
298
455
390
400

תקרת קומת קרקע

(רצפת קומה א')

1:50

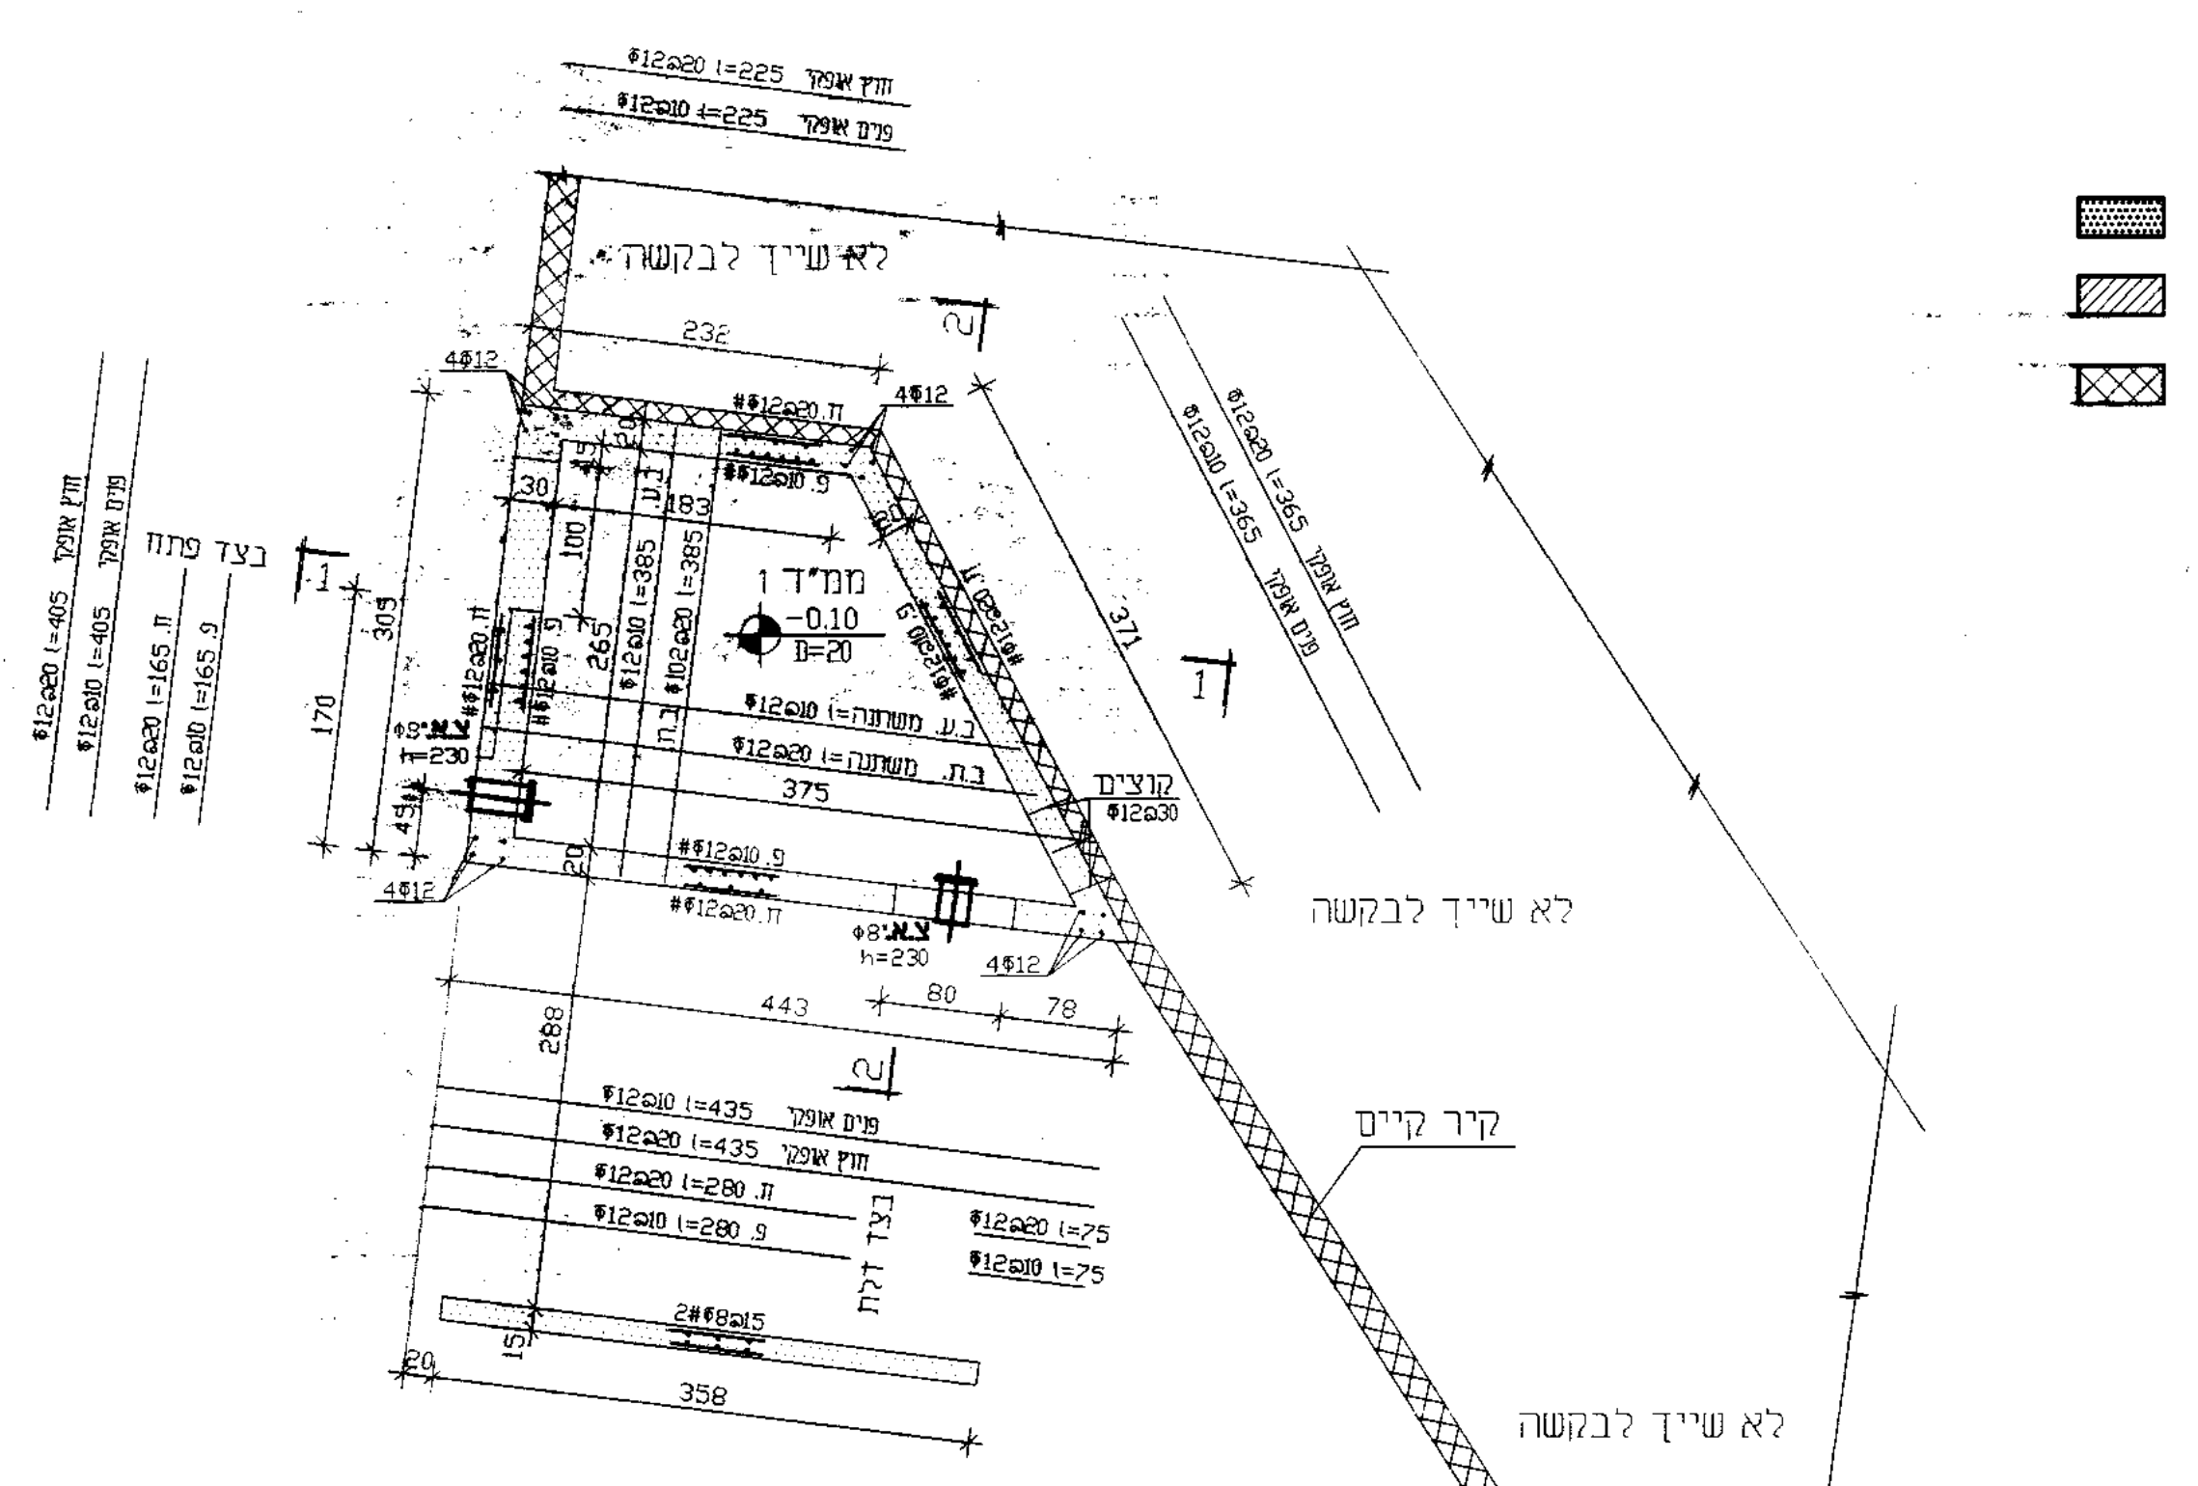
לא שייך לבקשה
קיר קיים
ממ"ד 1
-0.10
D=20
בצד פתח
בצד דלת
ב.ע. משתנה
ב.ת. משתנה
קוצים
Φ12@30
חוץ אופקי Φ12@20 l=225
פנים אופקי Φ12@10 l=225
Φ12@20 l=365
Φ12@10 l=365
Φ12@20 l=405
Φ12@10 l=405
Φ12@20 l=435
Φ12@10 l=435
Φ12@20 l=75
Φ12@10 l=75
2#Φ8@15
232
375
443
358
288
305
170

רצפת קומת קרקע

1:50

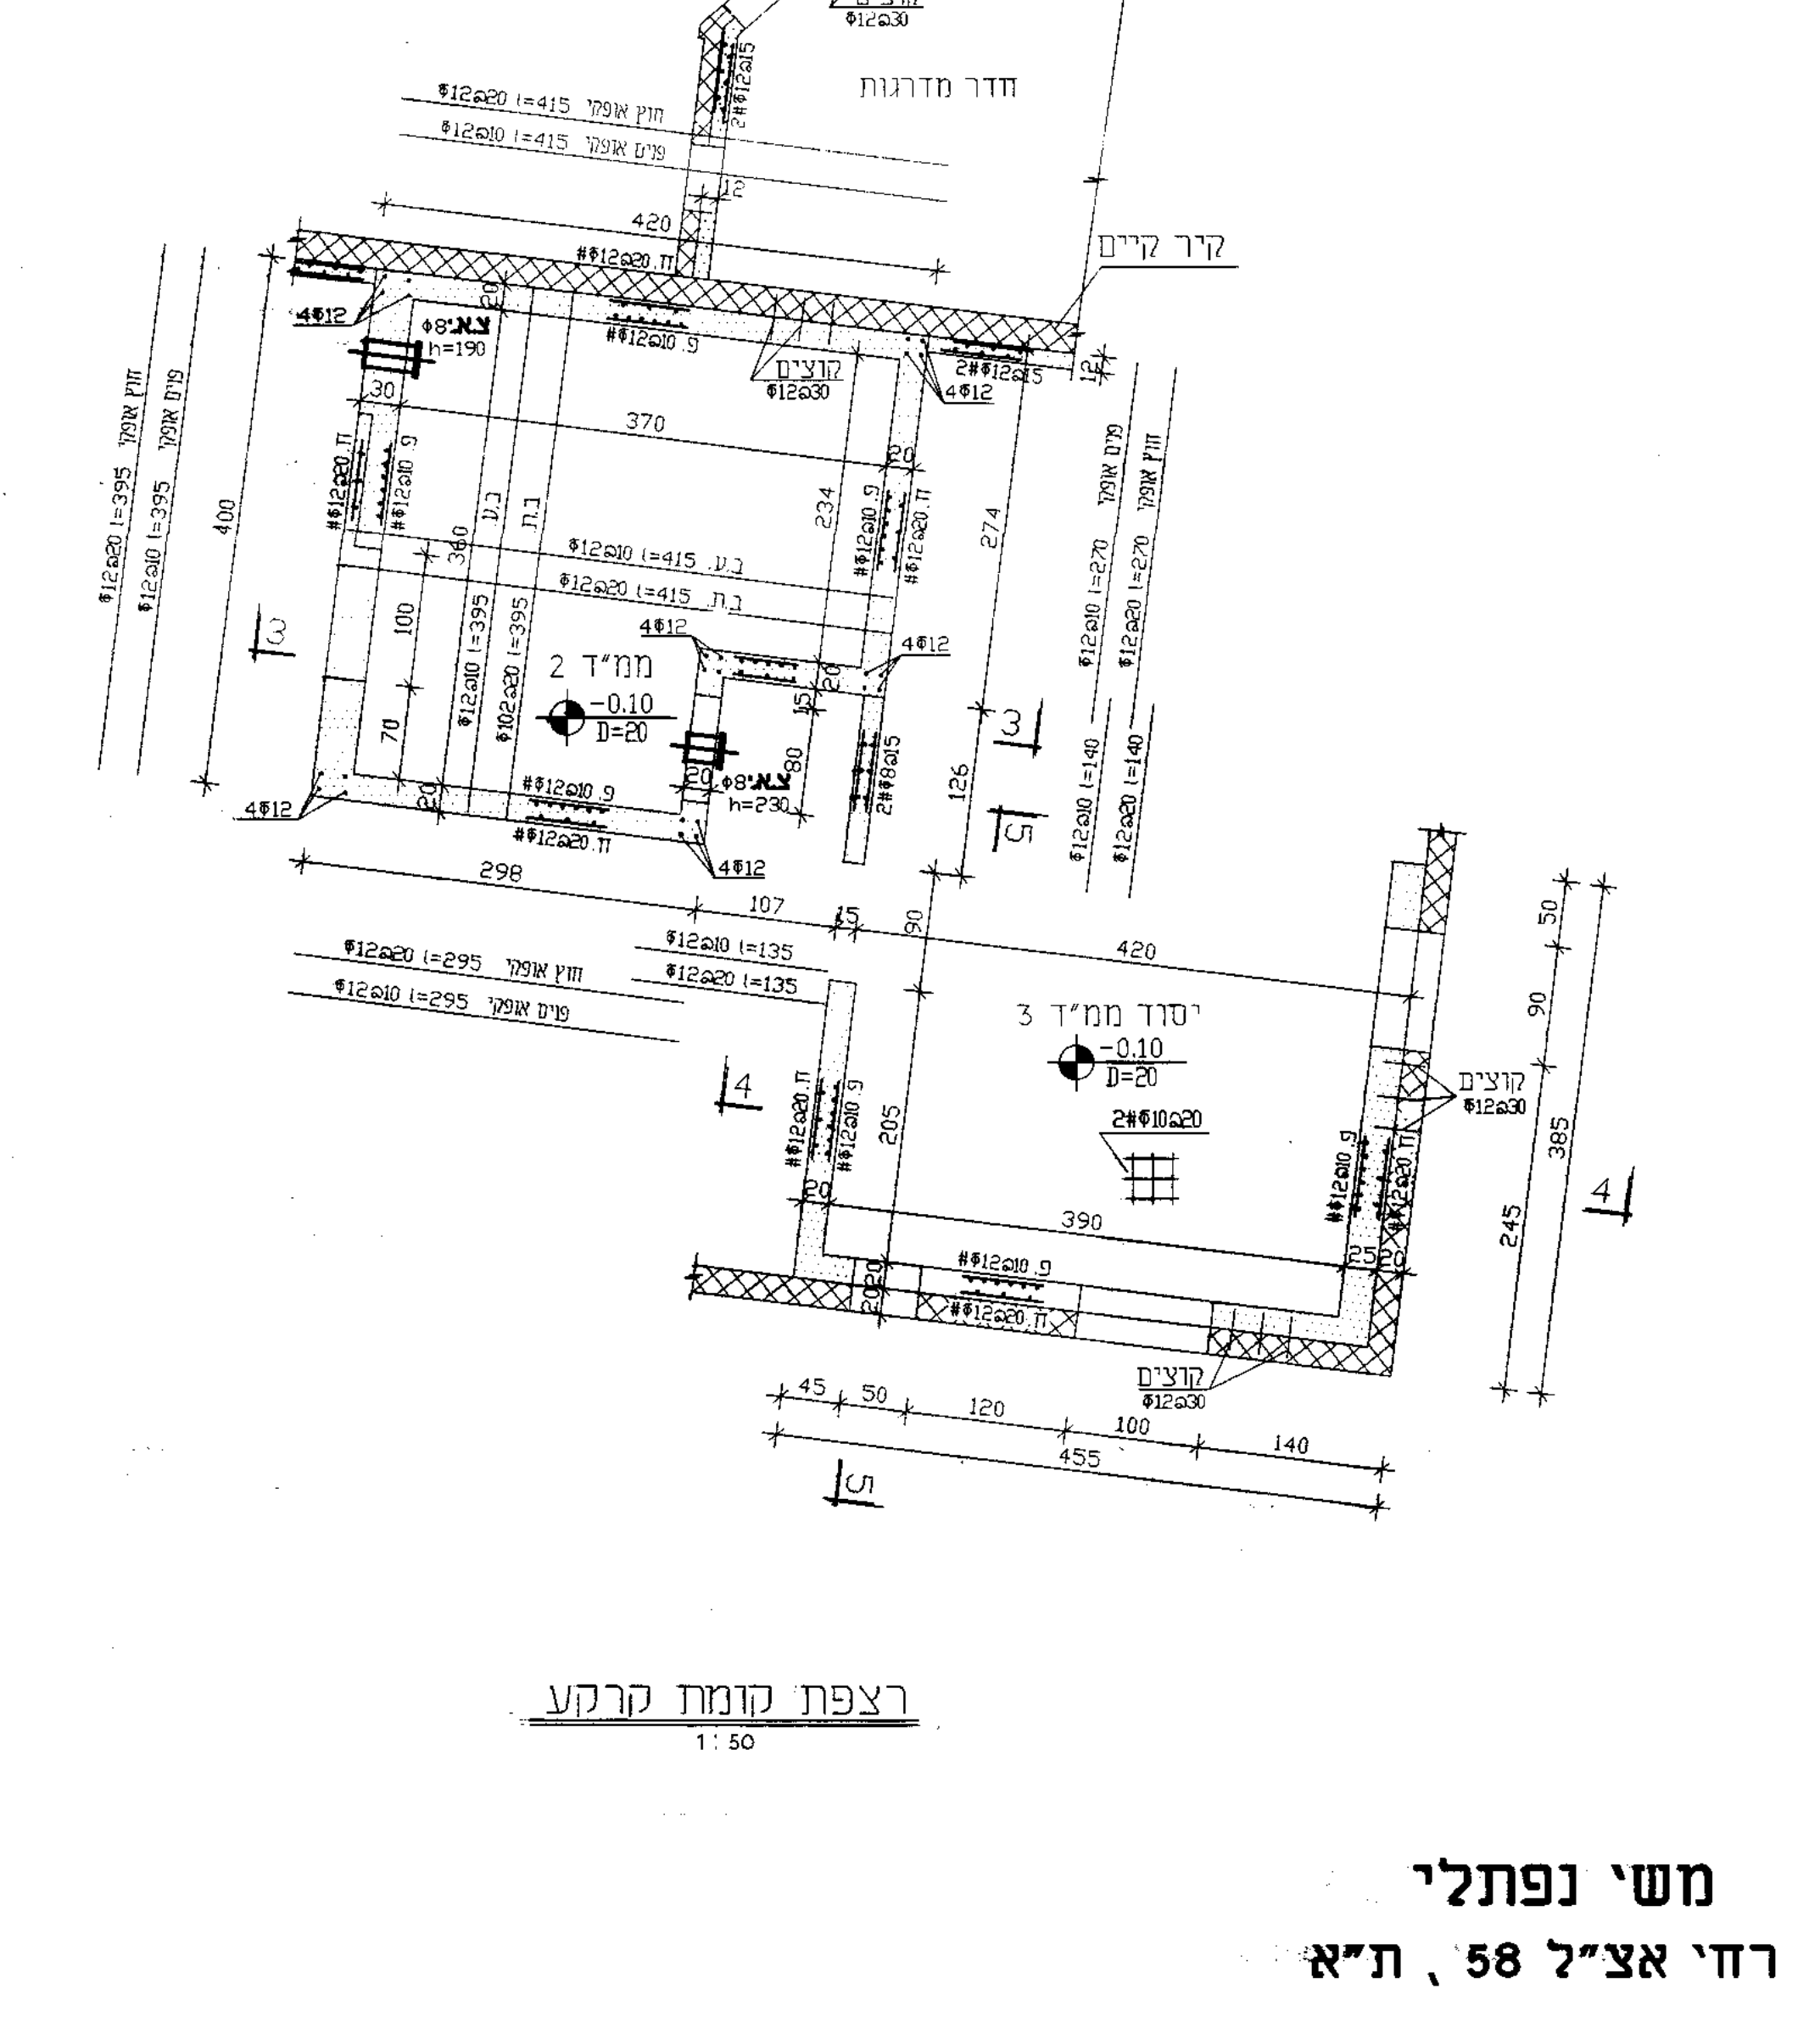
חדר מדרגות
קיר קיים
לא שייך לבקשה
ממ"ד 2
-0.10
יסוד ממ"ד 3
D=20
2#Φ10@20
קוצים
Φ12@30
חוץ אופקי Φ12@20 l=415
פנים אופקי Φ12@10 l=415
Φ12@20 l=395
Φ12@10 l=395
Φ12@20 l=295
Φ12@10 l=295
Φ12@20 l=270
Φ12@10 l=270
Φ12@20 l=140
Φ12@10 l=140
Φ12@10 l=135
420
370
298
455
390
385

רצפת קומת קרקע

1:50

מיקרא:

- ▩ בטון ממשיך
- ▨ בטון מפסיק
- ☒ קיים

משי נפתלי

רחי אצ"ל 58 , ת"א

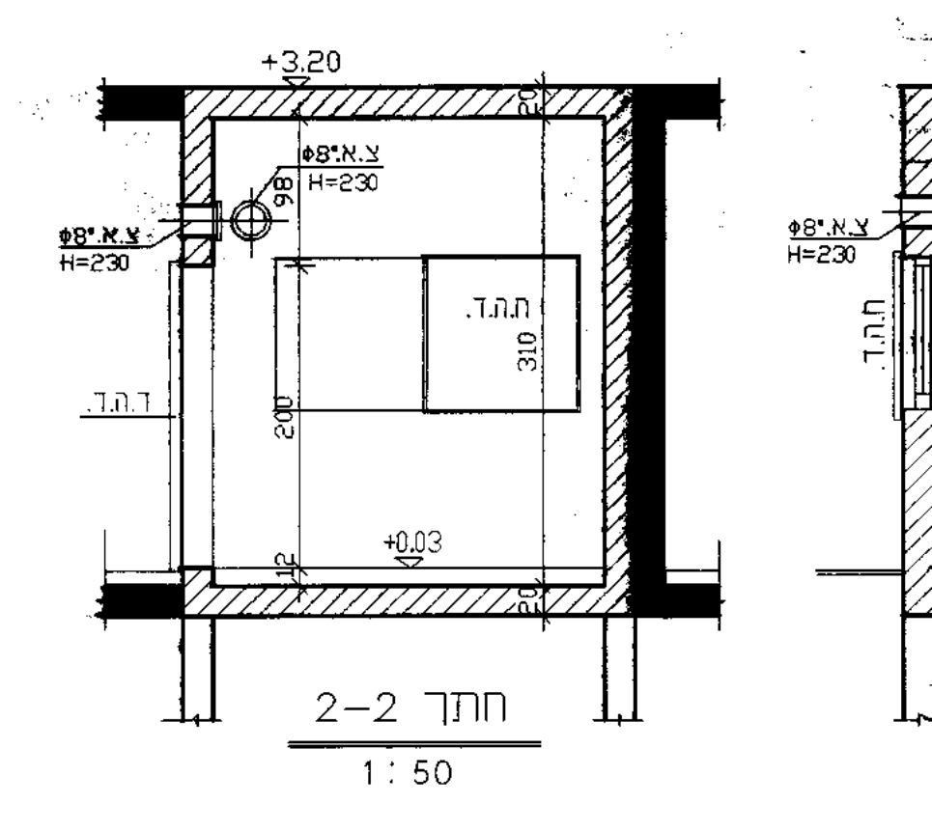
+3.20
Φ8"צ.א.
H=230
ת.ה.ד.
ד.ה.ת.
+0.03
200
310

חתך 2–2

1:50

מקרא

- ⅄ שקע
- ⊐ T.V טלויזיה
- ⓣ טלפון
- ⓗ 40w ג.ת. חרום
- ▬ ג.ת. פלורסנט 2✱40w
- ♂ מפסק בודד

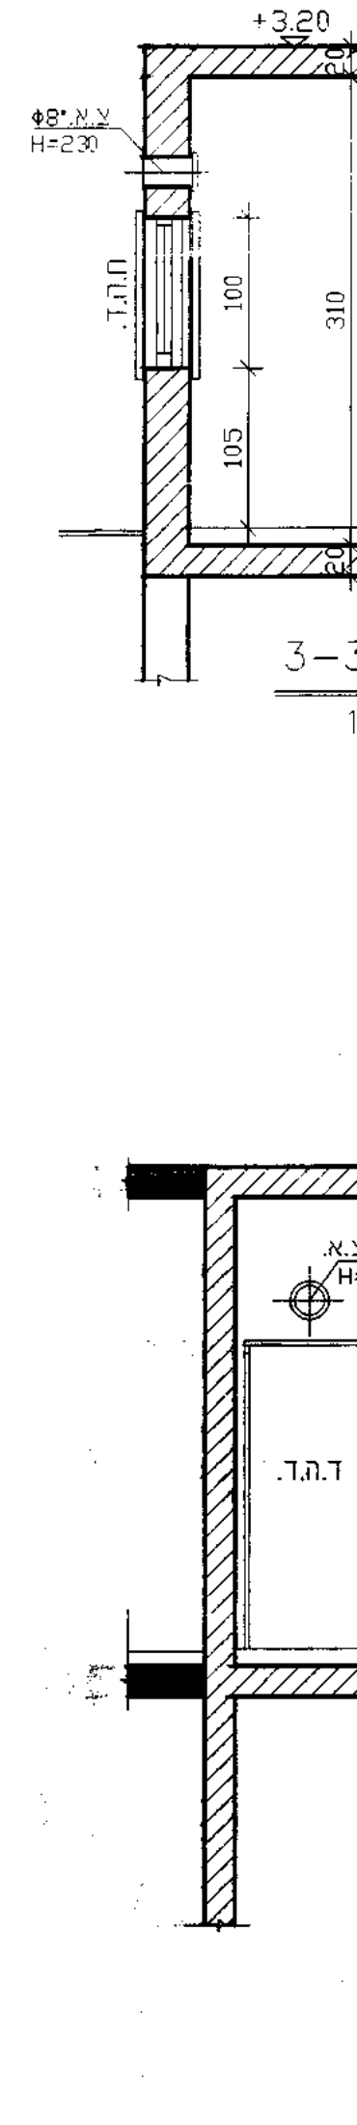
+3.20
Φ8"צ.א.
H=230
ת.ה.ח.
100
105
310
ד.ה.ד.
3–3