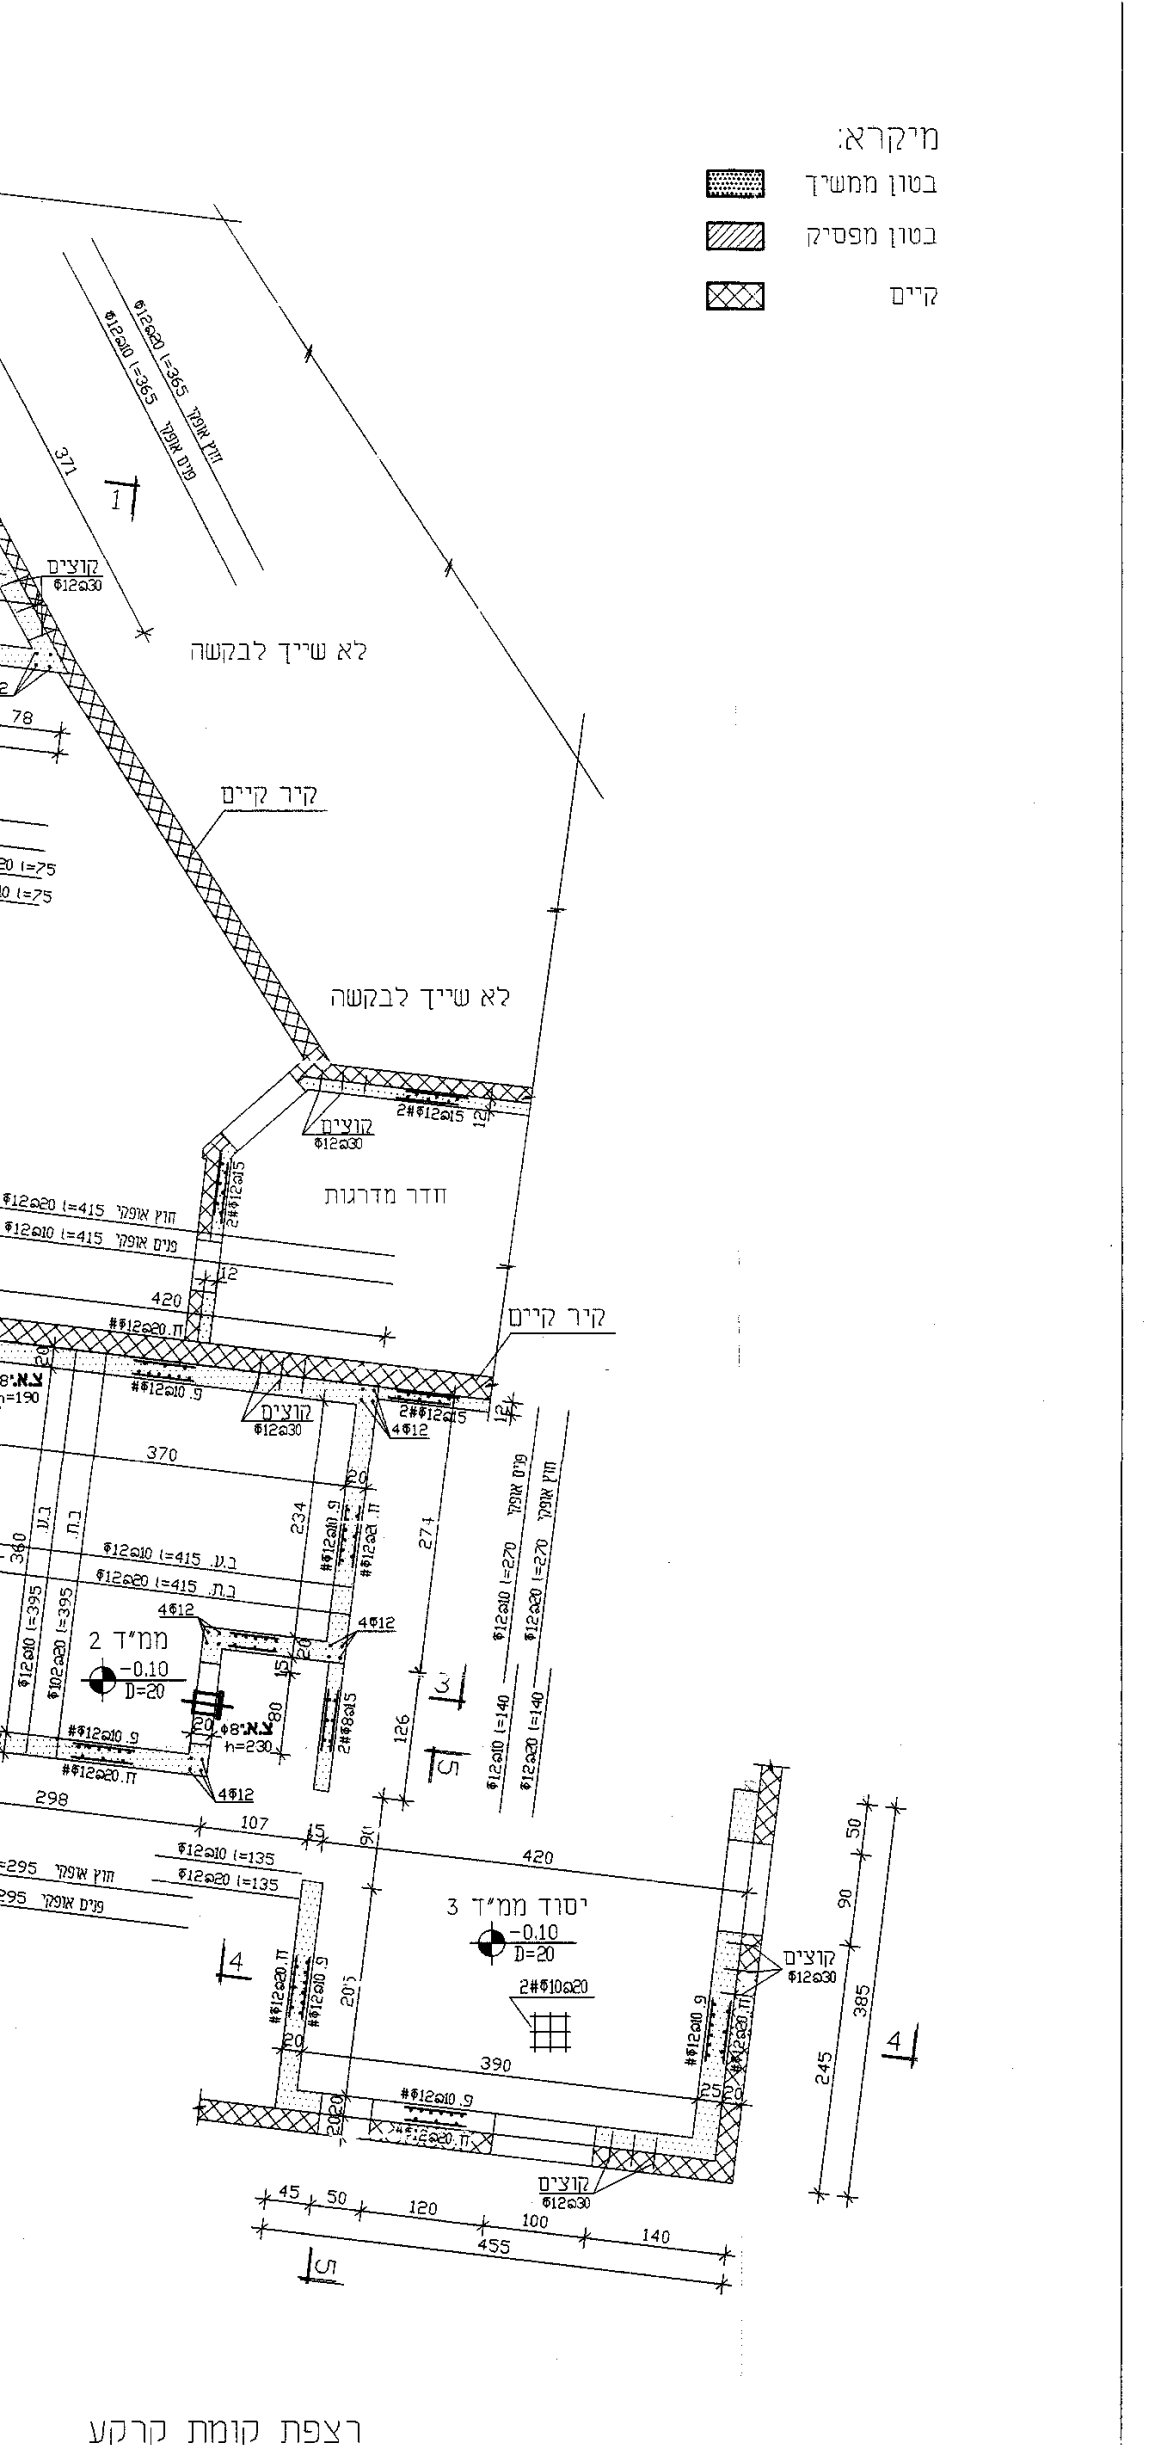
מיקרא:
בטון ממשיך
בטון מספק
קיים
לא שייך לבקשה
קיר קיים
ממ"ד 2
ממ"ד 3
חדר מדרגות

רצפת קומת קרקע
1:50

משי נפתלי
רח' אצ"ל 58, ת"א

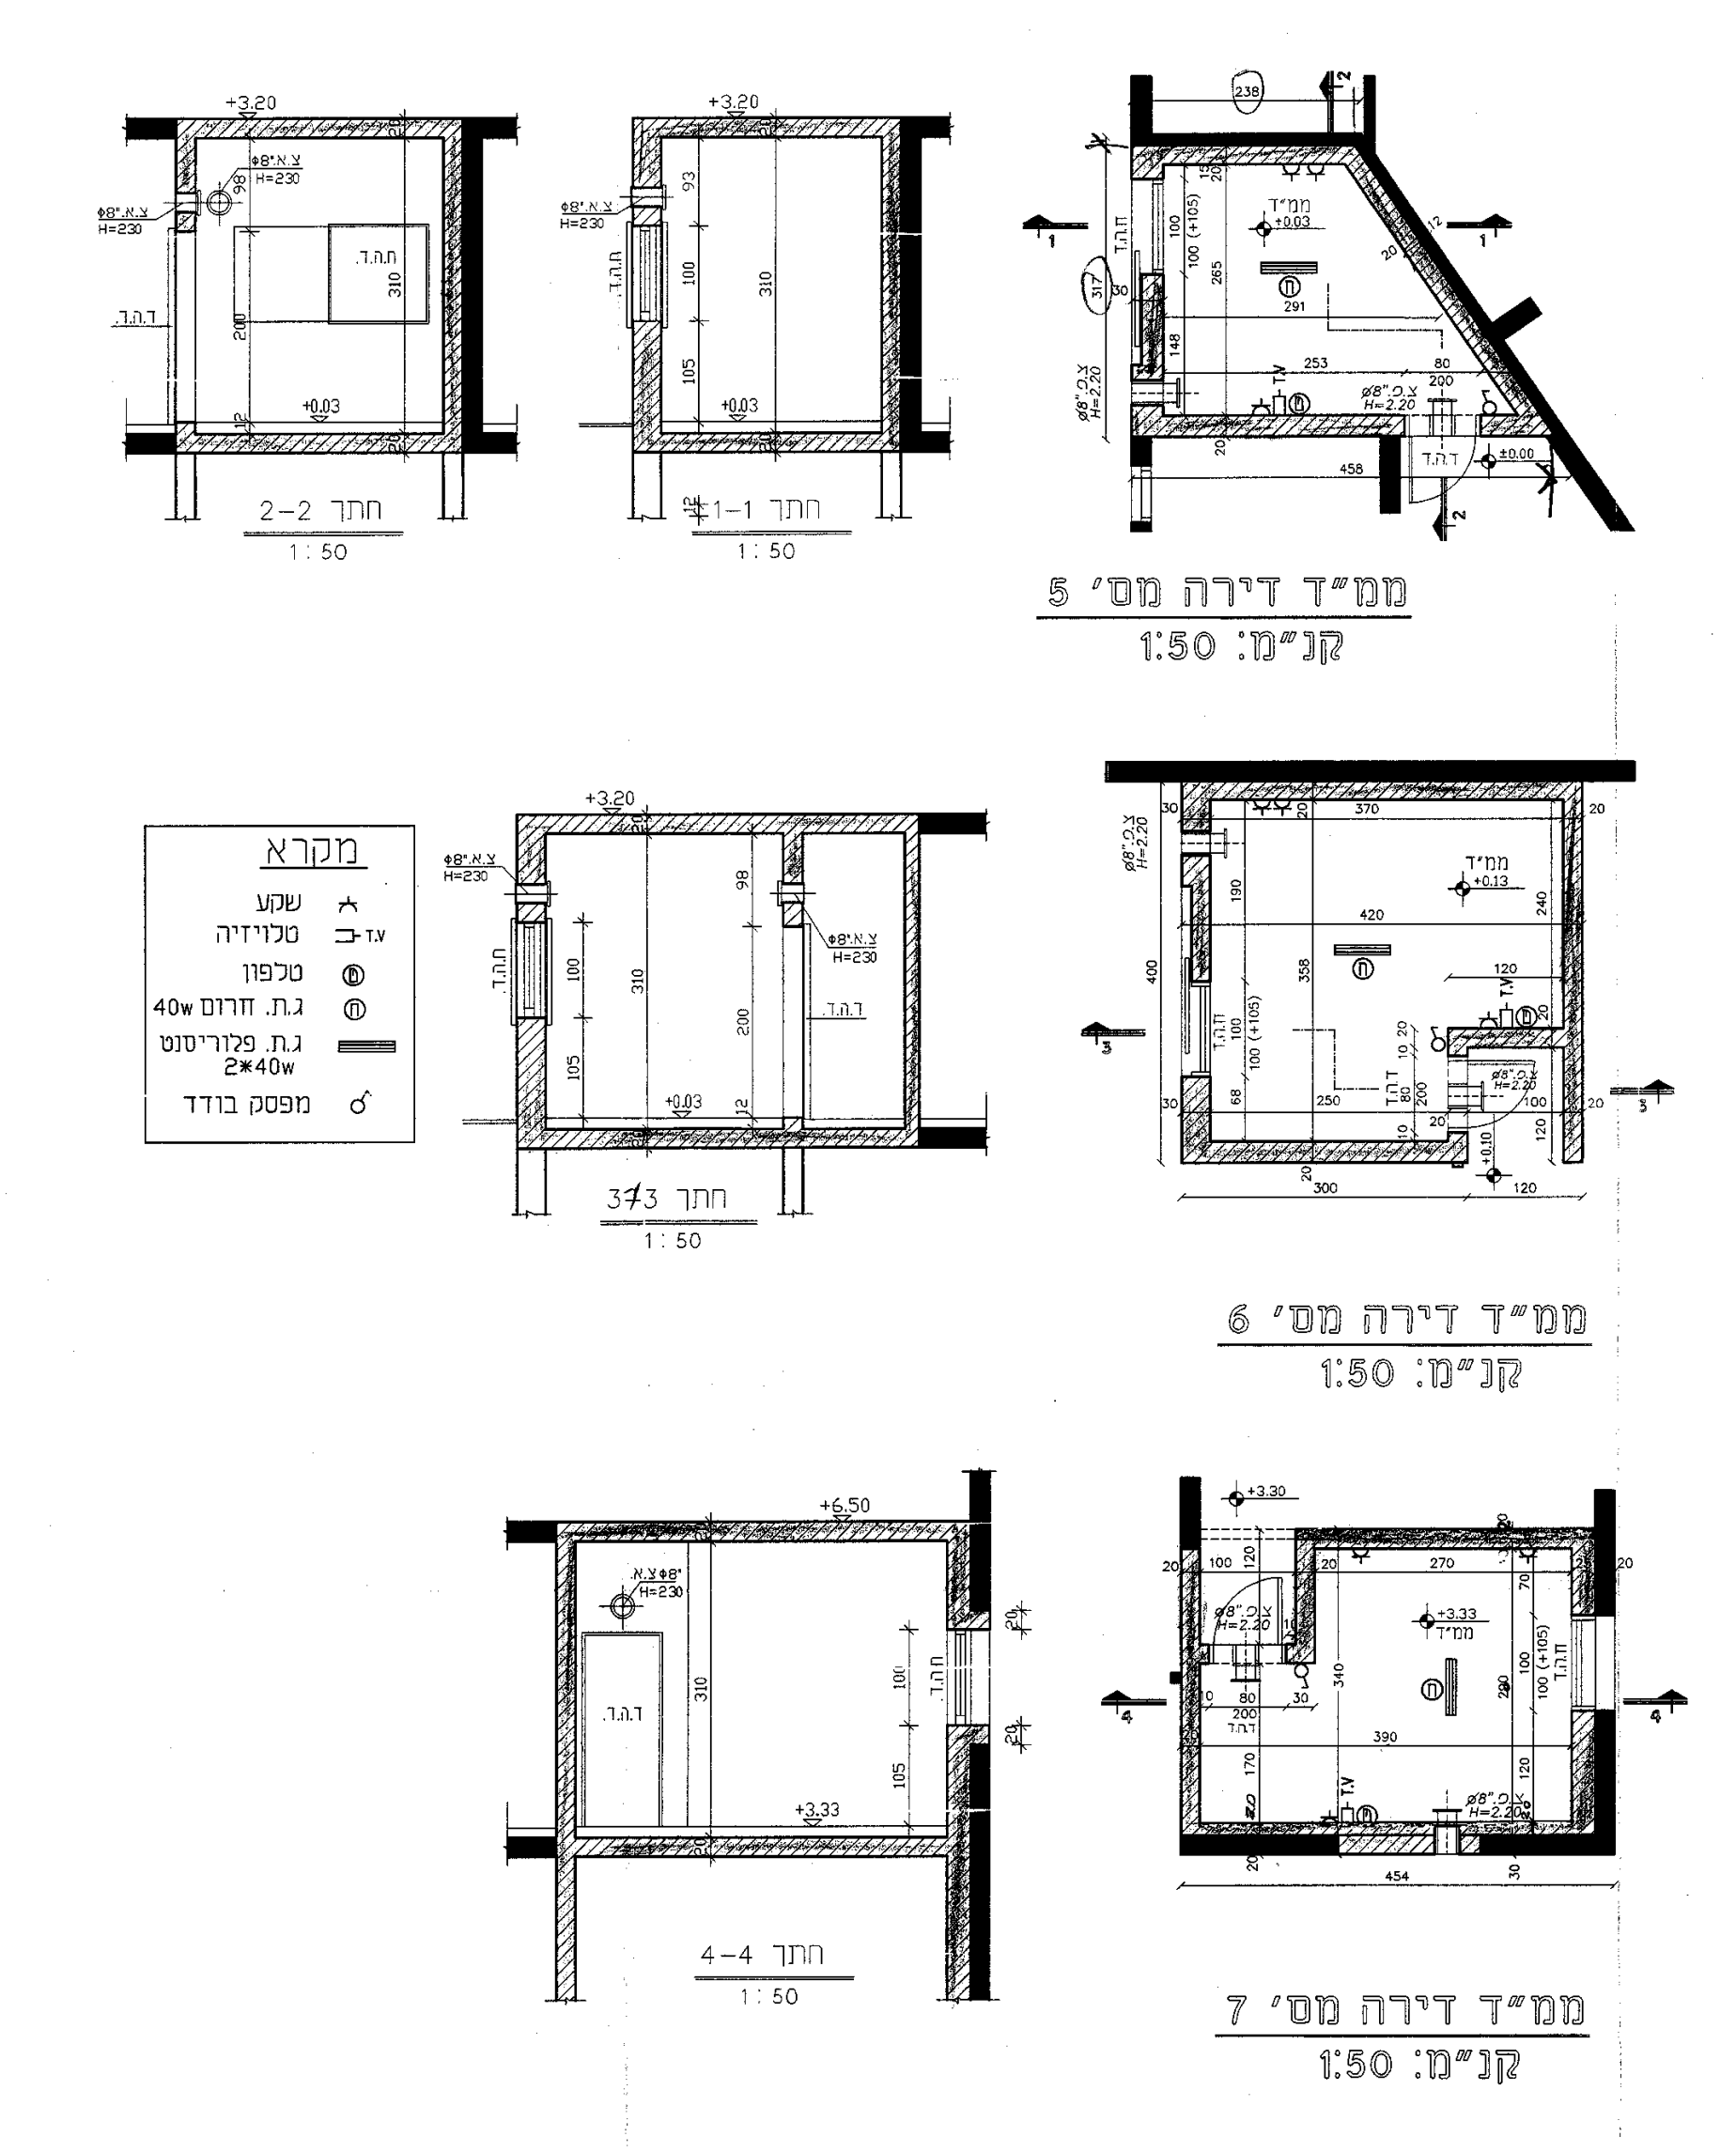
חתך 2-2
1:50
חתך 1-1
1:50
חתך 3-3
1:50
חתך 4-4
1:50
מקרא
שקע
טלויזיה
טלפון
ג.ת. חרום 40w
ג.ת. פלורסנט 2x40w
מפסק בודד

ממ"ד דירה מס' 5
קנ"מ: 1:50

ממ"ד דירה מס' 6
קנ"מ: 1:50

ממ"ד דירה מס' 7
קנ"מ: 1:50

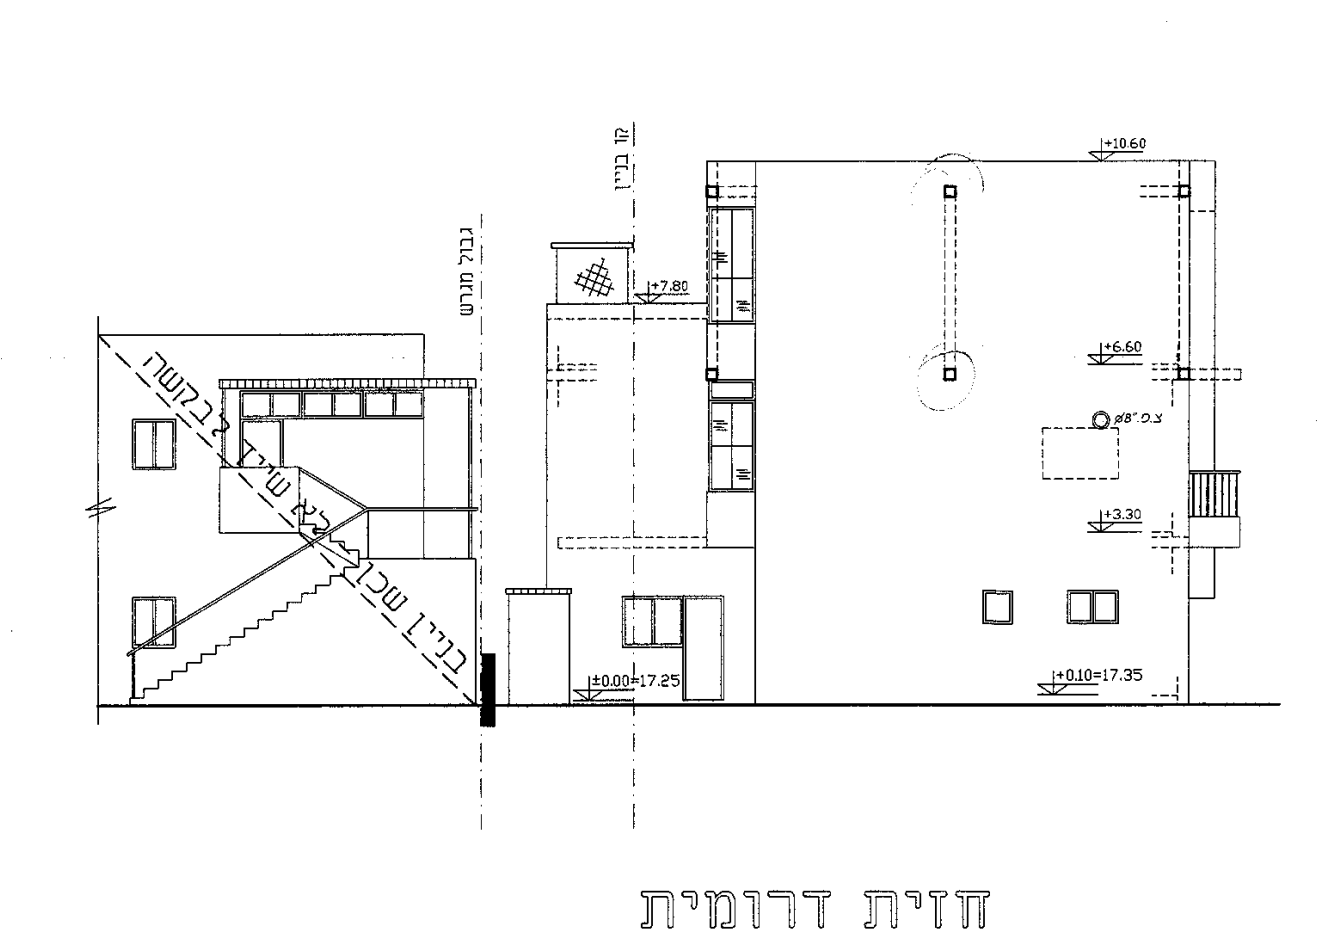
בניין שכן - לא שייך לבקשה

חזית דרומית
קנ"מ: 1:100

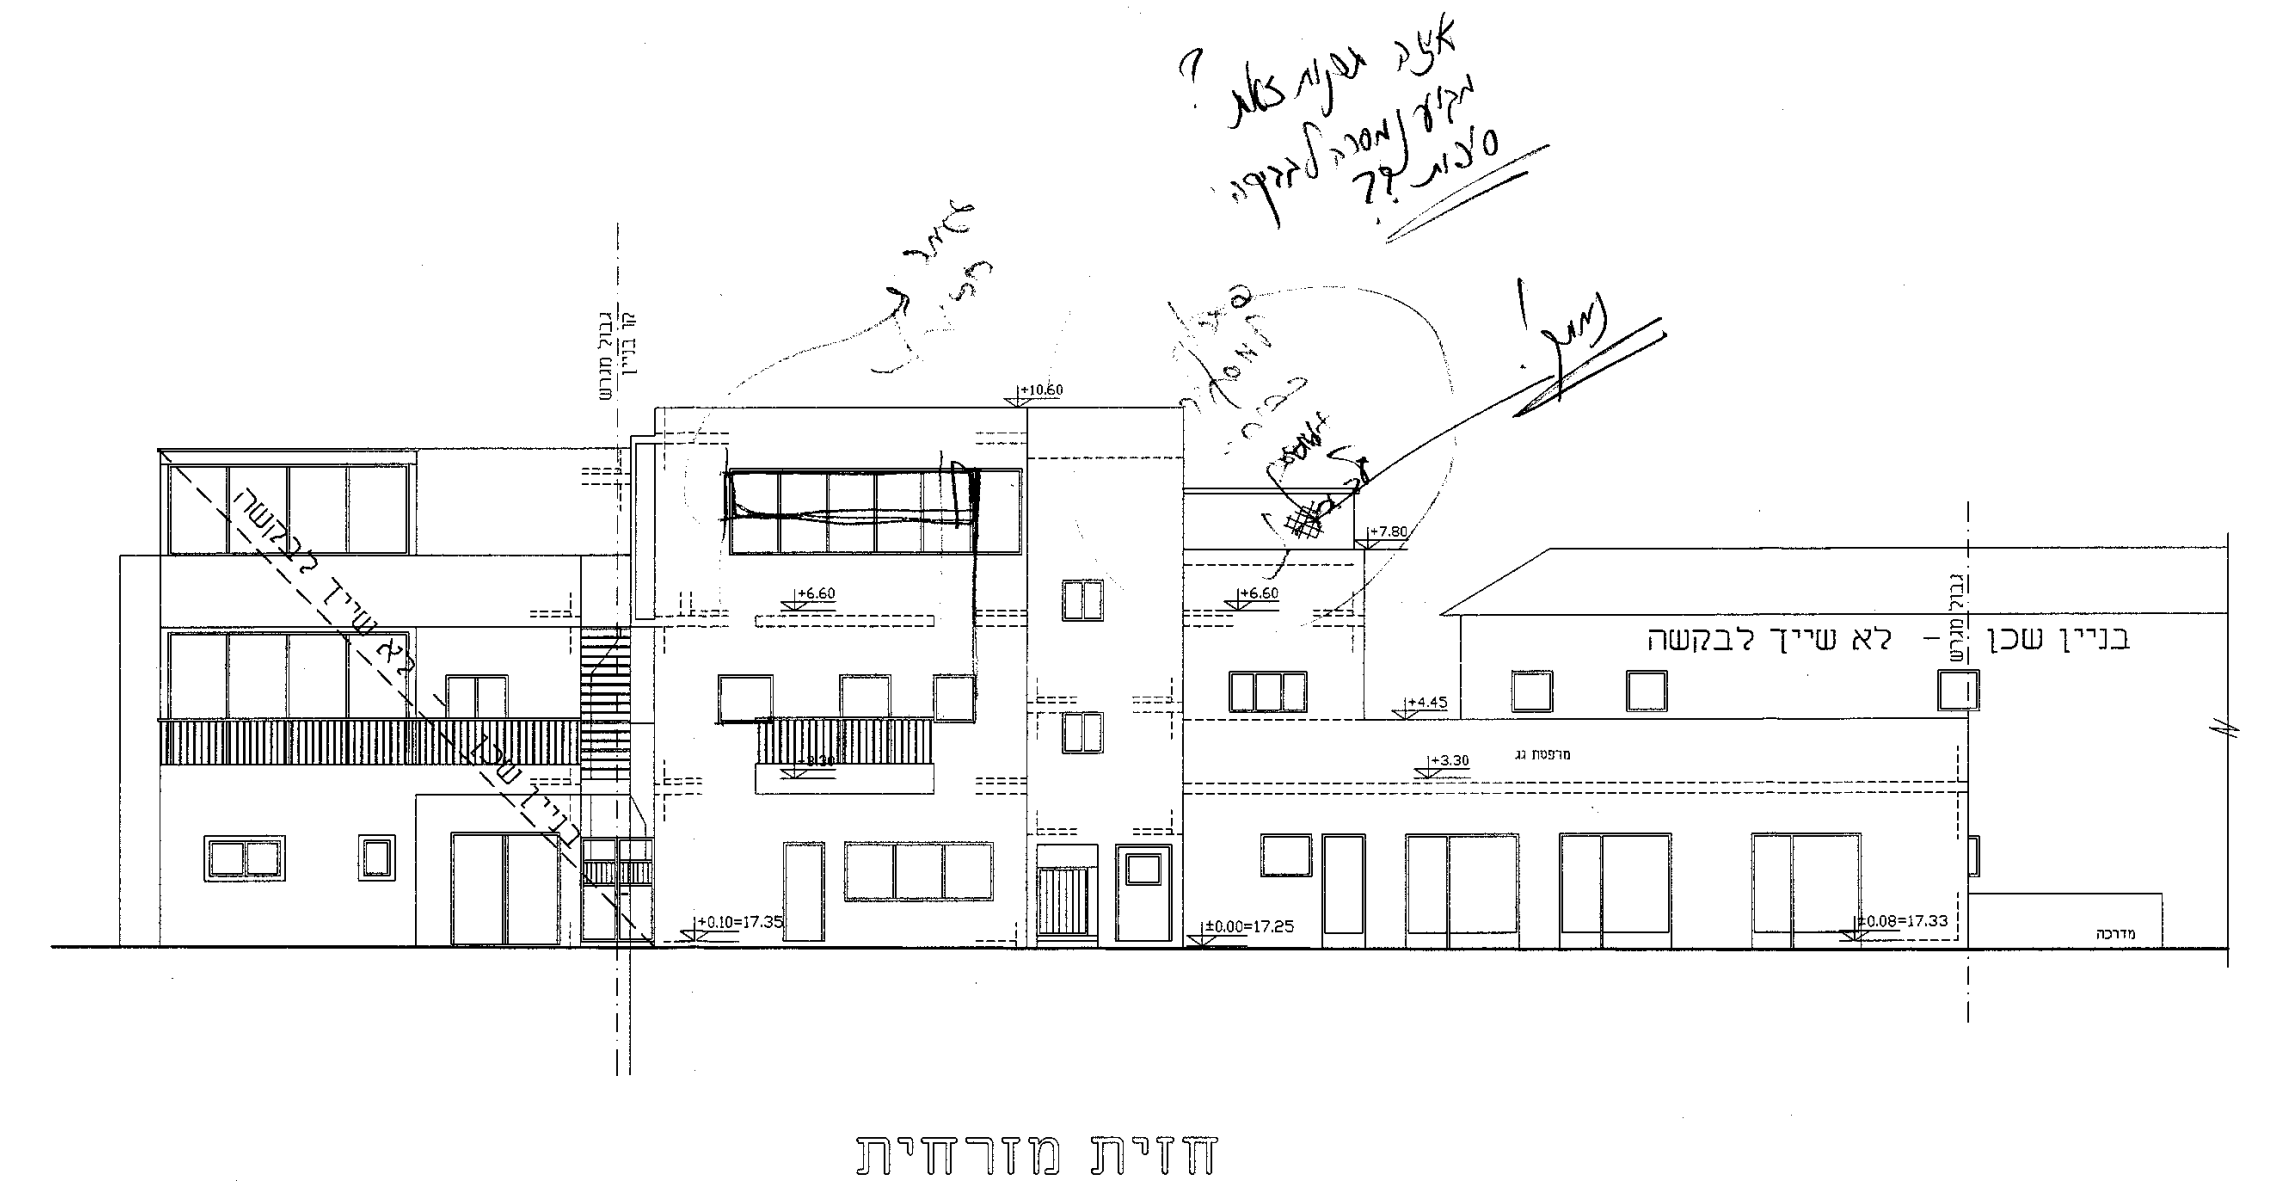
בניין שכן - לא שייך לבקשה
אצל גוון צבע
מקומי למבנה לבנוני
סטנדרט

חזית מזרחית
קנ"מ: 1:100

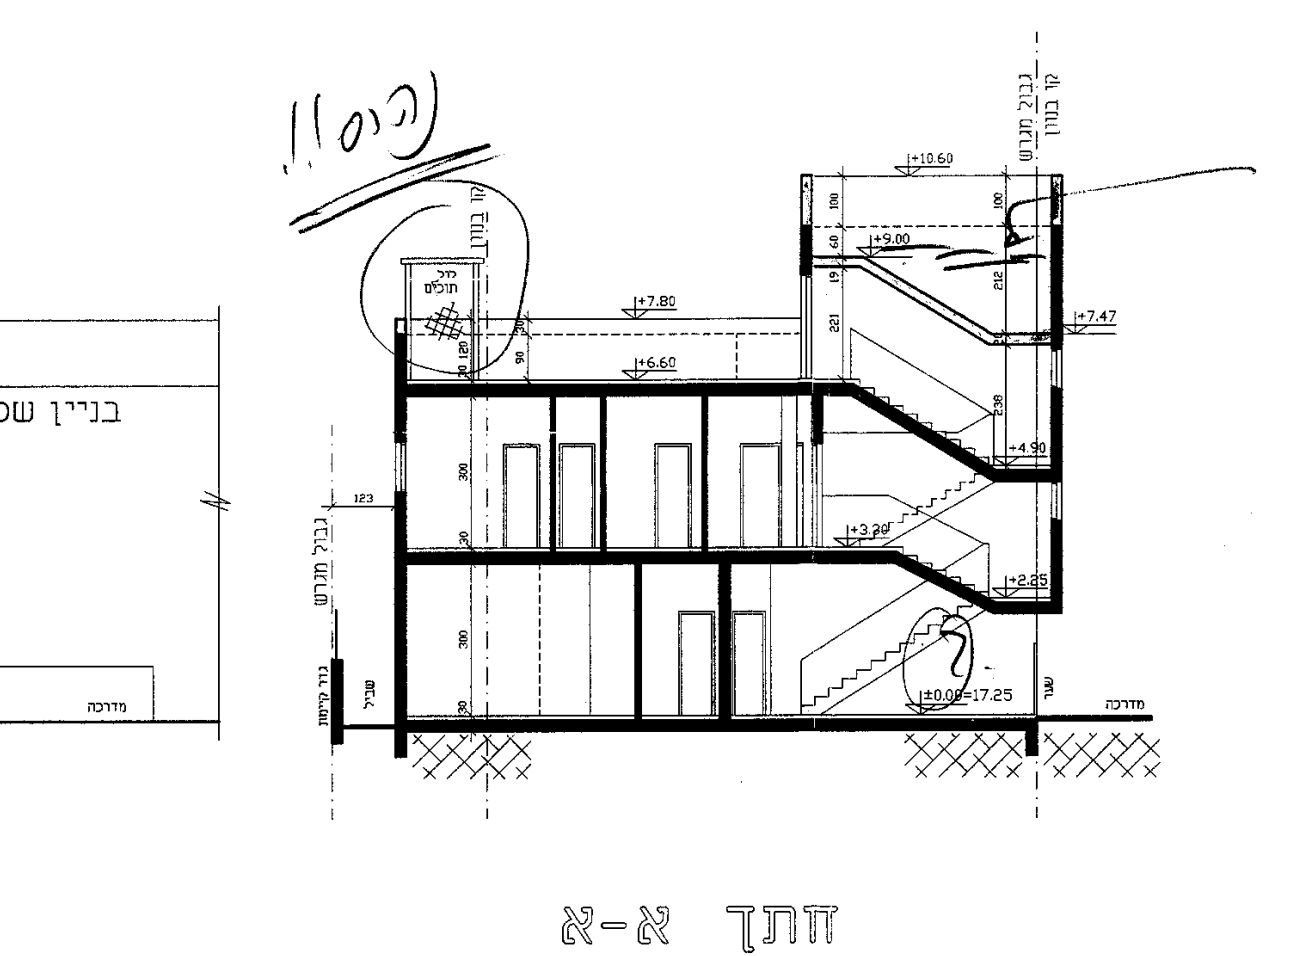

חתך א-א
קנ"מ: 1:100

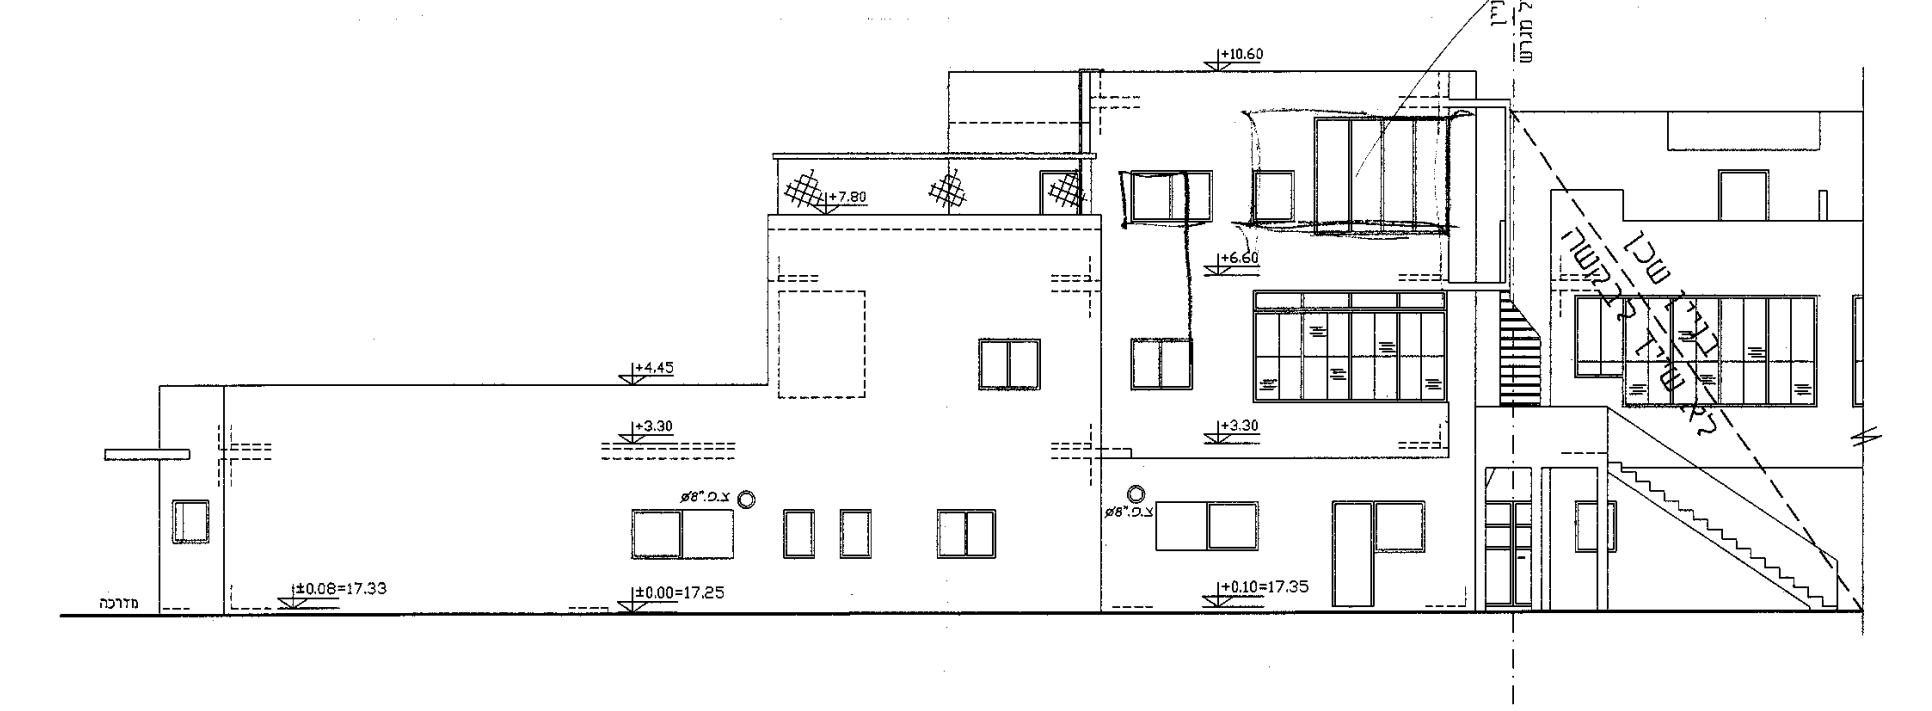
בניין שכן - לא שייך לבקשה

חזית מערבית
קנ"מ: 1:100

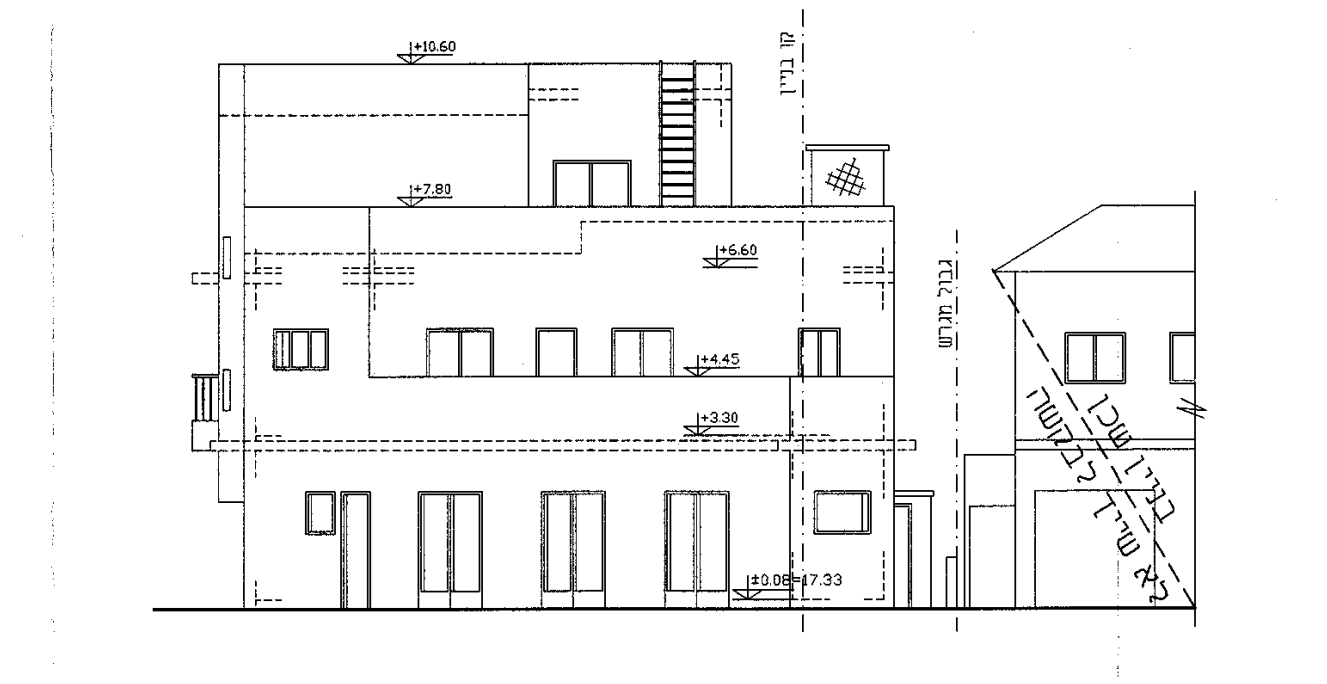
בניין שכן - לא שייך לבקשה

חזית צפונית
קנ"מ: 1:100

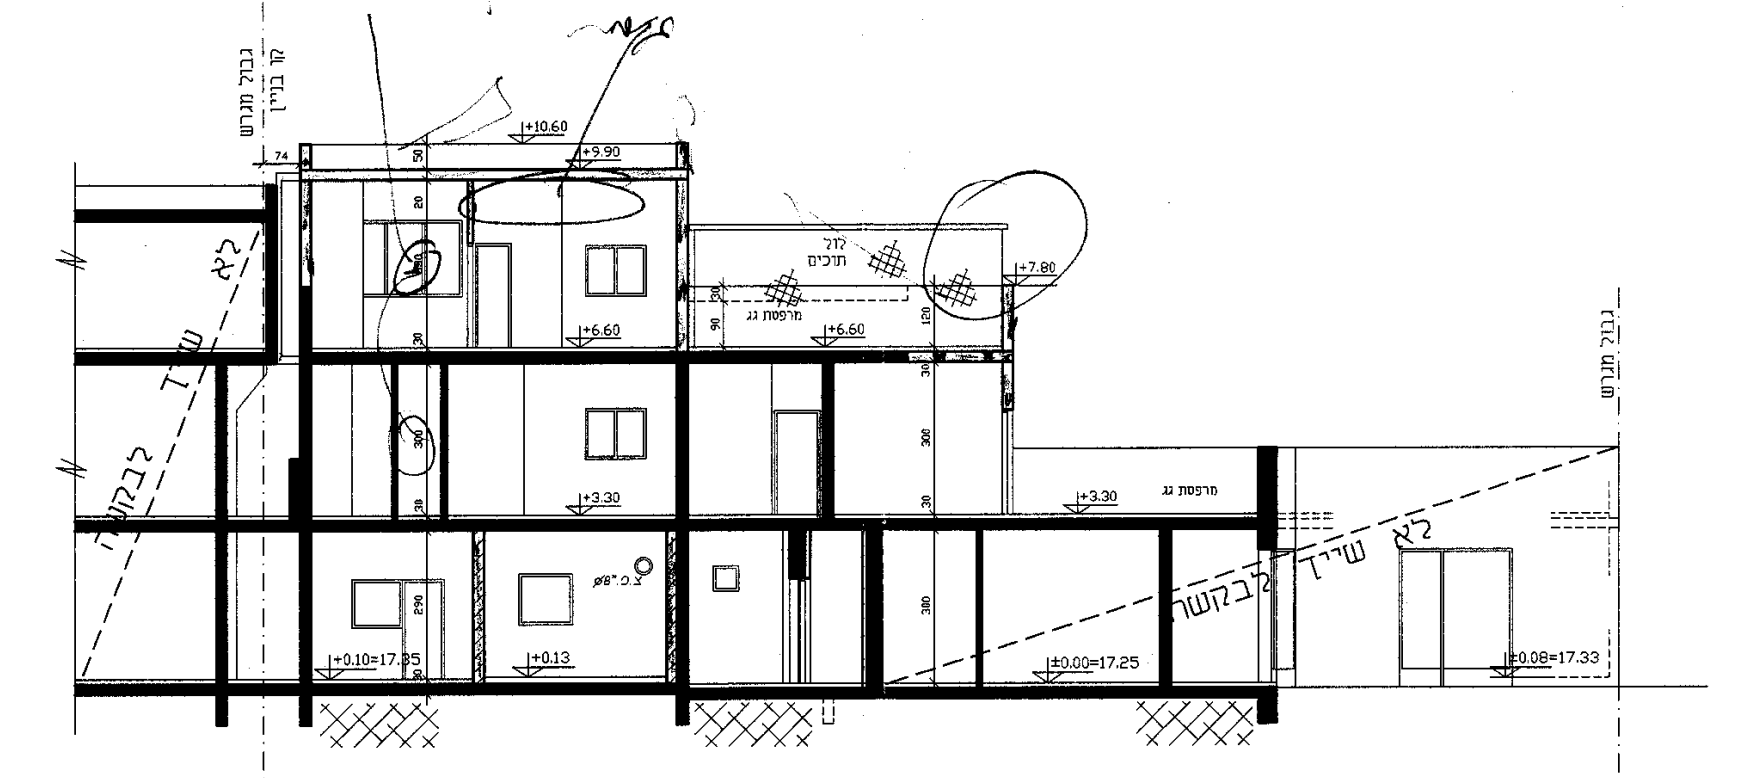
לא שייך לבקשה

חתך ב-ב
קנ"מ: 1:100

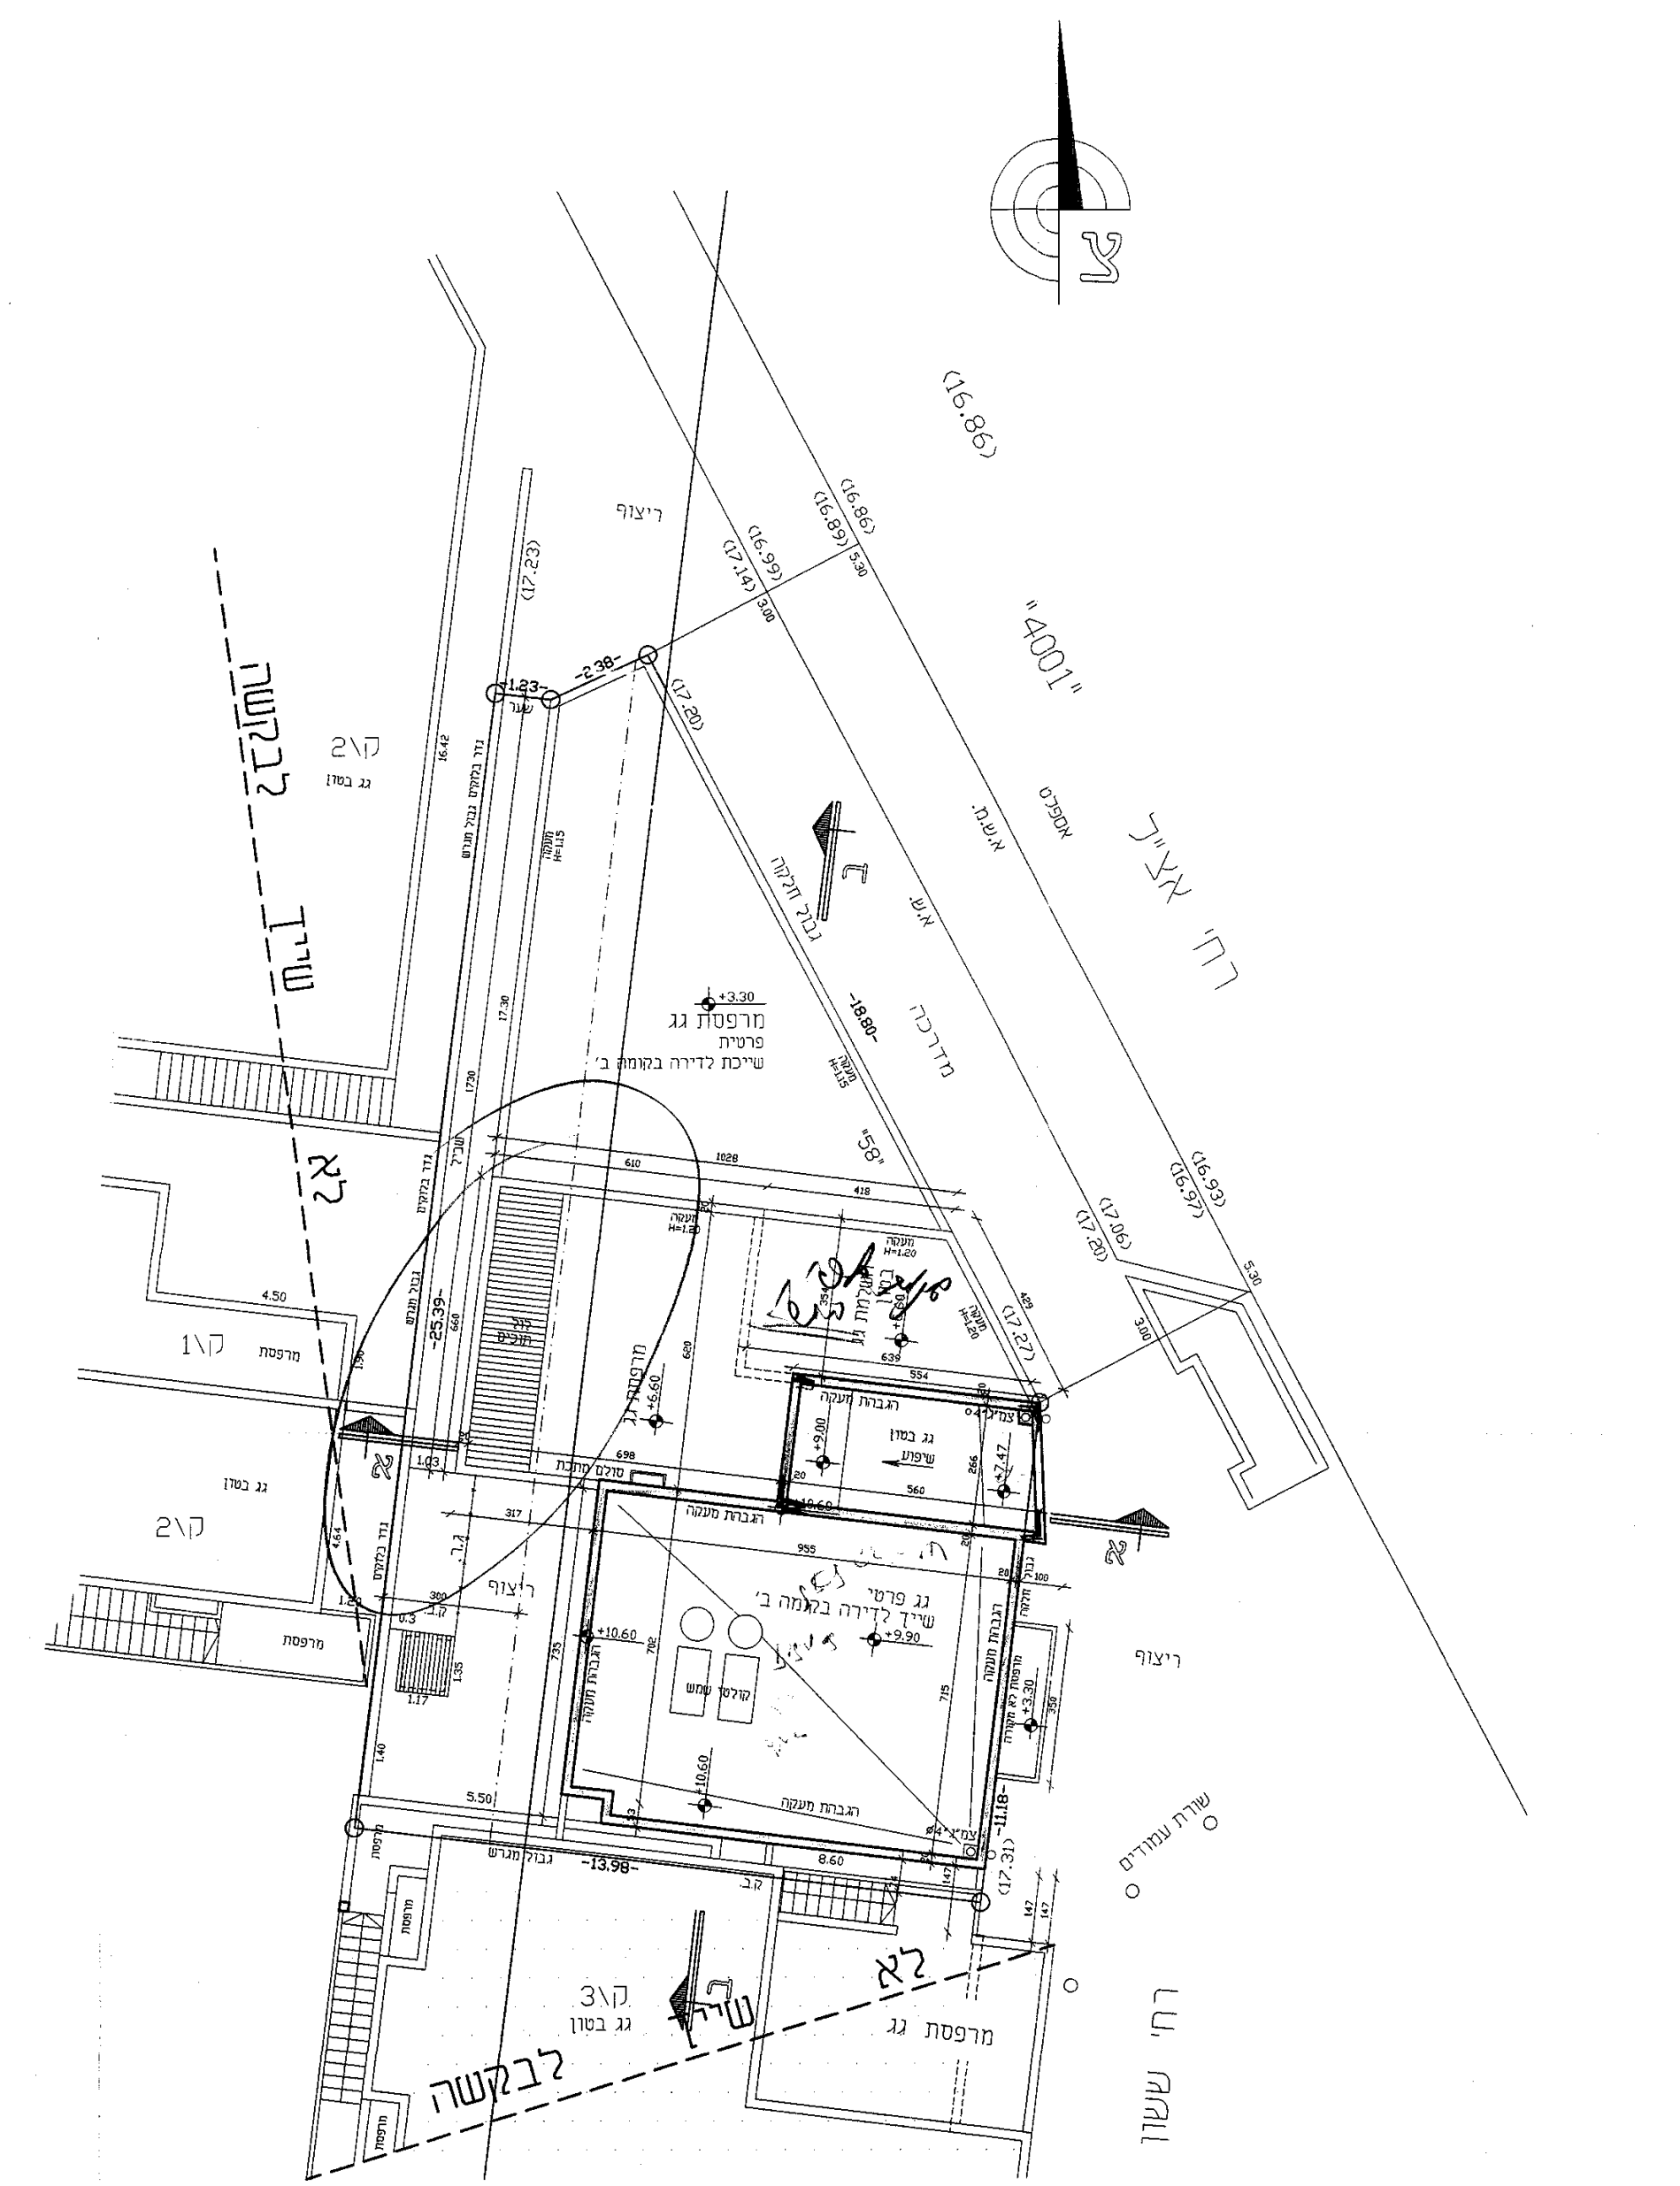
רח' אצ"ל
(16.86)
"4001"
ריצוף
שייך לבקשה
מרפסת גג
מדרכה
ק\1
ק\2
ק\3
לא שייך לבקשה
רח' ששון

תוכנית גג
קנ"מ: 1:100

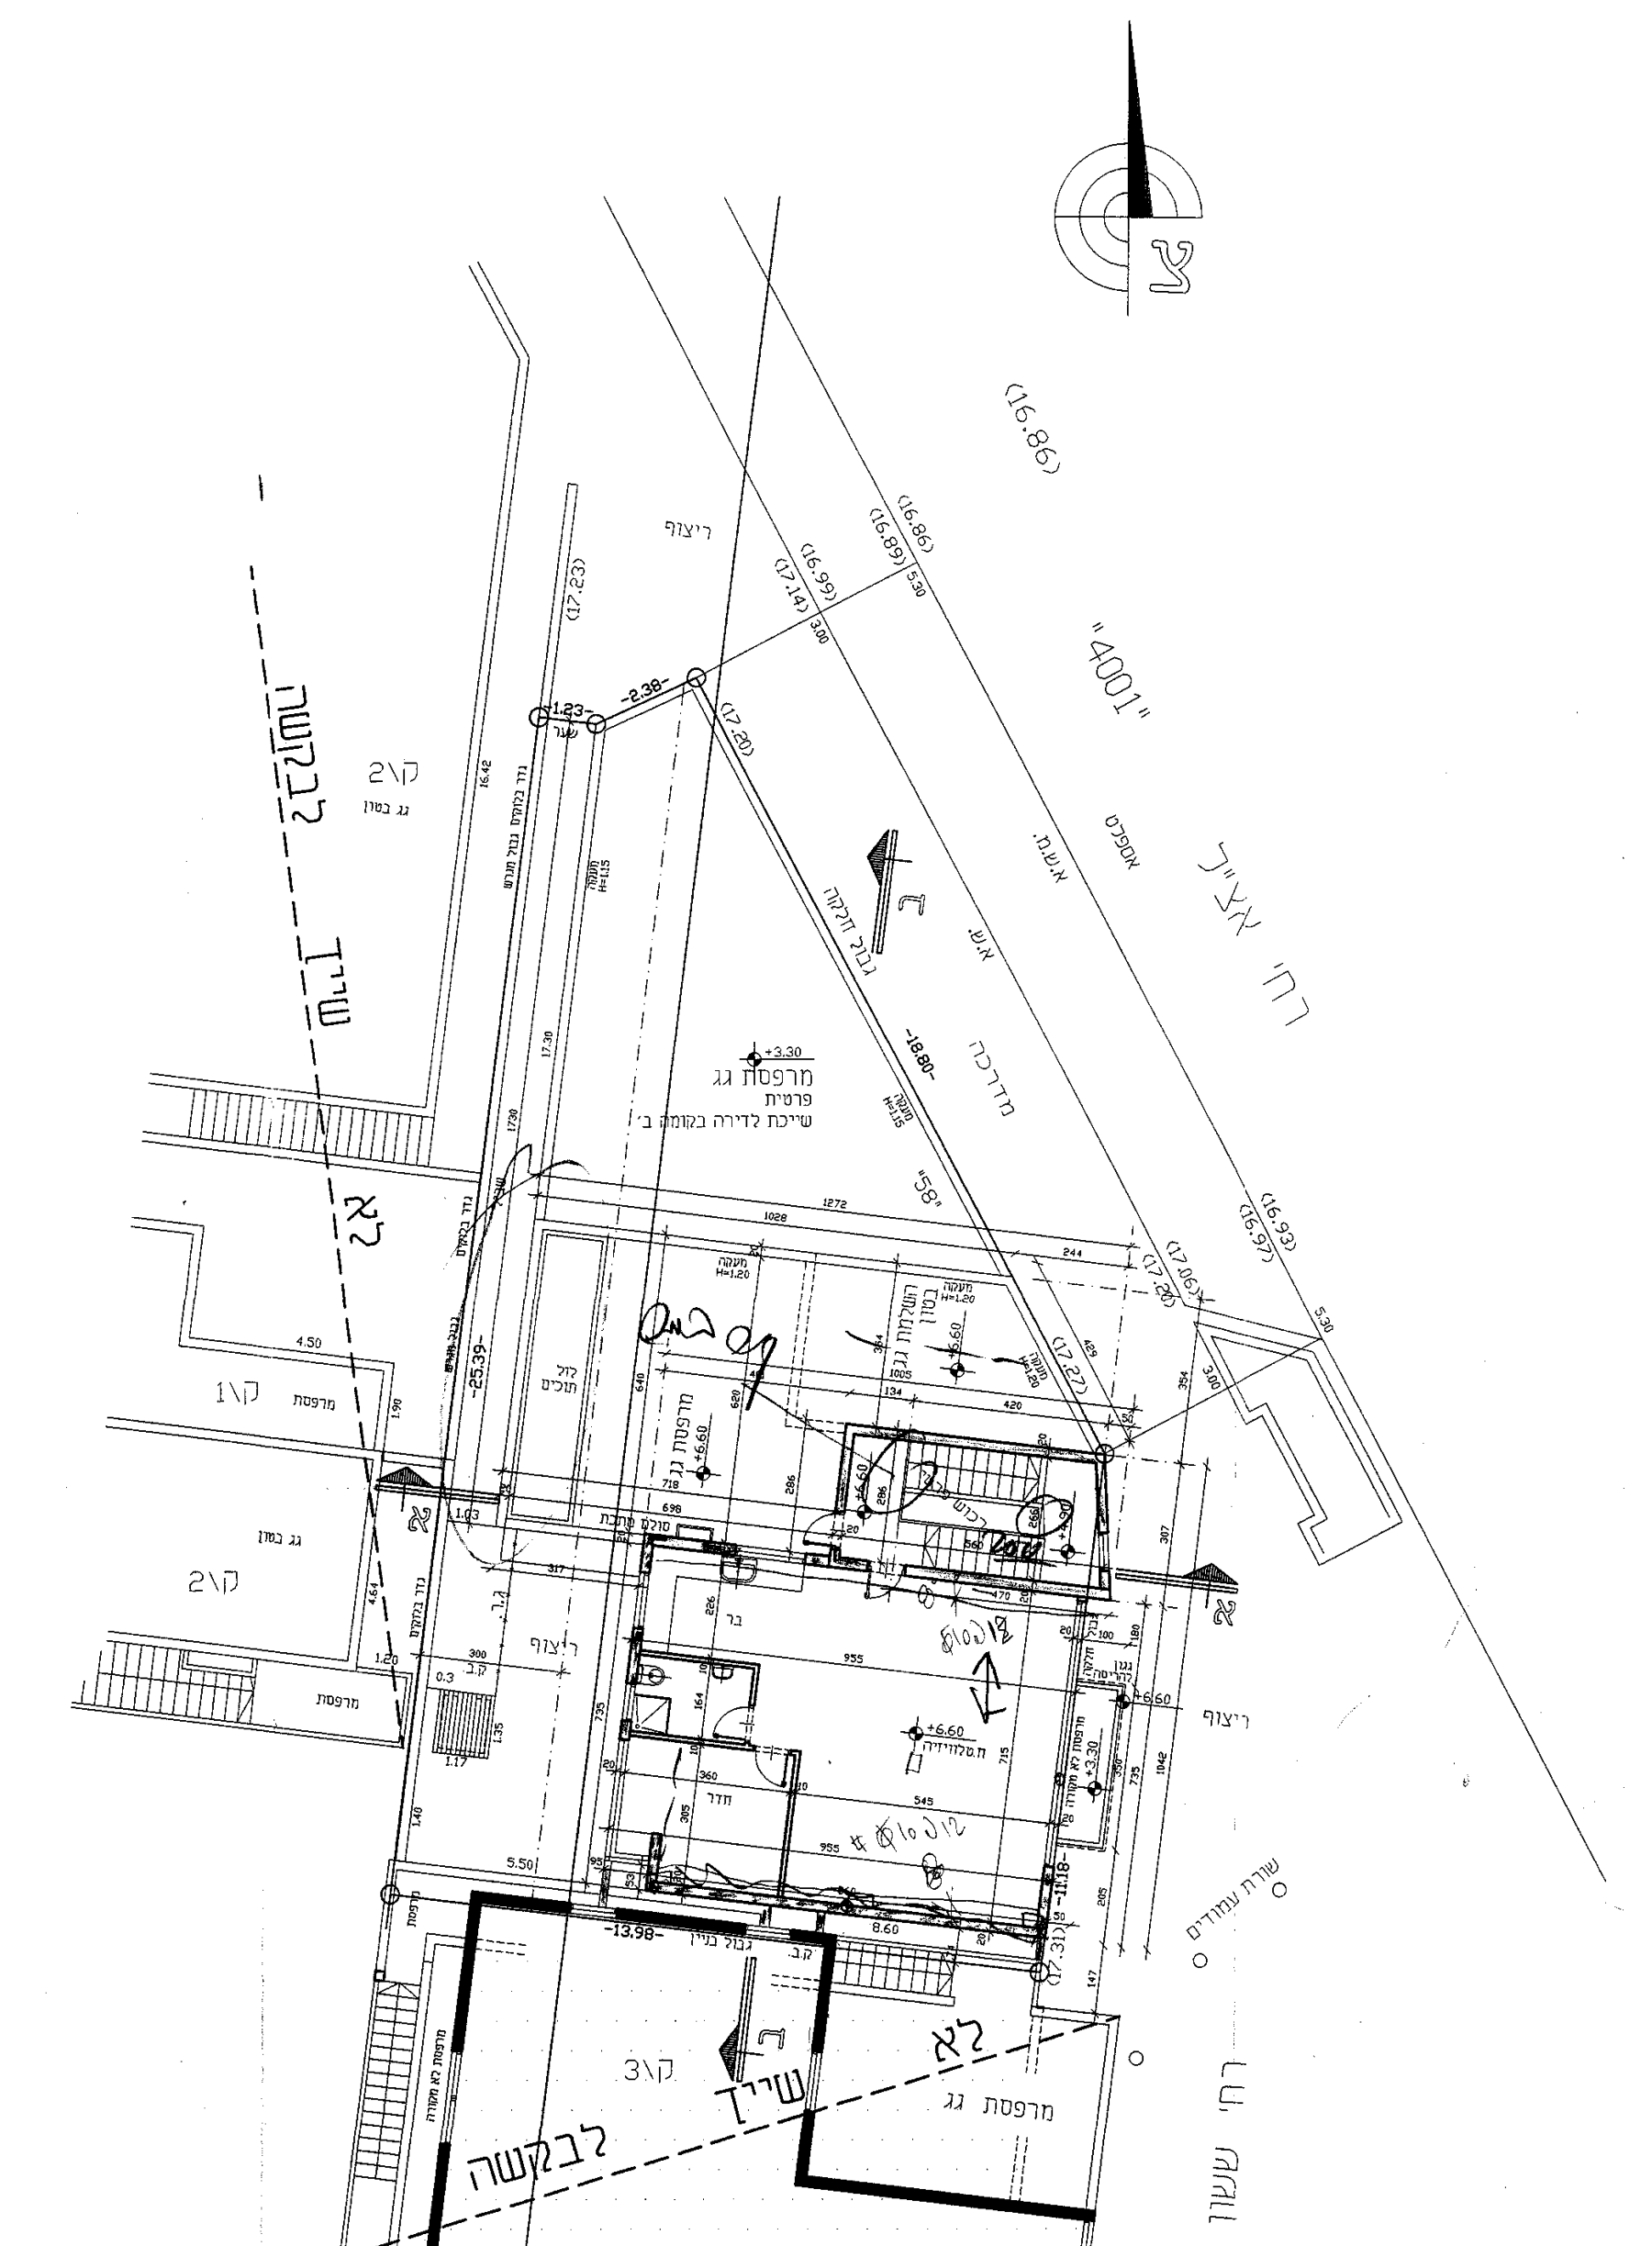
רח' אצ"ל
(16.86)
"4001"
לא שייך לבקשה
ק\1
ק\2
ק\3
רח' ששון

תוכנית קומה 'ב
קנ"מ: 1:100

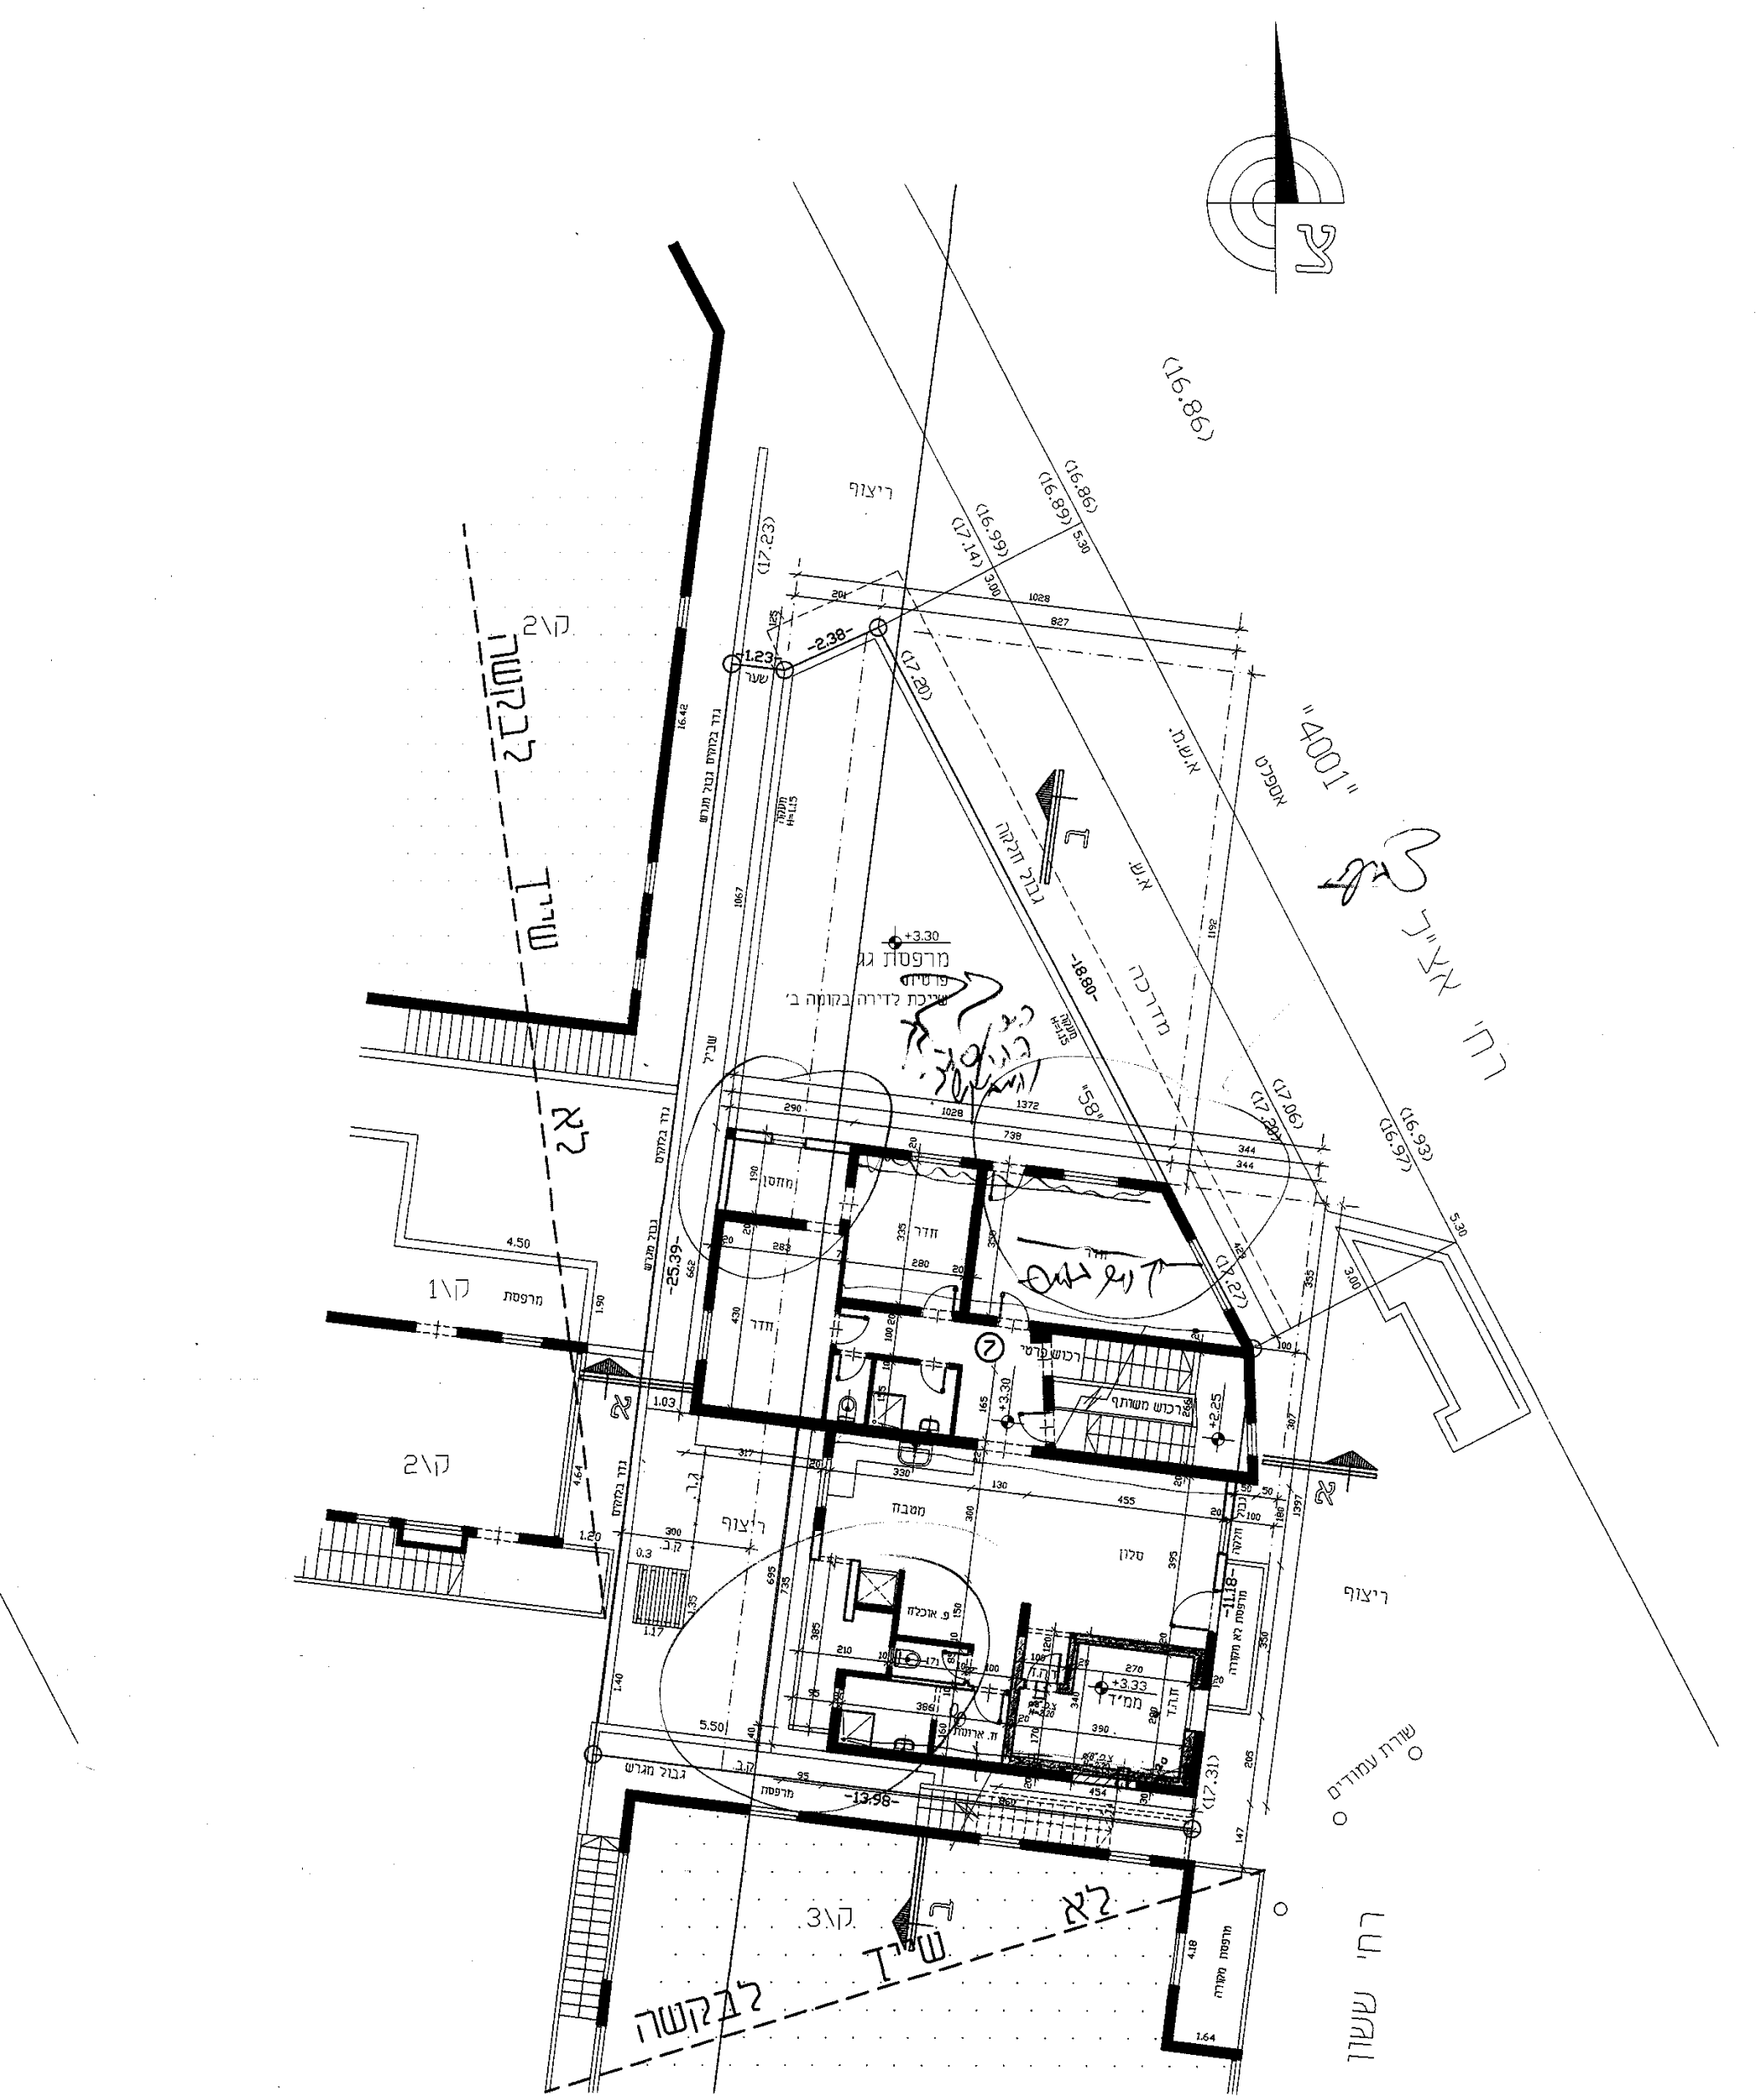
רח' אצ"ל
(16.86)
"4001"
לא שייך לבקשה
ק\1
ק\2
ק\3
רח' ששון

תוכנית קומה 'א
קנ"מ: 1:100

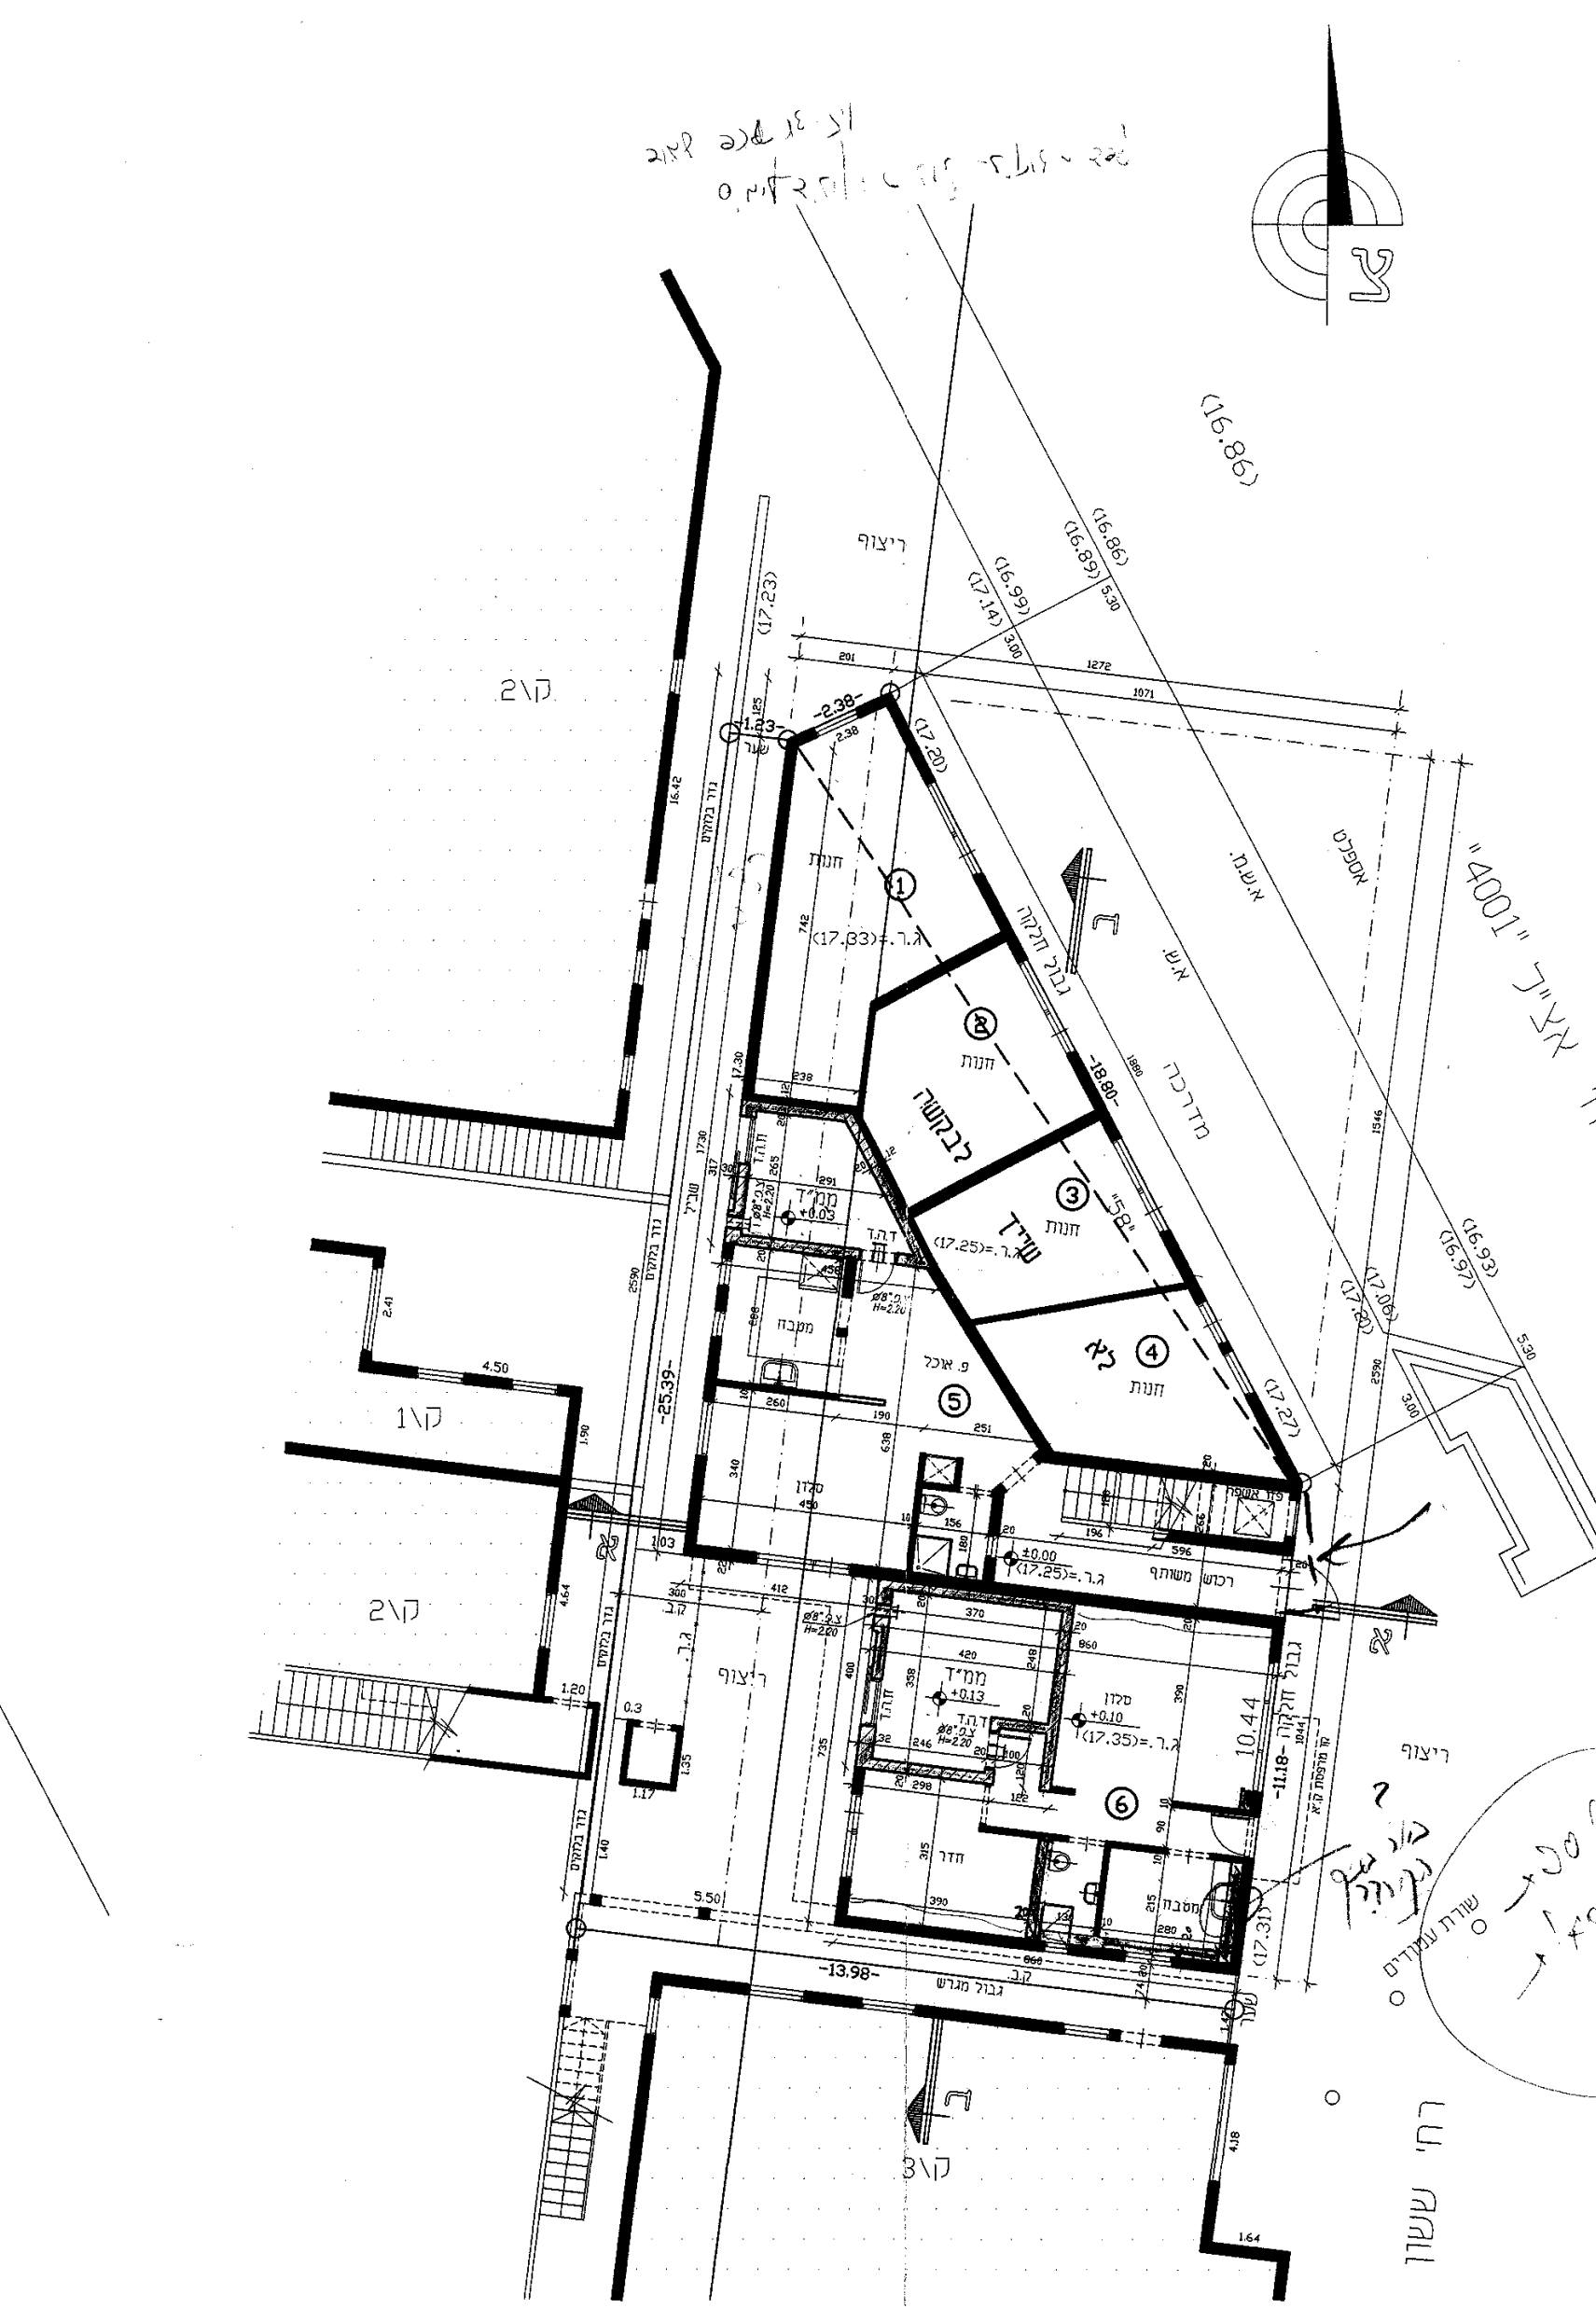
רח' אצ"ל
(16.86)
"4001"
לא שייך לבקשה
ק\1
ק\2
ק\3
רח' ששון

תוכנית קומת קרקע
קנ"מ: 1:100

חישוב שטחים

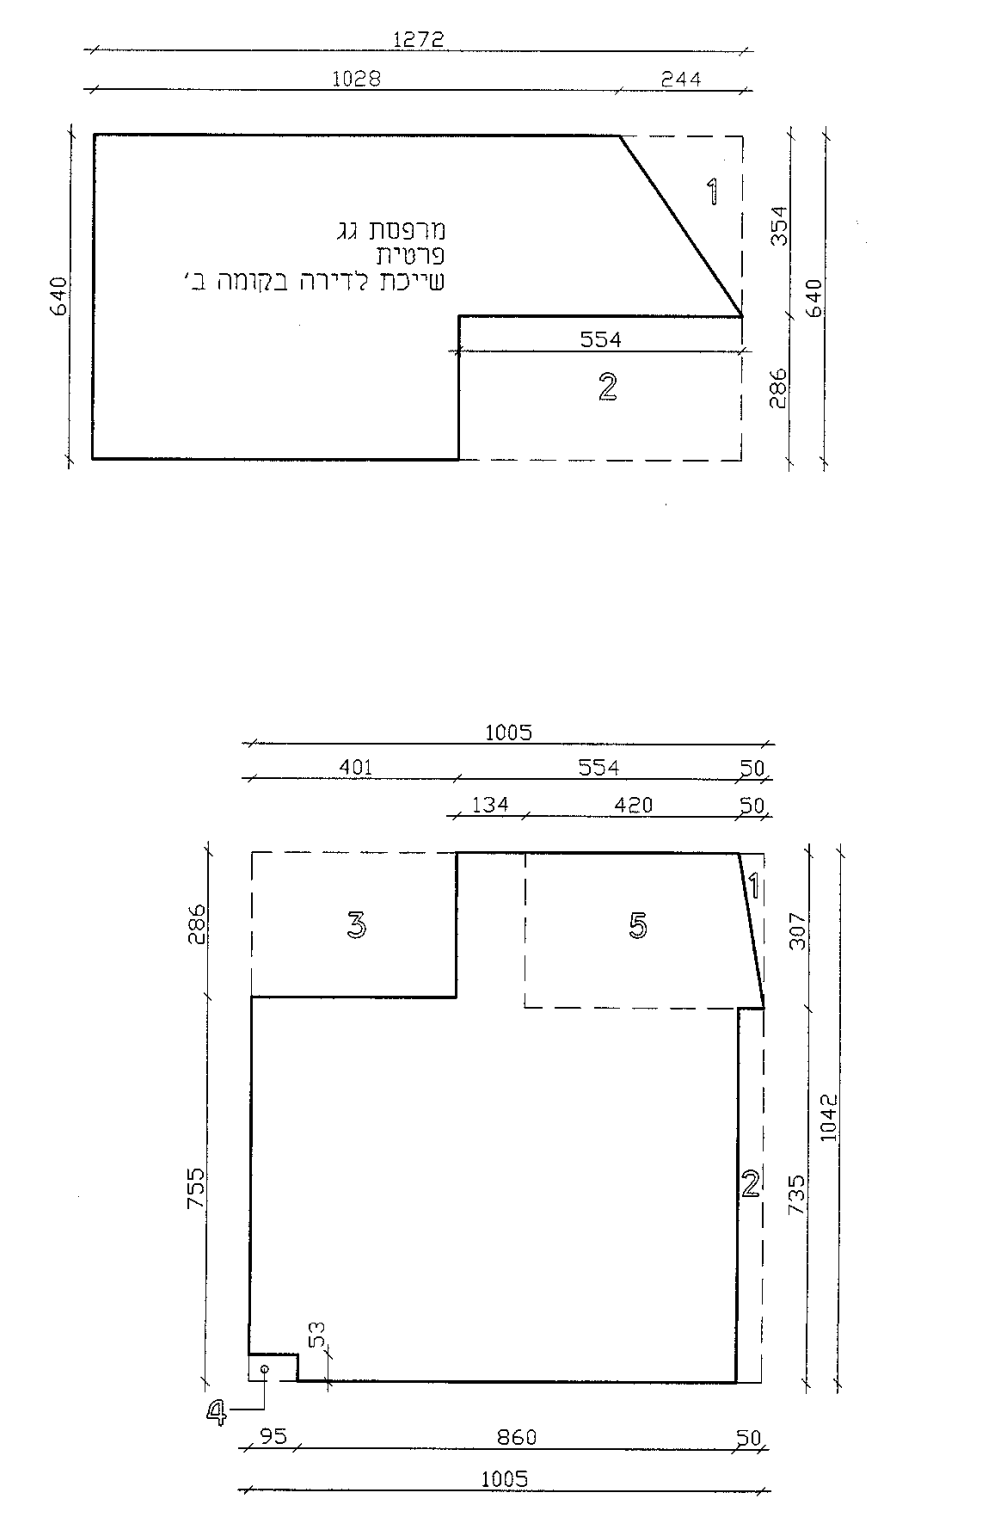
1272
1028
244
מרפסת גג
פרטית
שייכת לדירה בקומה ב'
1
2
554
1005
3
5
4
95
860
50

קומה 'ב

שטח מסגרת : 10.05 x 10.42 = 104.72

הורדות :
1) 0.5 x 3.07/2 = 0.77
2) 0.5 x 7.35 = 3.68
3) 2.86 x 4.01 = 11.47
4) 0.95 x 0.53 = 0.50
5) (4.20+4.70)/2X3.07 = 13.66 : חדר מדרגות

סה"כ הורדות : 30.08

סה"כ שטח עיקרי : 104.72 - 30.08 = 74.64

שטח מרפסת גג ק.'ב

שטח מסגרת : 12.72 x 6.62 = 84.21

הורדות :
1) 2.44 x 3.53/2 = 4.31
2) 5.54 x 2.87 = 15.90
3) 9.55 x 0.22 = 2.10

סה"כ שטח מרפסת : 61.90

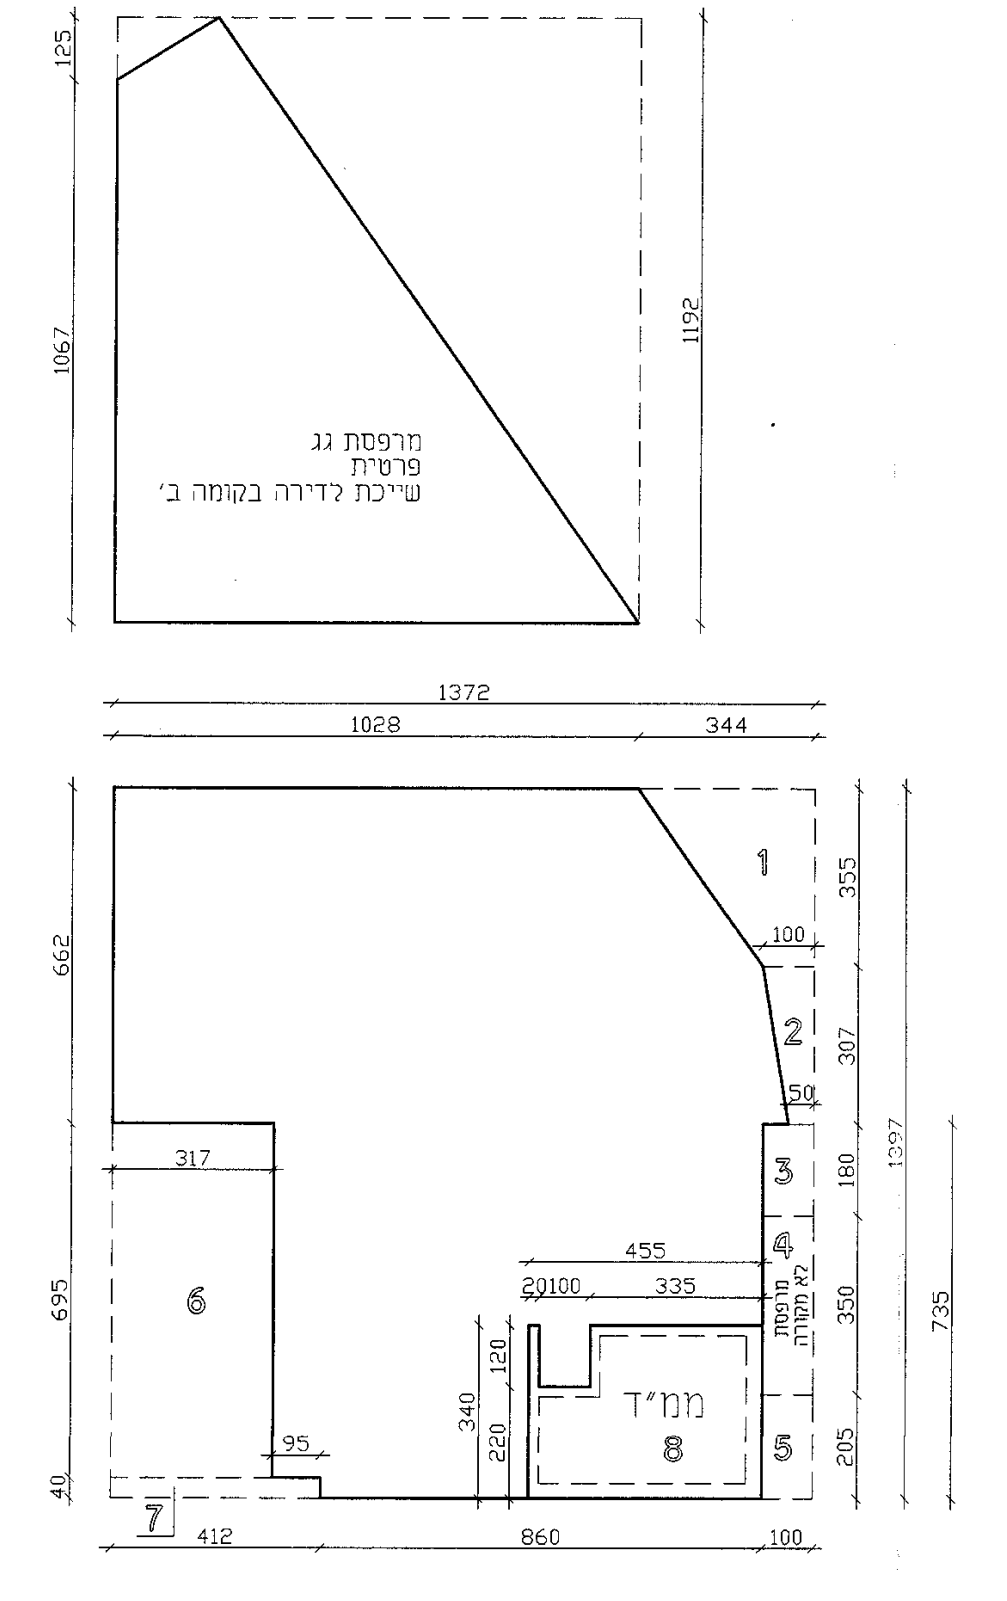
1028
201
827
מרפסת גג
פרטית
שייכת לדירה בקומה ב'
1272
344
1
3
6
ממ"ד
8
5
4
7
412
860
100

קומה 'א

שטח מסגרת : 13.72 x 13.97 = 191.67

הורדות :
1) (3.44+1.00)/2 x 3.55 = 7.88
2) (1.00+0.50)/2 x 3.07 = 2.30
3) 1.80 x 1.00 = 1.80
4) 3.50 x 1.00 = 3.50 : מרפסת לא מקורה
5) 2.05 x 1.00 = 2.05
6) 3.17 x 6.95 = 22.03
7) 0.4 x 4.12 = 1.65
8) 4.55X3.40-1.20X1.00 =14.27 : שטח ממ"ד
7.50 : סה"כ שטח להורדה

סה"כ הורדות : 48.71

סה"כ שטח עיקרי : 191.67 - 48.71 = 142.96

שטח קיים לפי היתר : 103.89
סה"כ שטח תוספת החדשה : 142.96 - 103.89 = 39.07

שטח מרפסת גג ק.'א

שטח מסגרת : 10.28 x 11.92 = 122.54

הורדות :
1) 8.27 x 11.92/2 = 49.29
2) 2.01 x 1.25/2 = 1.26

סה"כ שטח מרפסת : 71.99

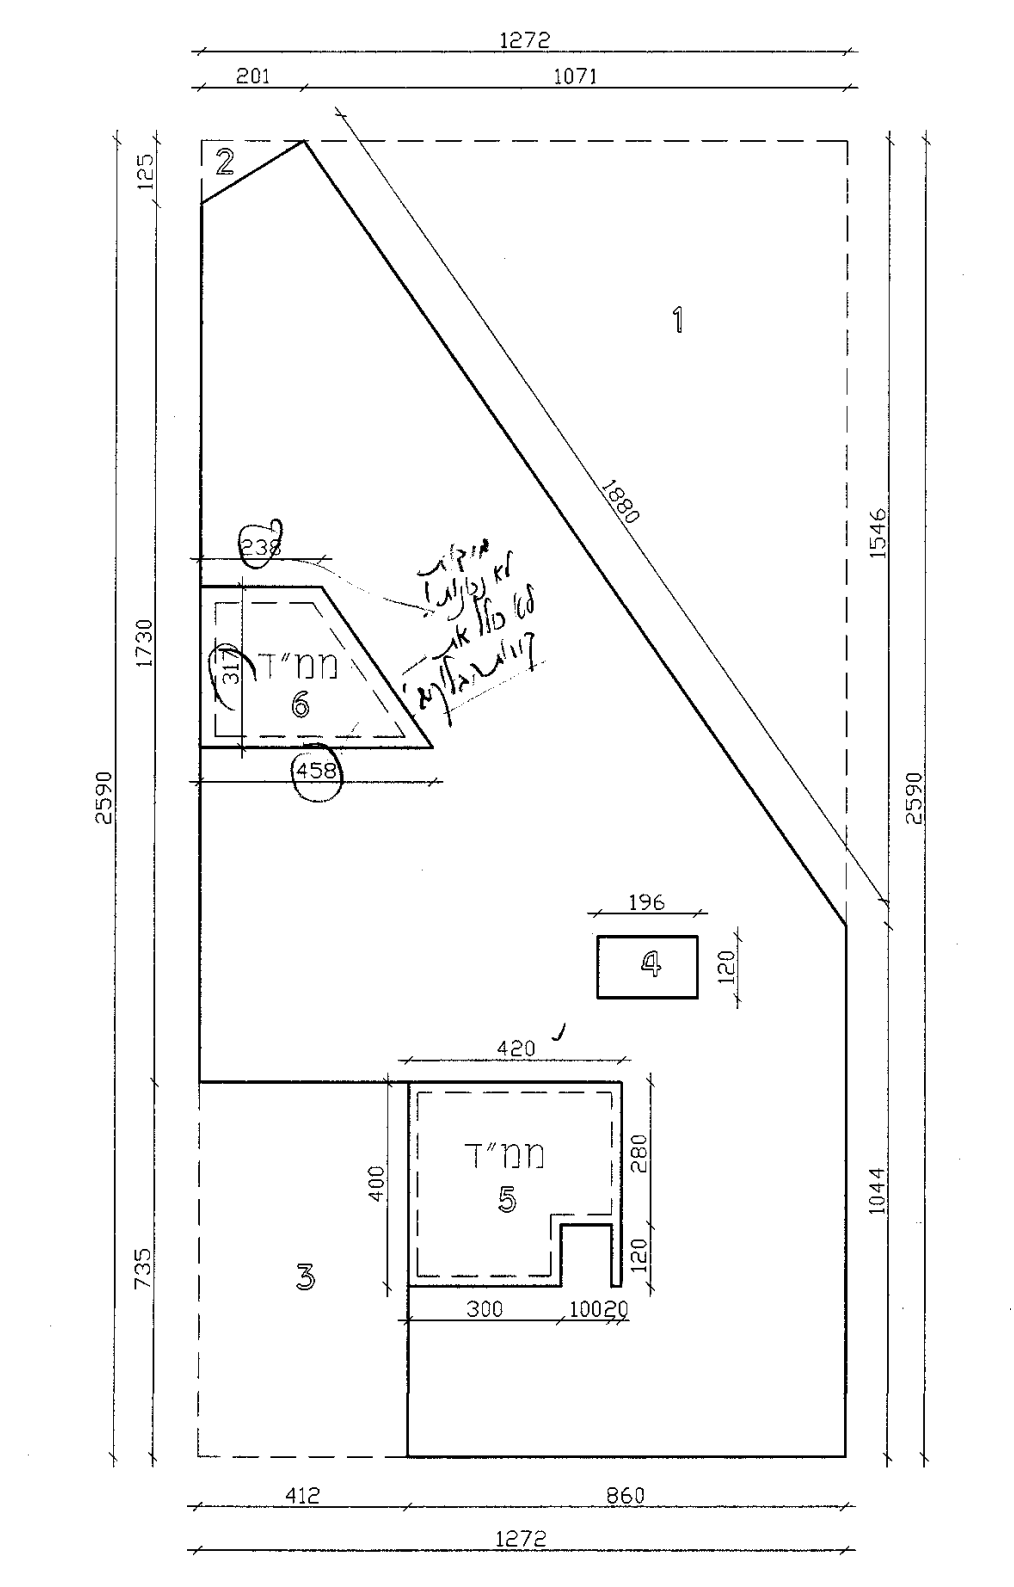
1272
1071
201
1
1880
2590
1546
196
4
ממ"ד
5
3
420
300
100
412
860
1044

ממ"ד
6
לא שייך
לשטח
עיקרי

קומת קרקע

שטח מסגרת : 12.72 x 25.90 = 329.49

הורדות :
1) 10.71 x 15.46 /2 = 82.79
2) 1.25 x 2.01 /2 =1.26
3) 7.35 x 4.12 = 30.28
4) 1.96 x 1.20 =- 2.35 : שטח מדרגות
מתחת לגובה (H=+1.20)
5) 4.00x4.20-1.00X1.20 = 15.60 : שטח ממ"ד
7.50 : סה"כ שטח להורדה
6) (2.38+4.58)/2 x 3.17 = 11.03 : שטח ממ"ד
7.50 : סה"כ שטח להורדה

סה"כ הורדות : 131.70

סה"כ שטח עיקרי : 329.49 - 131.70 = 197.79

לתקן עיקרי נטו!

תל-אביב
גוש : 6135
כתובת : רח' אצ"ל, 58 פינת רח' ששון, 2
הוכן עבור : משפ' יצחקי
מטרת המדידה : היתר בניה
חלקות : 45,44 (חלק)

מפה טופוגרפית
1 : 250

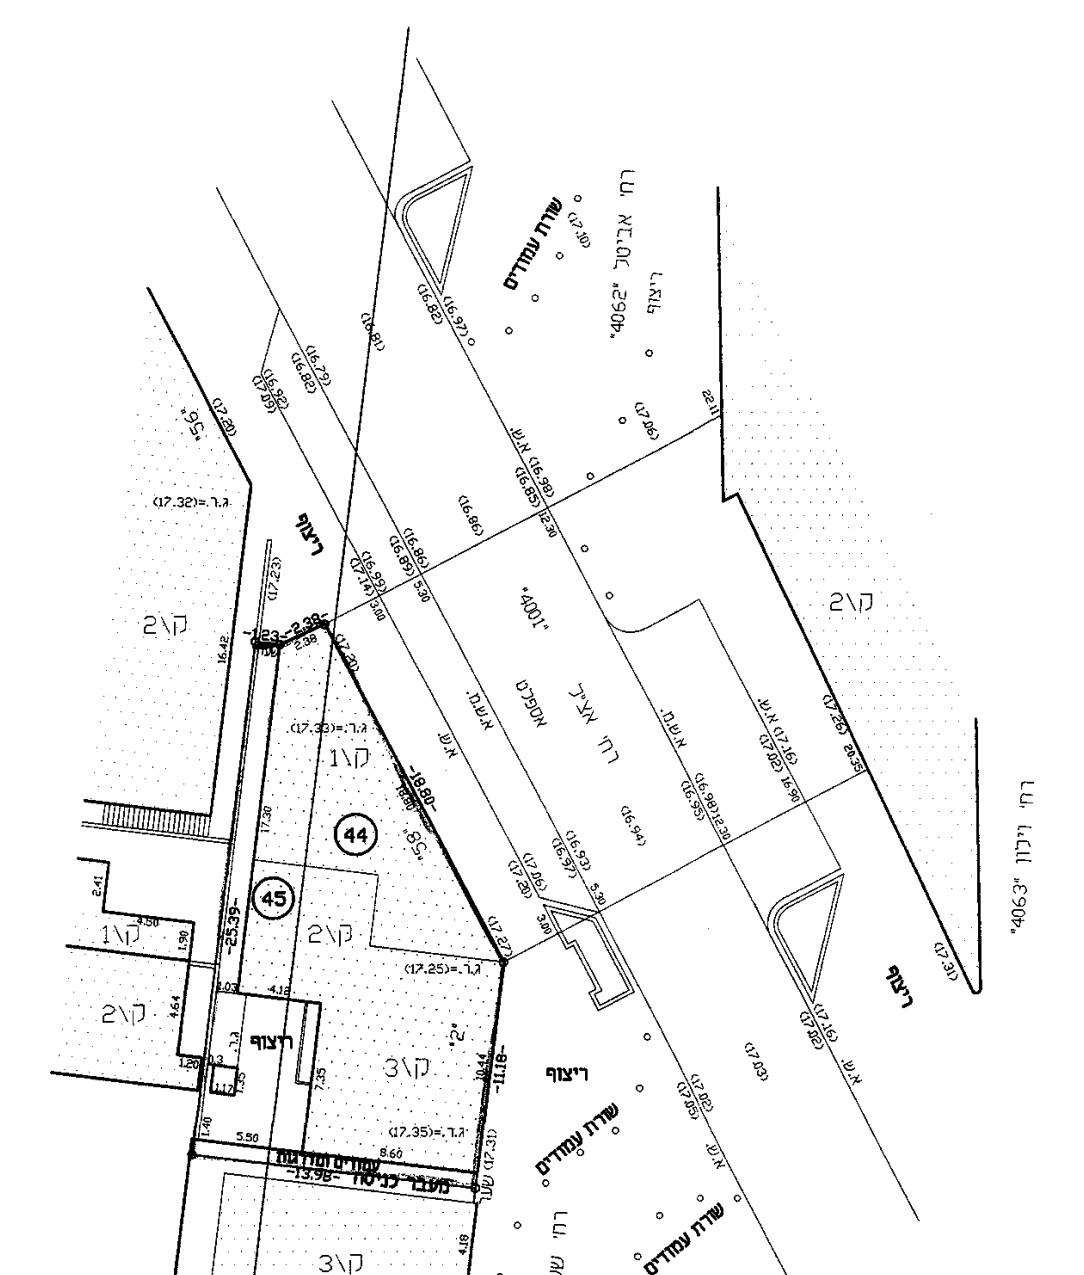
רח' אצ"ל
"4001"
רח' אריה"ט "4062"
שדרת עמודים
ריצוף
44
45
ק\1
ק\2
ק\3
רח' ששון
"4046"
רח' יונתן "4063"
אספלט

חלקה	שם הבעלים	מס' ת.ז.	שטח חלקה כולה	בעלות בחלקים	בעלות במ"ר
44	יצחקי שושנה	0481321\8	11.476.00	32\11476	32
	יצחקי זהבה	0481322\6		11\11476	11
	יצחקי נפתלי	0481318		108\11476	108
	בן אברהם יאיר	5119051		11\57380	2.2
	דייכובסקי אביגיל	478999		11\57380	2.2
	יצחקי חנה	04449625		11\57380	2.2
	בן אברהם יונתן	004790002		11\57380	2.2
	טסה נאוה	58907663		11\57380	2.2
	מדני מזל	0479542		9\11476	9
	אריאל רחל	0481317		9\11476	9
	ורון נעמי	0481319		11\11476	11
	ורון צפורה	0481320		9\11476	9
	מזרחי חרותה	0481323		11\11476	11
					211
45	בן אברהם מירים	0478998	9.821.00	5\9821	5
	מדני מזל	0479542		4\9821	4
	אריאל רחל	0481317		4\9821	4
	ירון נעמי	0481319		5\9821	5
	ירון ציפורה	0481320		4\9821	4
	יצחקי שושנה	0481321\8		18\9821	18
	יצחקי זהבה	0481322\6		5\9821	5
	מזרחי חרותה	0481323		5\9821	5
	יצחקי נפתלי	0481318		51\9821	51
					101
				סה"כ	312

בעלות במ"ר : 312
שטח מדוד (מ"ר) : 286.72 (188.50+98.22)
חלקה44 188.50מ"ר
חלקה45 98.22 מ"ר

שטח מגרש משני : ______
שטח להפקעה : ______

ריאתב הפמ וכדע 6.10.2005
ריאתב הפמ וכדע 5.01.2005

לא לצרכי רישום

הנני מצהיר בזה שהמפה נעשתה לפי
חוק התכנון והבניה, התקנות וההנחיות
של עיריית תל-אביב-יפו.

תל אביב
תאריך : 1.12.2003
י.אברבוך מודד מוסמך
רשיון מס' "461"
חב' אברבוך ושות' מודדים מוסמכים בע"מ
רח' דיזנגוף 190, תל-אביב טל5235891, 03-5226791

תרשים הסביבה 1:1250

רח' אצ"ל
"4001"
"4046"

הערות:
1. המספרים בסוגריים מציינים גבהים.
2. הגבהים מבוססים על נ.ק. עירונית מס' 188 שגובהה 17.530 מ'.

עיריית תל - אביב - יפו
מינהל ההנדסה, אגף רישוי ופיקוח על הבנייה
חוק התכנון והבניה, התשכ"ה-1965
בקשה להיתר בנייה או לשימוש במקרקעין

לכבוד ☒ הועדה המקומית לתכנון ולבנייה
☐ רשות הרישוי המקומית

~~725-0337~~
22 ר/06-0027
מס' תיק הבניין : 4001-058

א. פרטי הנכס והמבקשים
רחוב : אצ"ל | מס' בית : 58 | גוש : 6135 | חלקה : 44,45

	שם משפחה	שם פרטי	מס' זהות	כתובת	טלפון
מבקש 1	בן יהודה	נפתלי	02355164-1	רח' אצ"ל 58 תל-אביב	058631247
מבקש 2	יצחקי יצחקי	נפתלי ציונה	00481318-4 0046932-4	רח' אצ"ל 58 תל-אביב	03-6374166
בעל הזכות בנכס	יצחקי	נפתלי	00481318-4	רח' אצ"ל 58 תל-אביב	03-6374166
עורך הבקשה	בן מיכאל	דוד	313616799	רח' משה דיין 66 חולון	03-5530617
מתכנן שלד הבניין	בן מיכאל	דוד	313616799	רח' משה דיין 66 חולון	03-5530617

ב. מהות הבקשה
☒ בקשה לתוספת בנייה ☐ בקשה להרחבת דיור
תוספת 1 קומות לבניין
הכוללות 2 יחידות דיור
☒ תוספת בנייה בקומה א', ב' ☒ רחוב ☐ ראשור ☒ רצד
בשטח של 121.21 מ"ר
☒ שינויים פנימיים הכוללים : שינויים בקומת קרקע
והקומה 'א קומת גג + ביצוע ממ"דים
☒ אישור מצב קיים
קיים בניין בן-2 קומות + בניה על הגג
השימוש המבוקש : מגורים

ג. מפרט - תיאור הבקשה
קיים בניין בן-2 קומות + בניה על הגג
סה"כ 7 יח' דיור
☒ מגורים
☒ תוספת לבניין
שטח המגרש : 286.72 מ"ר
439.03 מ"ר
153.13 %

יב. מינויים מטעם מבקש ההיתר
דוד בן מיכאל 313616799
ביצוע: אחראי ראשי

לבקשה
22.6.06
אבנית לבקשה
ב-2.11.06

עיריית תל-אביב יפו
רשות הרישוי
30-10-2006
התקבל

מחלקת מקלטים
אישור רשות מוסמכת
עיריית תל-אביב-יפו
רשות מוסמכת
התכנית נבדקה והתאמה
לדרישות התקנות
לבנית מקלטים 1997
18.06.06
אישור מס' 5-59/06
האישור בתוקף עד תאריך 18.06.07

מפקדת ראש הג"א - ענף הנדסה ומיגון
את הבטון, פלדת הזיון, החסימה נגד מים ורטיבות
הגנת הקירות, המסגרות, המתקנים התברואתיים
והחשמליים, הניקוז, הציפוי והצביעה של הקירות
והסימונים יש לבצע לפי דרישות תקנות התגוננות
האזרחית למקלטים 5289/90 ולמרחבים מוגנים
5606/95. הקבלן חייב להחזיק תכנית מאושרת של
המקלט (מרחב מוגן) באתר הבניה עד לסיום הקמתו.

נבדק

חלון בלי כיס
זיון סביב פתח בקיר

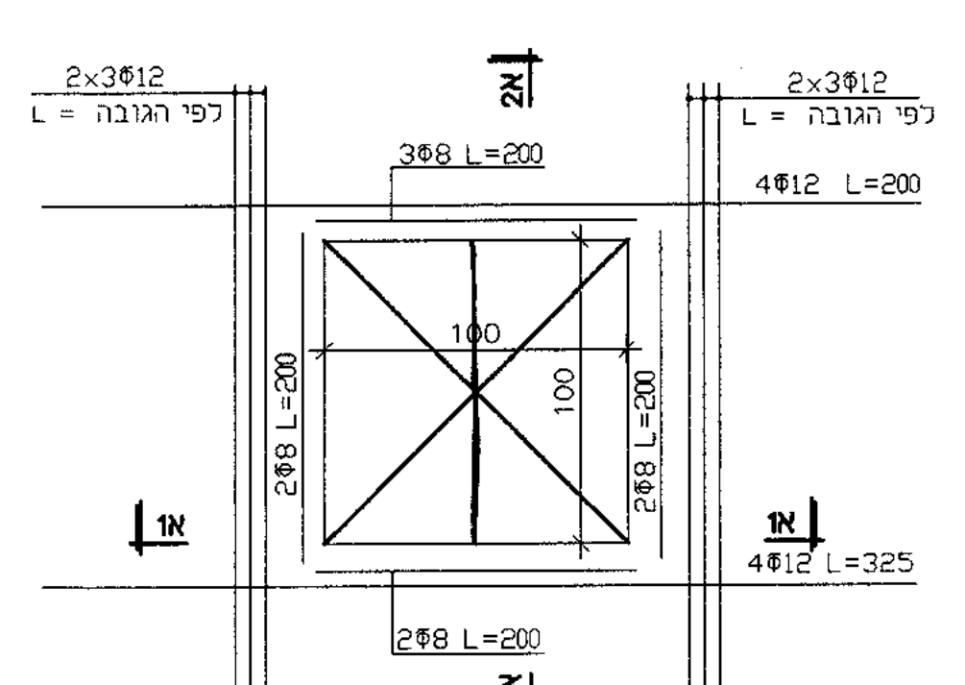
2x3Φ12
L = לפי הגובה
3Φ8 L=200
4Φ12 L=200
100
2Φ8 L=200
4Φ12 L=325
2Φ8 L=200
א1
א2

① חתך אופקי בקיר מרחב מוגן

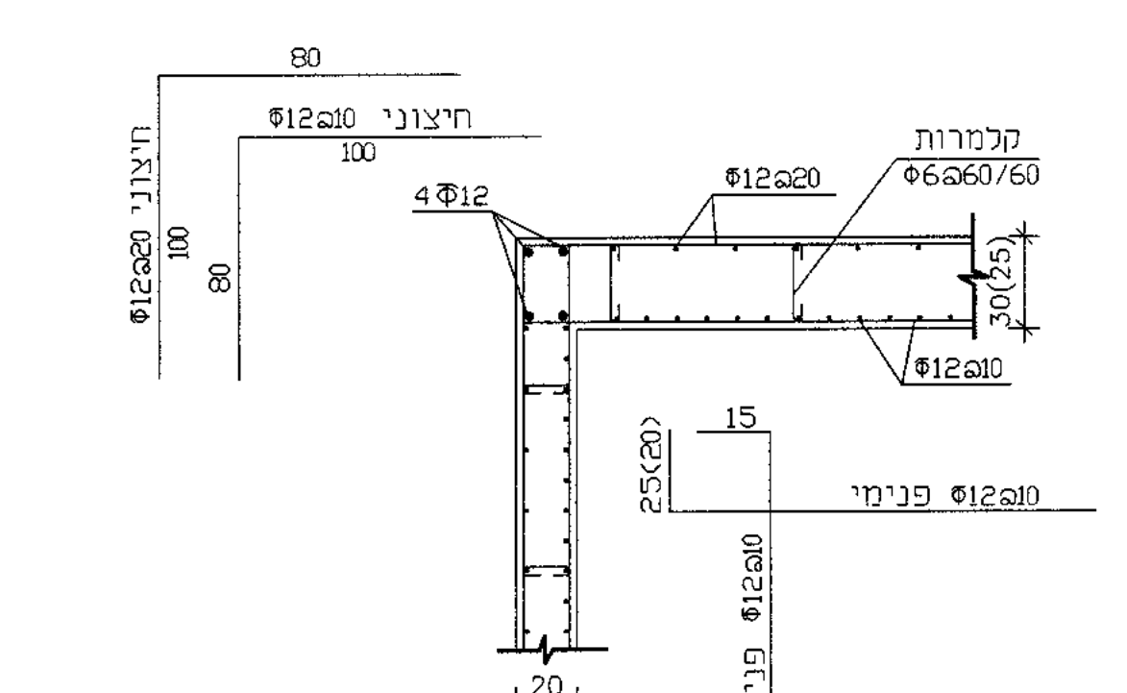
80
Φ12a10 חיצוני
Φ12a20 חיצוני
4Φ12
Φ12a20
קלמרות Φ6a60/60
30(25)
Φ12a10
15
25(20)
Φ12a10 פנימי
20

חלון עם כיס
זיון סביב פתח בקיר

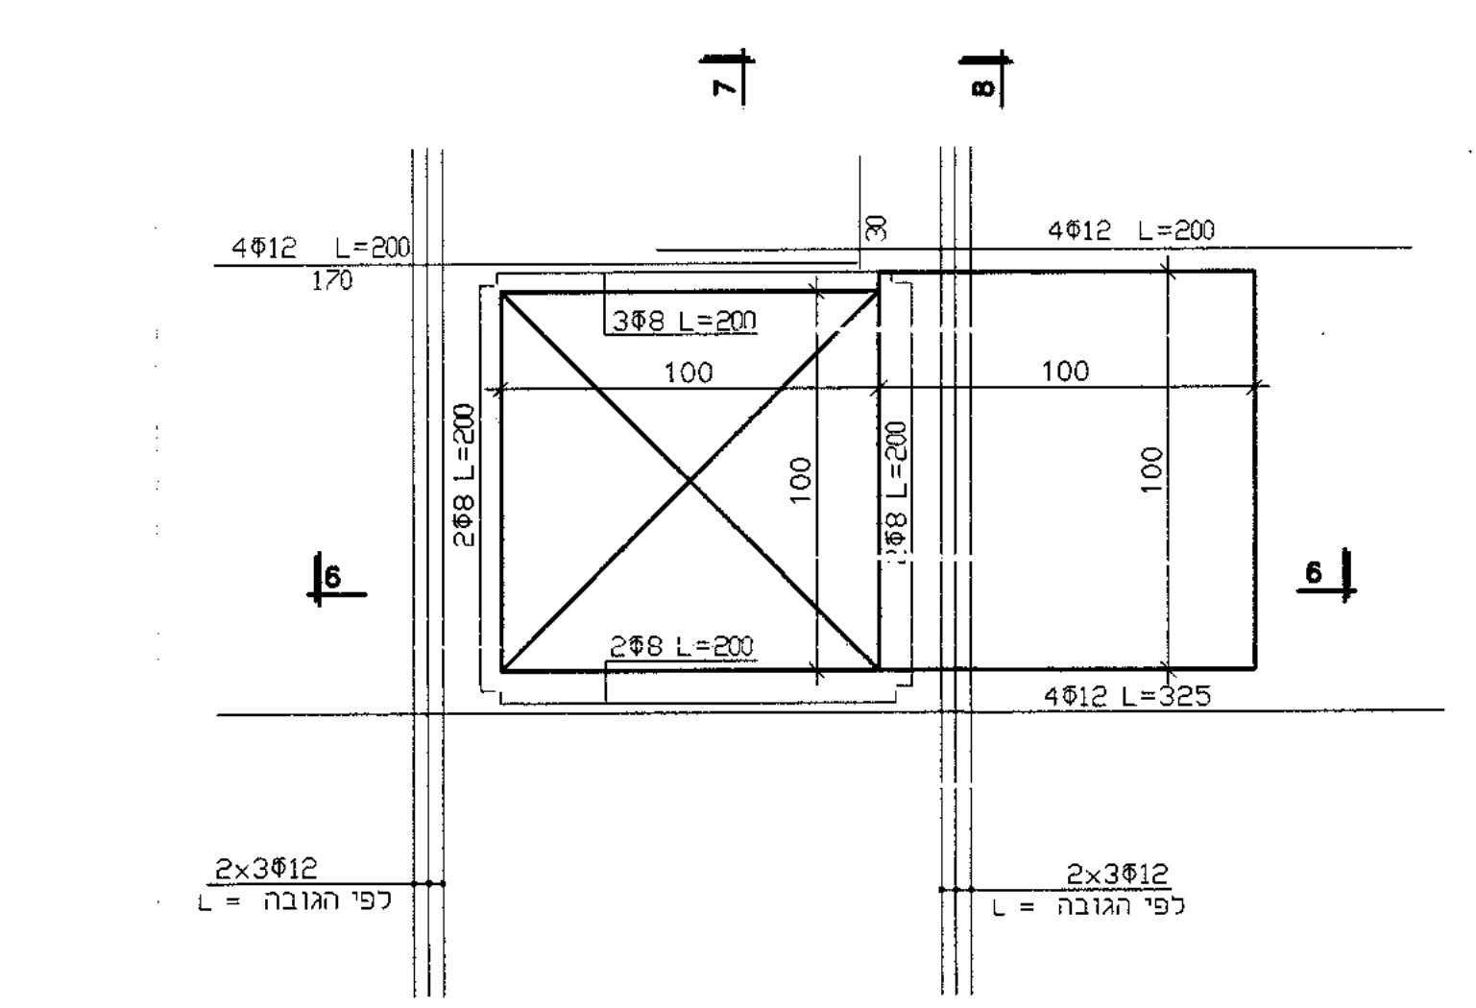
4Φ12 L=200
170
3Φ8 L=200
4Φ12 L=200
100
100
2Φ8 L=200
4Φ12 L=325
2x3Φ12
L = לפי הגובה
6
7
8

דלת
זיון סביב פתח בקיר

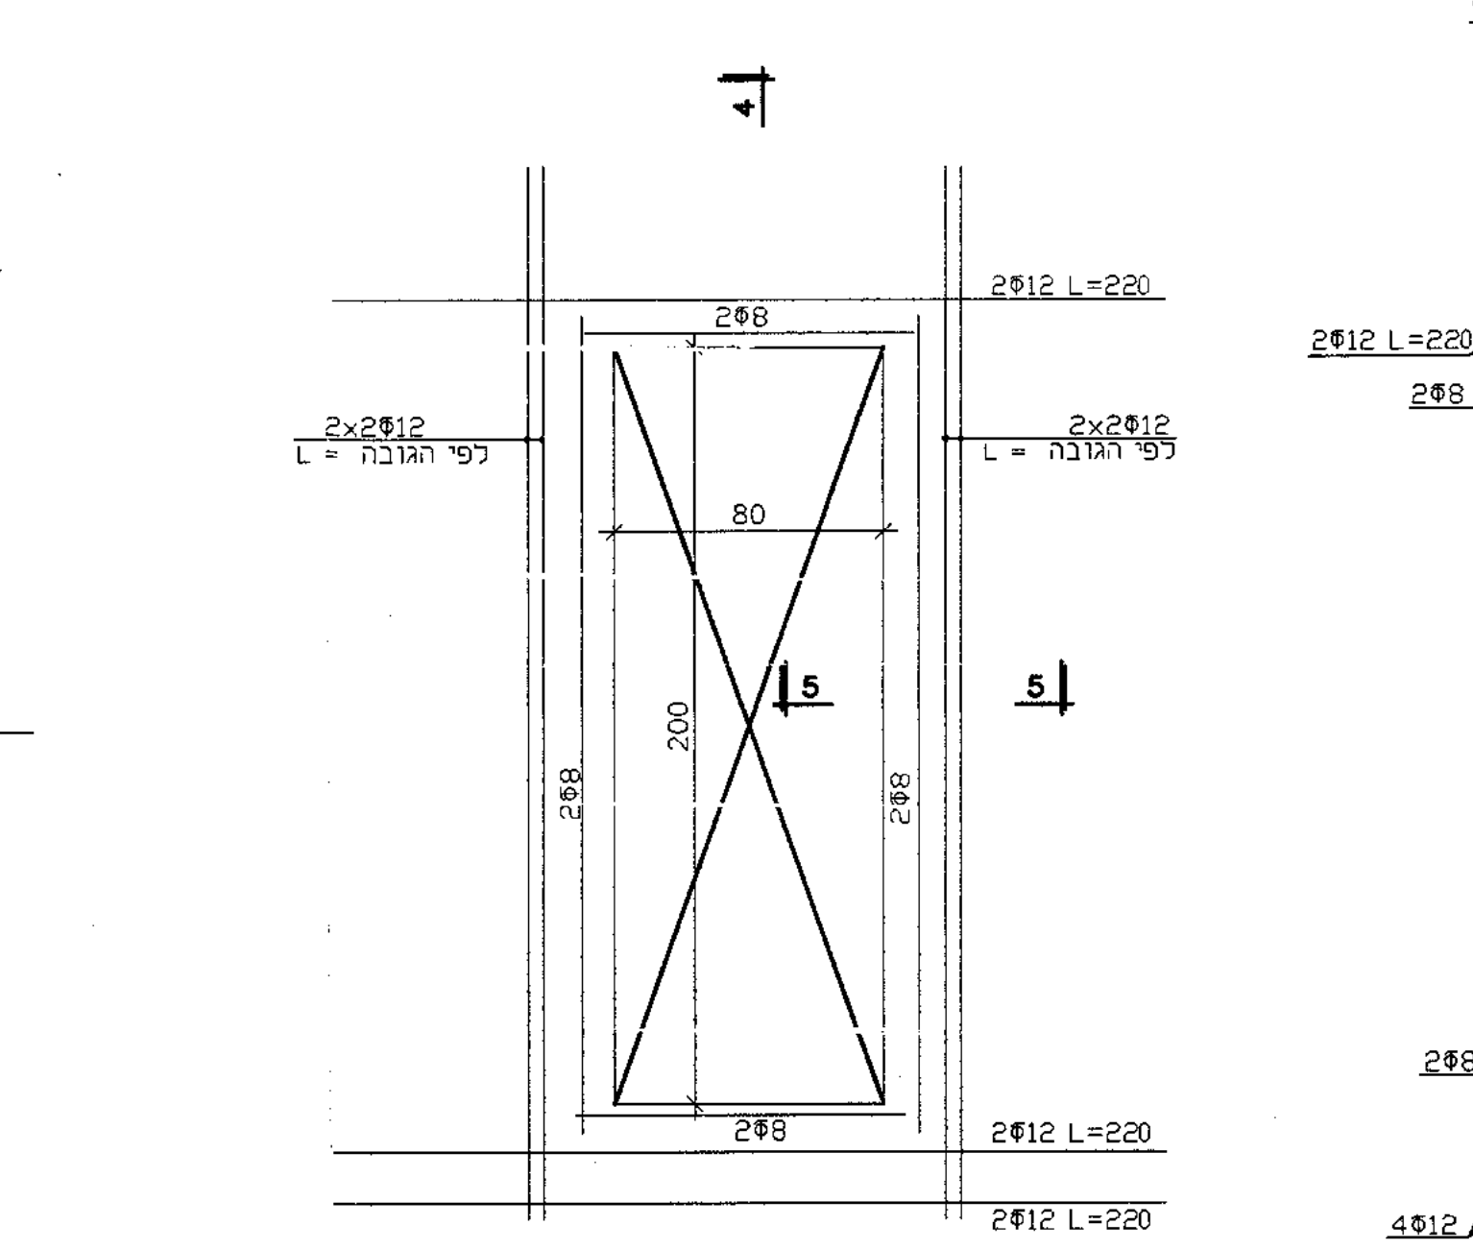
2Φ12 L=220
2Φ8
2x2Φ12
L = לפי הגובה
80
200
2Φ8
4
5

חתך 4-4

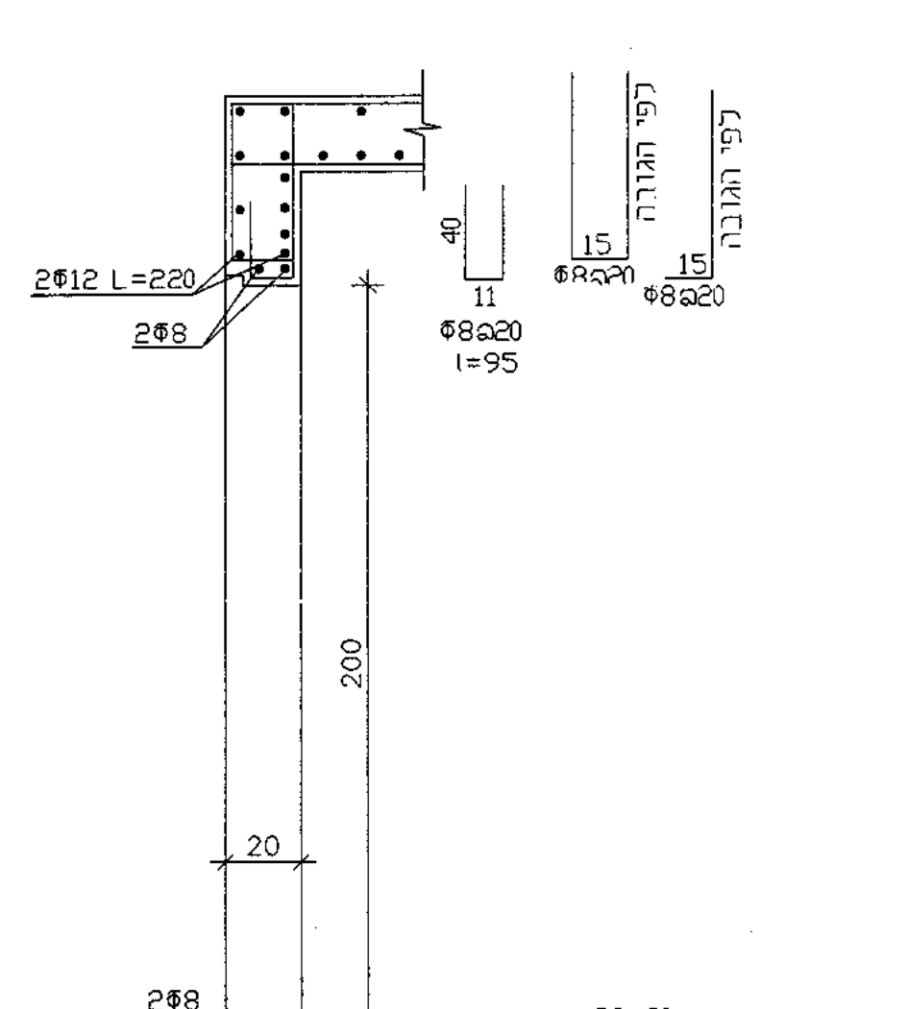
2Φ12 L=220
2Φ8
Φ8a20 l=95
לפי הגובה
200
20
4Φ12
Φ8a20 L=90
Φ8a20 l=90

חתך א1-א1

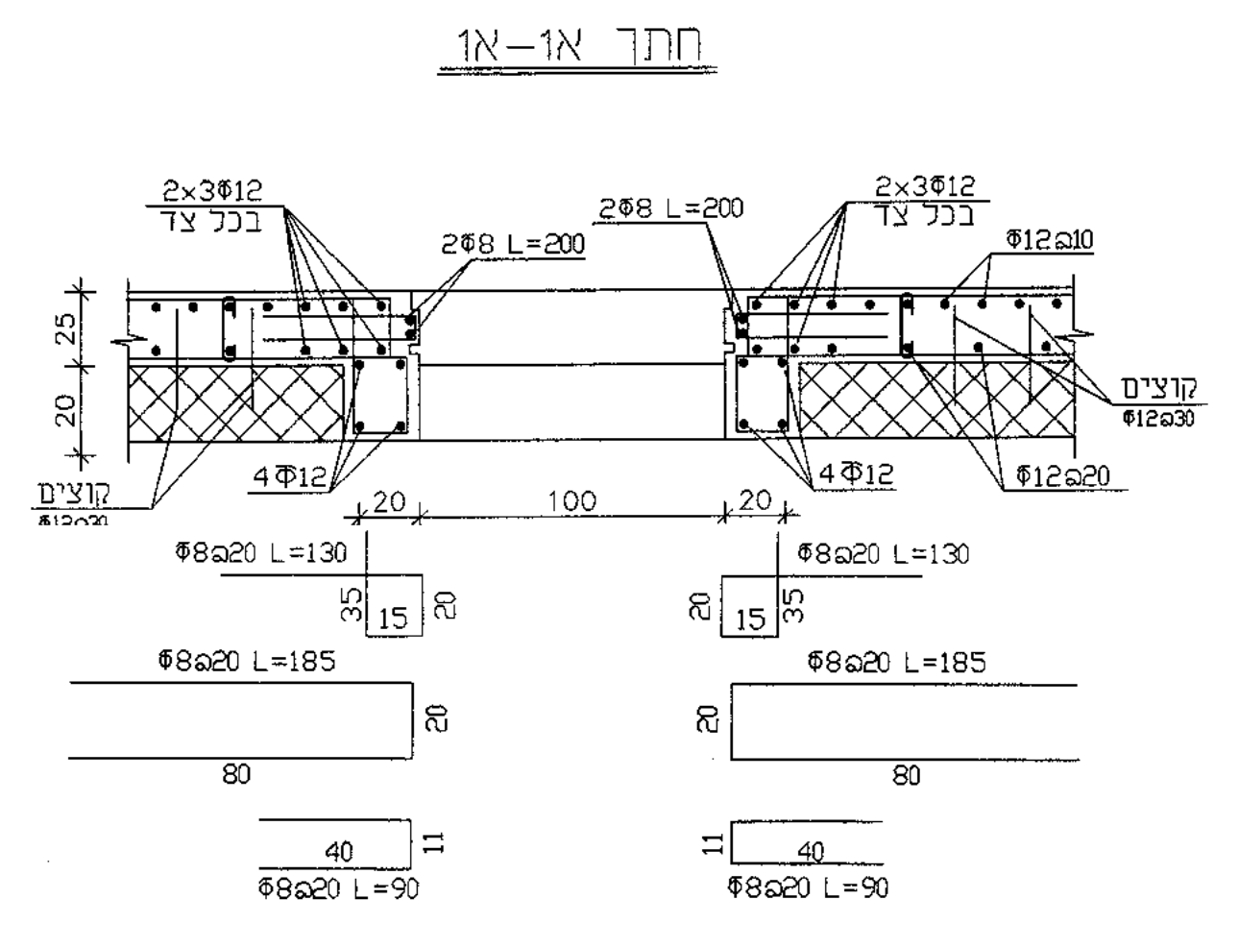
2x3Φ12 בכל צד
2Φ8 L=200
Φ12a10
קוצים Φ12a30
4Φ12
Φ12a20
Φ8a20 L=130
Φ8a20 L=185
Φ8a20 L=90
100
80
40

② פרט ריתום אנכי בין רצפה לקירות

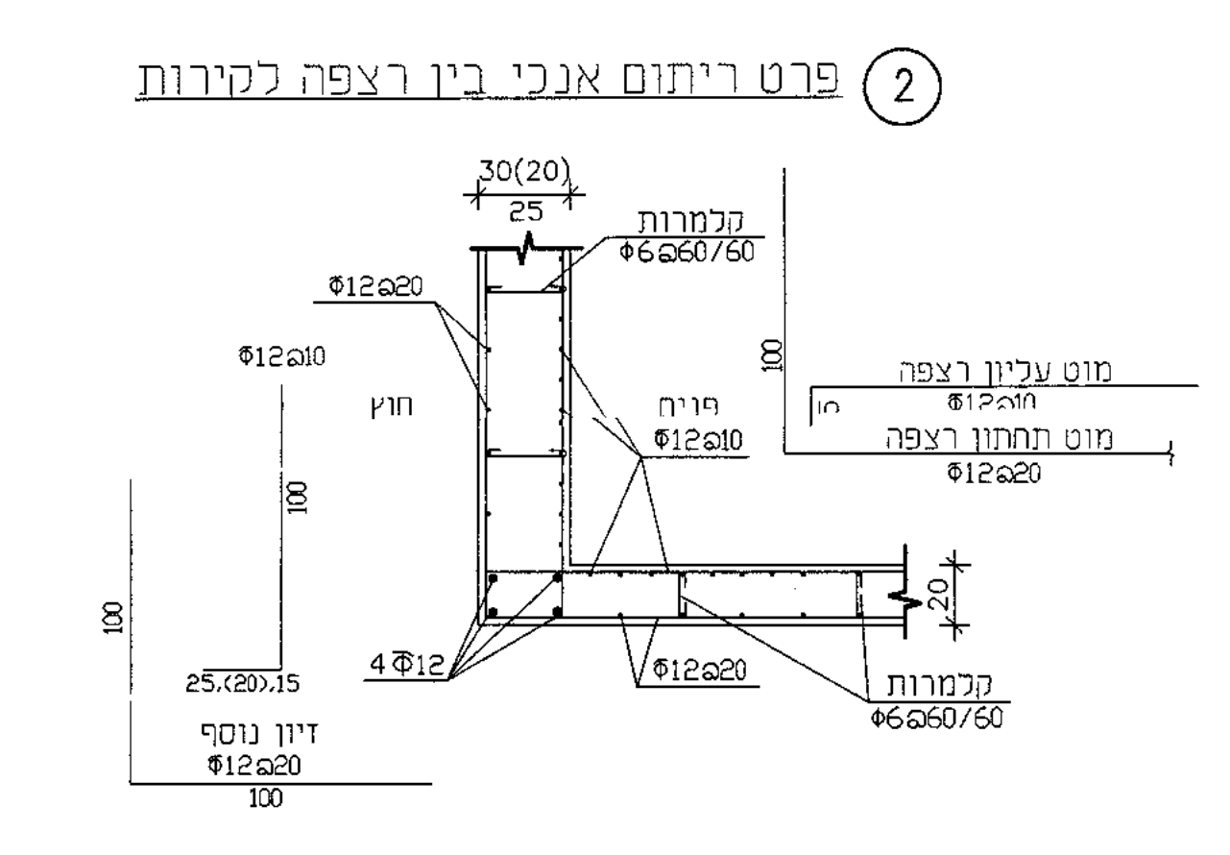
30(20)
25
קלמרות Φ6a60/60
Φ12a20
Φ12a10
חוץ
פנים
Φ12a10
מוט עליון רצפה Φ12a10
מוט תחתון רצפה Φ12a20
4Φ12
Φ12a20
קלמרות Φ6a60/60
זיון נוסף Φ12a20
25(20)15
100

חתך 6-6

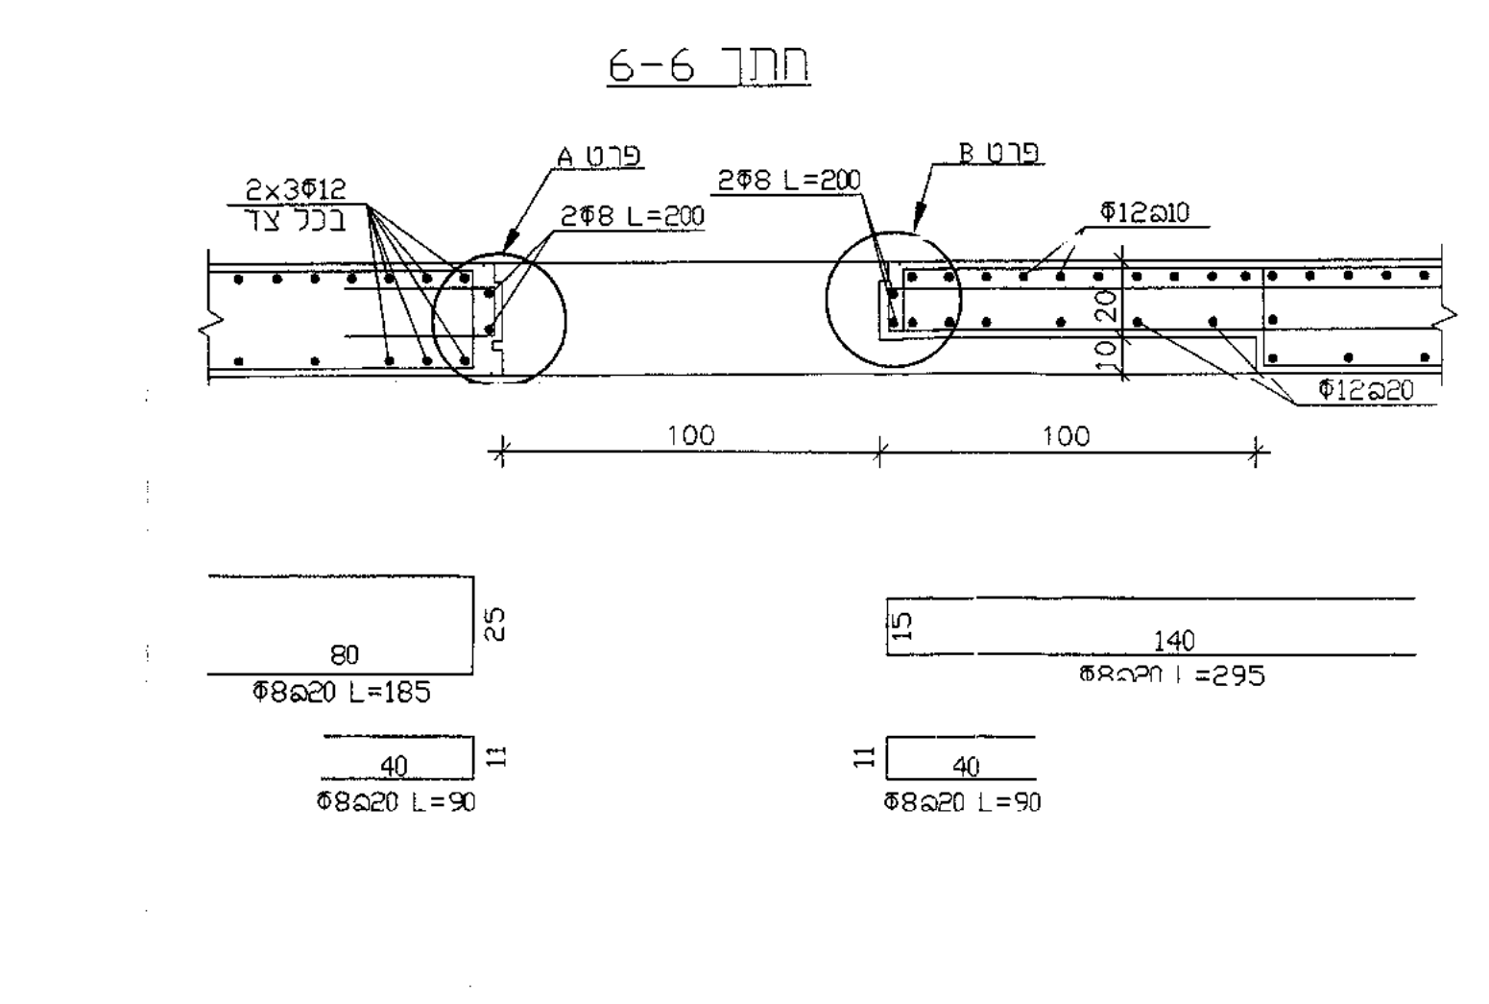
2x3Φ12 בכל צד
פרט A
2Φ8 L=200
פרט B
Φ12a10
Φ12a20
100
100
Φ8a20 L=185
Φ8a20 L=295
Φ8a20 L=90

חתך 5-5

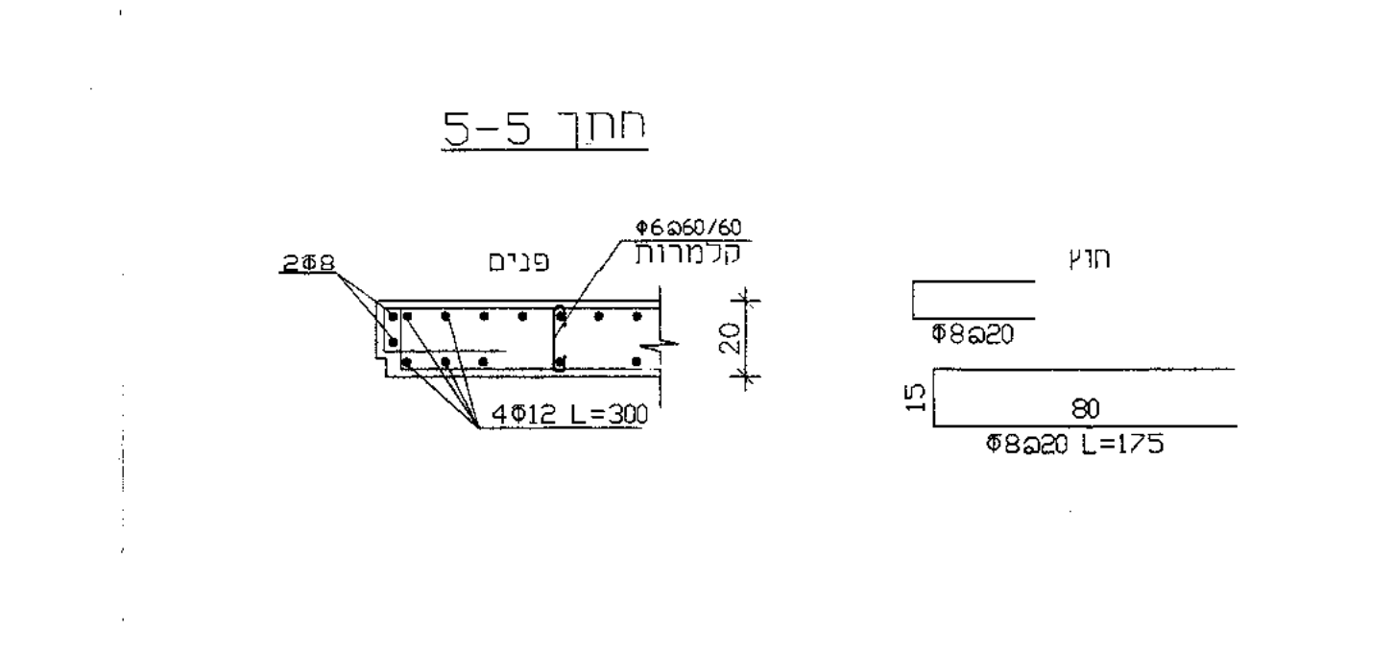
2Φ8
פנים
קלמרות Φ6a60/60
4Φ12 L=300
חוץ
Φ8a20
Φ8a20 L=175

חתך א2-א2

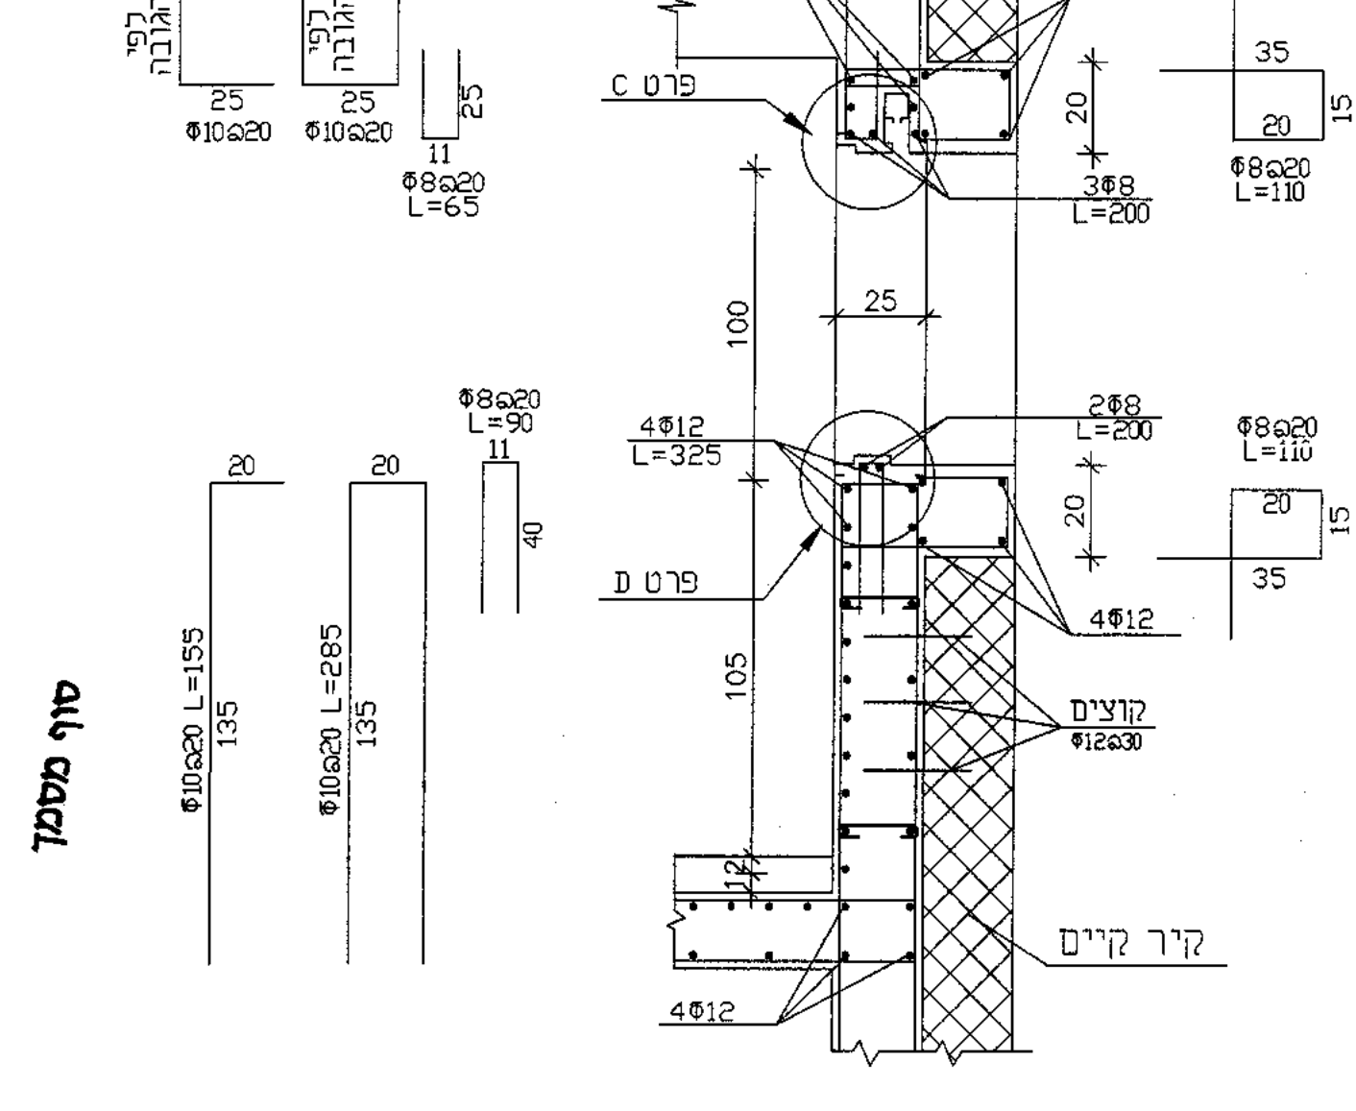
4Φ12 L=200
פרט C
3Φ8 L=200
Φ8a20 L=110
4Φ12 L=325
פרט D
2Φ8 L=200
קוצים Φ12a30
קיר קיים
4Φ12
Φ10a20 L=155
Φ10a20 L=285
Φ8a20 L=65
Φ8a20 L=90

סוף מסמך

③ פרט ריתום אנכי בין קיר לגג

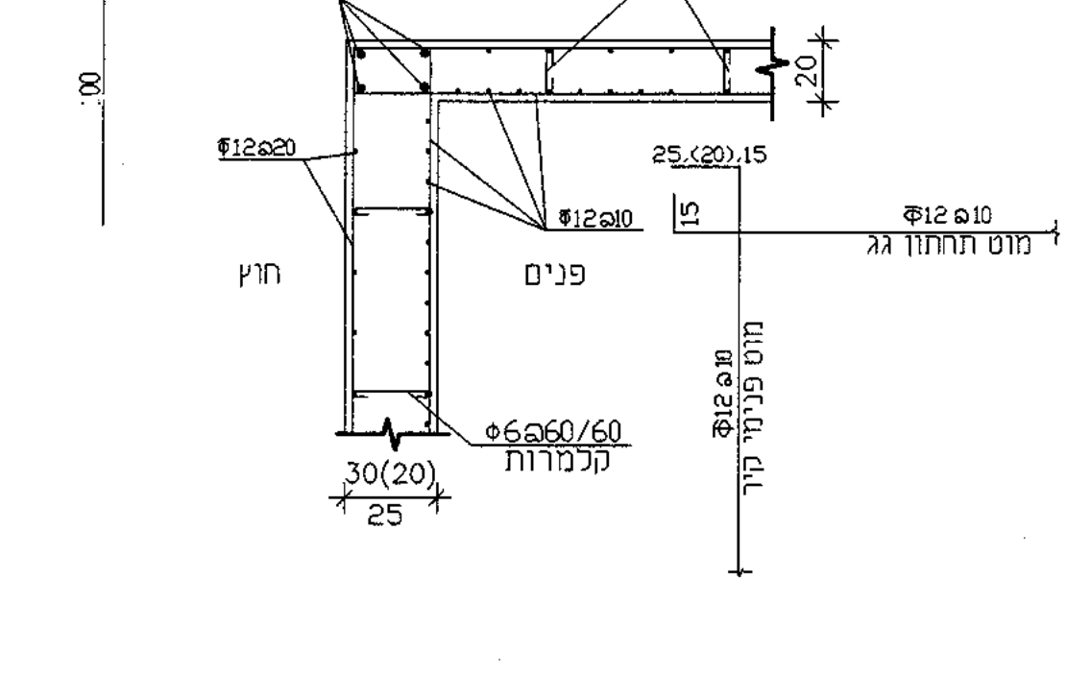
זיון נוסף Φ12a10
4Φ12
Φ6a60/60 קלמרות
Φ12a20
Φ12a10
חוץ
פנים
מוט תחתון גג Φ12a10
מוט פנימי קיר Φ12a10
30(20)
25

חתך 8-8

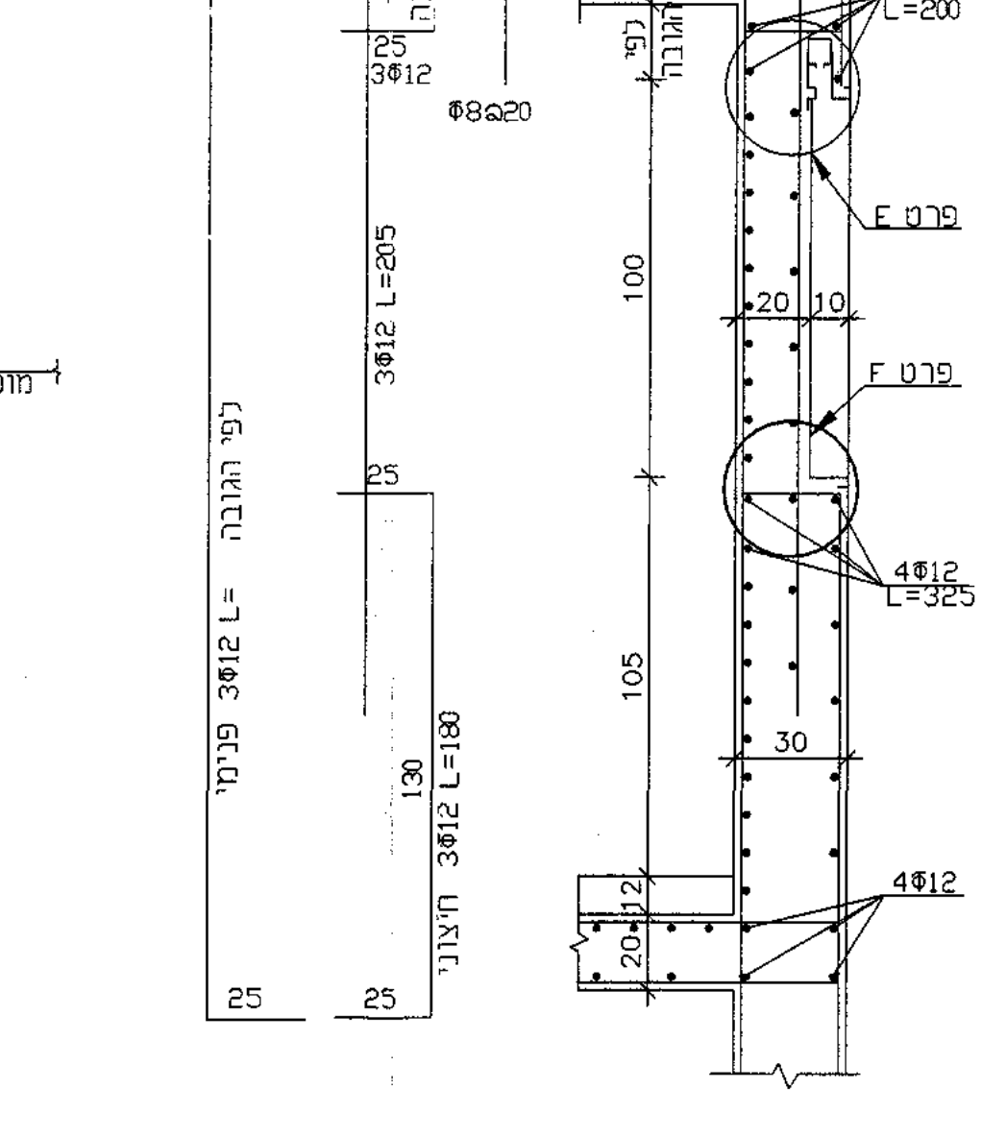
4Φ12
4Φ12 L=200
פרט E
פרט F
4Φ12 L=325
3Φ12 L=205
3Φ12 L=180
3Φ12 L = לפי הגובה
Φ8a20
100
105
30

חתך 7-7

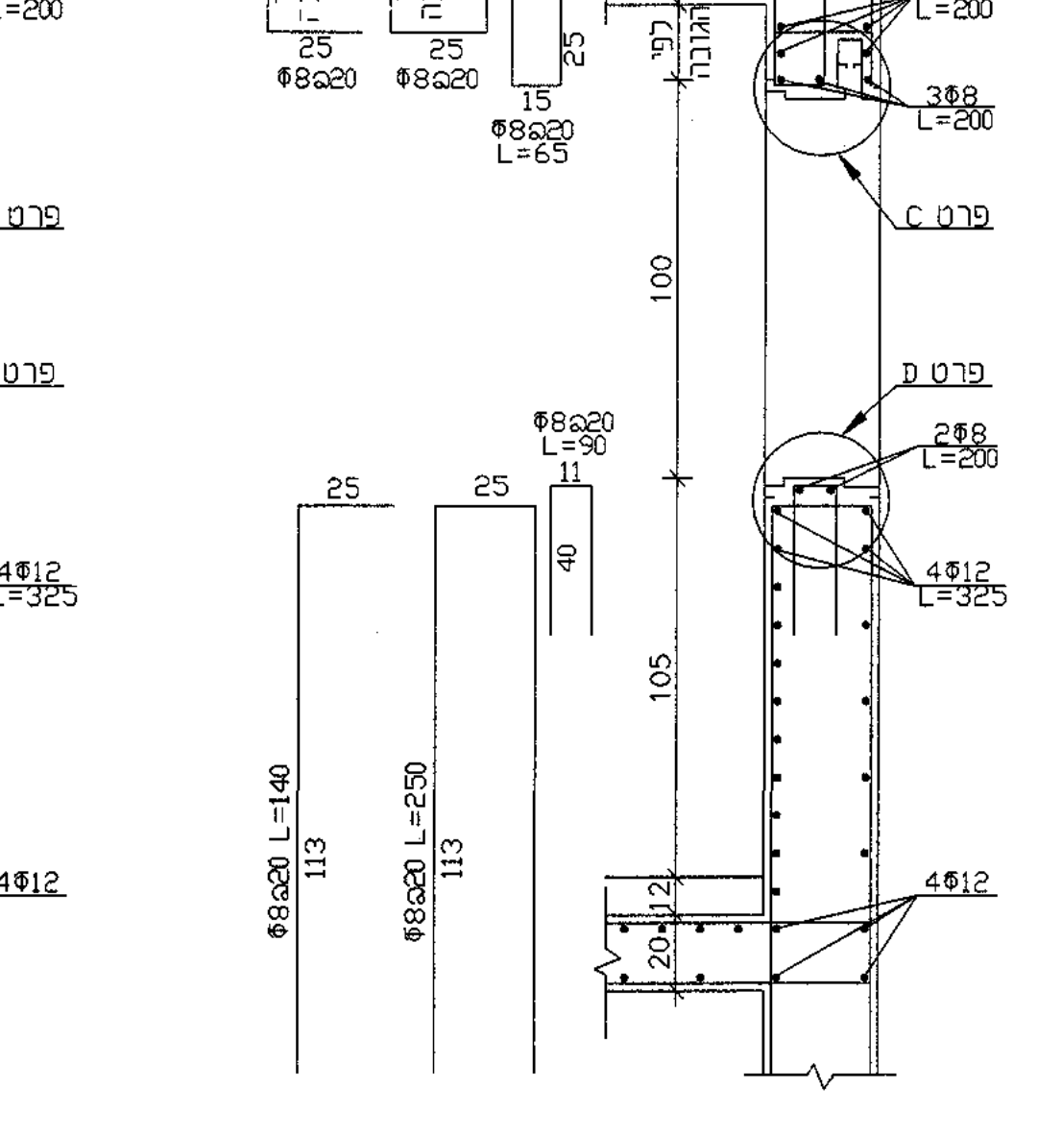
4Φ12
4Φ12 L=200
3Φ8 L=200
פרט C
פרט D
2Φ8 L=200
4Φ12 L=325
Φ8a20 L=140
Φ8a20 L=250
Φ8a20 L=90
Φ8a20 L=65

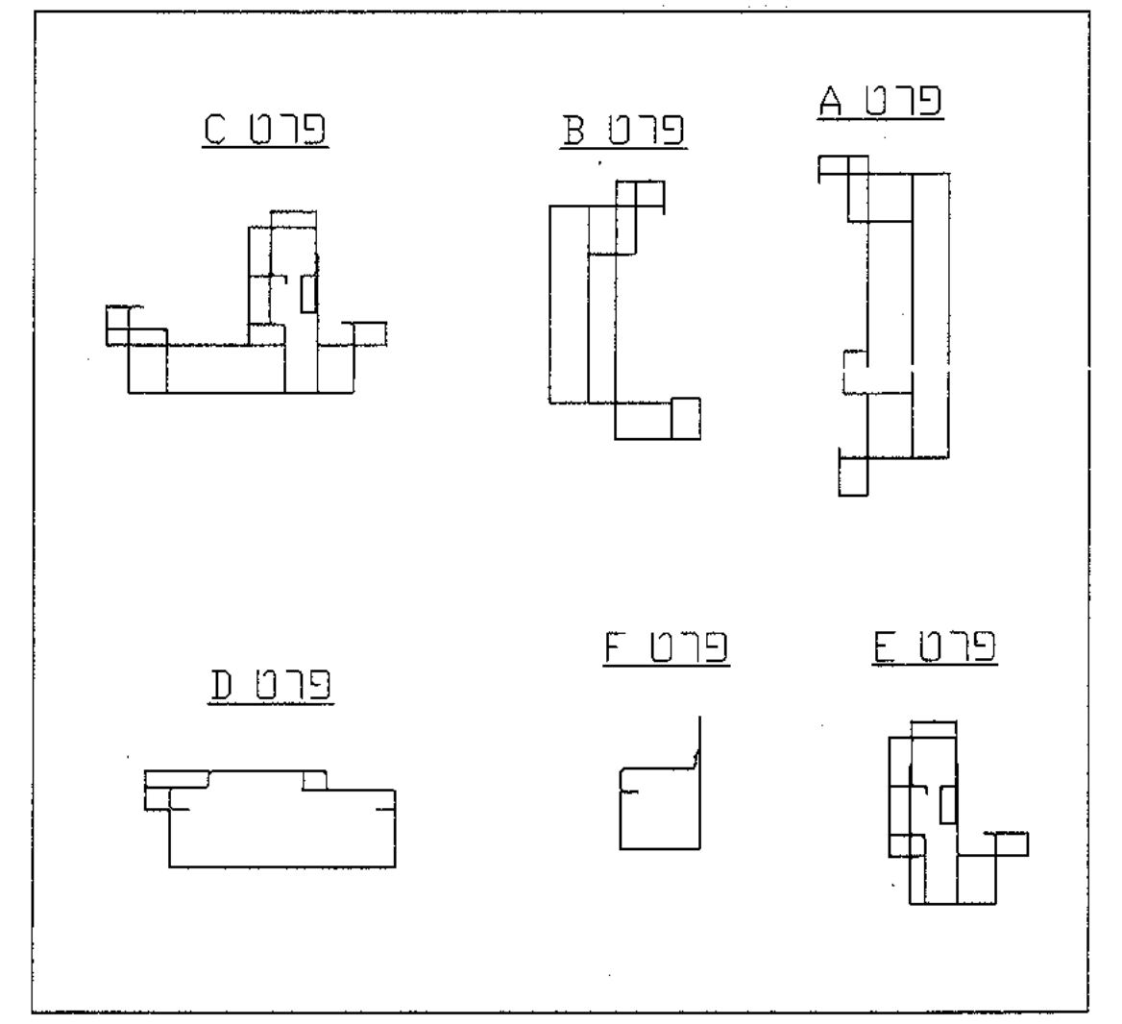
פרט C
פרט B
פרט A
פרט D
פרט F
פרט E

חתך 2-2
1:50

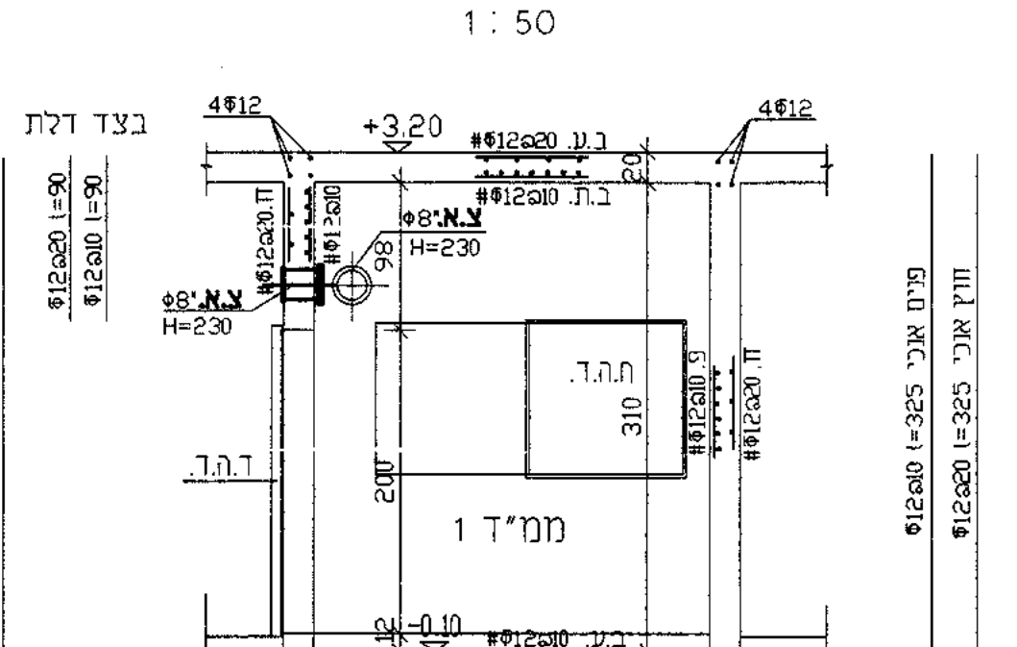
בצד דלת
+3.20
צ.א.Φ8 H=230
ת.ה.ד.
ד.ה.ד.
ממ"ד 1
-0.10
4Φ12
Φ12a20 l=325 חוץ אנכי
Φ12a10 l=325 פנים אנכי

חתך 1-1
1:50

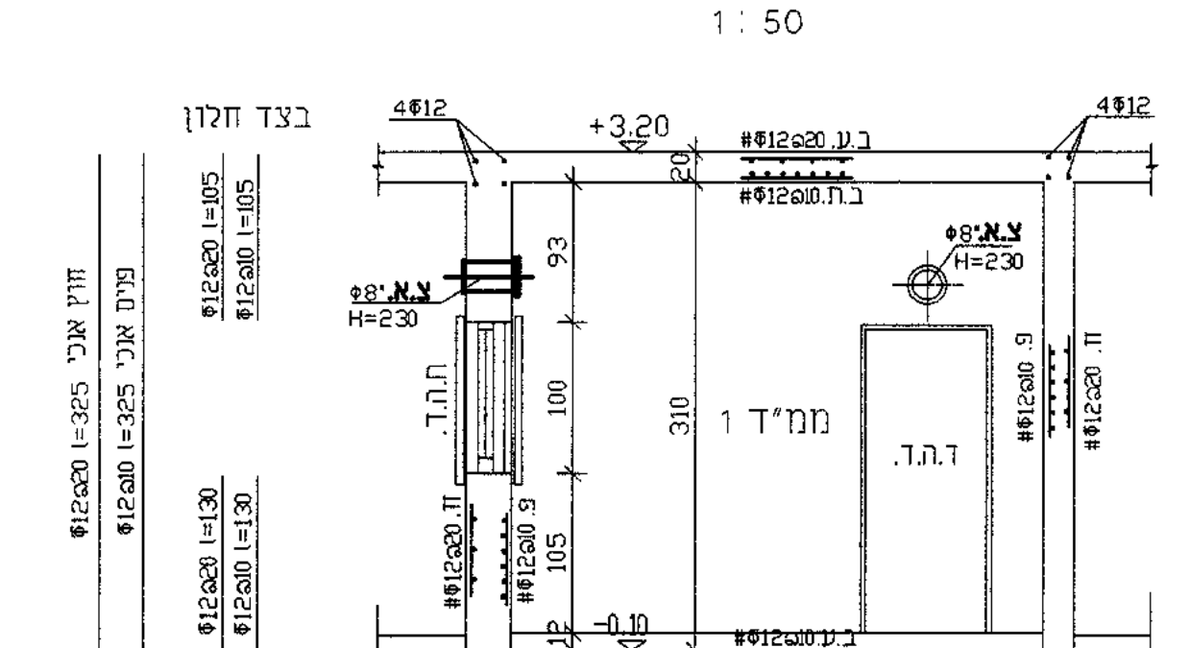
בצד חלון
+3.20
ממ"ד 1
ת.ה.ד.
ה.ה.ת.
-0.10
4Φ12

חתך 4-4
1:50

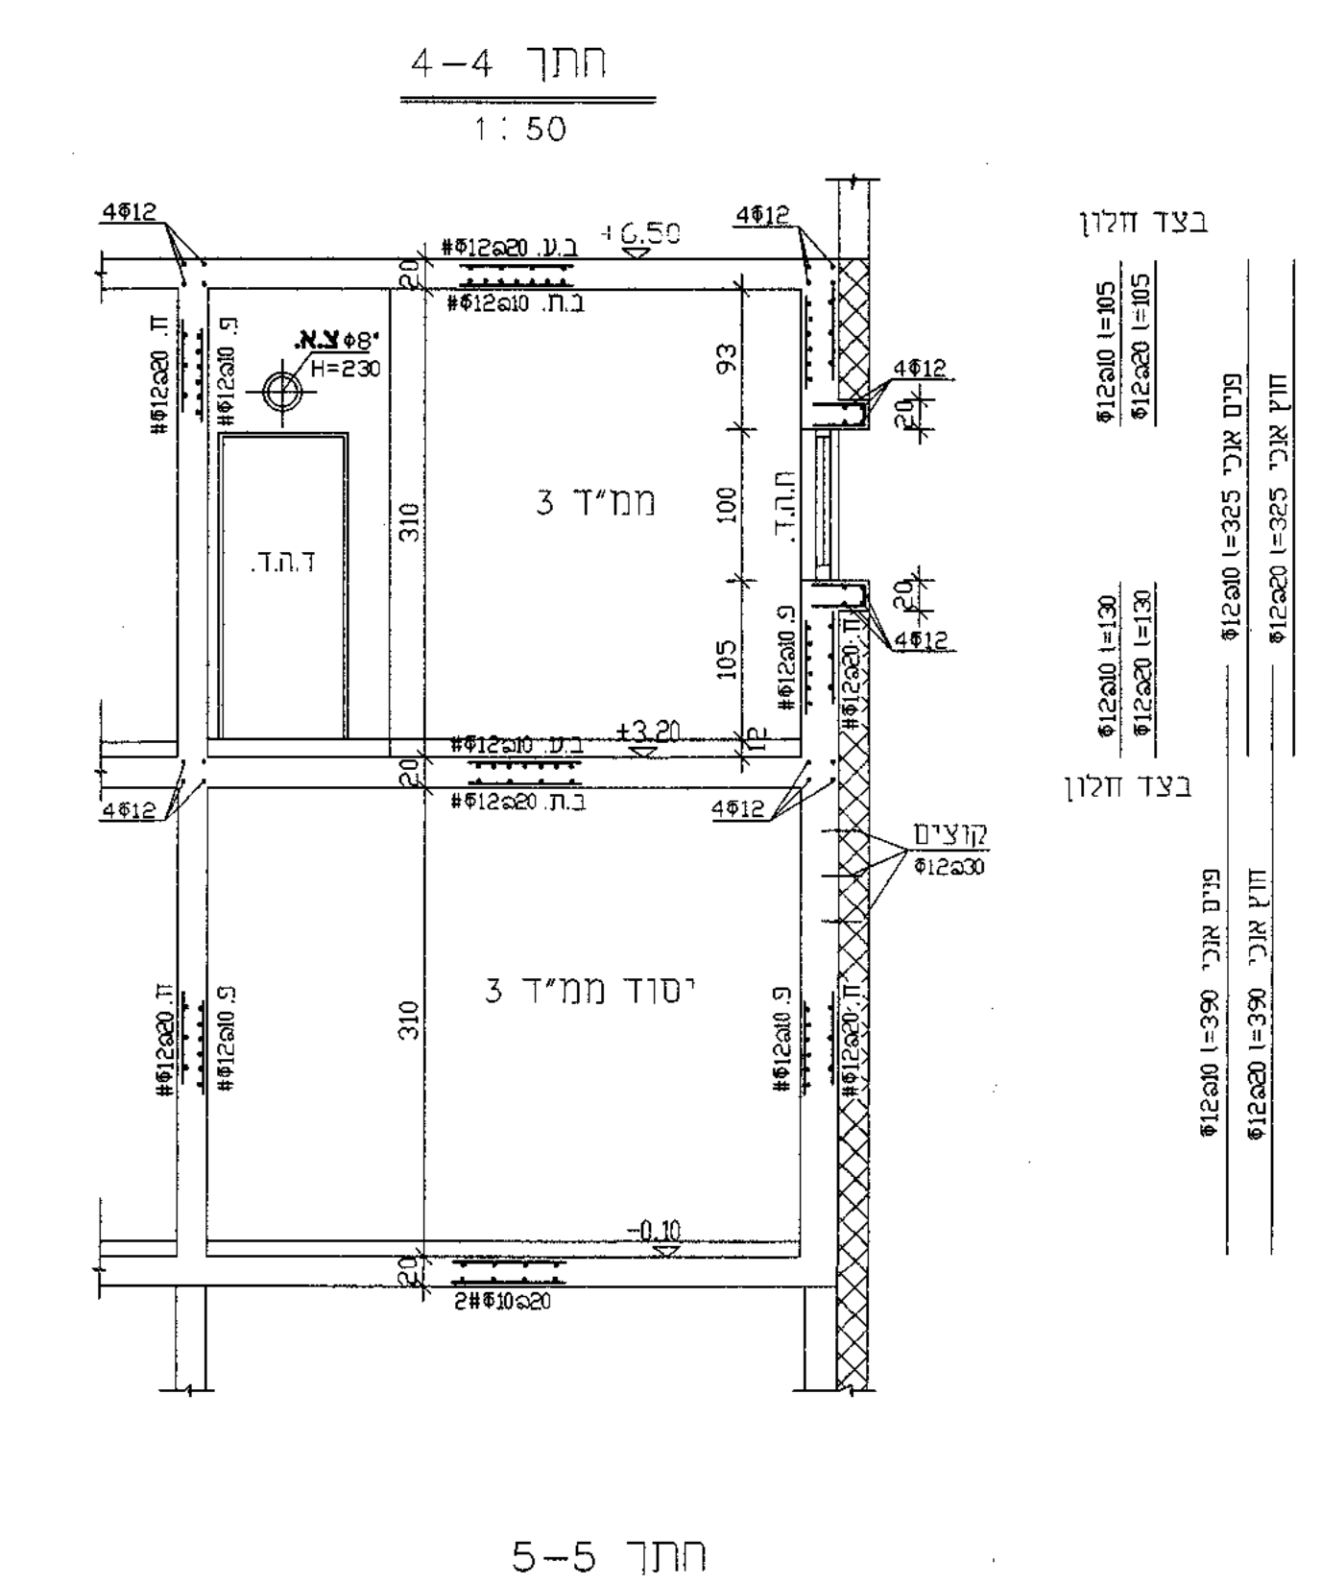
+6.50
ממ"ד 3
ד.ה.ד.
ה.ה.ת.
+3.20
יסוד ממ"ד 3
-0.10
קוצים Φ12a30
בצד חלון
4Φ12

חתך 3-3
1:50

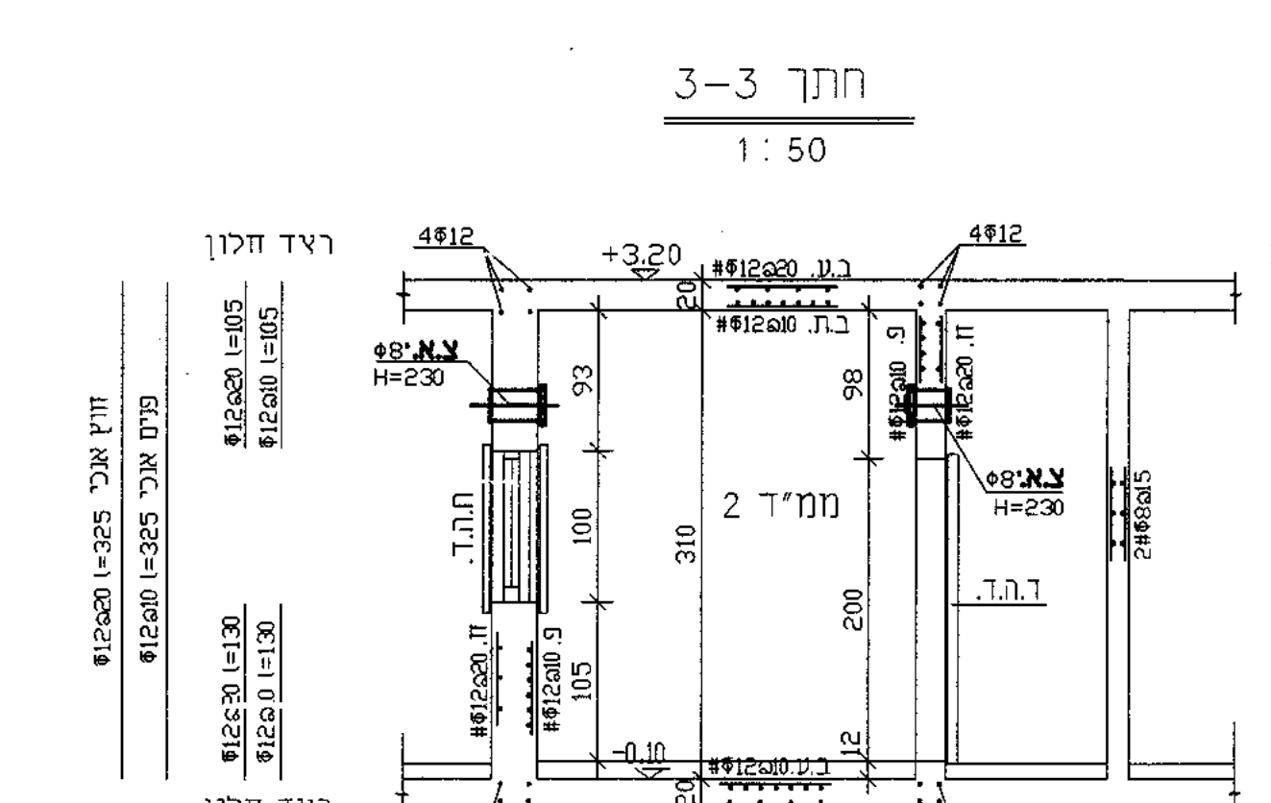
ראד חלון
+3.20
ממ"ד 2
ה.ה.ת.
ד.ה.ד.
-0.10
בצד דלת
בצד חלון
4Φ12

חתך 5-5
1:50

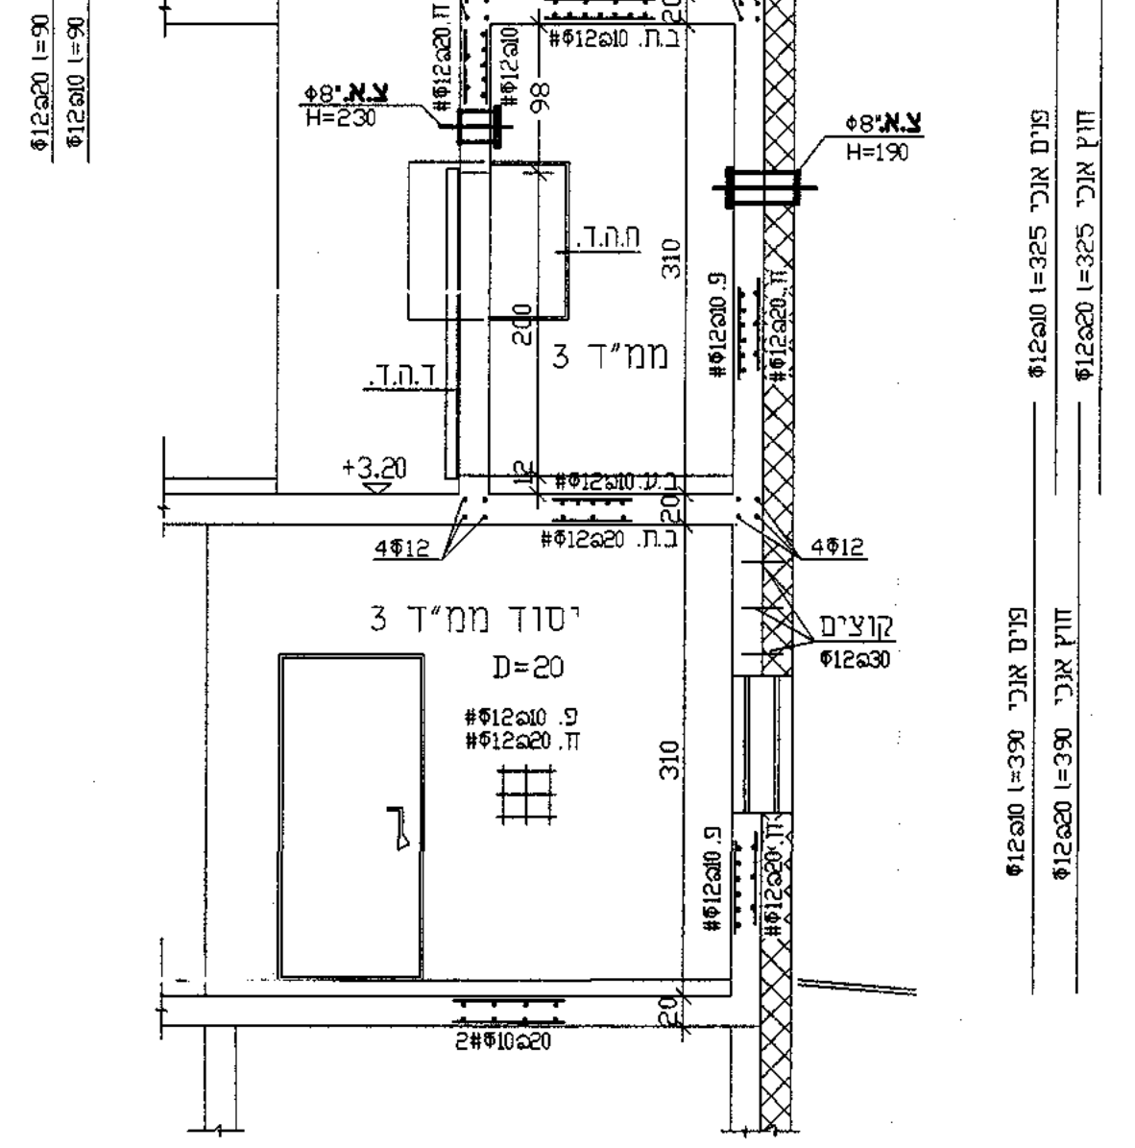
בצד דלת
+6.50
צ.א.Φ8 H=230
ת.ה.ד.
ד.ה.ד.
ממ"ד 3
+3.20
יסוד ממ"ד 3
D=20
קוצים Φ12a30
4Φ12

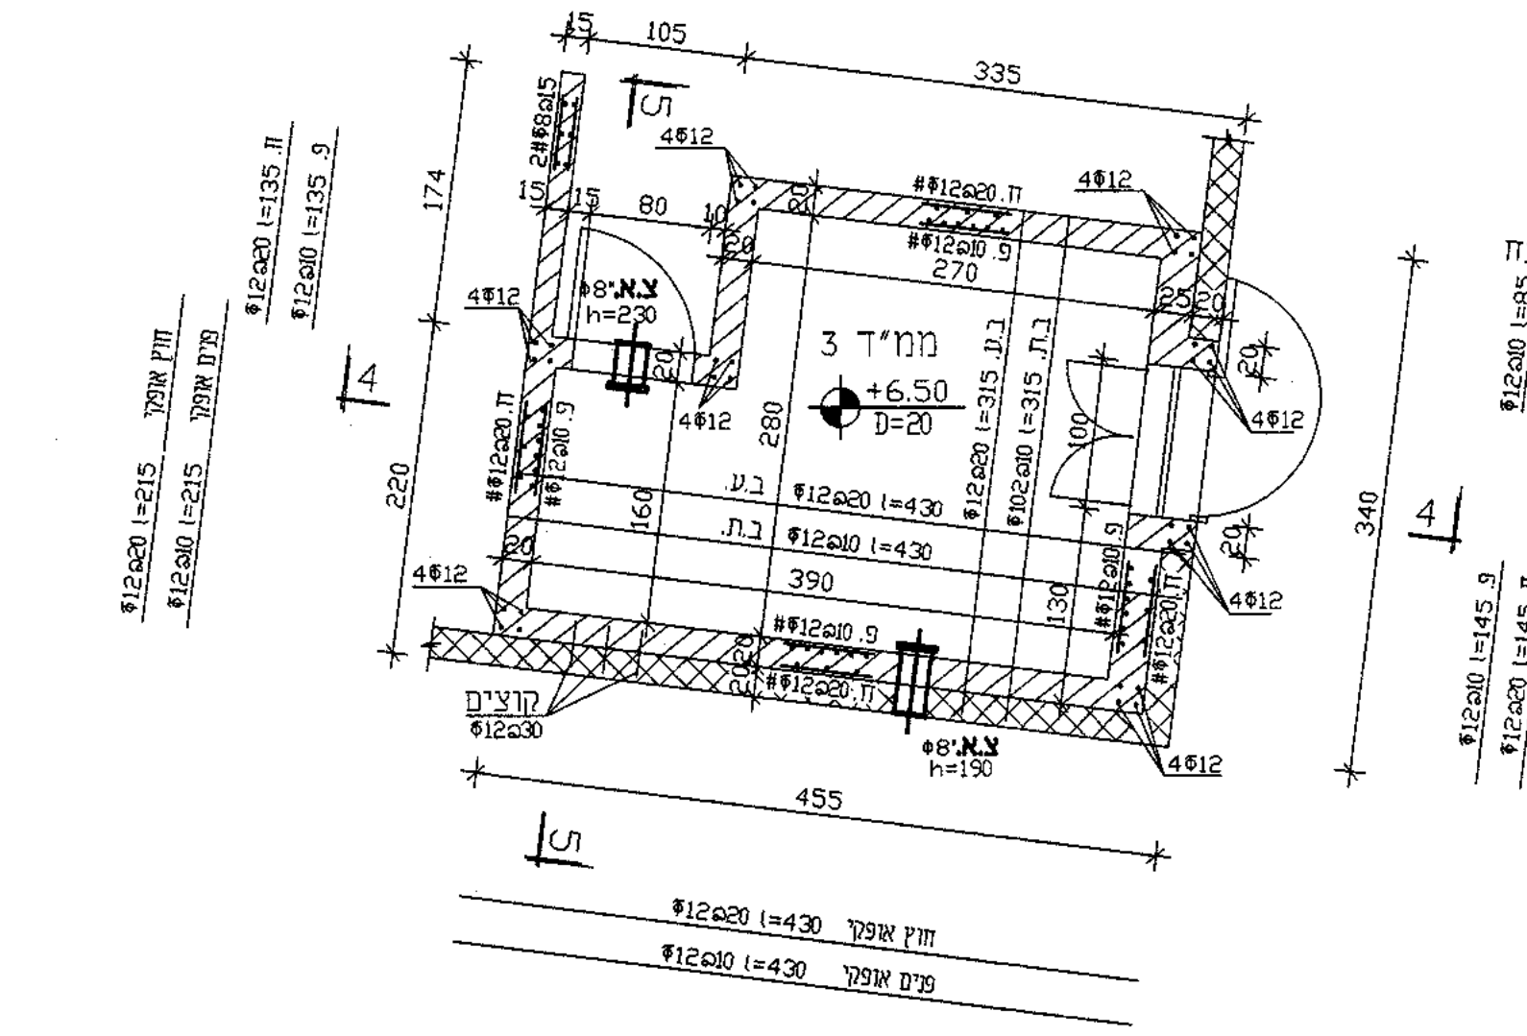
ממ"ד 3
+6.50
D=20
בצד פתח
קוצים Φ12a30
335
455
340
270
390
4Φ12

תקרת קומה א'
(רצפת קומה ב')
1:50

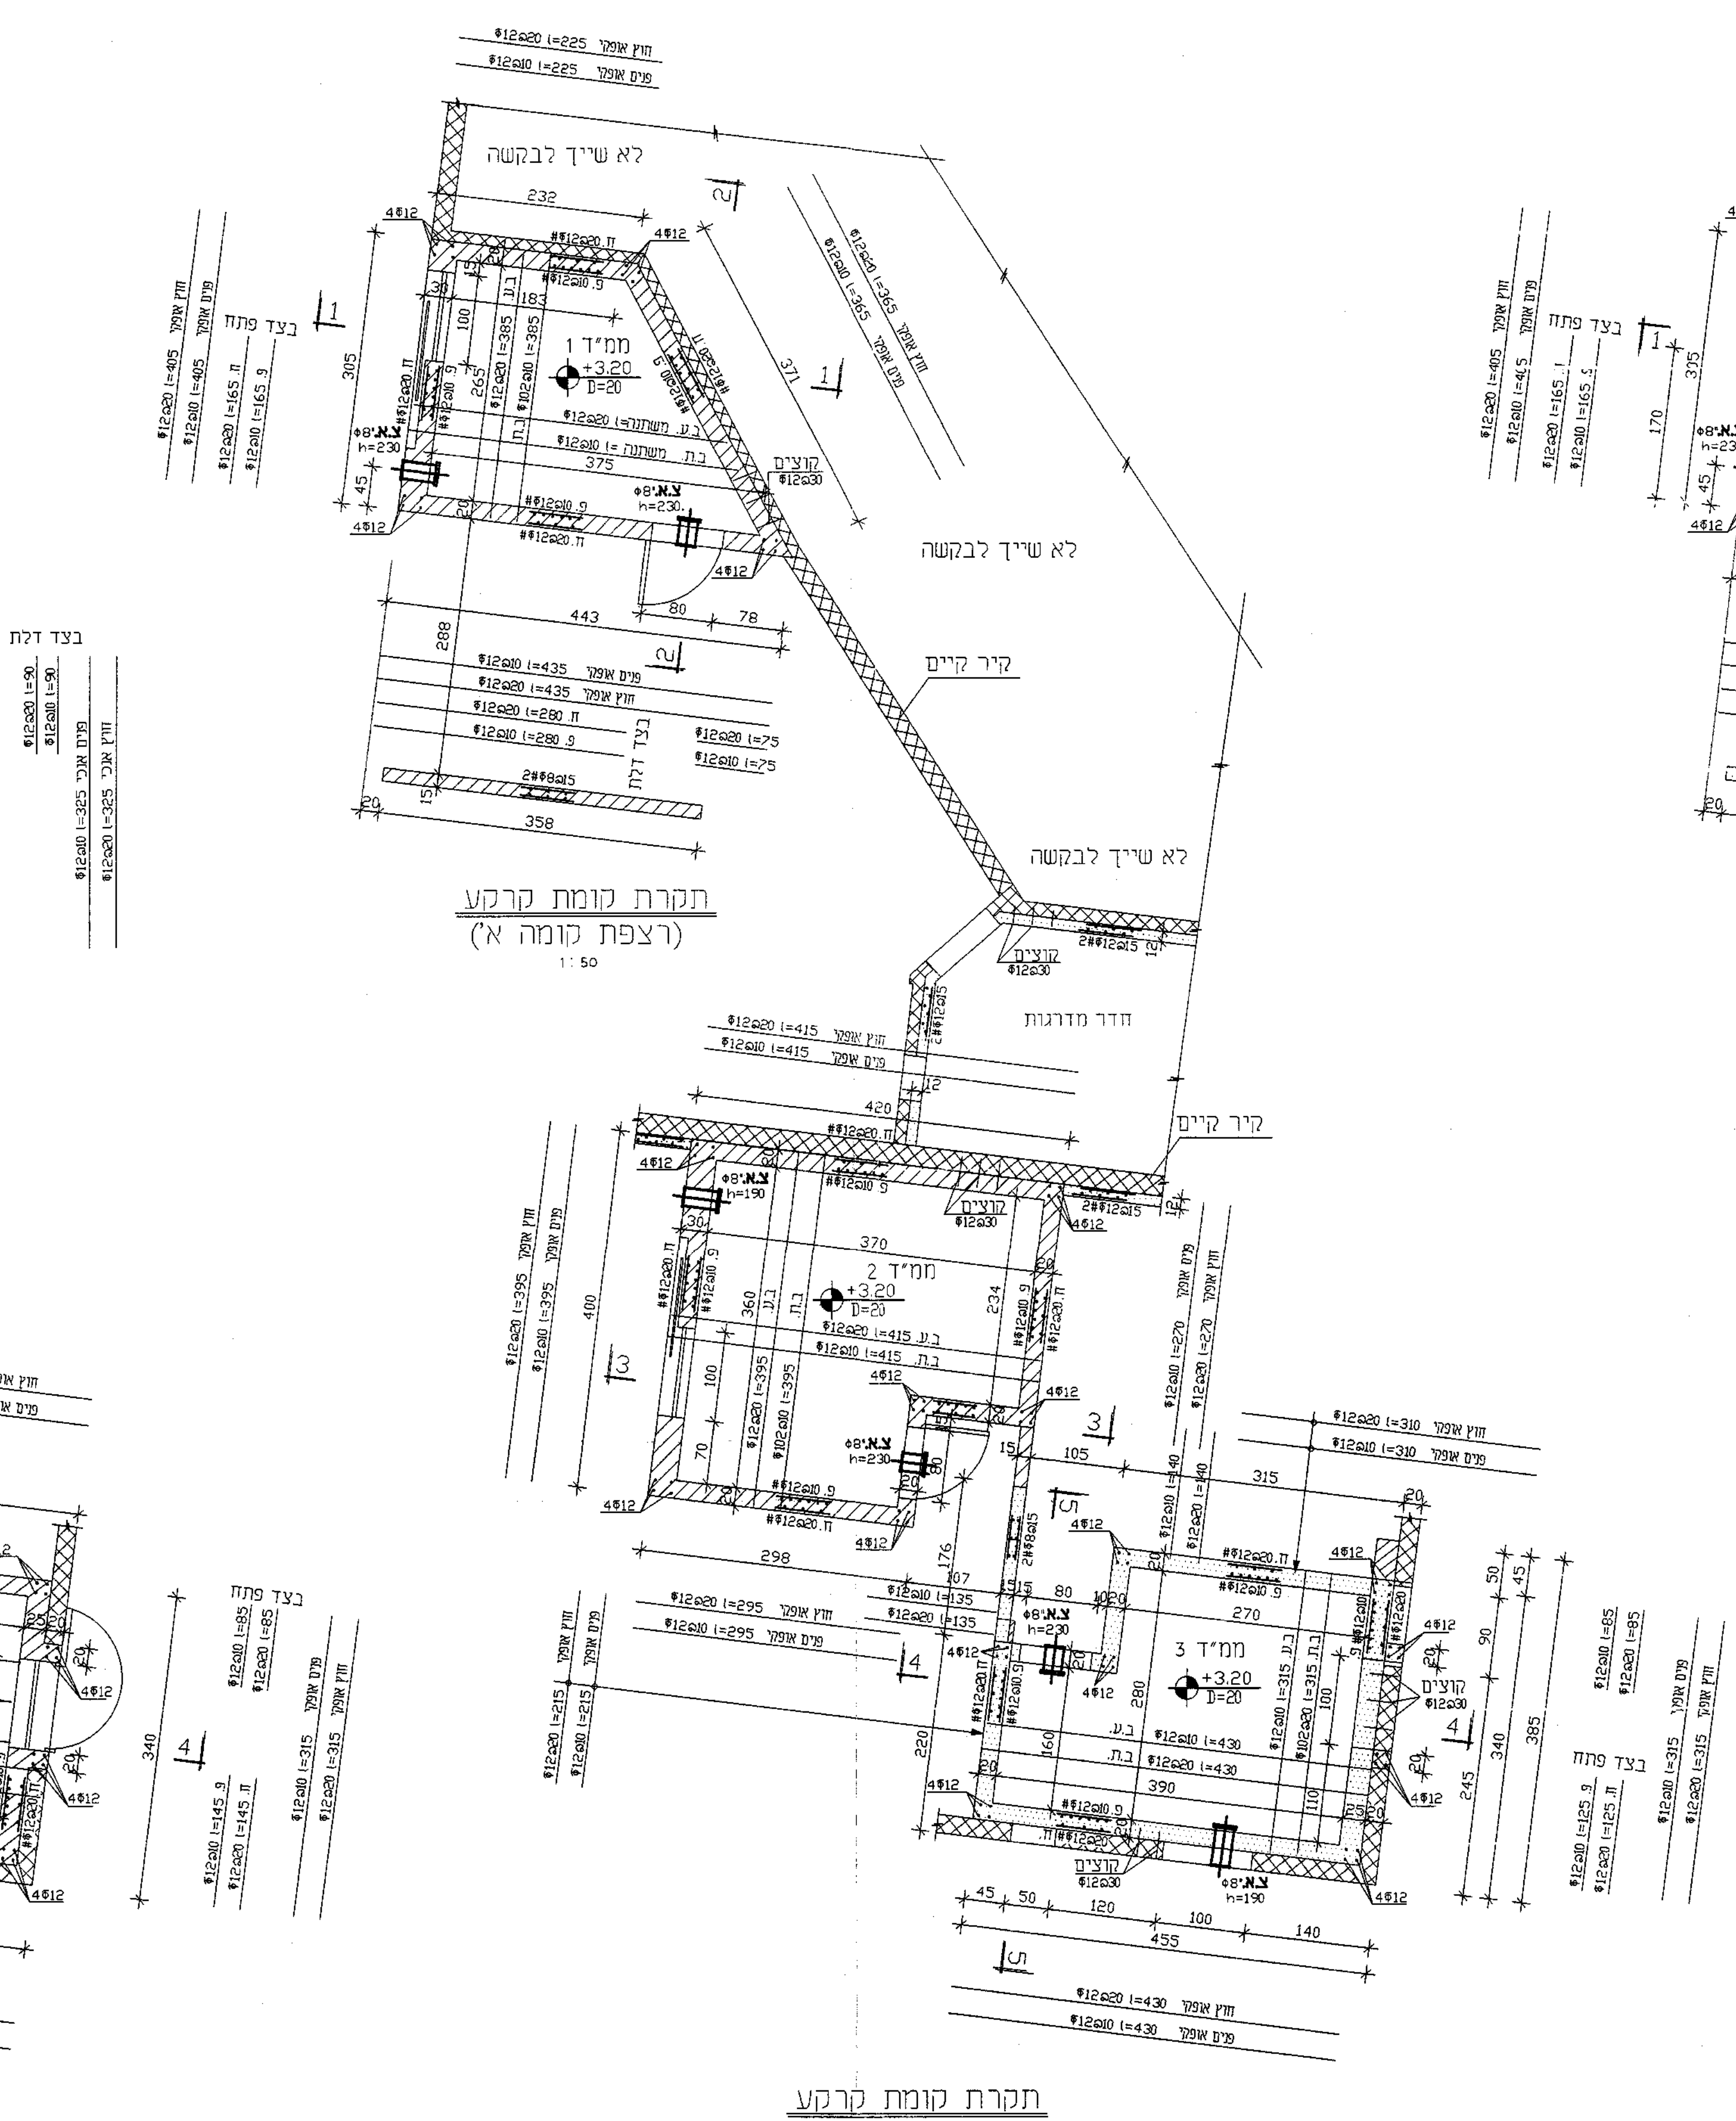
לא שייך לבקשה
ממ"ד 1
+3.20
D=20
קיר קיים
חדר מדרגות
ממ"ד 2
+3.20
ממ"ד 3
+3.20
בצד דלת
בצד פתח
קוצים Φ12a30
4Φ12

תקרת קומת קרקע
(רצפת קומה א')
1:50

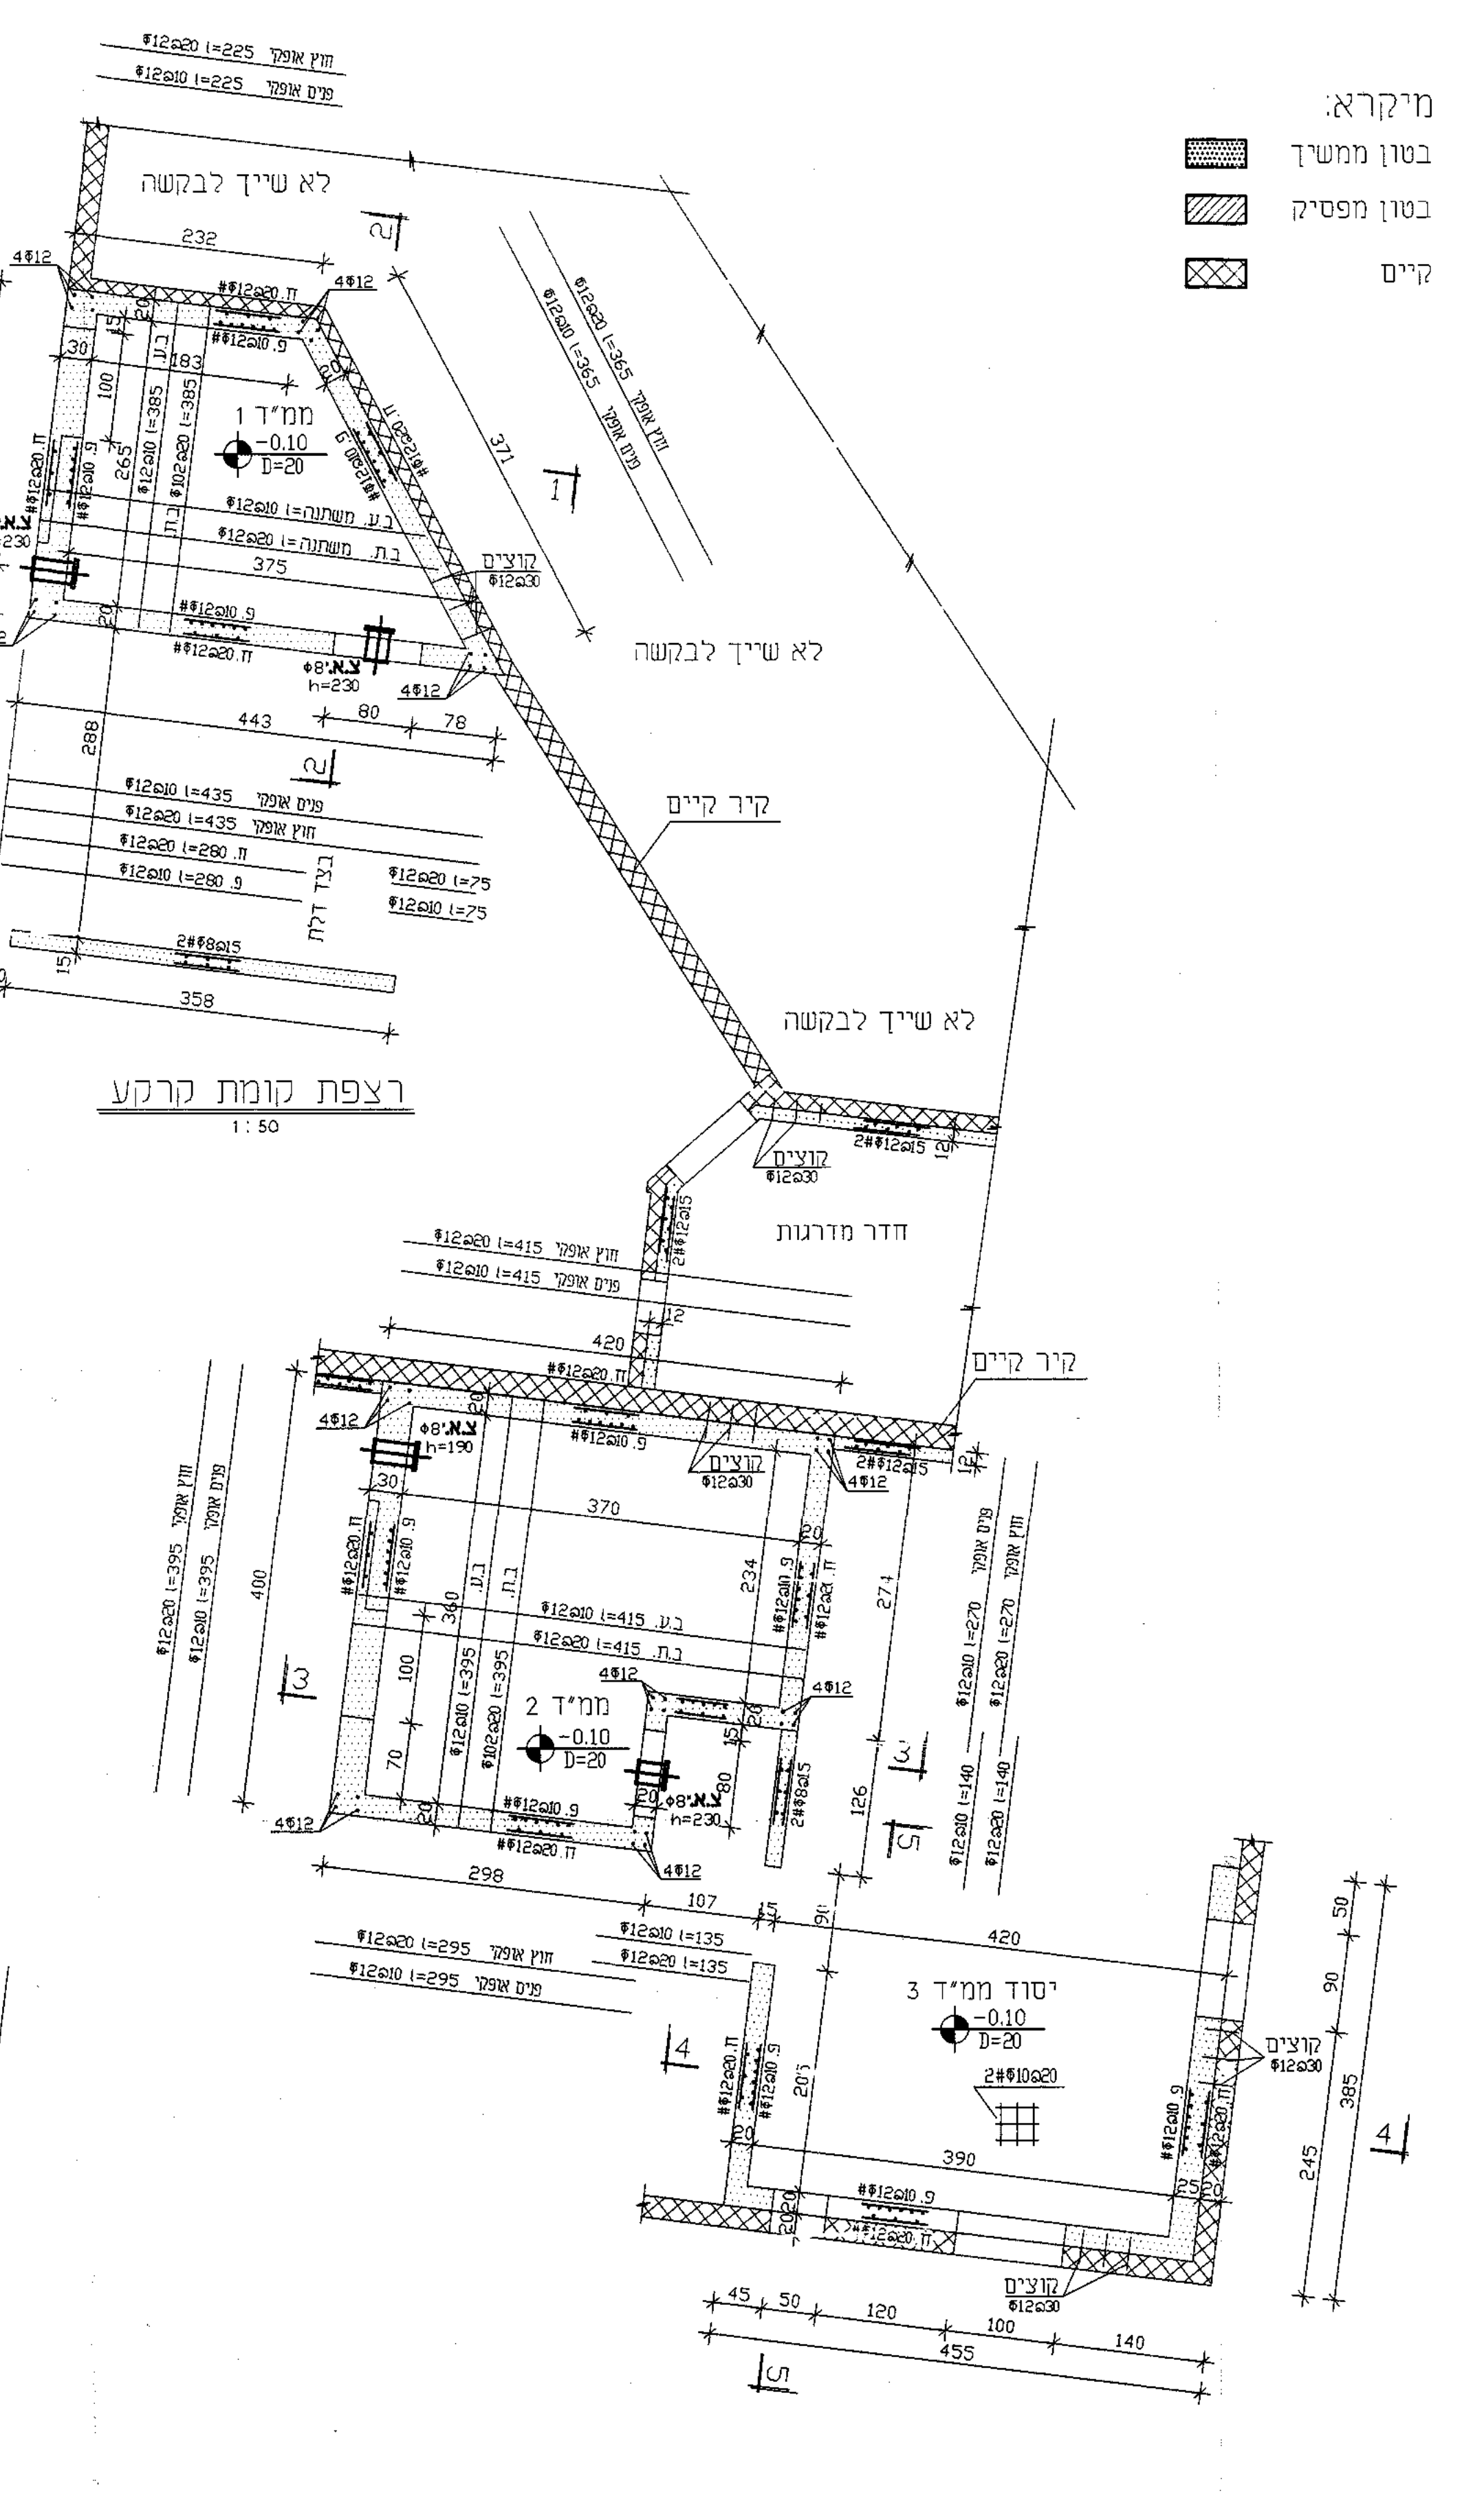
לא שייך לבקשה
ממ"ד 1
-0.10
D=20
קיר קיים
חדר מדרגות
ממ"ד 2
-0.10
יסוד ממ"ד 3
-0.10
D=20
2#Φ10a20
קוצים Φ12a30
בצד פתח
בצד דלת

רצפת קומת קרקע
1:50

מיקרא:
- ▩ בטון ממשיך
- ▨ בטון מפסיק
- ☒ קיים

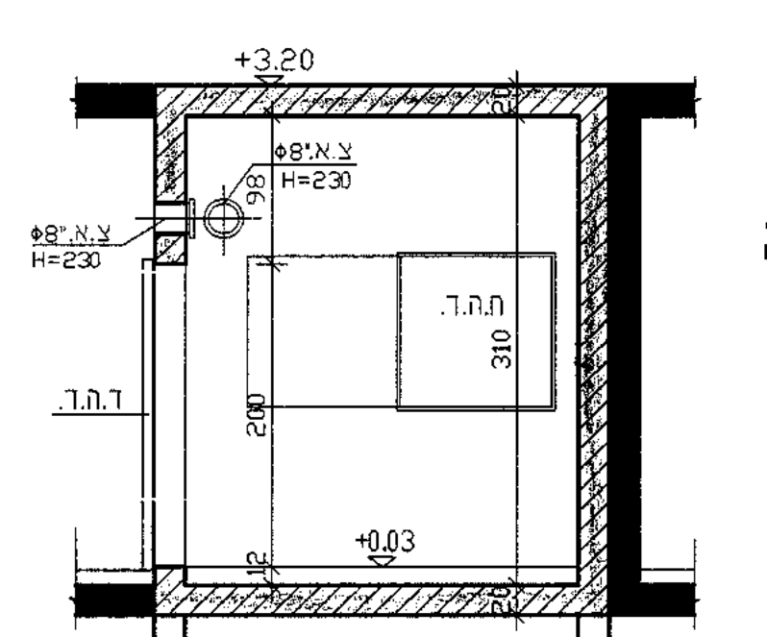
+3.20
צ.א.Φ8 H=230
ת.ה.ד.
ד.ה.ד.
310
200
+0.03

חתך 2-2
1:50

מקרא
- ⅄ שקע
- T.V טלויזיה
- Ⓣ טלפון
- Ⓜ ג.ת. חרום 40w
- ▭ ג.ת. פלוריסנט 2*40w
- ♂ מפסק בודד

צ.א.Φ8 H=230
ת.ה.ד.

משי נפתלי
רח' אצ"ל 58 , ת"א