



מפה טופוגרפית
1 : 250

תל-אביב
גוש : 6135
כתובת : רח' אצ"ל, 58 פינת רח' שושן, 2
הוכן עבור : משפ' יצחקי
מטרת המדידה : היתר בניה
חלקות : 45.44 (חלק)

חלקה	שם הבעלים	מס' ח.ד.	שטח חלקה כולה	בעלות בחלקים	בעלות במ"ר
44	יצחקי שושנה	0481321\8	11.476.00	32\11476	32
	יצחקי זהבה	0481322\6		11\11476	11
	יצחקי נפתלי	0481318		108\11476	108
	בן אברהם יאיר	5119051		11\57380	2.2
	דייכובסקי אביגיל	4789999		11\57380	2.2
	יצחקי חנה	04449625		11\57380	2.2
	בן אברהם יונתן	004790002		11\57380	2.2
	טסה נאווה	58907663		11\57380	2.2
	מדני מזל	0479542		9\11476	9
	אריאל רחל	0481317		9\11476	9
	ורון נעמי	0481319		11\11476	11
	ורון צפורה	0481320		9\11476	9
	מזרחי חרותה	0481323		11\11476	11
				211	
45	בן אברהם מיריס	0478998	9.821.00	5\9821	5
	מדני מזל	0479542		4\9821	4
	אריאל רחל	0481317		4\9821	4
	ירון נעמי	0481319		5\9821	5
	ירון ציפורה	0481320		4\9821	4
	יצחקי שושנה	0481321\8		18\9821	18
	יצחקי זהבה	0481322\6		5\9821	5
	מזרחי חרותה	0481323		5\9821	5
	יצחקי נפתלי	0481318		51\9821	51
				101	

סה"כ 312

בעלות במ"ר : 312

שטח מדוד (מ"ר) : 286.72 (188.50+98.22)


חלקה 44 188.5 מ"ר
חלקה 45 98.22 מ"ר

שטח מגרש משני :

שטח להפקעה :



נס"מ

תרשים הסביבה 1:1250

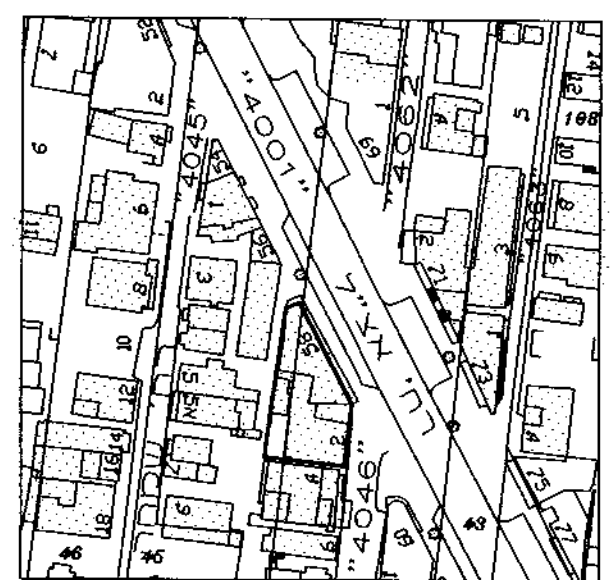

הערות

- המספרים בסוגריים מציינים גבהים.
- הגבהים מבוססים על נק. עירונית מס' 188 שגובהה 17.530 מ'.

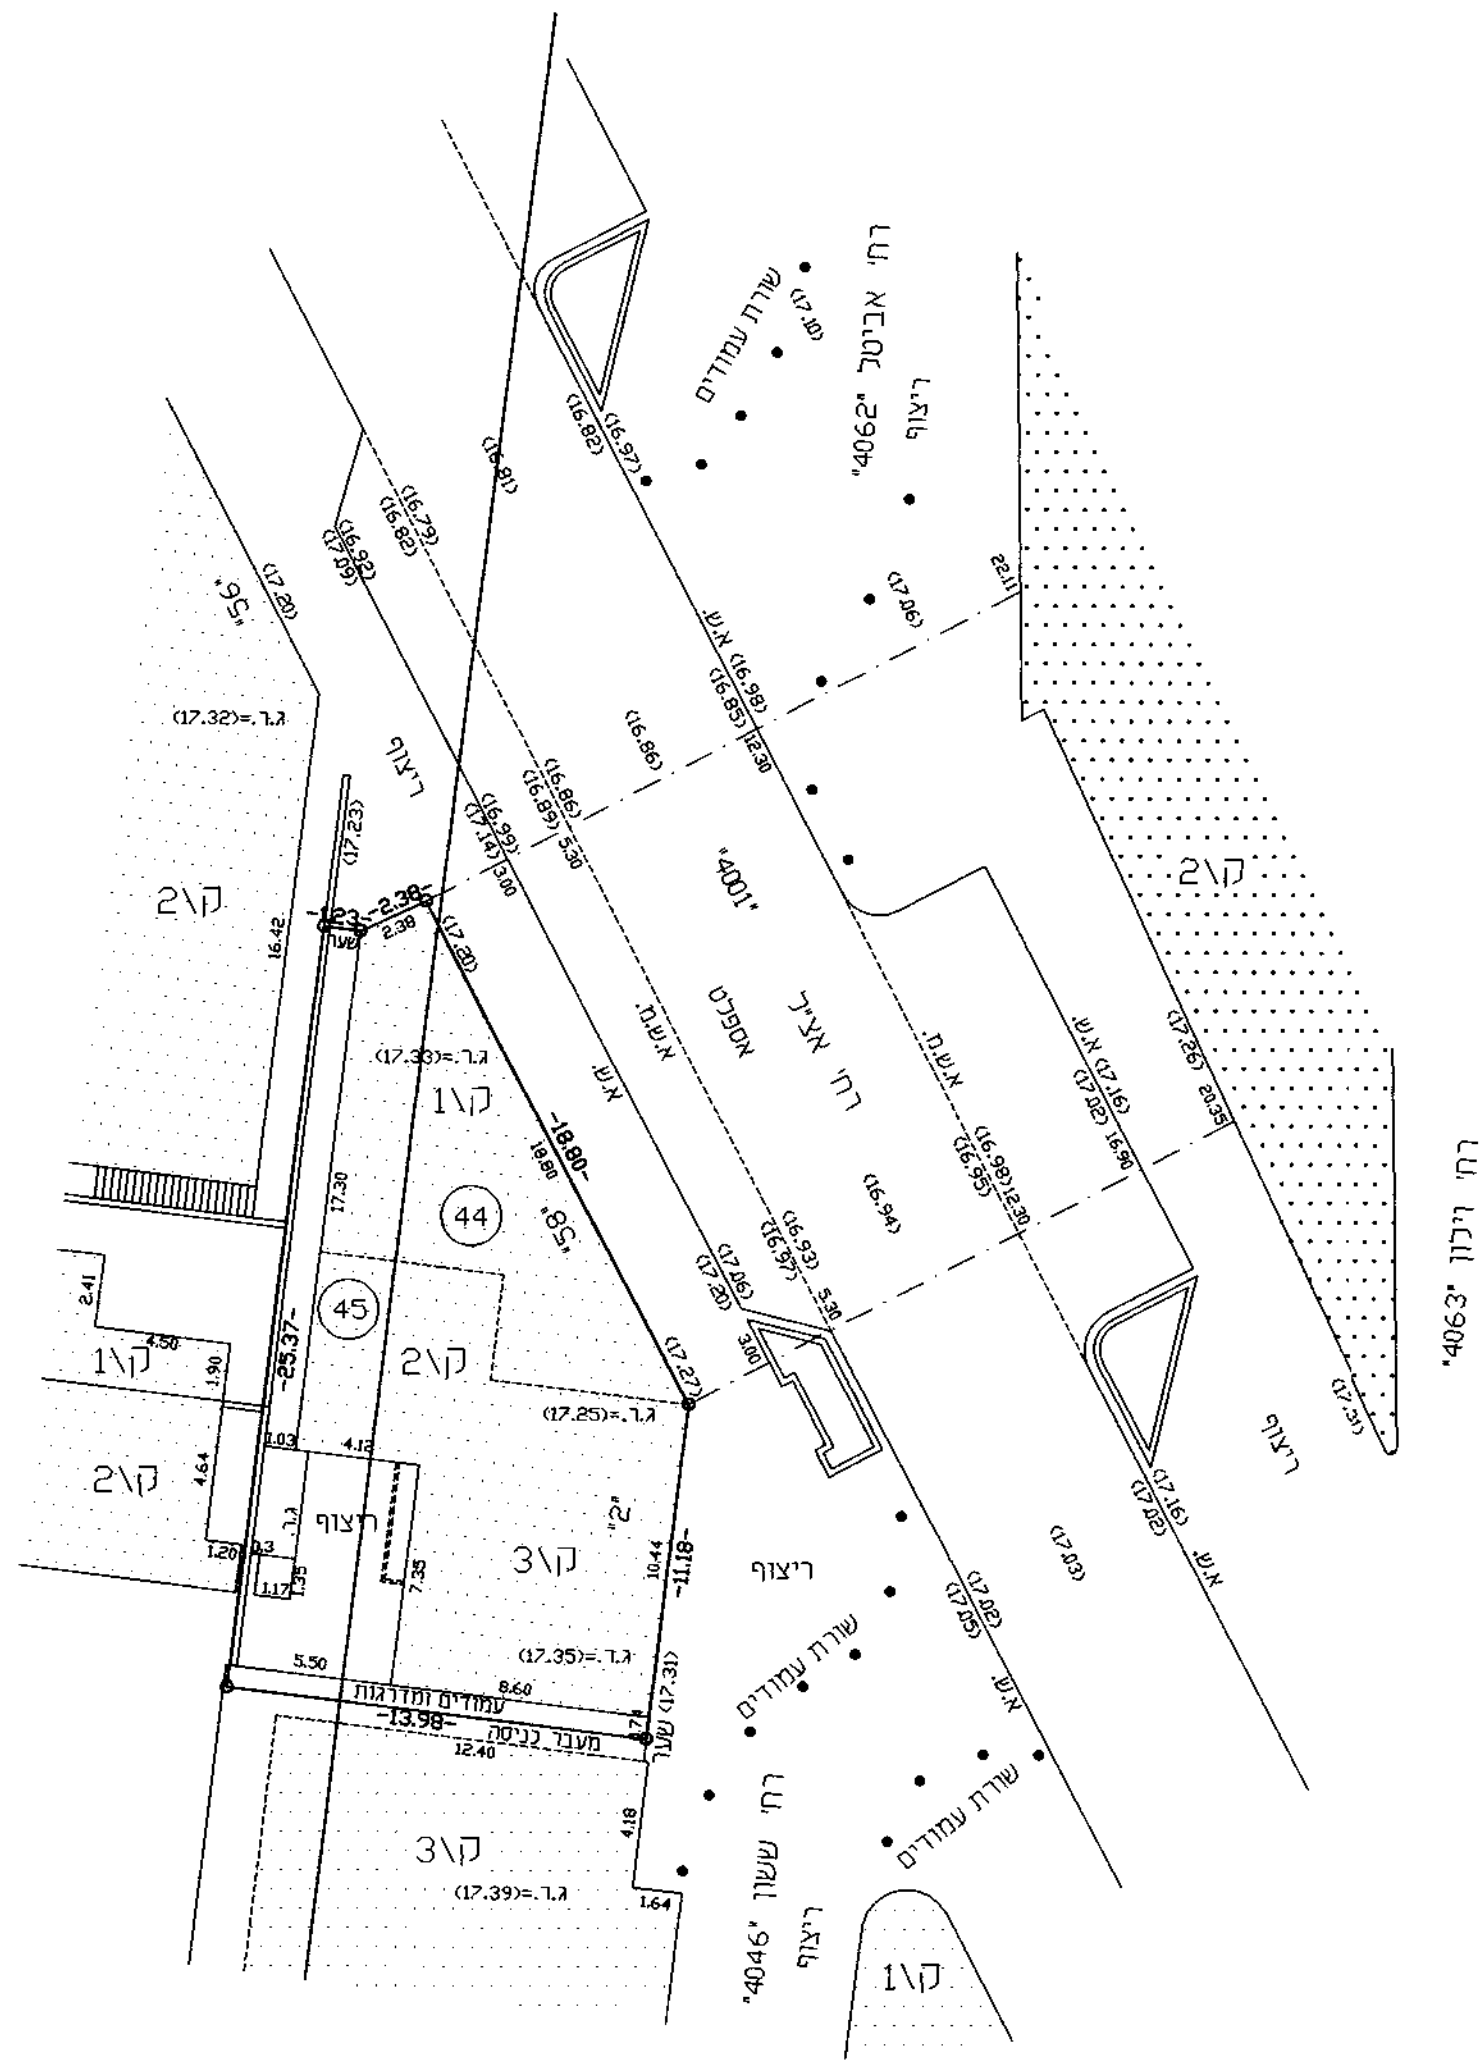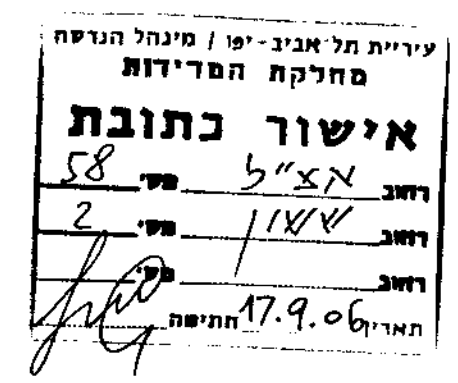

סוף מסמך

עידכון מפה בתאריך 7.03.2006
עידכון מפה בתאריך 5.01.2005

לא לצרכי רישום

תל אביב
תאריך : 1.12.2003
י.אברבך
חב' אברבך ושות' מודדים מוסמכים בע"מ
רח' דיונגוף, 190. תל-אביב טל' 5235891, 03-5226791

הנני מצהיר בזה שהמפה נעשתה לפי חוק התכנון והבניה, התקנות וההנחיות של עיריית תל-אביב-יפו.