

27-01-2001

מנהל ההנדסה / אגף תכנון ובנין ערים
מח' שרותי בנין ערים - מדור המידע

הערות למפה טופ' / מצבית

גוש - 6135 חלקה - 71

מס' תיק מידע 107-21

רח' 4001-אצ"ל 66

קווי בנין: צד 1 - 3.00 אחור - 5.00

יעוד בתוקף - מגורים ב שיקום

תכניות בתוקף - ג,ע, 2215, 2215א1

תכניות בתכנון - ח

הפקעה

הערות - רחוב 4001-האצ"ל ברוחב 20.0 מ'. קו בנין

2.0 מ'. האזור ב' שיקום עם חזית מסחרית.

קו בנין לצדדים 3.0 מ' או 0.0 מ' בקיר משותף

ולאחור 5.0 מ'.

שיעור הבניה יהיה 140% משטח המגרש ותכנית הקרקע

לא תעלה על 60%. גובה הבנין 3 קומות.

צפיפות הדיור לפי תכנית 2215 א/1 לפיה נקבע כי

שטח יחיד לא יקטן מ-90 מ"ר כולל ממ"ד, למעט

מקרים בהם הועדה המקומית תהיה רשאית לאשר עד

שתי יחיד לא פחות מ-70 מ"ר כל אחת.

על פי תכנית ג' ניתן לבנות עליונות גג בבית צמוד

קרקע וחדר יציאה לגג בשטח של 23 מ"ר ופרגולה

בבנין דירות בתנאים.

מרתף בהיקף הבית לשימוש הדיירים לפי תכנית ע'.

היטל השבחה ייגבה בבנין חזית מסחרית.

עריית תל-אביב-יפו
טוביה שלום
ממונה ת"ת ומקרקעין
אגף תכנון ובנין ערים

חתימה

16-01-2001



אסתר חזן
מנהלת מדור המידע
עיריית תל-אביב-יפו

15.1.01

תל אביב
גוש : 6135
חלקה : 71 (חלקה)

מפה טופוגרפית
קנה מידה 1:250

מהות הבקשה : תוספת בניה
שטח מדוד : 132.00 מ.
שטח רשום : 135.00 מ. (כפי נסח)
כונן צבאי ו.א.כ.א.א.

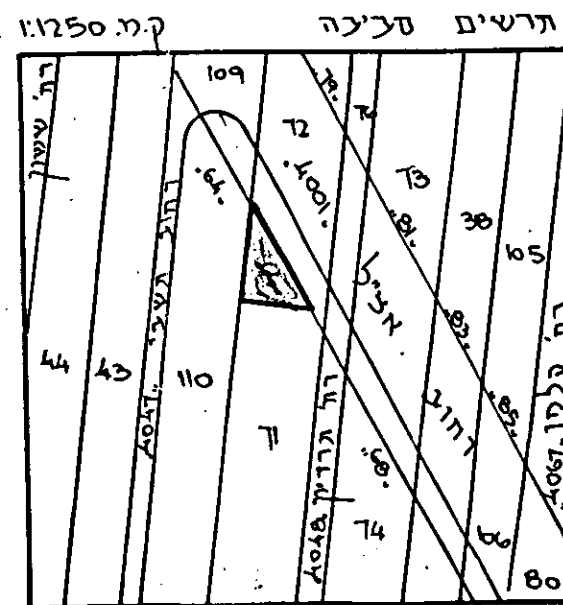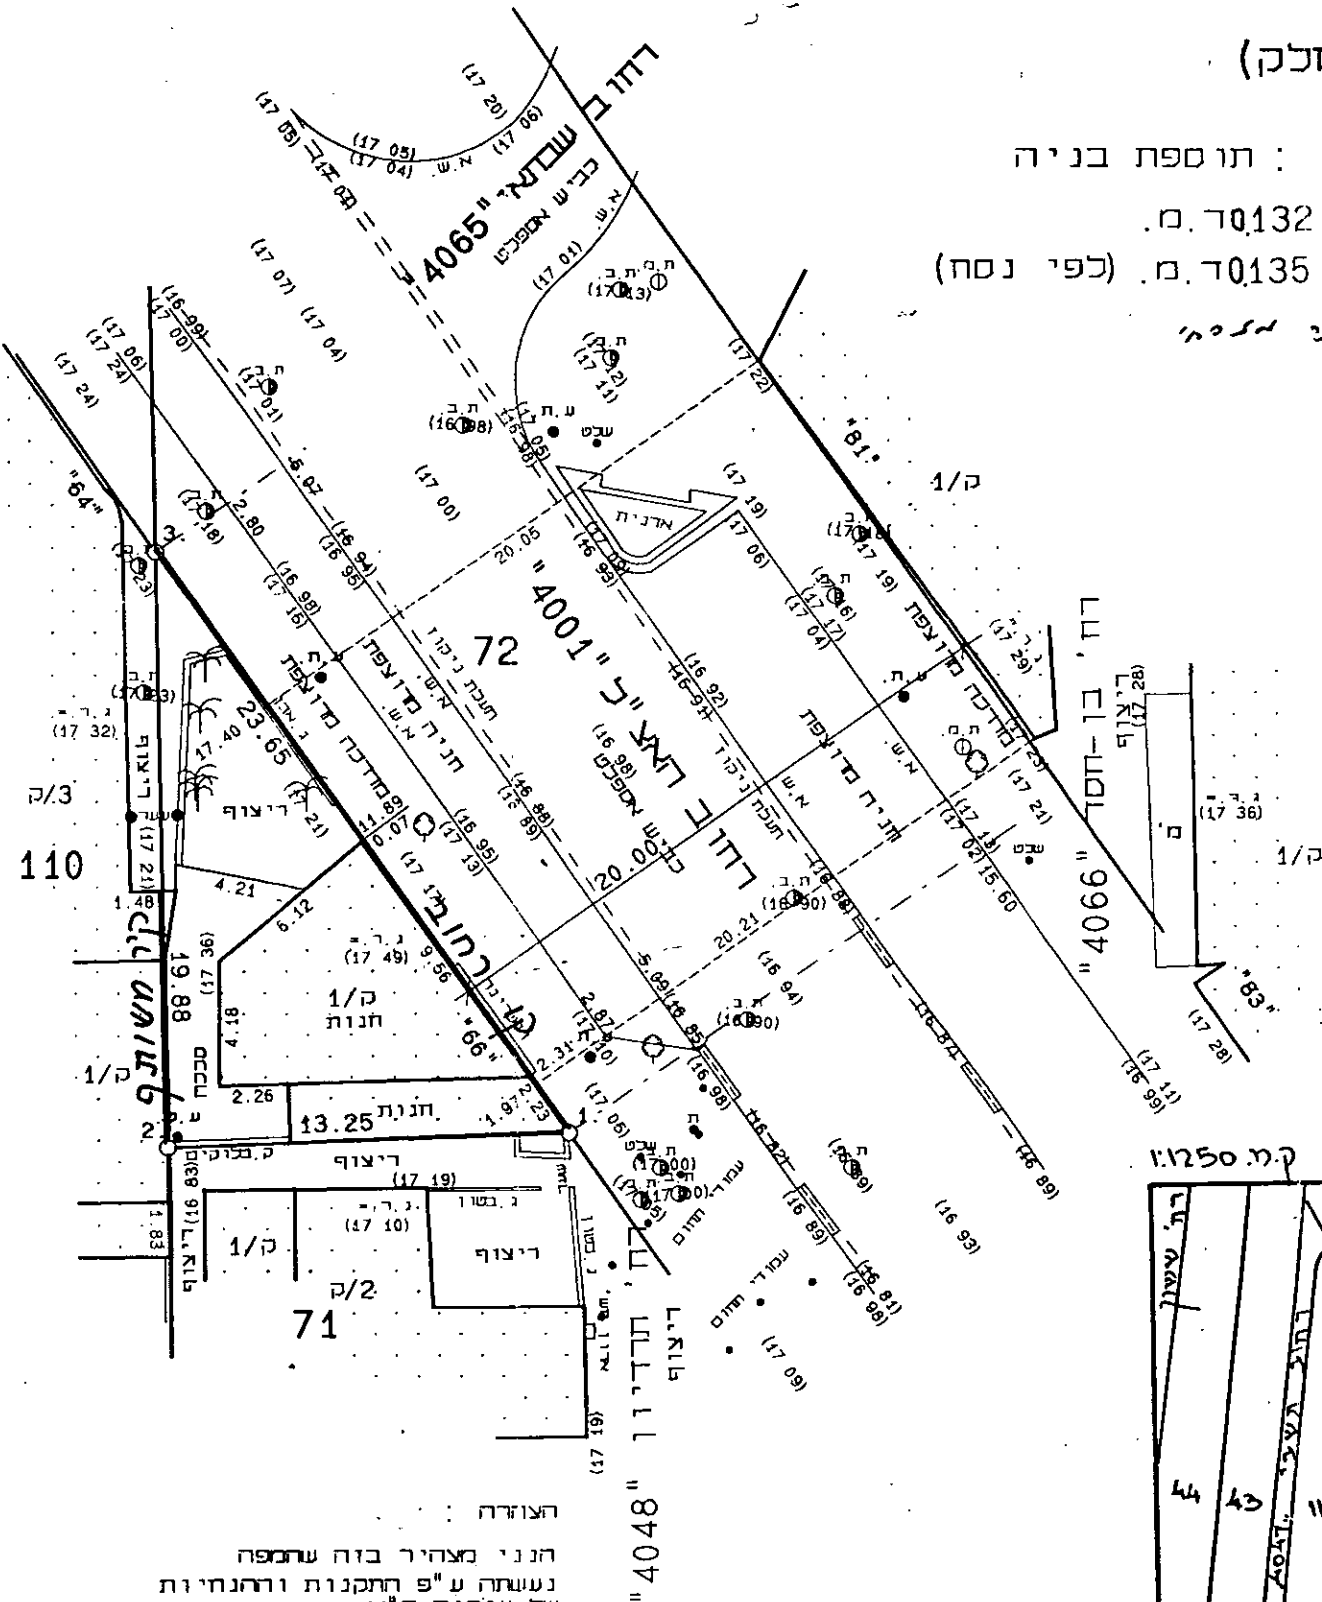

עיריית תל-אביב-יפו
מנהל בינוי ותשתית / אגף עבודות ציבוריות
מחלקת מדידות
חתימה _____
חתימה _____
תאריך: 21.01.2001

שטח הפקעה (לצורך חשוב זכויות בניה)
מאושר (ת.ב.ע.) _____ מ"מ (גרפי)
יוצע (ת.ב.ע.) _____ מ"מ (גרפי)
גרמי שטח הפקעה (כפי יתברר בגומה לצורכי רישום)

עיריית תל-אביב-יפו / מינהל הנדסה
מחלקת המדידות
אישור כתובת
רחוב _____ מס' _____
רחוב _____ מס' _____
רחוב _____ מס' _____
תאריך: 11.01.01 חתימה _____

תאריך: 9.1.01
מודד מוסמך
ד"ר ש' מדידות בע"מ
דניאל שטרן מודד מוסמך מ.ר. 475
ראשכ"צ, בדקת 51 טל. 9622524, פקס: 9622569

הערות:
1. הגבהים מבוססים על נ.ק. עירונית 187 שגובהה 17.549 מ'.
2. הגבהים רשומים בסוגריים.
3176-X2.PRJ

מ.ר. 475