
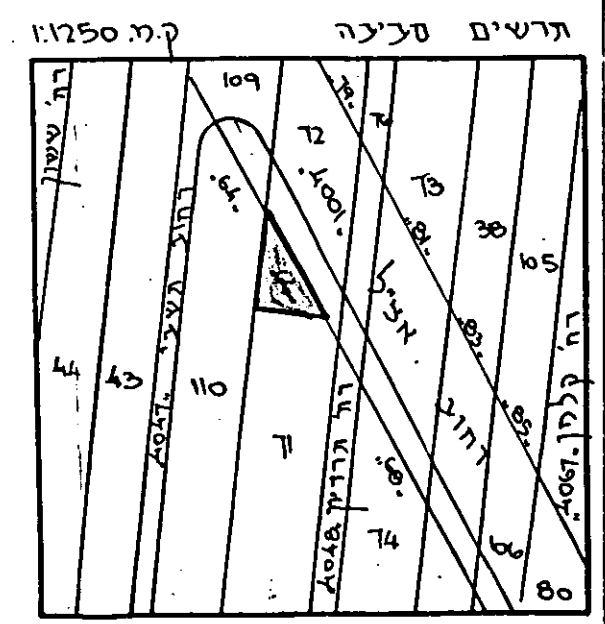


210107

תל אביב
גוש : 6135
חלקה : 71 (חלק)

מפה טופוגרפית
קנה מידה 1:250

מהות הבקשה : תוספת בניה
שטח מדור : 0.132 ד.מ.
שטח רשום : 0.135 ד.מ. (לפי נסח)
הוכח כי אין צורך להגיש תוכנית

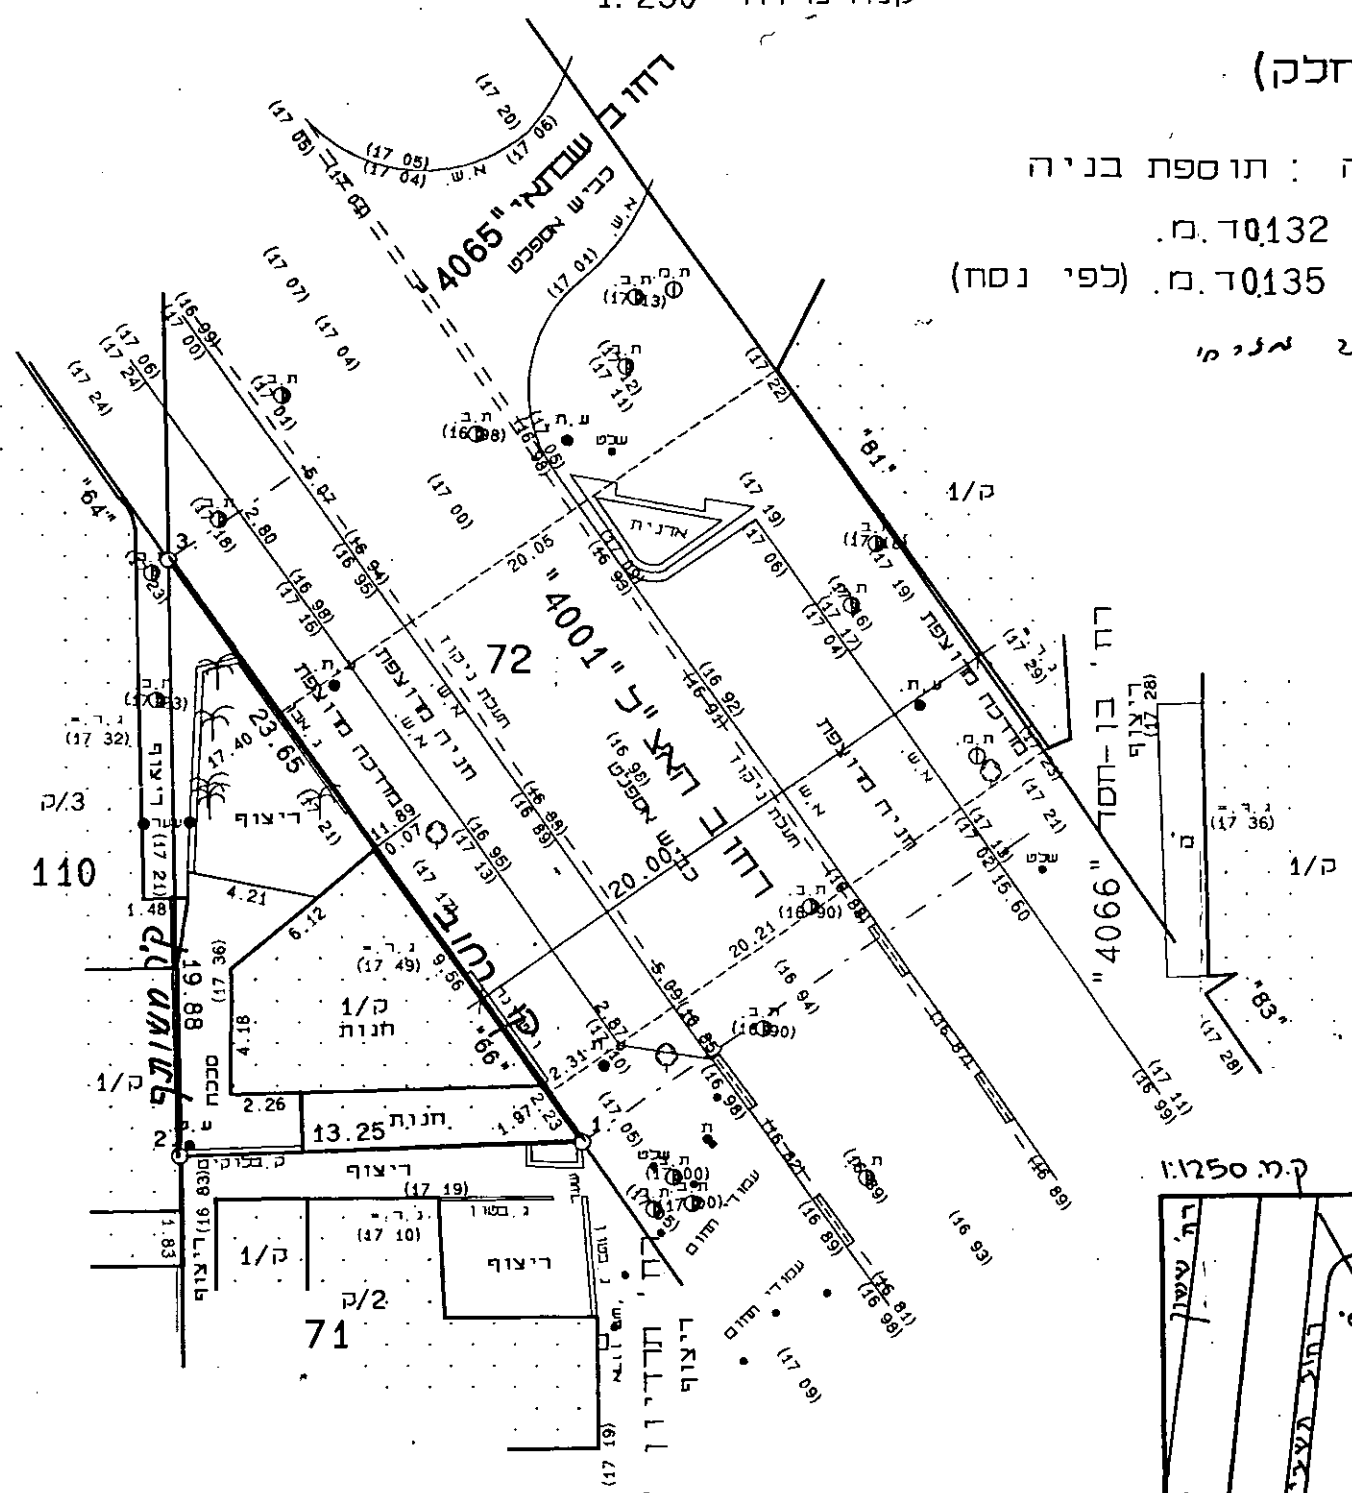

הצהרה
הנני מצהיר בזה שתוכן
נעשה ע"פ התקנות והתנחיות
של עיריית ת"א

תאריך : 9.1.01
מועד מוסבר

ד"ש מדידות בע"מ

דניאל שטרן מודד מוסבר מ.ר. 475
ראש"צ, ברקת 51 טל. 9622524, פקס : 9622569

הערות :
1. הגבהים מבוססים על נ.ק. עירונית 187 שגובהה 17.549 מ'.
2. הגבהים רשומים בסוגריים.
3176-X2.PRJ

עיריית תל אביב-יפו
מחלקת תכנון ותשתית / אגף עבודות ציבוריות
מחלקת מדידות
חתימה _____
חתימה _____
תאריך : 21.01.2001

הפקעה (לצורך חשבוש זכויות בניה)
ת.ב.ע. _____
מ"מ (גרפי) _____
מ"מ (גרפי) _____
מ"מ (גרפי) _____

עיריית תל אביב-יפו / מינהל הנדסה
מחלקת המדידות
אישור כתובת
רחוב : 4001
מס' : 66
רחוב : _____
מס' : _____
רחוב : _____
מס' : _____
תאריך : 11.01.01 חתימה _____

22

18-01-2001

מנהל ההנדסה / אגף תכנון ובנין ערים
מח' שרותי בנין ערים - מדור המידע

הערות למפה טופ' / מצבית

גוש - 6135 חלקה - 71

מס' תיק מידע 107-21

רח' 4001-אצ"ל 66

קווי בנין: צד 1 - 3.00 אחור - 5.00

יעוד בתוקף - מגורים ב שיקום

תכניות בתוקף - ג,ע, 2215, 2215א

תכניות בתכנון - ח

הפקעה

הערות - רחוב 4001- האצ"ל ברוחב 20.0 מ'. קו בנין

2.0 מ'. האזור ב' שיקום עם חזית מסחרית.

קווי בנין לצדדים 3.0 מ' או 0.0 מ' בקיר משותף

ולאחור 5.0 מ'.

שיעור הבניה יהיה 140% משטח המגרש ותכסית הקרקע

לא תעלה על 60%. גובה הבנין 3 קומות.

צפיפות הדיור לפי תכנית 2215 א/1 לפיה נקבע כי

שטח יחיד לא יקטן מ-90 מ"ר כולל ממ"ד, למעט

מקרים בהם הועדה המקומית תהיה רשאית לאשר עד

שתי יחיד לא פחות מ-70 מ"ר כל אחת.

על פי תכנית ג' ניתן לבנות עליית גג בבית צמוד

קרקע וחדר יציאה לגג בשטח של 23 מ"ר ופרגולה

בבנין דירות בתנאים.

מרתף בהיקף הבית לשימוש הדיירים לפי תכנית ע'.

היטל השבחה ייגבה בגין חזית מסחרית.

עיריית תל-אביב-יפו

טוביה שלום

ממונת תשתיות ומקרקעין

אגף תכנון ובנין ערים

חתימה

מנהל מדור המידע
עיריית תל-אביב-יפו
מנהל מדור המידע
חתימה
מנהל מדור המידע
עיריית תל-אביב-יפו

16-01-2001

15.01.01