
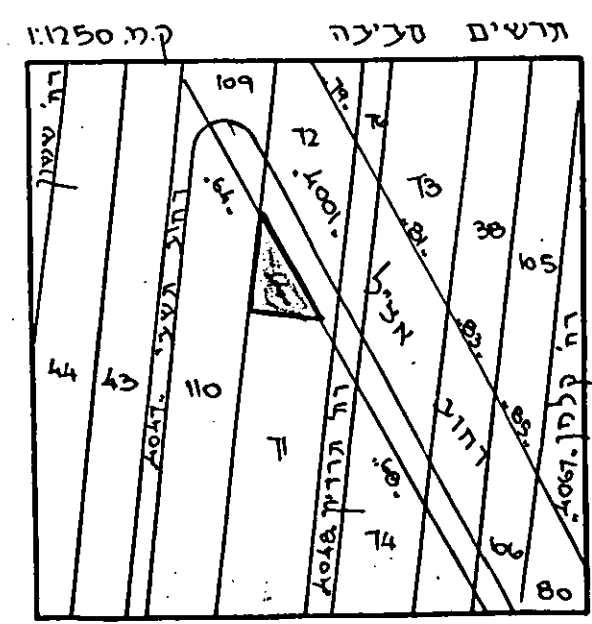


d/210107

תל אביב
גוש : 6135
חלקה : 71 (חלק)

מפה טופוגרפית
קנה מידה 1:250

מהות הבקשה : תוספת בניה
שטח מדוד : 132.00 מ.
שטח רשום : 135.00 מ. (כפי נסח)
יום ציור האדמה : 1971

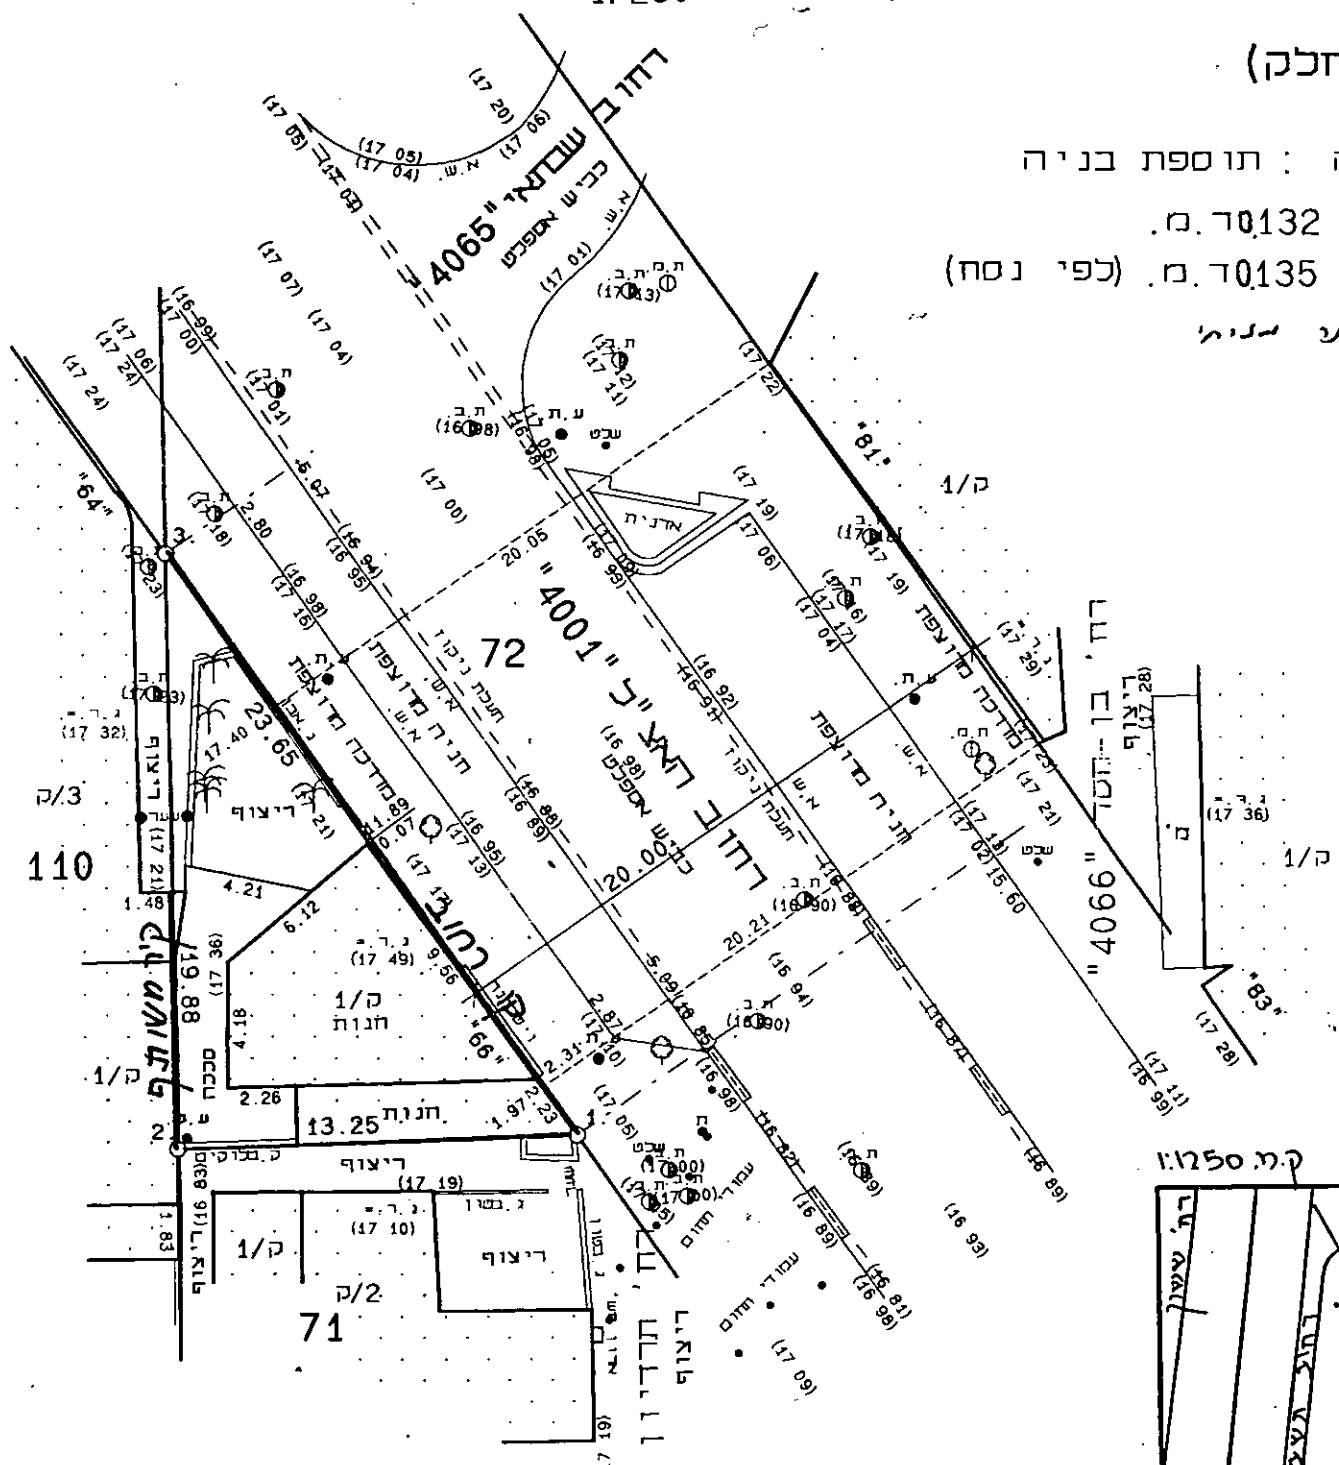

עיריית תל אביב - יפו
מחלקת ביוני ותשתית / אגף עבודות ציבוריות
מחלקת מדידות
חתימה _____
חתימה _____
תאריך: 21.01.2001

שטח הפקעה (לצורך חשוב זכויות בניה)
שטח (ת.ב.ע.) _____ מ"מ (גרפי)
שטח (ת.ב.ע.) _____ מ"מ (גרפי)
שטח (ת.ב.ע.) _____ מ"מ (גרפי)

עיריית תל אביב - יפו / מינהל הנדסה
מחלקת המדידות
אישור כתובת
רחוב: _____ מס': _____
רחוב: _____ מס': _____
תאריך: 11.01.01 חתימה: _____

הצוהר:
הנני מצהיר בזה שתוכן
נעשה ע"פ החקנות וההנחיות
של עיריית ת"א
תאריך: 9.1.01 מודד מוסמך
ד"ש מדידות בע"מ
דניאל שטרן מודד מוסמך מ.ר. 475
ראש"צ, ברקת 51 טל. 9622524, פקס: 9622569

הערות:
1. הגבהים מבוססים על נ.ק. עירונית 187 שגובהה 17.549 מ'.
2. הגבהים רשומים בסוגריים.
3176-X2.PRJ

מנהל ההנדסה / אגף תכנון ובנין ערים
מח' שרותי בנין ערים - מדור המידע

הערות למפה טופ' / מצבית

גוש - 6135 חלקה - 71

מס' תיק מידע 107-21

רח' 4001-אצ"ל 66

קווי בנין: צד 1 - 3.00 אחור - 5.00

יעוד בתוקף - מגורים ב שיקום

תכניות בתוקף - ג, ע, 2215, 2215א

תכניות בתכנון - ח

הפקעה

הערות - רחוב 4001-האצ"ל ברוחב 20.0 מ'. קו בנין

2.0 מ'. האזור ב' שיקום עם חזית מסחרית.

קו בנין לצדדים 3.0 מ' או 0.0 מ' בקיר משותף

ולאחור 5.0 מ'.

שיעור הבניה יהיה 140% משטח המגרש ותכסית הקרקע

לא תעלה על 60%. גובה הבנין 3 קומות.

צפיפות הדיור לפי תכנית 2215 א/1 לפיה נקבע כי

שטח יחיד לא יקטן מ-90 מ"ר כולל ממ"ד, למעט

מקרים בהם הועדה המקומית תהיה רשאית לאשר עד

שתי יחיד לא פחות מ-70 מ"ר כל אחת.

על פי תכנית ג' ניתן לבנות עליית גג בבית צמוד

קרקע וחדר יציאה לגג בשטח של 23 מ"ר ופרגולה

בבנין דירות בתנאים.

מרתף בהיקף הבית לשימוש הדיירים לפי תכנית ע'.

היטל השבחה ייגבה בגין חזית מסחרית.

עיריית תל-אביב-יפו
טובה שלום
ממונה חזיתות ומקרקעין
אגף תכנון ובנין ערים

חתימה

חתימה

16-01-2001

אסתר חזן
מנהלת מדור המידע
עיריית תל-אביב-יפו

15.1.01