

27-18-01-2001

מנהל ההנדסה / אגף תכנון ובנין ערים
מח' שרותי בנין ערים - מדור המידע

איכות גמורה

הערות למפה טופ' / מצבית

גוש - 6135 חלקה - 71

מס' תיק מידע 107-21

רח' 4001-אצ"ל 66

קווי בנין: צד 1 - 3.00 אחר - 5.00

יעוד בתוקף - מגורים ב שיקום

תכניות בתוקף - ג, ע, 2215, 2215א

תכניות בתכנון - ח

הפקעה

הערות - רחוב 4001-האצ"ל ברוחב 20.0 מ'. קו בנין

2.0 מ'. האזור ב' שיקום עם חזית מסחרית.

קו בנין לצדדים 3.0 מ' או 0.0 מ' בקיר משותף

ולאחר 5.0 מ'.

שיעור הבניה יהיה 140% משטח המגרש ותכנית הקרקע

לא תעלה על 60%. גובה בנין 3 קומות.

צפיפות הדיור לפי תכנית 2215 א/1 לפיה נקבע כי

שטח יחיד לא יקטן מ-90 מ"ר כולל ממ"ד, למעט

מקרים בהם הועדה המקומית תהיה רשאית לאשר עד

שתי יחיד לא פחות מ-70 מ"ר כל אחת.

על פי תכנית ג' ניתן לבנות עליית גג בבית צמוד

קרקע וחדר יציאה לגג בשטח של 23 מ"ר ופרגולה

בבנין דירות בתנאים.

מרתף בהיקף הבית לשימוש הדיירים לפי תכנית ע'.

היטל השבחה ייגבה בגין חזית מסחרית.

עיריית תל-אביב-יפו
טוביה שלום
ממונה על שטחים ומקרקעין
אגף תכנון ובנין ערים

חתימה

חתימה

16-01-2001

אסתר חזן
מנהלת מדור המידע
עיריית תל-אביב-יפו
מנהל מדור המידע



15.1.01

210107

תל אביב
גוש : 6135
חלקה : 71 (חלק)

מפה טופוגרפית
קנה מידה 1:250

מהות הבקשה : תוספת בניה
שטח מדוד : 0.132 ד.מ.
שטח רשום : 0.135 ד.מ. (כפי נסח)
הוכן ציור י. אבן-אליה

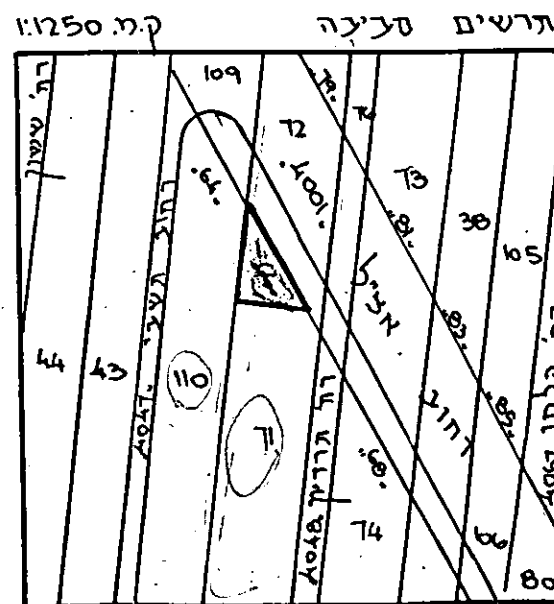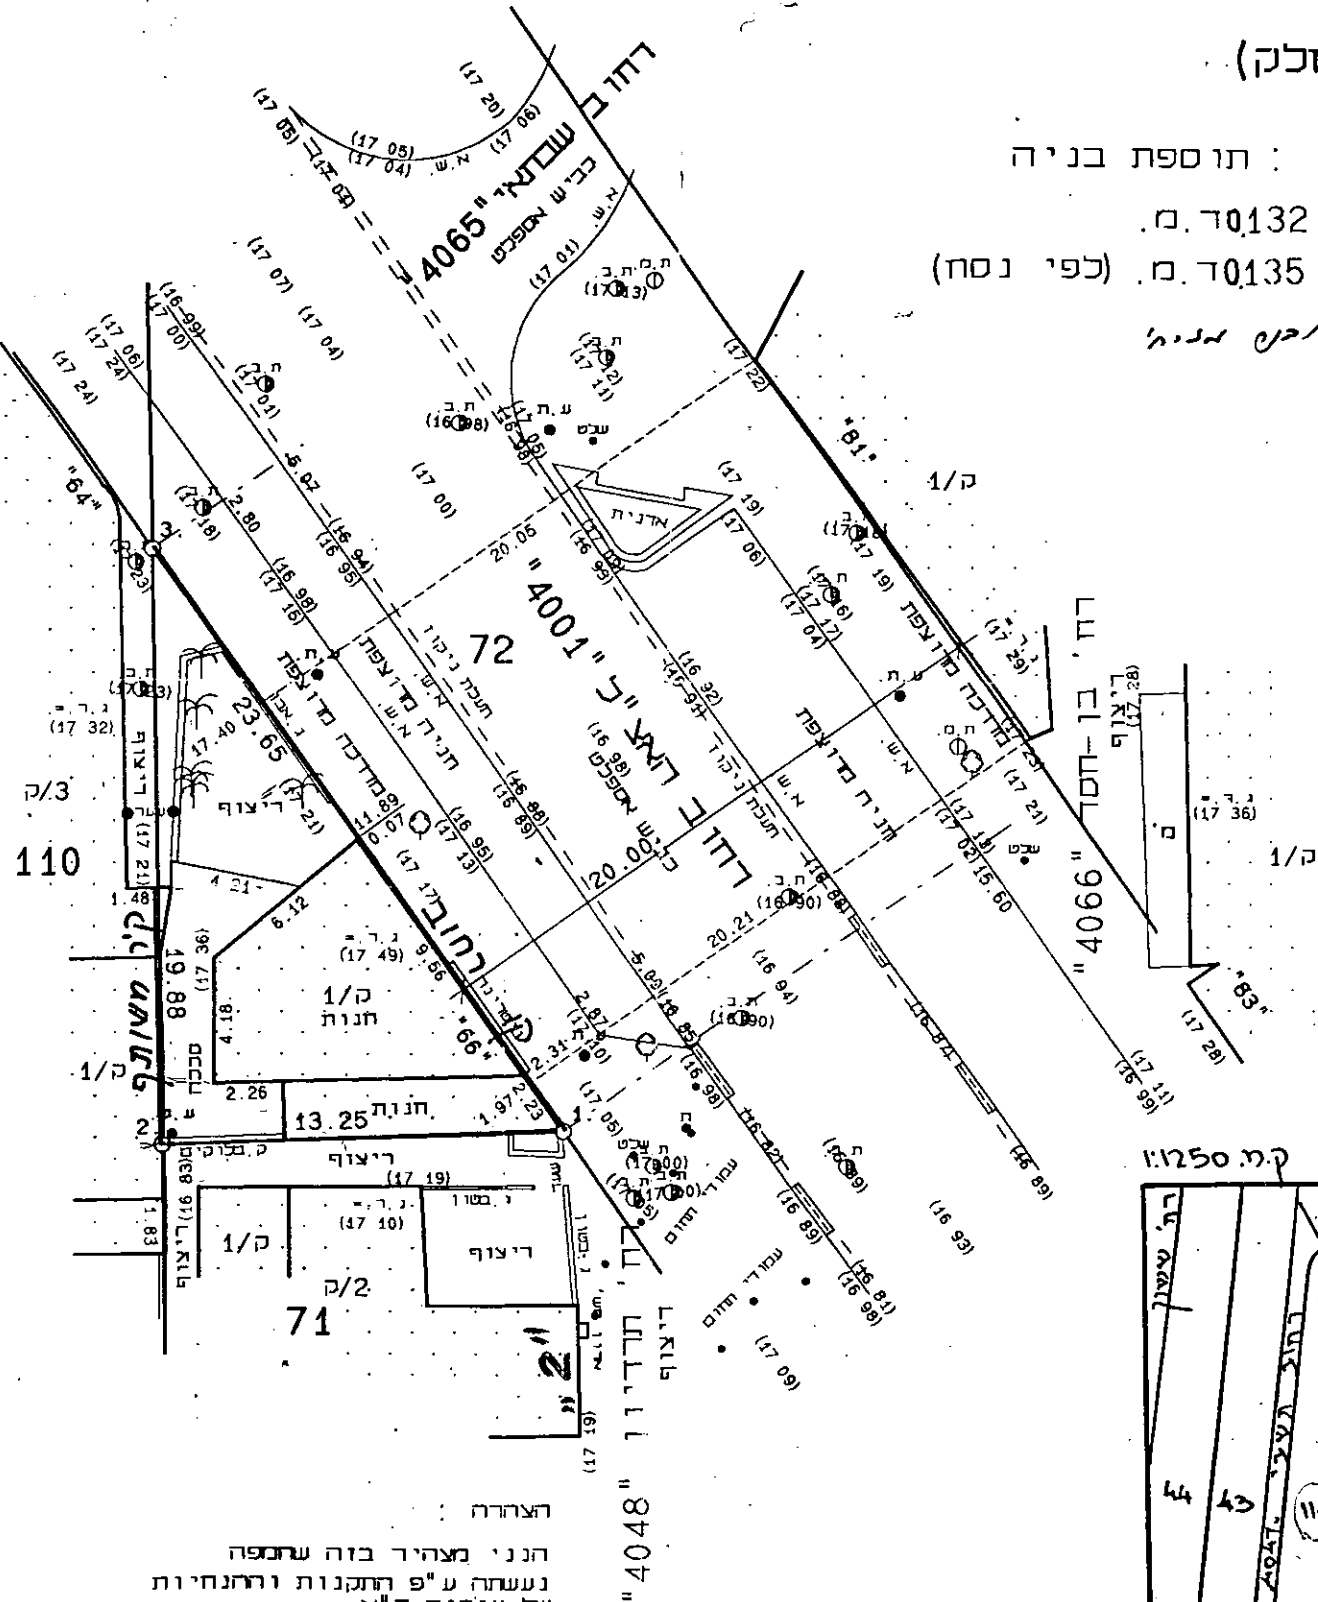

תאריך : 9.1.01 מודד מוסמך
ד"ר ש' מדידות בע"מ
דניאל שטרן מודד מוסמך מ.ר. 475
ראש"צ, ברקת 51 טכ. 9622524, פקס : 9622569

עיריית תל-אביב-יפו
מחלקת ביוני ותשתית / אגף עבודות ציבוריות
מחלקת מדידות
חתימה
חתימה
תאריך 21.01.2001

שטח הפקעה (לצורך חשוב זכויות בניה)
מאושר (ת.ב.ע.) מ"מ (גרפי)
י"א (ת.ב.ע.) מ"מ (גרפי)
שטח המדידה הוכן לפי תכנית להגדרת רשות

עיריית תל-אביב-יפו / מינהל הנדסה
מחלקת המדידות
אישור כתובת
רחוב אצ"ל מס' 66
רחוב
רחוב
תאריך 11.01.01 חתימה

הערות :
1. הגבהים מבוססים על נ.ק. עירונית 187 שגובהה 17.549 מ'.
2. הגבהים רשומים בסוגריים
3176-X2.PRJ