


חפה טופוגרפית
ק"מ 1:250

סינווא

תל-אביב

גוש: 6135
חלקה: 44 (חלק)
שטח: 0.065 ד"מ (מדוד)
מהות הבקשה: היתר בניה

מוכן עבור: סניף דוד

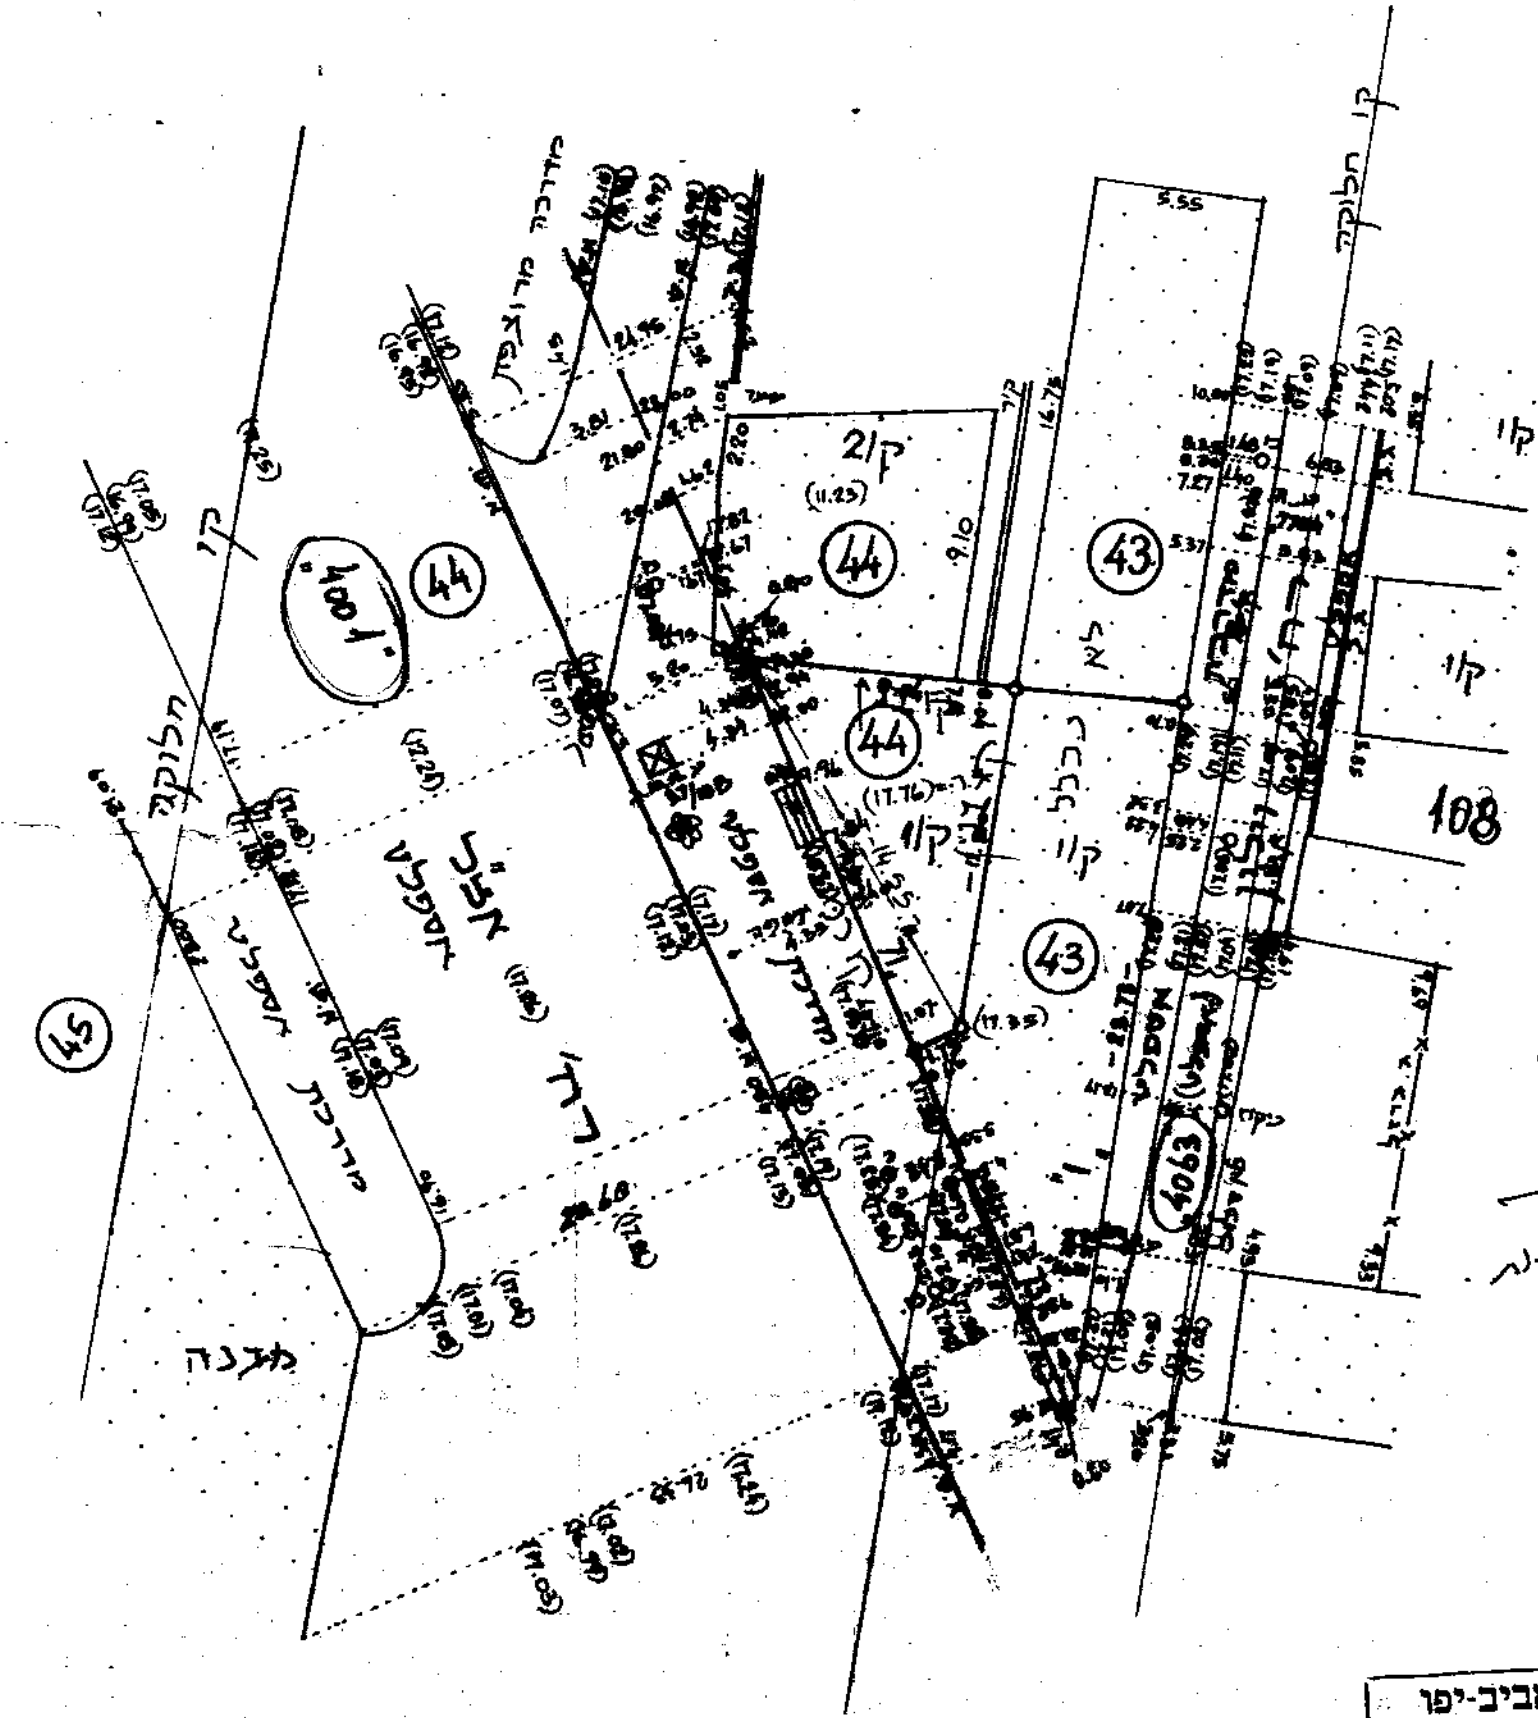

חולת מ' ביבם
לפי רשיון א"מ - (18.67)
במסגרת השטח המיועד
בין חולת
לפי אקולוגיה ב"ר - א"מ
בשטח המיועד הצמוד

עיריית תל-אביב-יפו
מנהל הנדסה / אגף תכנון ובנין ערים
מחלקת מידע - מדור המידע

המפה נכרה בסמל:
דרכים ☒
מים ☒
ביוב ☒
הנחיות צוות ☒
אנשים ☒
תניה ☒
נחית אישון ☒
מדידת כחן ☒
חתימה ☒
תאריך ☒

מנהל הנדסה / אגף תכנון ובנין ערים
מח' שרותי בנין ערים - מדור המידע

הערות למפה טופ' / מצבית

גוש - 6135	חלקה - 44
מס' תיק מידע	1643-92
רח' 3671-לוד	31
רח' 4001-אצ"ל	58-60
רח' 4001-אצ"ל	69
רח' 4046-ששון	
רח' 4062-אביטל	
רח' 4064-מושיע	6-8


יעוד בתוקף - אזור מגורים ב
תכנית בתוקף - 2215
הערות - רחוב 4001-אצ"ל ברוחב 20 מ', קו בנין 0-2 מ'
מצטרף לרחוב קו בנין צדדיים 0.
קו בנין אחורי 5 מ'. גובה הבנין 3 קומות.
אחוזי הבניה הכוללים 140%, תכנית קרקע מירבית
60% מרתף לפי תכנית ע'.
הצפיפות 10 דירות לדונם.
אין לגבות היטל השבחה היות והשבחה הוכרזה
כשכונת שקום. הסדר המגרש יעשה במסגרת הסדר כללי
של השכונה.
יש לתאם את התכנון עם צוות מזרח באגף תב"ע.
נא לא לבצע שינויים במסמך

חתימה
2.11.93
חתימה
2.11.93
חתימה
2.11.93
מנהל מדור המידע
2.11.93

עיריית תל-אביב-יפו / מנהל הנדסה
מחלקת המדידות
אישור כתובת
רחוב אצ"ל מס' 71
רחוב מס'
רחוב מס'
רחוב מס'
תאריך 3.11.93 חתימה

תנאים סביבה 1:250

עיריית תל-אביב-יפו
מחלקת הכיב והתעול
(מידע מוקדם)
בנין סופו
תעול
תעול
תעול
תעול
תאריך 8.11.93 חתימה

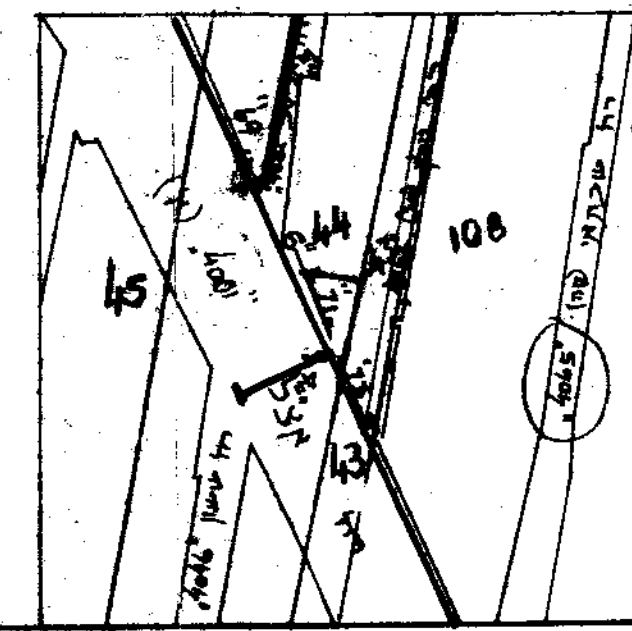

עיריית תל-אביב-יפו
מנהל בנין ותשתית / אגף עבודות ציבוריות
מחלקת מדידות
חתימה
חתימה
חתימה
חתימה
תאריך 3.11.93

שטח הפקעה (לצורך חשבון זכויות בניה)
מאושר (תב"ע) () מ"מ (גרפי)
מוצע (תב"ע) () מ"מ (גרפי)
השטח הפקעה שיהיה יקבע במסגרת הצרכי רשות
נא לא לבצע שינויים במסמך

נסרק

לא לצרכי דישום
הנני מצהיר שהמפה נעשתה לפי חוק המדידה והבנין
התקנות וההנחיות של עיריית תל-אביב-יפו.
בבעתים 4.6.93
ש. הכפר מודד מוטמן מר. 484
כחוב המעלות 12, ובעתים, טל' 4322/3-03

הערות:
1. המסמך נסוויים עם נבחנים
2. הנבונים פנוסטים על נק' 157 = 17.549
3. לא נמצא רישום בטאב