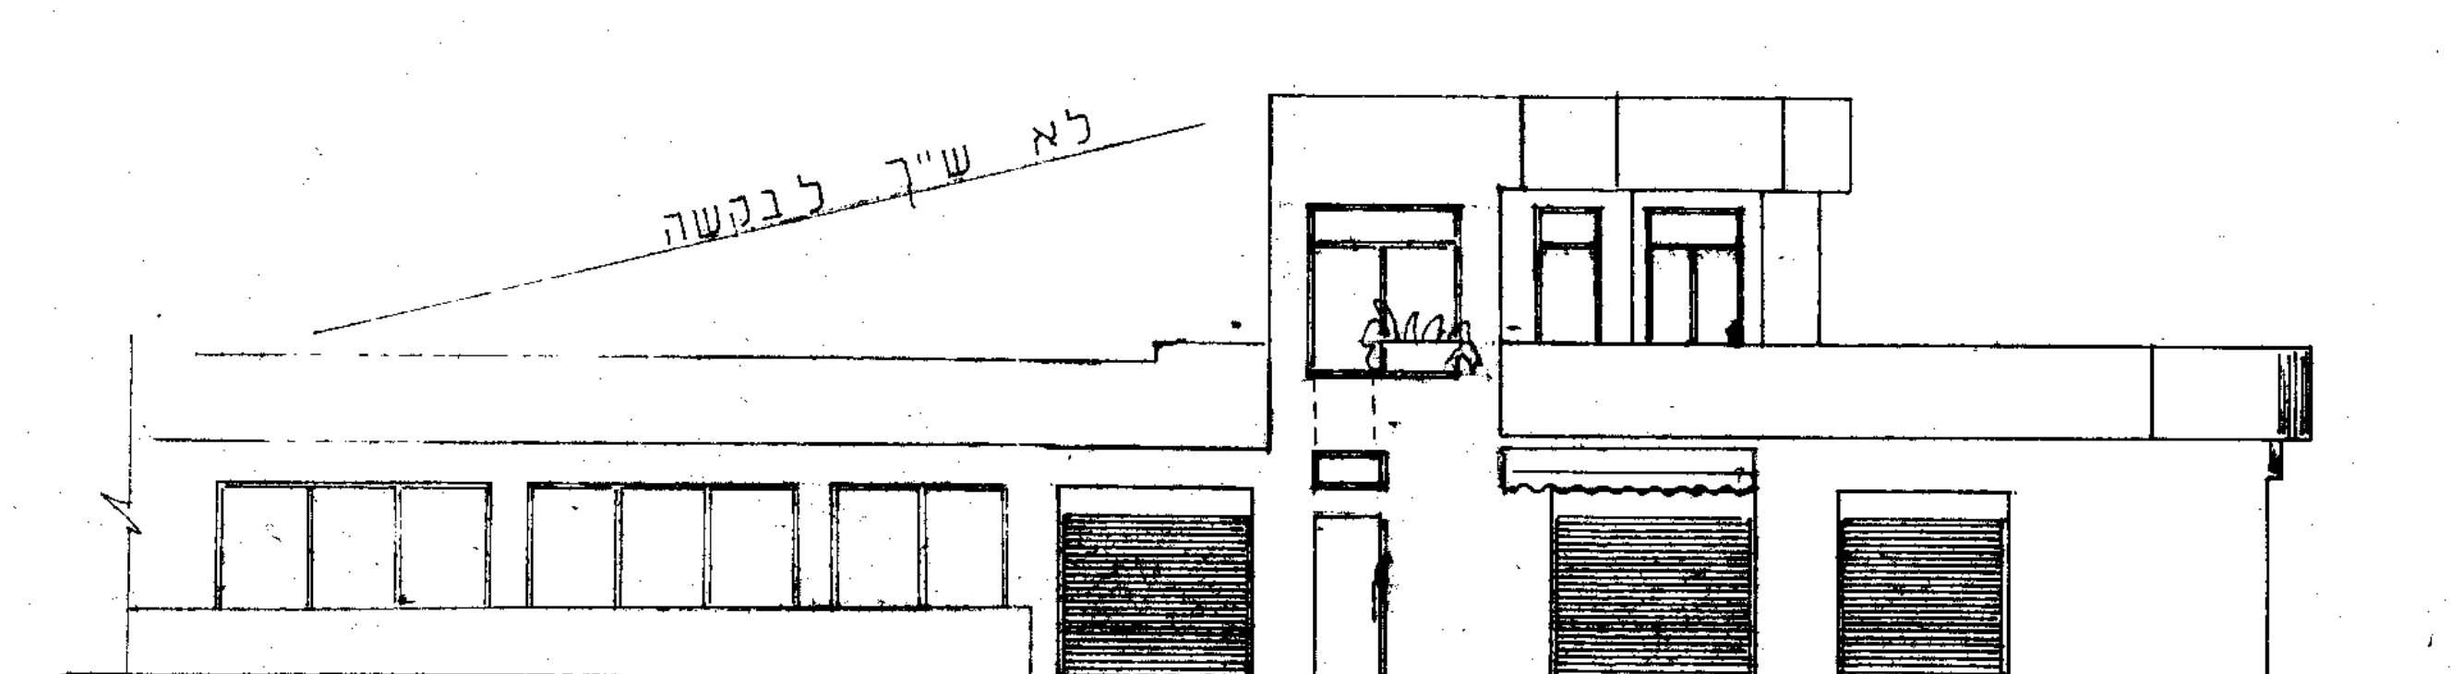
לא שייך לבקשה
+7.80
+6.50
+4.50
+3.50
+3.20
±0.00

חזית מרחוב אצ"ל 1:100

גמר טיח אקרילי
בגוון בהיר
(כולל קירות משותפים)

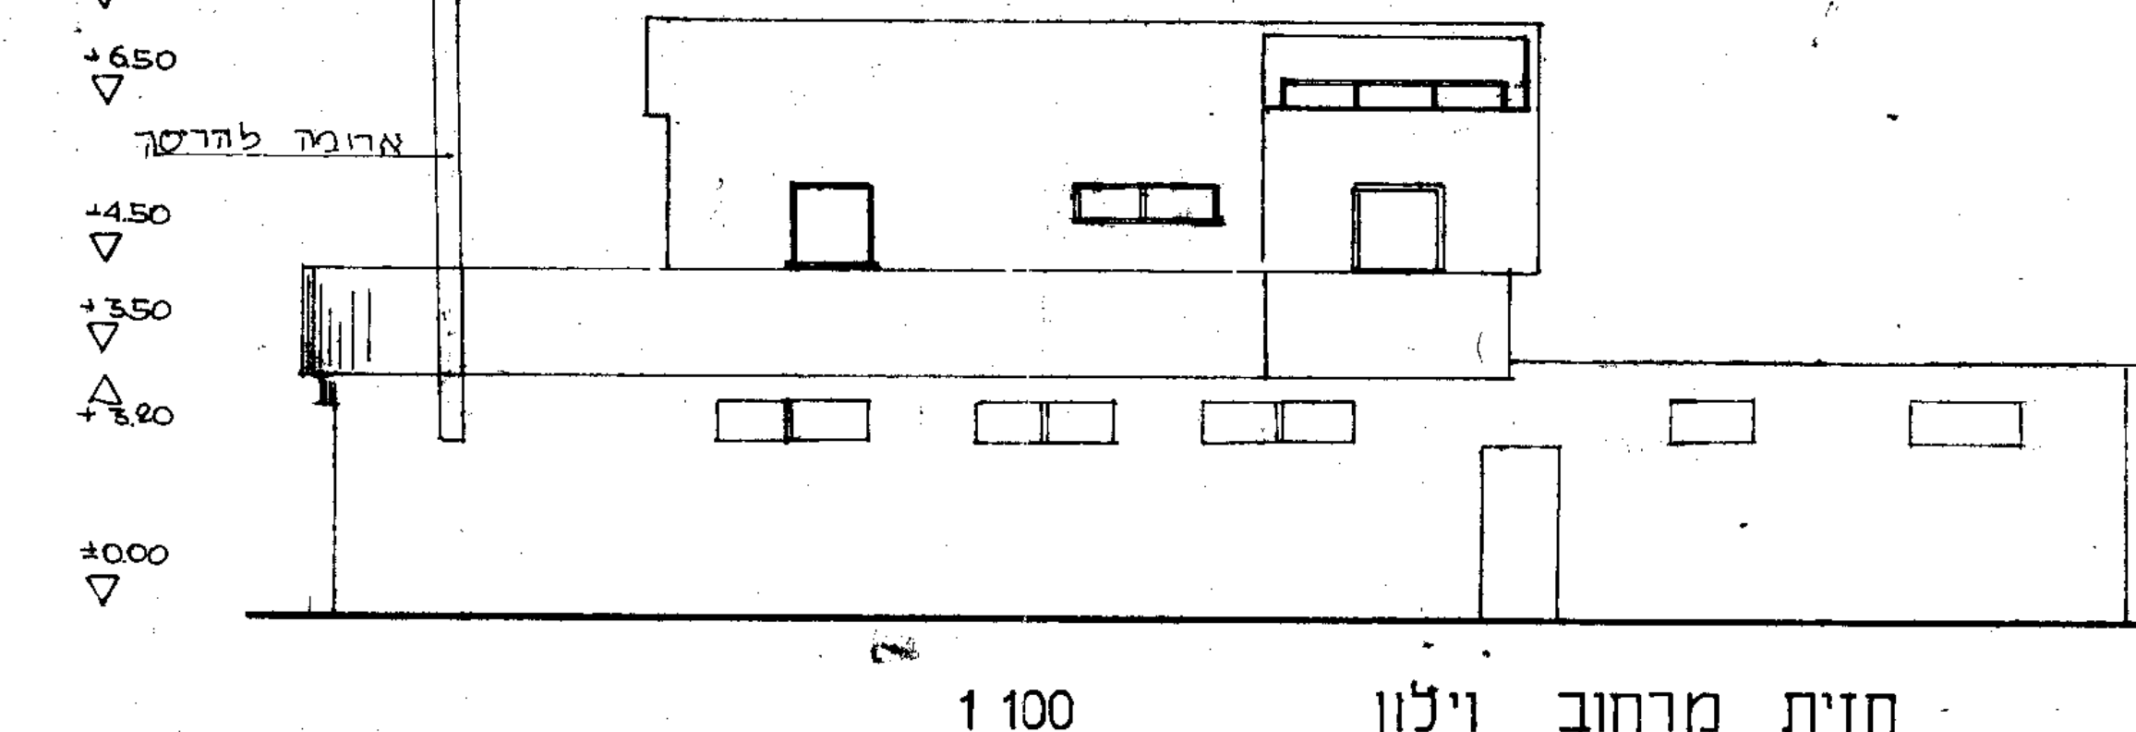
ארובה להריסה
+7.80
+6.50
+4.50
+3.50
+3.20
±0.00

גמר: טיח אקרילי
בגוון בהיר
(כולל קירות)

חזית מרחוב וילון 1:100

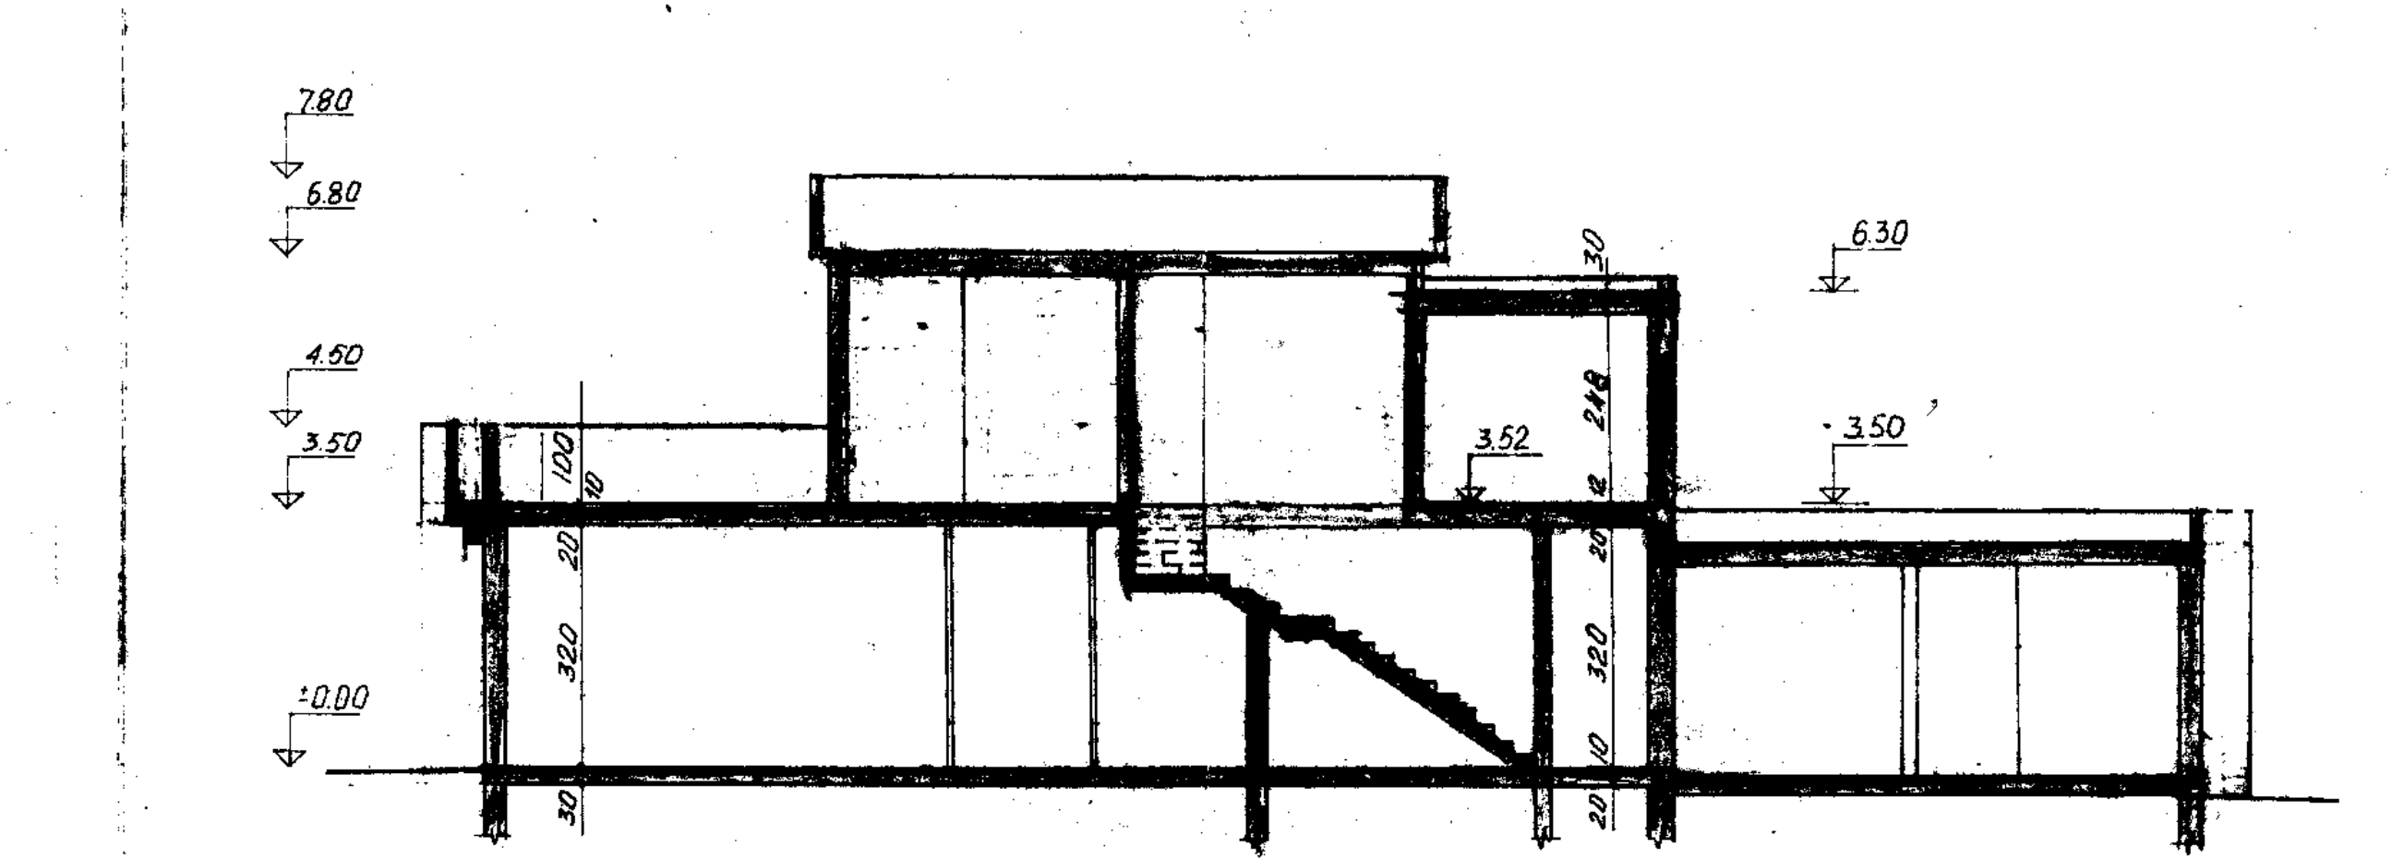
7.80
6.80
6.30
4.50
3.50
3.52
3.40
3.00
±0.00
-0.18

חתך א-א 1:100

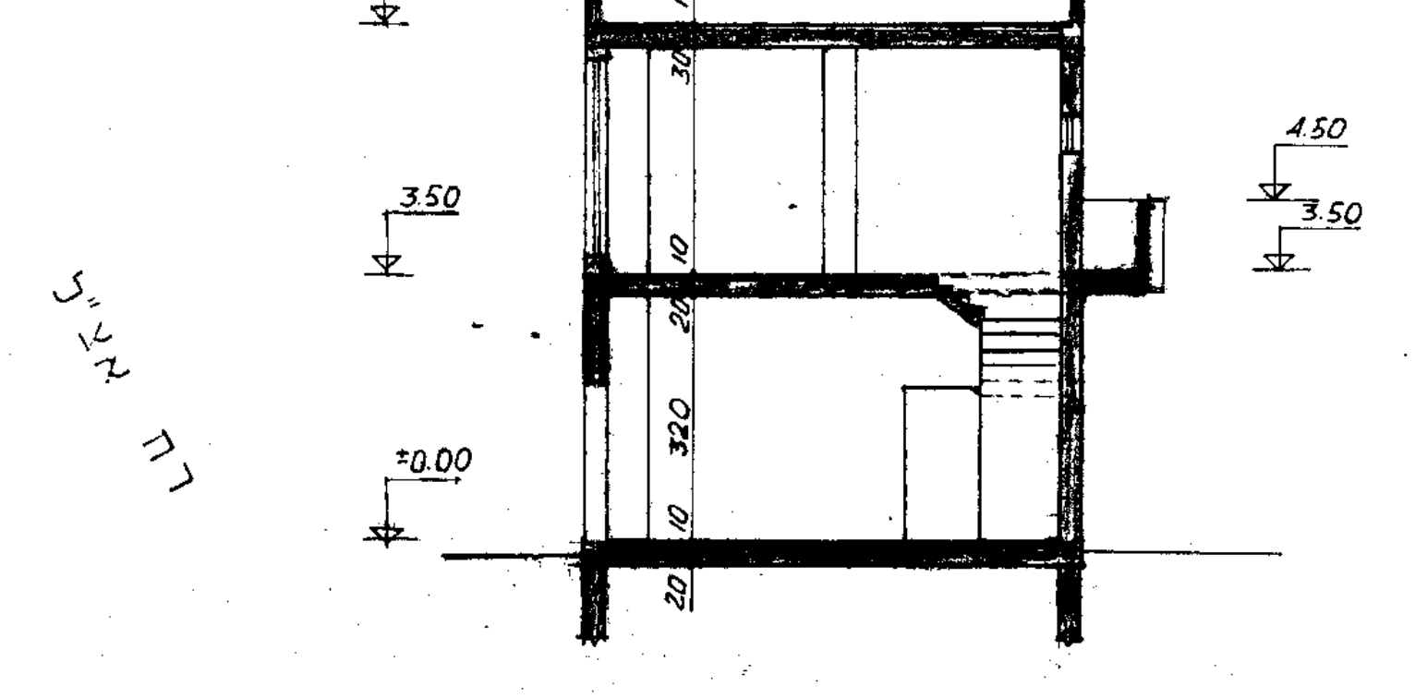
7.80
6.80
4.50
3.50
±0.00

חתך ב-ב 1:100

רח' וילון
רח' אצ"ל

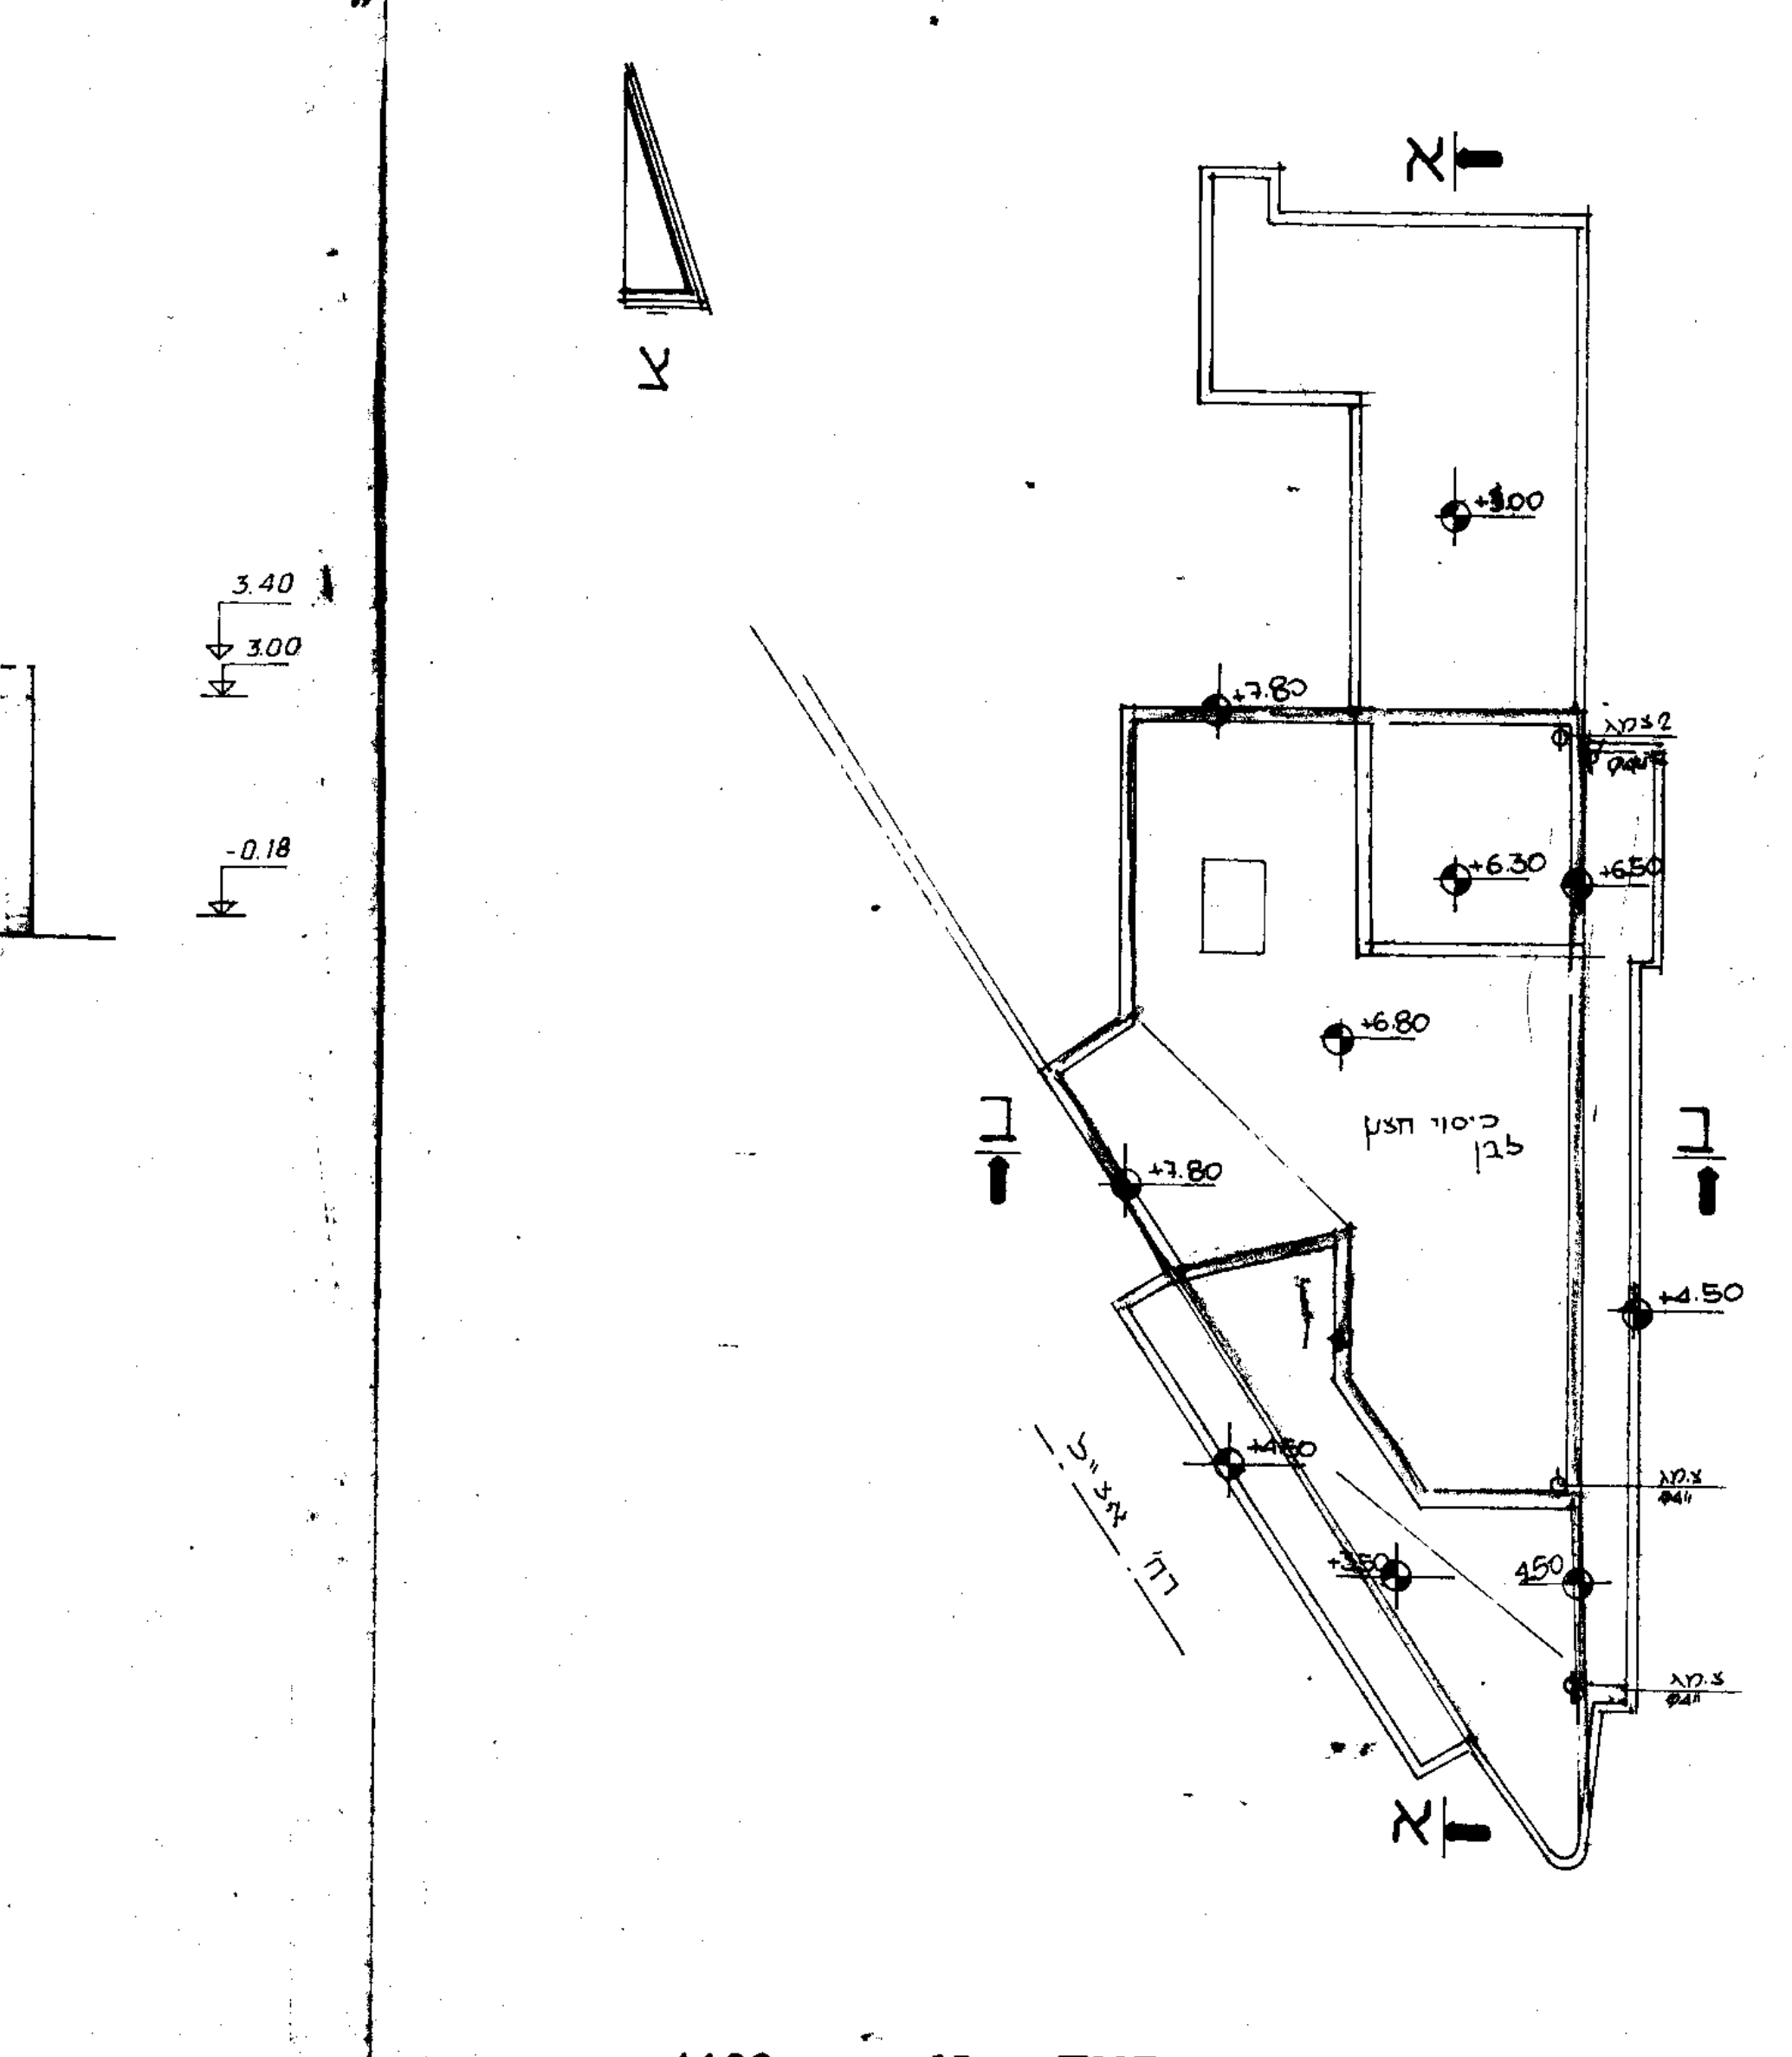
א
ב
ב
צ
+8.00
+7.80
+6.30
+6.80
+4.50
כיסוי חצץ לבן
רח' וילון
רח' אצ"ל

תכנית גג 1:100

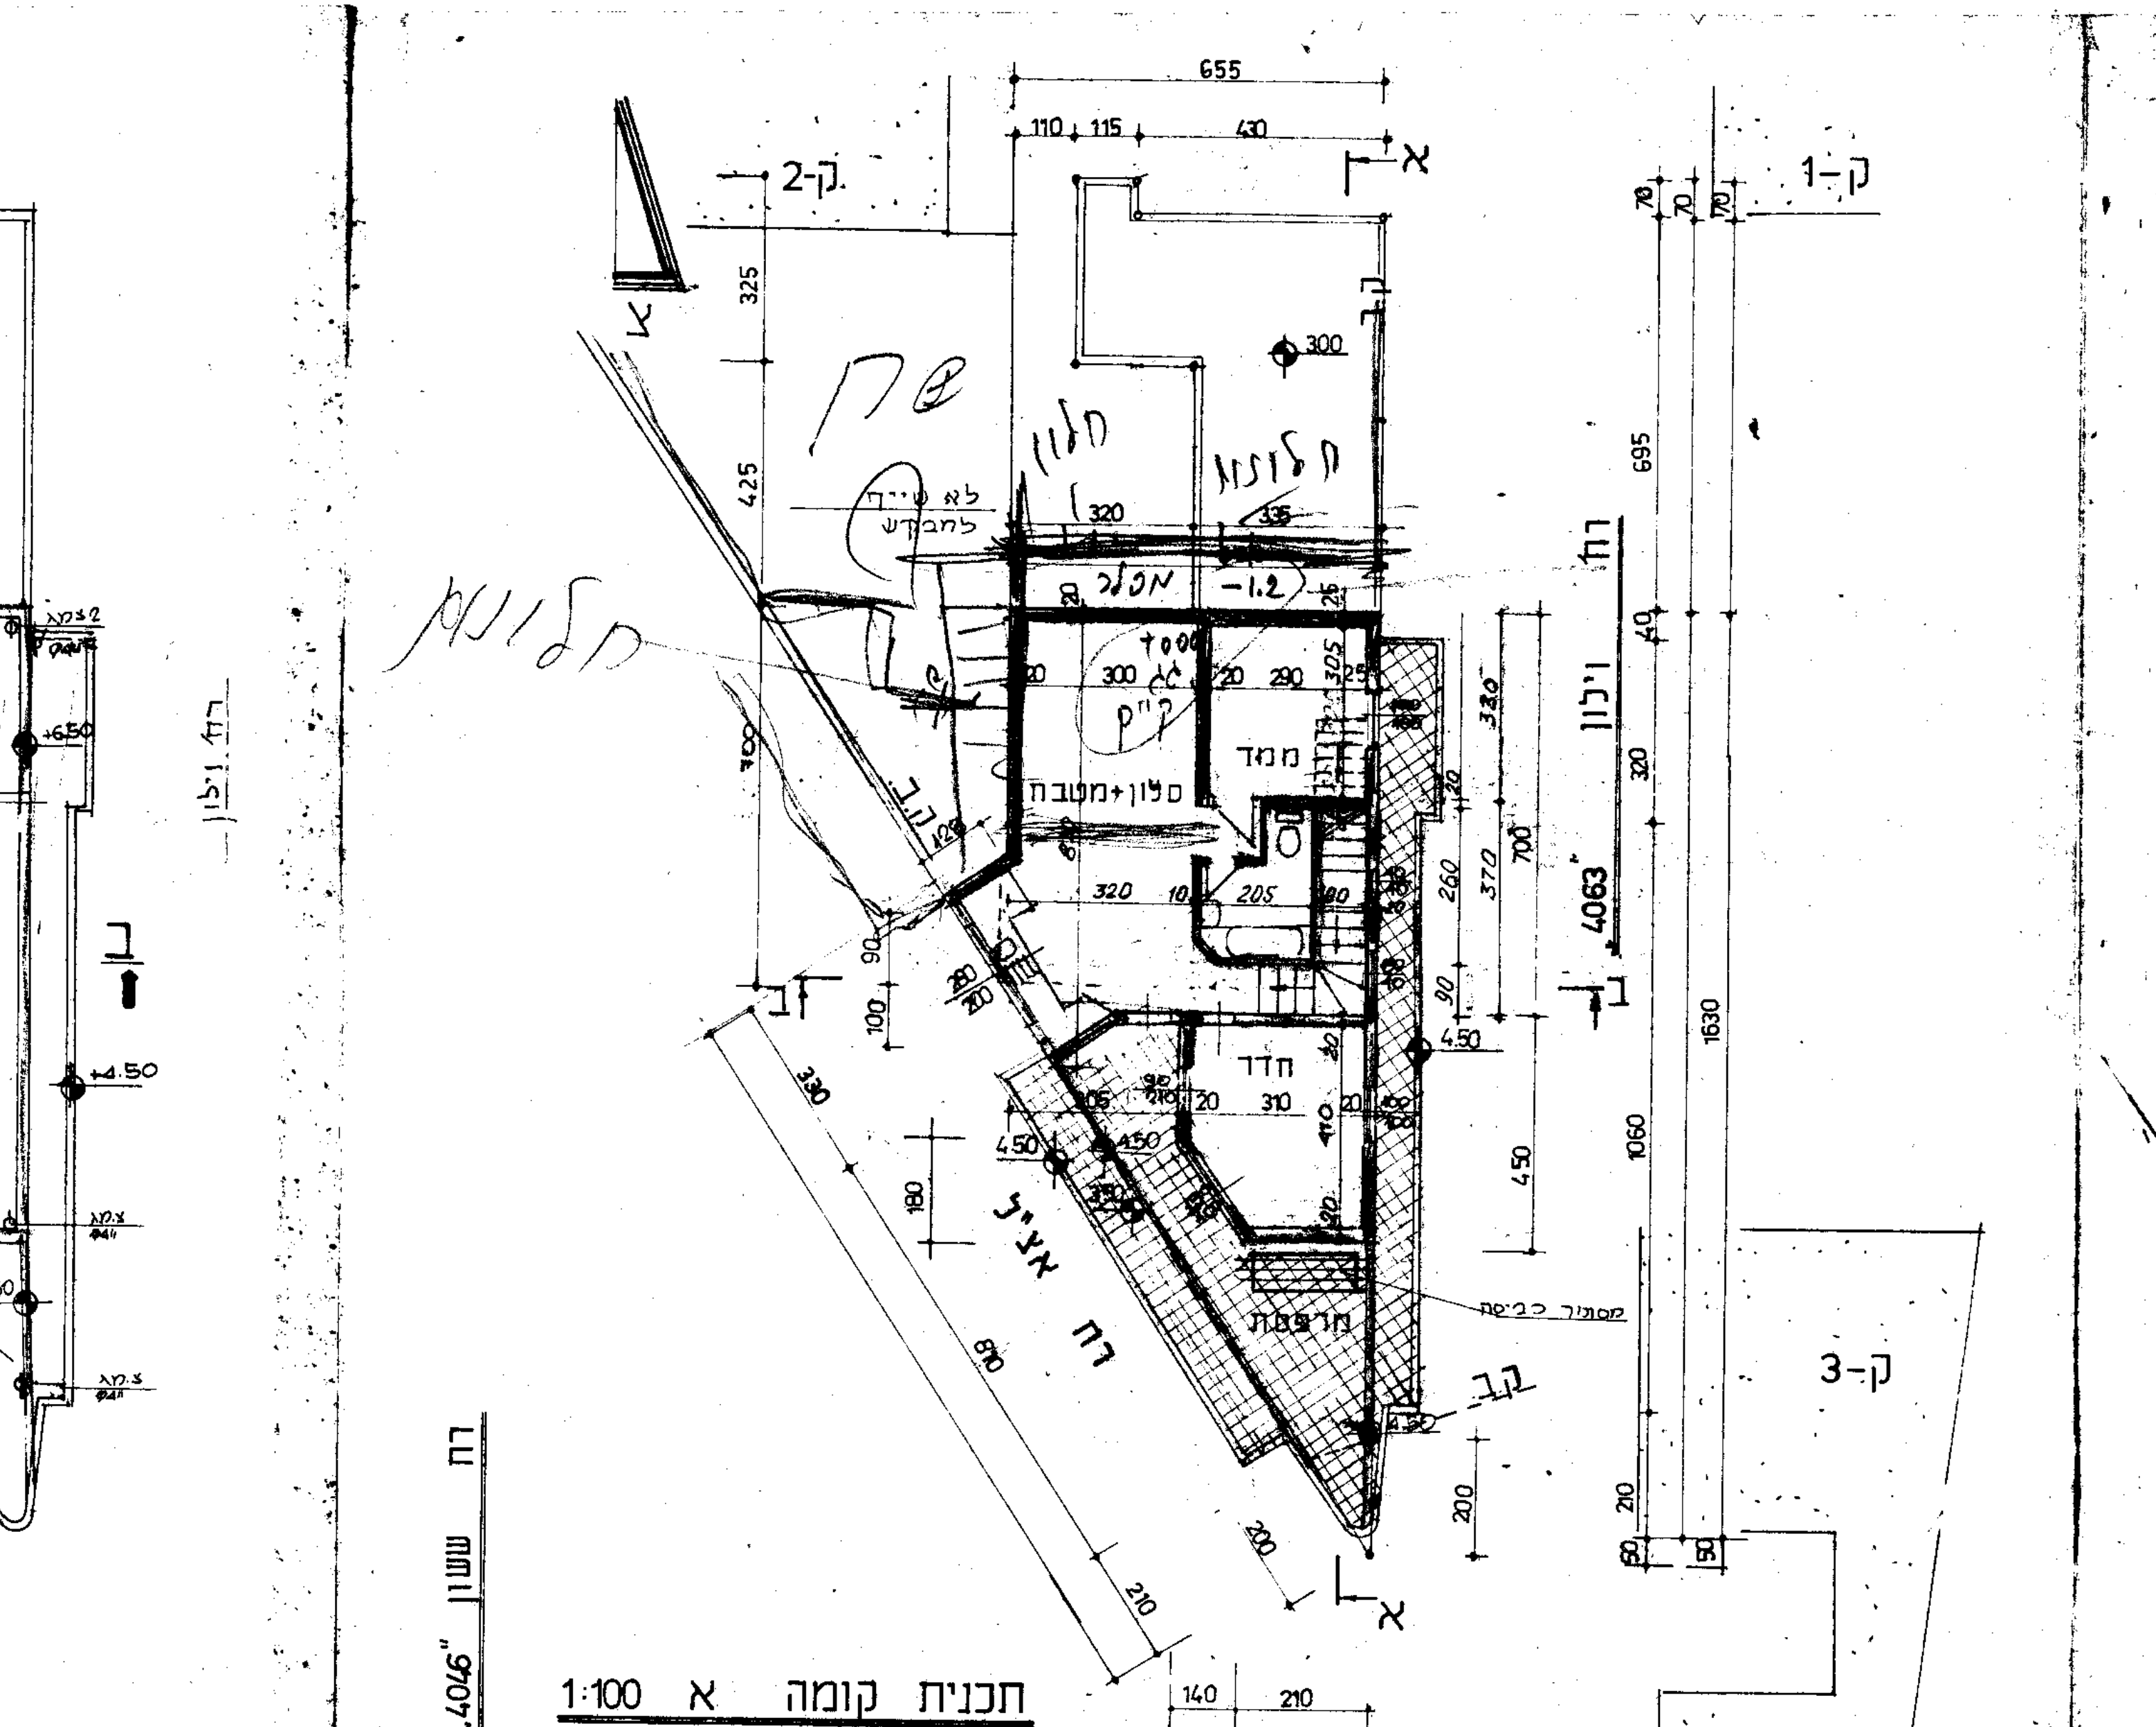
655
110 115 430
ק-2
א
צ
ממ"ד
חלון
חלונות
לא שייך לבקשה
מעקה
סלון+מטבח
חדר
מרפסת
רח' וילון
רח' אצ"ל
רח' ששון
4063
4046
140 210
350

תכנית קומה א 1:100

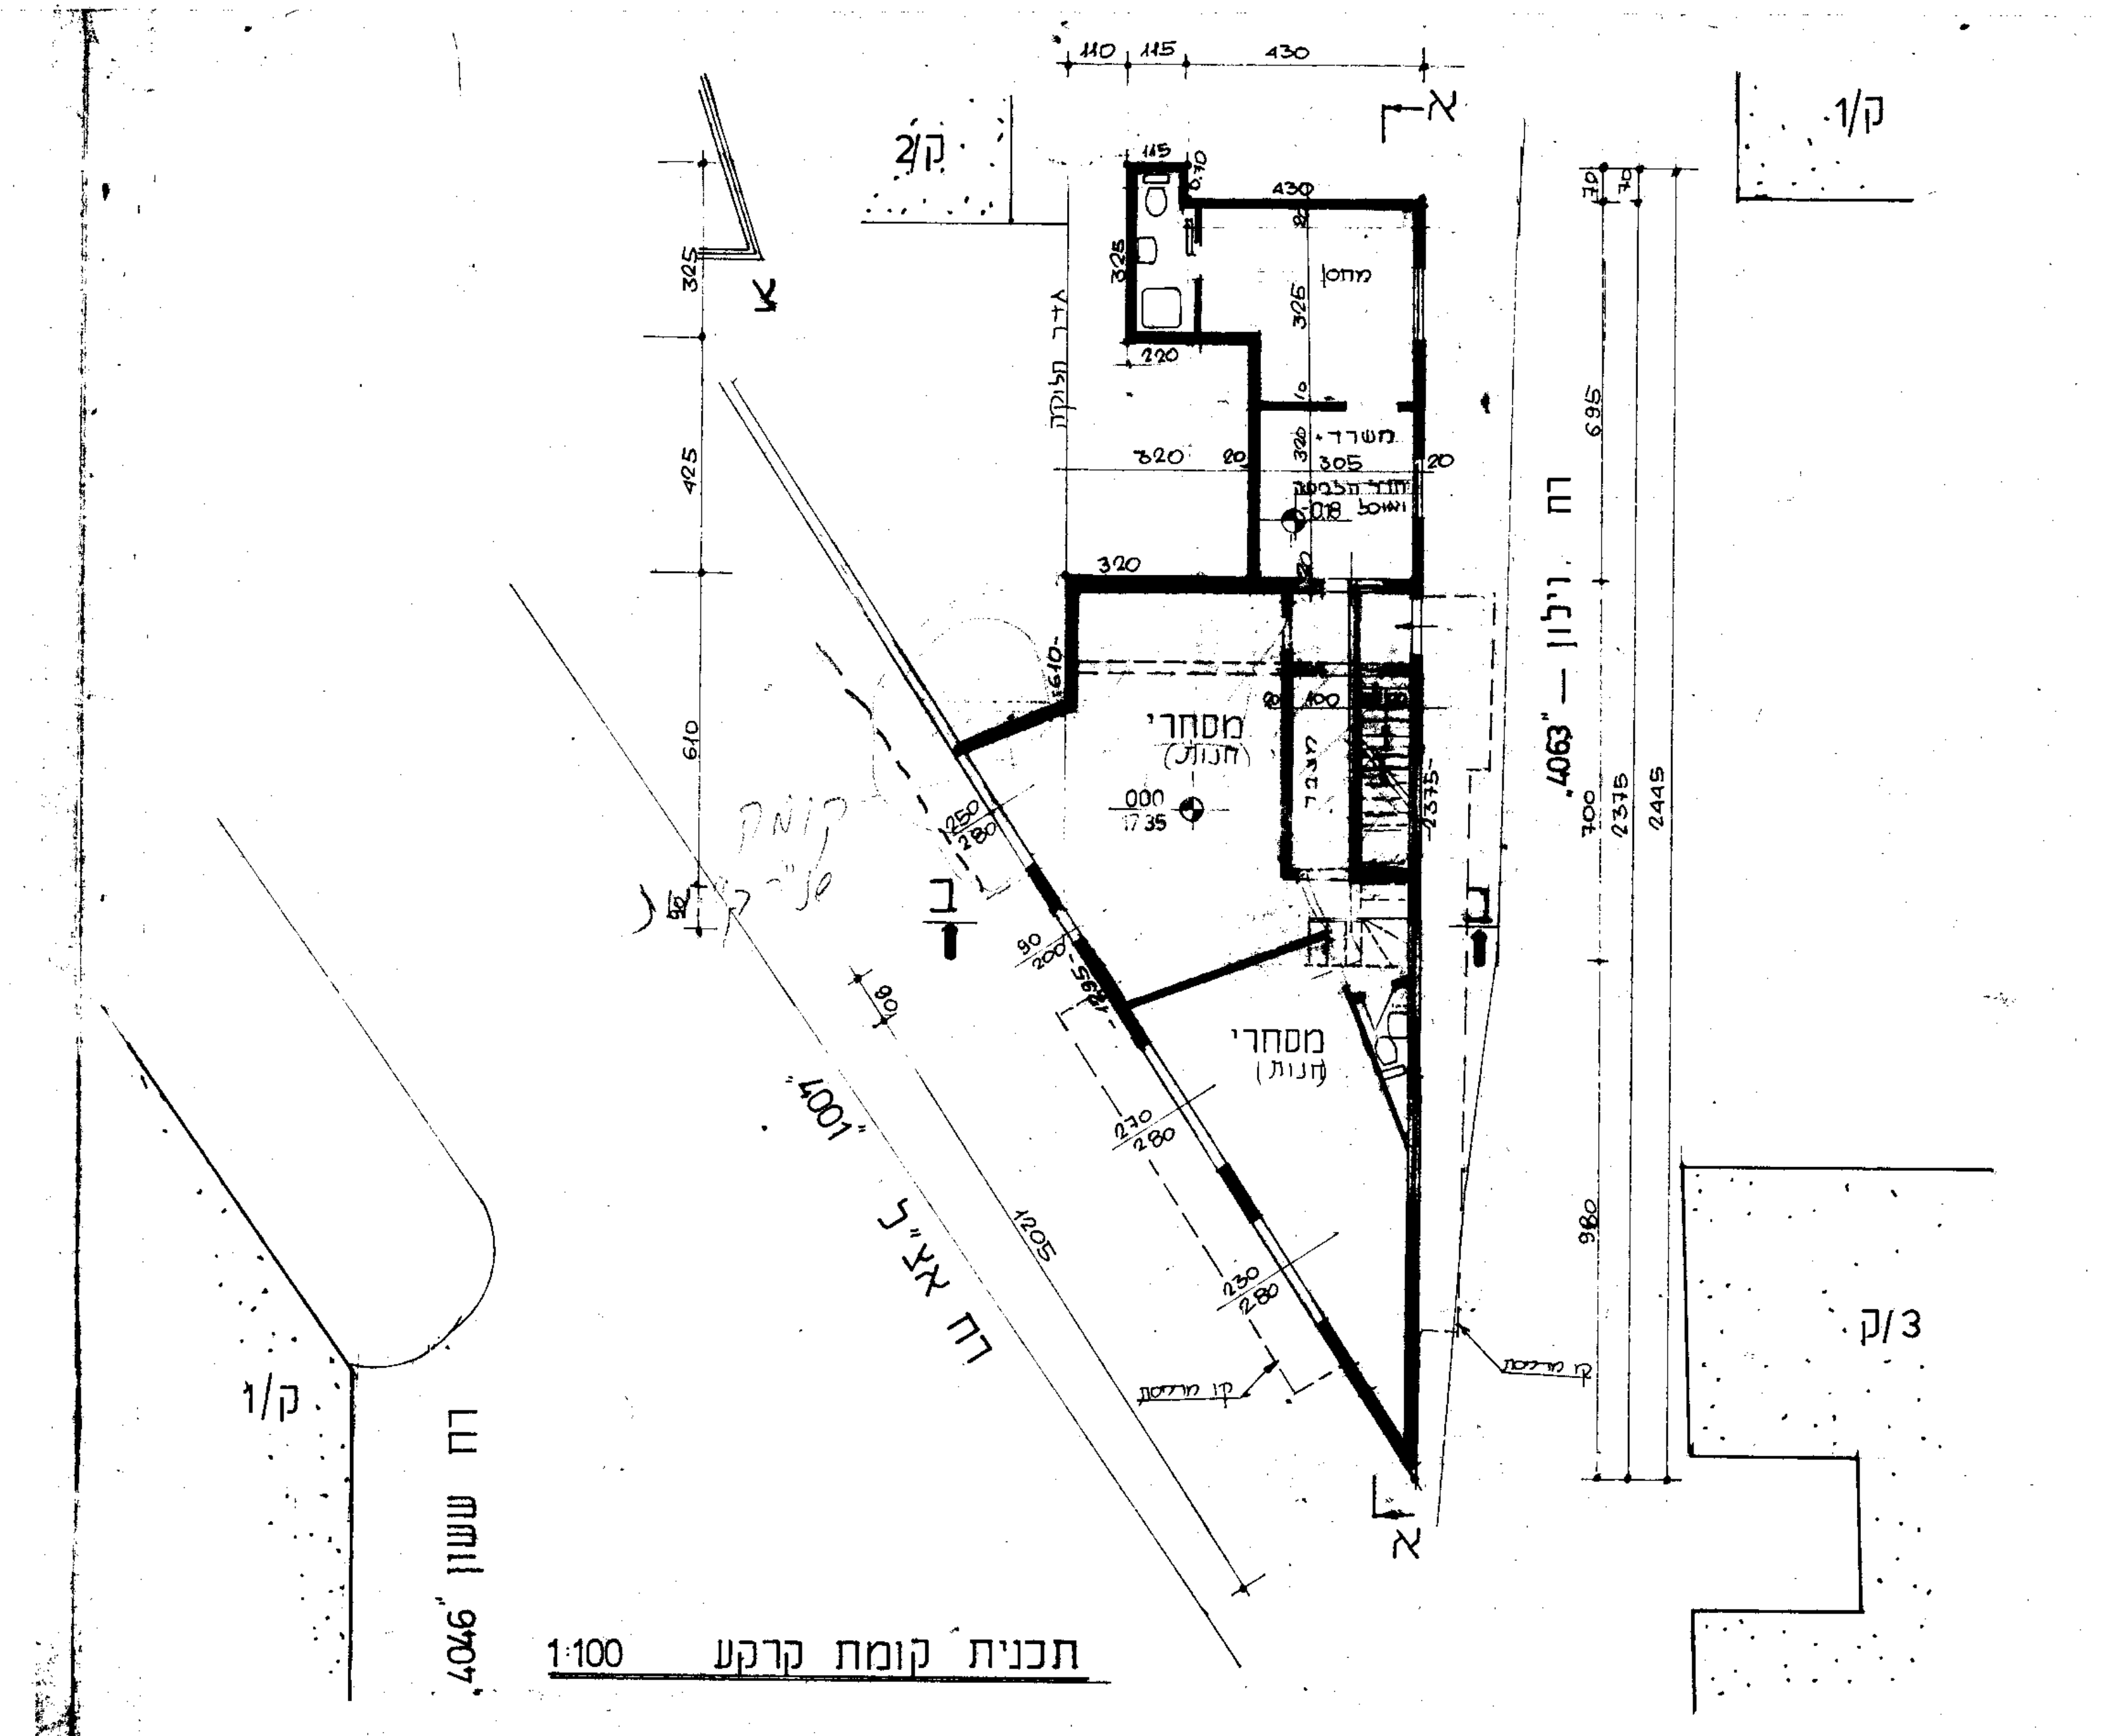
110 115 430
ק/2
א
צ
ק/1
משרד
מחסן
מסחרי
(חנות)
ק/3
ק/1
רח' אצ"ל
רח' ששון
רח' וילון
4001
4046
2345
2445
1205

תכנית קומת קרקע 1:100

חישוב שטחים

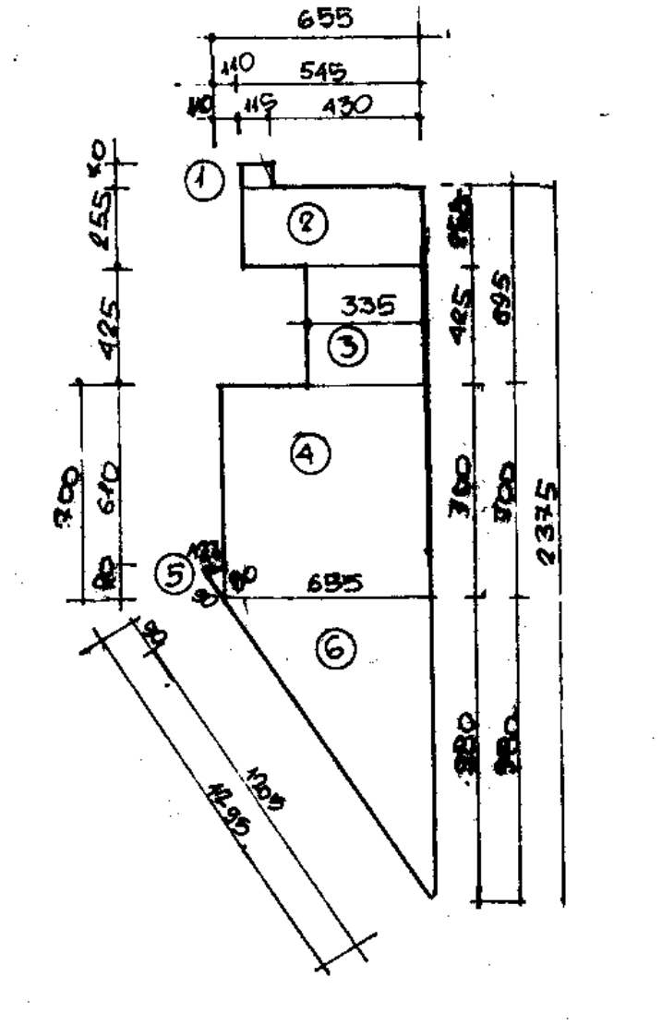
655
110 545
110 115 430
①
②
③
④
⑤
⑥
335
695
2375

קומת קרקע קיימת

① 0.70 × 1.15 = 0.81

② 2.55 × 5.45 = 13.90

③ 3.25 × 4.25 = 13.81

④ 7.00 × 6.55 = 45.85

⑤ (0.90 × 0.90)/2 = 0.40

⑥ (9.80 × 6.55)/2 = 32.10

סה"כ 106.80 מ"ר

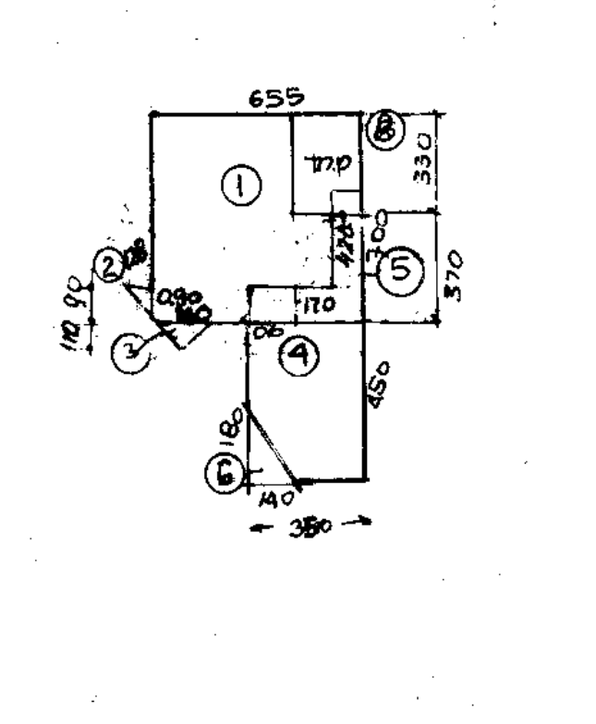
655
①
②
③
④
⑤
⑥
⑧
ממ"ד
330
370
450
350

קומה א' מוצע

① 6.95 × 7.00 = 45.80

② (0.90 × 0.90)/2 = 0.40

③ (1.10 × 1.60)/2 = 0.80

④ 3.50 × 4.50 = 15.70

⑤ (4.20 + 1.70) × 1.1 = 6.50 מדרגות

⑥ (1.40 × 0.80)/2 = 1.30

62.30

⑧ ממ"ד – 7.70

מ"ר 47.20

תל-אביב-יפו
גוש 6135
חלקה 43
השטח מדוד 110 מ"ר
השטח רשום 161 מ"ר
רחוב האצ"ל מס' 73

13-12-02-1996

מפה טופוגרפית 1:250

הוכן עבור: יוסף

מהות הבקשה היתר לתוספת בניה

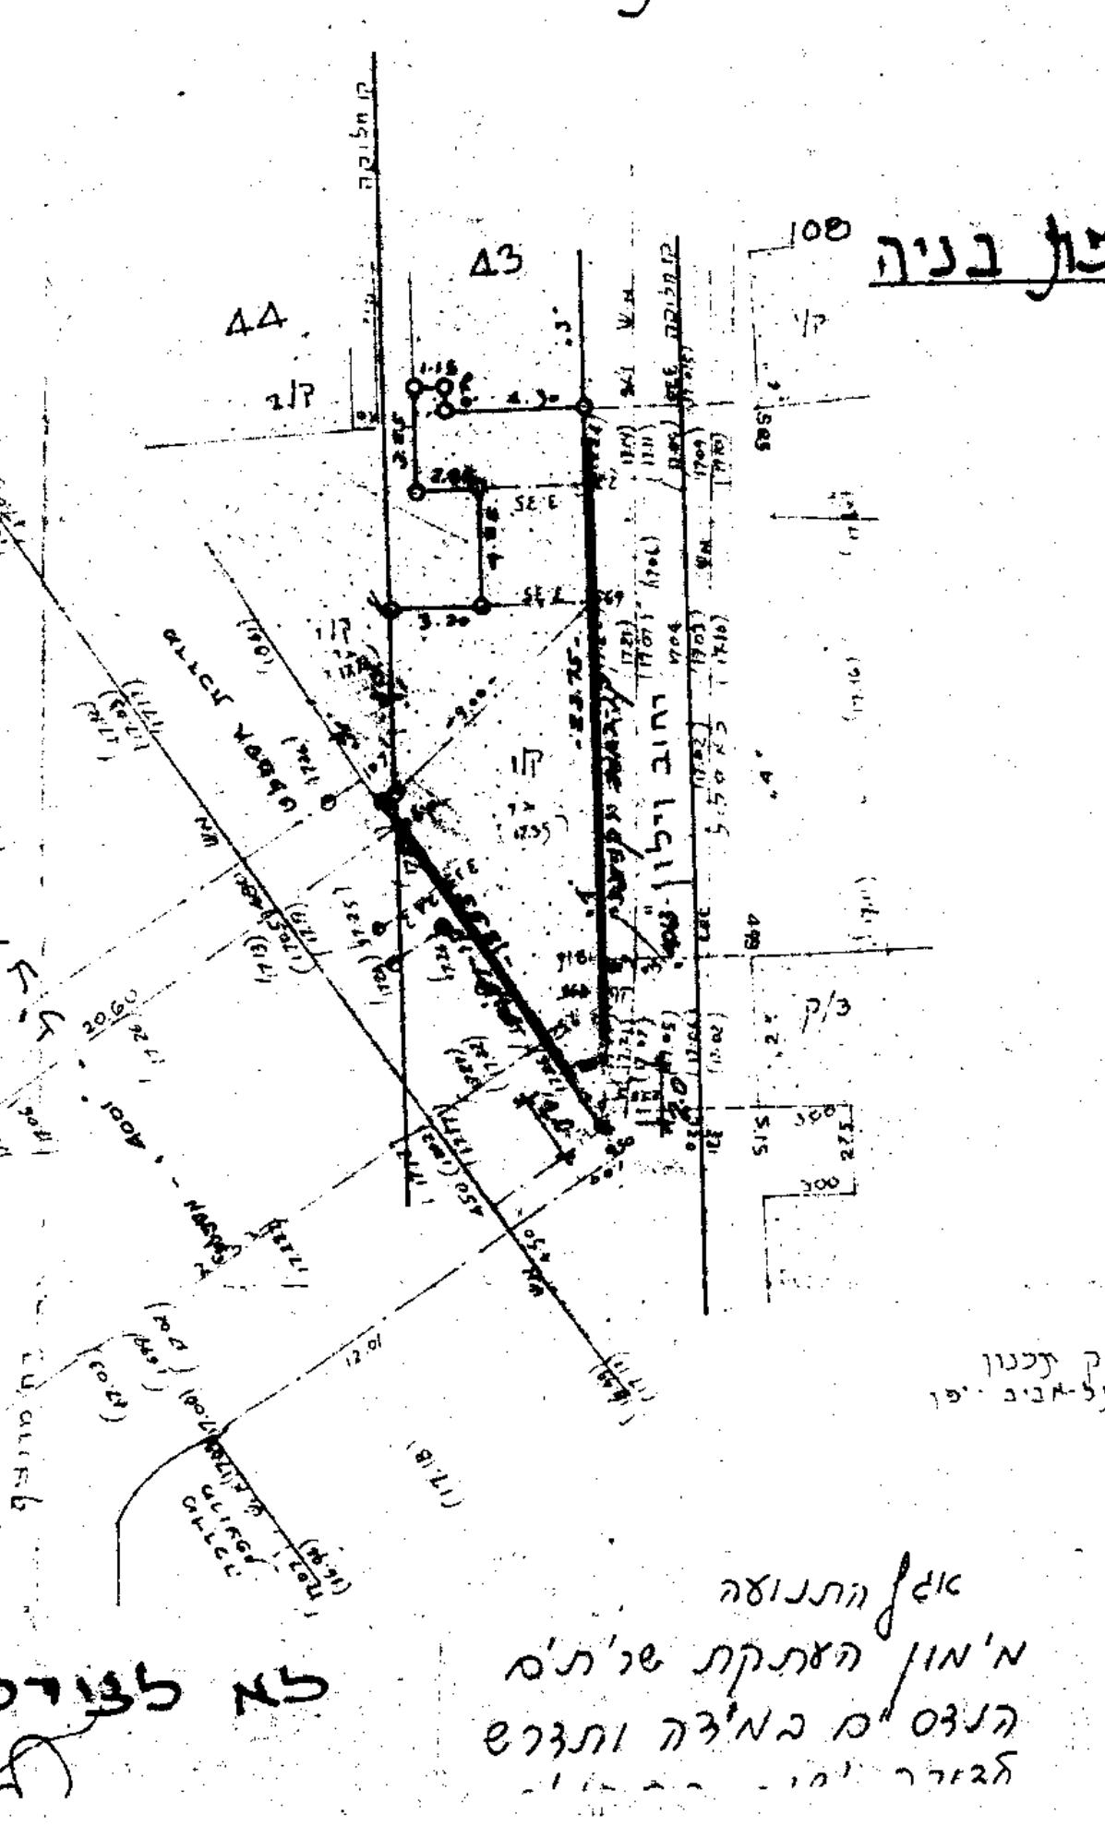
44
43
108
ק/3
רחוב וילון
רחוב אצ"ל
רחוב ששון

תרשים הסביבה 1:1250

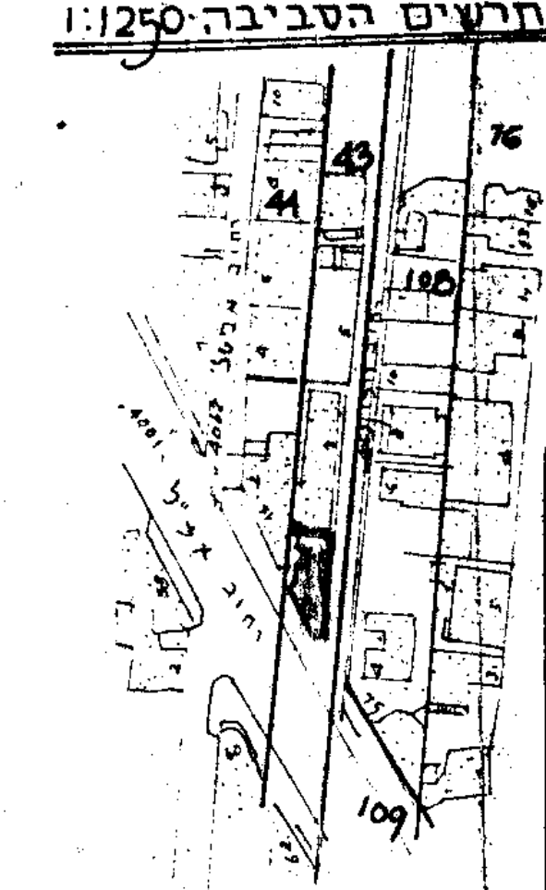
43
41
108
76
109
רחוב אצ"ל

עיריית תל-אביב
מינהל ההנדסה
מחלקת מדידות

הספה עברה במחלקות:
- ☐ דרכים
- ☑ מים
- ☑ ביוב
- ☑ הנחיות צווה
- ☐ אשפה
- ☑ חניה
- ☐ וחיבי אילן
- ☐

עדינה כהן

הנני מצהיר בזה שמפה נעשתה לפי חוק תכנון והבניה ... של עירית תל-אביב יפו

לא לצורכי רישום

אין התנועה
מ"מון העתקת שר"ת"מ
הנוס"ם במידה ותדרש

עיריית תל-אביב-יפו
מחלקה ל... והתעו
(מידע מוקדם)
ביוב
הערות: ...
ביוב קיים בשטח

אישור כתובת

רוחב דרך-20.0, קו בנין-2.00
רוחב דרך-8.0

רוחב 20 מ' קו בנין 0-2 מ'
רוחב 5-8 מ' קו בנין 0 מ'.
קרקע מירבית 60%. מרתף לפי
לפי תכנית ג'. אין לגבות
השכונה מוכרזת כשכונת שיקום.
חל היטל בגין השימוש
קע ומרתף תחתון אם יותר.
דות דיור לדונם נטו.
ת תכנון מזרח.
מסגרת הסדר הגוש כולו.

8.2.96

ג. קוי בניה

לרחוב/לצד	חזית	מותר	סטיה ס'	סטיה %
שם רחוב: אצ"ל	0	0		
שם רחוב: וילון	0	0		
צד: קדימה	2.0	2.0		
אחור				

4. מס' יחידות דיור: קיים 1, מותר 1

9. תאור הקיים על המגרש: קיים מבנה בן קומה -1 מסחרי

11. רשות רישוי - מסלול רגיל ☒

עיריית תל-אביב-יפו
מינהל ההנדסה

הועדה המקומית לתכנון ובניה - ת"א-יפו

מס' תיק בקשה	
מס' תיק בנין	4001-73
מס' תיק מידע	96-0361
מס' בקשה קודמת	
מחזור הרישוי	

טופס השלמת פרטים
עפ"י סעיף 11 ב' (תקנות התכנון והבניה)

חלק א' - תאור הבקשה

1. סיווג הבקשה: ב. תוספת עד 50 מ"ר

ט. עבודה מצומצמת - תאור העבודה: תוספת בקומה א'

2. פירוט השטחים הקיימים בהיתר ושלא בהיתר - (שטחים עיקריים)

קומה	קיים בהיתר	קיים ללא היתר	מתוכנן/אישור בניה קיימת	שטח	אחוז
מרתף					
ק.קרקע	106.80			66.0	60%
א			47.20	44	40%
ב				44	40%
ג					
ד					
ה					
ו					
ז					
ממ"ד			7.70		
הכניסה הקובעת					
חדרי מדרגות					
בניה על הגג					
סה"כ				154	140%

א. מינויים והצהרות המבקשים

שמות עורכי הבקשה		חתימות עורכי הבקשה	מס' רשיון
1. ז'בגורסקי	(עורך ראשי)		15320

30.07.96

2. הצהרת המתכנן שלד הבנין: 1468785 ז'בגורסקי 15320 15320

30.07.96

שמות עורכי הבקשה	תחום פעולה	מען	טלפון	פקס
1. ז'בגורסקי	עורך ראשי	באר טוביה 11		
		5221162 ת"א		

מינוי מתכנן השלד: 1468785 ז'בגורסקי, באר טוביה 11, 5221162

יוסף ישכר

השטחים המבוקשים לבניה בכל מפלס בנפרד (עפ"י תכנית הבניה)

	השימושים העיקריים (מ"ר) מסחרי קיים	מגורים מוצע	סה"כ מ"ר	סה"כ % משטח המגרש	חלקי שירות מקלט	סה"כ מ"ר	סה"כ %	סה"כ הבנין מ"ר	סה"כ הבנין %
	106.80		106.80	97.10				106.80	97.10
		47.20	47.20	42.90	7.70	7.70	7.0%	54.90	49.90
סה"כ	106.80	47.20	154.0	140%			7.%		147.%

השטחים המותרים לבניה בכל המפלסים יחד (עפ"י אסמכתא: חוק, תקנות, תכנית)

	מסחרי	מגורים	סה"כ מ"ר	סה"כ %	מקלט	סה"כ מ"ר	סה"כ %	סה"כ מ"ר	%
	106.80	47.20	154.0	140%				154.0	140
					7.70	7.70	7.%	7.70	7.00
סה"כ	106.80	47.20	154	140%			7		147

הנני מצהיר על נכונות הפרטים דלעיל: ז'בגורסקי 30.07.96

חתימות נוספות:
המבקש: יוסף 30.07.96
בעל הזכות בנכס: — " — 30.07.96
מתכנן שלד הבנין: ז'בגורסקי 30.07.96

נבדק מטעם הוועדה/רשות הרישוי ע"י:

22

חוק התכנון והבניה, התשכ"ה-1965
בקשה להיתר בניה או לשימוש במקרקעין

עיריית תל-אביב-יפו
מינהל הנדסה
18-02-1997

97-0347

[redacted]

ועדה מקומית לתכנון ובניה / רשות רישוי	ת"א
מס' תיק	4001-073
כתובת: שם הישוב	ת"א
שם הרחוב	אצ"ל
מס' בית	73
סמל רחוב	4001
גוש	6135
חלקה	43
התכנית/יות החלה/ות במקום	2215

	שם	משפחה	מס' זהות	מען	
המבקש	יוסף	מיכאל	5100232	רח' אצ"ל 73 ת"א	
בעל הזכות בנכס	יוסף מיכאל יוסף ישכר		5100232 047981	רח' אצ"ל 73 ת"א	
עורך הבקשה הראשי	ז'בגורסקי	אלכס	1468785	רח' באר טוביה 11 ת"א	5221162
מתכנן שלד הבנין	— " —	— " —	— " —	— " —	— " —

תאור הבקשה: תוספת למבנה קיים בקומה א', בשטח 47.20 + ממ"ד 7.70

שטח: % בניה 140% — 154 מ"ר — 110

עיריית תל-אביב-יפו
מינהל ההנדסה
מחלקת פקוח על הבניה
חבל 34
תכנית מס' 97-0347
נבדקה בשטח 2.3.97
מהנדס אזורי

מצב קיים לא מתאים למציאות

14.00

פרטי הבנין – לשימוש הלשכה המרכזית לסטטיסטיקה

נסרק

איכות נמוכה