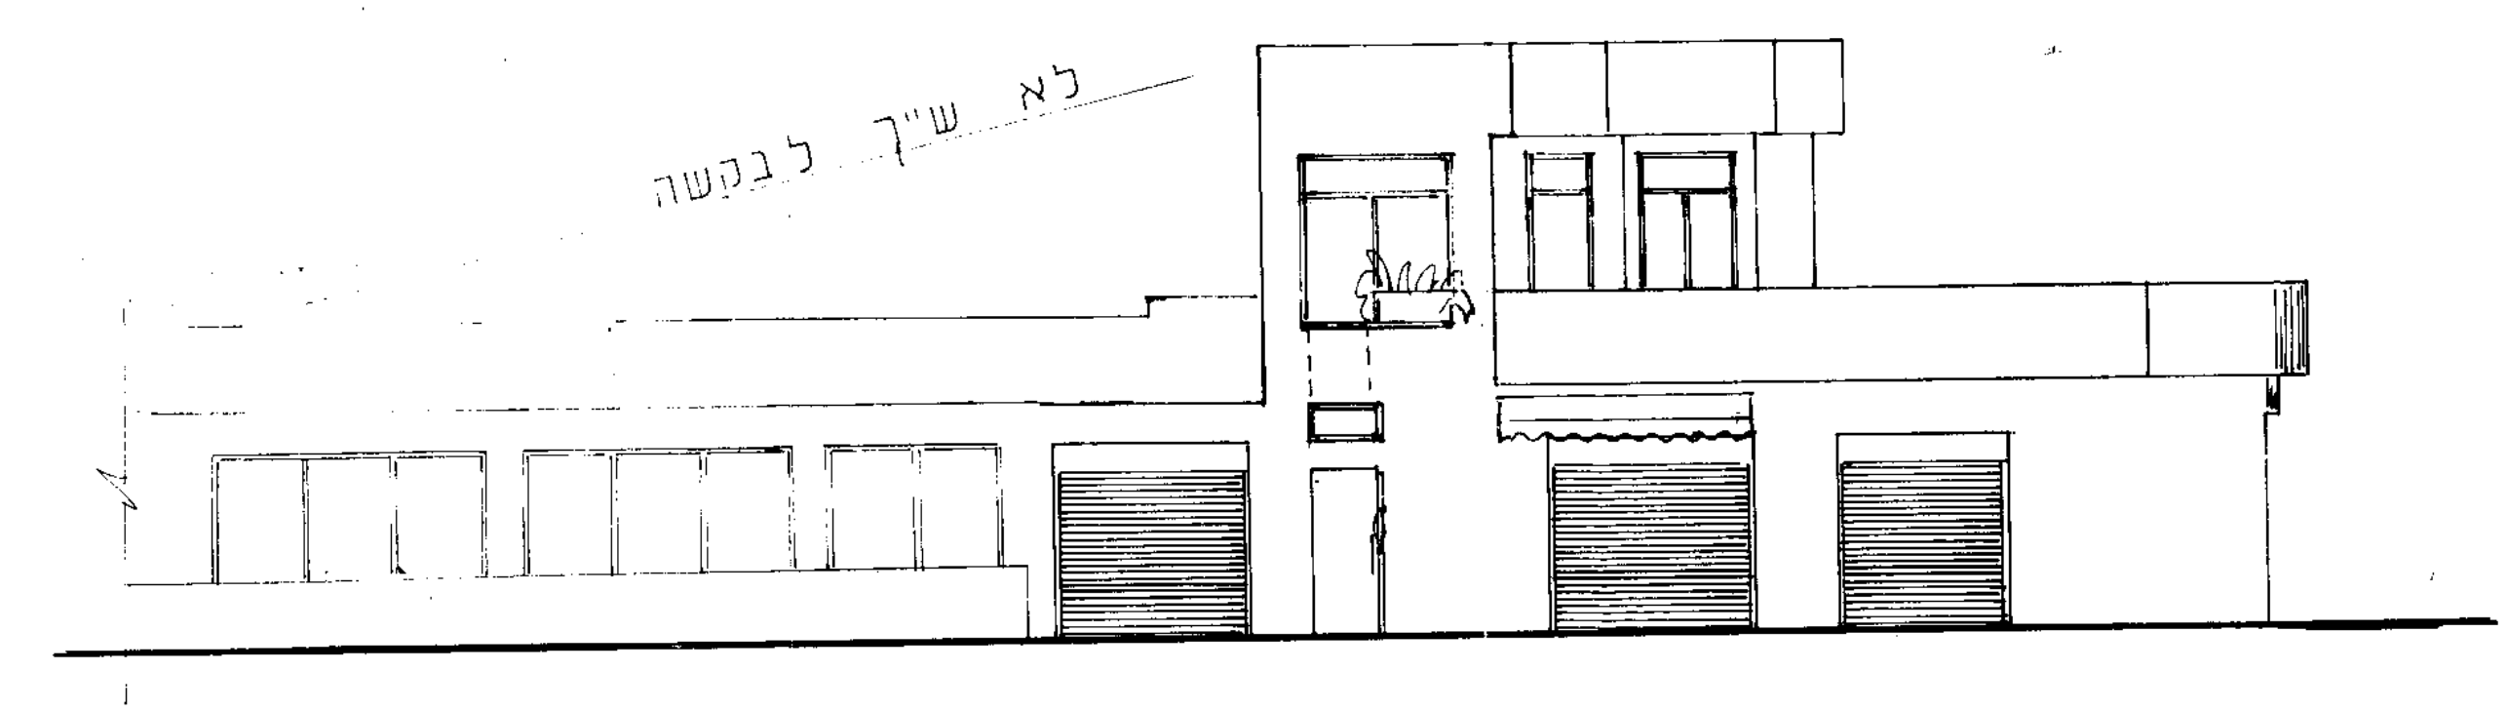
לא שייך לבקשה
+7.80
+6.50
+4.50
+3.50
+3.20
±0.00

חזית מרחוב אצ"ל 1:100

גמר טיח אקרילי
בגוון בהיר
(כולל קירות משותפים)

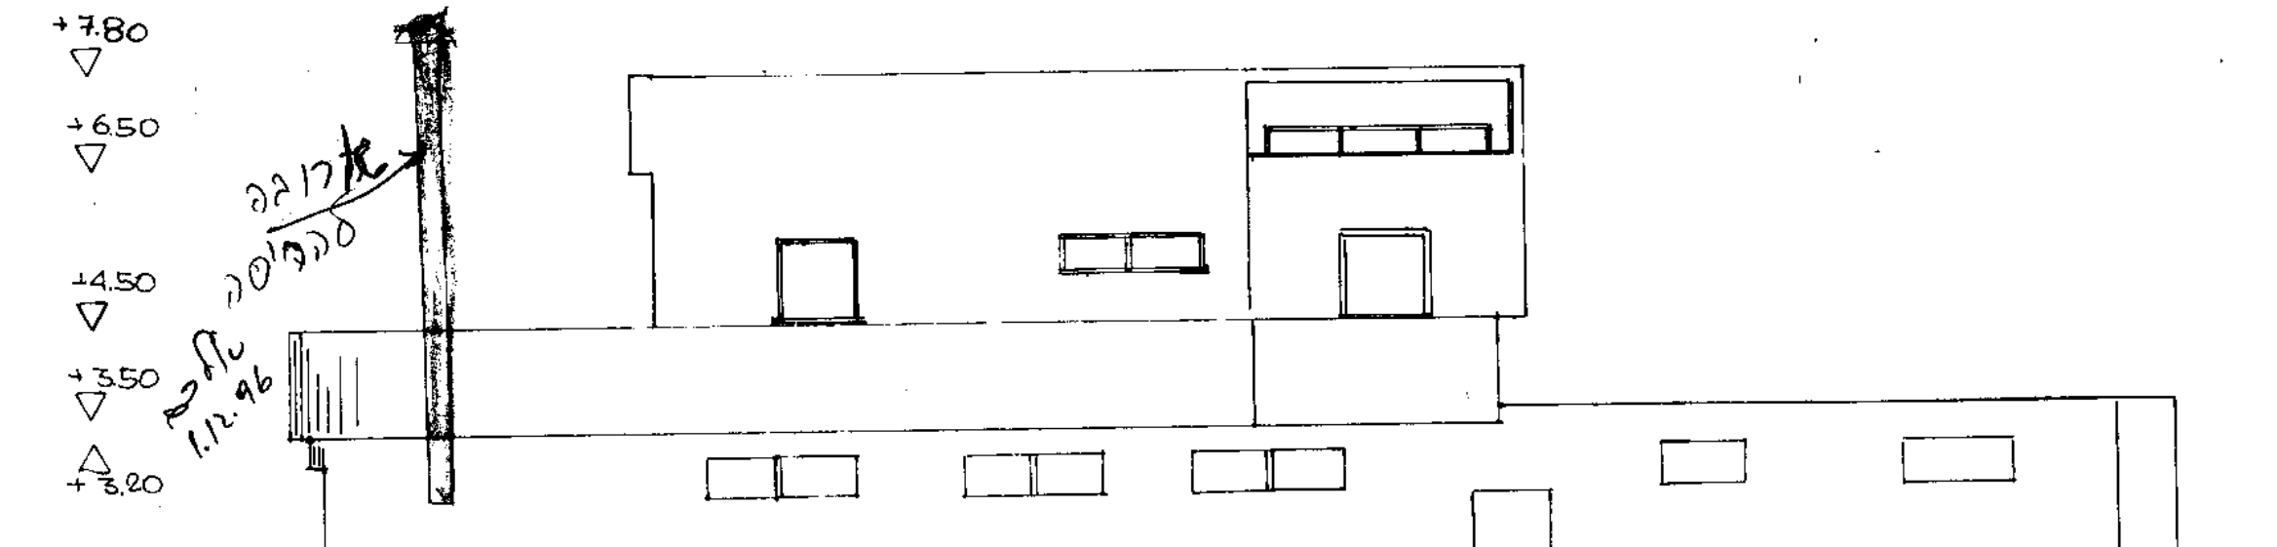
+7.80
+6.50
+4.50
+3.50
+3.20
±0.00
ארובה להריסה

חזית מרחוב וילון 1:100

גמר טיח אקרילי
בגוון בהיר
(לשני קירות)

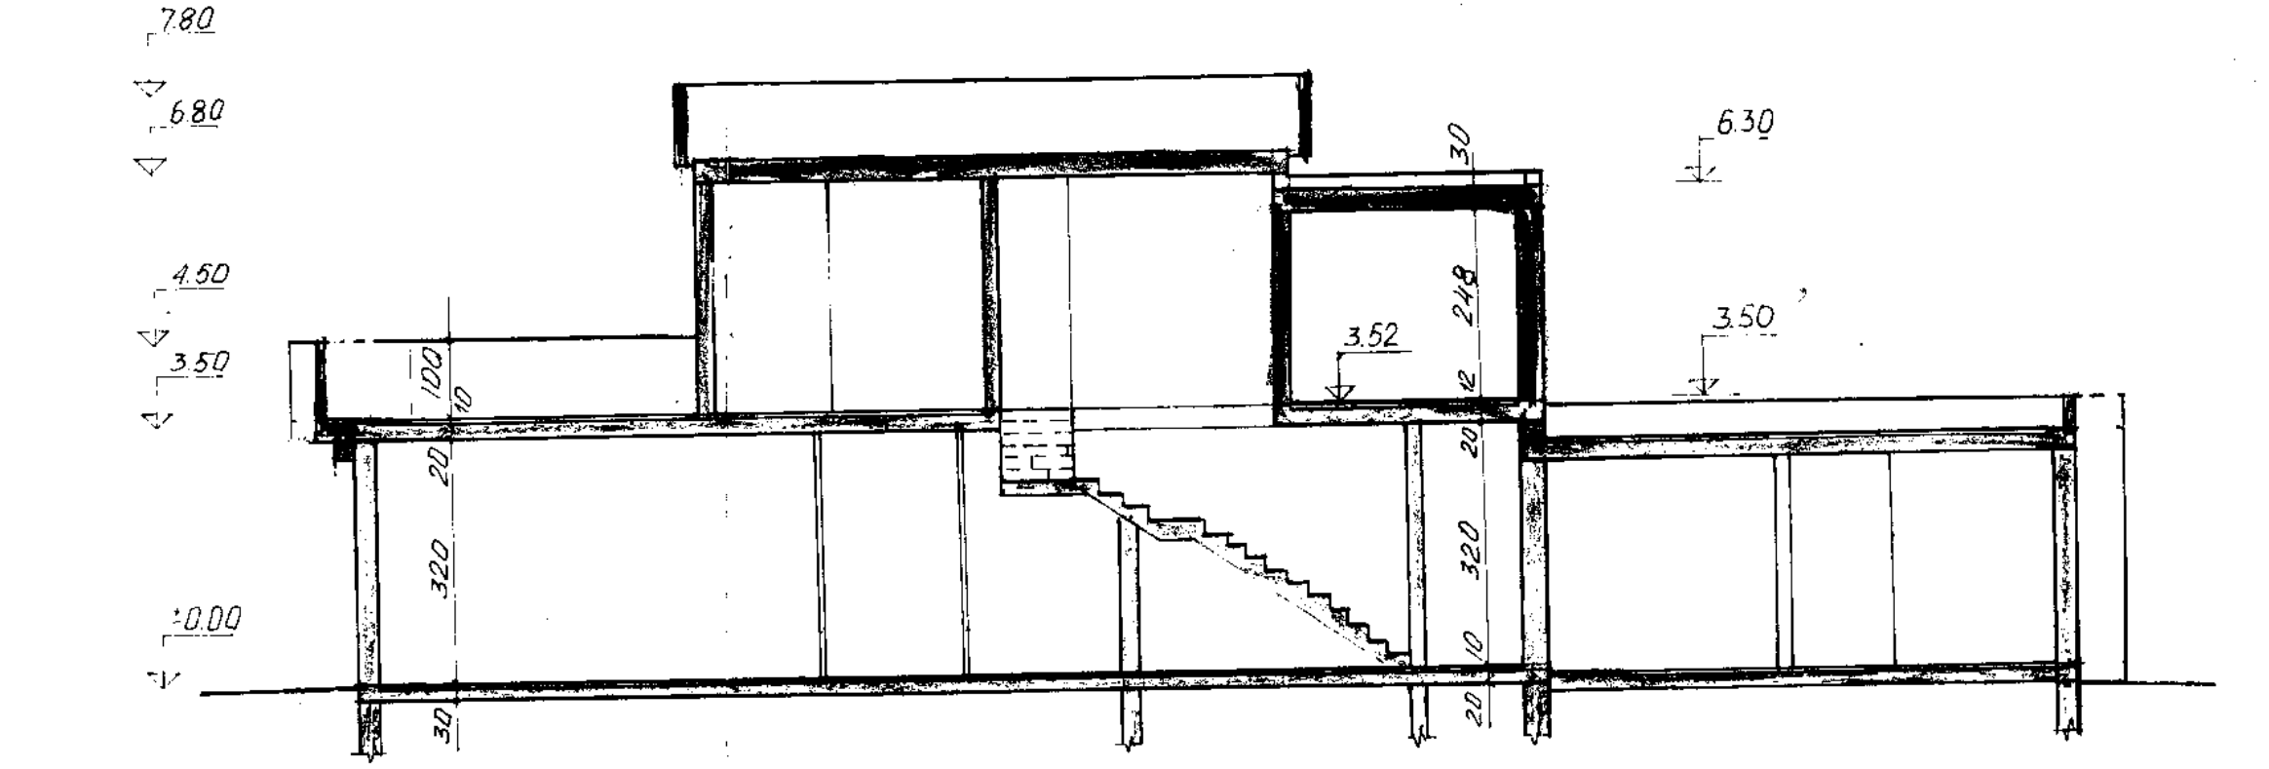
7.80
6.80
6.30
4.50
3.50
3.52
3.50
±0.00

חתך א-א 1:100

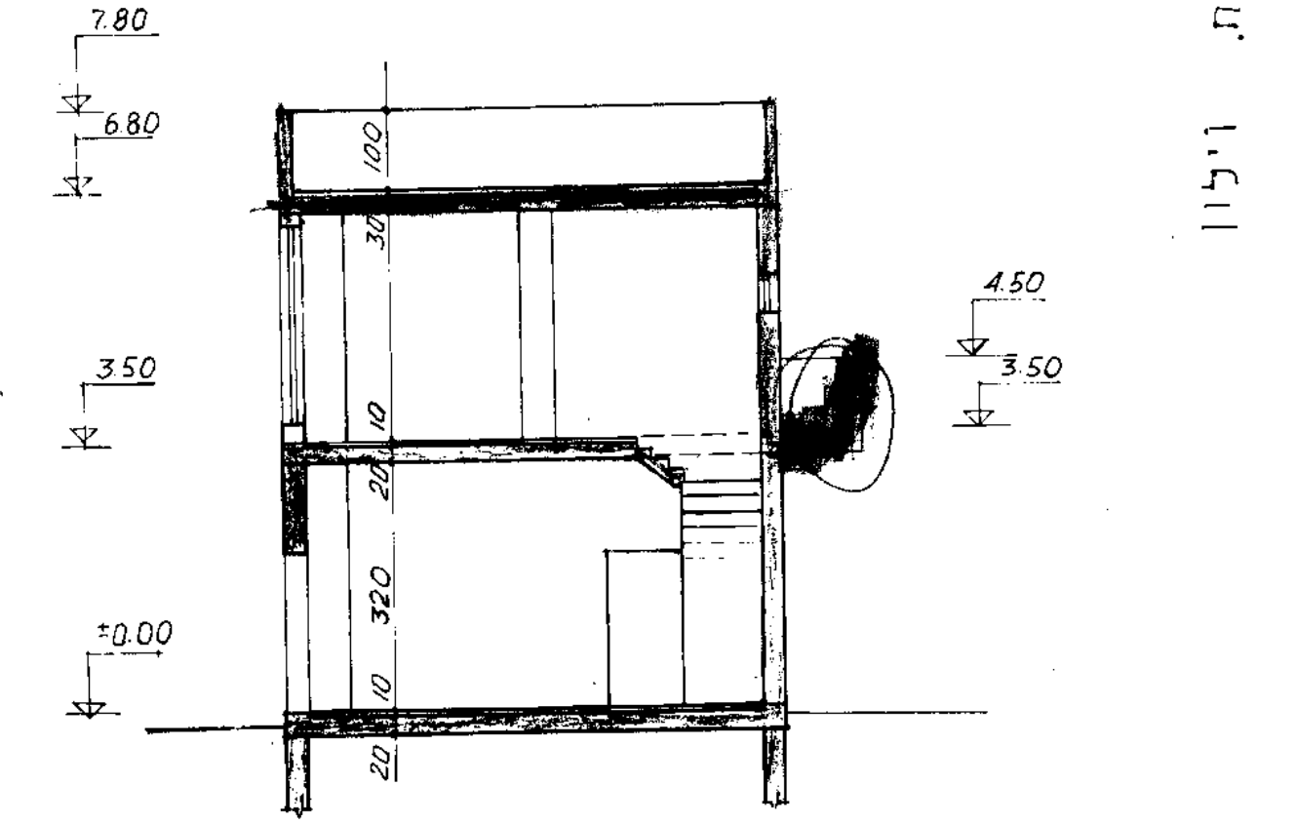
7.80
6.80
4.50
3.50
3.50
±0.00

חתך ב-ב 1:100

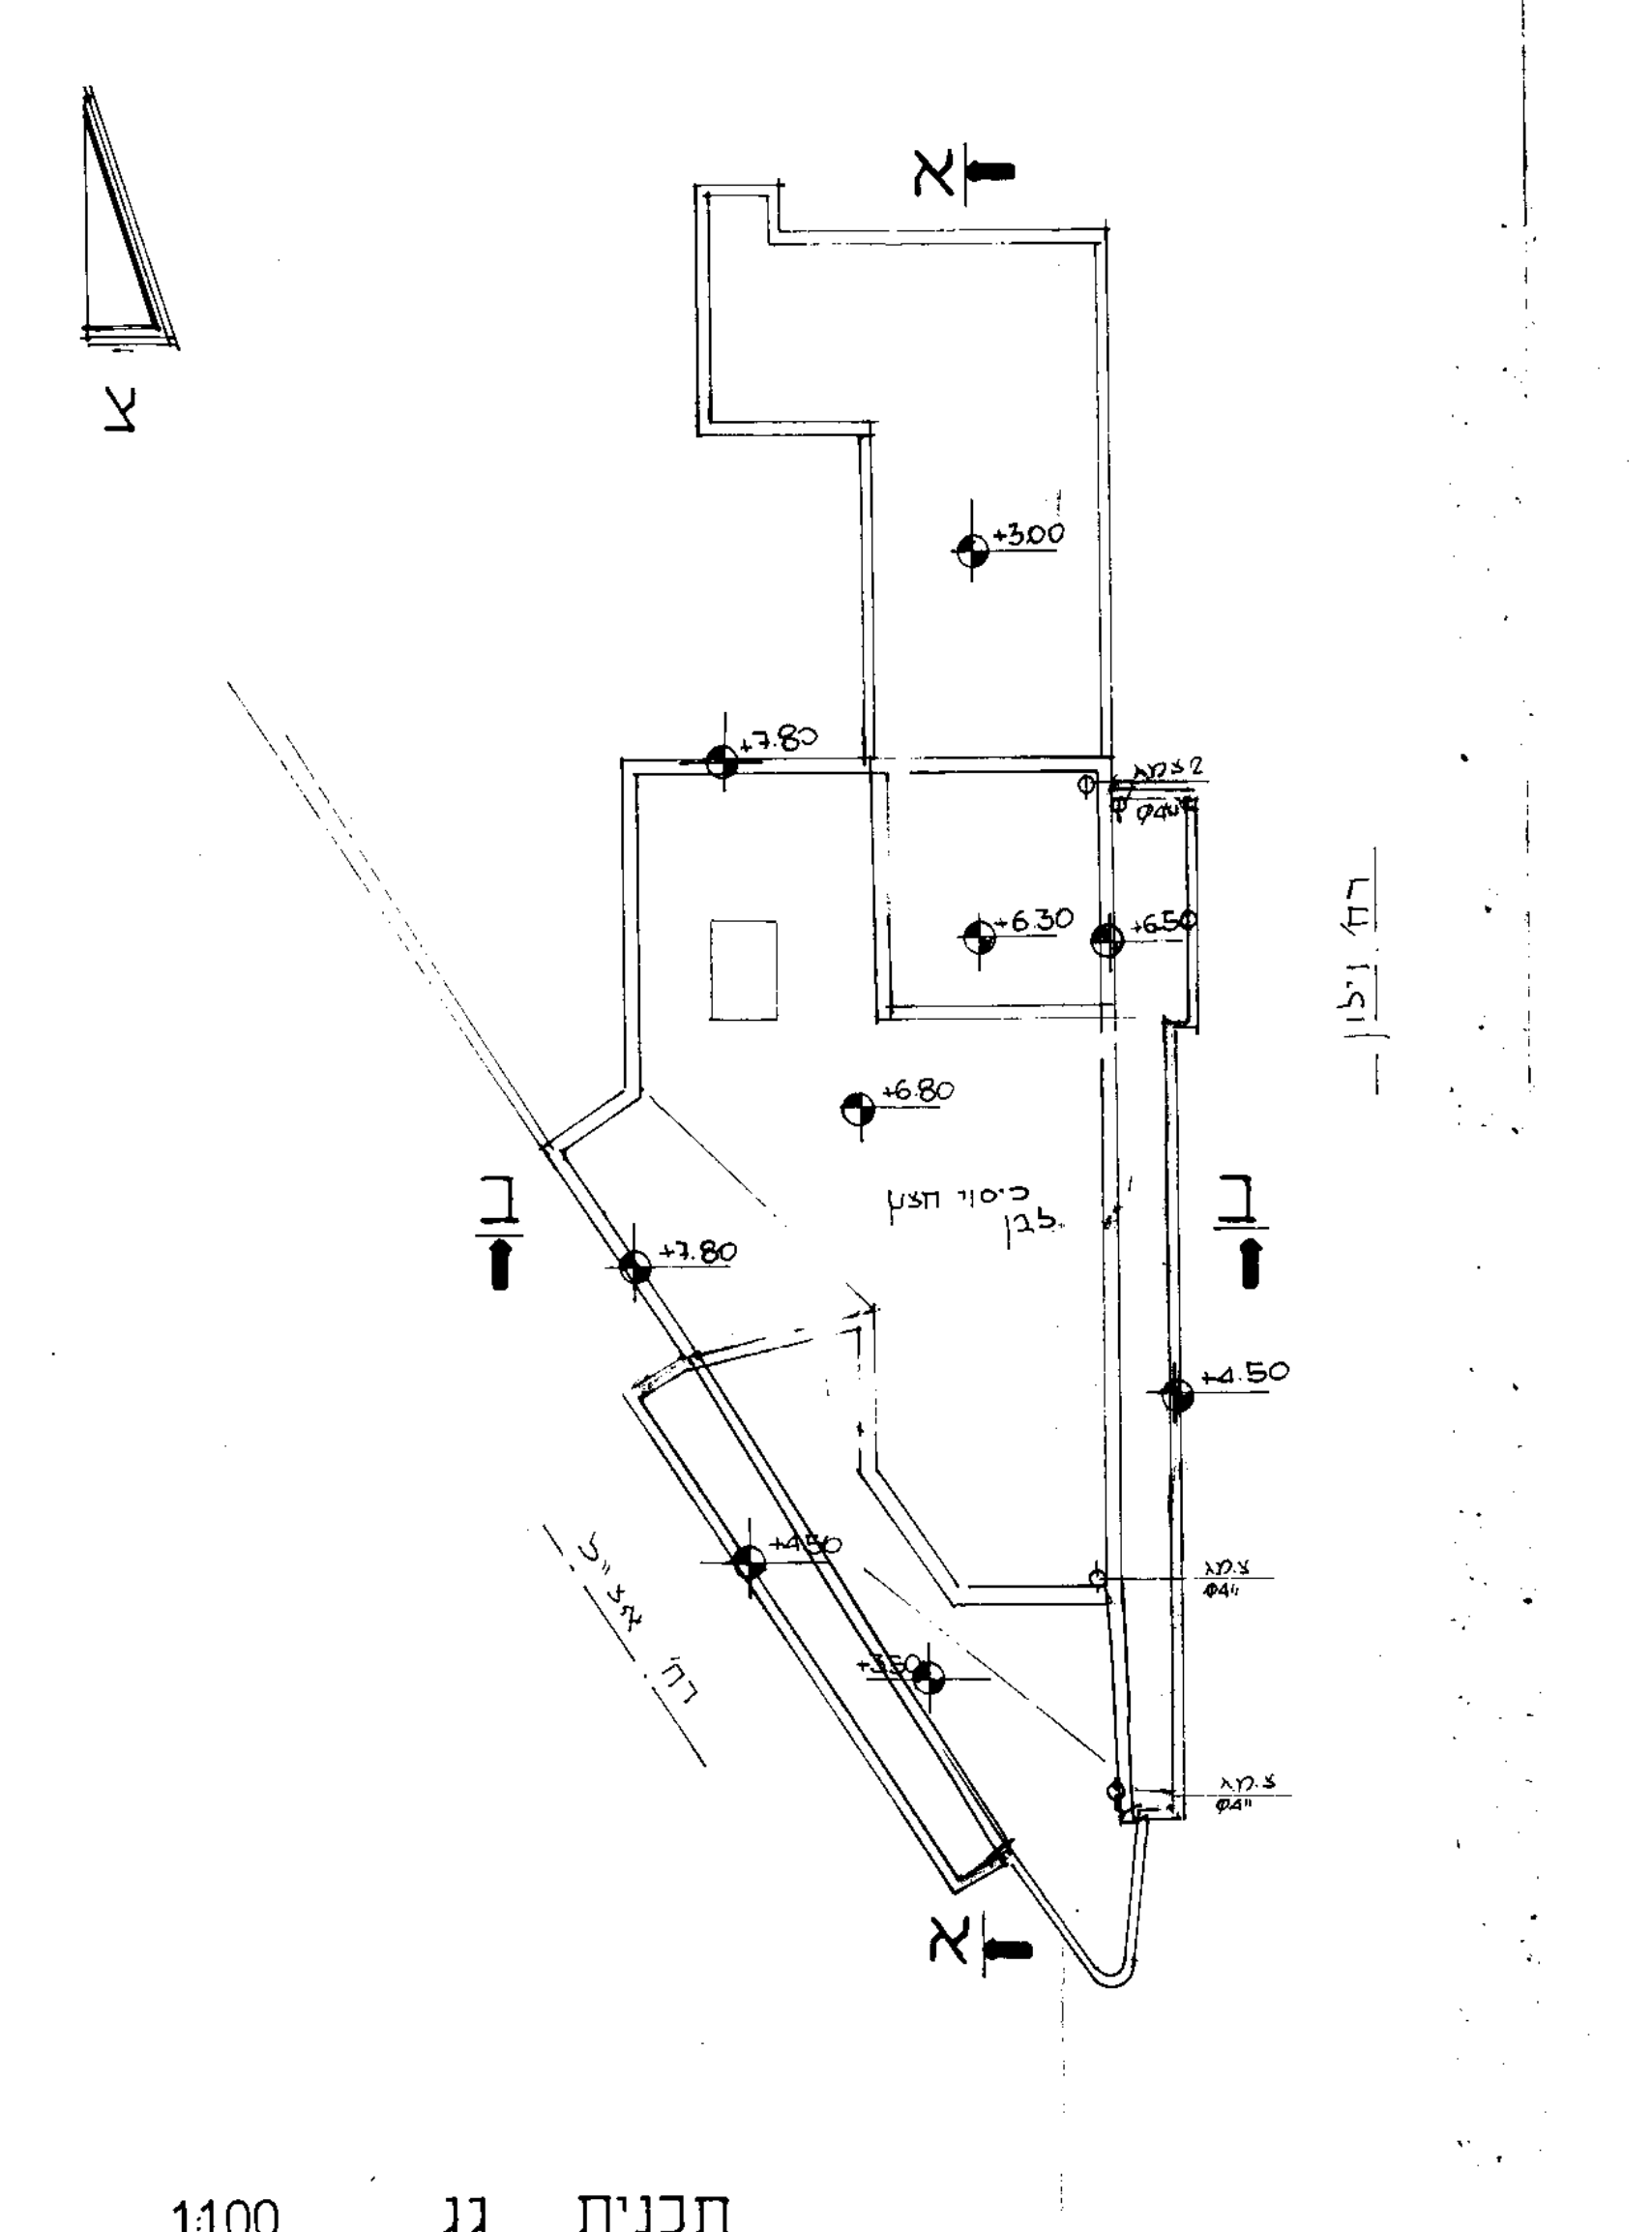
צ
א
ב
+3.00
+7.80
+6.30
+6.50
+6.80
+3.80
+4.50
כיסוי חצץ
רח' וילון
רח' אצ"ל

תכנית גג 1:100

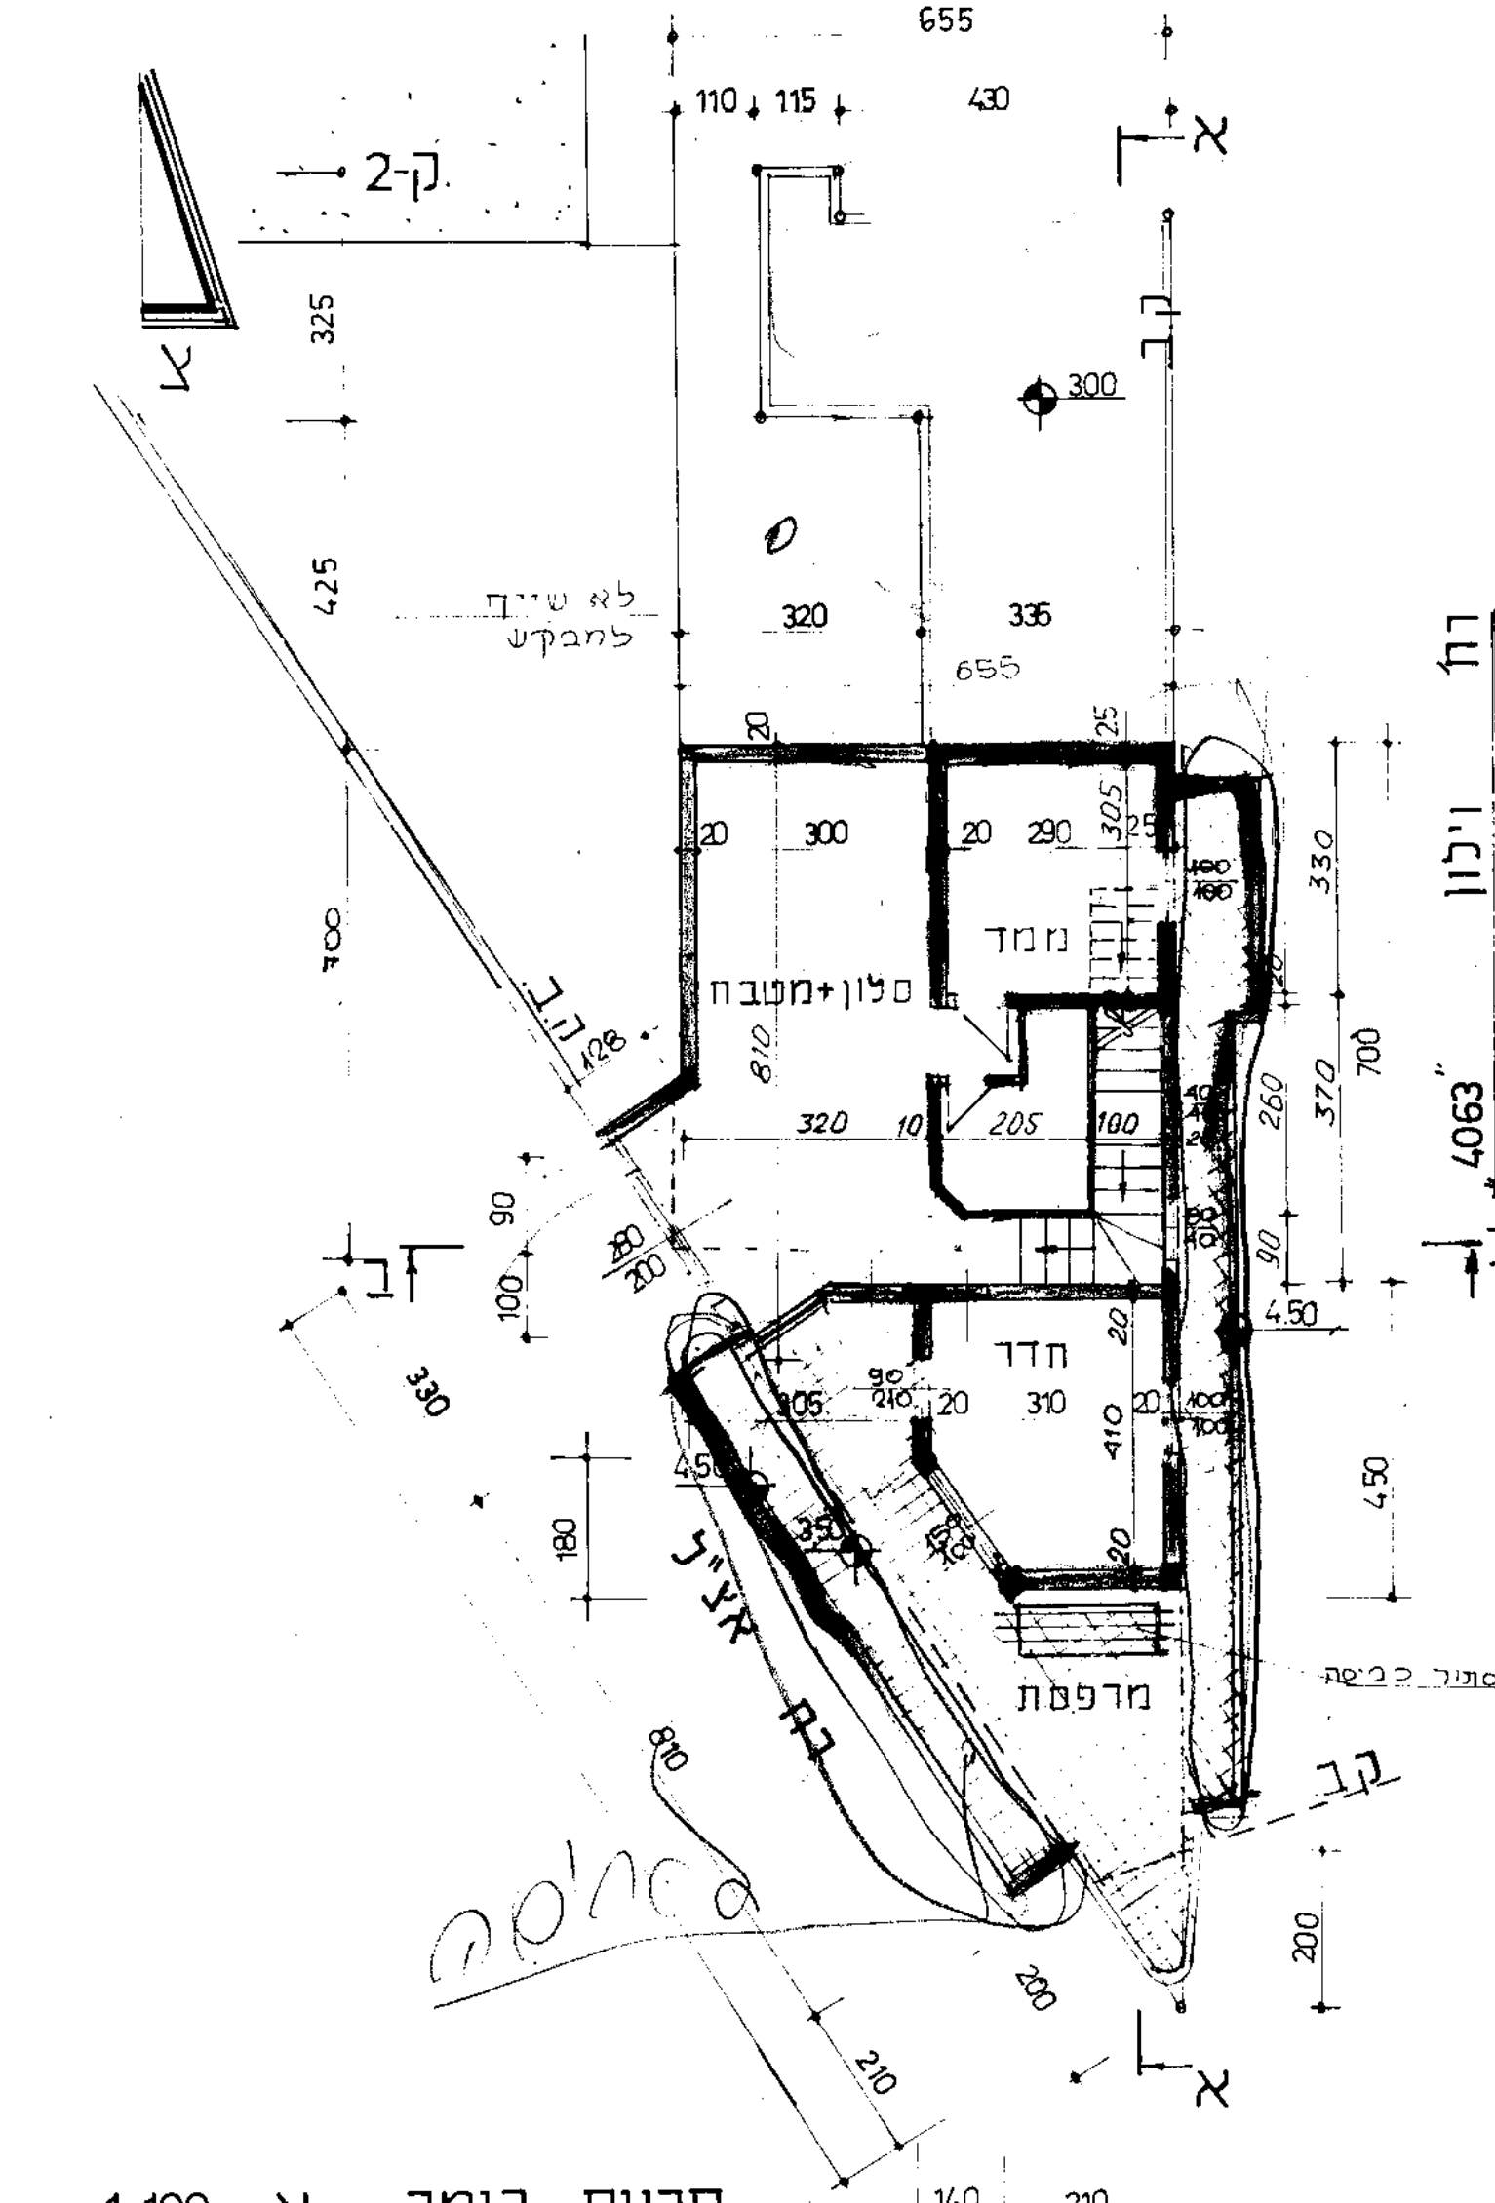
ק-2
655
110 115 430
לא שייך לבקשה
סלון+מטבח
ממד
חדר
מרפסת
רח' וילון
רח' אצ"ל
4063
להריסה
א
ב

תכנית קומה א 1:100

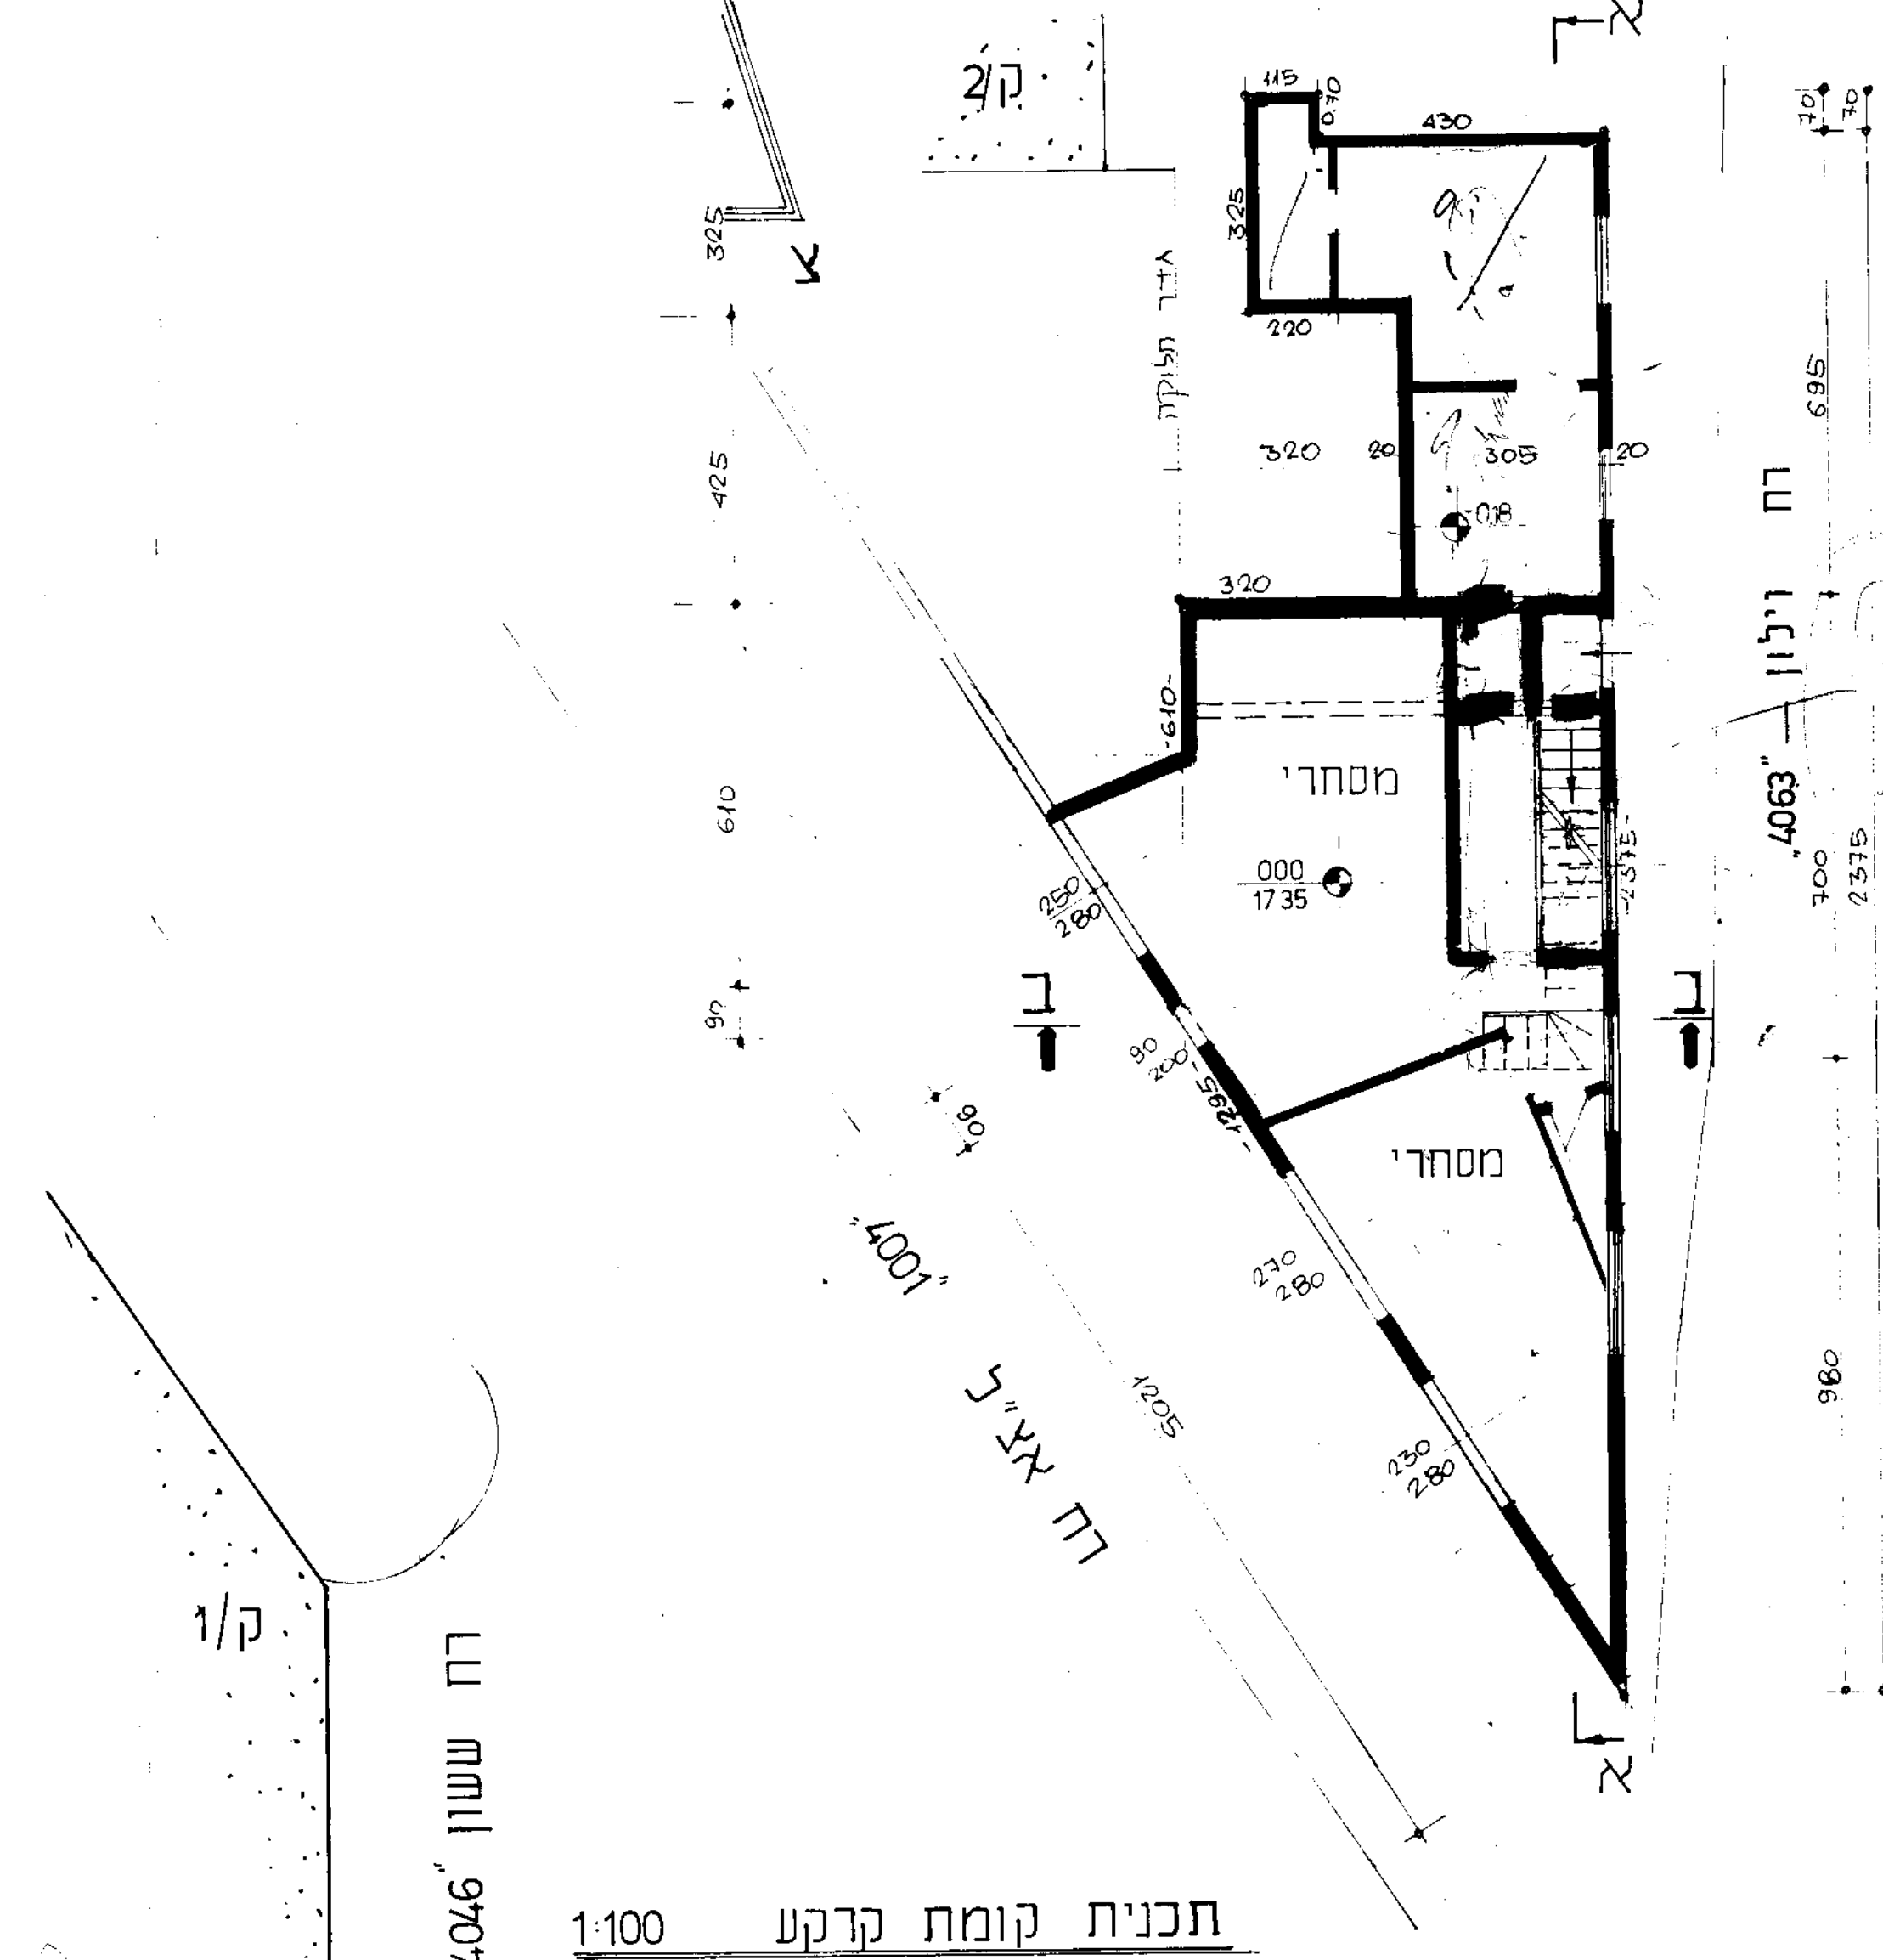
ק/2
ק-1
ק-3
ק/1
ק/3
גדר חלקה
מסחרי
±0.00
17.35
רח' וילון
רח' אצ"ל
רח' ששון
4001
4046
א
ב

תכנית קומת קרקע 1:100

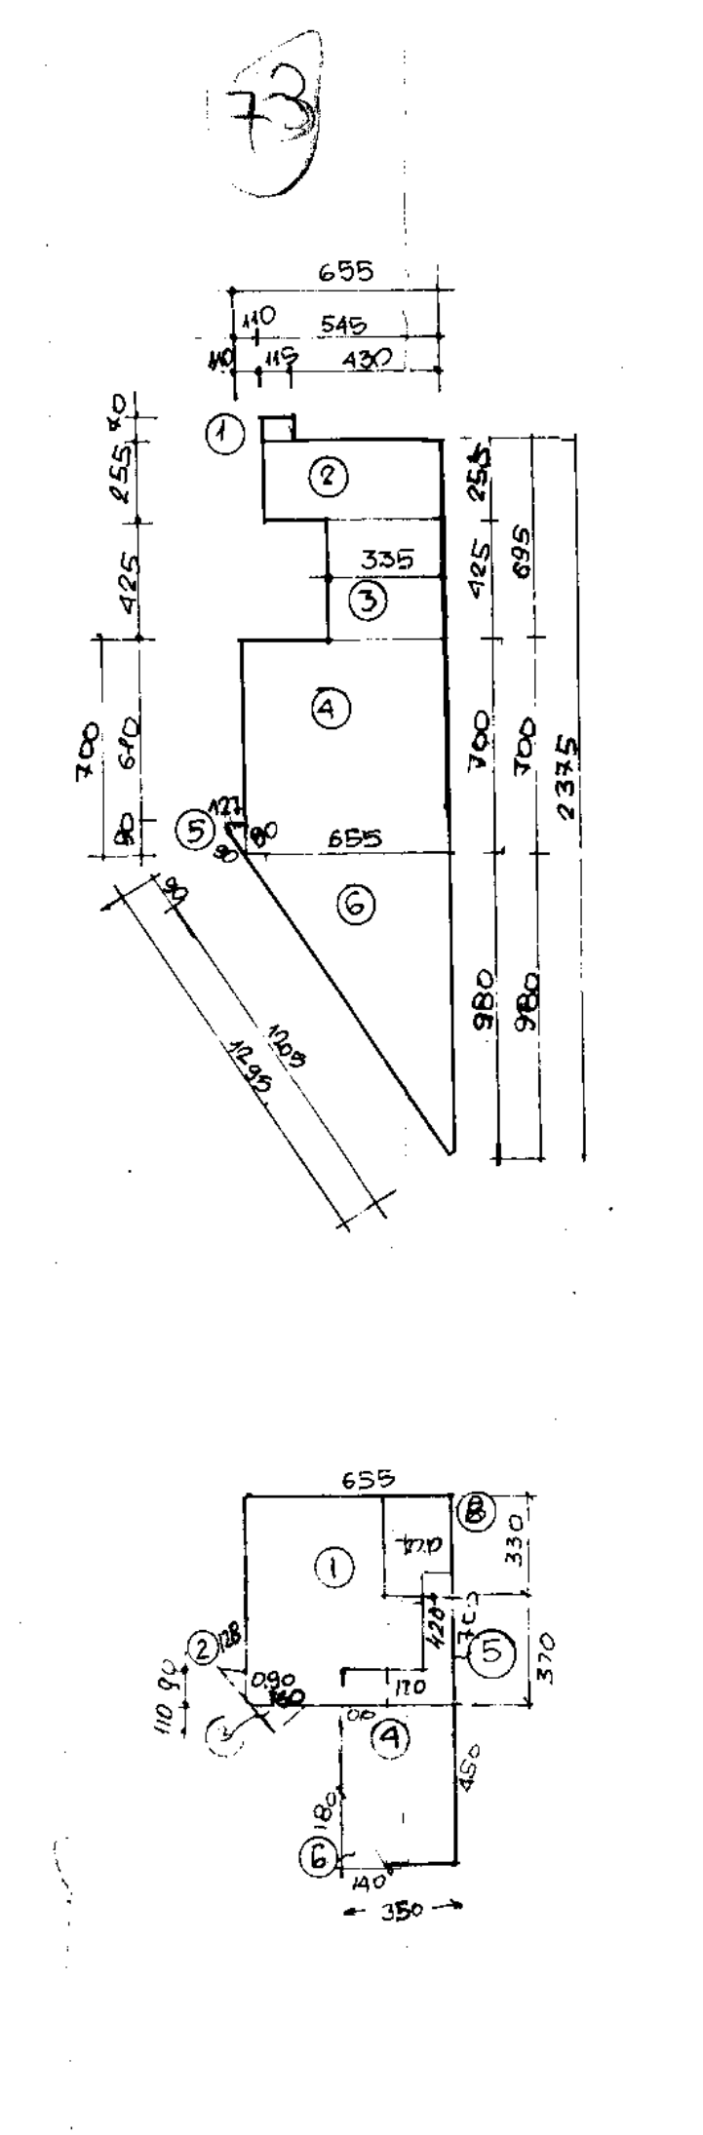

חישוב שטחים

קומת קרקע קיימת

① 0.70 x 1.15 = 0.81
② 2.55 x 5.45 = 13.90
③ 3.25 x 4.25 = 13.81
④ 7.00 x 6.55 = 45.85
⑤ 0.90x0.90/2 = 0.40
⑥ 9.80/2 x 6.55 = 32.10
106.80 מ"ר

קומה א' מוצע

① 6.55 x 7.00 = 45.80
② 0.90x0.90/2 = 0.40
③ 1.10x1.60/2 = 0.80
④ 3.50 x 4.50 = 15.70
⑤ (1.20+1.70)x1.1 = 6.50 מרפסת
⑥ 1.10x0.90/2 = 1.30
62.70
7.55
⑦ ממד
מ"ר =47.20

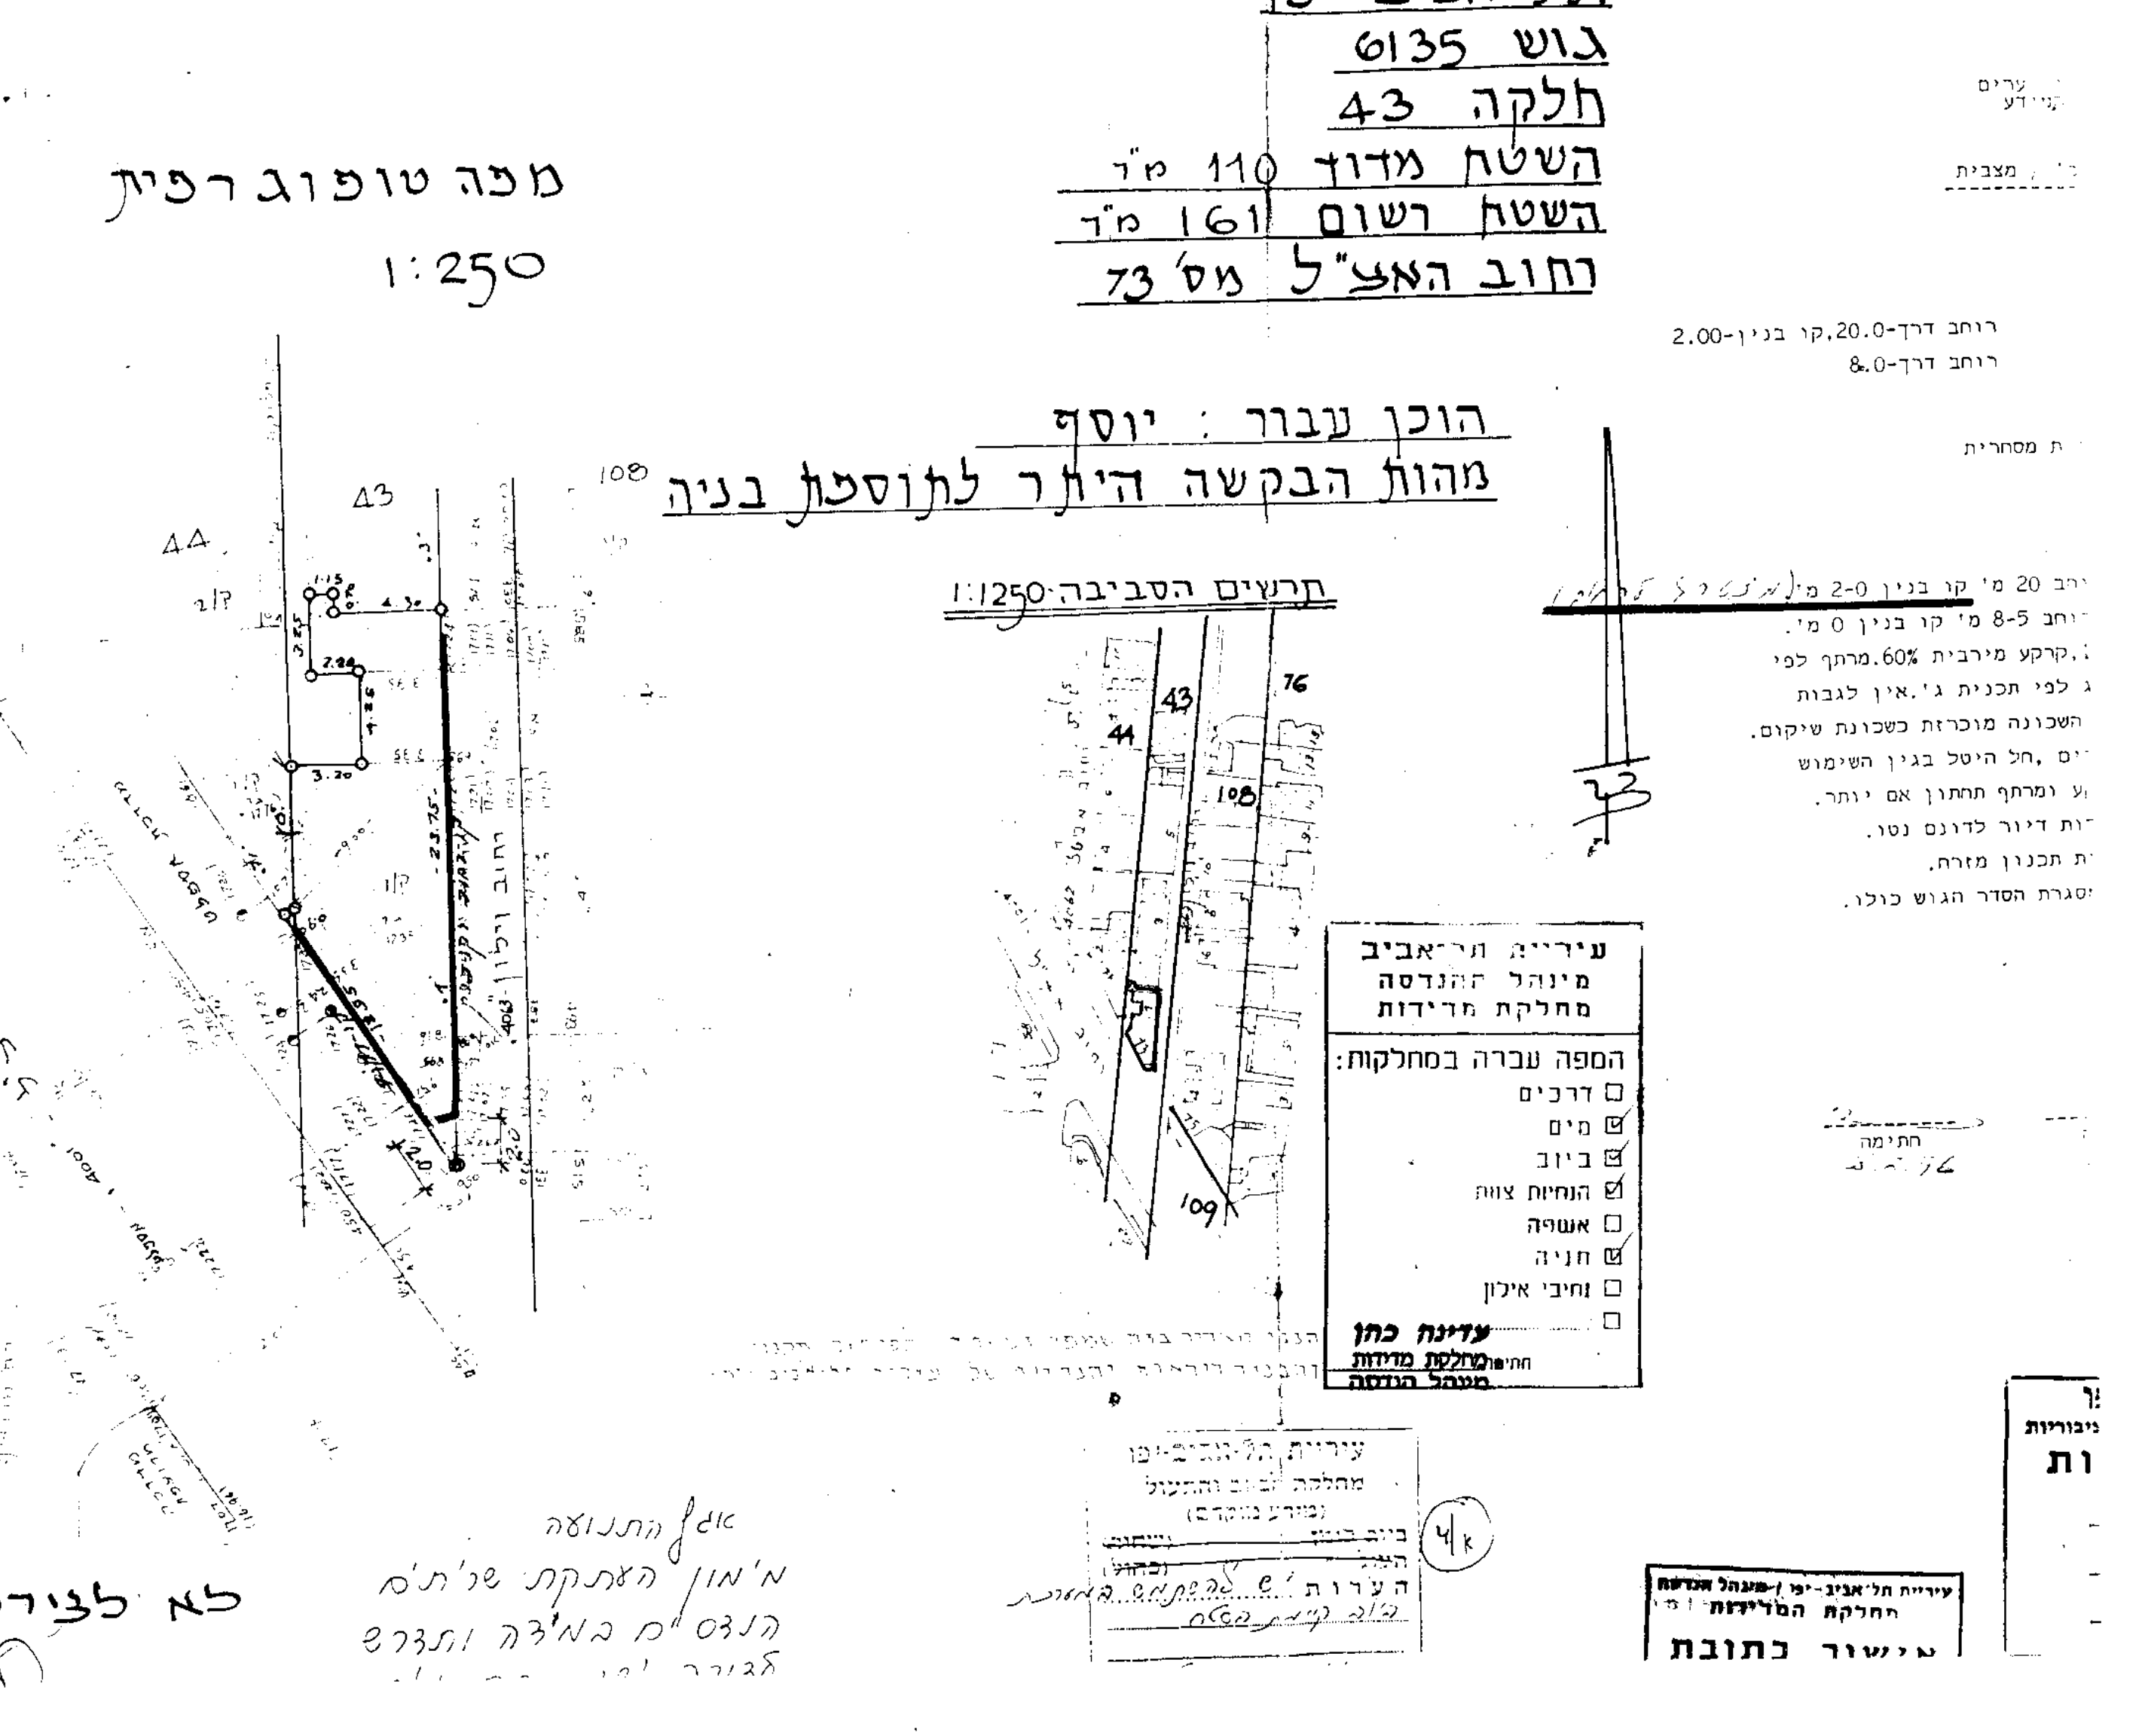

מפה טופוגרפית
1:250

תל-אביב-יפו
גוש 6135
חלקה 43
השטח מדוד 110 מ"ר
השטח רשום 161 מ"ר
רחוב האצ"ל מס' 73

הוכן עבור: יוסף
מהות הבקשה היתר לתוספת בניה

תרשים הסביבה 1:1250

לא לצרכי רישום

עיריית תל-אביב
מינהל ההנדסה
מחלקת מדידות
המפה עברה במחלקות:
☐ דרכים
☑ מים
☑ ביוב
☑ הוצאות צורה
☐ אשפה
☑ חניה
☐ נתיבי איילון

אגף התנועה
אין התנגדות

עיריית תל-אביב-יפו
אישור כתובת

עיריית תל-אביב-יפו
מינהל ההנדסה

הועדה המקומית לתכנון ולבניה תל-אביב-יפו

4001-33
96-0361

טופס השלמת פרטים

חלק א' - תאור הבקשה

שם רחוב	אצ"ל
	וילון
	קדימה
	20 20

קיים מבנה בן קומה -1
מסחרי

תוספת בקומה א.

שימוש	קיים	מוצע
קרקע	60% 66.0	106.80
	40% 44	47.20
	40% 44	
		7.70
סה"כ	140% 154	

חוק התכנון והבניה, התשכ"ה-1965
בקשה להיתר בניה או לשימוש במקרקעין

186

97-0347

4001-073

2215	43	6135	4001	ת"א

יוסף
רח' אצ"ל 73 ת"א
זבגורסקי 1468785
5221162

תוספת למבנה קיים בקומה א' בשטח 47.20 מ"ר + ממ"ד

השטחים המבוקשים לבניה בכל מפלס בנפרד

97.10	106.80				106.80
49.90	54.90	7.70		47.20	
147	161.30	7	7.70	47.20	106.80
140	154.0				

זבגורסקי 30.07.96
יוסף 30.07.96
זבגורסקי 30.07.96

נסרק

לא ניתן לאשר את המבוקש
24-12-96