

מפה טופוגרפית
1:250

תל-אביב-יפו
גוש 6135
חלקות 44.45
השטח 254 מ"ר

920094

38-92-31

92-1-92





רחוב ששון 8-10

הוכן בשביל מלחמה שלום (טרעב)
מהות הבקשה - קבלת היתר בניה

שטח דשום 225 מ"ר

לפי תכנית 2215 (טרם פורסמה למתן תוקף)
רחוב 4046 - ששון
רוחב הרח' 5-8 מ', קו בנין 0.
קו בנין צדדיים 3 מ' או קירות משותפים, לאחר 5 מ'.
גובה הבנין 3 קומות, טה"כ 140%.
תכנית קרקע מירבית 60%.
הצפיפות 10 דירות לדונם.
מרתפים לפי תכנית "ע", יציאות לגג לפי תכנית 1680.
אין לגבות היטל השבחה היות והשבחה הוכרזה כשכונת
שיקום.
יש לתאם את התכנון עם צוות מזור באגף ת.ב.ע.

תרשים הטביעה - 1:250

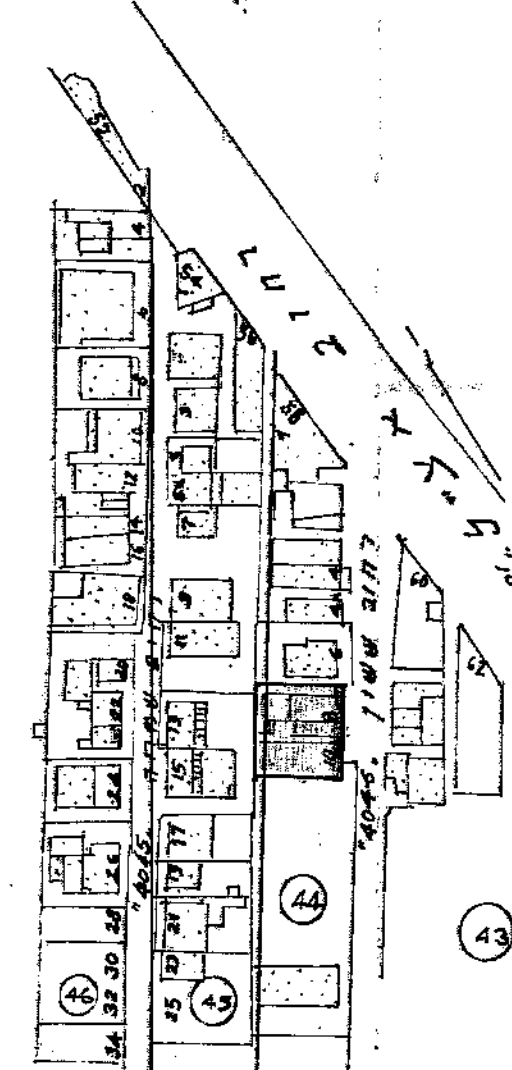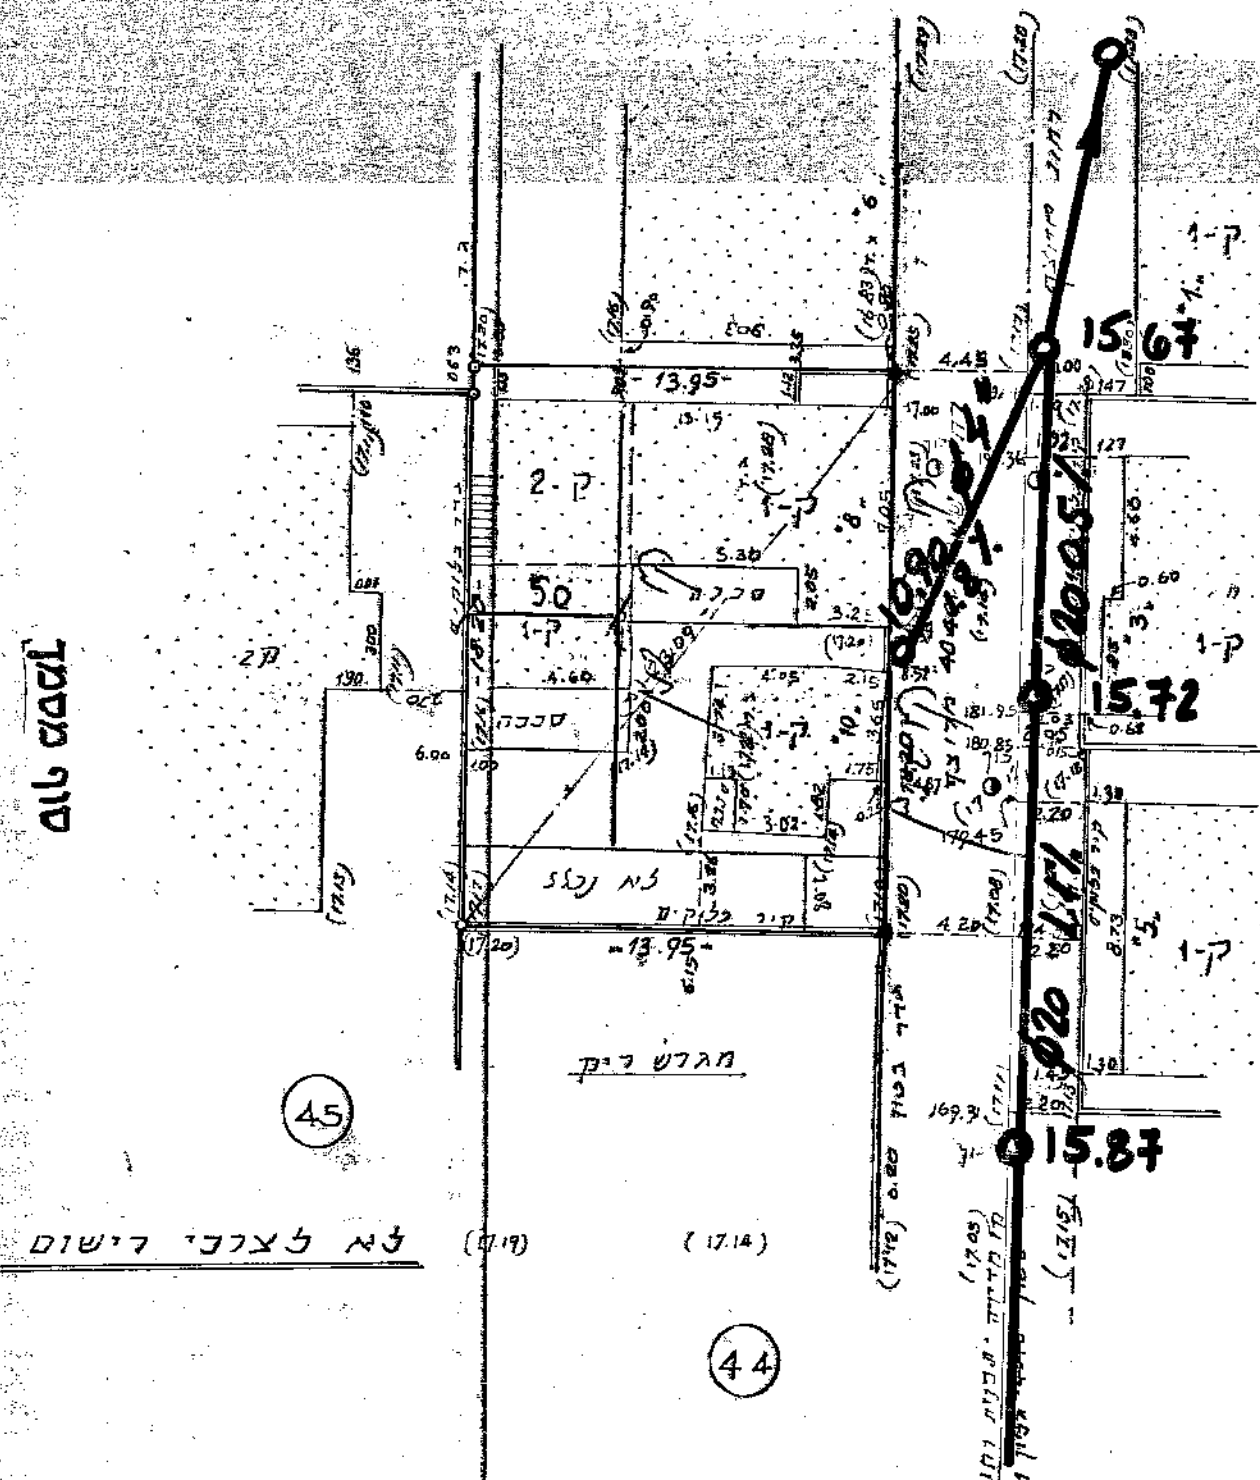

עיריית תל-אביב
מנהל ההנדסה
מחלקת מדידות

המפה עברה במחלקות:

- ☒ דרכים
- ☒ ביוט
- ☒ מים
- ☒ הנחיות צוות
- ☐ אשכול דקל

חתימה: *[Signature]*

עיריית תל-אביב-יפו
מנהל בנין והשתות / אגף עבודות עיבודיות
מחלקת מדידות

חתימה: *[Signature]*
חתימה: *[Signature]*
תאריך: 23.01.1992

שטח המסעדה (לצורך חשבון זכויות בניה)
מאוסר (לחבון) _____ מ"מ (גרפי)
מרוצף (הרצף) _____ מ"מ (גרפי)
השטח הכולל _____ מ"ר

הכני מאשר שהתכנית נעשה לפי חוק
התכנון והבניה לשינויים עיריית תל-אביב-יפו

כאן קובעת מידת הריבוע

עיריית תל-אביב-יפו
מנהל בנין והשתות / אגף עבודות עיבודיות
מחלקת מדידות

אשר: *[Signature]*
רחוב: *[Signature]*
פינת רח' *[Signature]*
תאריך: 23.01.1992

תל-אביב
6.1.1992
מורד מוסמך
278 / גשיון

לאון בהנא
משרד עבני למדידות
תכנון ופקוח בע"מ
רח' יבוצינסקי 152, תל-אביב
טל. 03-6957238

הערות:
1. הריבוע מבוטאים על גובה נ"ק 17.543
2. המספרים בטבלה מסמנים גובהים
3. המחזיקה של רחוב ששון תכנית עיריית
תל-אביב 4046/1
4. העברת גבולות החלקות - גרפית

14.1.92