

מפה טופוגרפית
1:250

תל-אביב-יפו

גוש 6135

חלקות 44.45

השטח 254 מ"ר

רחוב ששון 8-10

הוכן בשביל מלחמה שלום (שרעב)

מהות הנקשה קבלת תעודת בניה

שטח שלום 225 מ"ר

4920094

26

38-92-3

22.1.92





לפי תכנית 2215 (טרם פורסמה למתן תוקף)
רחוב 4046 - ששון
רוחב הרח' 5-8 מ', קו בנין 0.
קו בנין צדדיים 3 מ' או קירות משותפים, לאחר 5 מ'.
גובה הבנין 3 קומות, טה"כ 140%.
תכנית קרקע מירבית 60%.
הצפיפות 10 דירות לדונם.
מרתפים לפי תכנית "ע", יציאות לגג לפי תכנית 1680.
אין לגבות היטל השבחה היות והשכונה הוכרזה כשכונת שיקום.
יש לתאם את התכנון עם צוות מזרח באגף ת.ב.ע.

מיושג אל אלו

תרשים הסביבה - 1:1250

למשך אום

איכות נמוכה

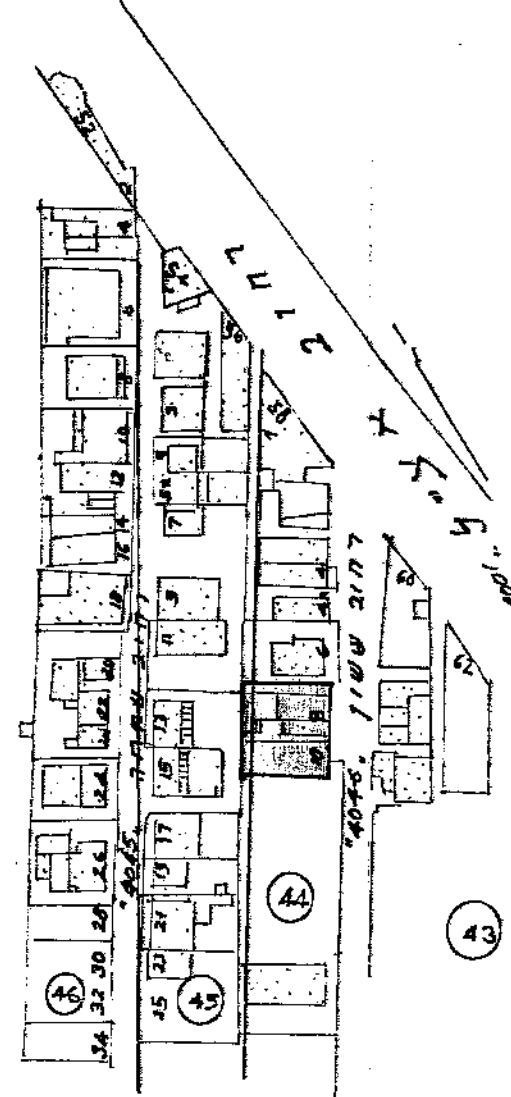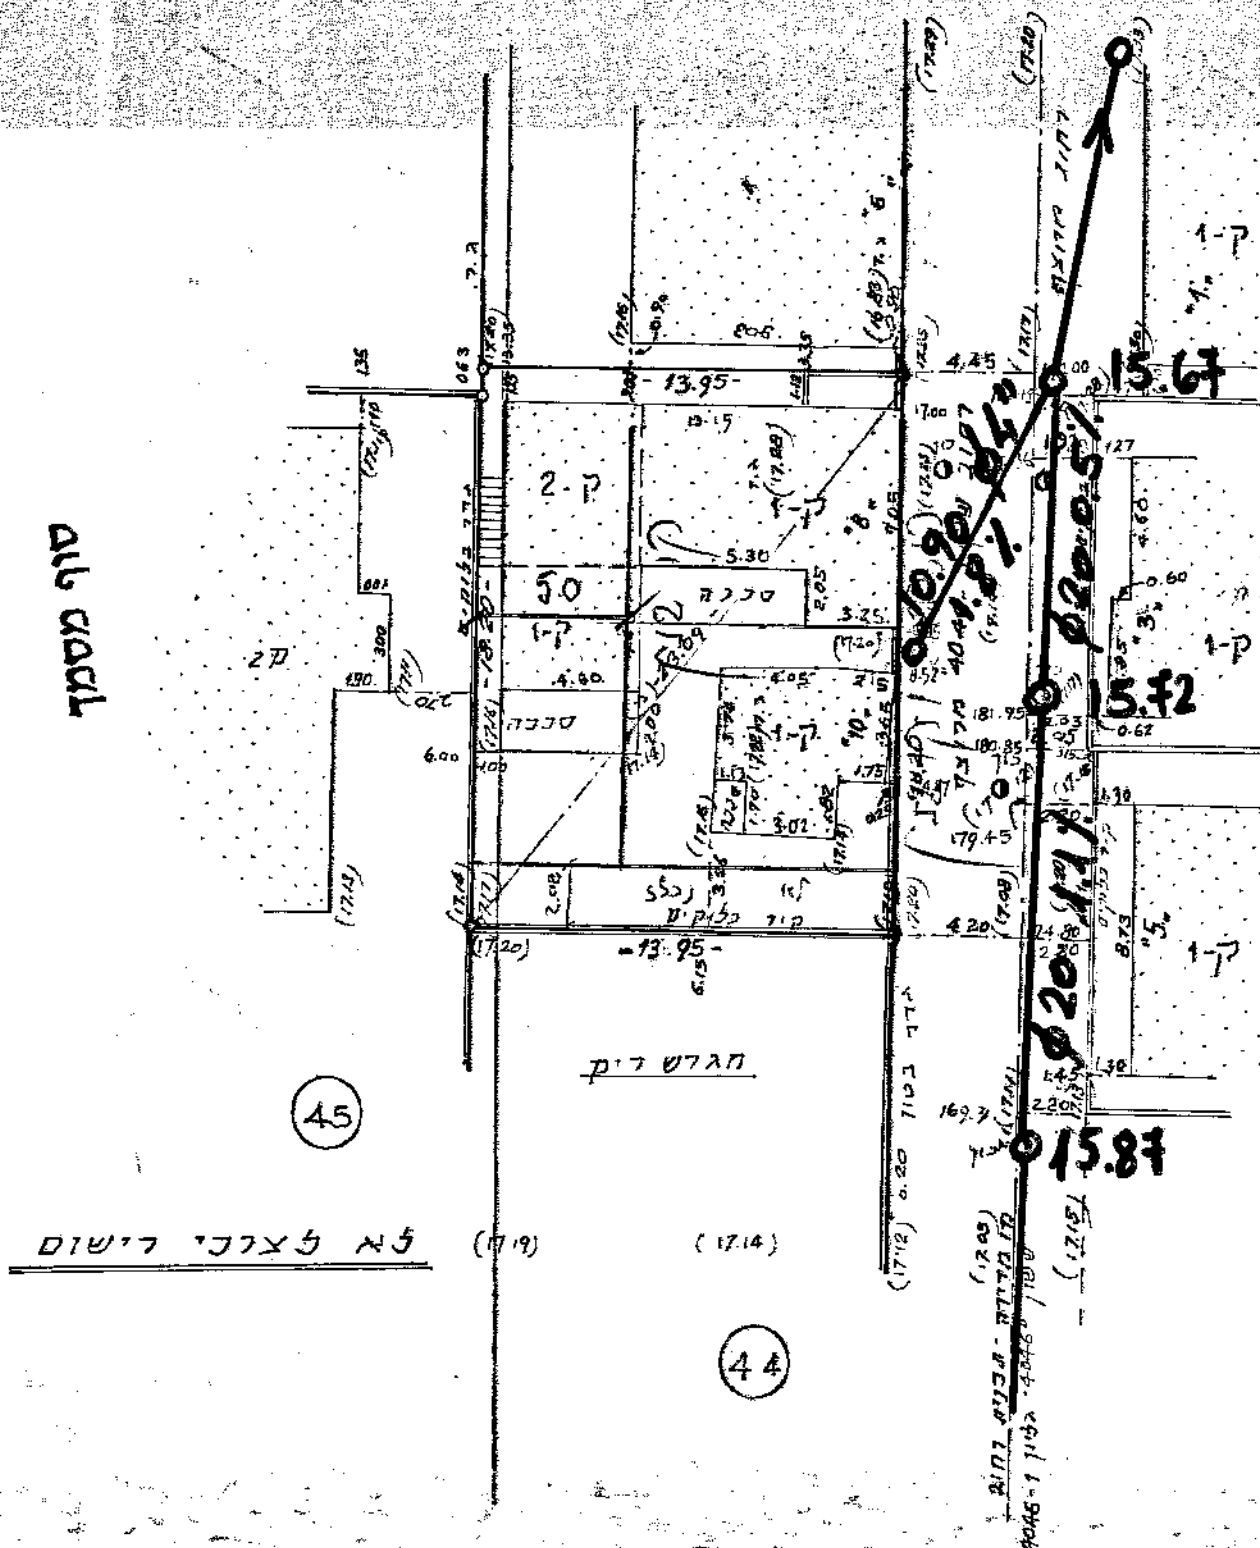

עיריית תל-אביב-יפו
מינהל בינוי ותשתית / אגף עבודות ציבוריות
סחלקת מדידות
חתימה (י"מ) 13.01.1992
חתימה
תאריך 13.01.1992
שטח הפקעה (לצורך חשבוש זכויות בניה)
ת"ש (ת"ב) מ"מ (גרפי)
מ"מ (גרפי) מ"מ (גרפי)
מ"מ (גרפי) מ"מ (גרפי)

עיריית תל-אביב-יפו
מינהל הריסות
מחלקת מדידות
המפה עברה במחלקות:
☒ דרכים
☒ ביוג
☒ מים
☒ הנחיות צוות
☐ חתומה חתומה
חתימה חתומה

עיריית תל-אביב-יפו
מינהל הריסות
מחלקת מדידות
מ"מ (גרפי) מ"מ (גרפי)
מ"מ (גרפי) מ"מ (גרפי)
מ"מ (גרפי) מ"מ (גרפי)
מ"מ (גרפי) מ"מ (גרפי)

תל-אביב 6.1.1992
מורד מוסמך
278
(לכתוב)

לאון כהנא
מושרד טכני למדידות
תכנון ופקוח בע"מ
רח' ז'בוטינסקי 152, תל-אביב
טל 6957234-03

הערות
1. ההגבלות מבוססים על גובה נ"ק 17.549-187
2. המספרים בסוגריים חסומים גובהים
3. המחזיקה של רחוב ששון תכנית עירית
י"מ-אביב 4046/1
4. העברת גבולות החלקות - גרפית

14.1.92 37.3