עירית תל־אביב־יפו
מינהל ההנדסה
6 -01- 1986
יתקבל באגף הרשוי

תכנית זו מתאימה לדרישות
קובץ התקנות והתנאים הכלליים
להיתר בניה ותעודת גמר.
תאריך 24.3.86 חתימה

חוק התכנון והבניה, התשכ"ה—1965
תקנות התכנון והבניה (בקשה להיתר, תנאיו ואגרות), התש"ל—1970

טופס 2 (תקנה 2(א))

מיפרט

הוועדה המקומית לתכנון ולבניה
תל־אביב־יפו

תיק מס' 15736

תיאור הבנין

1. המקום	הרחוב	מס'	גוש	חלקה	תכנית מיתאר מקומית או מפורטת	מגרש
שכונת התקוה	ששון	14	6135	44 (חלק)		

	השם	המען	מס' הטלפון
2. המבקש	שרעבי רפי ורונית	ש. התקוה רח' ששון 14	
3. בעל הזכות בנכס	—״—	—״—	
4. עורך הבקשה*	כץ - פרחי אדריכלים	רח. שלמה המלך 15 ת.א.	239997
5. האחראי לביצוע השלד	י. לגני מהנדס	רח' ריבלין 28 ת.א.	737060

6. אזור הבניה: ■ מגורים ☐ מסחר ☐ תעשיה ☐ בנין ציבורי ☐ חקלאי ☐ ....

7. שטח המגרש/החלקה: 126.14 מ"ר. אחוז הבניה המותר: 60% ....

8. מטרת הבנין: ● מגורים ☐ הארחה ☐ עסקים ☐ תעשיה ☐ חקלאי ☐ ציבורי ☐ ....

9. מהות הבנין ותכליתו: בית מגורים חדש במקום בית קיים במסגרת פרויקט בנה ביתך

10. תיאור העבודה המוצעת: ☒ בנין חדש ☐ תוספת לבנין קיים ☐ הריסה ☐ תיקונים ☐ שינוי בבנין ☐ ....
☐ שינוי בשימוש ממטרה: .... למטרה: ....

11. האם הבניה היא בעד: ☐ משרד ממשלתי ☐ הרשות המקומית ☐ הסוכנות היהודית

היקף הבניה

קומה	קיים	מוצע	סך הכל	אחוז הבניה	מגורים בדירות עד 45 מ"ר	עד 65 מ"ר	עד 90 מ"ר	עד 100 מ"ר	100 מ"ר	עסק: הארחה וכו'	ציבורי	שונות	מס' הדרים קיים	מס' הדרים מוצע
1	2	3	4	5	6	7	8	9	10	11	12	13	14	15
מרתף														
הכניסה הקובעת לבנין			~~54.12~~ 54.12	42.9										
א			62.76	49.7										
ב			22.93	18.1										
ג														
ד														
ה														
ו														
ז														
חדרי מדרגות														
בניני עזר														
סך הכל			139.81	110.7										

הנפח המוצע: של הבנין העיקרי .... מ"ק. של בנין עזר .... מ"ק.

מינהל ההנדסה
מחלקת פקוח על הבניה
חבל מזרח
תכנית כס' 200
3.01.86
נבדק ביום
③

הערות מח אדריכלות
מיום 12.1.86

שימוש בבנין — הבניה המוצעת למגורים

דירות בנות:	שטח כל דירה מ"ר	מספר דירות מכל סוג	כל הדירות	רצפות חדרי דיור בלבד, ומרפסות מקורות	רצפות חדרי שירות ופרוזדורים בלבד	רצפות של מרפסות בלתי מקורות	מספר החדרים:				
1	2	3	4	5	6	7	8	9	10	11	12
חדר אחד	ראה: תעריים סכימתי של שטחי הבניה בכל קומה, המציין מספר החדרים ושטח כל דירה.										
2 חדרים											
3 חדרים											
4 חדרים							1	1	2	2	3
5 חדרים											
6 חדרים											
7 חדרים ויותר											
חדרים נוספים לדירות קיימות											
בניני עזר											
סך הכל		1									

נסרק

1/4 14

2. הבניה הקיימת והמוצעת לתעשיה ולמלאכה

פרטים	קיים שטח	גובה	נפח	% הבניה	מוצע שטח	גובה	נפח	% הבניה	סך הכל שטח	נפח	% הבניה	הערות
1	2	3	4	5	6	7	8	9	10	11	12	13
אולמי מלאכה												
משרדים												
חדרי שירות												
סככות												
בניני עזר												
הדרי מדרגות												
סך הכל												

3. הבניה המוצעת למטרות אחרות (הארחה, עסקים ומשרדים, בניני ציבור, בניני משק חקלאי, מכסות שונות).

השימוש המיועד	סך הכל מ"ר	שטחים — מ"ר מזה חדרים	אולמות	אחסנה	חדרי שירות	בנפח חדרים, אחדרים ובו'	
1	2	3	4	5	6	7	8
בניני עזר (למעט אלה המפורטים ב־ג(4))							

4. חלקי בנין אחרים — הבניה המוצעת. שטח במ"ר.

הדרי מדרגות	מרפסות שלא נכללו לעיל	מעליות	הדרי הסקה	הדרי כביסה	מקלטים	קומת עמודים מפולשת	מחסנים	מוסכים	בניני עזר נוספים	סך הכל
1	2	3	4	5	6	7	8	9	10	11
					8.64					

ד. חומר הבניה

קירות חיצונים	☐ בטון מזוין	☐ לבני בטון או בלוקים	☐ לבני סיליקט	☐ לבנים שרופות	☐ אבן טבעית
	☐ אבן מלאכותית	☐ איטונג	☐ עץ	☐ ברזל	☐ חמרים אחרים
תקרות	☐ בטון מזוין	☐ עץ	☐ חומר אחר		
גג	☐ בטון מזוין	☐ רעפים	☐ אסבסט	☐ פח	☐ חומר אחר

ה. גדרות: קיימות.................... מ"א מוצעות.................... מ"א

ו. מקרא

🟦 בטון או בטון מזוין	☐ אבן	🟩 רעפים עץ	▨ קיים
🟥 בלוקים או לבנים מבטון	☐ סיליקט או לבנים אדומות	☐ חומר אחר	☐ להריסה

הערות: ....

הנני מאשר כי הנתונים הנ"ל נכונים

תאריך 31.12.85 חתימת המבקש רפי שרעבי שרעבי רונית חתימת עורך הבקשה*

התימת האחראי לביצוע השלד התימת בעל הזכות בנכס רפי שרעבי שרעבי רונית

לשימוש הוועדה המקומית בלבד	מס' ההיתר	תאריך ההיתר	תאריך התחלת הבניה	תאריך גמר הבניה

אישורים של רשויות חוץ:

התימת הוועדה המקומית

* ד"ו מספר עורכי בקשה, כאמור בתקנה 2ה'. יבוא במקום כל אלה הראשון שברשימת עורכי הבקשה, כאמור בטופס 1.

ד.ב.ר-ה גלופה

תרשים הסביבה
1:1250

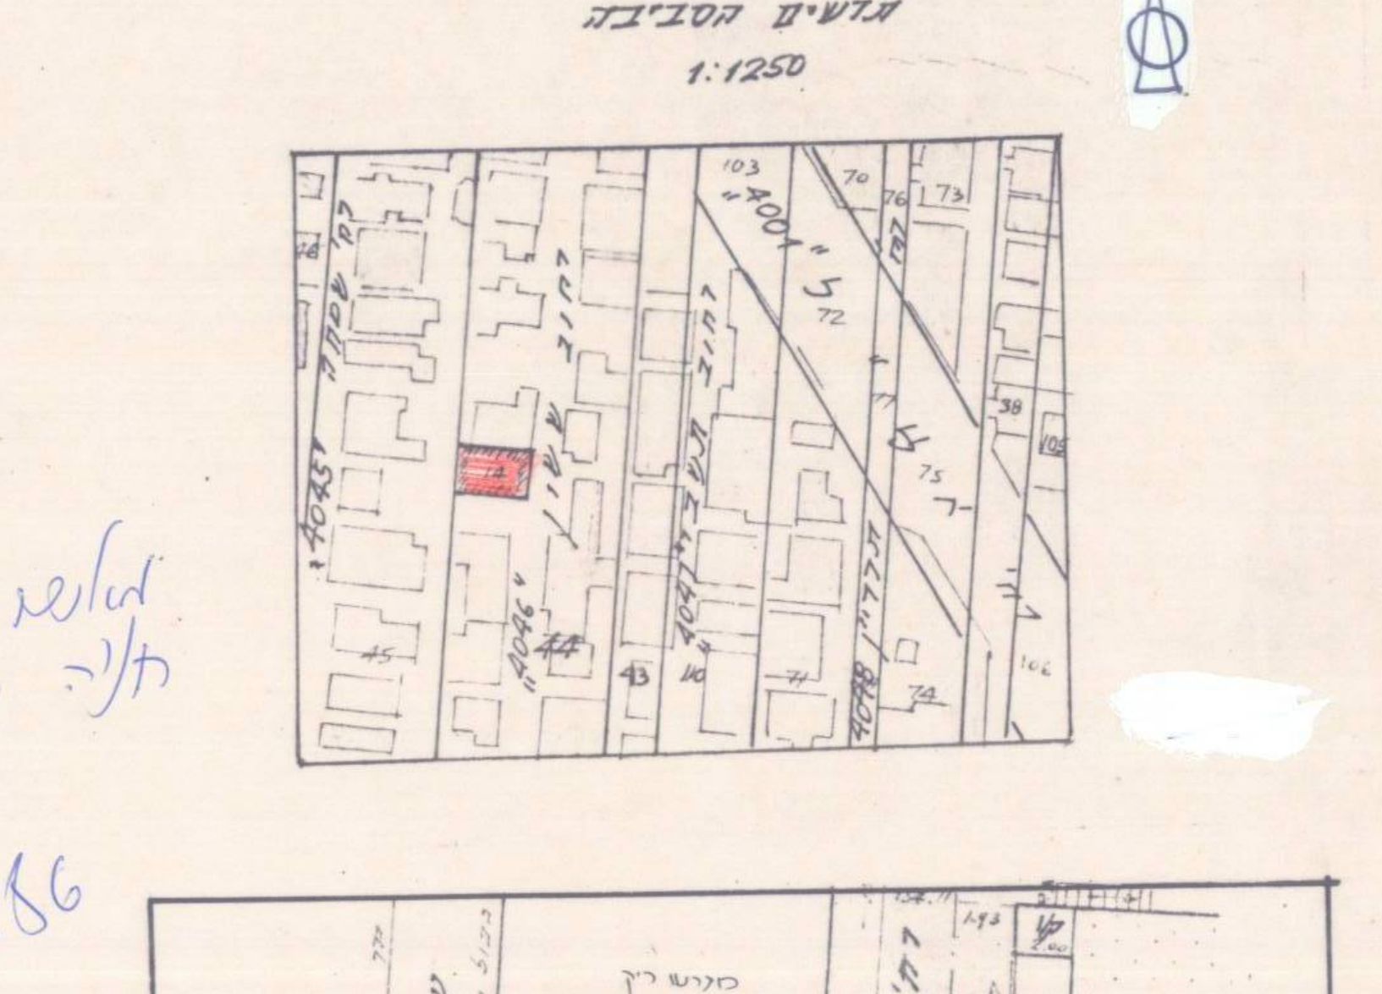

שלושה מקו
אחת
14.3.86

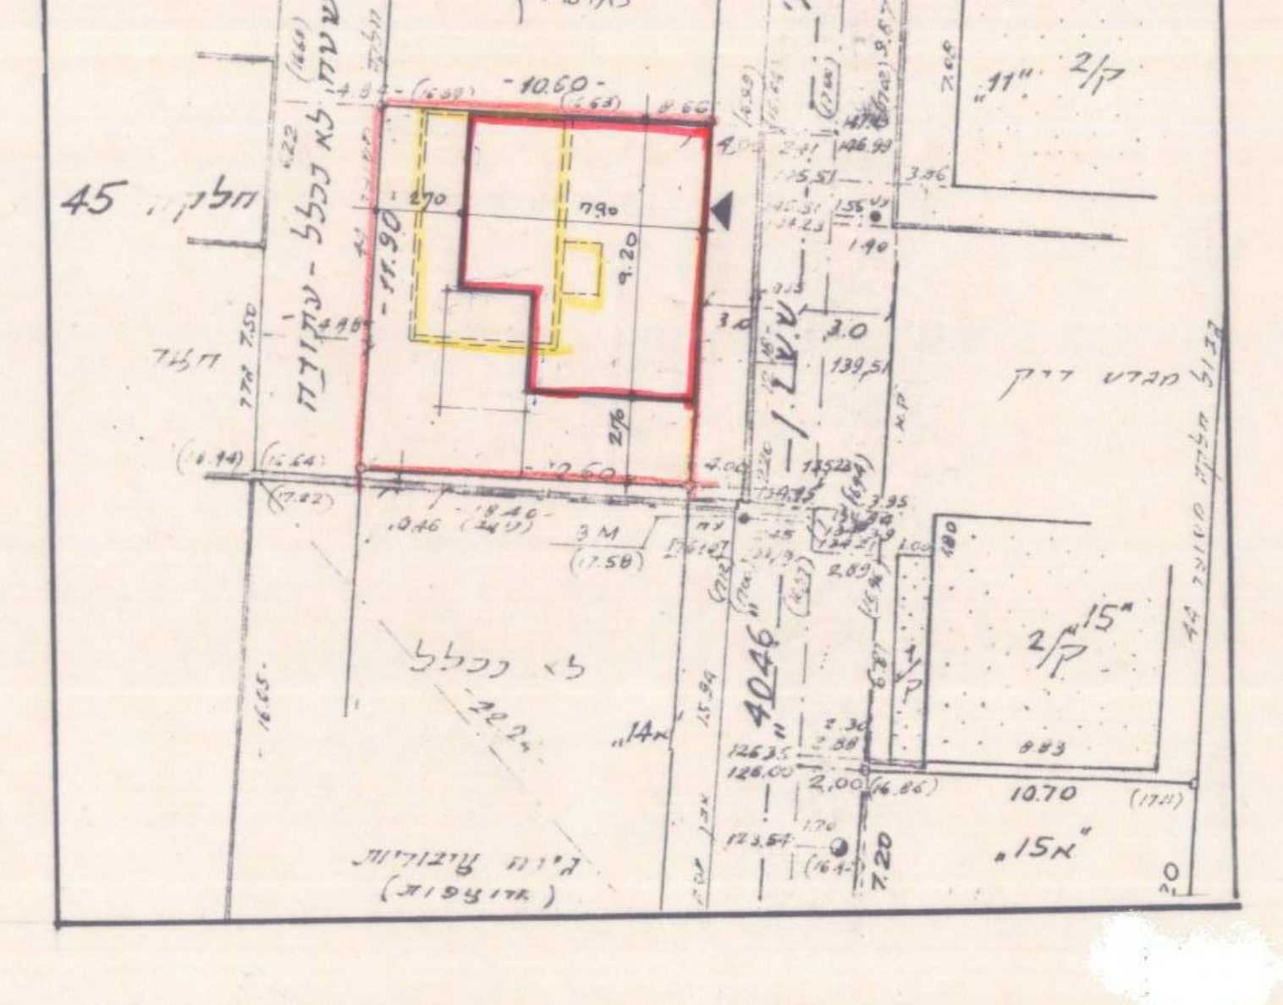

מגרש ריק
חלקה 45
שטח לא נכלל - עקודה
10.60
11.90
7.90
9.20
3.0
40.46
מגרש ריק
לא נכלל
15״
14״
15א
גינה ציבורית

תרשים המגרש 1:250

2/ שרעבי ששון 14

חשוב שטח:

ק. קרקע:

7.90 X 9.20 = 72.68
1: 3.10 X 2.10 = 6.51
2: 2.40 X 3.60 = 8.64 מקלט
3: $\frac{2.20 \times 3.10}{2}$ = 3.41 ½ מדרגה
סה הורדות 18.56
סה שטח 54.12 מ"ר

ק. עליונה:

9.20 x 7.90 = 72.68
1: 3.10 X 2.10 = 6.51
2: $\frac{2.20 \times 3.10}{2}$ = 3.41 ½ מדרגה
סה הורדות 9.92
סה שטח 62.76 מ"ר

חדר בגג רעפים:

6.10 x 3.20 = 19.52
$\frac{2.20 \times 3.10}{2}$ = 3.41 ½ מדרגה
סה שטח 22.93 מ"ר.

עירית תל-אביב-יפו / מנהל הנדסה / אגף הרישוי
אשור מס' 69/86
נתן אשור לכלי אשפה במקום ובמבנה שצויינו בתכנית בתנאי:
1) מתקן כלי אשפה יבנה בצורת ארון קיר בעל 4 דלתות ברזל הנושאים מיכלים פלסטיים של 76 ליטר, עם מכסה צמוד מדגם מאושר על ידי אגף התברואה.
2) ברז מים ובריכה ייקבעו החל ממתקן בעל 2 כלי אשפה ויותר והם יחוברו להספקת המים הכללית ולרשת הביוב של הבית.
3) ....
בכל מקרה של שינויים בתכנית הבניה יש לקבל אישור מחדש מאגף הרישוי על סוג, כמות, צורה ומספר כלי האשפה.
תאריך .... התימה ....
2 - מרץ 1986
לאחר גמר בנית הבנין, נא להתקשר עם מדור תכנון מתקנים במנהל ההנדסה אגף הרישוי לשם בדיקת התנאים הנ"ל.
רק לאחר ביצוע התנאים - נוכל לשחרר את הפקדון.

אין להשתמש בבטונדה
לפחי אשפה
ואין לפתוח שערים
ודלתות כלפי מדרכה
ציבורית

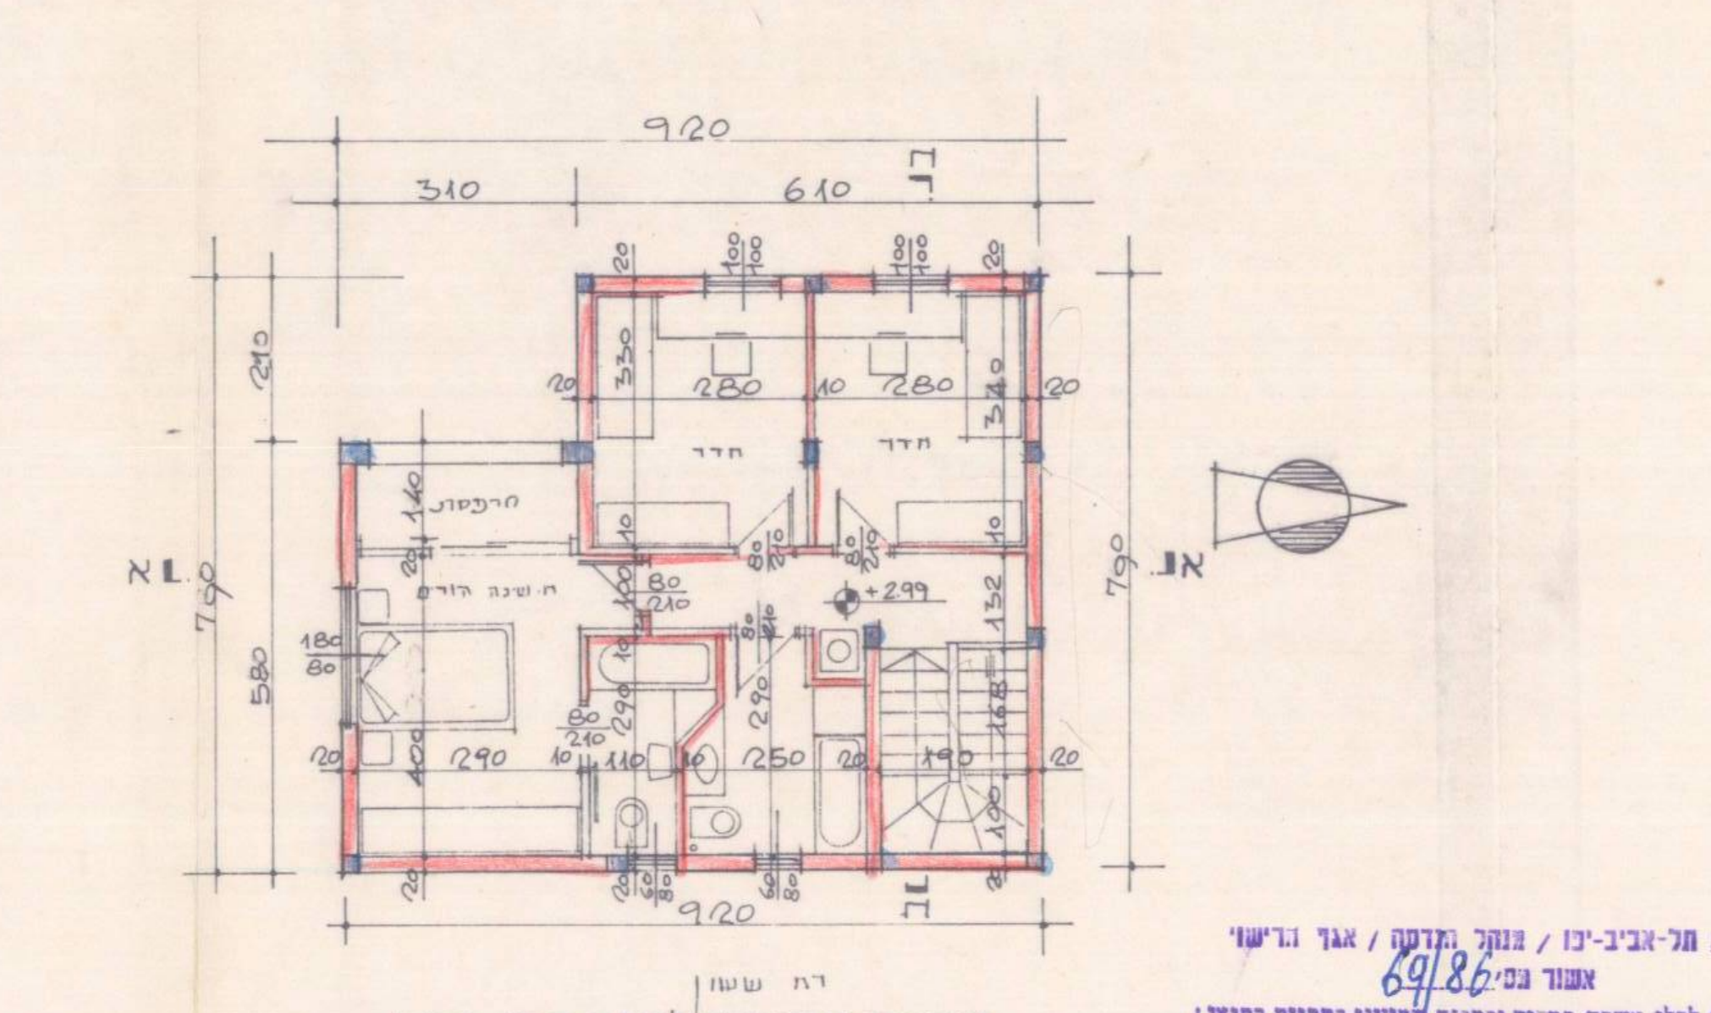

920
310
610
790
280
חדר
חדר
הורים
+2.99
250
290
רח׳ ששון

תכנית קומה עליונה קנ.מ-1:100

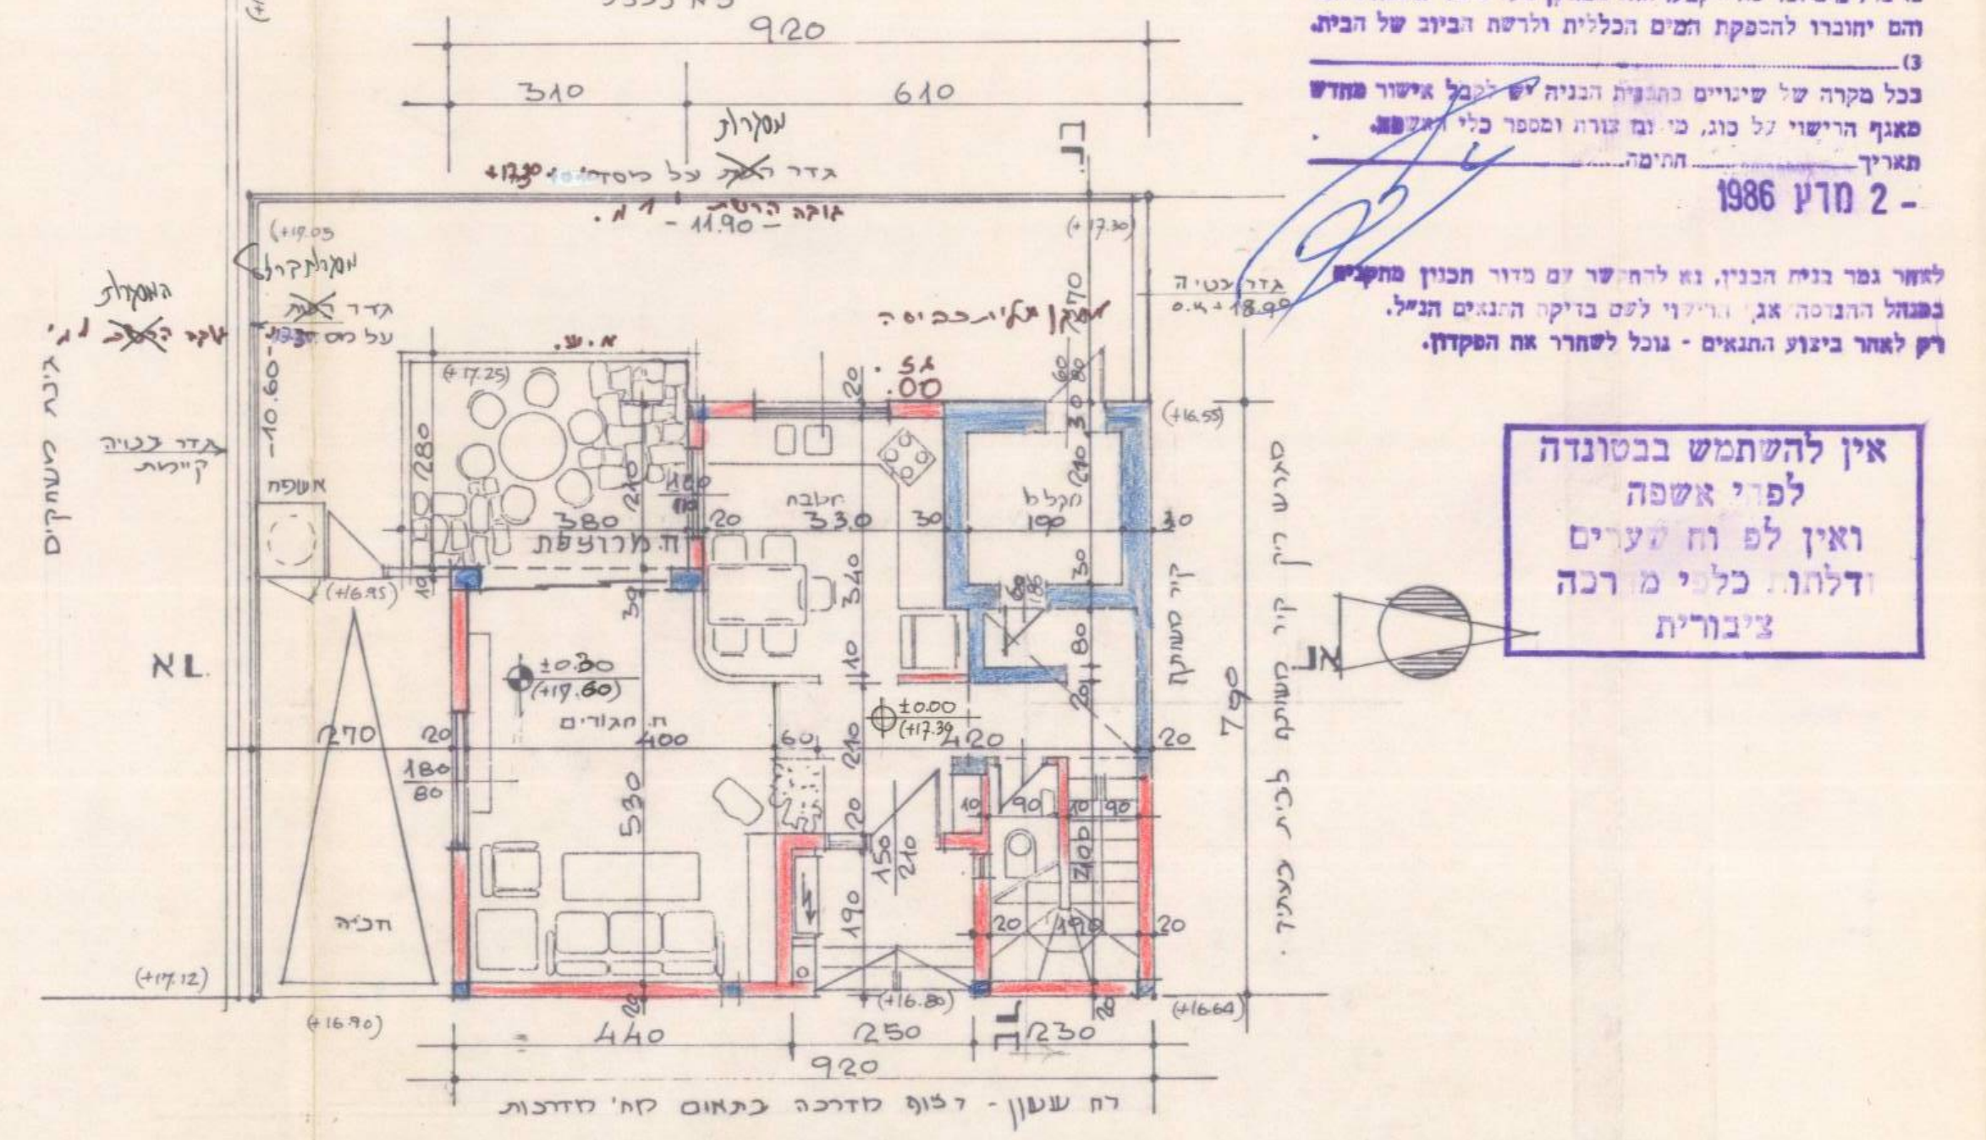

לא נכלל
920
310
610
מסגרות
גדר
ח. אוכל
מטבח
מקלט
330
190
ח. מגורים
590
440
250
±0.00
(+17.30)
790
קיר משותף
מגרש ריק
רח׳ ששון - דלת מדרכה כנתאם לקו׳ מדרכה

תכנית קומת קרקע קנ.מ-1:100

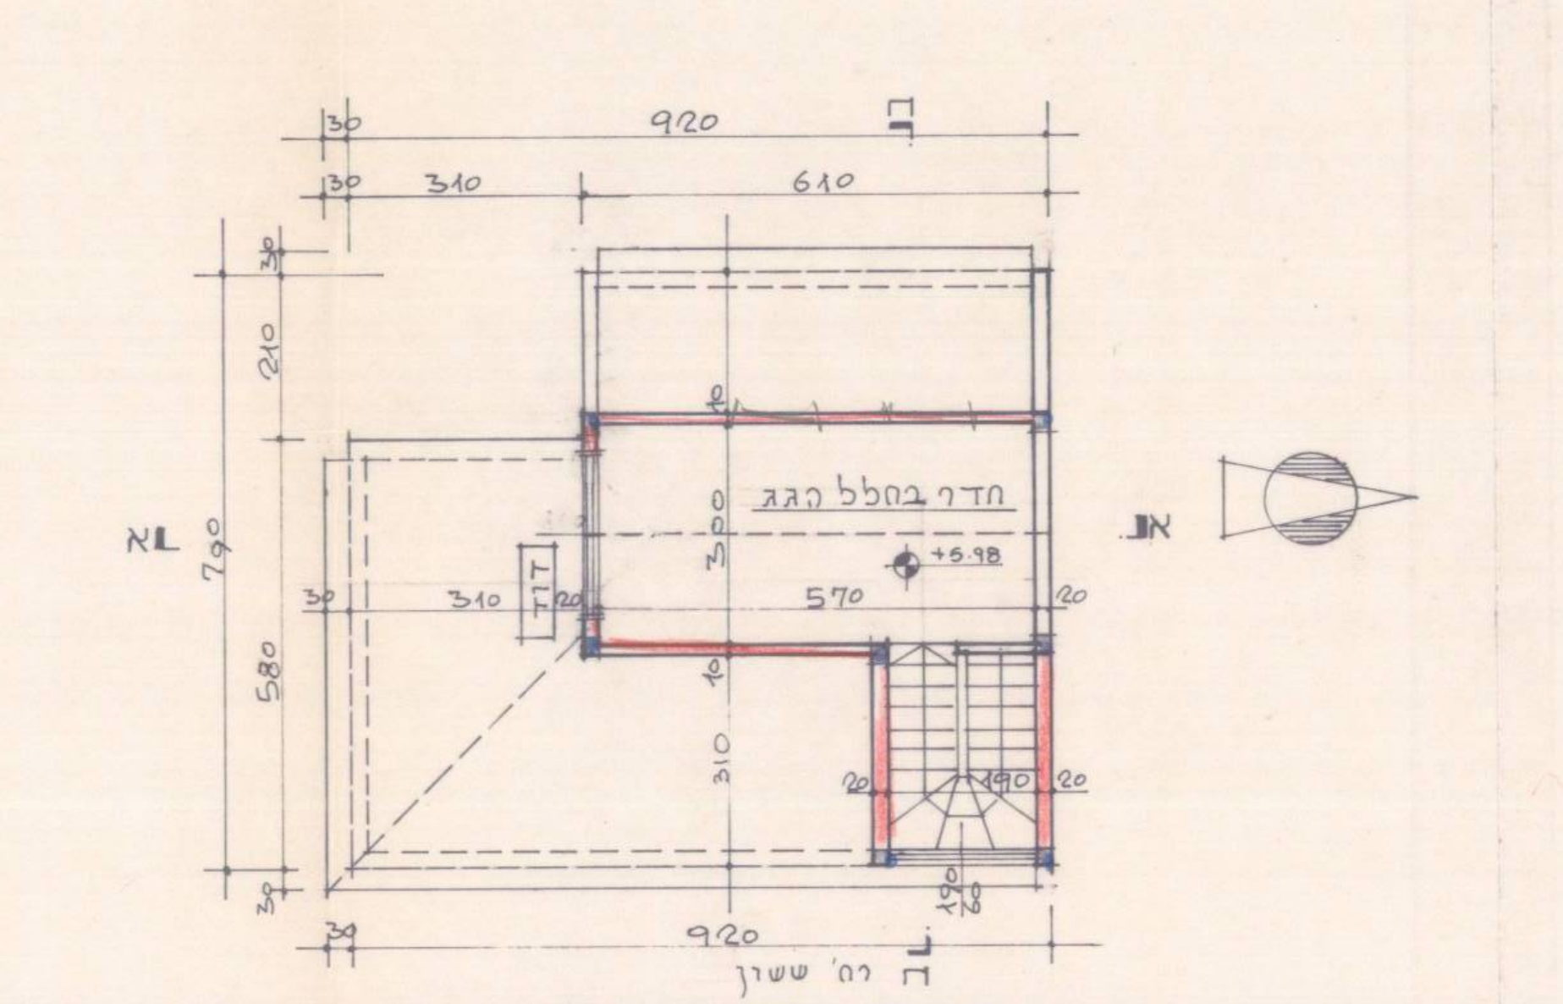

920
310
610
790
580
חדר בחלל הגג
570
+5.98
רח' ששון

תכנית עלית הגג קנ.מ-1:100

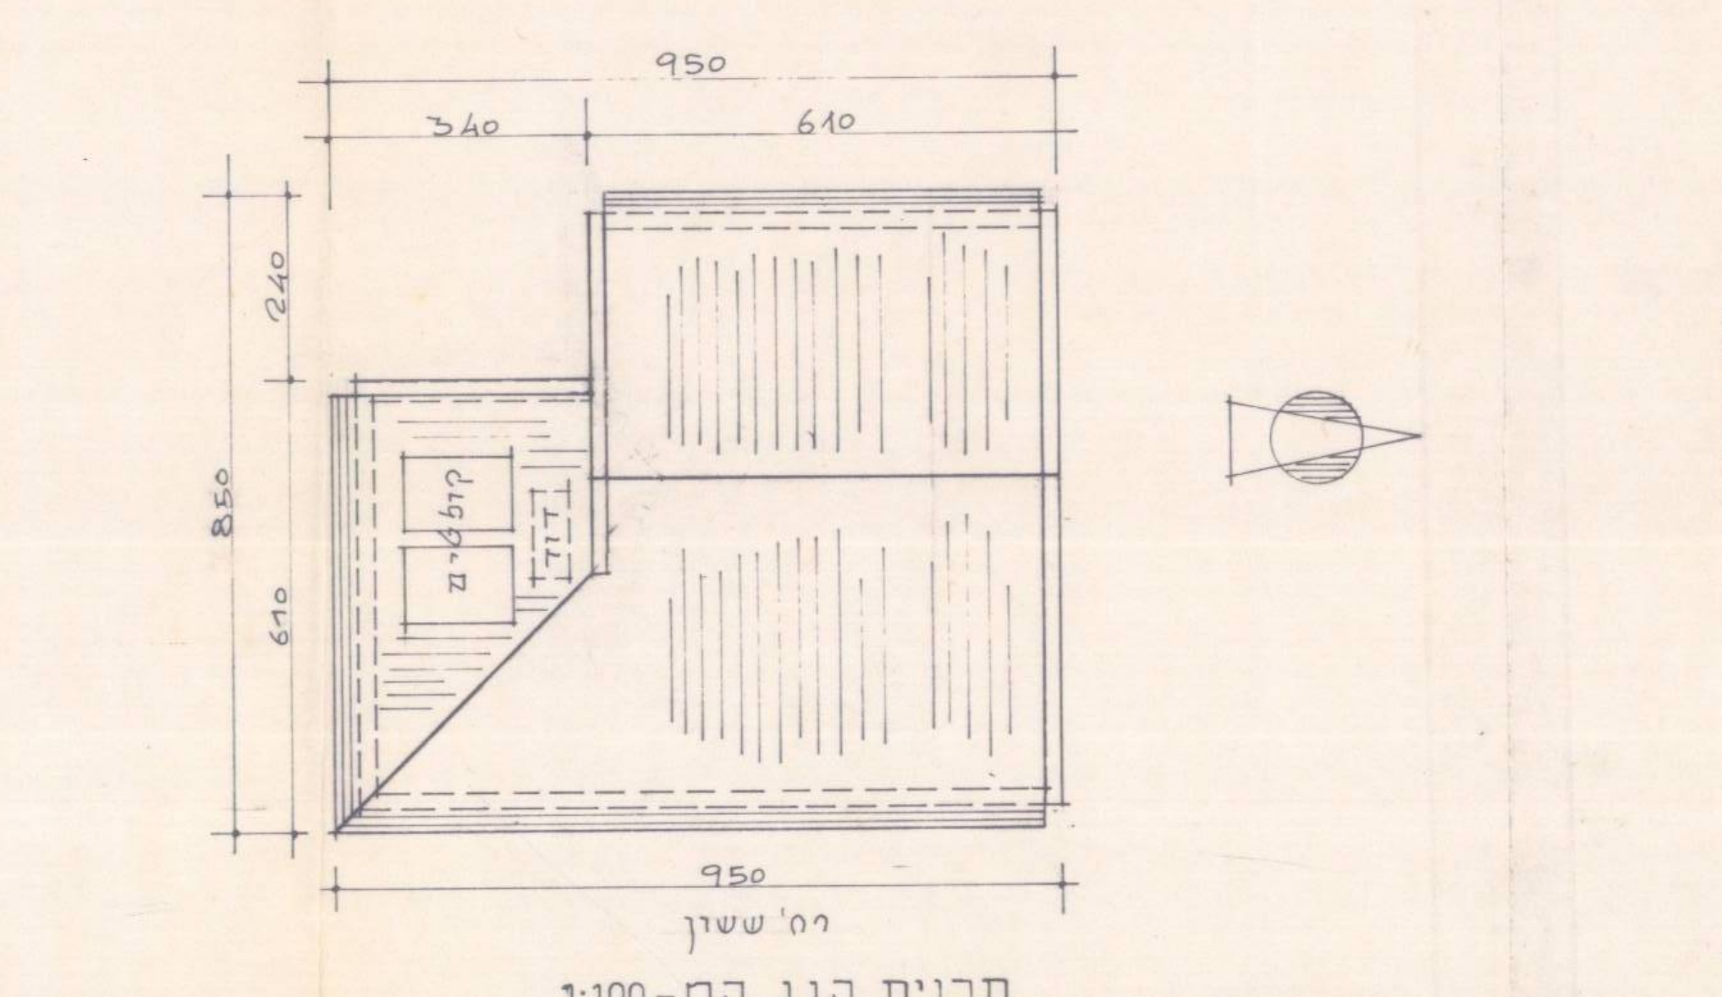

950
340
610
850
670
קולטים
דוד
רח' ששון

תכנית הגג קנ.מ-1:100

שרעבי רח' ששון 14

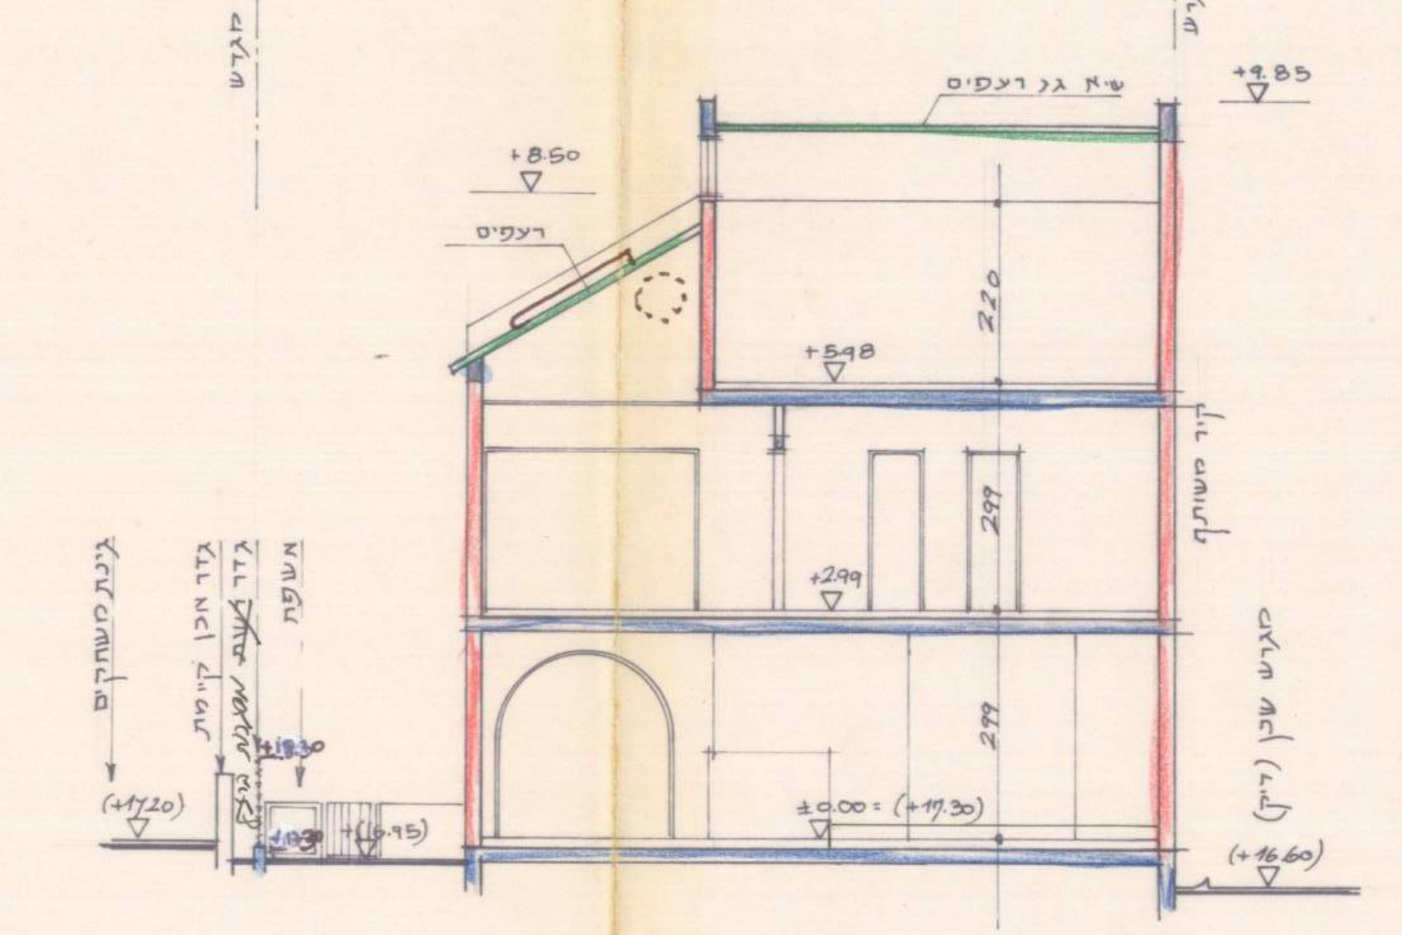

+9.85
+8.50
רעפים
גג רעפים
220
+5.98
299
+2.99
299
±0.00 (+17.30)
(+16.60)
גבול מגרש
קיר משותף

חתך א־א 1:100

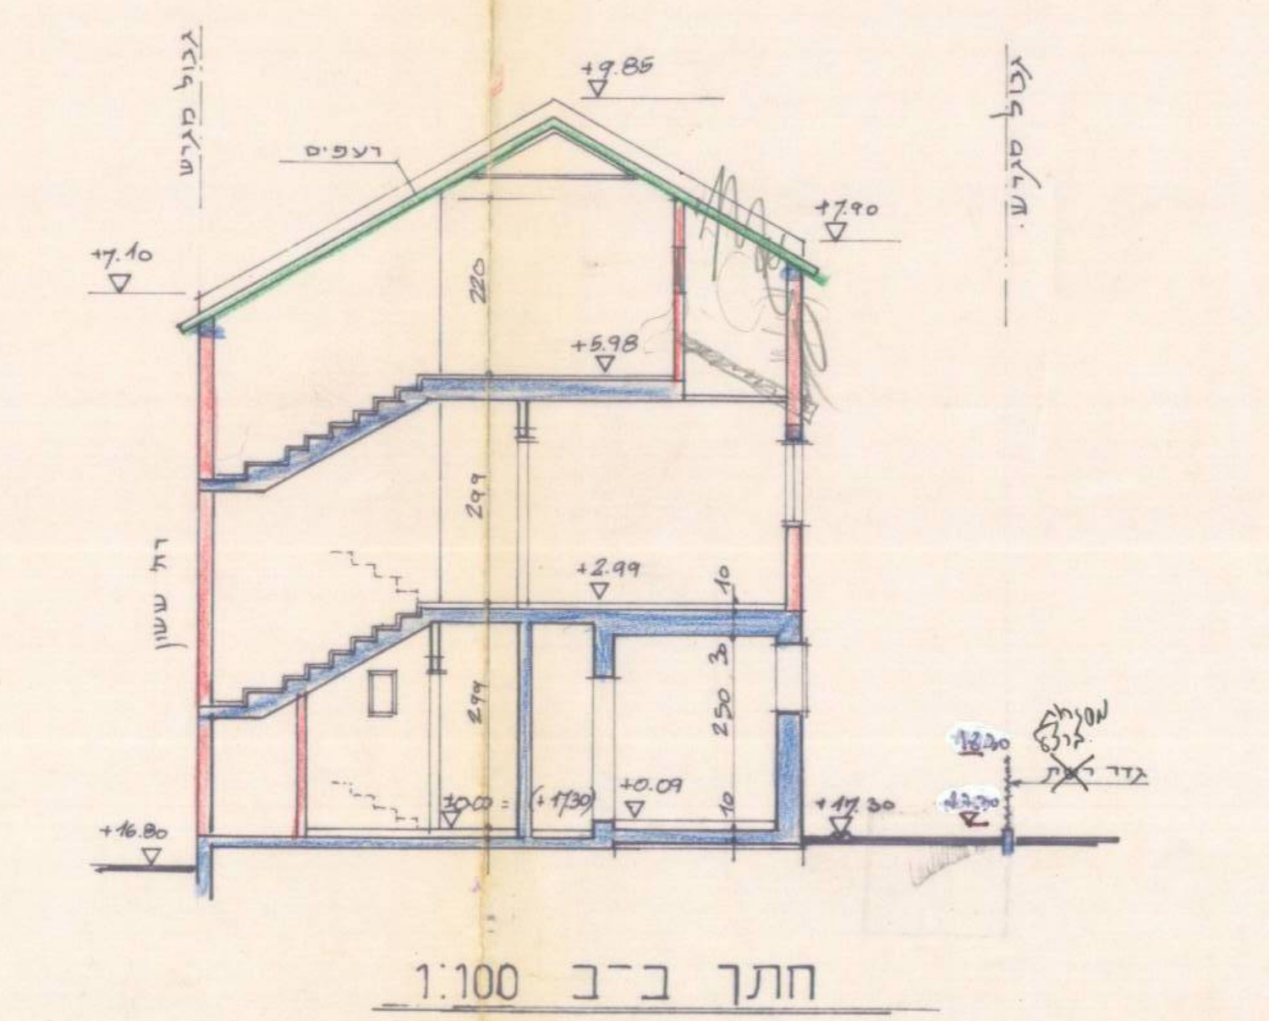

+9.85
רעפים
+7.90
+7.10
+5.98
+2.99
±0.00
+17.30
רח' ששון

חתך ב־ב 1:100

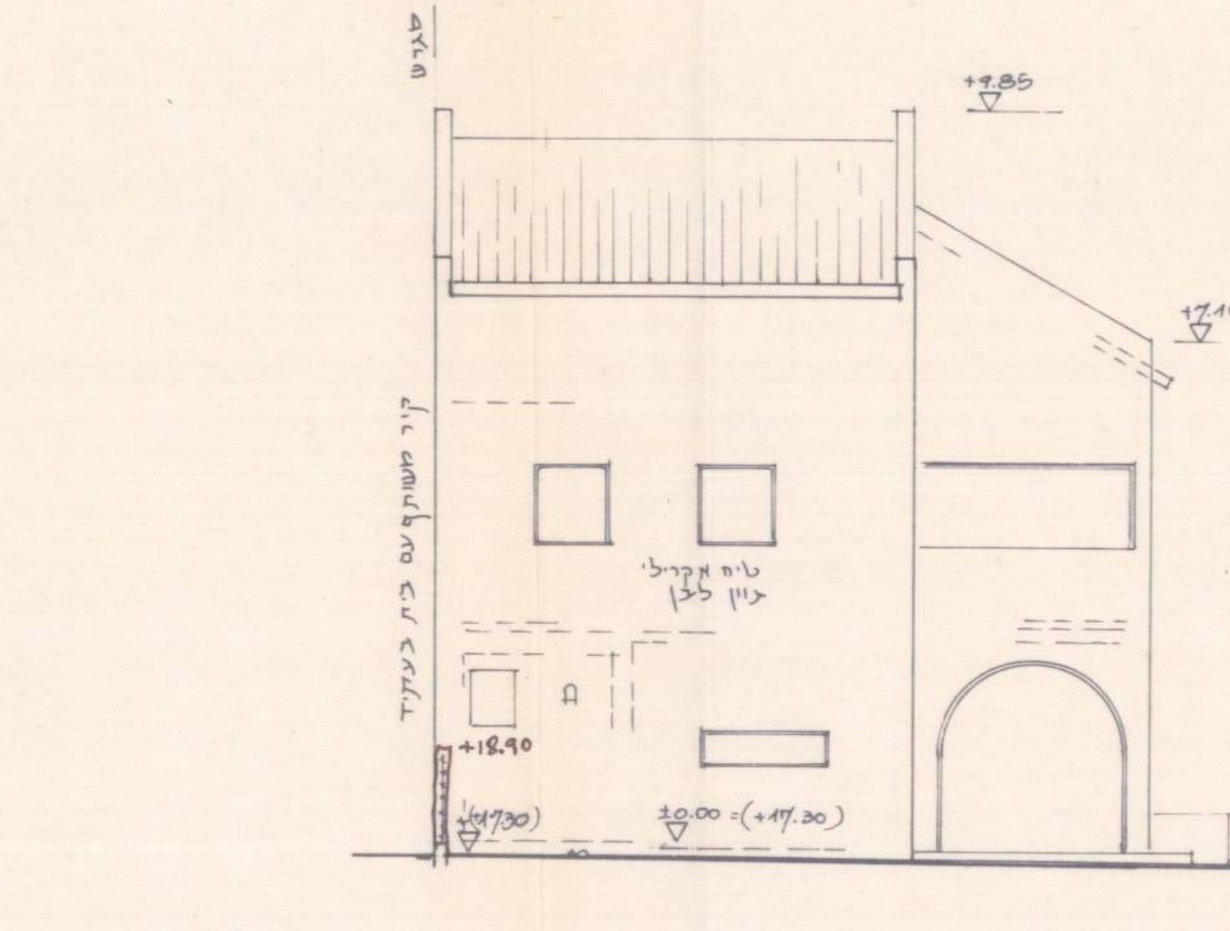

גבול מגרש
+9.85
+7.10
טיח אקרלי גוון לבן
+18.90
±0.00 (+17.30)
קיר משותף עם בית שכן בעתיד

ח. מערבית 1:100

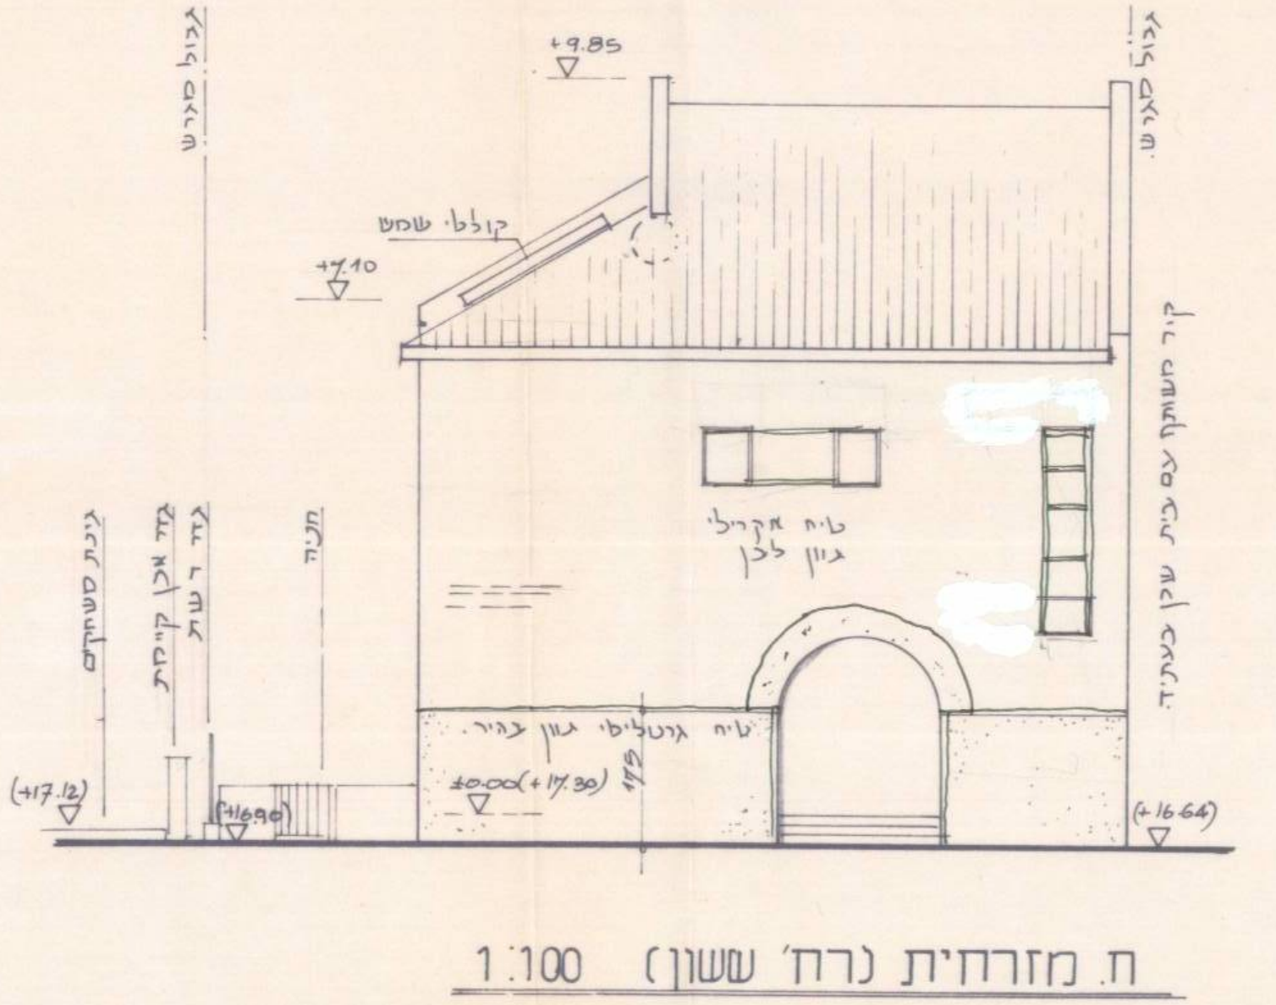

+9.85
+7.10
קולטי שמש
טיח אקרלי גוון לבן
טיח גרנוליט גוון בהיר
±0.00 (+17.30)
(+16.66)

ח. מזרחית (רח' ששון) 1:100

3/4 שרעבי ששון 14

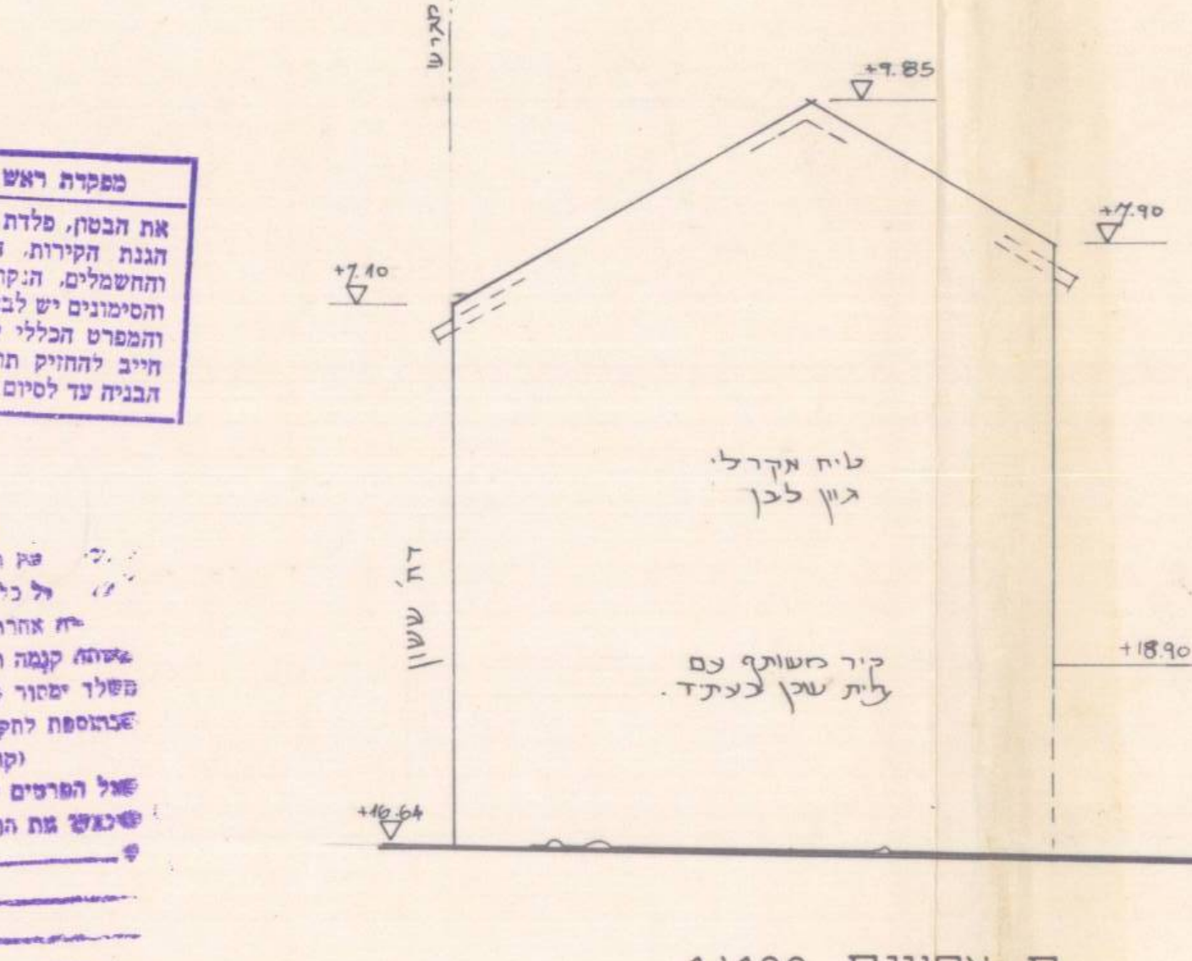

גבול מגרש
+9.85
+7.90
+7.10
טיח אקרלי גוון לבן
קיר משותף עם בית שכן בעתיד
+18.90
+16.64
+16.65
רח' ששון

ח. צפונית 1:100

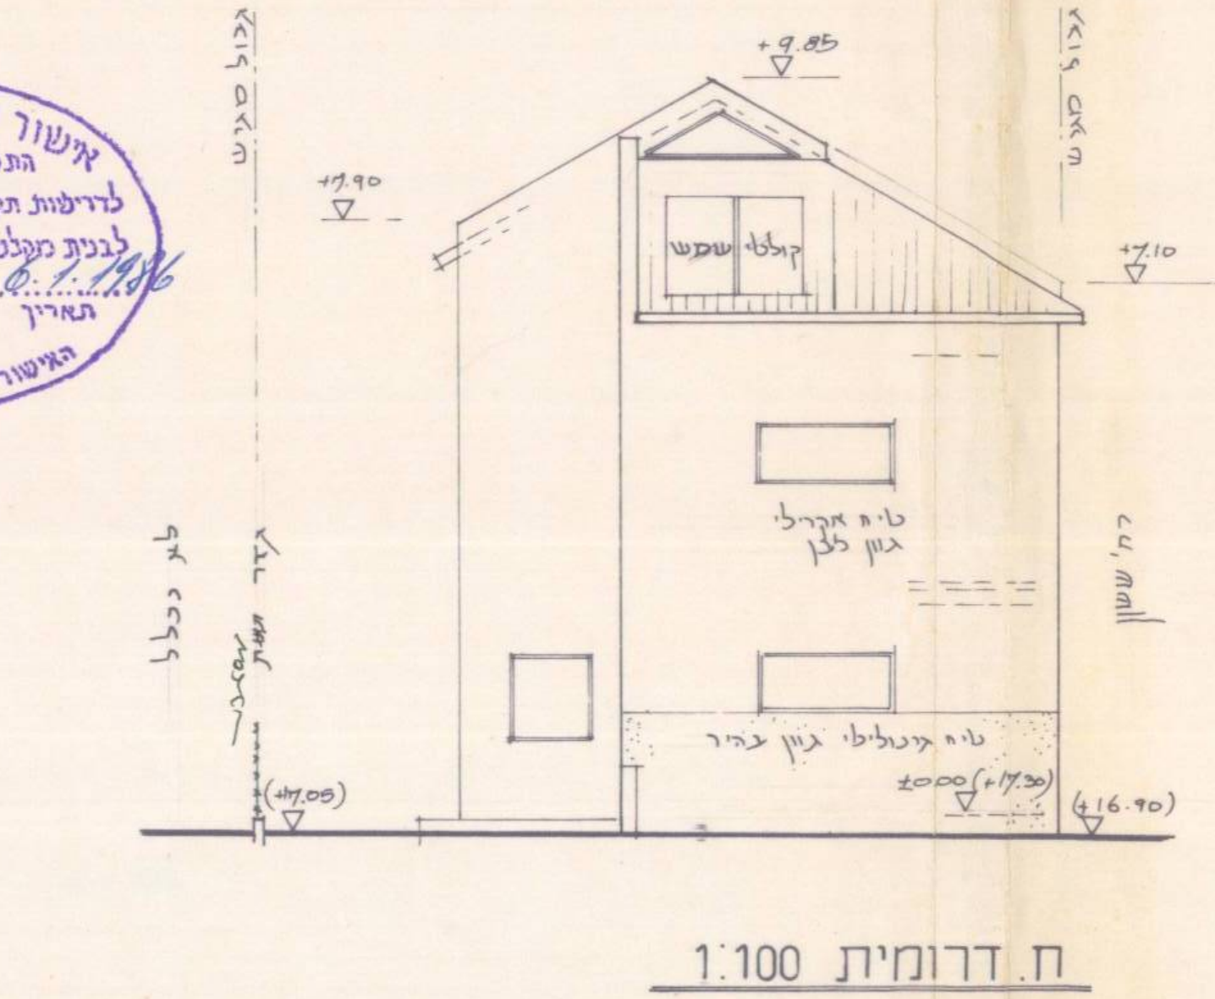

+9.85
+7.90
+7.10
קולטי שמש
טיח אקרלי גוון לבן
טיח גרנוליט גוון בהיר
±0.00 (+17.30)
(+16.90)

ח. דרומית 1:100

מפקדת ראש הג"א — ענף הנדסה ומיגון
את הבטון, פלדת הזיון, החסימה נגד מים ורטיבות, הגנת הקירות, המסגרות, המתקנים התברואתיים והחשמלים, הנקוז, הציפוי והצביעה של הקירות והסימונים יש לבצע לפי תקנות ההתגוננות האזרחית והמפרט הכללי למקלטים פרק 58 (1981). הקבלן חייב להחזיק תוכנית מאושרת של המקלט באתר הבניה עד לסיום הקמתו.
6884

את הוכנית מקלט זו ...
על כל חלקיו וכל הדרוש להקמתו יוקם ...
... אחרת בקומת המקלט, ולא יוסיפו ב...
... קומה ומעליה אלא לאחר שהאחראי ל...
השלד ימסור לוועדה המקומית תצהיר בנוסח
בהתוספת לתקנה 20/א לתקנות התכנון והבניה
וקובץ תקנות מס' 3592 מיום 21.9.78
כל הפרטים יבוצעו לפי תקני הג"א.
... את התקונים שרשמנו בגוף התוכ...
6.1.1986

אישור רשות מוסמכת מטעם ראש הג"א
התכנית נבדקה ונמצאה מתאימה
לדרישות תקנות ההתגוננות האזרחית (מפרטים
לבנית מקלטים), לבנית בינוי קדמי/עורפי
תאריך 6.1.1986 שם, משפחה התימה
אישור מס' 04-1074
האישור בתוקף עד תאריך 6.1.1987

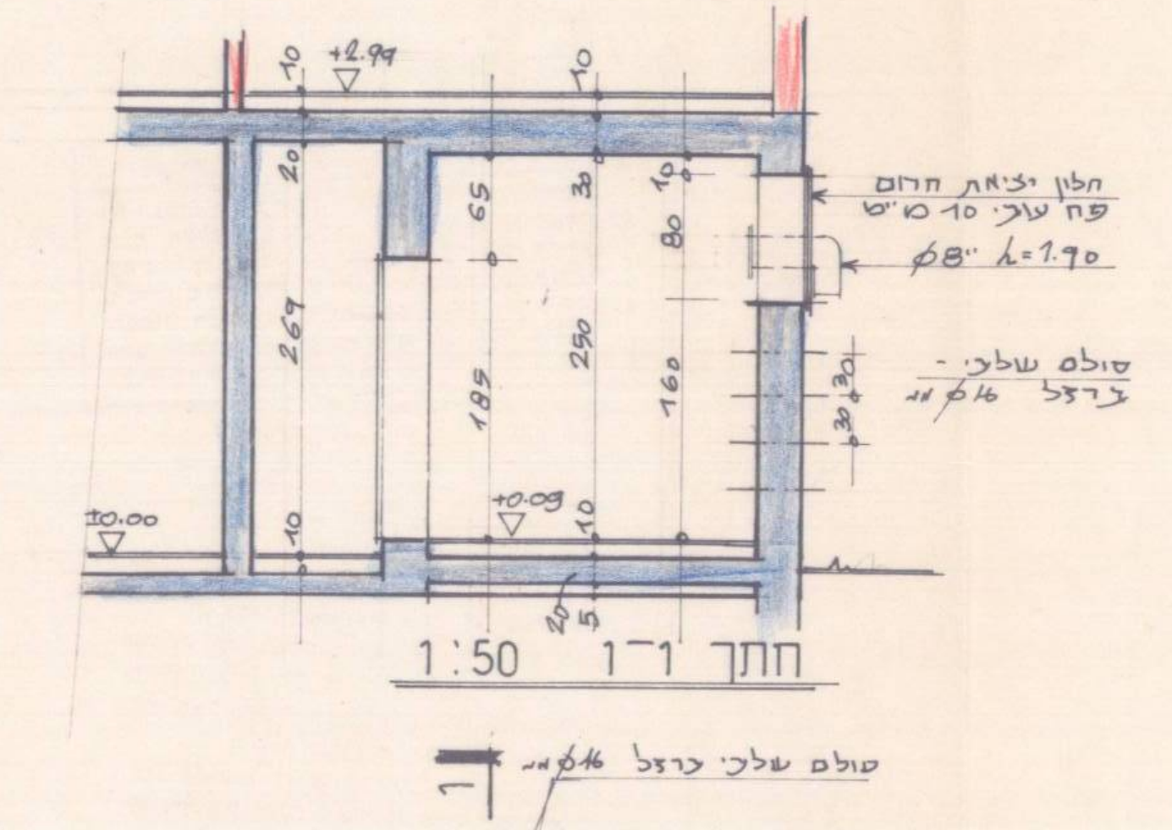

+2.99
חלון יציאת חרום פח עובי 10 מ"מ
ø8" h=1.90
סולם שלבי - ברזל ø16 מ"מ
267
185
250
160
±0.00

חתך ד־ד 1:50

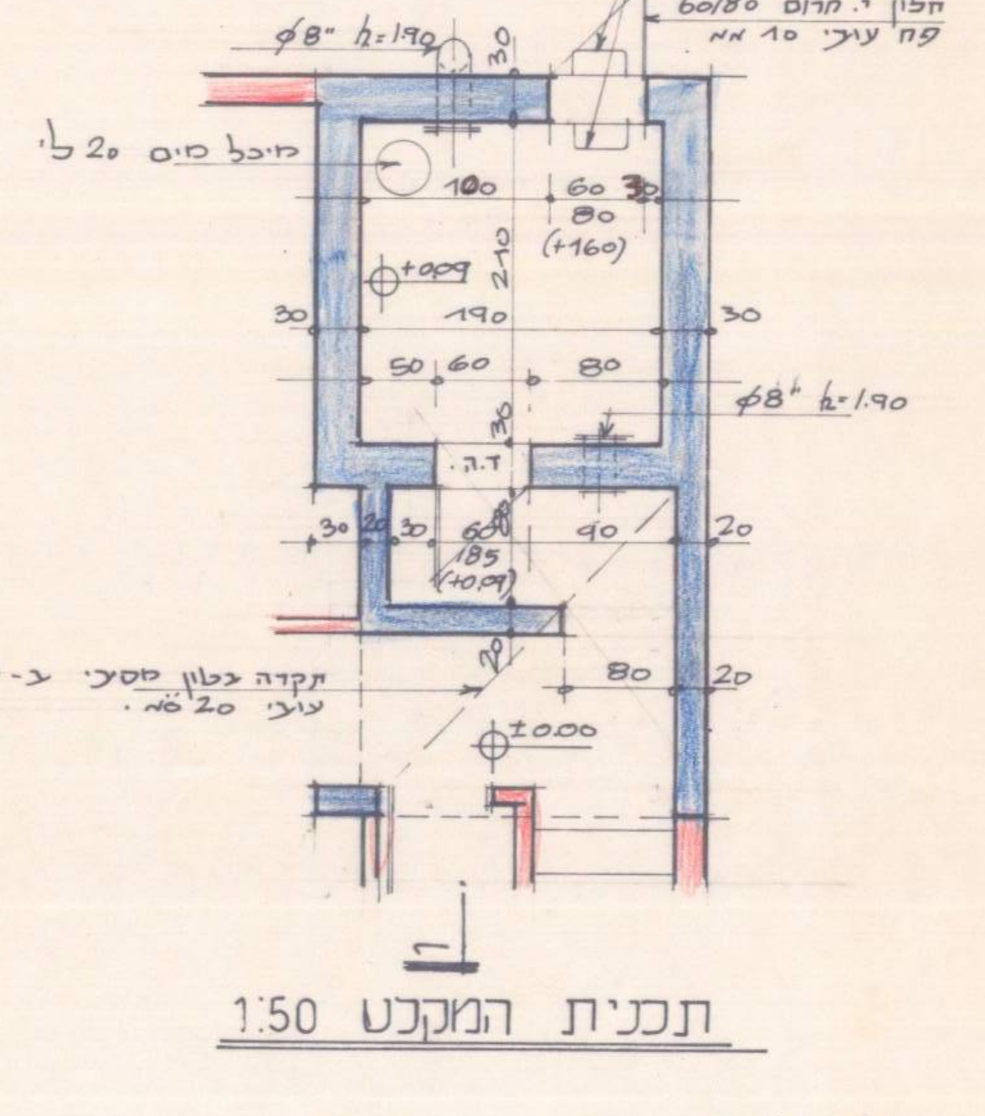

סולם שלבי ברזל ø16
ø8" h=1.90
חלון י. חרום 60/80 פח עובי 10 מ"מ
מיכל מים 20 ל׳
100
190
210
+0.09
30
50
60
ד.ה.
185
(+0.09)
80
20
±0.00
תקרה בטון מסוג ב-300 עובי 20 ס"מ

תכנית המקלט 1:50

שטח המקלט נטו 1.90 x 2.10= 4.00 m²

4/4 שרעבי ששון 14

הוראות ביצוע למקלט על-קרקעי

בטון רזה ב-150. תשתית בטון מתחת לרצפה.

בטון המקלט ב-300 - לפי התקן הישראלי 118 שנבדק ע"י מכון התקנים הישראלי או מוסד מוסמך אחר.

פלדת הזיון לפי תקן ישראלי

לפי המפורט במפרט הכללי למקלטים (58).

על הקבלן / המבקש להזמין את המהנדס האחראי על ביצוע השלד ולקבל אישור לביצוע כל שלבי המקלט.
עבודות הבידוד יש לבצע בהתאם למפרט הכללי למקלטים (58).
יש להזמין את המפקח מטעם הרשות המקומית לבדיקת שלבי בניית המקלט.

על הרשות המקומית להקפיד על מסירתה לועדה המקומית תצהיר של האחראי לביצוע השלד - בהתאם לקובץ התקנות ~~3592~~ 3892 מיום 21.9.78 (חוק התכנון והבניה תשכ"ה - 1965, תקנות בדבר תצהיר על הקמת שלד מקלט).

הוועדה המקומית לתכנון ולבניה
לשיכון תכנון תל־אביב־יפו
בהתאם לסעיף ... לתקנות התכנון והבניה (בקשה להיתר, תנאיו ואגרות) התש"ל-1970 ...
6/42
מיום 22.7.86
מהנדס העיר
תאריך 14-04-1986