

N-92-0061

26

25-92-9N 16-1-92



עיריית תל-אביב
מנהל התכנון
מחלקת מדידות

המפה עברה במחלקות:

☒	דרישים
☒	ביוב
☒	מים
☒	הנדסת חשמל
☒	הנדסת תשתית

חתימה: *[Signature]*

תל-אביב-יפו

גוש 6135

חלקה 44

שטח 108 מ"ר - מדוד

שטח 112 מ"ר - דשום


רח' ששון מס' 70

הוכן בשביל: ע"צ

סהות הנקשה - קבלת היתר בניה

מפה טופוגרפית

1:250

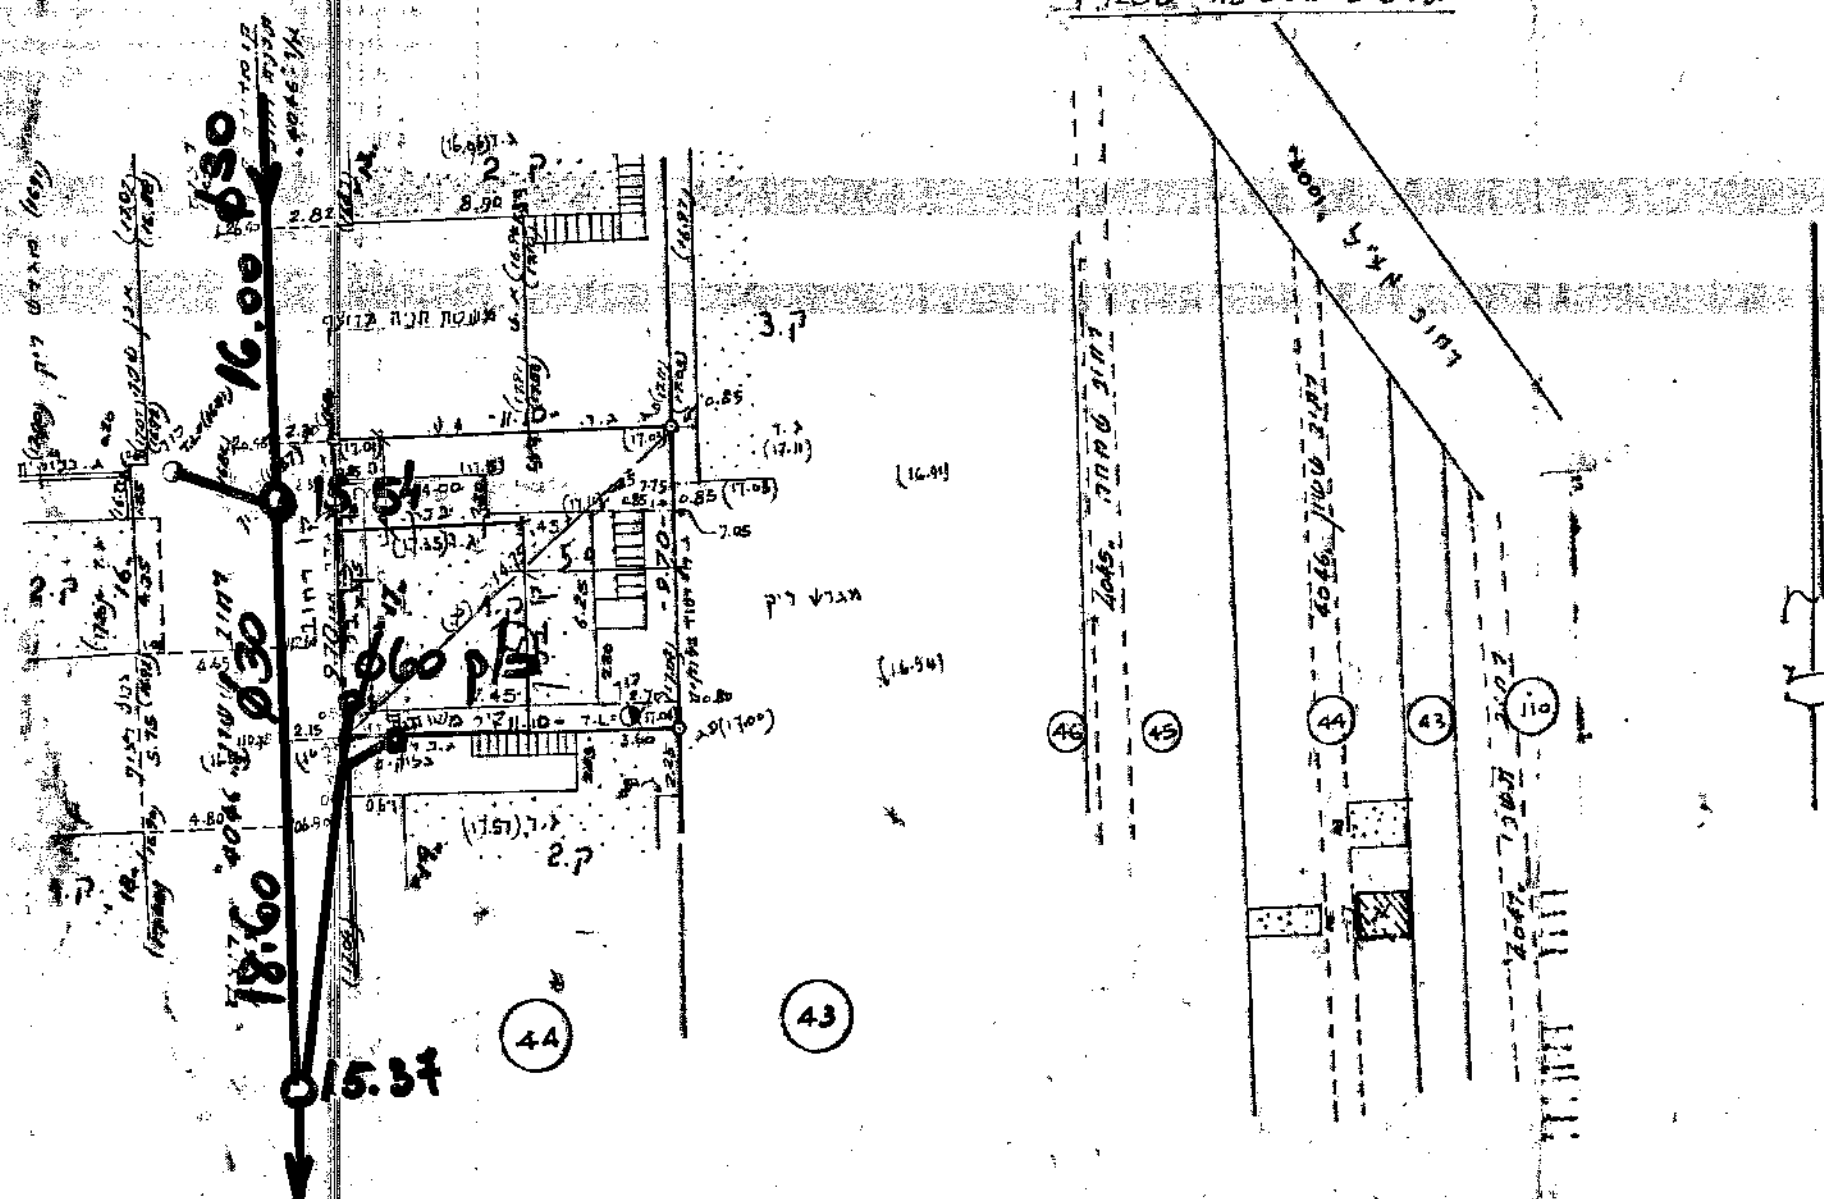

לפי תכנית 2215 (לא מאושרת) (תיק 92-0061)
רחוב 4046 - ששון - ברוחב 5-8 מ', קו בנין 0.
קו בנין צדדיים 3 מ' או קיר משותף, לאחר 5 מ'.
גובה הבנין 3 קומות, טה"כ 140%.
תכנית קרקע מירבית 60%.
הצפיפות 10 דירות לדונם.
יציאות לגג לפי תכנית 1680, מרתף לפי תכנית "ע".
אין לגבות היטל השבחה היות והשבחה הוכרזה כשכונת
שיקום.
ניתן להוציא היתרים לפי סעיף 97 א' לחוק.
יש לתאם את התכנון עם צוות מזרח באגף ת.ב.ע.

עיריית תל-אביב-יפו
מנהל תכנון ותשתית / אגף עבודות ציבוריות
מחלקת מדידות

חתימה: *[Signature]*
חתימה: *[Signature]*
תאריך: 19/1/92

שם: *[Signature]* (לצורך חשבוש זכויות בנין)
מספר: *[Signature]*
מספר: *[Signature]*
מספר: *[Signature]*

עיריית תל-אביב-יפו
מנהל תכנון ותשתית / אגף עבודות ציבוריות
מחלקת מדידות / מדור השליט והמספור

אשור כתובת
רחוב: *[Signature]* מס' 17
פינת רח' מס' *[Signature]*
תאריך: 19/1/92 חתימה: *[Signature]*

הנני מאשר שהתכנית נכונה לכל חוק תכנון ותכנית
והחוקות והלחיות של עיריית תל-אביב-יפו

הערות
ו. הגבהים מרומשים על גובה ניק. 187 = 17.549
2. המספרים במאגדים בעגנים גובהים

נמרק 292-0061

לא לצדדכי דישום

קודד גוש: 278
דשון: *[Signature]*
(5.7.92)

תל-אביב
7.12.1991

למנו בהנא
משרד פכני למדידות
תכנון (מקום ציפי)
רח' יבנה 152, תל-אביב
03-6972234