

N92-0061

26

25-92-91 16-1-92



איכות נמוכה

עיריית תל-אביב-יפו
מחלקת הבינוי והתעו"ל
(מידע מוקדם)
בנין סוג: (שחור)
תע"ל: (במחיר)
ח' ע' ר' ו' ת'
תאריך: 23.1.92 חתימה:

תל-אביב-יפו

גוש 6135

חלקה 44

שטח 108 מ' - מדוד

שטח 120 מ' - דשום

רח' ששון מס' 17


קוטר בשביל: ע"צ

סהות הצללה - קבלת מידע בניה

עקומת תל-אביב
מנהל מדינת
מחלקת מדינות
המנה עברה במחלקות:
☒ דרישה
☒ בינוי
☒ מים
☒ הנחיות צוות
☐ חשימה
חתימה:

חפה טופוגרפית

1:250

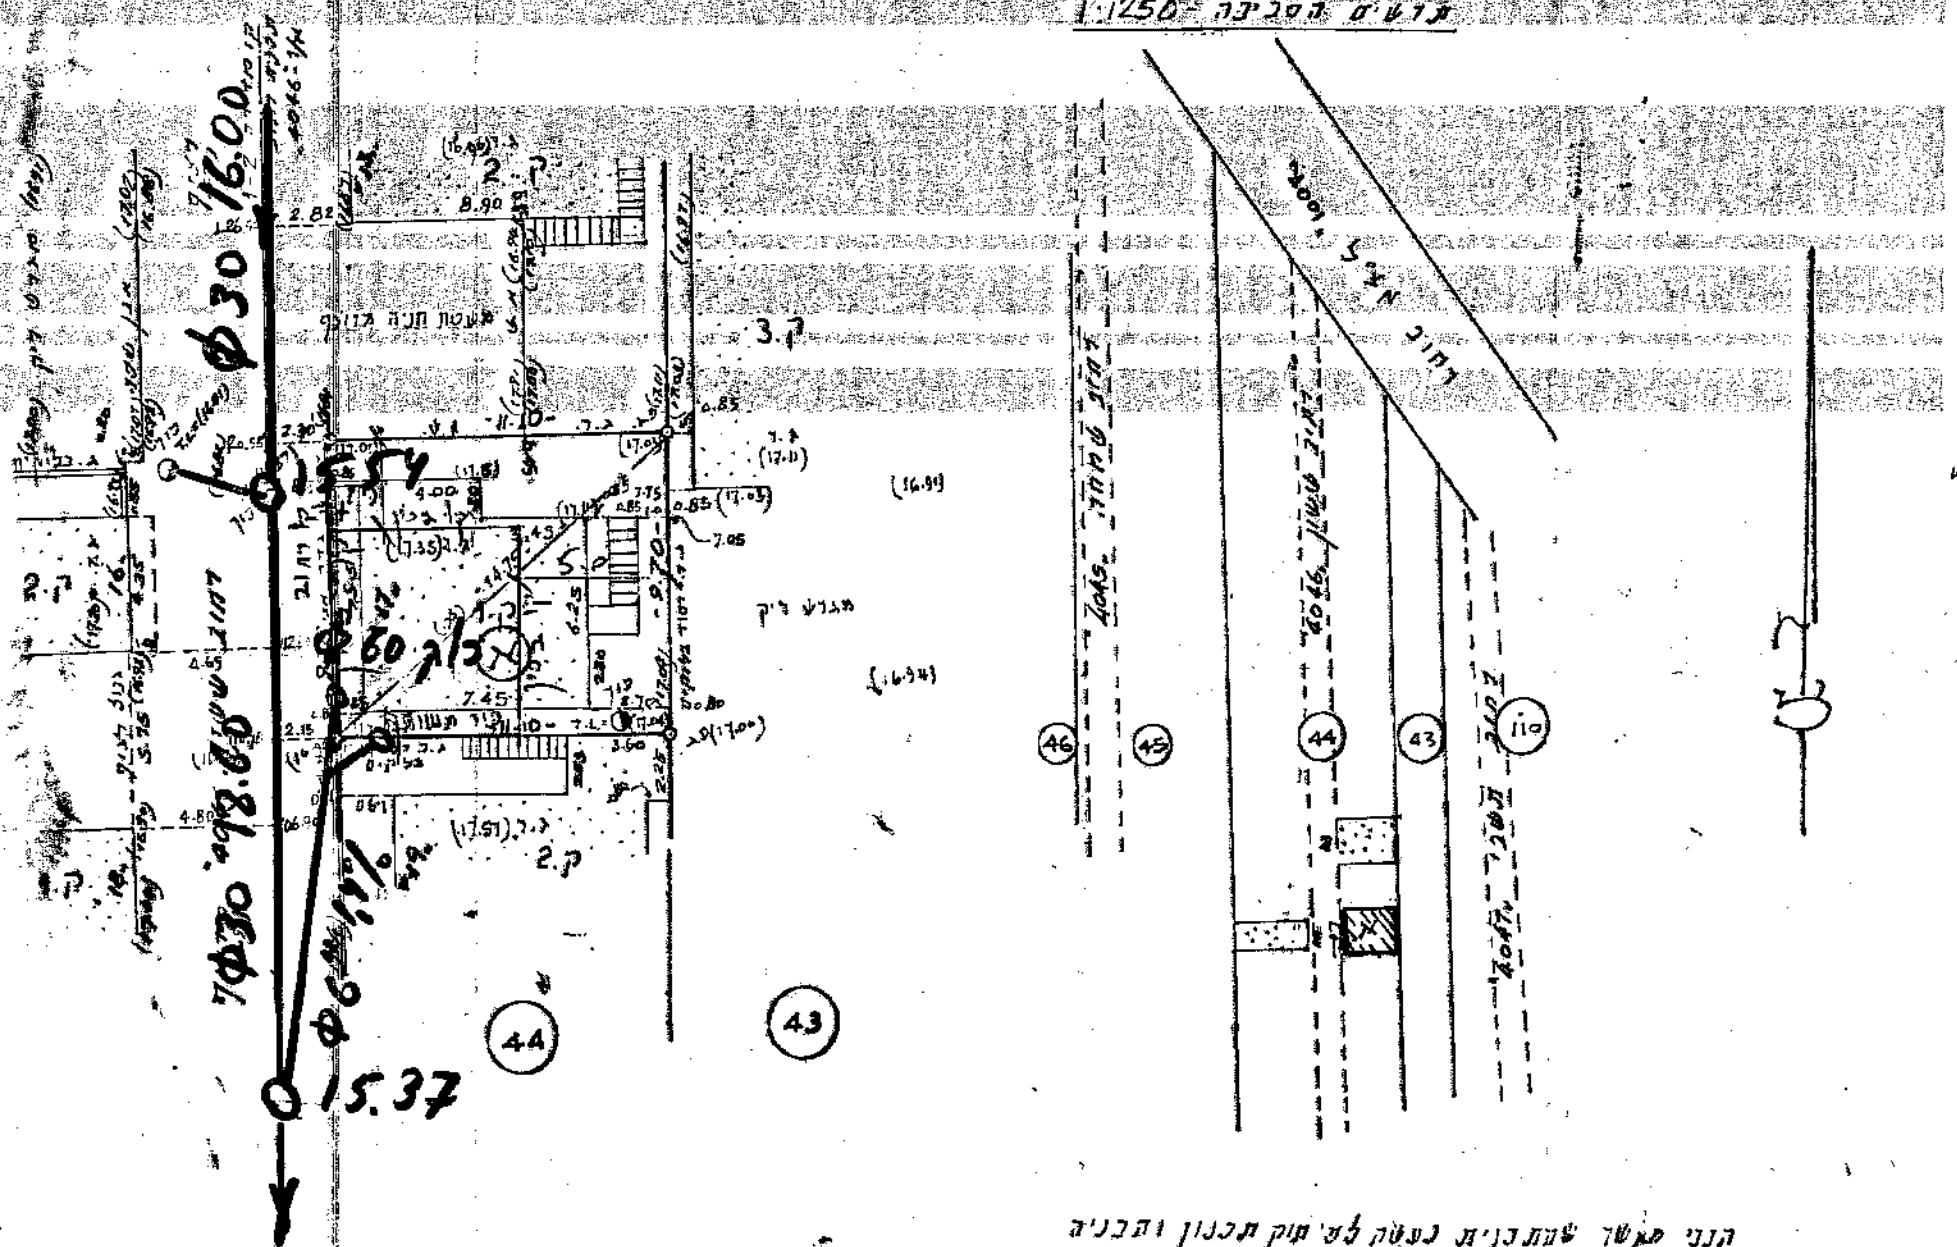

לפי תכנית 2215 (לא מאושרת) (תיק 92-0061)
רחוב 4046 - ששון - ברוחב 5-8 מ', קו בנין 0.
קו בנין צדדיים 3 מ' או קיר משותף, לאחר 5 מ'.
גובה הבנין 3 קומות, סה"כ 140%
תכנית קרקע מירבית 60%
הצפיפות 10 דירות לדונם.
יציאות לגג לפי תכנית 1680, מרחף לפי תכנית "ע".
אין לגבות היטל השבחה היות והשכונה הוכרזה כשכונת
שיקום.
ניתן להוציא היתרים לפי סעיף 97 א' לחוק.
יש לתאם את התכנון עם צוות מזרח באגר ת.ב.ע.

עיריית תל-אביב-יפו
מנהל בינוי ותשתית / אגף עבודות ציבוריות
מחלקת מדינות
חתימה: 1/1/92
חתימה: 1/1/92
תאריך: 1/1/92

שטח הפקעה (לצורך חשבון זכויות בנ'
מאושר (ת.ב.ע.) מ"מ: ()
נורצע (ת.ב.ע.) מ"מ: ()
הפקעה סופית יקבע בהמשך

עיריית תל-אביב-יפו
מנהל מדינות / אגף עבודות ציבוריות
מחלקת מדינות / מועד חשילוט והמספור
אשרור כותבת
רחוב מס' 17
פינת רח' מס' 17
תאריך: 1/1/92 חתימה:

הנני מאשר שהתכנית נכונה לשימוש תכנון ותכנית
והוראות והנחיות של עיריית תל-אביב-יפו

הערות
1. הגבהים מבוססים על גובה נק. 780 = 7.549
2. המספרים בסוגריים בסמנים גובהים

לא לצדדכי דישום

מודד גוסמן
דשין 278
(ח.ב.מ.)

תל-אביב
7.12.1991

למון כהנא
משרד טכני למדידות
תכנון ומדידות
רח' מנחם בגין 152, תל-אביב
טל 03-6957234

נסרק

92-0061