26

מפה טופוגרפית
קנה מידה 1:250

מחוז : תל-אביב
נפה : תל-אביב' יפו
מקום : תל אביב
גוש 6135
חלקה :44
הוכן עבורעוזון אהרון (יוסף) ת.ז 04830840 .
(שם הבעלים כרשום בנסח טאבו)
מטרת מפה הגדרת מגרש משני עפ"י ת.ב.ע2215 .
היתר לשיקום סככה קיימת
כתובת : רח' ששון 22""
תיק בנין : 4046-022/0
שטח לפי :נסח
שטח החלקה כולה :(מ"ר) 11.476
בעלות בחלקים (כרשום בנסח טאבו) /12614345
בעלות במ"ר 100.80
שטח מדוד (מ"ר) 100.80
שטח מגרש משני 100.80
שטח .....לגריעה.

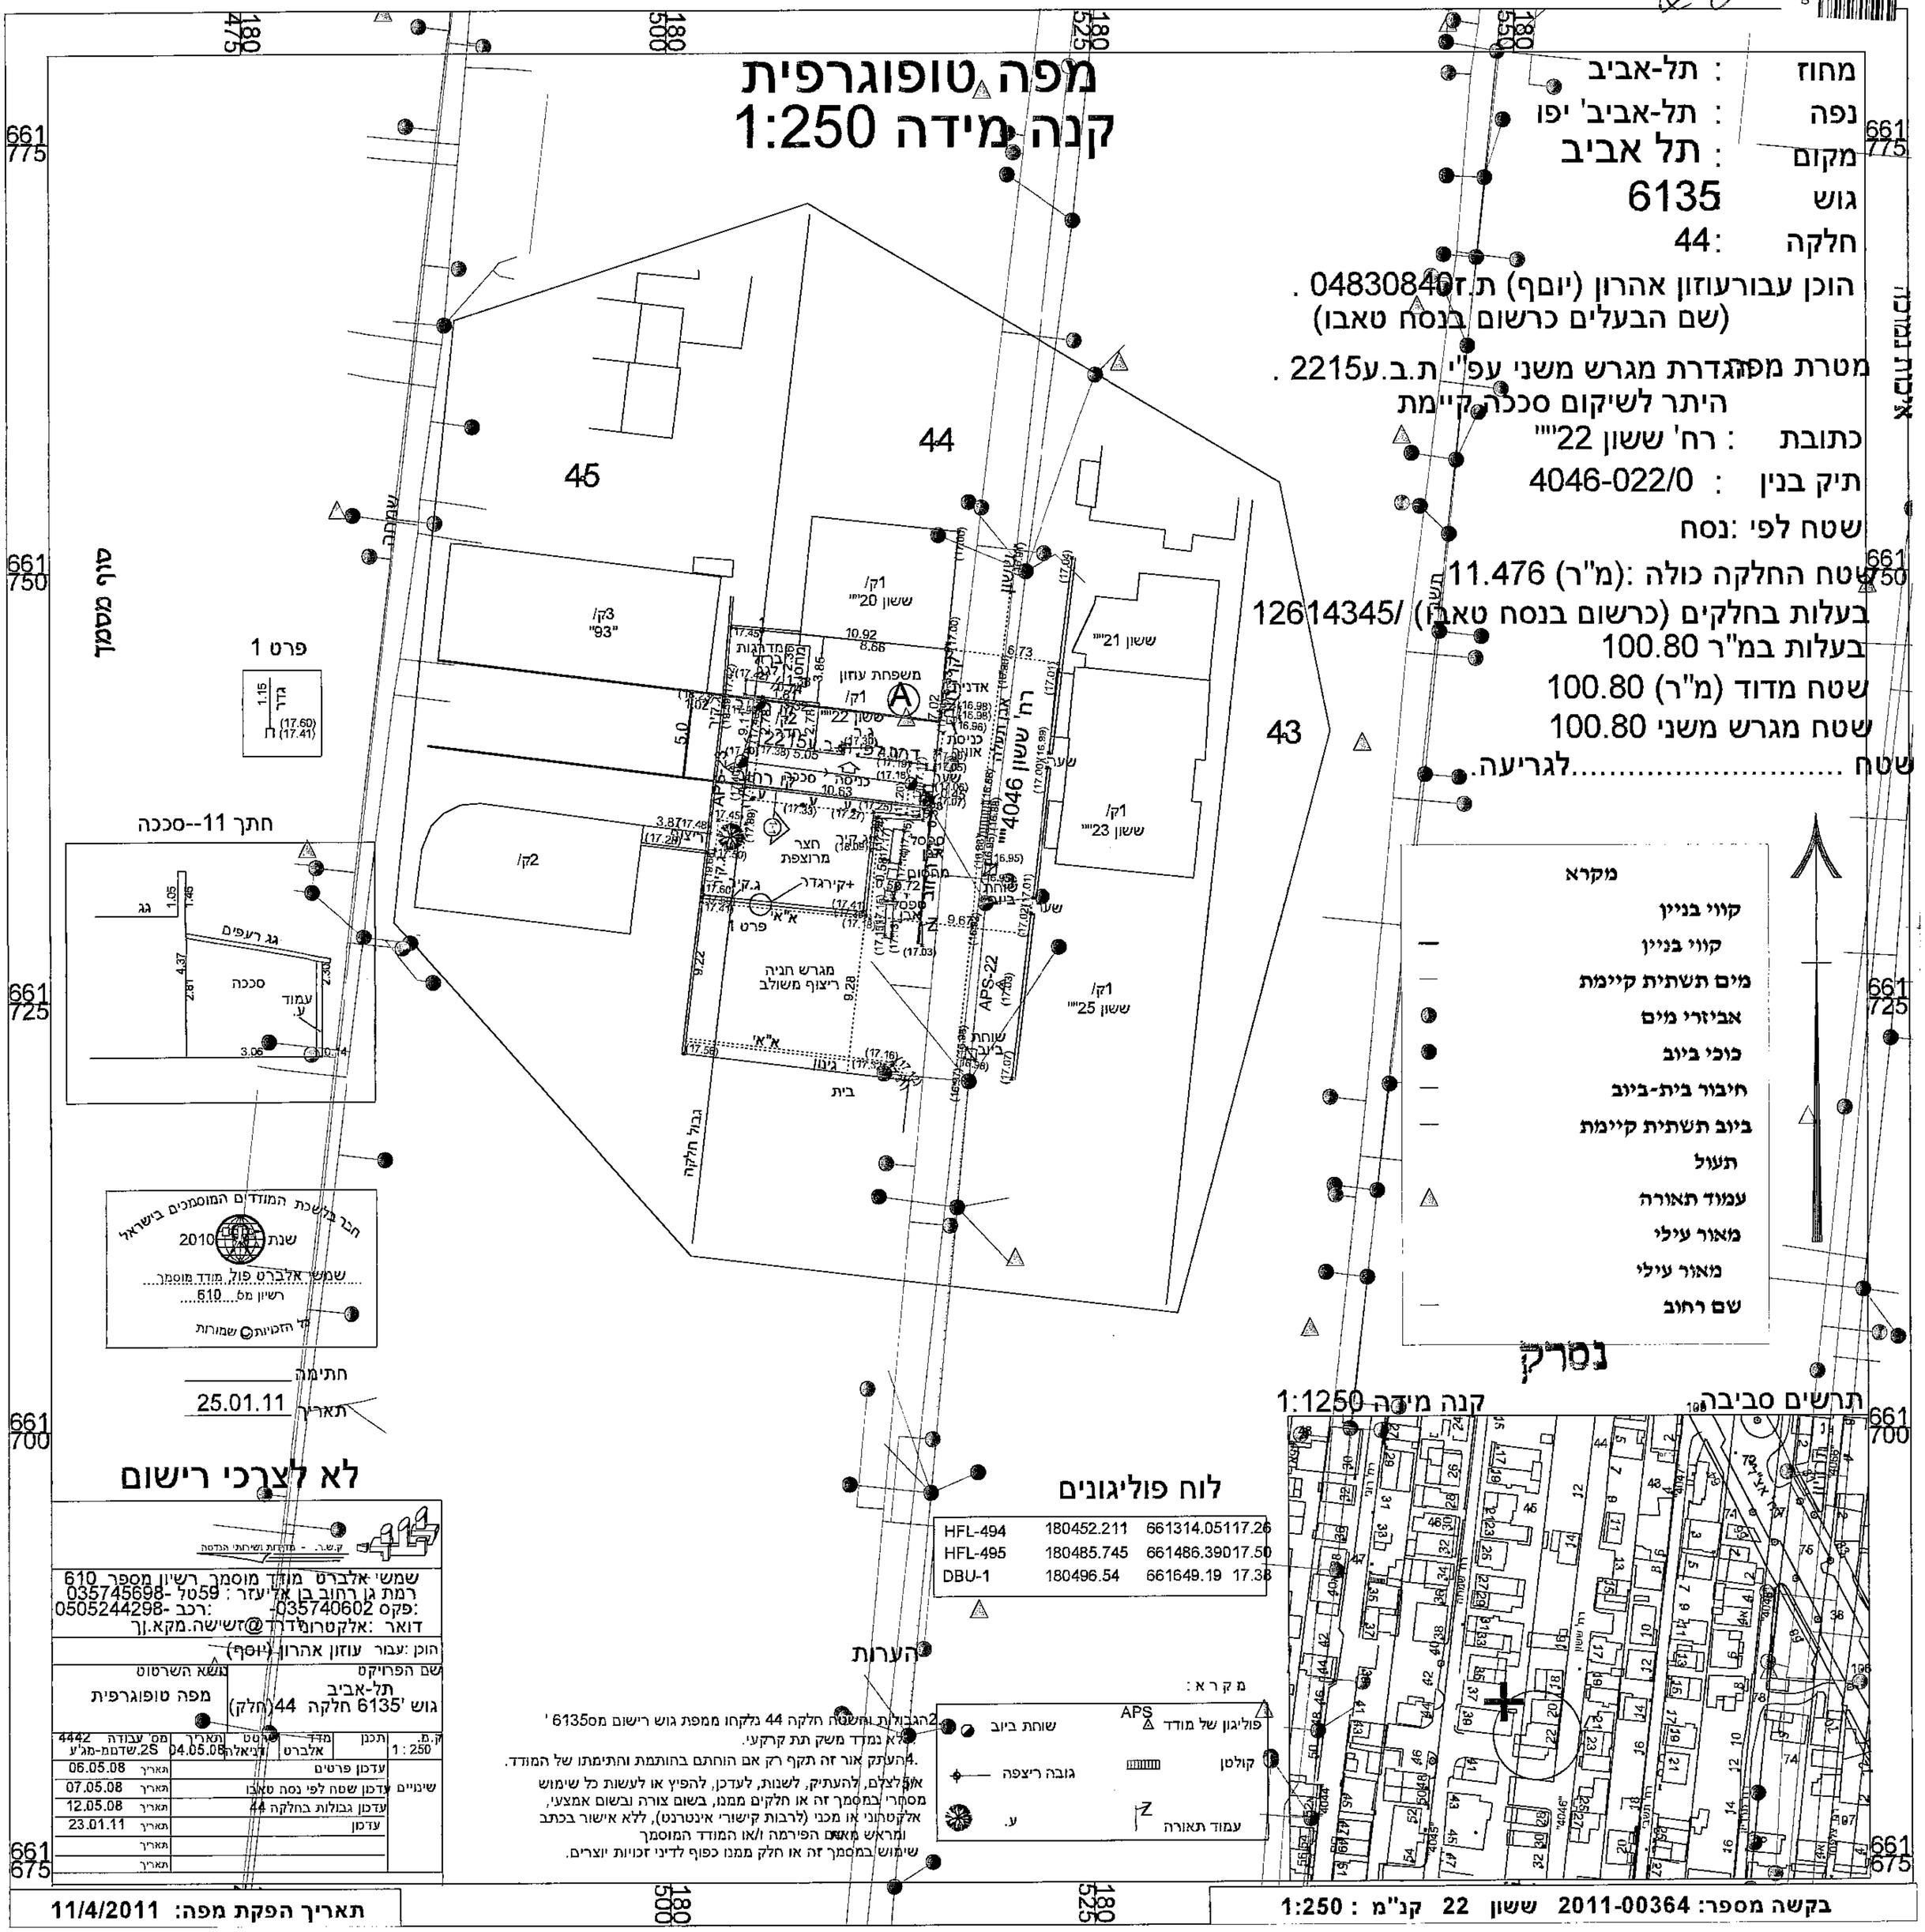

חתימה
תאריך 25.01.11

לא לצרכי רישום

ק.ש.ר. - מדידות ושירותי הנדסה

שמשי אלברט מודד מוסמך רשיון מספר 610
רמת גן רחוב בן אליעזר : 59טל -035745698
:פקס 035740602- :רכב -0505244298
דואר :אלקטרוני לדרך@זשישה.מקא.נך

הוכן :עבור עוזון אהרון (יוסף)

שם הפרויקט	נושא השרטוט
תל-אביב גוש '6135 חלקה 44(חלק)	מפה טופוגרפית

ק.מ. 1 : 250	תכנן	מדד אלברט	שרטט דניאלה	תאריך 04.05.08	מס' עבודה 4442 2S.שדממ-מג'ע
	עדכון פרטים				תאריך 06.05.08
שינויים	עדכון שטח לפי נסח טאבו				תאריך 07.05.08
	עדכון גבולות בחלקה 44				תאריך 12.05.08
	עדכון				תאריך 23.01.11
					תאריך
					תאריך

לוח פוליגונים

HFL-494	180452.211	661314.05117.26
HFL-495	180485.745	661486.39017.50
DBU-1	180496.54	661649.19 17.38

הערות

מקרא :
פוליגון של מודד APS
שוחת ביוב
קולטן
גובה ריצפה
עמוד תאורה
ע.

2.הגבולות והשטח חלקה 44 נלקחו ממפת גוש רישום מס6135 '
.לא נמדד משק תת קרקעי.
4.העתק אור זה תקף רק אם הוחתם בחותמת וחתימתו של המודד.
אי לצלם, להעתיק, לשנות, לעדכן, להפיץ או לעשות כל שימוש
מסחרי במסמך זה או חלקים ממנו, בשום צורה ובשום אמצעי,
אלקטרוני או מכני (לרבות קישורי אינטרנט), ללא אישור בכתב
ומראש מאת הפירמה ו/או המודד המוסמך
שימוש במסמך זה או חלק ממנו כפוף לדיני זכויות יוצרים.

מקרא

קווי בניין
קווי בניין
מים תשתית קיימת
אביזרי מים
כוכי ביוב
חיבור בית-ביוב
ביוב תשתית קיימת
תעול
עמוד תאורה
מאור עילי
מאור עילי
שם רחוב

נסרק

תרשים סביבה קנה מידה 1:1250

תאריך הפקת מפה: 11/4/2011

בקשה מספר: 2011-00364 ששון 22 קנ"מ : 1:250