1

20

עירית תל־אביב־יפו
מינהל ההנדסה
21-09-1989
נתקבל במח' רשוי
רשום

חוק התכנון והבניה, התשכ"ה–1965
תקנות התכנון והבניה (בקשה להיתר, תנאיו ואגרות), התש"ל–1970

טופס 2 (תקנה 2(א))

תיק מס 4046-027

מיפרט

012

הוועדה המקומית לתכנון ולבניה תל אביב

איכות נמוכה

א. תיאור הבנין

מגרש	תכנית מיתאר מקומית או מפורטת	חלקה	גוש	מס'	הרחוב	1. המקום
		44(חלק)	6135	27	ששון	תל אביב

מס' הטלפון	המען	השם	
993502	ת.ד. 4266 רמת אליהו ראל"צ	סגלוביץ משה	2. המבקש
	—״—	—״—	3. בעל הזכות בנכס
239997	רח' אדם הכהן 16 ת.א.	פרחי אדריכלים בע"מ	4. עורך הבקשה *
7521921	רח' רוקח 35 רמת גן	י. לבני מהנדס	5. האחראי לביצוע השלד

6. אזור הבניה: ■ מגורים ☐ מסחר ☐ תעשיה ☐ בנין ציבורי ☐ חקלאי ☐ ....
7. שטח המגרש/החלקה: 105 מ"ר. אחוז הבניה המותר: ....%
8. מטרת הבנין: ■ מגורים ☐ הארחה ☐ עסקים ☐ תעשיה ☐ חקלאי ☐ ציבורי ☐ ....
9. מהות הבנין ותכליתו: בית מגורים חדש במקום בית קיים במסגרת פרויקט בנה ביתך
10. תיאור העבודה המוצעת: ■ בנין חדש ☐ תוספת לבנין קיים ☐ הריסה ☐ תיקונים ☐ שינוי בבנין ☐ .... ☐ שינוי בשימוש ממטרה: .... למטרה: ....
11. האם הבניה היא בעד: ☐ משרד ממשלתי ☐ הרשות המקומית ☐ הסוכנות היהודית

ב. היקף הבניה

קומה	קיים	מוצע	סך הכל	אחוז הבניה	מגורים בדירות עד 45 מ"ר	עד 65 מ"ר	עד 90 מ"ר	עד 100 מ"ר	מעל 100 מ"ר	עסק; הארחה; וכו'	ציבורי	שונות	מס' חדרים קיים	מס' חדרים מוצע
1	2	3	4	5	6	7	8	9	10	11	12	13	14	15
קרקע		52.87		50.35%										
א		48.46		46.15%										
ב		23.83		22.69%										
ג														
ד														
ה														
ו														
ז														
הבניה הקובעת לבנין														
חדרי מדרגות														
בניני עזר														
סך הכל		125.16		119.19%										

הנפח המוצע: של הבנין העיקרי.......... מ"ק. של בנין עזר.......... מ"ק.

ג. השימוש בבנין

1. הבניה המוצעת למגורים

דירות בנות:	שטח כל דירה מ"ר	מספר דירות מכל סוג	כל הדירות	מזה: רצפות חדרי דיור בלבד, ומרפסות מקורות	מזה: רצפות חדרי שירות ופרוזדורים בלבד	מזה: רצפות של מרפסות בלתי מקורות	מספר חדרים: דיור	מטבחים	אמבטיות	בתי שימוש	אחרים
1	2	3	4	5	6	7	8	9	10	11	12
חדר אחד	ראה השרטוט סכימתי של שטחי הבניה בכל קומה, המציין מספר החדרים והשטח בכל דירה.										
2 חדרים											
3 חדרים											
4 חדרים							4	1	2	2	1
5 חדרים											
6 חדרים											
7 חדרים ויותר											
חדרים נוספים לדירות קיימות											
בניני עזר											
סך הכל		1									

איכות נמוכה

נסרק

2

2. הבניה הקיימת והמוצעת לתעשיה ולמלאכה

פרטים	קיים: שטח	קיים: גובה	קיים: נפח	קיים: % הבניה	מוצע: שטח	מוצע: גובה	מוצע: נפח	מוצע: % הבניה	סך הכל: שטח	סך הכל: נפח	סך הכל: % הבניה	הערות
1	2	3	4	5	6	7	8	9	10	11	12	13
אולמי מלאכה												
משרדים												
חדרי שירות												
סככות												
בניני עזר												
חדרי מדרגות												
סך הכל												

3. הבניה המוצעת למטרות אחרות (הארחה, עסקים ומשרדים, בניני ציבור, בניני משק חקלאי, מטרות שונות).

השימוש המיועד	סך הכל מ"ר	שטחים – מ"ר מזה: חדרים	אולמות	אחסנה	חדרי שירות	מספר חדרים, אולמות וכו': חדרים	אולמות	אחסנה	חדרי שירות
1	2	3	4	5	6	7	8	9	10
בניני עזר (למעט אלה המפורטים ב־ג(4))									

4. חלקי בנין אחרים – הבניה המוצעת, שטח במ"ר.

חדרי מדרגות	מרפסות שלא נכללו לעיל	מעליות	חדרי הסקה	חדרי כביסה	מקלטים	קומת עמודים מפולשת	מחסנים	מוסכים	בניני עזר נוספים	סך הכל
1	2	3	4	5	6	7	8	9	10	11
	25.77				7.04					

ד. חומר הבניה

קירות חיצונים	☐ בטון מזוין	☐ לבני בטון או בלוקים	☐ לבני סיליקט	☐ לבנים שרופות	☐ אבן טבעית
	☐ אבן מלאכותית	☐ איטונג	☐ עץ	☐ ברזל	☐ חמרים אחרים
תקרות	☐ בטון מזוין	☐ עץ	☐ חומר אחר		
גג	☐ בטון מזוין	☐ רעפים	☐ אסבסט	☐ פח	☐ חומר אחר ....

ה. גדרות קיימות.......... מ"א מוצעות.......... מ"א

ו. מקרא

🟦 בטון או בטון מזוין	☐ אבן	☐ עץ	☐ איטונג
🟥 בלוקים או לבנים מבטון	☐ סיליקט או לבנים אדומות	☐ חומר אחר	☐ להריסה

הערות:

הנני מאשר כי הנתונים הנ"ל נכונים

תאריך 28-12-88 חתימת המבקש

חתימת עורך הבקשה * י. רפפא

חתימת האחראי לביצוע השלד

חתימת בעל הזכות בנכס

לשימוש הוועדה המקומית בלבד	מס' ההיתר	תאריך ההיתר	תאריך התחלת הבניה	תאריך גמר הבניה

אישורים של רשויות חוץ:

חותמת הוועדה המקומית

* היו מספר עורכי בקשה, כאמור בתקנה 2ה'. יבוא במקום כל אלה. הראשון שברשימת עורכי הבקשה, כאמור בטופס 1.

תרשים הסביבה
ק.מ. 1:1250

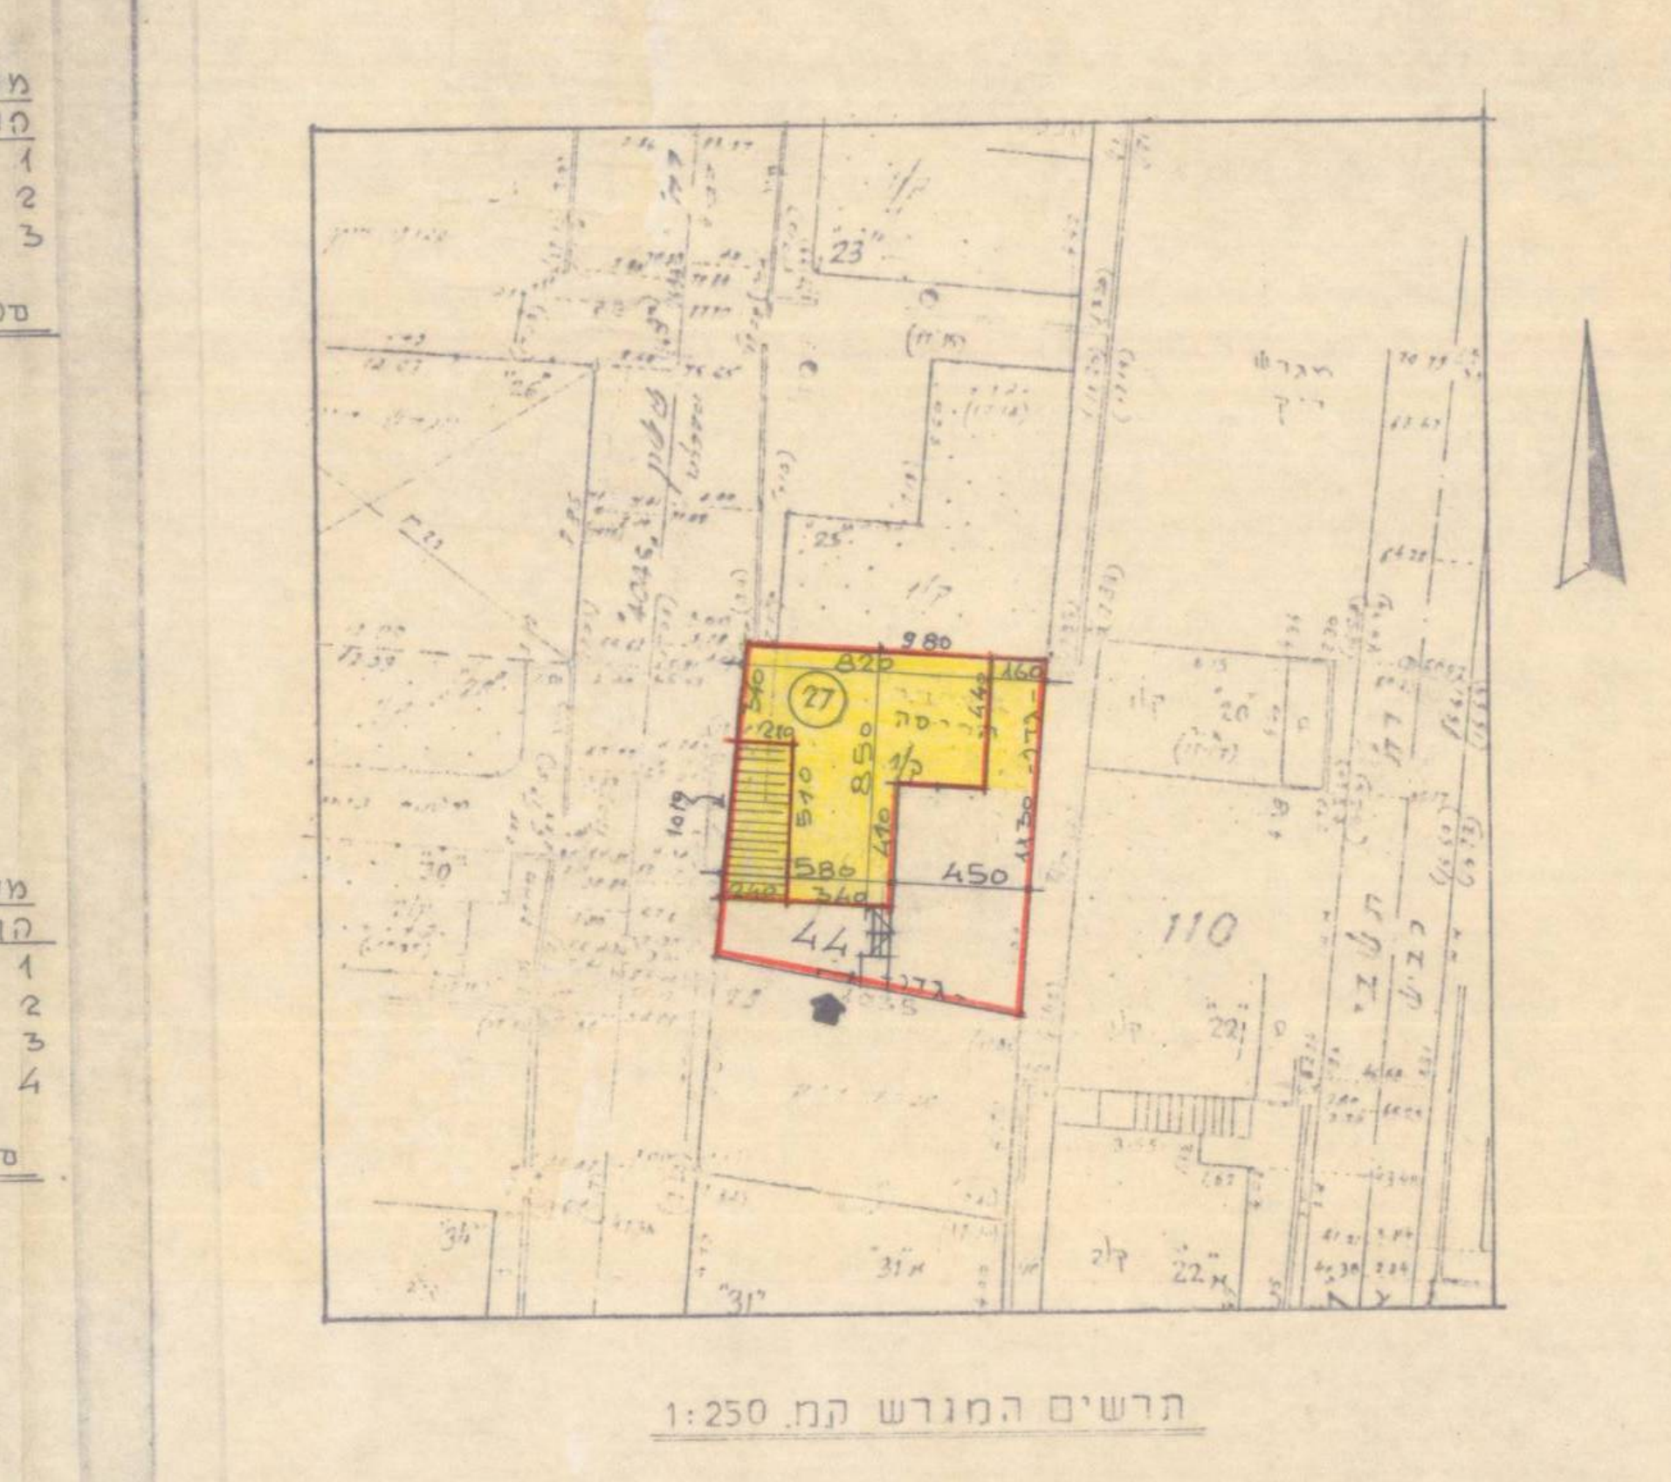
27
44
23
25
34
31
110

הרשים המגרש קמ 1:250

3

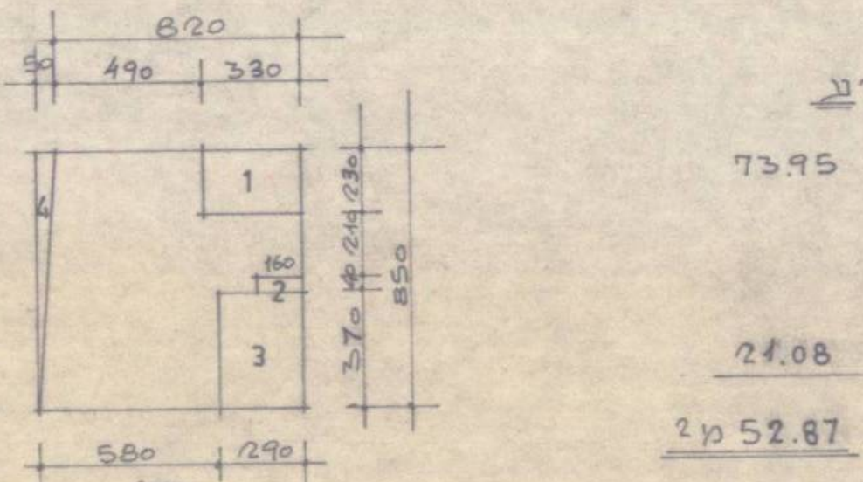
820
490
330
850
580
290
870
1
2
3
4

חישוב שטח ק. קרקע

מסגרת: 73.95 = 870 × 850
הורדות:
1 330 × 230 = 7.59
2 160 × 0.40 = 0.64
3 290 × 3.70 = 10.73
4 (850 × 0.50)/2 = 2.12 — 21.08

סה"כ שטח .... 52.87 מ"ר
שטח המקלט ① 330 × 230 = 7.59 מ"ר

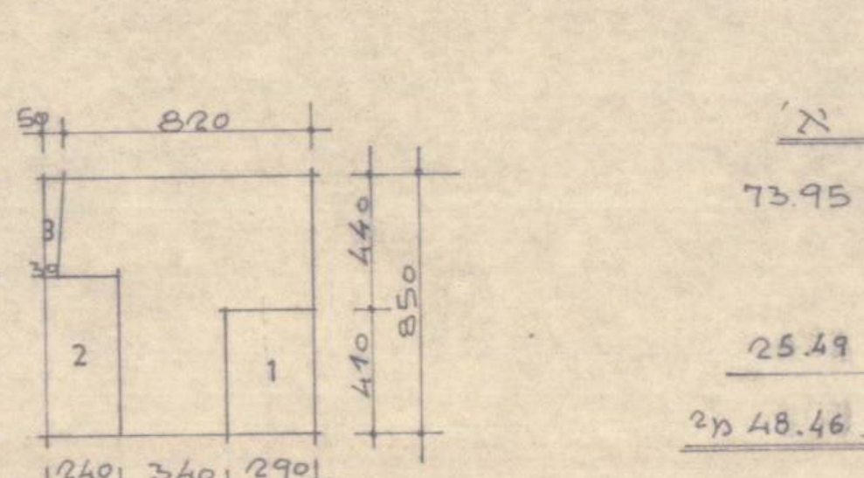
820
340
510
440
410
850
240
340
290
870
1
2
3

חישוב שטח קומה א'

מסגרת: 73.95 = 870 × 850
הורדות:
1 290 × 410 = 11.89
2 240 × 5.10 = 12.24
3 (50+30 × 3.40)/2 = 1.36 — 25.49

סה"כ שטח .... 48.46 מ"ר

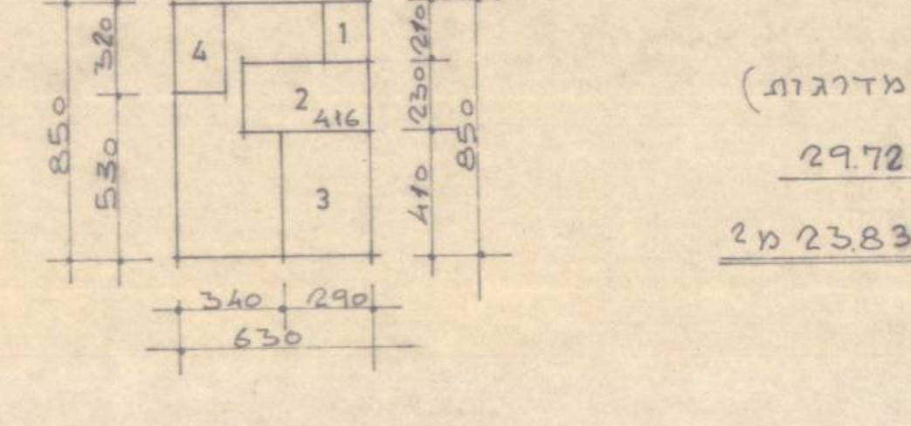
160
320
150
850
530
320
410
230
340
290
630
1
2
3
4
416

חישוב שטח קומה ב'

מסגרת: 53.55 = 850 × 630
הורדות:
1 150 × 210 = 3.15
2 416 × 230 = 9.56 (חדר מדרגות)
3 290 × 410 = 11.89
4 320 × 160 = 5.12 — 29.72

סה"כ שטח .... 23.83 מ"ר

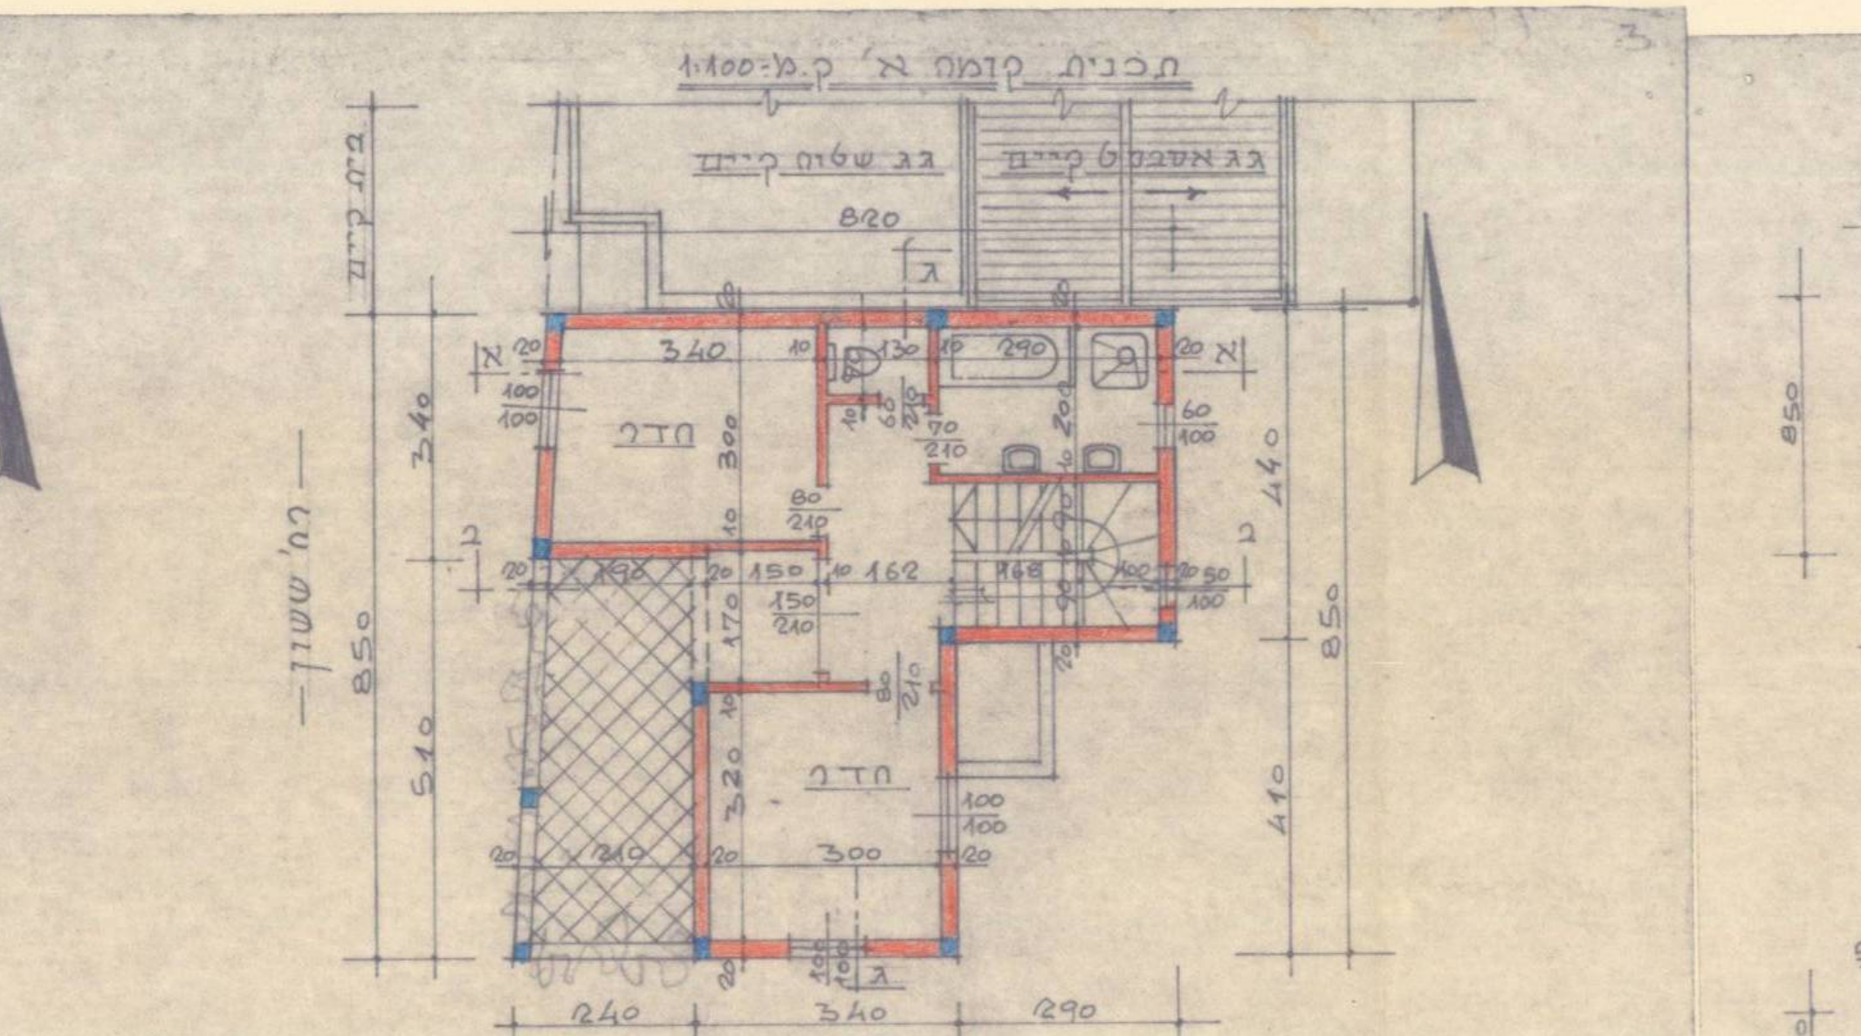
גג אסבסט
גג שלוחה קיים
חדר
בית קיים
רח' ששון
340
820
870
850
410

תכנית קומה א' ק.מ. 1:100

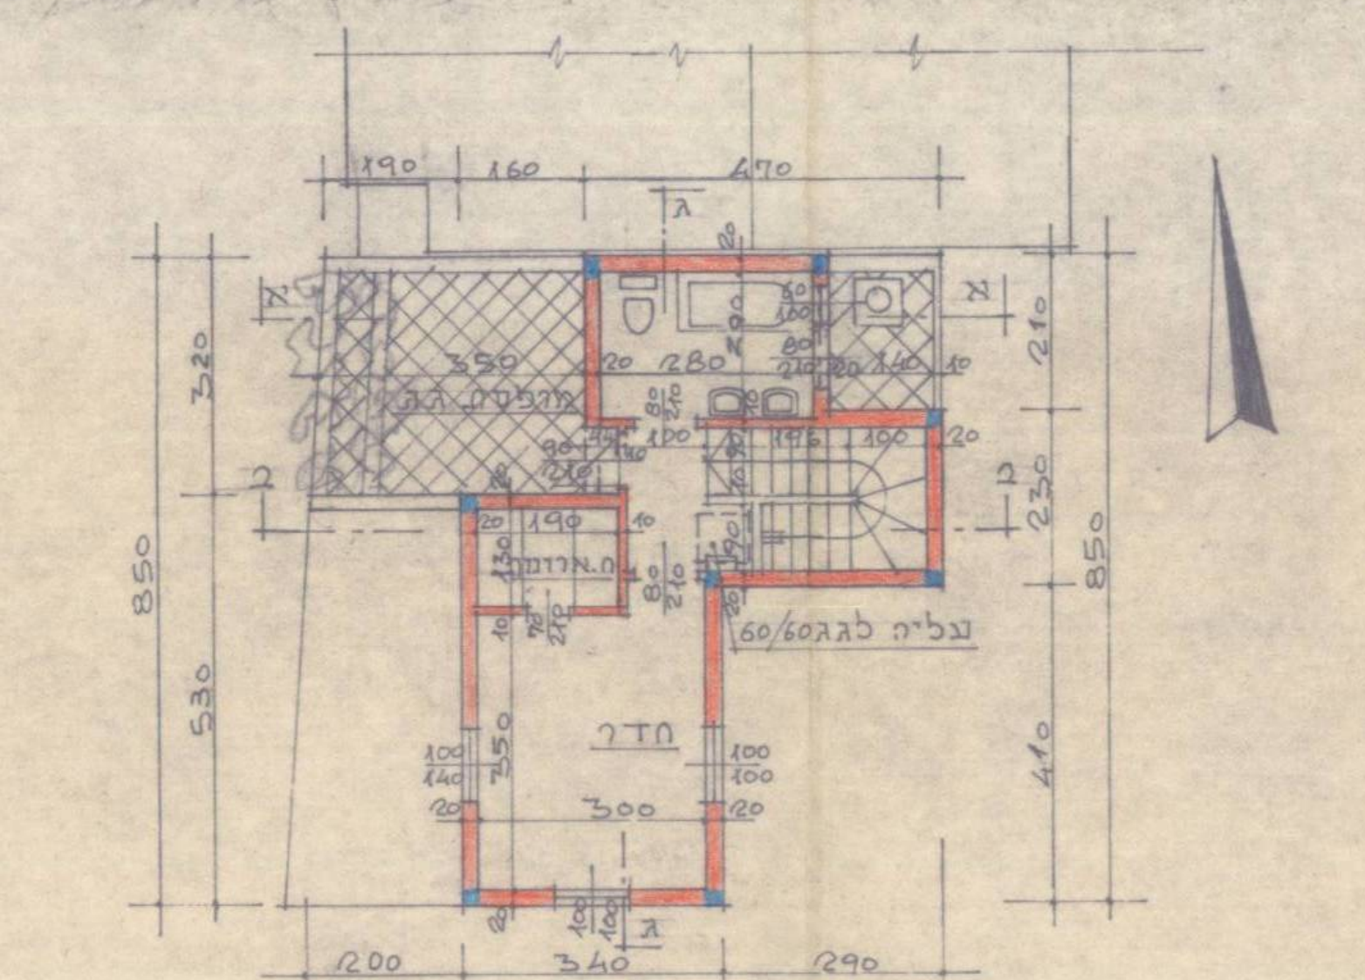
חדר
300
340
830
850
200
290

תכנית קומה ב' ק.מ. 1:100

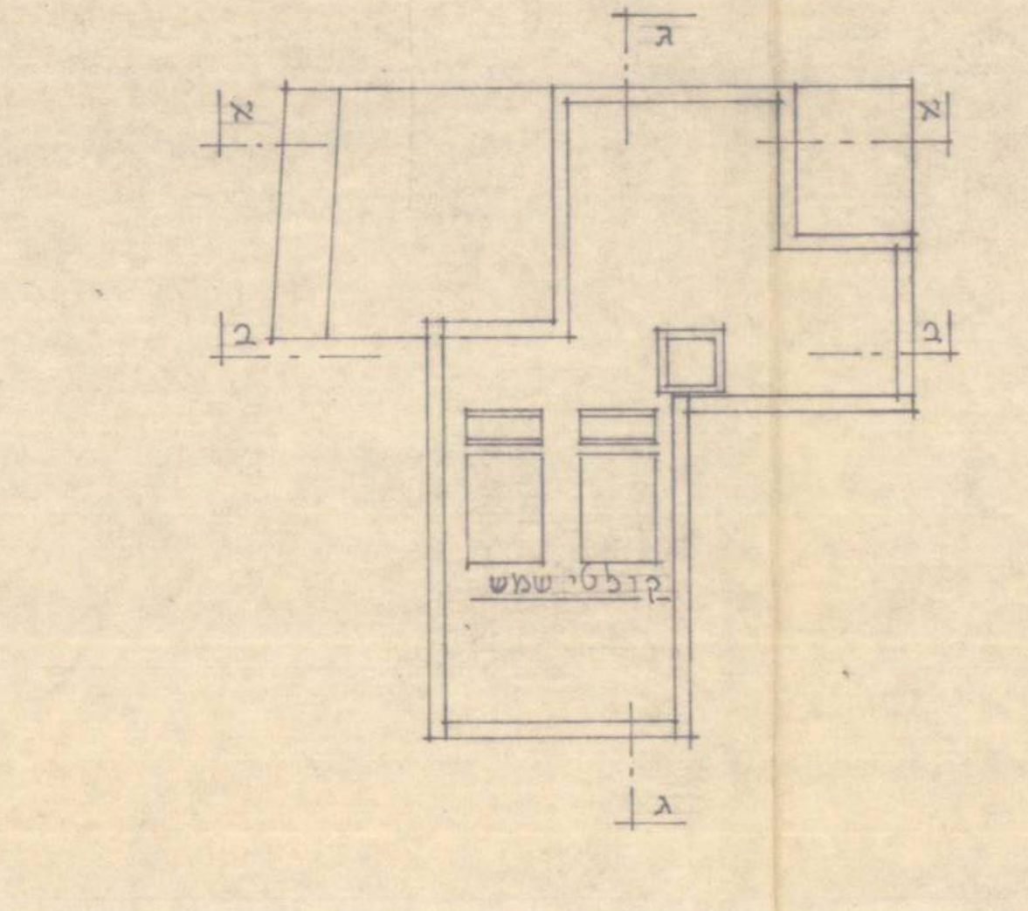
קולטי שמש
א
ב
ג

תכנית הגג קמ. 1:100

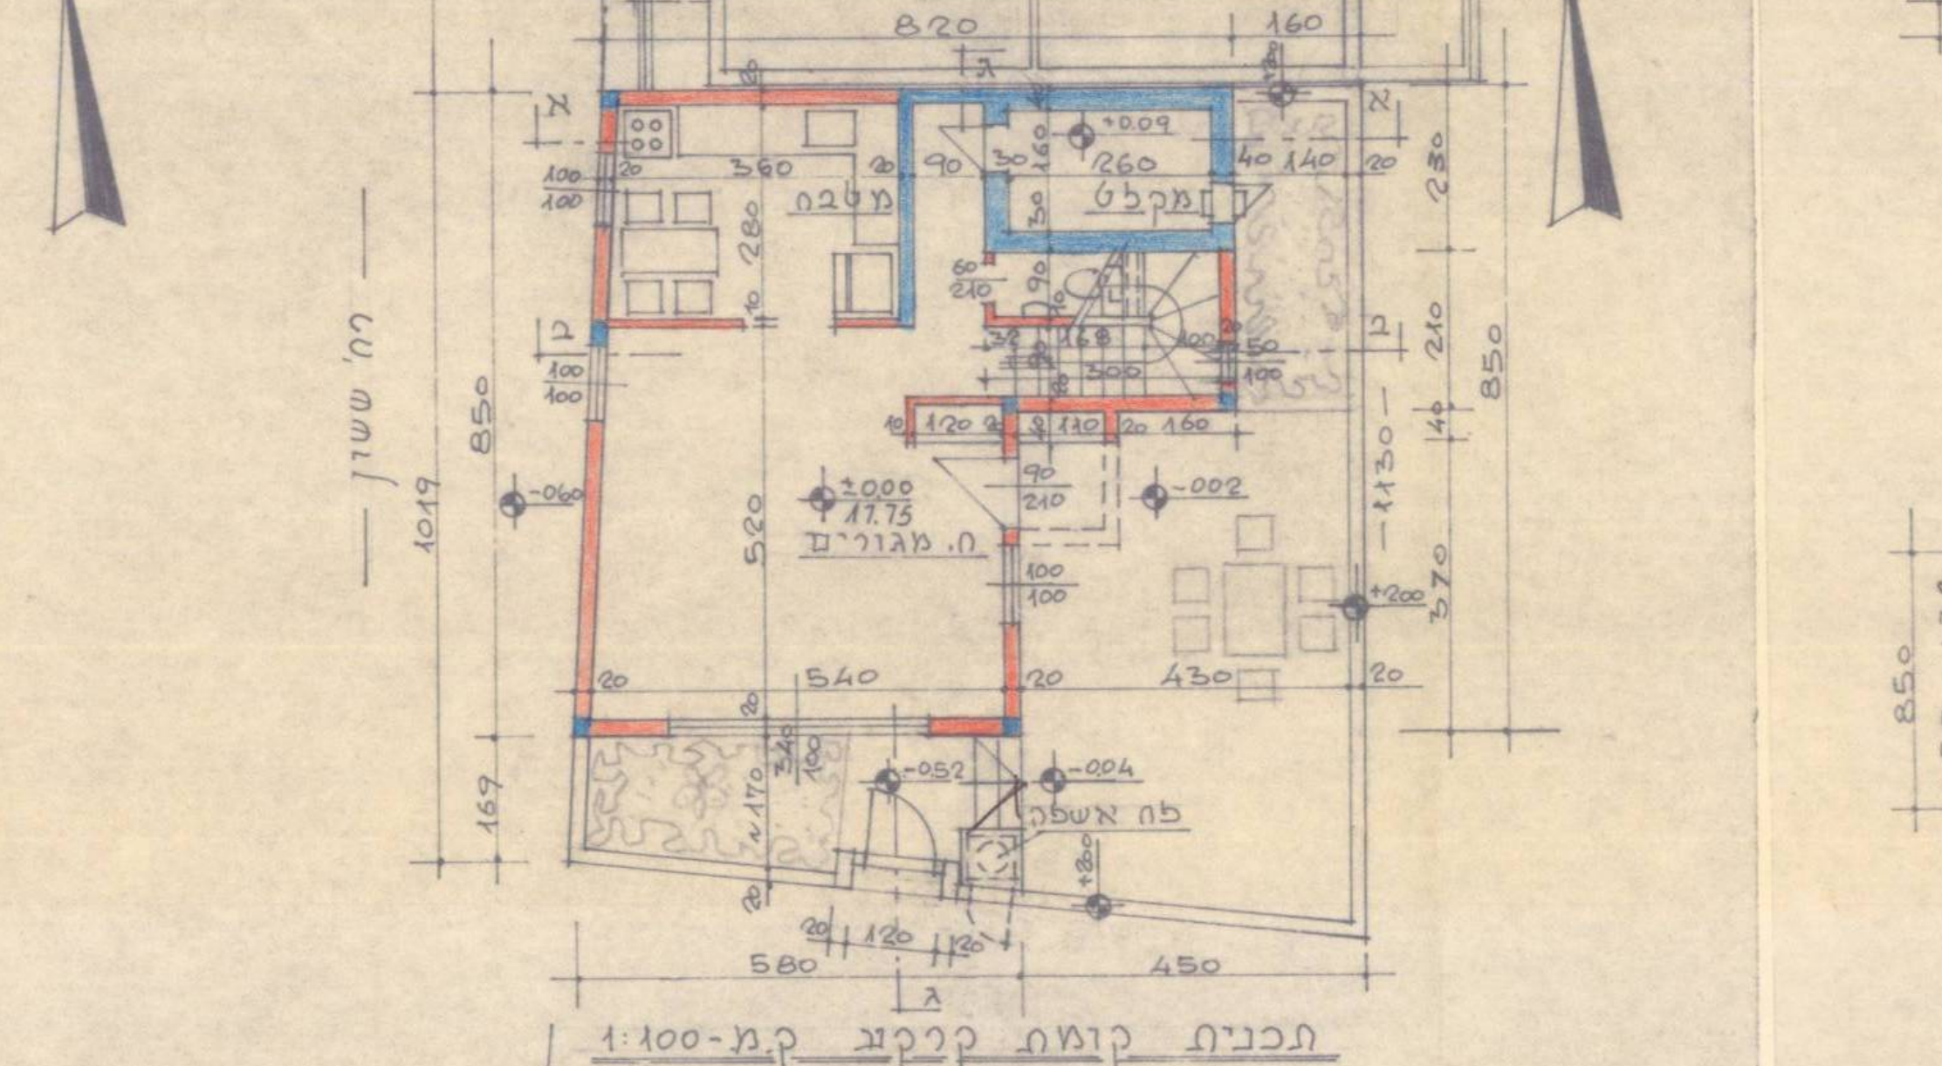
גדר משותפת
חדר
מקלט
מטבח
ח. מגורים
פח אשפה
רח' ששון
850
1019
540
580
450
1035

תכנית קומת קרקע קמ. 1:100

סגלוביץ רח' ששון 27

4

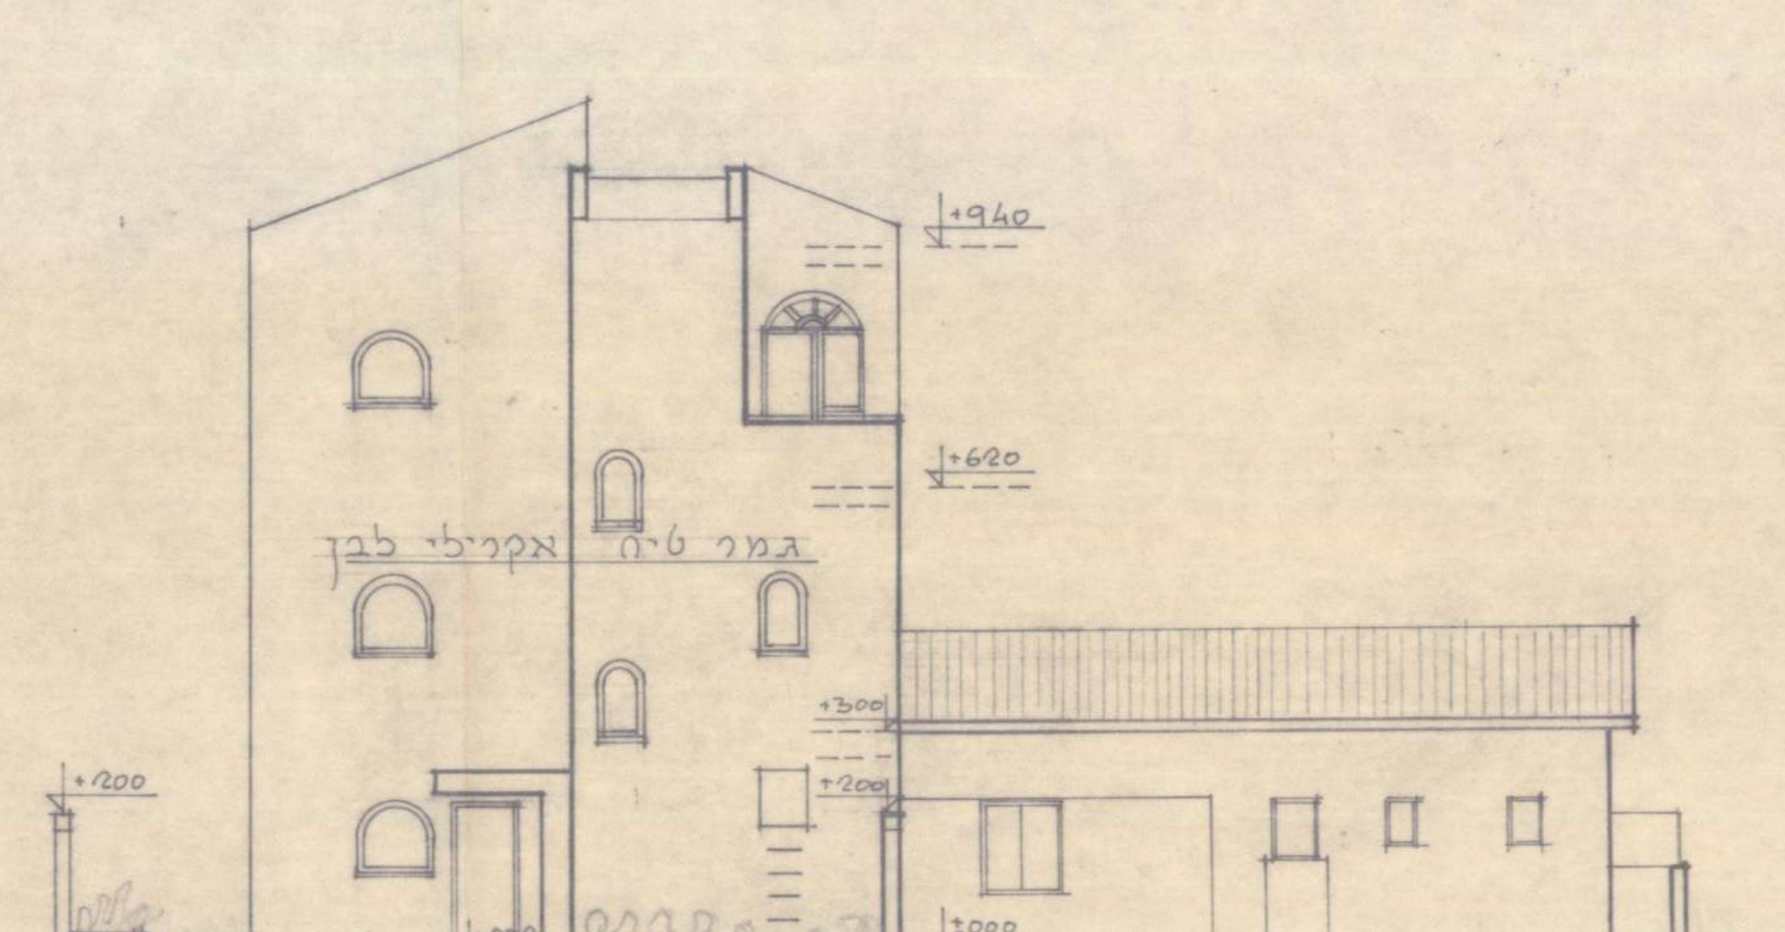
גמר טיח אקרילי לבן
בית קיים
+9.40
+6.20
+3.00
±0.00

חזית מזרחית ק.מ. 1:100

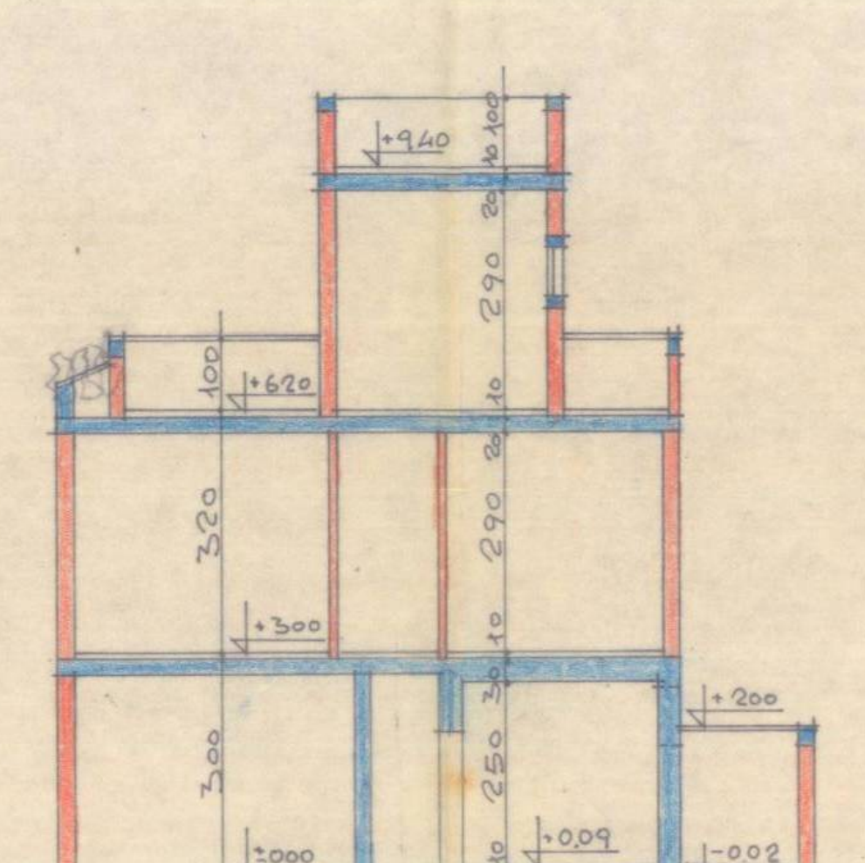
+9.40
+6.20
+3.00
±0.00

חתך א-א ק.מ. 1:100

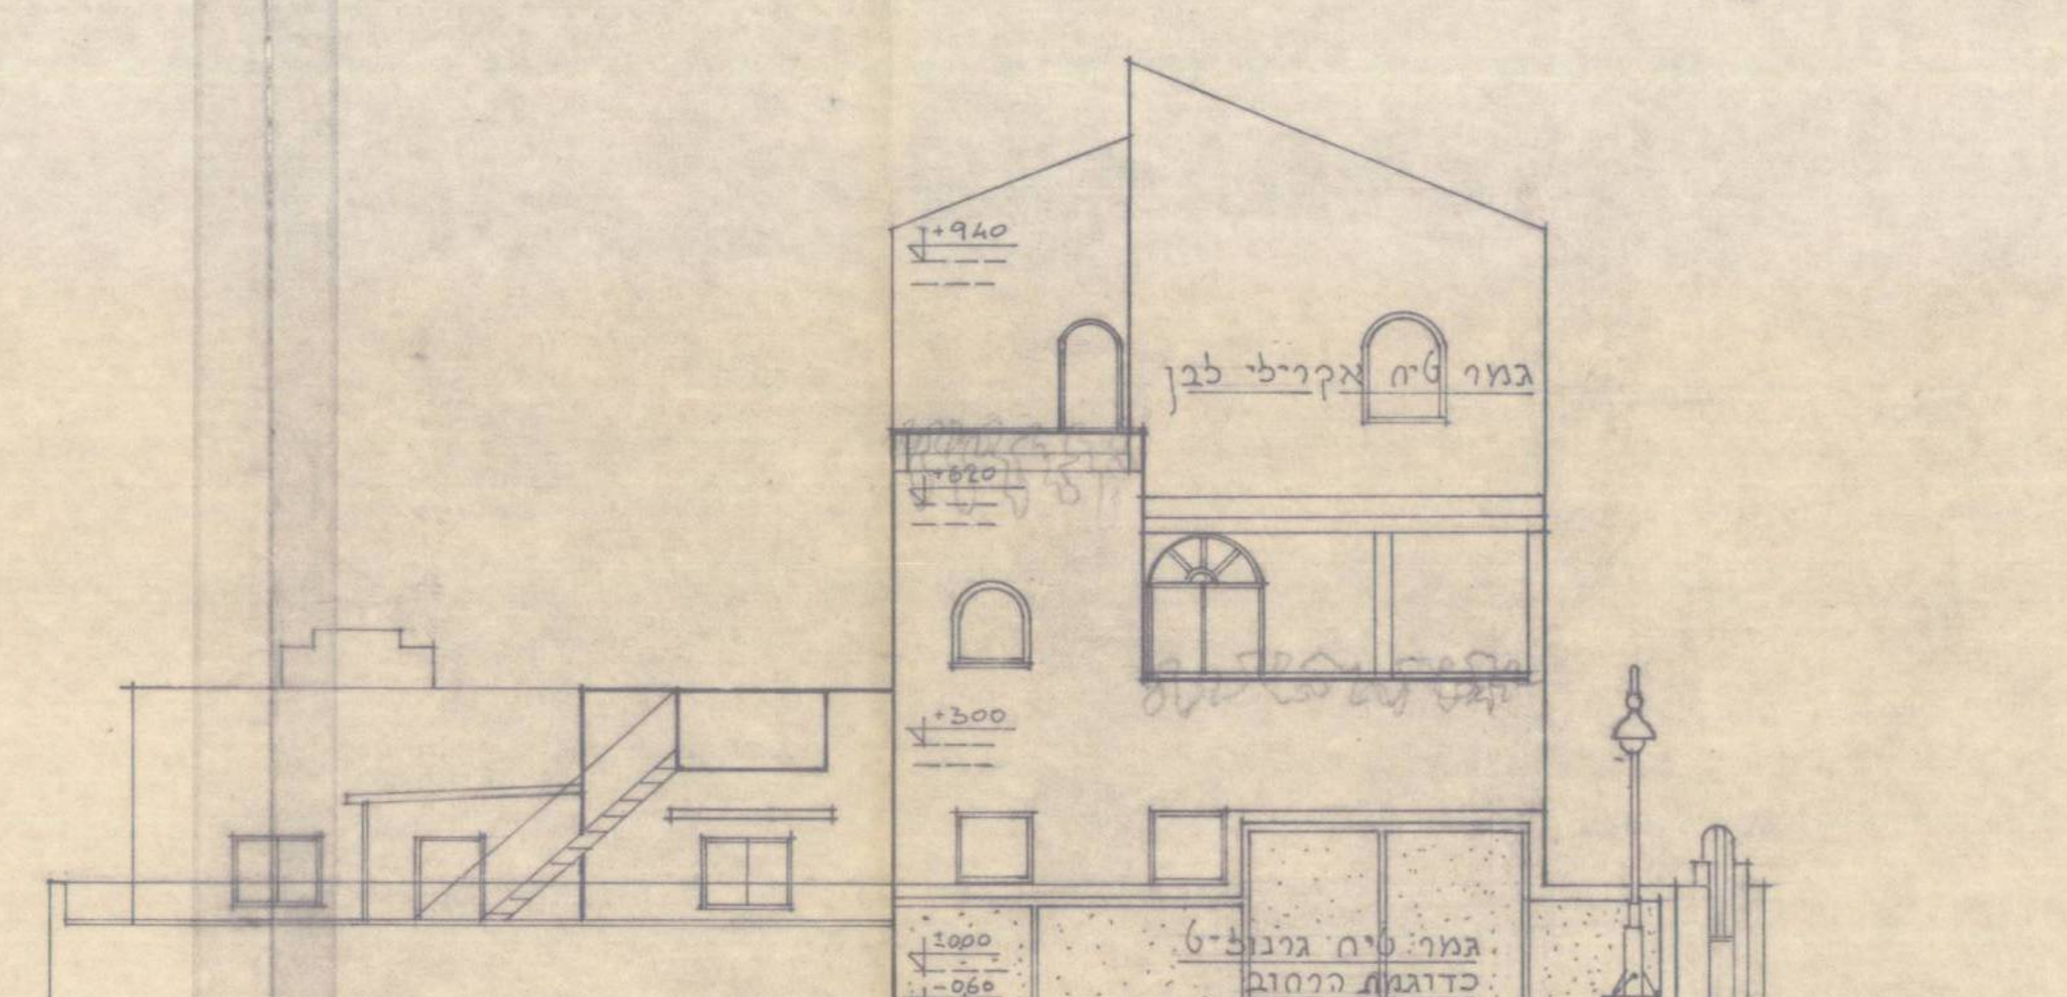
גמר טיח אקרילי לבן
גמר טיח גרנוליט כדוגמת הרחוב
בית קיים
+9.40
+3.00
±0.00
-0.60

חזית מערבית ק.מ. 1:100

אדנית ועמוד תאורה לפי תכנית פיתוח מאושרת. רח' ששון - בביצוע

סורגים פנימיים בגוון לבן בלבד

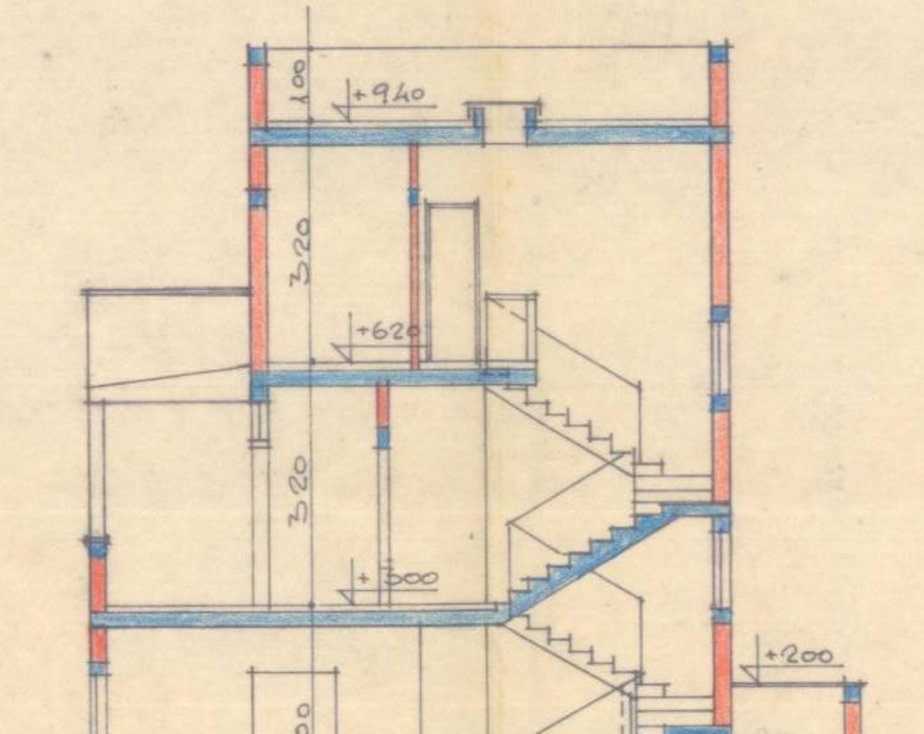
+9.40
+6.20
+3.00
±0.00
-0.60

חתך ב-ב ק.מ. 1:100

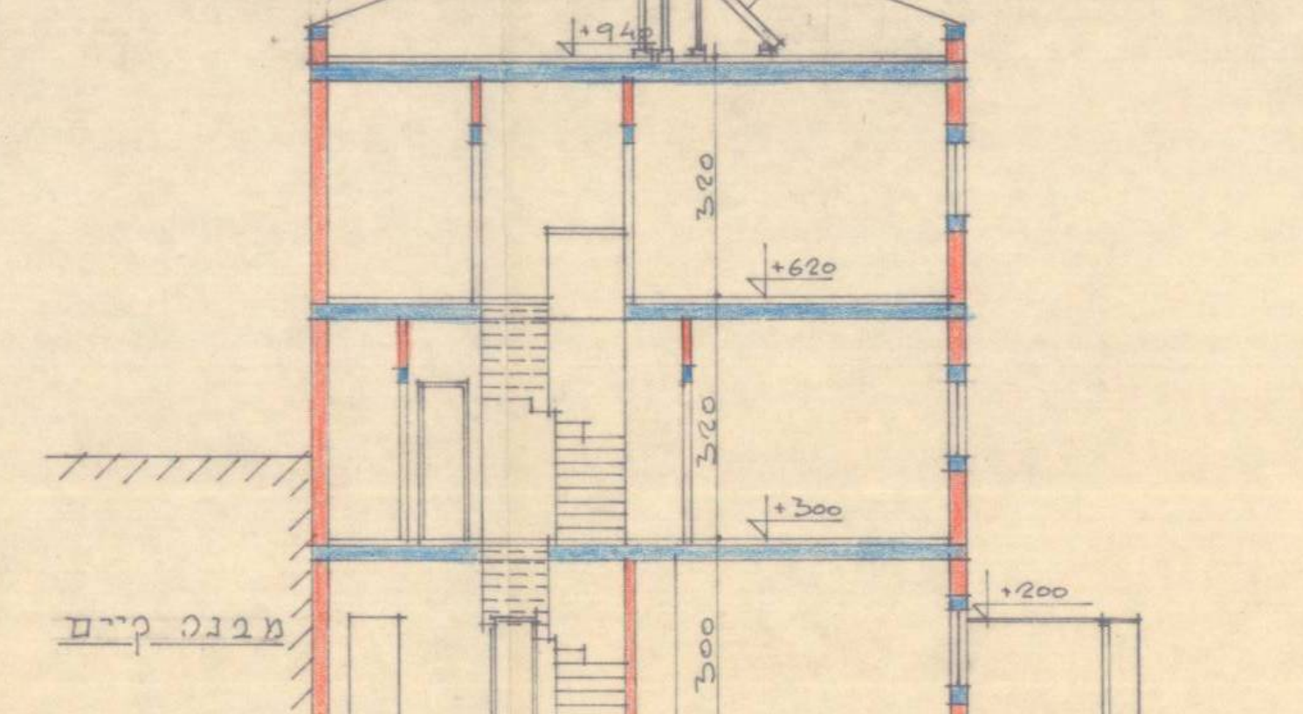
קולטי שמש
מבנה קיים
+9.40
+6.20
+3.00
±0.00

חתך ג-ג ק.מ. 1:100

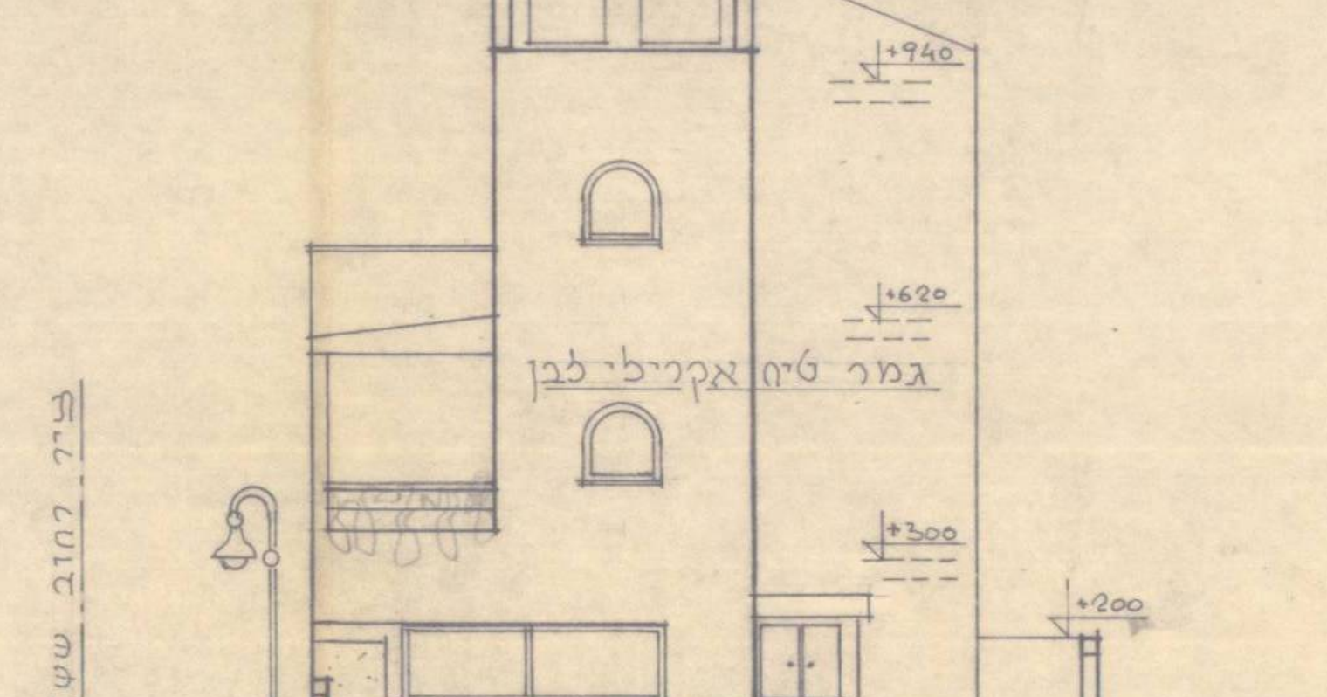
גמר טיח אקרילי לבן
ציר רחוב ששון
+9.40
+6.20
+3.00
±0.00
-0.60

חזית דרומית ק.מ. 1:100

סגלוביץ רח' ששון 27

5

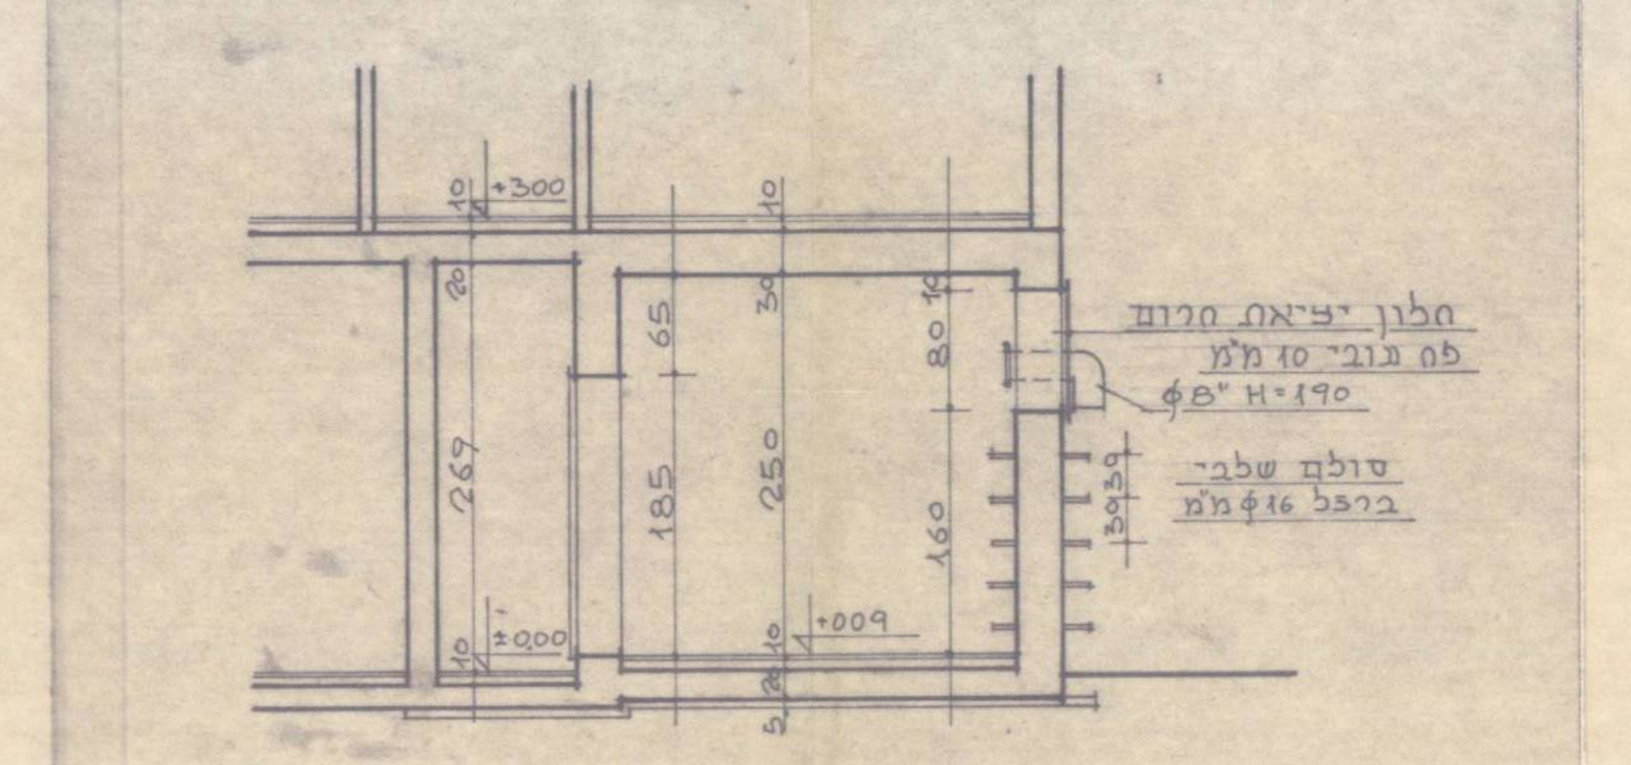
חלון יציאה חרום
פח עובי 50 מ"מ
ϕ8" H=190
סולם שלבי ברזל ϕ16 מ"מ
269
185
250
160
±0.00
+3.00

חתך 1-1 – 1:50

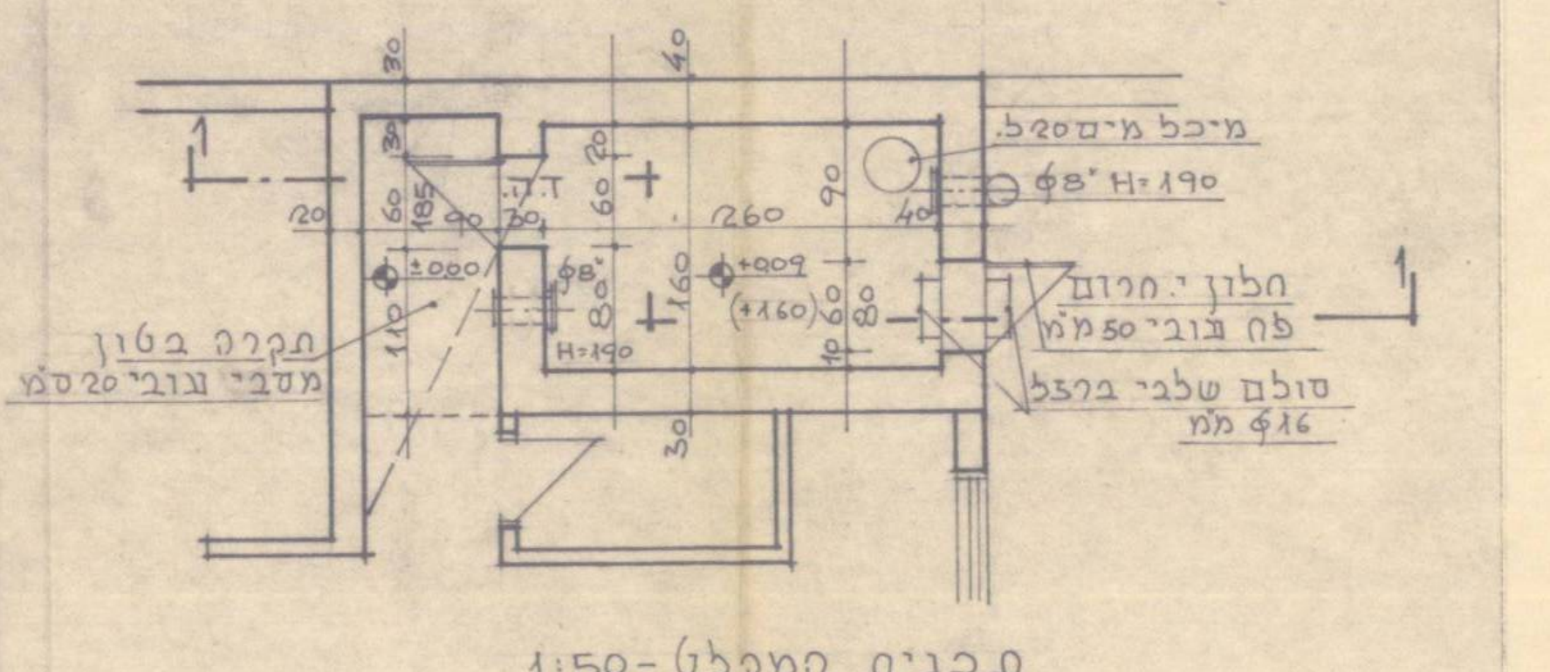
מיכל מים 50 ל.
ϕ8" H=190
חלון חרום פח עובי 50 מ"מ
סולם שלבי ברזל ϕ16 מ"מ
תקרה בטון מעבי עובי 20 ס"מ
260
160

תכנית המקלט 1:50

שטח המקלט נטו 260 × 160 = 4.16 מ"ר

סגלוביץ רח' ששון 27

6

הוראות ביצוע למקלט

א. ב-150 - תשתית בטון מתחת לרצפה.

ב. בטון המקלט ב-300 לפי תקן ישראלי 118 שנבדק ע"י מכון התקנים או מוסד מוסמך אחר.

ג. פלדת הזיון לפי תקן ישראלי כמפורט במפרט הכללי למקלטים (58).

ד. בידוד הרצפה והקירות יש לבצע בהתאם למפרט הכללי למקלטים, להלן פירוט מערכת ביטומנית, לאחר שהמקלט יבנה בתנאי סביבה רגילה (ללא מי תהום או אדמה חרסית בעלת פלסטיות גבוהה):-

1. **רצפה** פריימר זפת חם 75/25, שתי שכבות סיבאסט עם שכבת זפת חם 75/25 ביניהם, שכבת זפת חם 75/25 עם ניר טול 4 פליי.
2. **קירות חוץ** פריימר זפת חם 75/25, ארג זכוכית, זפת חם 75/25, קלקר 2.5 ס"מ.

ה. לא יבוצעו טיח קירות + תקרה או כל ציפוי אחר במקלט ובדרך הגישה אליו.

ו. היציקות יש לבצע בתבניות מדיקטים או לוחות ממתכת בלבד.

על הקבלן/המבקש להזמין את המהנדס האחראי על ביצוע השלד ולקבל אישור לביצוע כל שלבי המקלט, יש להזמין את המפקח מטעם הרשות המקומית לבדיקת שלבי בנית המקלט, על הרשות המקומית להקפיד על מסירה לועדה המקומית תצהיר של האחראי לביצוע השלד בהתאם לקובץ התקנות 3892 מיום 21.9.78 לחוק התכנון והבניה תשכ"ה - 1965 תקנות בדבר תצהיר על הקמת שלד מקלט.

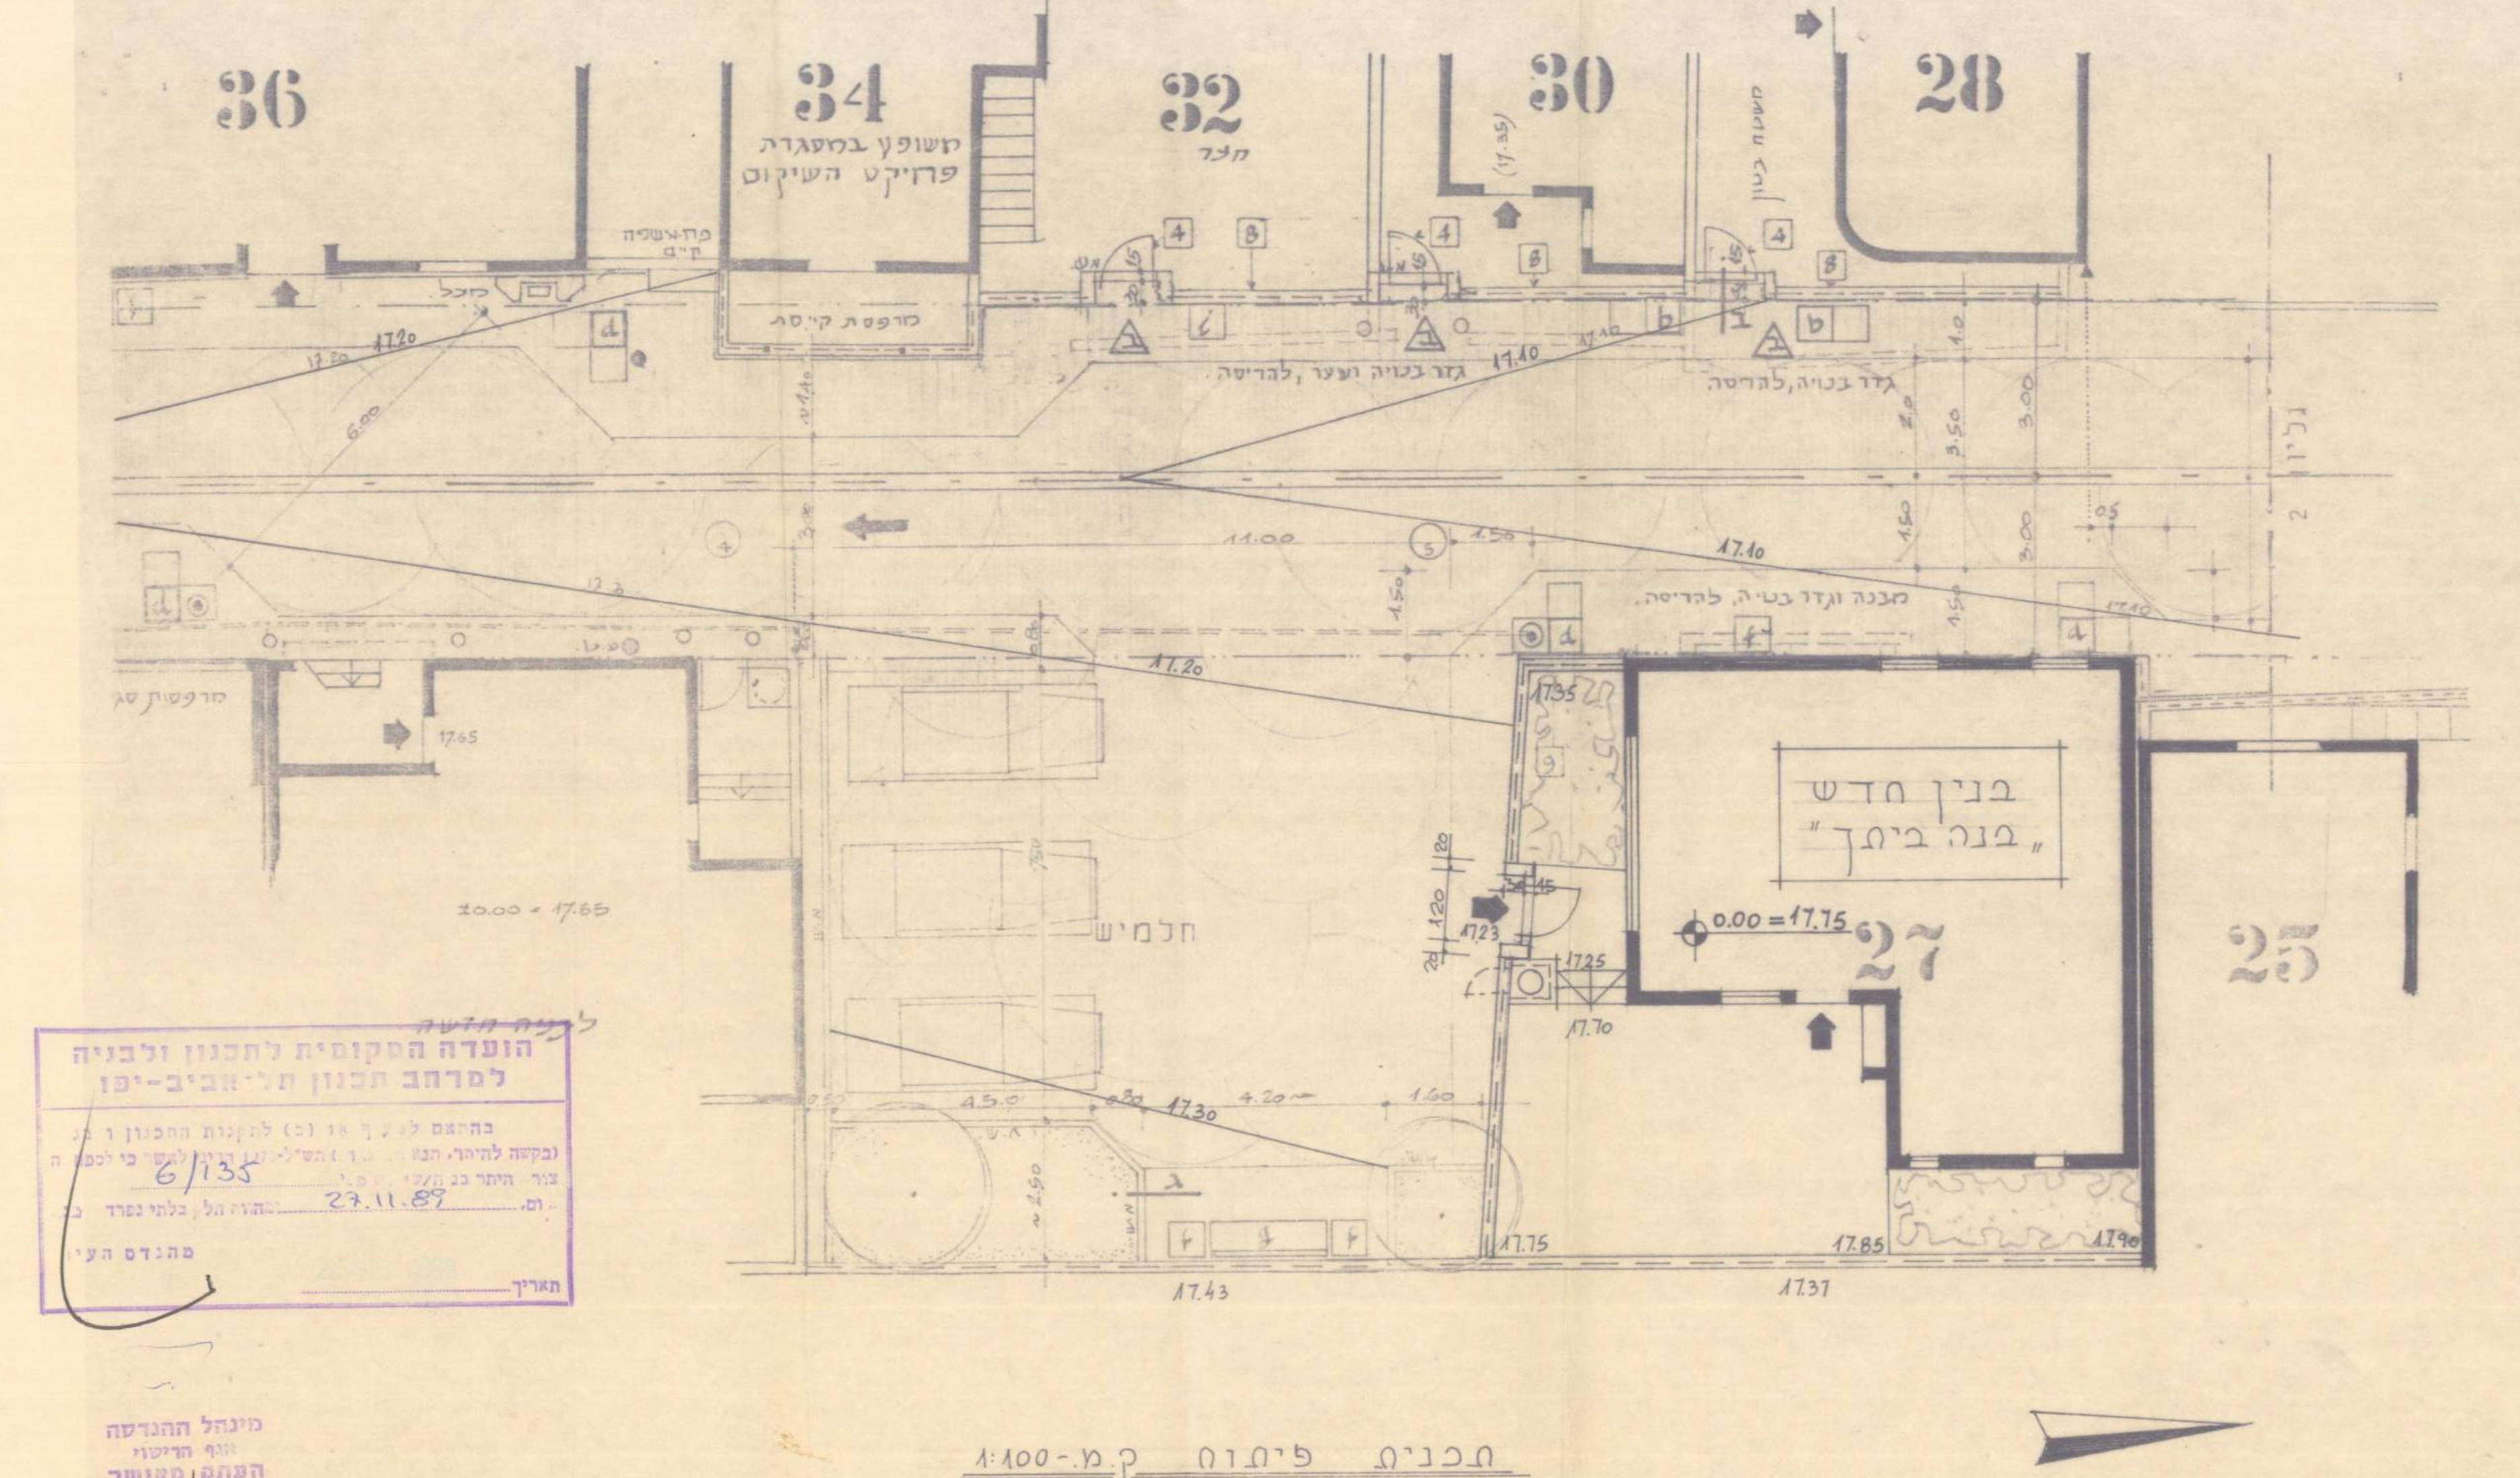
36
34
32
30
28
27
25
יושפץ במסגרת פרויקט השיקום
בנין חדש בנה ביתך
0.00 = 17.75
חלמיש
17.40
17.75
17.85
17.90
17.43
17.37
גן ליון

תכנית פיתוח קמ-1:100

הועדה המקומית לתכנון ולבניה לסרחב תכנון תל־אביב־יפו
6/135
23.11.89
מהנדס העיר
תאריך

מינהל ההנדסה
הפקח המוסמך