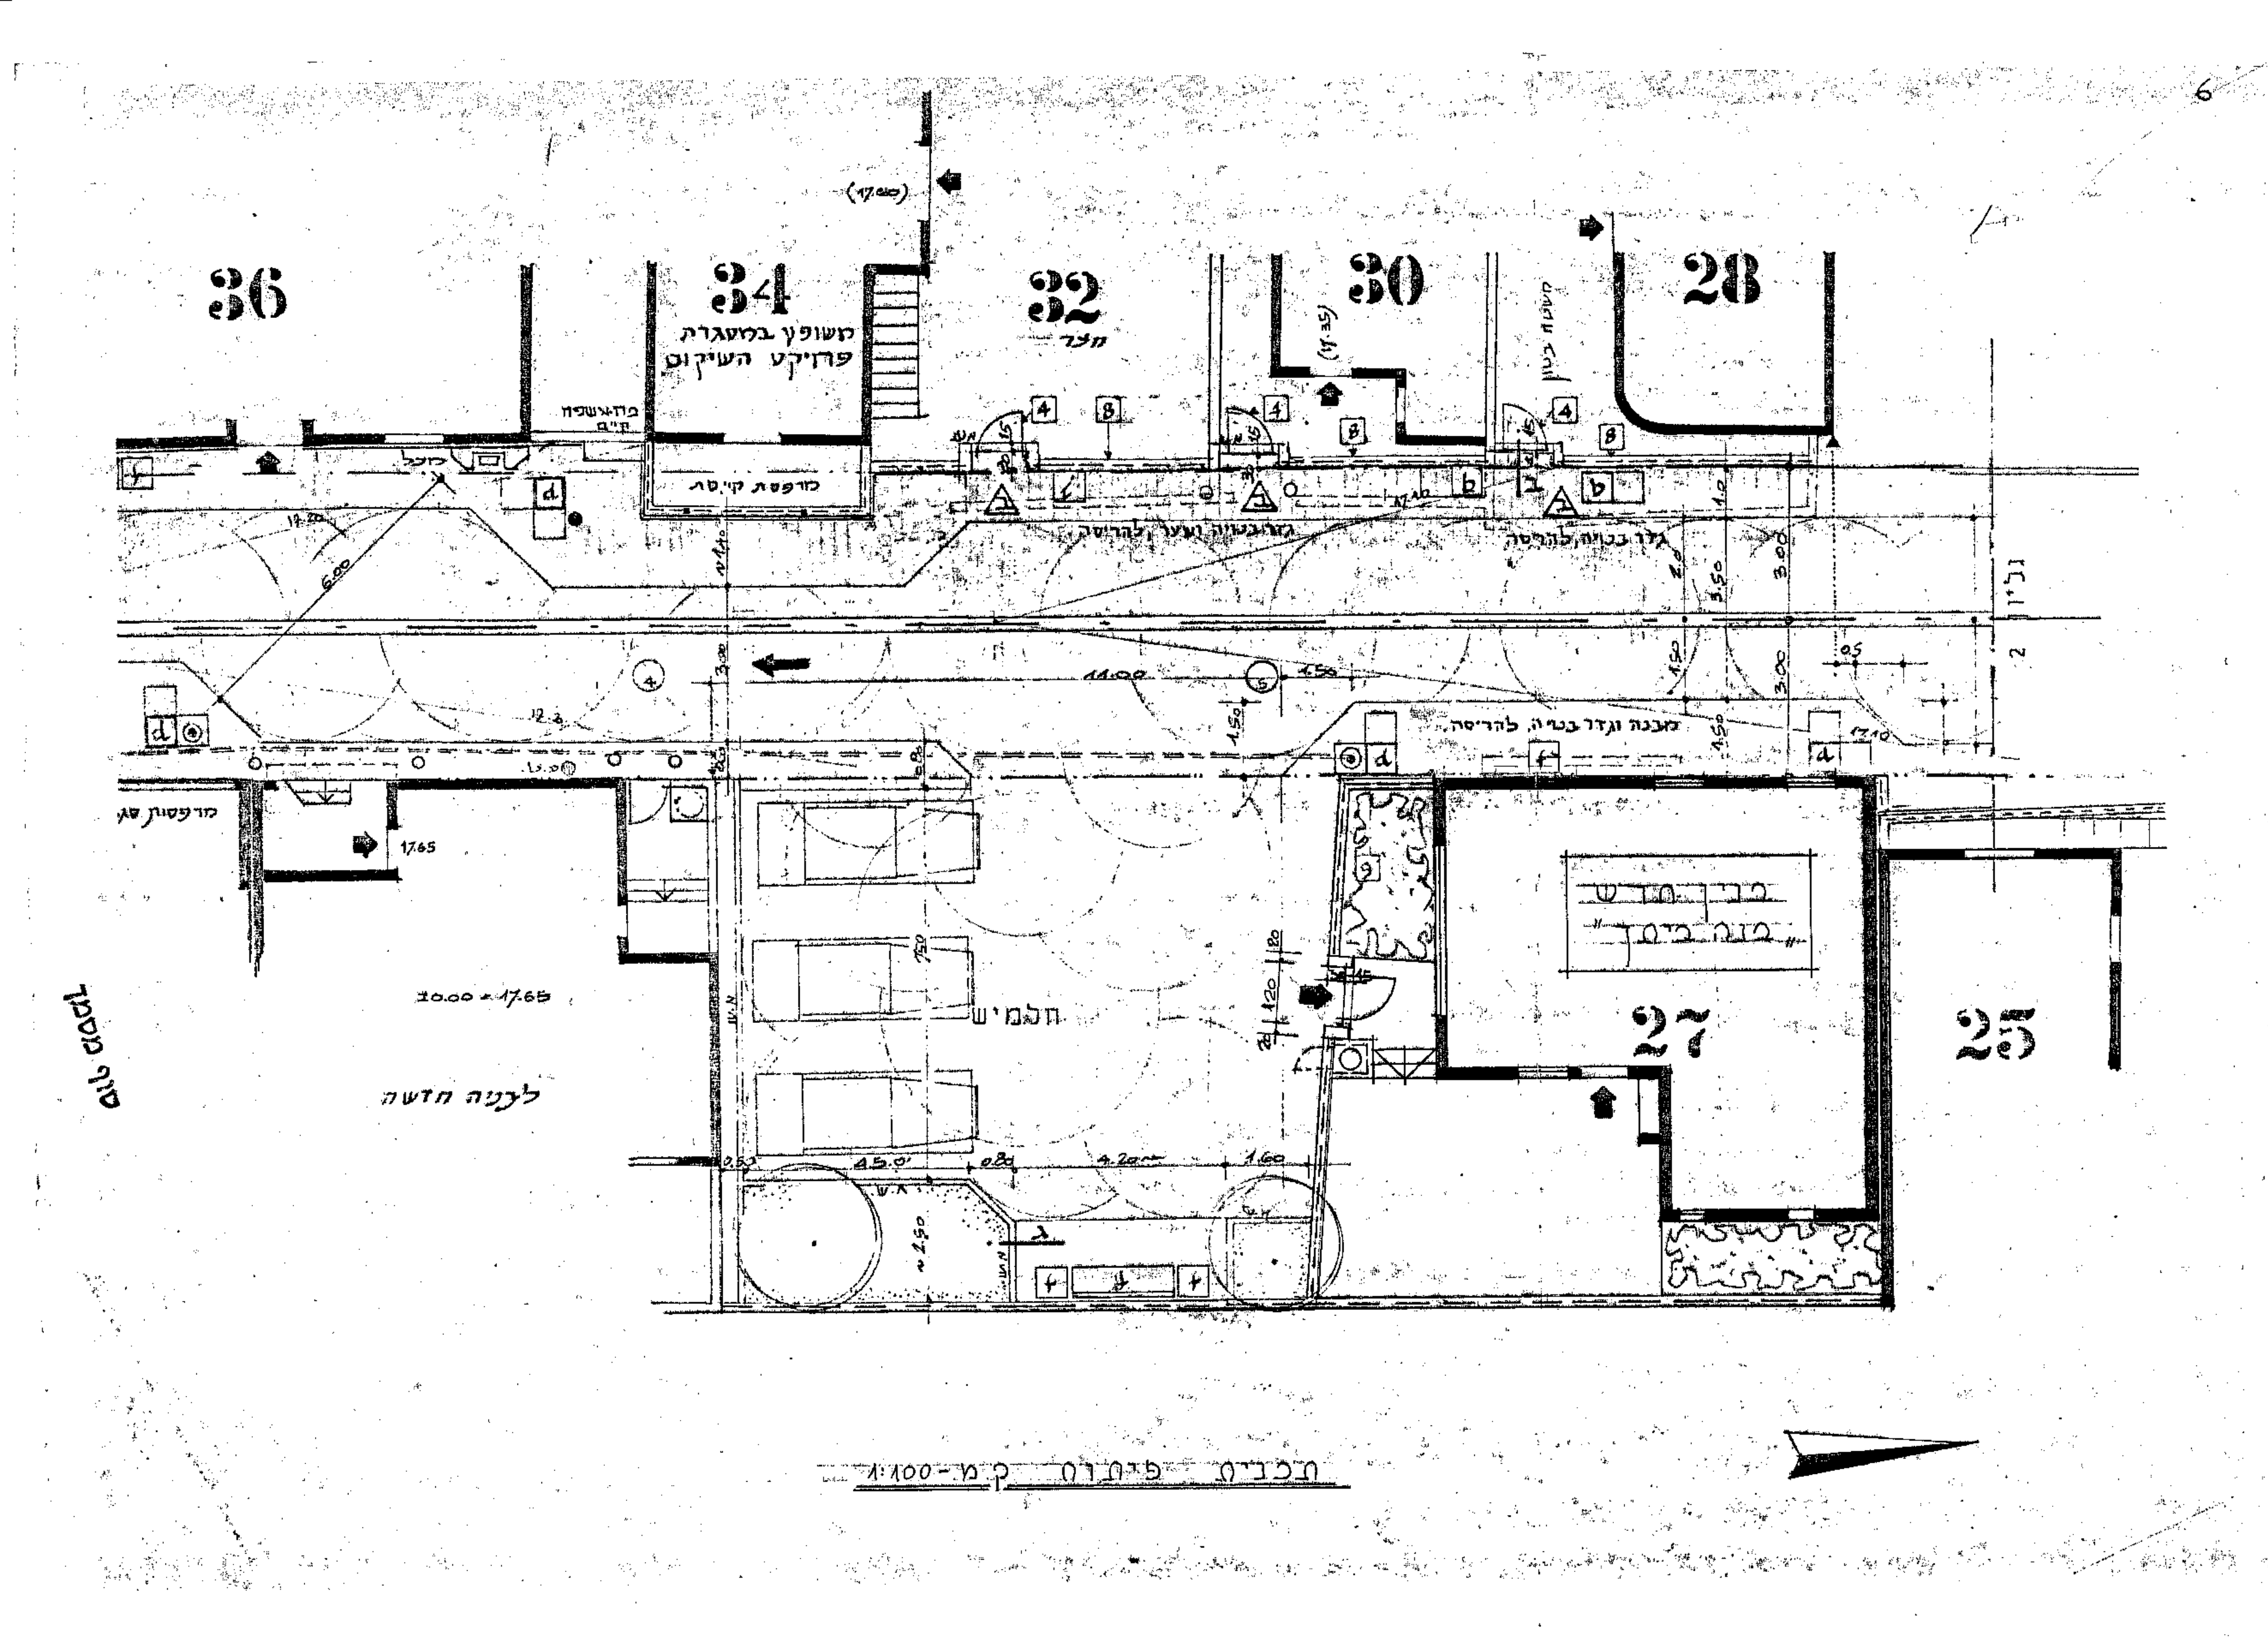
36
34
32
30
28
27
25
משופץ במסגרת פרויקט השיקום
מעבר
תכנית חדש
בנין חדש בנה בביצוע
חמש
לבנות חדשה
ששון
30.00 + 17.65
גן בנוי להריסה
מבנה וגדר בנויה להריסה
מדרכה קיימת
11.00

תכנית פיתוח קנ"מ 1:100

הוראות ביצוע למקלט

א. ב-150 – תשתית בטון מתחת לרצפה.

ב. בטון המקלט ב-300 לפי תקן ישראלי 118 שנבדק ע"י מכון התקנים או מוסד מוסמך אחר.

ג. פלדת הזיון לפי תקן ישראלי כמפורט במפרט הכללי למקלטים (58).

ד. בידוד הרצפה והקירות יש לבצע בהתאם למפרט הכללי למקלטים, להלן פירוט מערכת ביטומנית, לאחר שהמקלט יבנה בתנאי סביבה רגילה (ללא מי תהום או אדמה חרסית בעלת פלסטיות גבוהה):-

1. **רצפה** פריימר ופת חם 75/25, שתי שכבות סיבאסט עם שכבת זפת חם 75/25 ביניהם, שכבת זפת חם 75/25 עם ניר טול 4 פליי.
2. **קירות חוץ** פריימר וזפת חם 75/25, ארג זכוכית, זפת 75/25 קלקר 2.5 ס"מ.

על הקבלן/המבקש להזמין את המהנדס האחראי על ביצוע השלד ולקבל אישור לביצוע כל שלבי המקלט, יש להזמין את המפקח מטעם הרשות המקומית לבדיקת שלבי בנית המקלט, על הרשות המקומית להקפיד על מסירה לועדה המקומית תצהיר של האחראי לביצוע השלד בהתאם לקובץ התקנות 3892 מיום 21.9.78 לחוק התכנון והבניה תשכ"ה – 1965 תקנות בדבר תצהיר על הקמת שלד מקלט.

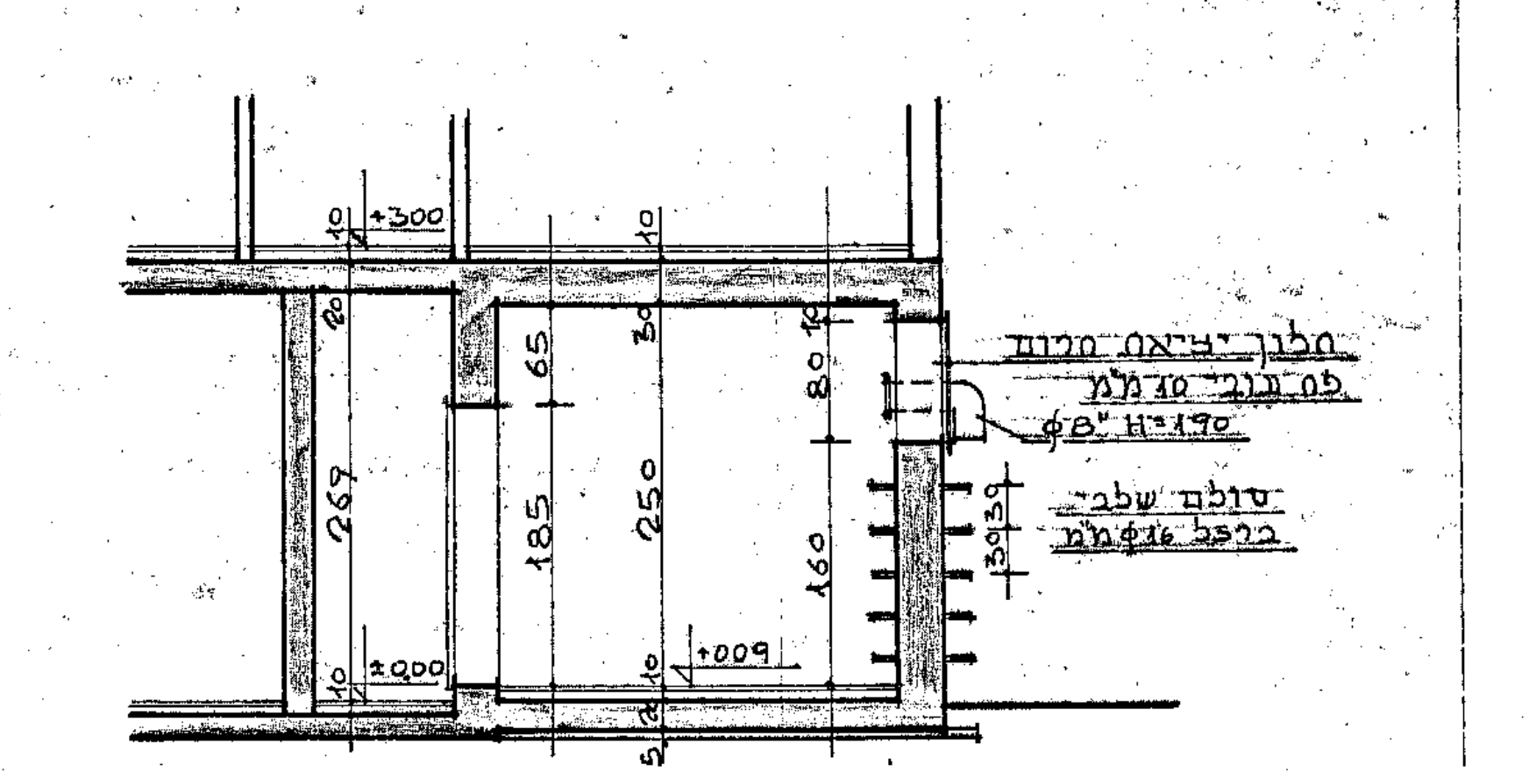
5
מלבן יציאה חרום
פח בובר 10 מ"מ
60×80 H=190
סולם שלבי ברזל 16 מ"מ
+300
±000
+009
267
185
250
160

חתך 1-1 1:50

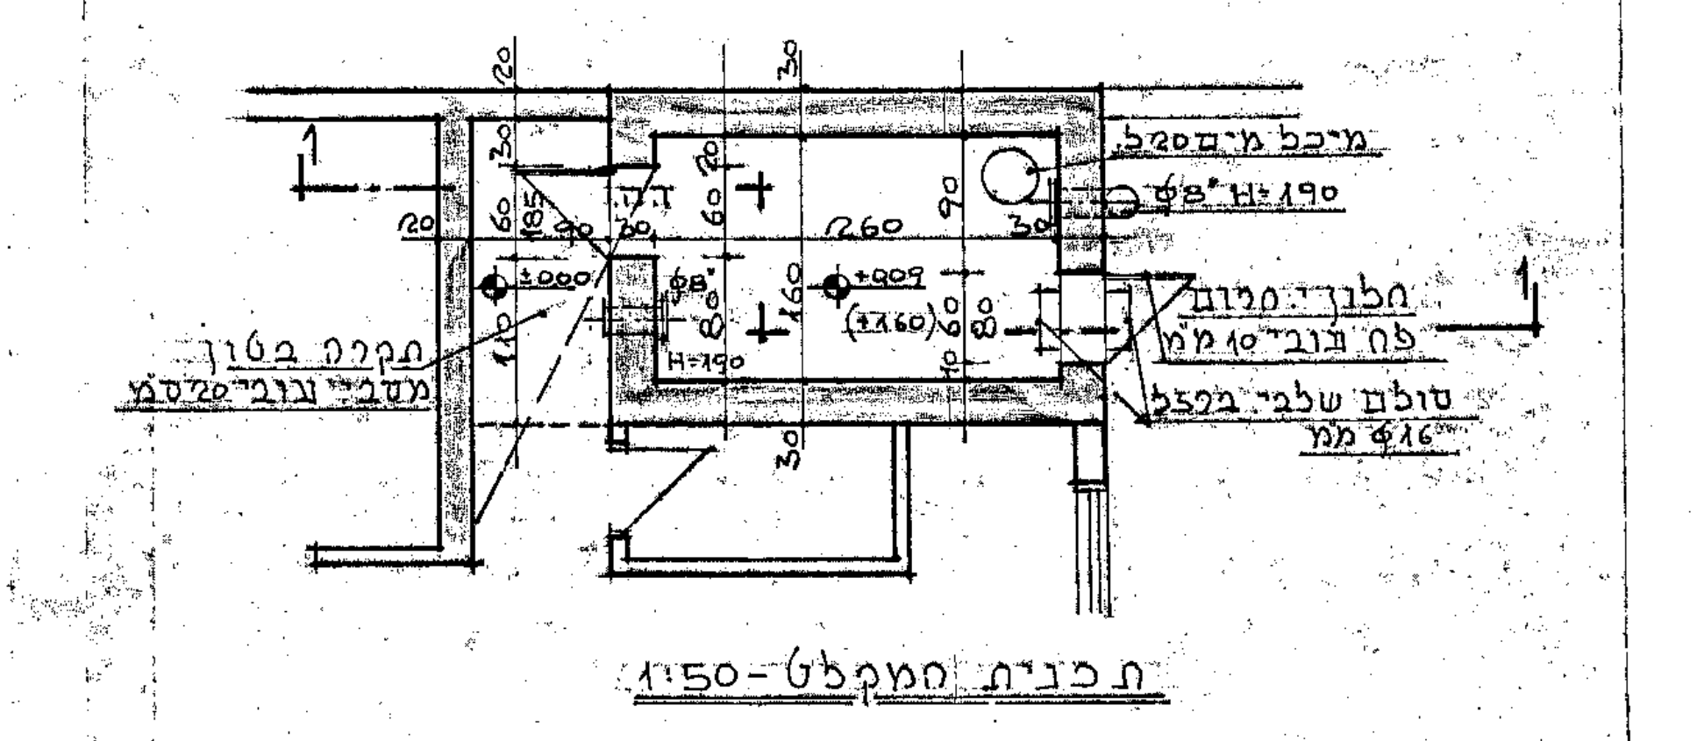
מיכל מים 50 ל'
80×H190
חלון חרום
פח בובר 10 מ"מ
סולם שלבי ברזל 16 מ"מ
תקרת בטון
משטח ברזל סמוי
260
160
±000
+009

תכנית המקלט 1:50

שטח המקלט נטו 4.16 = 2.60 × 1.60 מ"ר

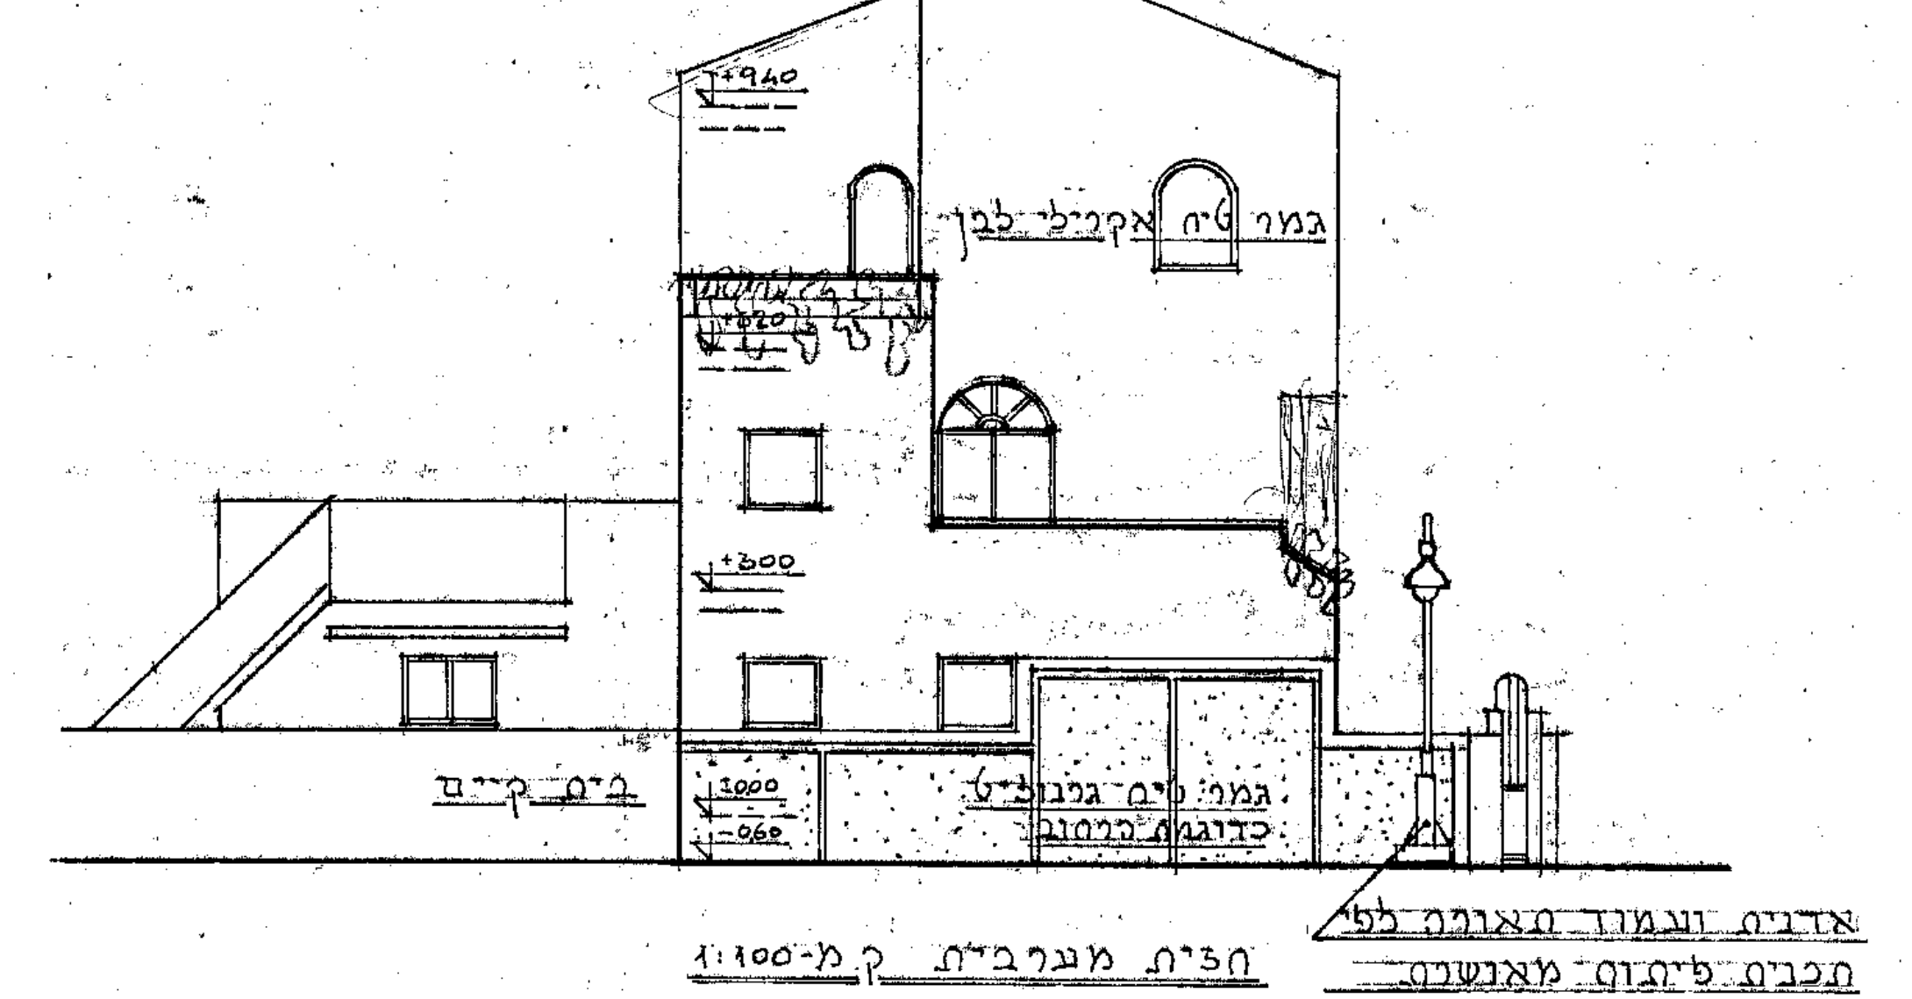
+940
+620
+300
±000
-060
גמר טיח אקרילי לבן
גמר טיח בגוון ט
בית קיים

חזית מערבית קנ"מ 1:100

אדנית ועמוד תאורה לפי תכנית פיתוח מאושרת רח' ששון – בביצוע

סורגים פנימיים בגוון לבן בלבד

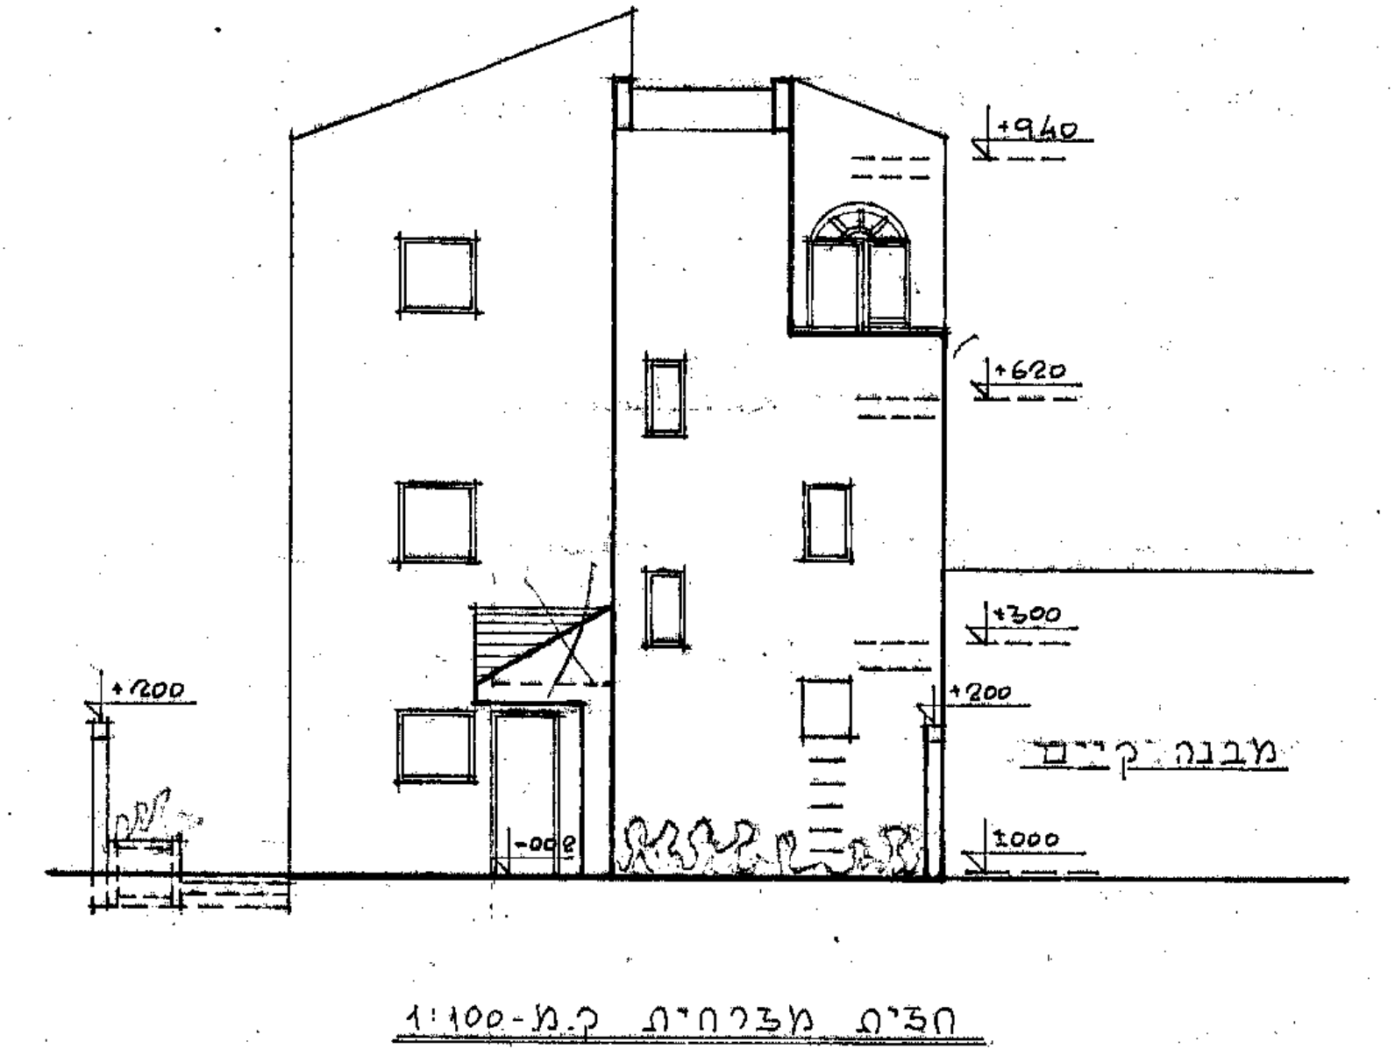
+940
+620
+300
+200
±000
מבנה קיים

חזית מזרחית קנ"מ 1:100

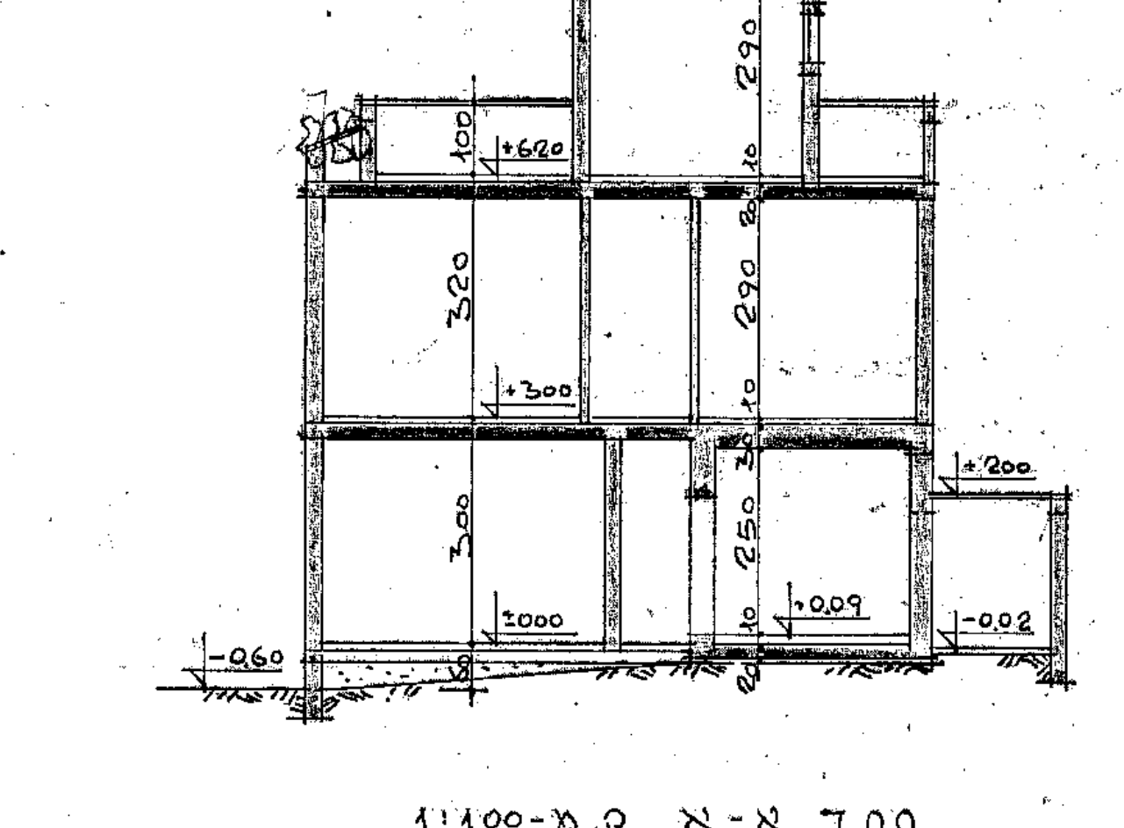
+940
+620
+300
+200
±000
-060
320
290
300

חתך א-א קנ"מ 1:100

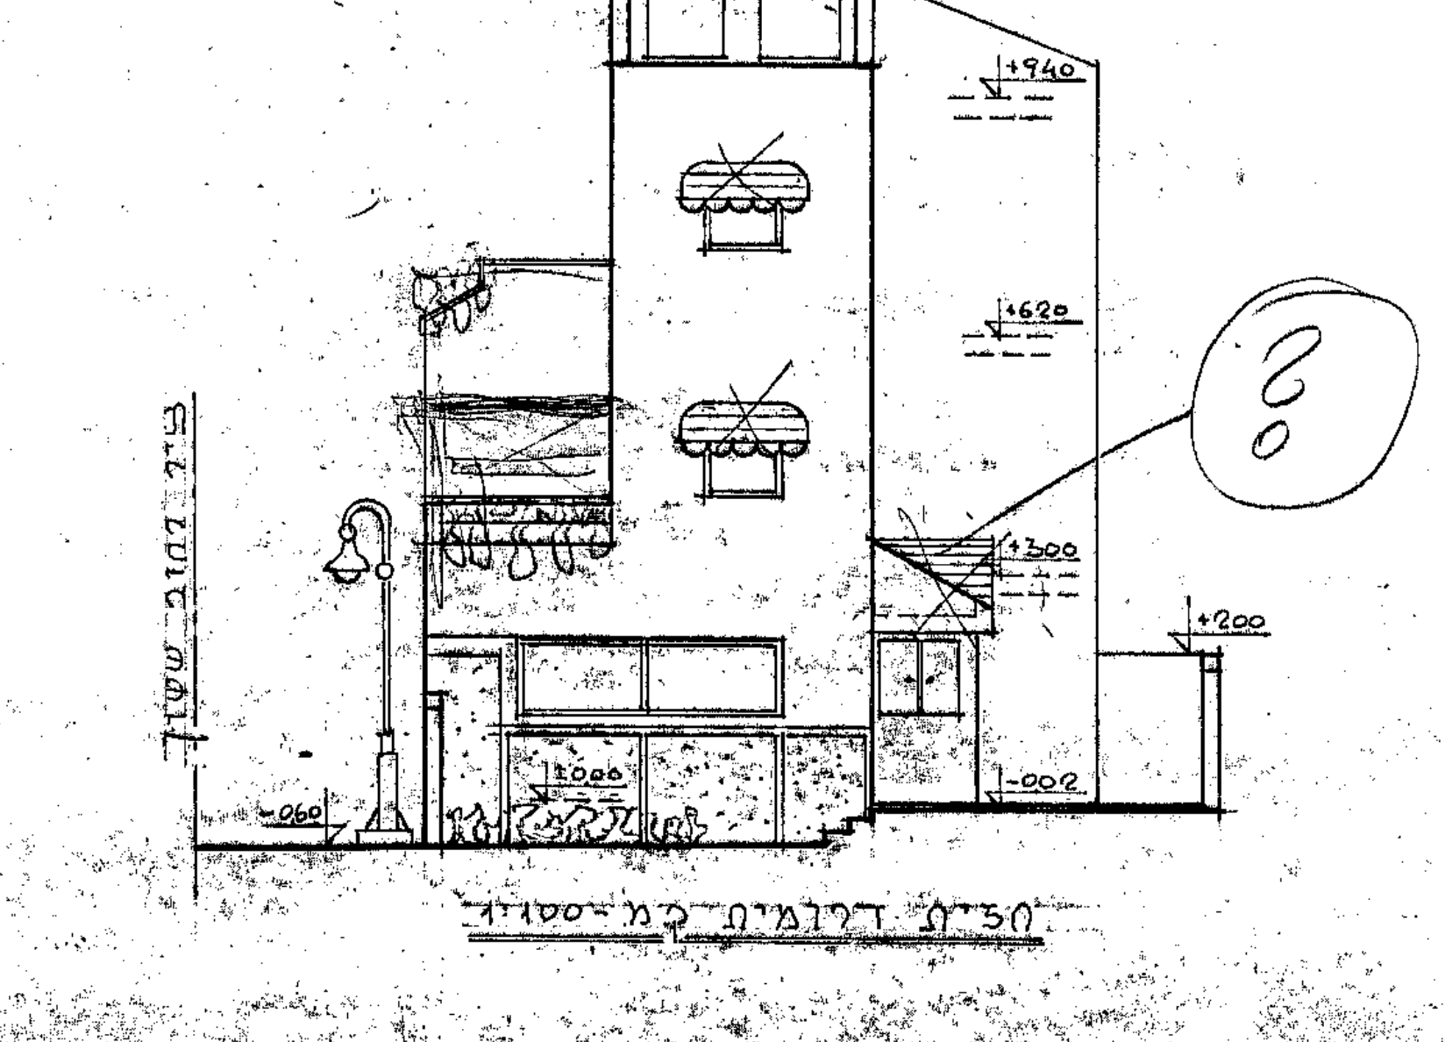
+940
+620
+300
+200
±000
-060
?
גדר רחוב ששון

חזית דרומית קנ"מ 1:100

9.1.89

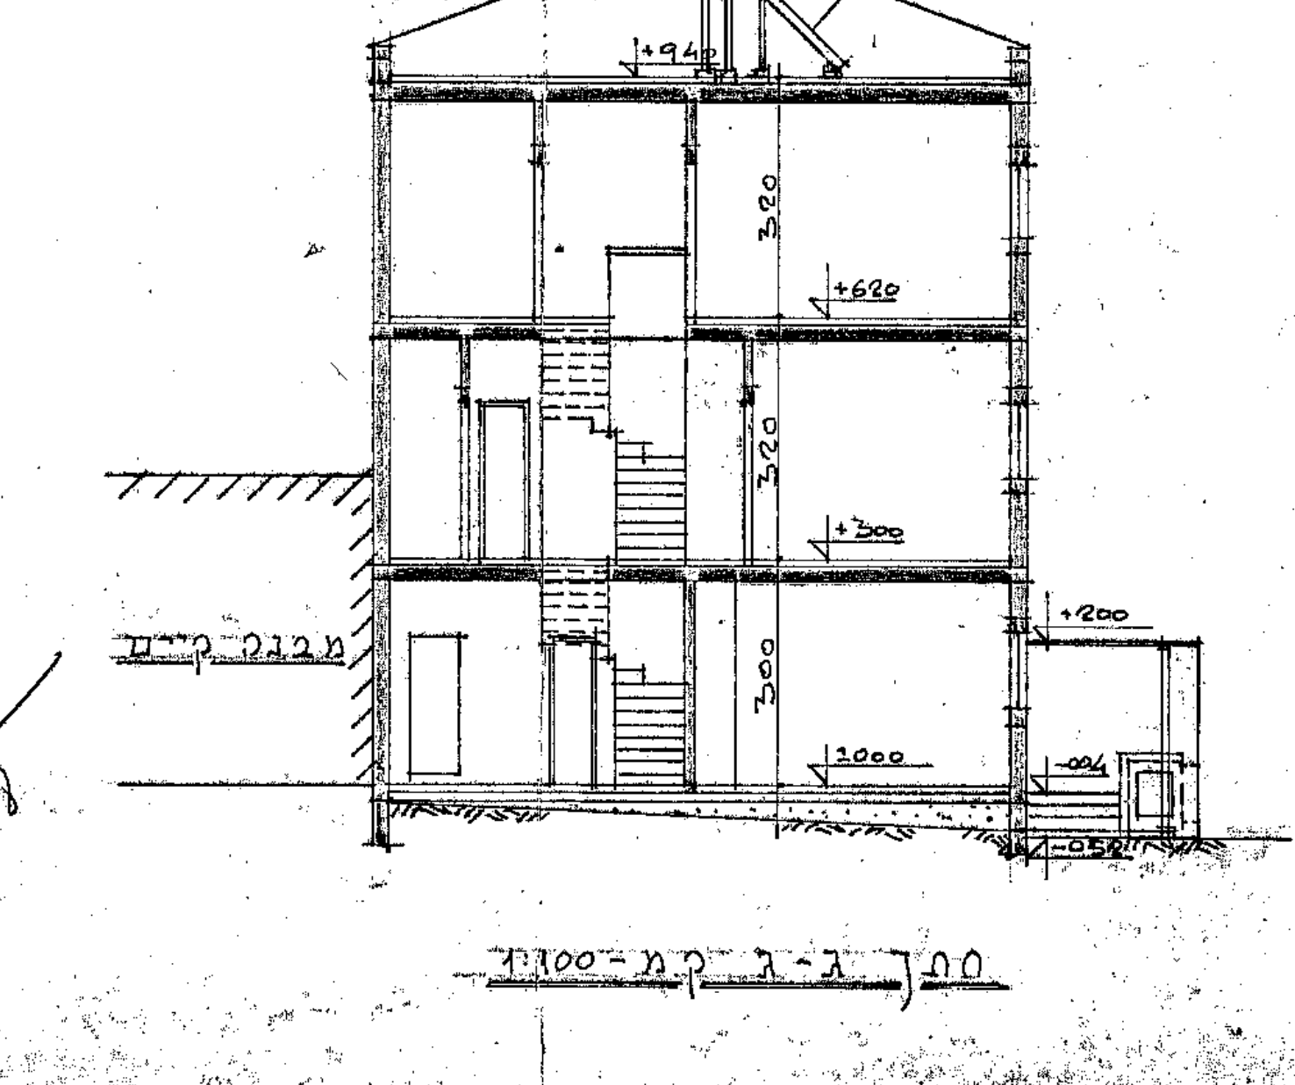
קולטי שמש
+940
+620
+300
±000
מבנה קיים
320
300

חתך ג-ג קנ"מ 1:100

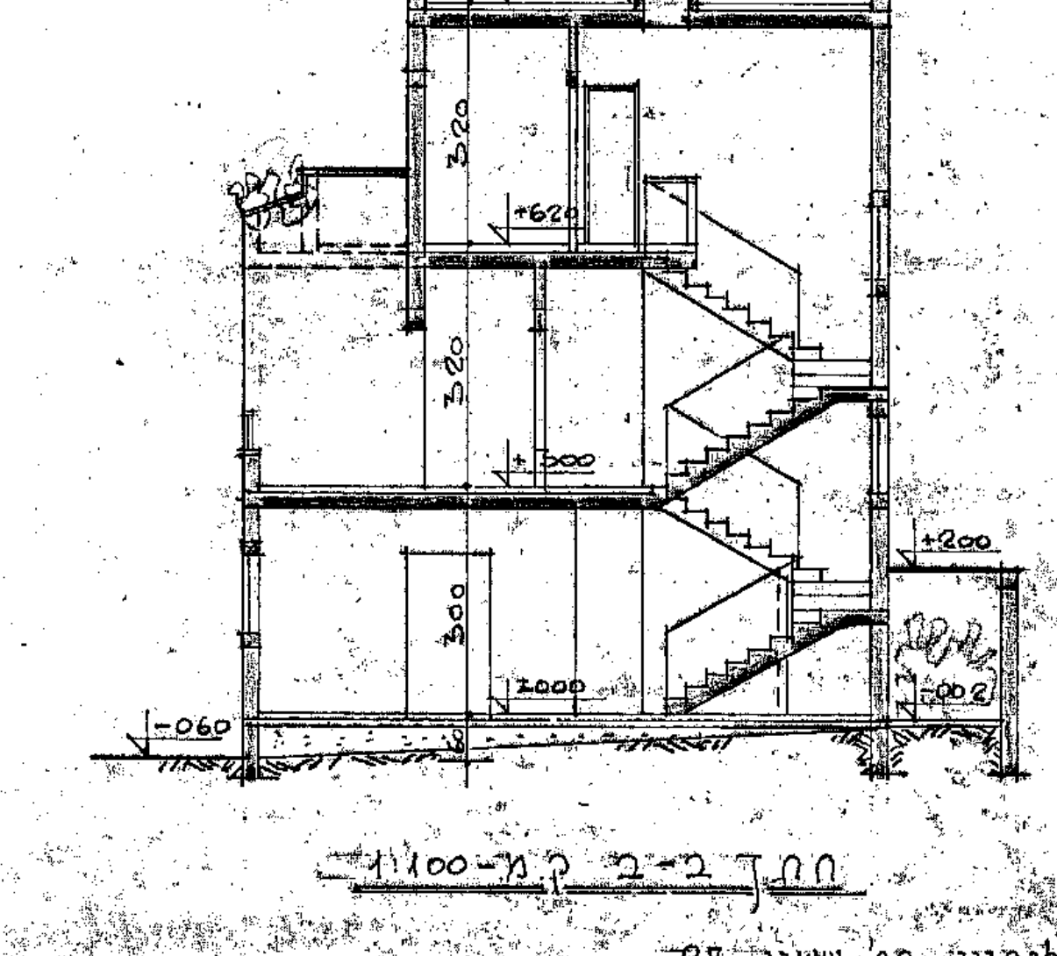
+940
+620
+300
+200
±000
-060
320
300

חתך ב-ב קנ"מ 1:100

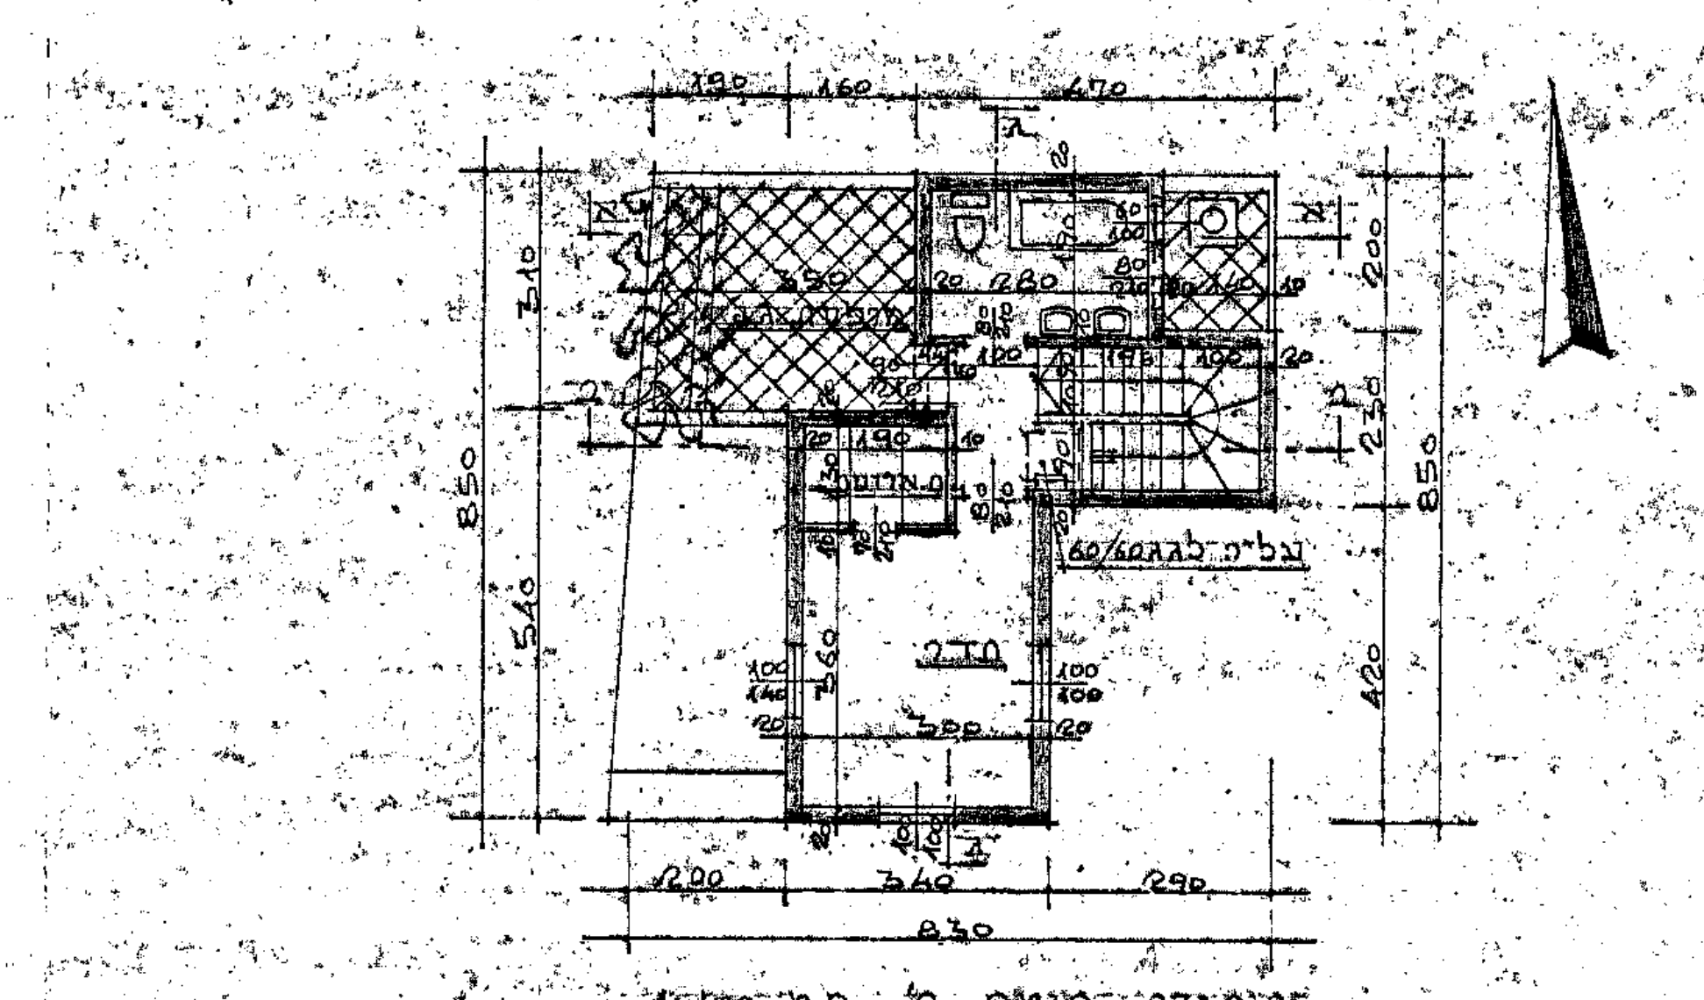
א
ב
ג
חדר
גלריה
830
850
540
340
290

תכנית קומה ב' קנ"מ 1:100

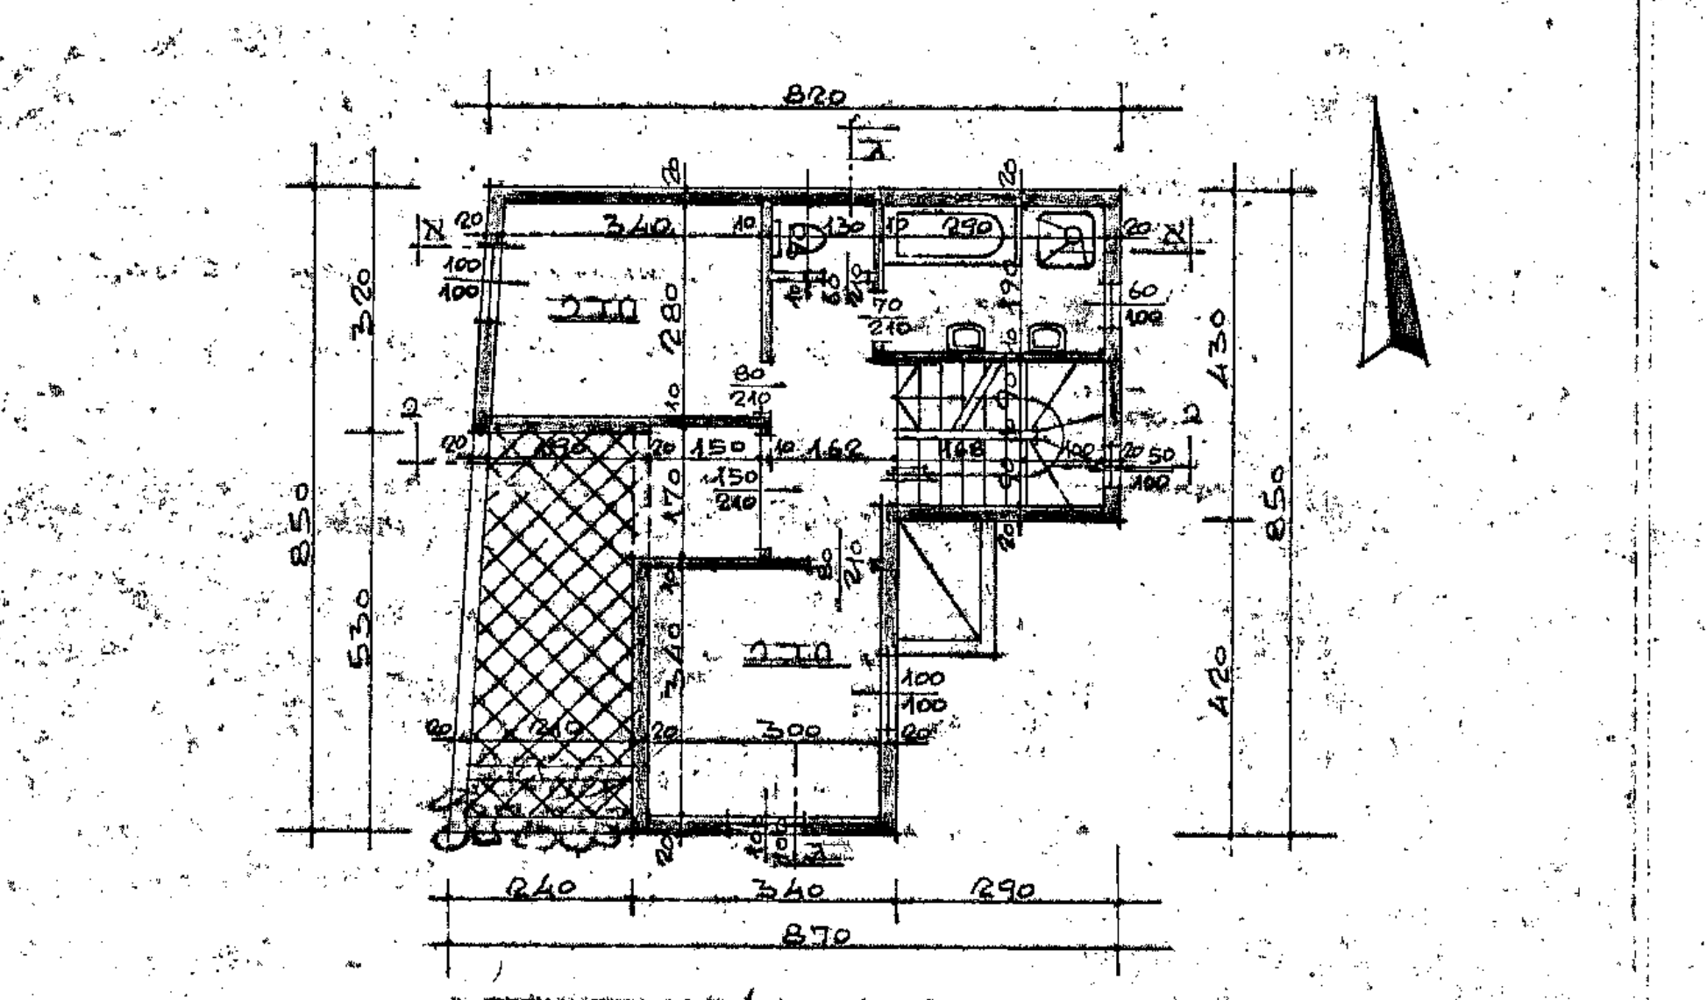
א
ב
ג
חדר
820
850
870
340
290

תכנית קומה א' קנ"מ 1:100

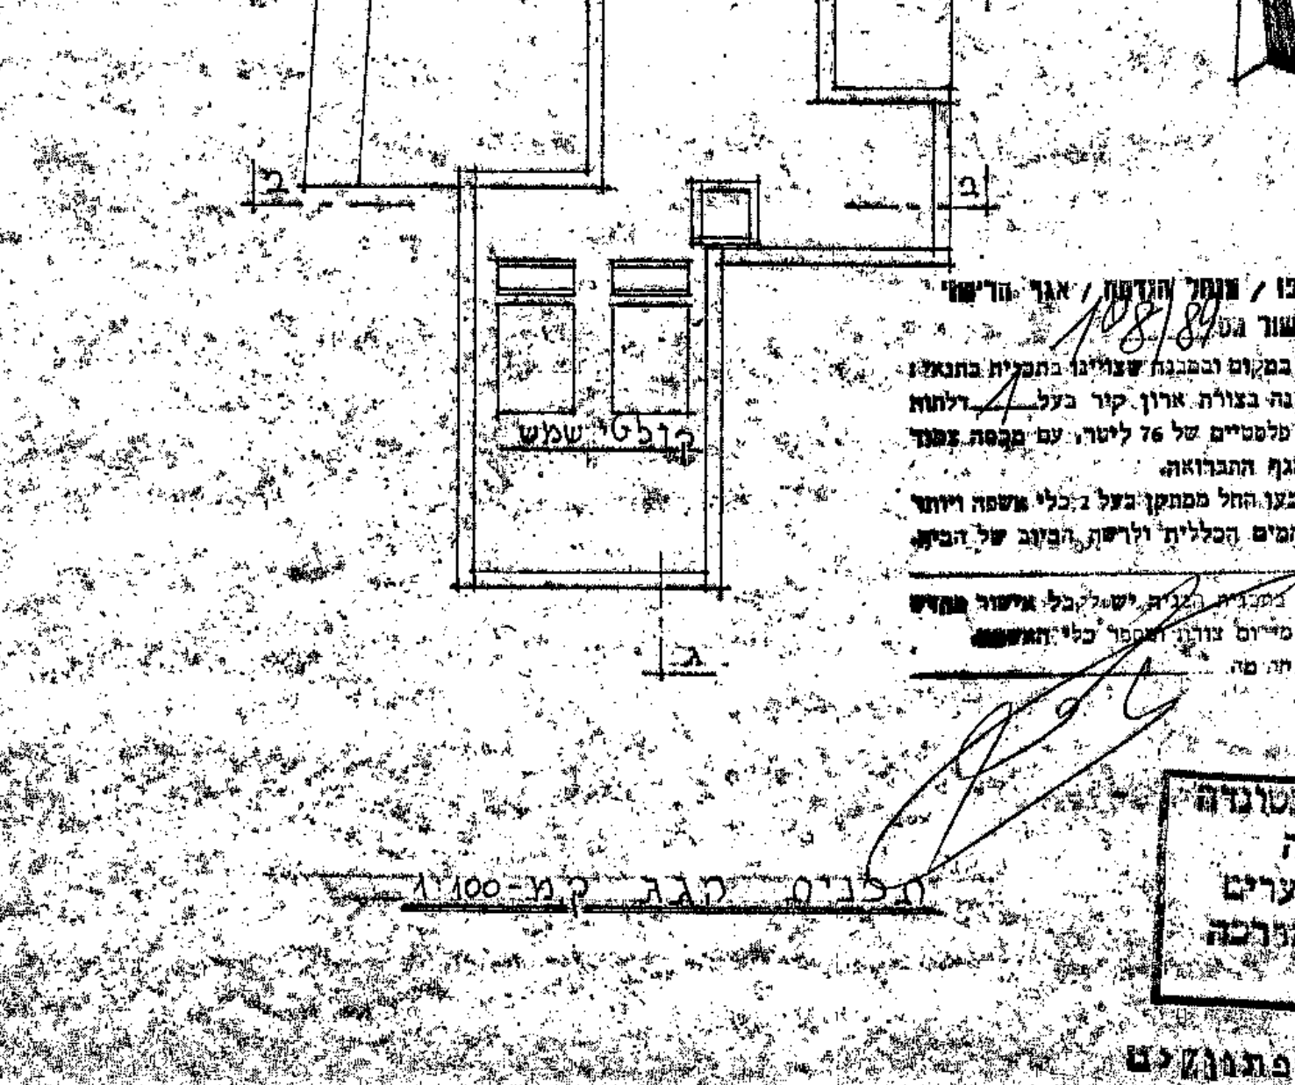

תכנית הגג קנ"מ 1:100

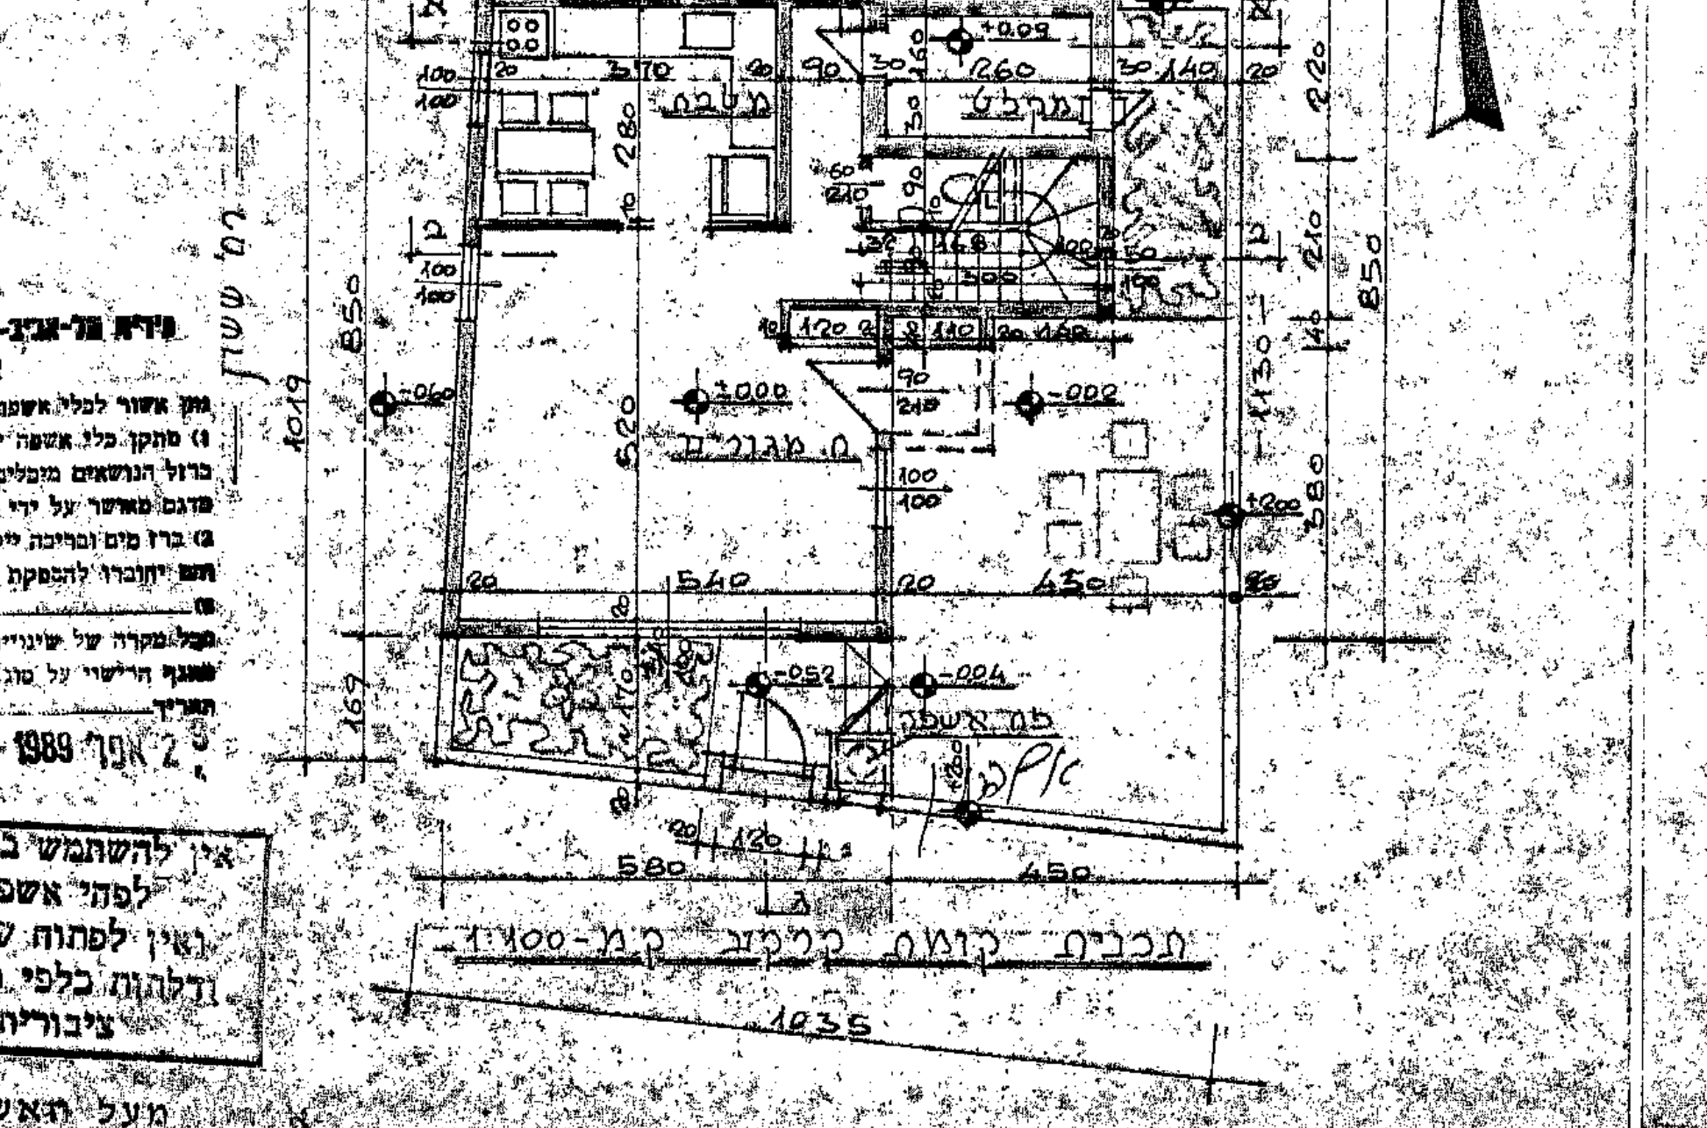
רח' ששון
מטבח
מרפסת
ח. מגורים
חניה
+009
±000
-024
980
820
850
560
450

תכנית קומת קרקע קנ"מ 1:100

עיריית תל-אביב-יפו / מנהל הנדסה / אגף הרישוי

אושר על פי [illegible]

2 אפר' 1989

אין להשתמש בבטונדה לפחי אשפה ואין לפתוח שערים ולהוציא כלפי מדרכה ציבורית

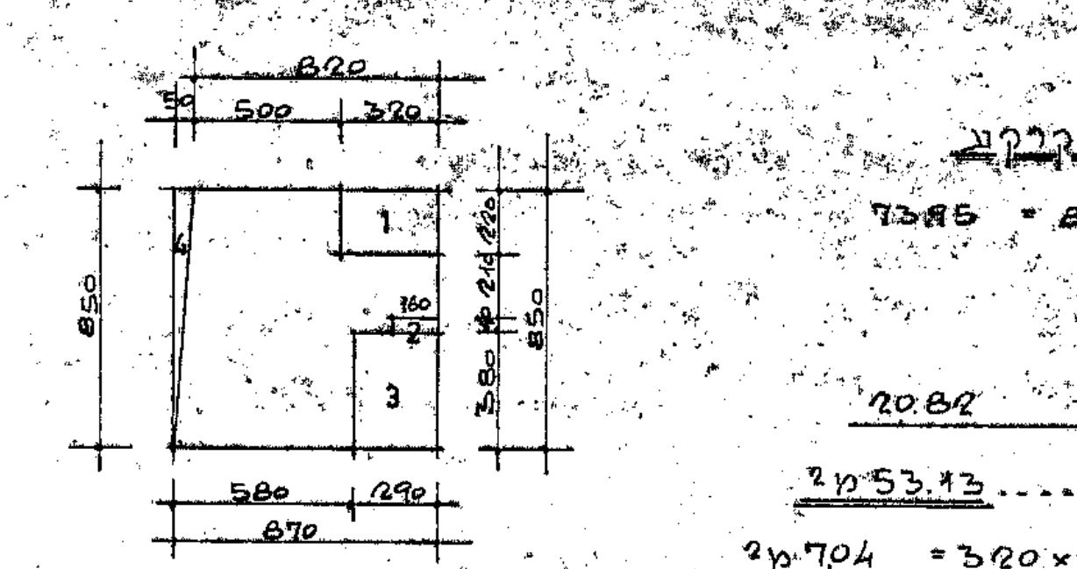
820
500
850
580
290
870
1
2
3
4

חישוב שטח קרקע

53.13 מ"ר = 73.95 – 20.82

מלבן: 73.95 = 8.70 × 8.50

מגרעות:

1. 7.04 = 3.20 × 2.20
2. 0.64 = 1.60 × 0.40
3. 11.02 = 2.90 × 3.80
4. 2.12 = (8.50 × 0.50) / 2

20.82

סה"כ שטח 53.13 מ"ר

שטח המקלט (1) 7.04 מ"ר = 3.20 × 2.20

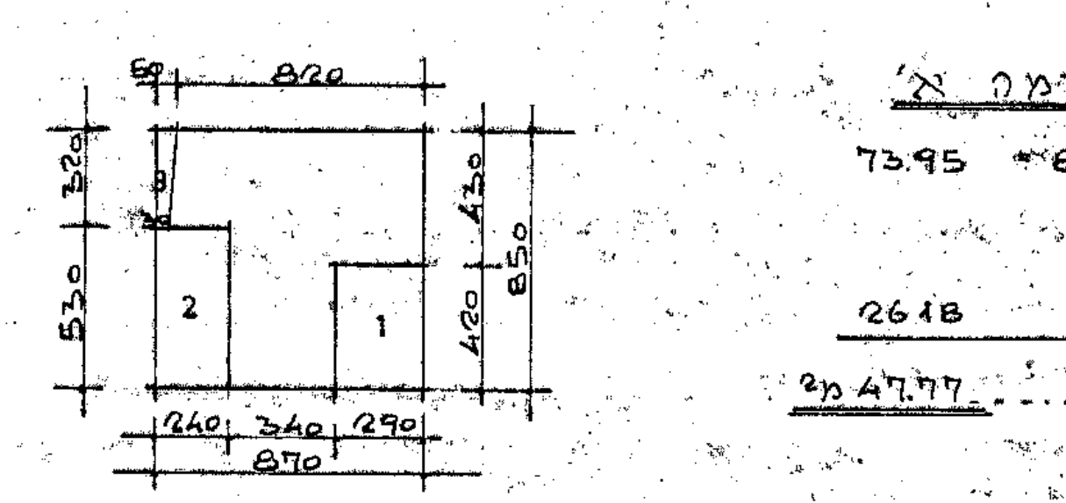
820
850
1
2
3
240
340
290
870

חישוב שטח קומה א'

47.77 מ"ר = 26.18 – 73.95

מלבן: 73.95 = 8.70 × 8.50

מגרעות:

1. 12.18 = 2.90 × 4.20
2. 12.72 = 2.40 × 5.30
3. 1.28 = (0.50 + 0.30 × 3.20) / 2

26.18

סה"כ שטח 47.77 מ"ר

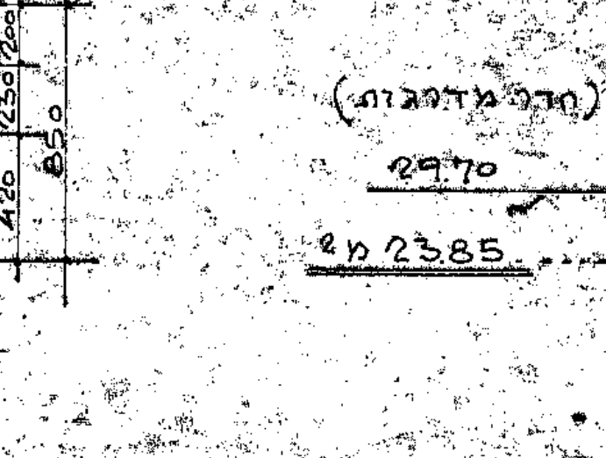
320
160
1
2
3
4
340
290
630

חישוב שטח קומה ב'

53.55 = 8.50 × 6.30

מגרעות:

1. 3.00 = 1.50 × 2.00
2. 9.56 = 4.16 × 2.30 (חדר מדרגות)
3. 12.18 = 2.90 × 4.20
4. 4.96 = (3.10 × 1.60) / 2

29.70

סה"כ שטח 23.85 מ"ר

תרשים הסביבה

ק.מ. 1:1250

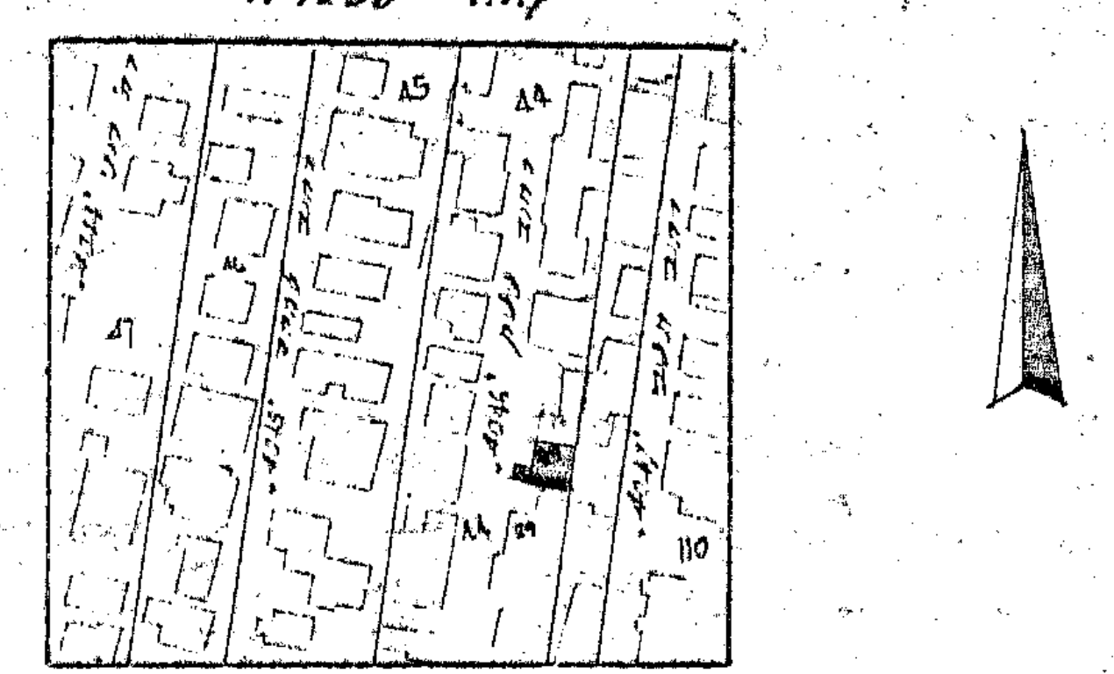

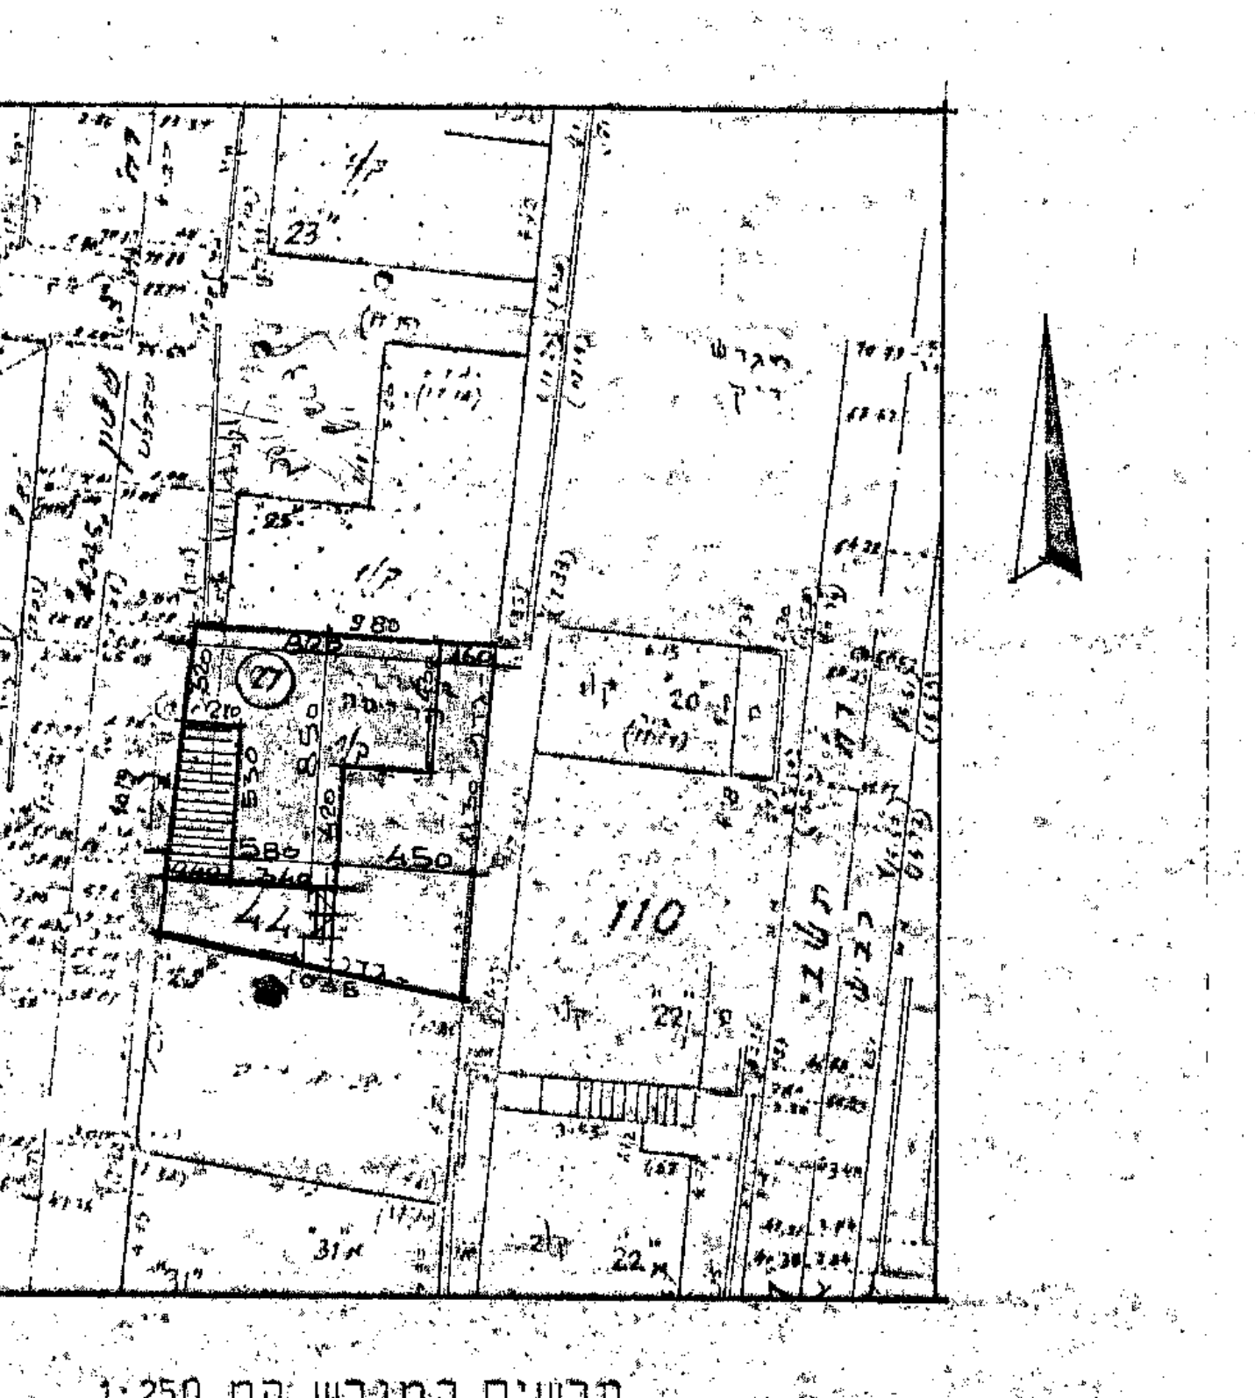
27
44
23
110
ששון

תרשים המגרש קנ"מ 1:250

2

13	12	11	10	9	8	7	6	5	4	3	2	1

הבניה המוצעת למטרות אחרות (תעשיה, עסקים ומשרדים, בנייני ציבור, בנייני משק חקלאי, מטרות שונות).

4. חלוקי בניין אחרים – הבניה המוצעת, שטח במ"ר.

סך הכל	בנוי עזר נוספים	מחסנים	מוסכים	קומת עמודים מפולשת	מקלטים	חדרי כביסה	חדרי הסקה	מעליות	מרפסות שלא נכללו לעיל	חדרי מדרגות
11	10	9	8	7	6	5	4	3	2	1
					7.04				25.77	

ד. חומר הבניה

ה. גדרות

ו. מקרא

הערות:

הנני מאשר כי הנתונים הנ"ל נכונים

תאריך: 28-12-88

חתימת המבקש

חתימת עורך הבקשה *

חתימת האחראי לביצוע השלד

חתימת בעל הזכות בנכס

אישורים של רשויות חוץ:

* היו מספר עורכי בקשה, כאמור בתקנה 2ג, יבוא בחשבון כל אלה.

22

חוק התכנון והבניה, התשכ"ה–1965

תקנות התכנון והבניה (בקשה להיתר, תנאיו ואגרות), התש"ל–1970

טופס 2 (תקנה 2(א))

תיק מס 446023

הוועדה המקומית לתכנון ולבניה תל אביב

מיפרט 89.0371

א. תיאור הבנין

מגרש	תכנית מיתאר מקומית או מפורטת	חלקה	גוש	מס'	הרחוב	1. המקום
		(חלק)44	6135	27	ששון	תל אביב

מס' הטלפון	המען	השם	
993502	ת.ד. 4266 רמת אליהו ראל"צ	סגלוביץ משה	2. המבקש
	—״—	—״—	3. בעל הזכות בנכס
239997	פרחי אדריכלים בע"מ רח' אדם הכהן 16 ת"א.		4. עורך הבקשה *
7521921	רח' רוקח 35 רמת גן	י. לבני מהנדס	5. האחראי לביצוע השלד

6. אזור הבניה: ■ מגורים ☐ מסחר ☐ תעשיה ☐ בנין ציבורי ☐ חקלאי ☐ ……

7. שטח המגרש/החלקה: 105 מ"ר. אחוז הבניה המותר: %……

8. מטרת הבנין: ■ מגורים ☐ הארחה ☐ עסקים ☐ תעשיה ☐ חקלאי ☐ ציבורי ☐ ……

9. מהות הבנין ותכליתו: בית מגורים חדש במקום בית קיים במסגרת פרויקט בנה ביתך

10. תיאור העבודה המוצעת: ■ בנין חדש ☐ תוספת לבנין קיים ☐ הריסה ☐ תיקונים ☐ שינוי בבנין ☐ ……
☐ שינוי בשימוש ממטרה: …… למטרה: ……

11. האם הבניה היא בעדי: ☐ משרד ממשלתי ☐ הרשות המקומית ☐ הסוכנות היהודית

ב. היקף הבניה

קומה	קיים	מוצע	סך הכל	אחוז הבניה	עד 45 מ"ר	עד 65 מ"ר	עד 90 מ"ר	עד 100 מ"ר	מעל 100 מ"ר	עסק: הארחה וכו'	ציבורי	שונות			
1	2	3	4	5	6	7	8	9	10	11	12	13	14	15	
קרקע		53.13	50.6%												
א		47.77	45.49%												
ב		23.85	22.71%												
סך הכל		124.75	118.8%												

ג. השימוש בבנין

1. הבניה המוצעת למגורים

דירות בנות:	שטח כל דירה במ"ר	מספר דירות מכל סוג							מספר חדרים				
1	2	3	4	5	6	7	8	9	10	11	12		
4 חדרים							4	1	2	2	1		

איכות נמוכה

גסרק