22

איכות נמוכה

חוק התכנון והבניה, התשכ"ה-1965

תקנות התכנון והבניה (בקשה להיתר, תנאיו ואגרות), התש"ל 1970

טופס 2 (תקנה 2(א))

תיק מס 4046027

014

מיפרט

הוועדה המקומית לתכנון ולבניה

רישום תל אביב

עיריית תל-אביב-יפו · · ·
12-05 1989
מחלקת רישוי בניה

א. תיאור הבנין

1. הישוב	הרחוב	מס'	גוש	חלקה	תכנית בינוי או מפורטת	מגרש
תל אביב	ששון	27	6135	44 (חלק)		

	השם	המען	מס' הטלפון
2. המבקש	סגלוביץ משה	ת.ד 4266 רמת אליהו ראל"צ	993502
3. בעל הזכות בנכס	— " —	— " —	
4. עורך הבקשה *	פרחי אדריכלים בע"מ	רח' אדם הכהן 16 ת"א	239997
5. האחראי לביצוע השלד	י. לבני מהנדס	רח' רוקח 35 רמת גן	7521921

6. אזור הבניה: ■ מגורים ☐ מסחר ☐ תעשיה ☐ בנין ציבורי ☐ חקלאי ☐

7. שטח: המגרש / החלקה: 105 מ"ר. אחוז הבניה המותר: ...... %

8. מטרת הבנין: ■ מגורים ☐ הארחה ☐ עסקים ☐ תעשיה ☐ חקלאי ☐ ציבורי ☐ ....

9. מהות הבנין ותכליתו: בית מגורים חדש במקום בית קיים במסגרת פרויקט בנה ביתך

10. תיאור העבודה המוצעת: ■ בנין חדש ☐ תוספת לבנין קיים ☐ הריסה ☐ תיקונים ☐ שינוי בבנין ☐ .... ☐ שינוי בשימוש מ..... למטרה: ....

11. האם הבניה היא בעד: ☐ משרד ממשלתי ☐ הרשות המקומית ☐ הסוכנות היהודית

ב. היקף הבניה

קומה	קיים	מוצע	סך הכל	אחוז הבניה	מגורים בדירות עד 45 מ"ר	עד 65 מ"ר	עד 90 מ"ר	עד 100 מ"ר	מעל 100 מ"ר	עסקי (הארחה וכו')	ציבורי	שונות	מס' חדרים קיים	מס' חדרים מוצע
1	2	3	4	5	6	7	8	9	10	11	12	13	14	15
קרקע		53.13		50.6%										
א		47.77		45.49%										
ב		23.85		22.71%										
ג														
ד														
ה														
ו														
ז														
הבניה הקובעת לבנין חדרי מדרגות														
בניני עזר														
סך הכל		124.75		118.8%										

16.4.88

הנפח המוצע: של הבנין העיקרי.......... מ"ק. של בנין עזר.......... מ"ק.

ג. השימוש בבנין

1. הבניה המוצעת למגורים

דירות בנות:	שטח כל דירה מ"ר	מספר דירות מכל סוג	כל הדירות	מזה: רצפות חדרי דיור בלבד, ומרפסות מקורות	מזה: רצפות חדרי שירות ופרוזדורים בלבד	מזה: רצפות של מרפסות בלתי מקורות	מספר חדרים: דיור	מטבחים	אמבטיות	בתי שימוש	אחרים
1	2	3	4	5	6	7	8	9	10	11	12
חדר אחד	ראה הערות סכימה של שטחי הבניה בכל קומה, מספר החדרים ושטח כל דירה.										
2 חדרים											
3 חדרים											
4 חדרים							4	1	2	2	1
5 חדרים											
6 חדרים											
7 חדרים ויותר											
חדרים נוספים לדירות קיימות											
בניני עזר											
סך הכל		1									

2. הבניה הקיימת והמוצעת לתעשיה ולמלאכה

פרטים	קיים: שטח	קיים: גובה	קיים: נפח	קיים: % הבניה	מוצע: שטח	מוצע: גובה	מוצע: נפח	מוצע: % הבניה	סך הכל: שטח	סך הכל: נפח	סך הכל: % הבניה	הערות
1	2	3	4	5	6	7	8	9	10	11	12	13
אולמי מלאכה												
משרדים												
חדרי שירות												
סככות												
בניני עזר												
חדרי מדרגות												
סך הכל												

3. הבניה המוצעת למטרות אחרות (הארחה, עסקים ומשרדים, בניני ציבור, בניני משק חקלאי, מטרות שונות).

השימוש המיועד	סך הכל מ"ר	שטחים – מ"ר, מזה: חדרים	אולמות	אחסנה	חדרי שירות	מספר חדרים, אולמות וכו': חדרים	אולמות	אחסנה	חדרי שירות
1	2	3	4	5	6	7	8	9	10
בניני עזר (למעט אלה המפורטים ב־ג(4))									

4. חלקי בנין אחרים – הבניה המוצעת, שטח במ"ר.

חדרי מדרגות	מרפסות שלא נכללו לעיל	מעליות	חדרי הסקה	חדרי כביסה	מקלטים	קומה עמודים מפולשת	מחסנים	מוסכים	בניני עזר נוספים	סך הכל
1	2	3	4	5	6	7	8	9	10	11
	25.77				7.04					

ד. חומר הבניה

קירות חיצוניים	☐ בטון מזוין	☐ לבני בטון או בלוקים	☐ לבני סיליקט	☐ לבנים שרופות	☐ אבן טבעית
	☐ אבן מלאכותית	☐ איטונג	☐ עץ	☐ ברזל	☐ חמרים אחרים
תקרות	☐ בטון מזוין	☐ עץ	☐ חומר אחר..........		
גג	☐ בטון מזוין	☐ רעפים	☐ אסבסט	☐ פח	☐ חומר אחר..........

ה. גדרות

קיימות.......... מ"א מוצעות.......... מ"א

ו. מקרא

▨ בטון או בטון מזוין	☐ אבן	☐ עץ	☐ איטונג
▨ בלוקים או לבנים מבטון	☐ סיליקט או לבנים אדומות	☐ חומר אחר	☐ להריסה

הערות:..........

הנני מאשר כי הנתונים הנ"ל נכונים

תאריך 28-12-88 חתימת המבקש .... חתימת עורך הבקשה * י. פרחי

חתימת האחראי לביצוע השלד .... חתימת בעל הזכות בנכס ....

לשימוש הוועדה המקומית בלבד	מס' ההיתר	תאריך ההיתר	תאריך התחלת הבניה	תאריך גמר הבניה

אישורים של רשויות חוץ:

חותמת הוועדה המקומית

* היו מספר עורכי בקשה, כאמור בתקנה 2ה'. יבוא במקום כל אלה הראשון שברשימת עורכי הבקשה, כאמור בטופס 1.

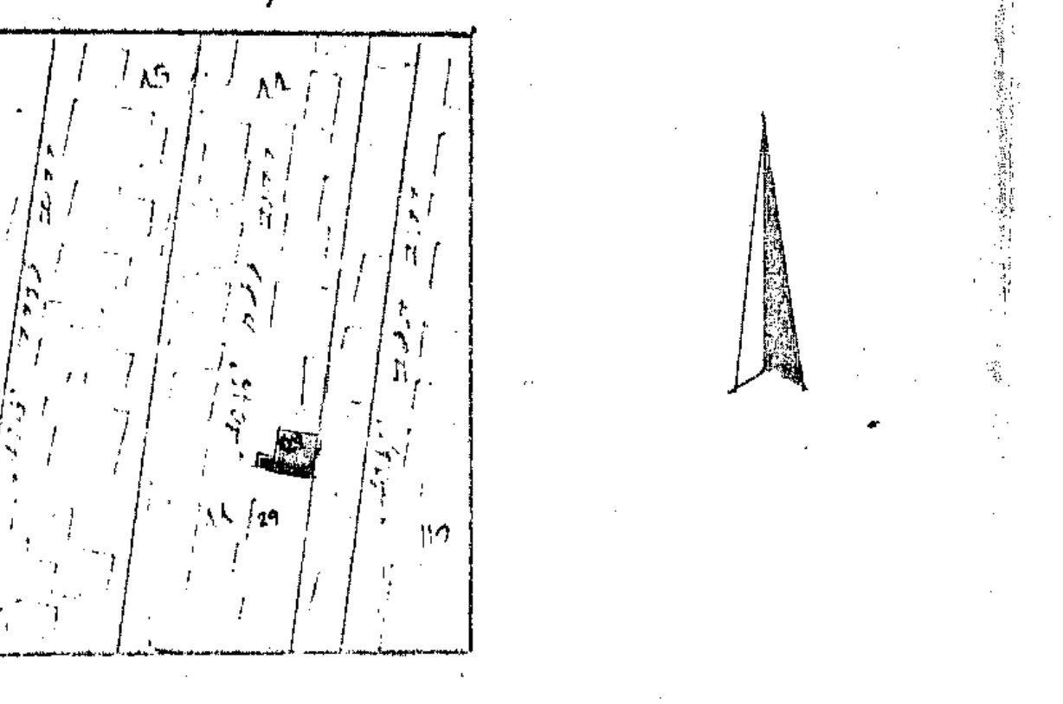

תרשים הסביבה
ק.מ. 1:1250

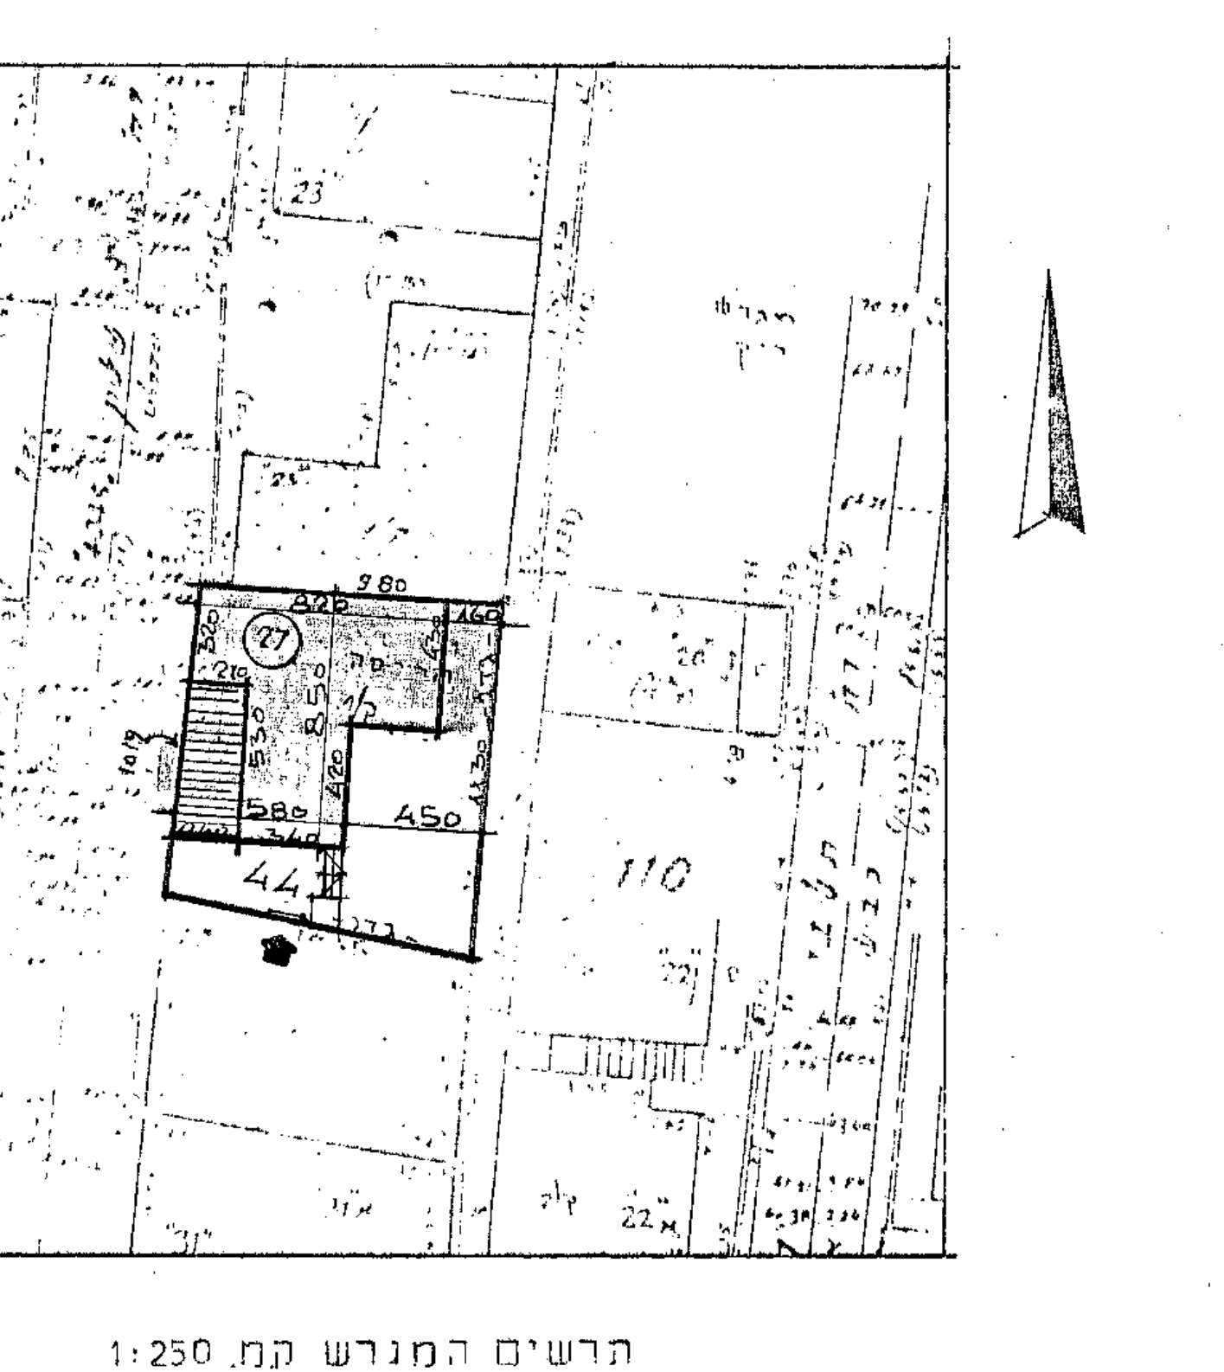
27
980
826
580
450
44
110
23

הרשים המגרש קמ. 1:250

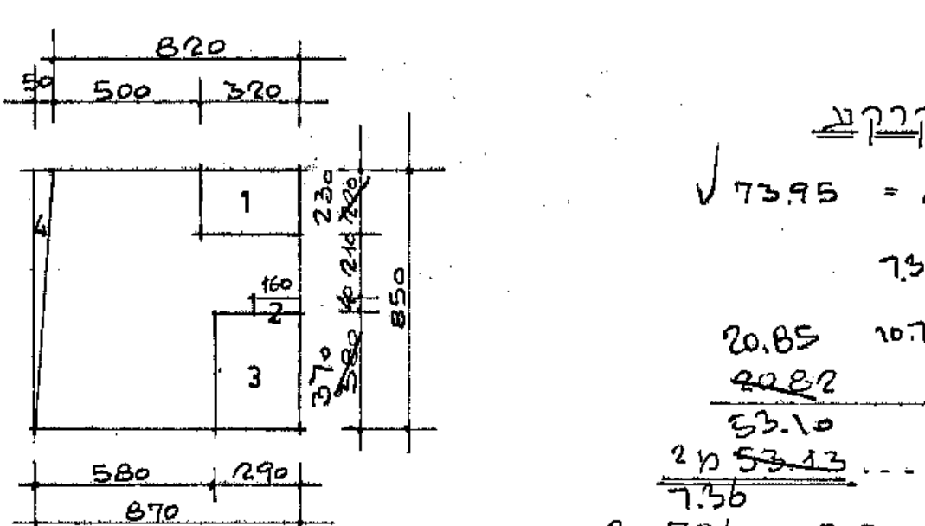
820
500
320
580
290
870
850
1
2
3
4

חישוב שטח ק. קרקע

מסגרת: 870 × 850 = 73.95 ✓
הורדות:
1. 320 × ~~220~~ 230 = ~~7.04~~ 7.36
2. 160 × 0.40 = 0.64
3. 290 × ~~3.80~~ 3.70 = ~~11.02~~ 10.73
4. (850 × 0.50) / 2 = 2.12

~~20.82~~ 20.85

53.10

סה"כ שטח .... ~~53.13~~ מ"ר

שטח המקלט ① 320 × ~~220~~ 230 = ~~7.04~~ 7.36 מ"ר

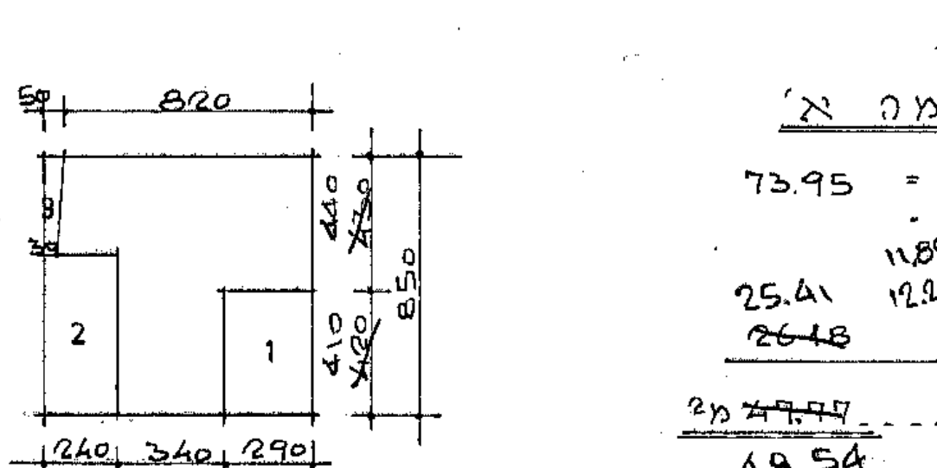
820
340
510
850
1
2
3
240
340
290
870

חישוב שטח קומה א'

מסגרת: 870 × 850 = 73.95
הורדות:
1. 290 × ~~4.30~~ 4.10 = ~~12.48~~ 11.89
2. 240 × ~~5.30~~ 5.10 = ~~12.72~~ 12.24
3. (50+30 × 320) / 2 = 1.28

~~26.48~~ 25.41

סה"כ שטח .... ~~47.77~~ מ"ר 48.54

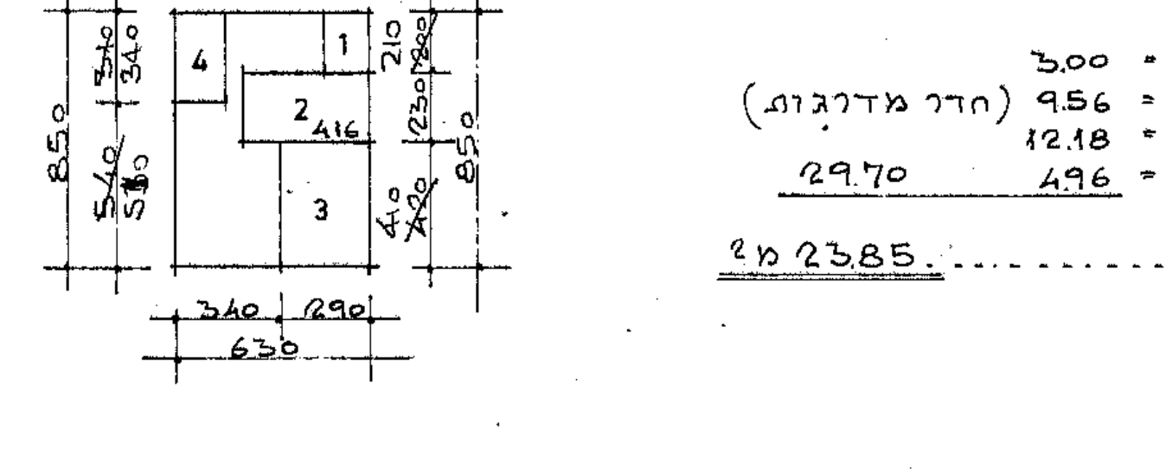
160
320
150
4
1
2
3
416
340
290
630
850

חישוב שטח קומה ב'

מסגרת: 850 × 630 = 53.55
הורדות:
1. 150 × 200 = 3.00
2. 416 × 230 = 9.56 (חדר מדרגות)
3. 290 × 420 = 12.18
4. 310 × 160 = 4.96

29.70

סה"כ שטח .... 23.85 מ"ר

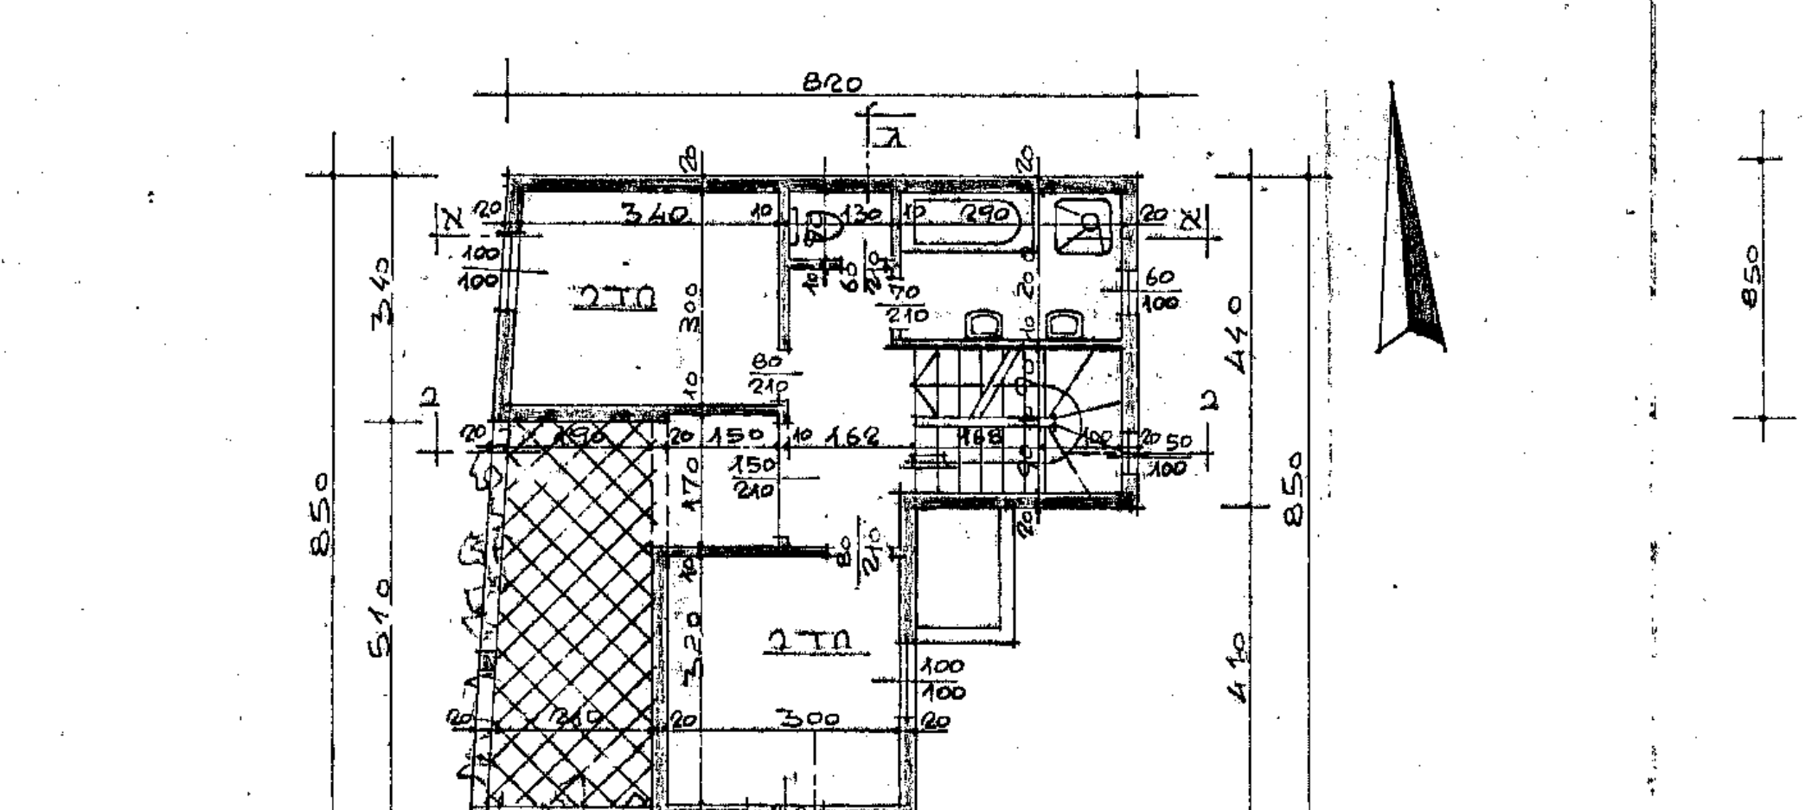
820
חדר
חדר
340
300
240
870
850

תכנית קומה א' קמ-1:100

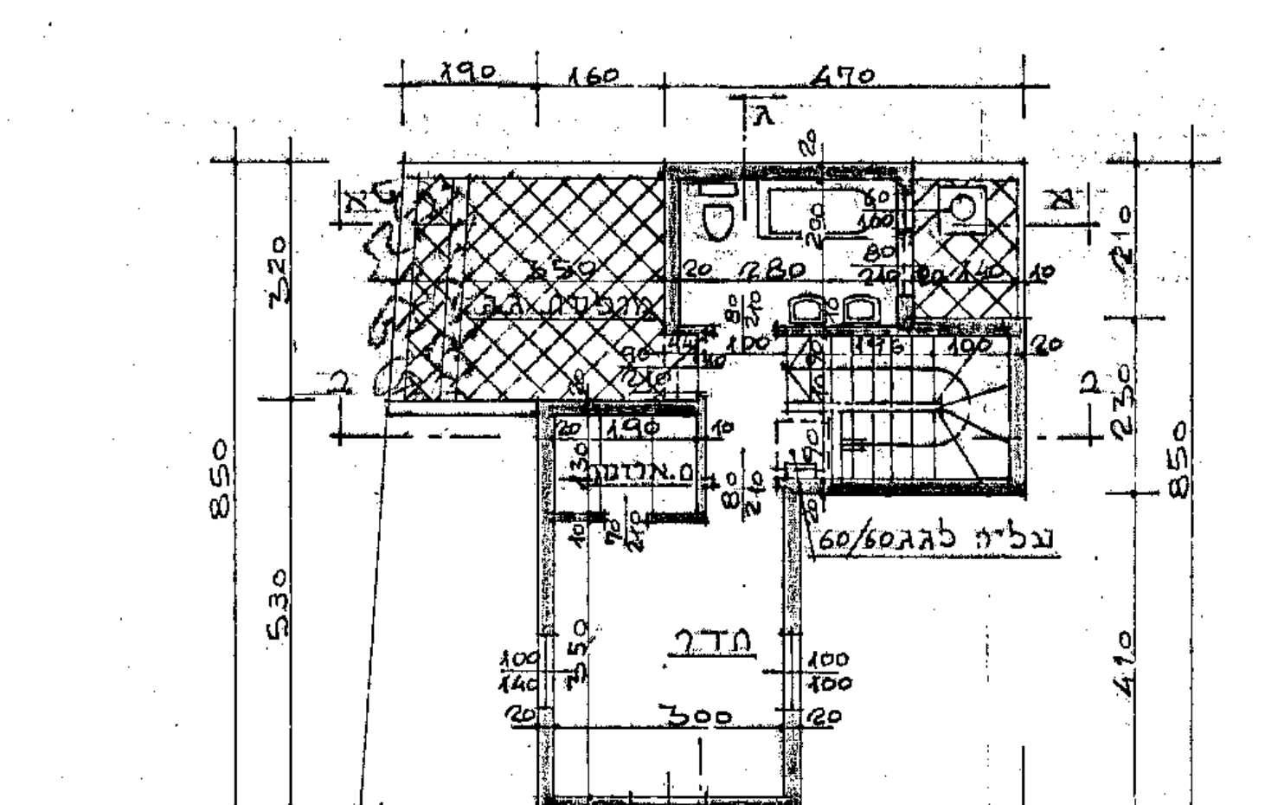
470
160
190
מרפסת
חדר
עליה לגג 60/60
200
340
290
830
850

תכנית קומה ב' קמ-1:100

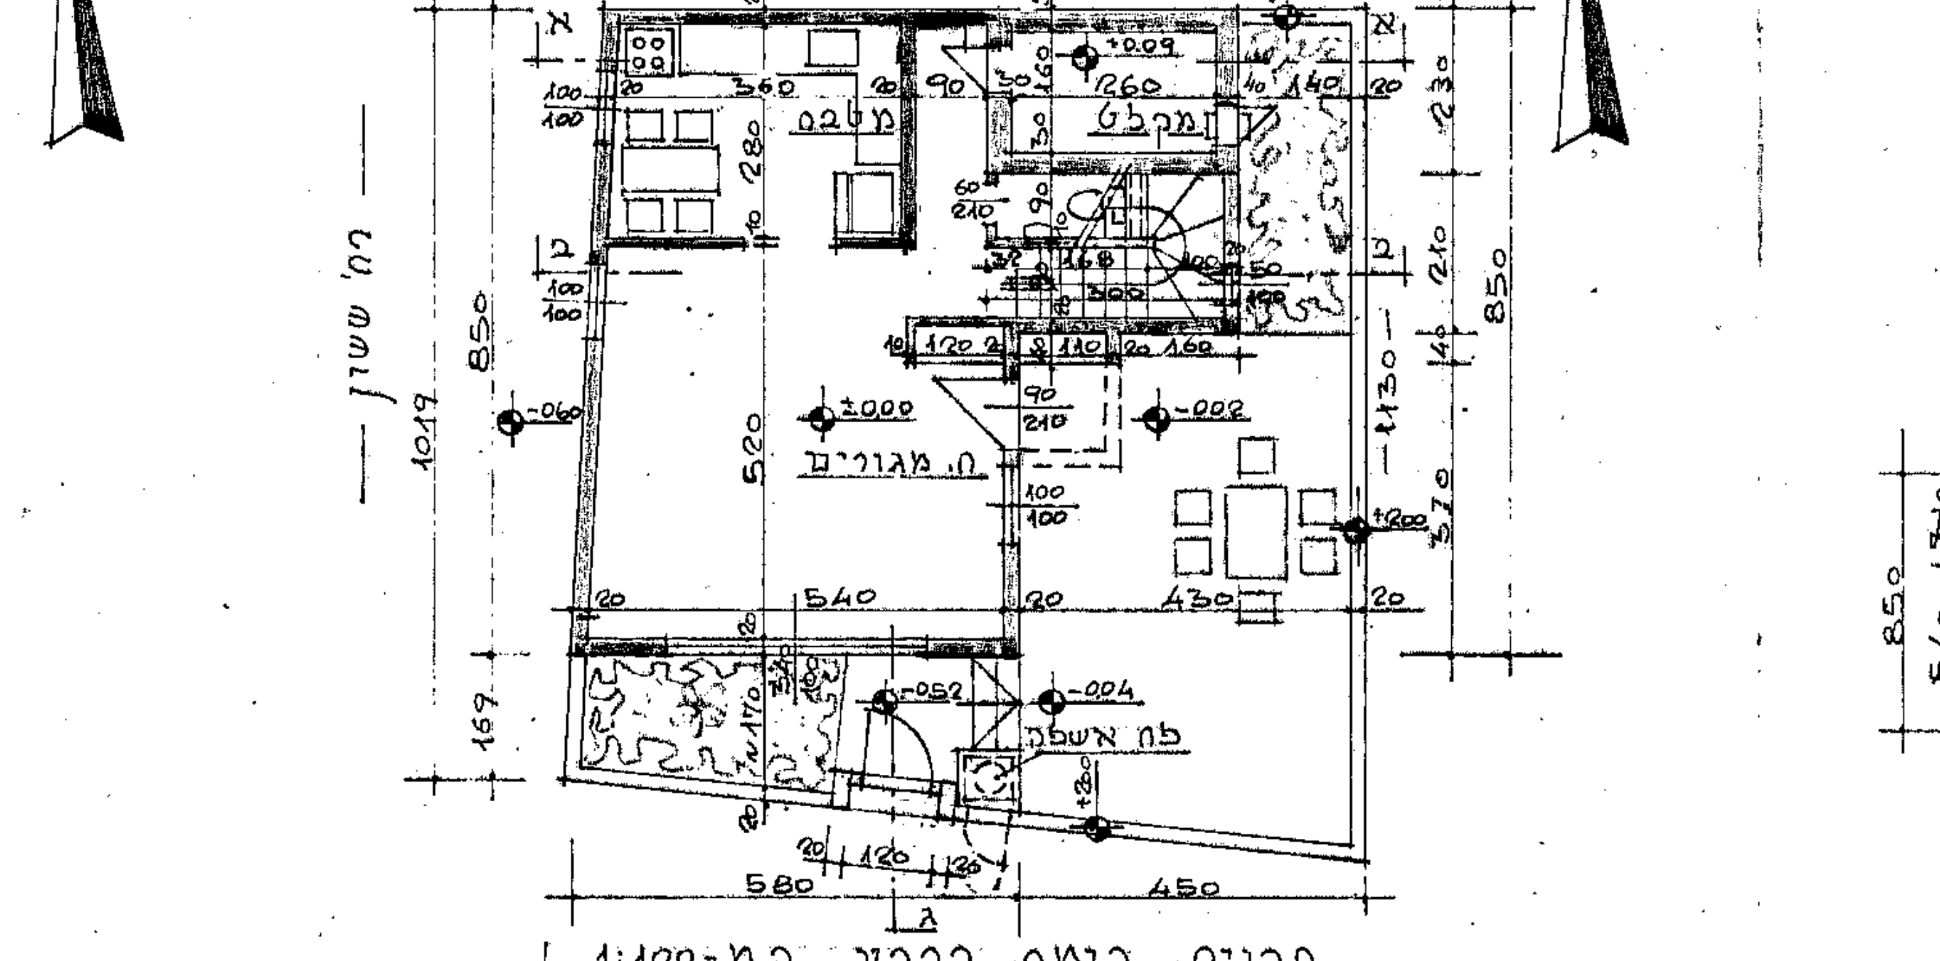
980
820
160
מטבח
מקלט
ח. מגורים
540
430
580
450
1019
1035
רח' ששון
לח אשפה

תכנית קומת קרקע קמ-1:100

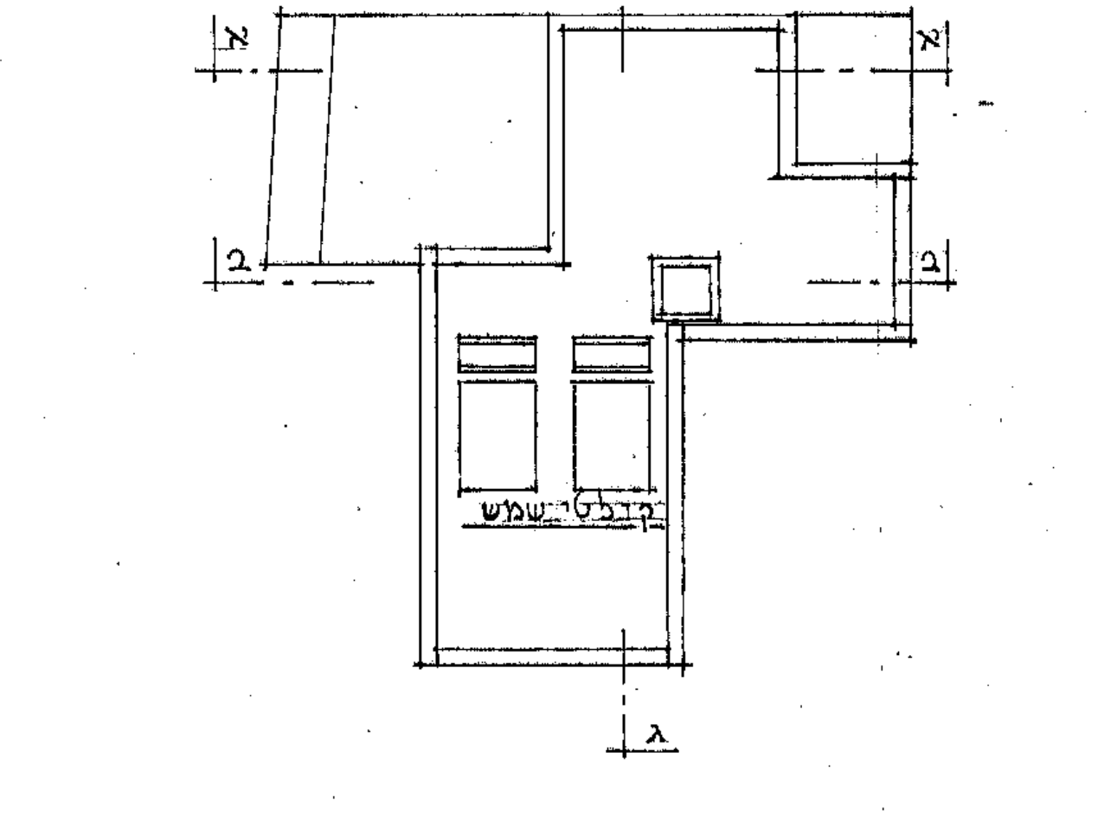

תכנית הגג קמ-1:100

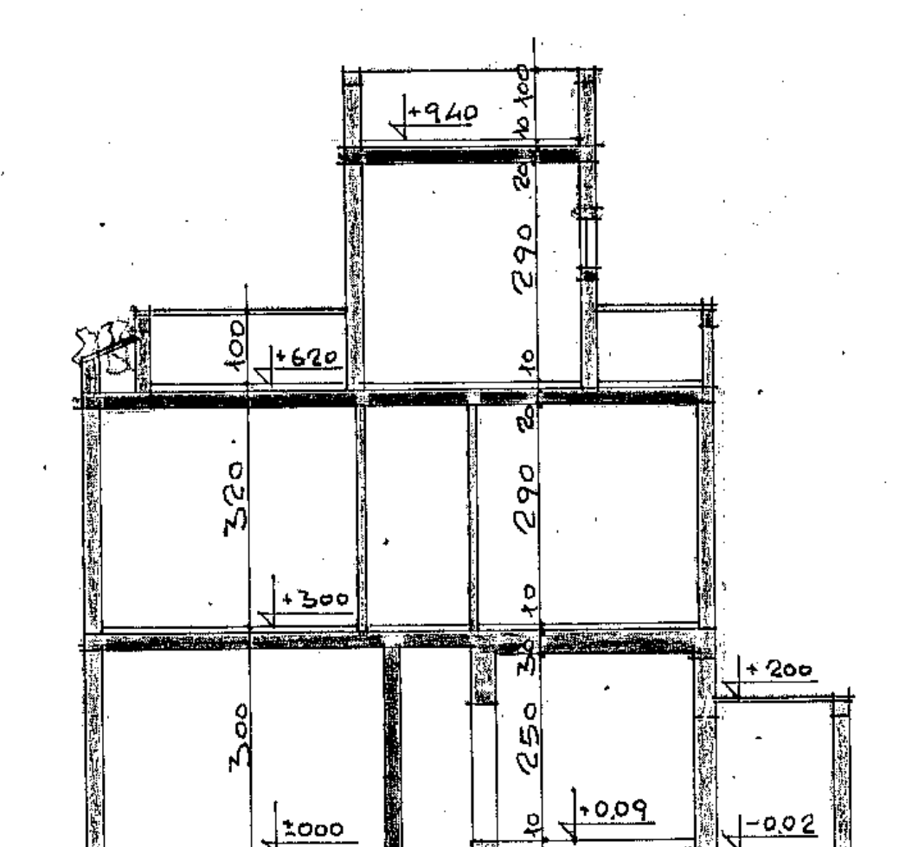
+9.40
+6.20
+3.00
±0.00
-0.60

חתך א-א קמ-1:100

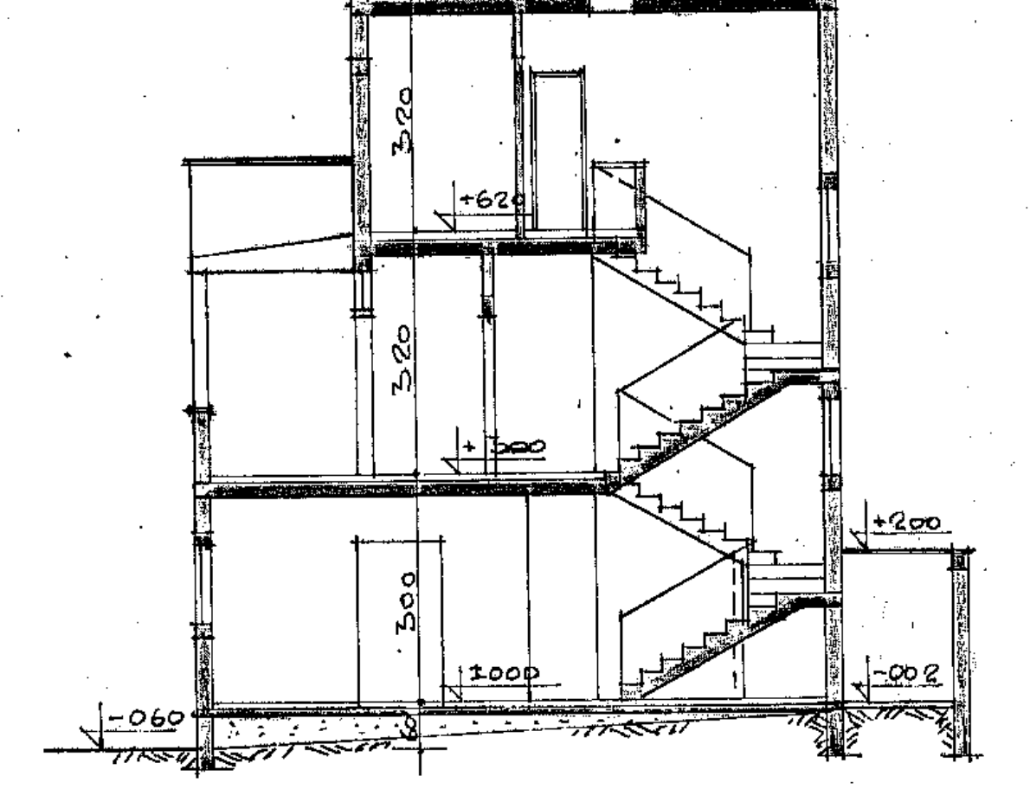
+9.40
+6.20
+3.00
±0.00
-0.60

חתך ב-ב קמ-1:100

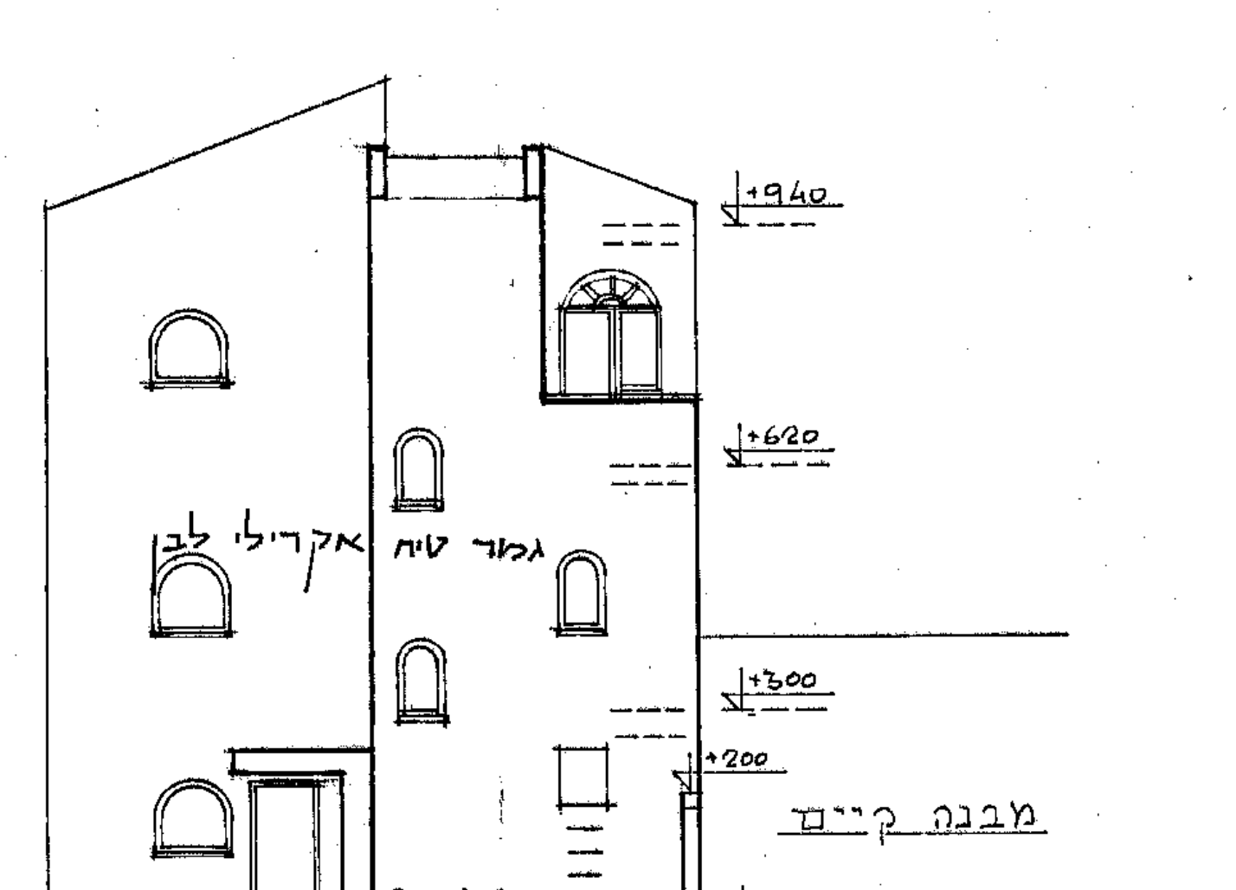
גמר טיח אקרילי לבן
+9.40
+6.20
+3.00
+2.00
±0.00
מבנה קיים

חזית מזרחית קמ-1:100

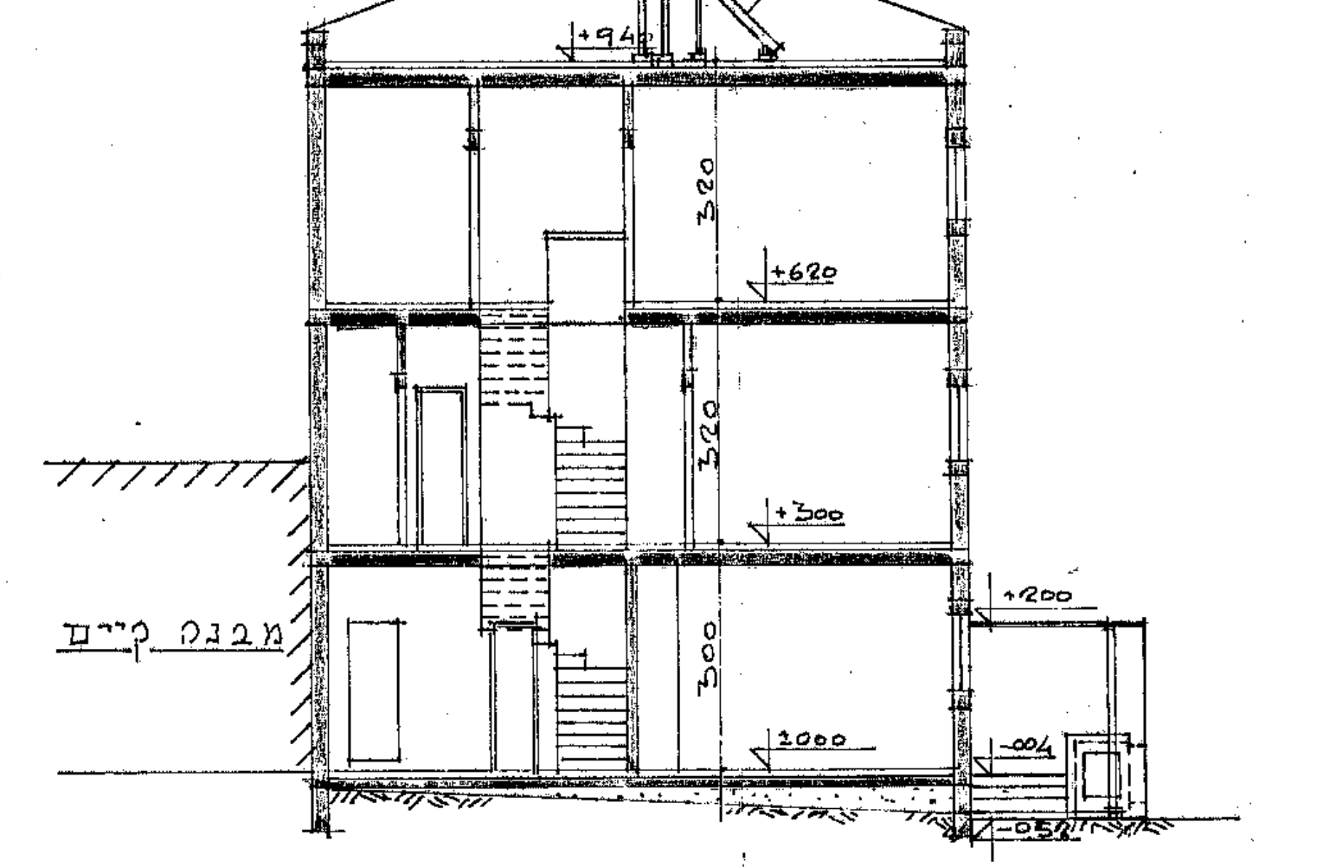
קולטי-שמש
+9.40
+6.20
+3.00
±0.00
מבנה קיים

חתך ג-ג קמ-1:100

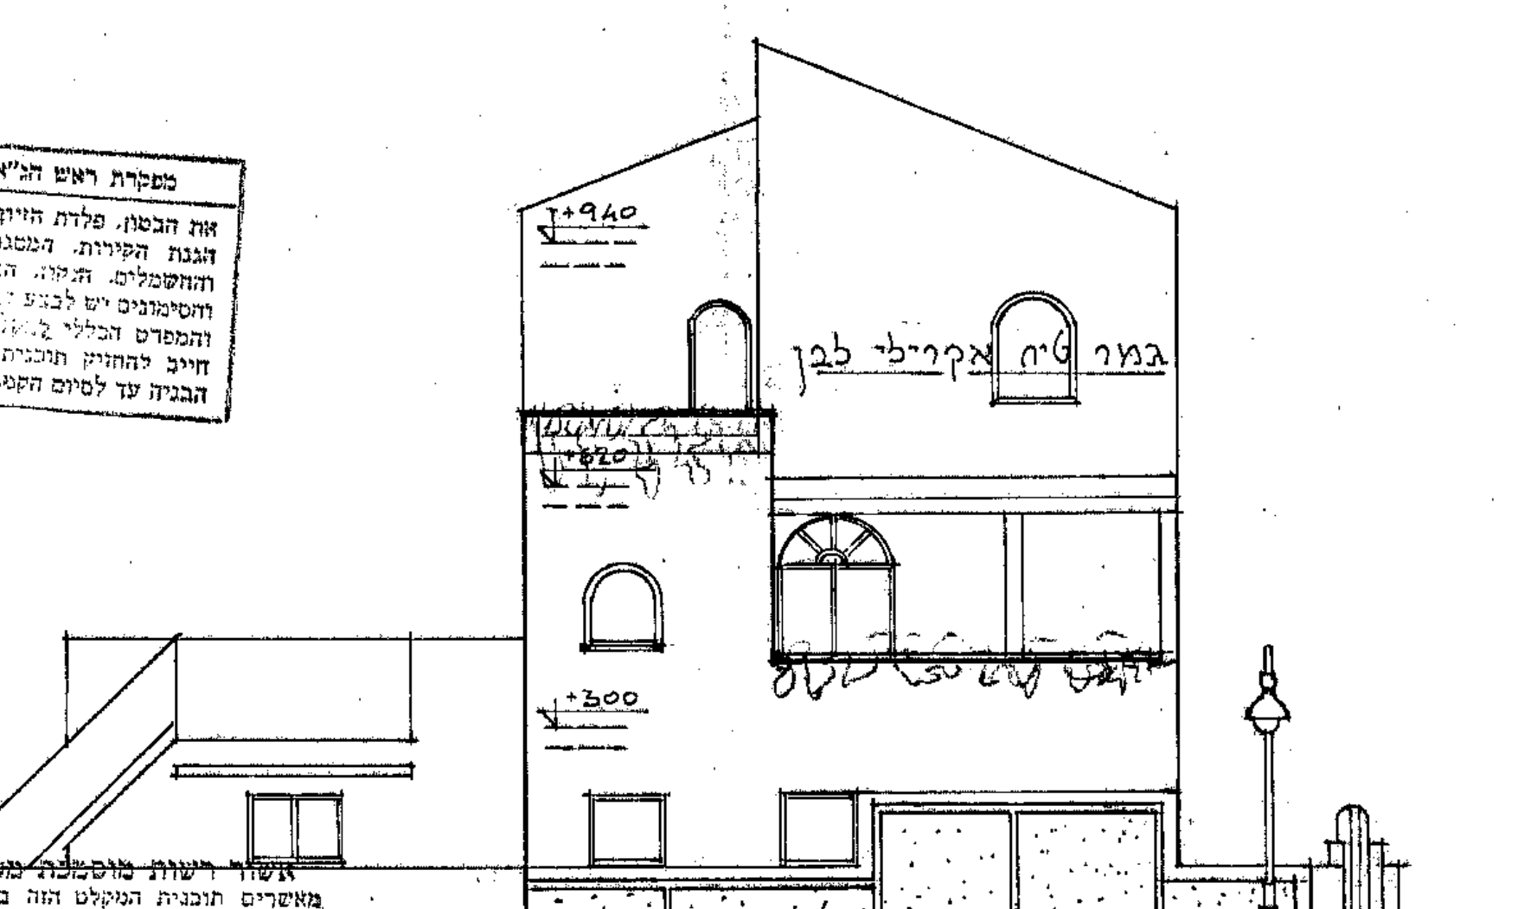
גמר טיח אקרילי לבן
+9.40
+6.20
+3.00
±0.00
-0.60
גמר טיח בלגי
כדורגל

חזית מערבית קמ-1:100

אדנית ועמוד תאורה לפי תכנית פיתוח מאושרת רח' ששון - בביצוע

סורגים פנימיים בגוון לבן בלבד

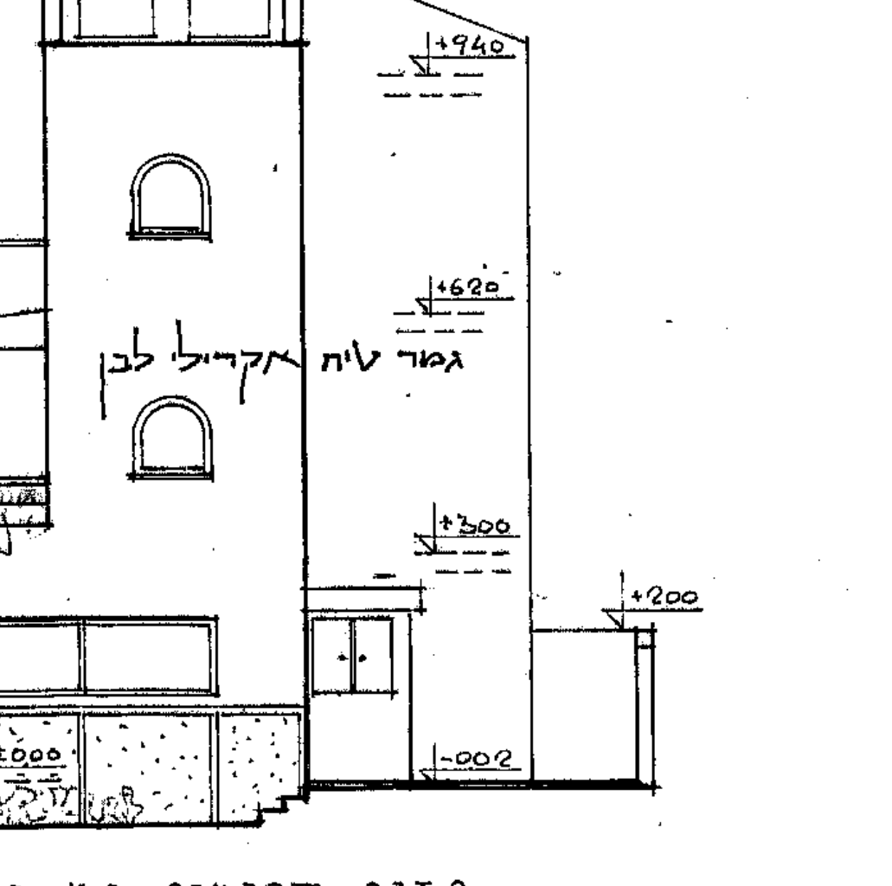
גמר טיח אקרילי לבן
+9.40
+6.20
+3.00
+2.00
±0.00
-0.60
גבול רח' ששון

חזית דרומית קמ-1:100

מפקדת ראש הג"א – ענף הנדסה ומיגון

את הבטון, פלדת הזיון, התקרות, הקירות, ... ויריעות איטום ... המקלט ... חייב להחזיק תכנית מאושרת של המקלט באתר הבניה עד לסיום הקמתו.

אישור רשות מוסמכת מטעם ראש הג"א

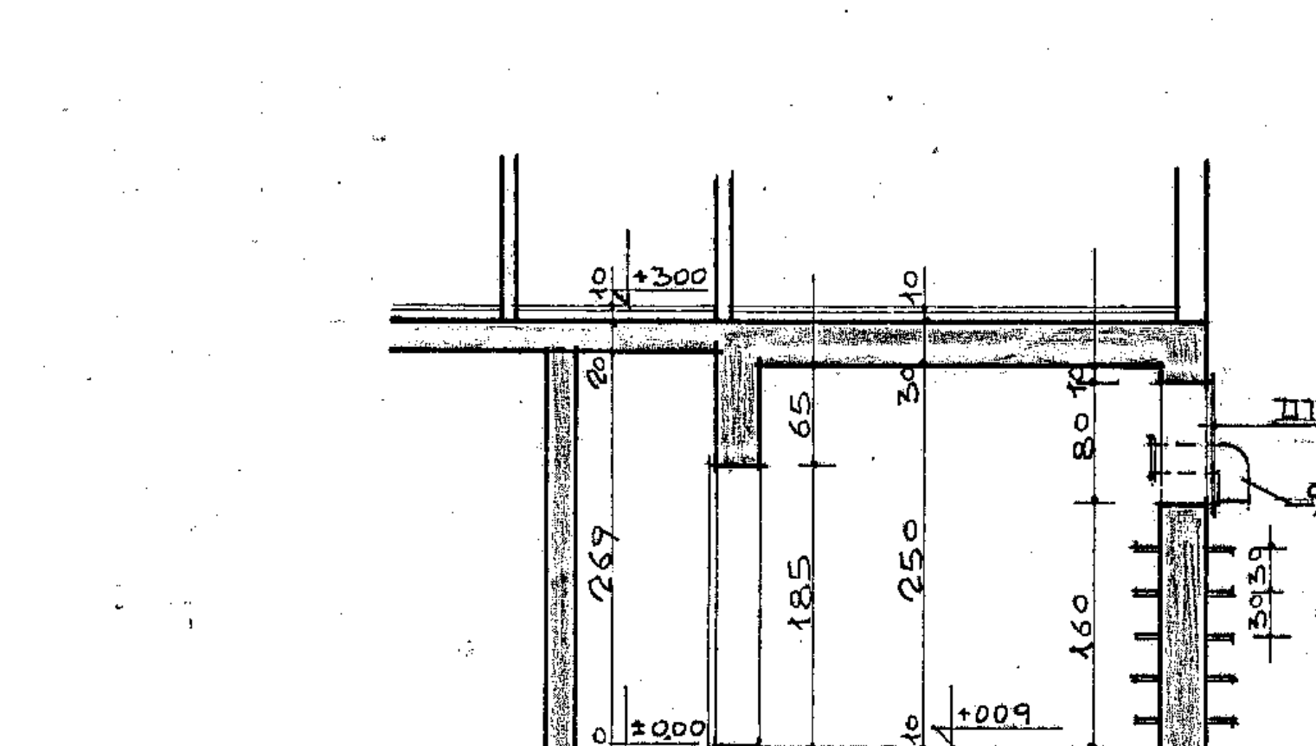
+3.00
±0.00
267
185
250
160
65
80
חלון יציאה חירום פח גובה 8 מ"מ H=190
סולם שלבי ברזל Ø16 מ"מ

חתך 1-1 1:50

12.3.89

רשות מוסמכת בפיקוד העורף ... עיריית תל-אביב-יפו

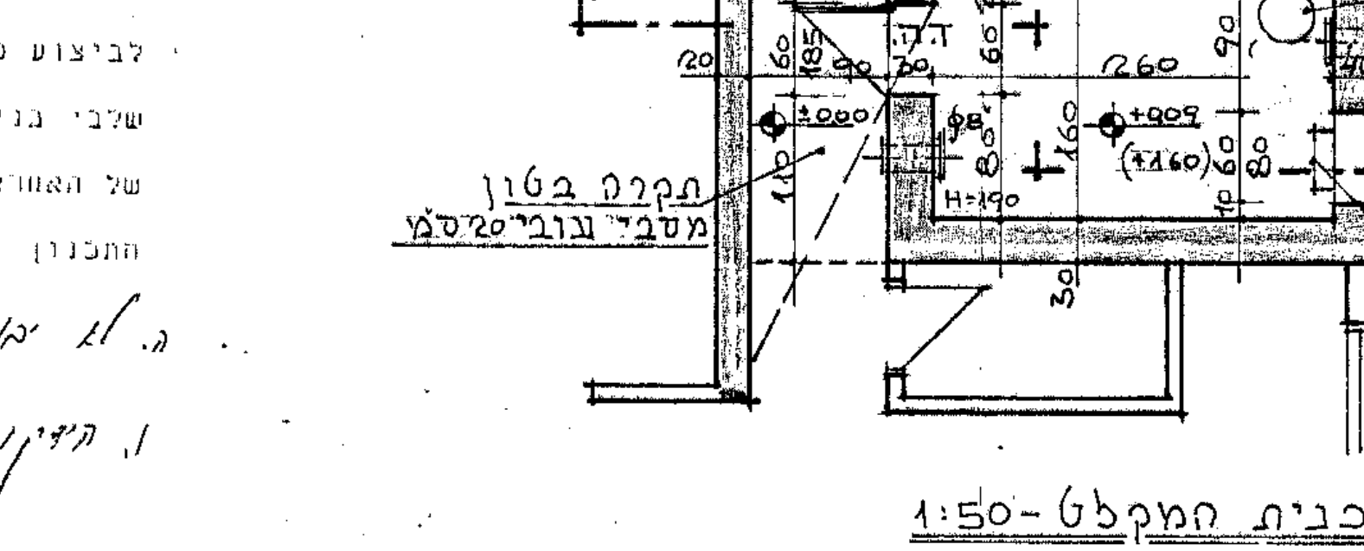
מיכל מים
H=190
260
160
+0.05
תקרה בטון
מעבר צינורות
חלון חירום פח גובה 5 מ"מ
סולם שלבי ברזל Ø16 מ"מ

תכנית המקלט 1:50

שטח המקלט נטו 260 × 160 = 4.16 מ"ר

אישור רשות מוסמכת מטעם ראש הג"א
12.3.89

הוראות ביצוע למקלט

א. ב-150 – תשתית בטון מתחת לרצפה.

ב. בטון המקלט ב-300 לפי תקן ישראלי 118 שנבדק ע"י מכון התקנים או מוסד מוסמך אחר.

ג. פלדת הזיון לפי תקן ישראלי כמפורט במפרט הכללי למקלטים (58).

ד. בידוד הרצפה והקירות יש לבצע בהתאם למפרט הכללי למקלטים, להלן פירוט מערכת ביטומנית, לאחר שהמקלט יבנה בתנאי סביבה רגילה (ללא מי תהום או אדמה חרסית בעלת פלסטיות גבוהה):-

1. רצפה פריימר זפת חם 75/25, שתי שכבות סיבאסט עם שכבת זפת חם 75/25 ביניהם, שכבת זפת חם 75/25 עם נייר טול 4 פליי.

2. קירות חוץ פריימר זפת חם 75/25, ארג זכוכית, זפת 75/25 קלקר 2.5 ס"מ.

על הקבלן/המבקש להזמין את המהנדס האחראי על ביצוע השלד ולקבל אישור לביצוע כל שלבי המקלט, יש להזמין את המפקח מטעם הרשות המקומית לבדיקת שלבי בנית המקלט, על הרשות המקומית להקפיד על מסירה לועדה המקומית תצהיר של האחראי לביצוע השלד בהתאם לקובץ התקנות 3392 מיום 21.9.78 לחוק התכנון והבניה תשכ"ה - 1965 תקנות בדבר תצהיר על הקמת שלד מקלט.

ה. לא יבוצע טיח קירות תקרה אלא דיפוי אחר במקלט ובדרך הגשה אלין

ו. הקירות יש לבצע בתבניות מבקטים או לוחות ממתכת בלבד.

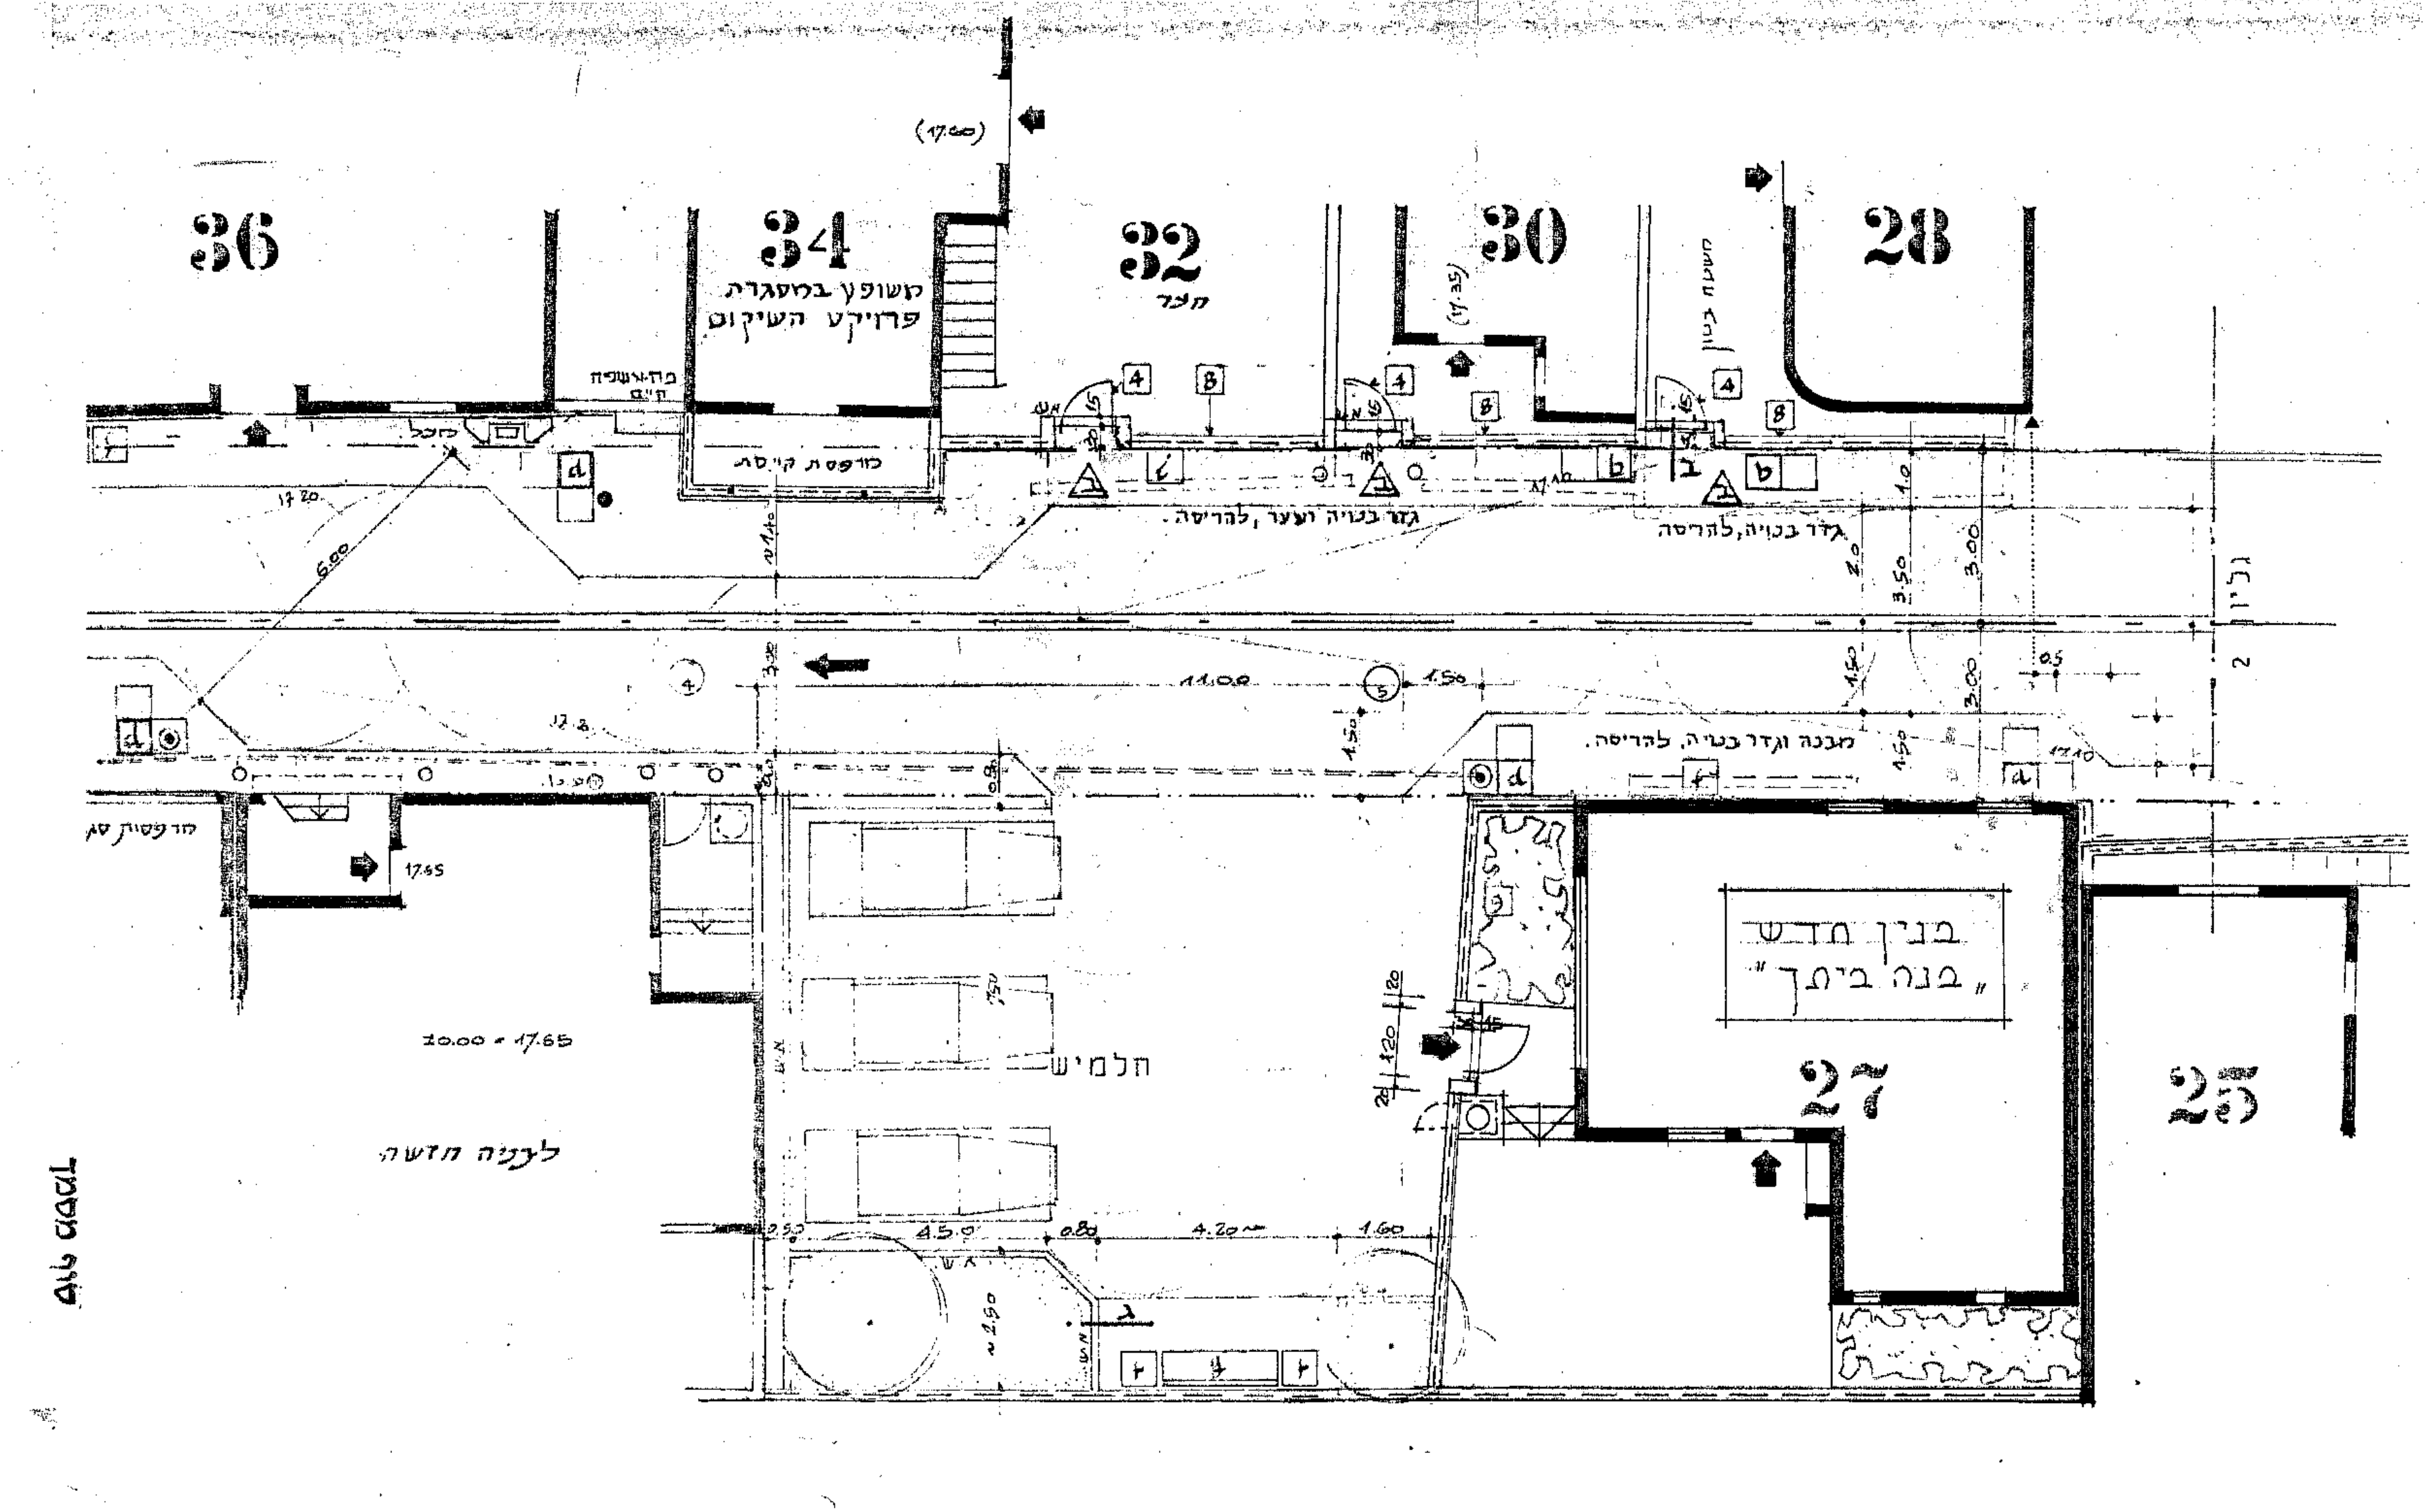
36
34
32
30
28
קשוטים במסגרת פרויקט העיקום
קיוסק
גדר בנויה ועצר להריסה
גדר בנויה ועצר להריסה
מבנה וגדר בנויה להריסה
בנין חדש "בנה ביתך"
27
25
חלמיש
לבנה חדשה
ג'ריין
20.00 × 17.65

תכנית פיתוח קמ-1:250