22

עיריית תל-אביב-יפו
מינהל ההנדסה
9-07-1989
נתקבל הוועדה המקומית לתכנון ולבניה
רישום

חוק התכנון והבניה, התשכ"ה-1965

תקנות התכנון והבניה (בקשה להיתר, תנאיו ואגרות), התש"ל-1970

טופס 2 (תקנה 2(א))

תיק מס 4046-027

015

מיפרט

א. תיאור הבנין

1. המקום	תל אביב	הרחוב: ששון	מס': 27	גוש: 6135	חלקה: 44 (חלק)	תכנית מיתאר מקומית או מפורטת	מגרש

	השם	המען	מס' הטלפון
2. המבקש	סגלוביץ משה	ת.ד. 4266 רמת אליהו ראל"צ	993502
3. בעל הזכות בנכס	—״—	—״—	
4. עורך הבקשה *	פרחי אדריכלים בע"מ רח' אדם הכהן 16 ת"א.		2439997
5. האחראי לביצוע השלד	י. לבני מהנדס	רח' רוקח 35 רמת גן	7521921

2430224
5239997

6. אזור הבניה: ■ מגורים ☐ מסחר ☐ תעשיה ☐ בנין ציבורי ☐ חקלאי ☐ ....

7. שטח: המגרש/החלקה: 105 מ"ר. אחוז הבניה המותר: % ....

8. מטרת הבנין: ■ מגורים ☐ הארחה ☐ עסקים ☐ תעשיה ☐ חקלאי ☐ ציבורי ☐ ....

9. מהות הבנין ותכליתו: בית מגורים חדש במקום בית קיים במסגרת פרויקט בנה ביתך

10. תיאור העבודה המוצעת: ■ בנין חדש ☐ תוספת לבנין קיים ☐ הריסה ☐ תיקונים ☐ שינוי בבנין ☐ ....
☐ שינוי בשימוש ממטרה: .... למטרה: ....

11. האם הבניה היא בעדי: ☐ משרד ממשלתי ☐ הרשות המקומית ☐ הסוכנות היהודית

אכות נמוכה

ב. היקף הבניה

קומה	קיים	מוצע	סך הכל	אחוז הבניה	מגורים בדירות – עד 45 מ"ר	עד 65 מ"ר	עד 90 מ"ר	עד 100 מ"ר	מעל 100 מ"ר	עסקי הארחה וכו'	ציבורי	שונות	מס' חדרים – קיים	מס' חדרים – מוצע
1	2	3	4	5	6	7	8	9	10	11	12	13	14	15
קרקע		52.87		50.35%										
א		~~48.06~~ 48.46		~~45.77%~~ 46.15%										
ב		23.83		22.69%										
ג														
ד														
ה														
ו														
ז														
הכניסה הקובעת לבנין														
חדרי מדרגות														
בניני עזר														
סך הכל		124.76		118.81%										

הנפח המוצע: של הבנין העיקרי .... מ"ק. של בנין עזר .... מ"ק.

ג. השימוש בבנין

1. הבניה המוצעת למגורים

דירות בנות:	שטח כל דירה מ"ר	מספר דירות מכל סוג	שטחים – מ"ר: כל הדירות	מזה: רצפות חדרי דיור בלבד, וטרסות מקורות	מזה: רצפות חדרי שירות ופרוזדורים בלבד	מזה: רצפות של מרפסות בלתי מקורות	מספר חדרים: דיור	מטבחים	אמבטיות	בתי שימוש	אחרים
1	2	3	4	5	6	7	8	9	10	11	12
חדר אחד											
2 חדרים											
3 חדרים											
4 חדרים							4	1	2	2	1
5 חדרים											
6 חדרים											
7 חדרים ויותר											
חדרים נוספים לדירות קיימות											
בניני עזר											
סך הכל		1									

נסרק

2

2. הבניה הקיימת והמוצעת לתעשיה ולמלאכה

פרטים	קיים – שטח	קיים – גובה	קיים – נפח	קיים – % הבניה	מוצע – שטח	מוצע – גובה	מוצע – נפח	מוצע – % הבניה	סך הכל – שטח	סך הכל – נפח	סך הכל – % הבניה	הערות
1	2	3	4	5	6	7	8	9	10	11	12	13
אולמי מלאכה												
משרדים												
חדרי שירות												
סככות												
בניני עזר												
חדרי מדרגות												
סך הכל												

3. הבניה המוצעת למטרות אחרות (הארחה, עסקים ומשרדים, בניני ציבור, בניני משק חקלאי, מטרות שונות).

השימוש המיועד	שטחים – מ"ר: סך הכל מ"ר	מזה: חדרים	מזה: אולמות	מזה: אחסנה	מזה: חדרי שירות	מספר חדרים, אולמות וכו': חדרים	אולמות	אחסנה	חדרי שירות
1	2	3	4	5	6	7	8	9	10
בניני עזר (למעט אלה המפורטים ב־ג(4))									

4. חלקי בנין אחרים – הבניה המוצעת, שטח במ"ר.

חדרי מדרגות	מרפסות שלא נכללו לעיל	מעליות	חדרי הסקה	חדרי כביסה	מקלטים	שטח עמודים מפולשת	מחסנים	מוסכים	בניני עזר נוספים	סך הכל
1	2	3	4	5	6	7	8	9	10	11
	25.77				7.04					

ד. חומר הבניה

קירות חיצוניים	☐ בטון מזוין	☐ לבני בטון או בלוקים	☐ לבני סיליקט	☐ לבנים שרופות	☐ אבן טבעית
	☐ אבן מלאכותית	☐ איטונג	☐ עץ	☐ ברזל	☐ חמרים אחרים
תקרות	☐ בטון מזוין	☐ עץ	☐ חומר אחר		
גג	☐ בטון מזוין	☐ רעפים	☐ אסבסט	☐ פח	☐ חומר אחר ....

ה. גדרות

קיימות.................. מ"א מוצעות.................. מ"א

ו. מקרא

▨ בטון או בטון מזוין	☐ אבן	☐ עץ	☐ איטונג
▨ בלוקים או לבנים מבטון	☐ סיליקט או לבנים אדומות	☐ חומר אחר	☐ להריסה

הערות:

הנני מאשר כי הנתונים הנ"ל נכונים

תאריך: 28-12-88 חתימת המבקש ×

יוסי פרחי אדריכל
רח' אדם הכהן 16 ת"א 64 585
טלפון 2439997, 243524

חתימת עורך הבקשה *

חתימת האחראי לביצוע השלד

עקיבא לבני
מהנדס בנין

חתימת בעל הזכות בנכס ×

לשימוש הוועדה המקומית בלבד	מס' ההיתר	תאריך ההיתר	תאריך התחלת הבניה	תאריך גמר הבניה

חותמת הוועדה המקומית

אישורים של רשויות חוץ: טפן כ־סיק
חתימת המבקש:
כתובת: ששון 25 ת"א
ת.ז. 0,01936665

* היו מספר עורכי בקשה, כאמור בתקנה 3ה', יבוא במקום כל אלה.
הראשון שברשימת עורכי הבקשה, כאמור בטופס 1.

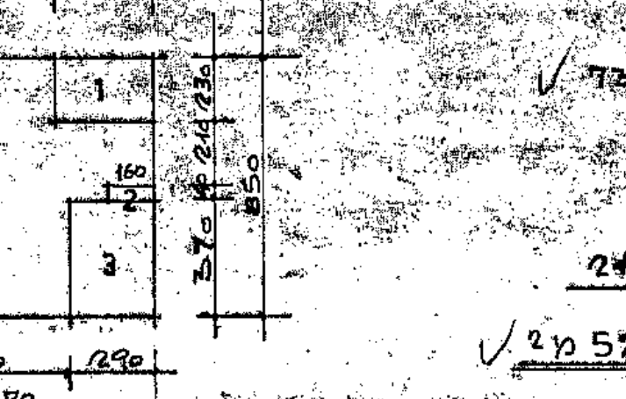

חישוב שטח ק. קרקע

מסגרת: 870 × 850 = 73.95 ✓

הורדות:
1. 330 × 230 = 7.59 ✓
2. 160 × 0.40 = 0.64 ✓
3. 290 × 370 = 10.73 ✓
4. 850 × 0.50 / 2 = 2.12 ✓

21.08

סה"כ שטח .... 52.87 מ"ר ✓

שטח המקלט ① = 380 × 280 = 7.59 מ"ר

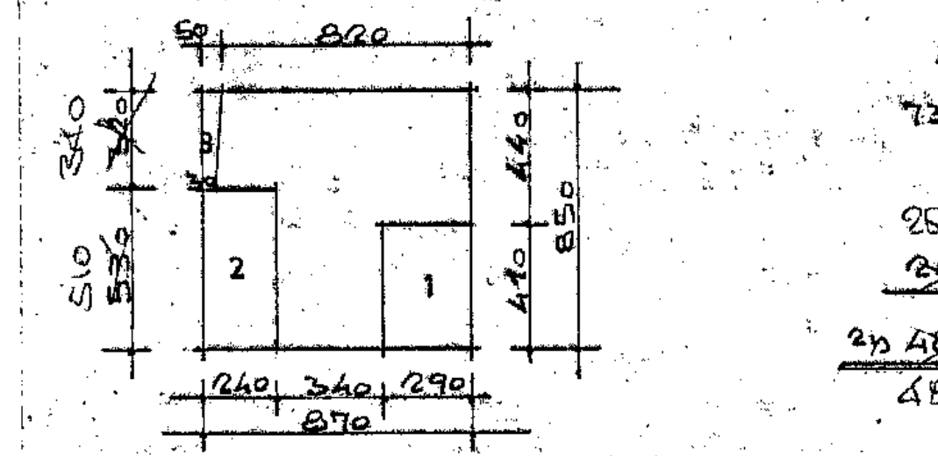

חישוב שטח קומה א'

מסגרת: 870 × 850 = 73.95

הורדות:
1. 290 × 410 = ~~11.89~~
2. 240 × ~~530~~ 510 = ~~12.72~~ 12.24
3. (50+30) × 340 / 2 = ~~1.28~~ 1.36

~~26.89~~ 25.49

סה"כ שטח .... ~~48.06~~ 48.46 מ"ר

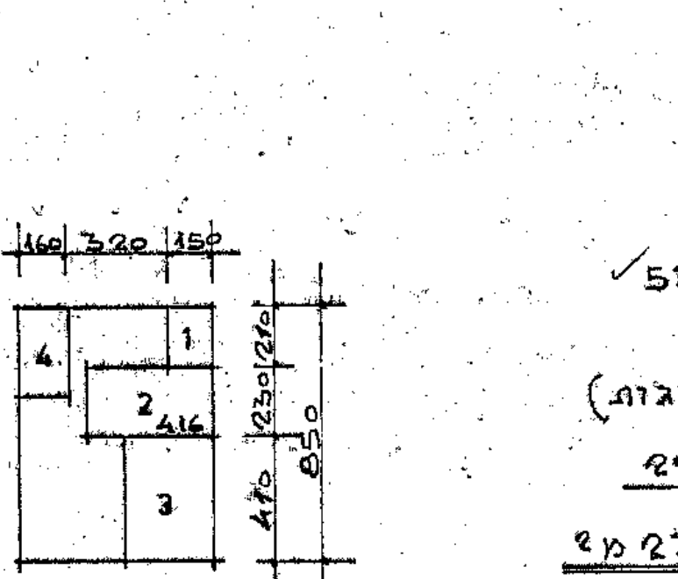

חישוב שטח קומה ב'

מסגרת: 850 × 630 = 53.55 ✓

הורדות:
1. 150 × 240 = 3.45 ✓
2. 416 × 230 = 9.56 ✓ (חדר מדרגות)
3. 290 × 440 = 11.89 ✓
4. 320 × 160 = 5.12 ✓

29.72

סה"כ שטח .... 23.83 מ"ר

תרשים הסביבה
ק.מ. 1:1250

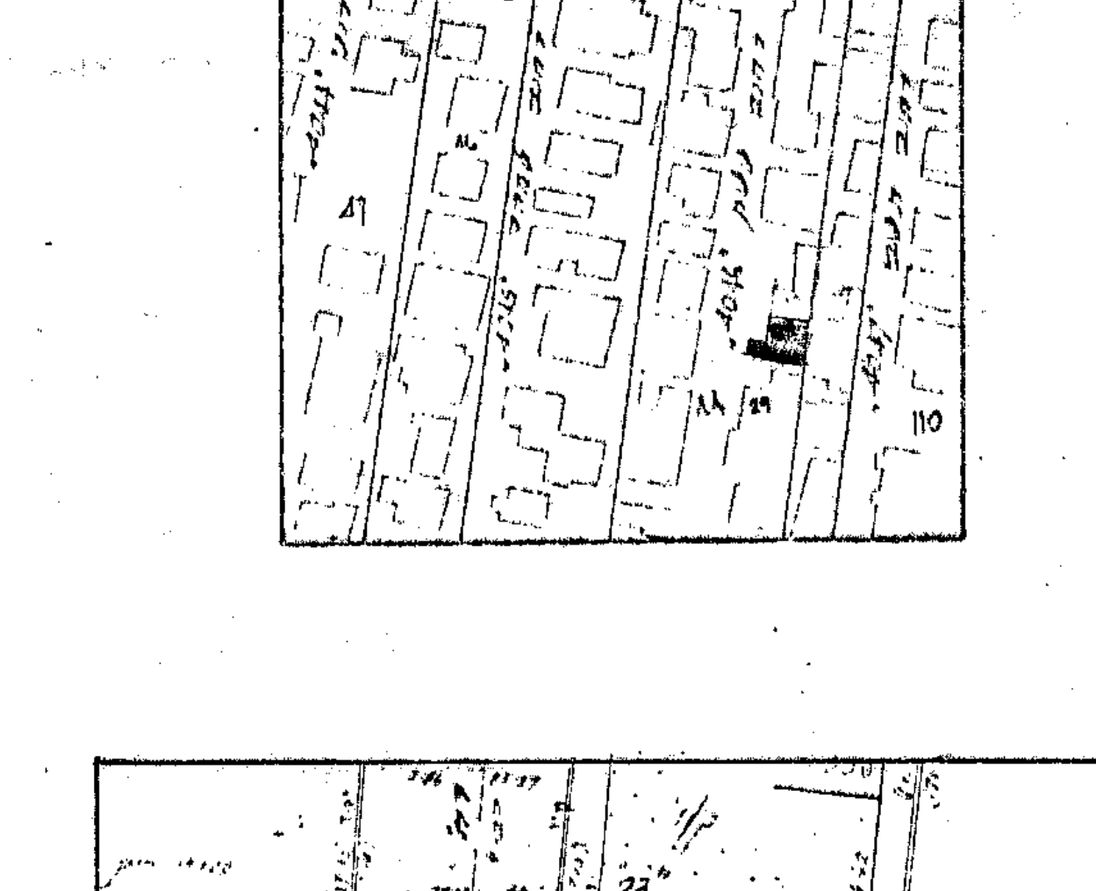

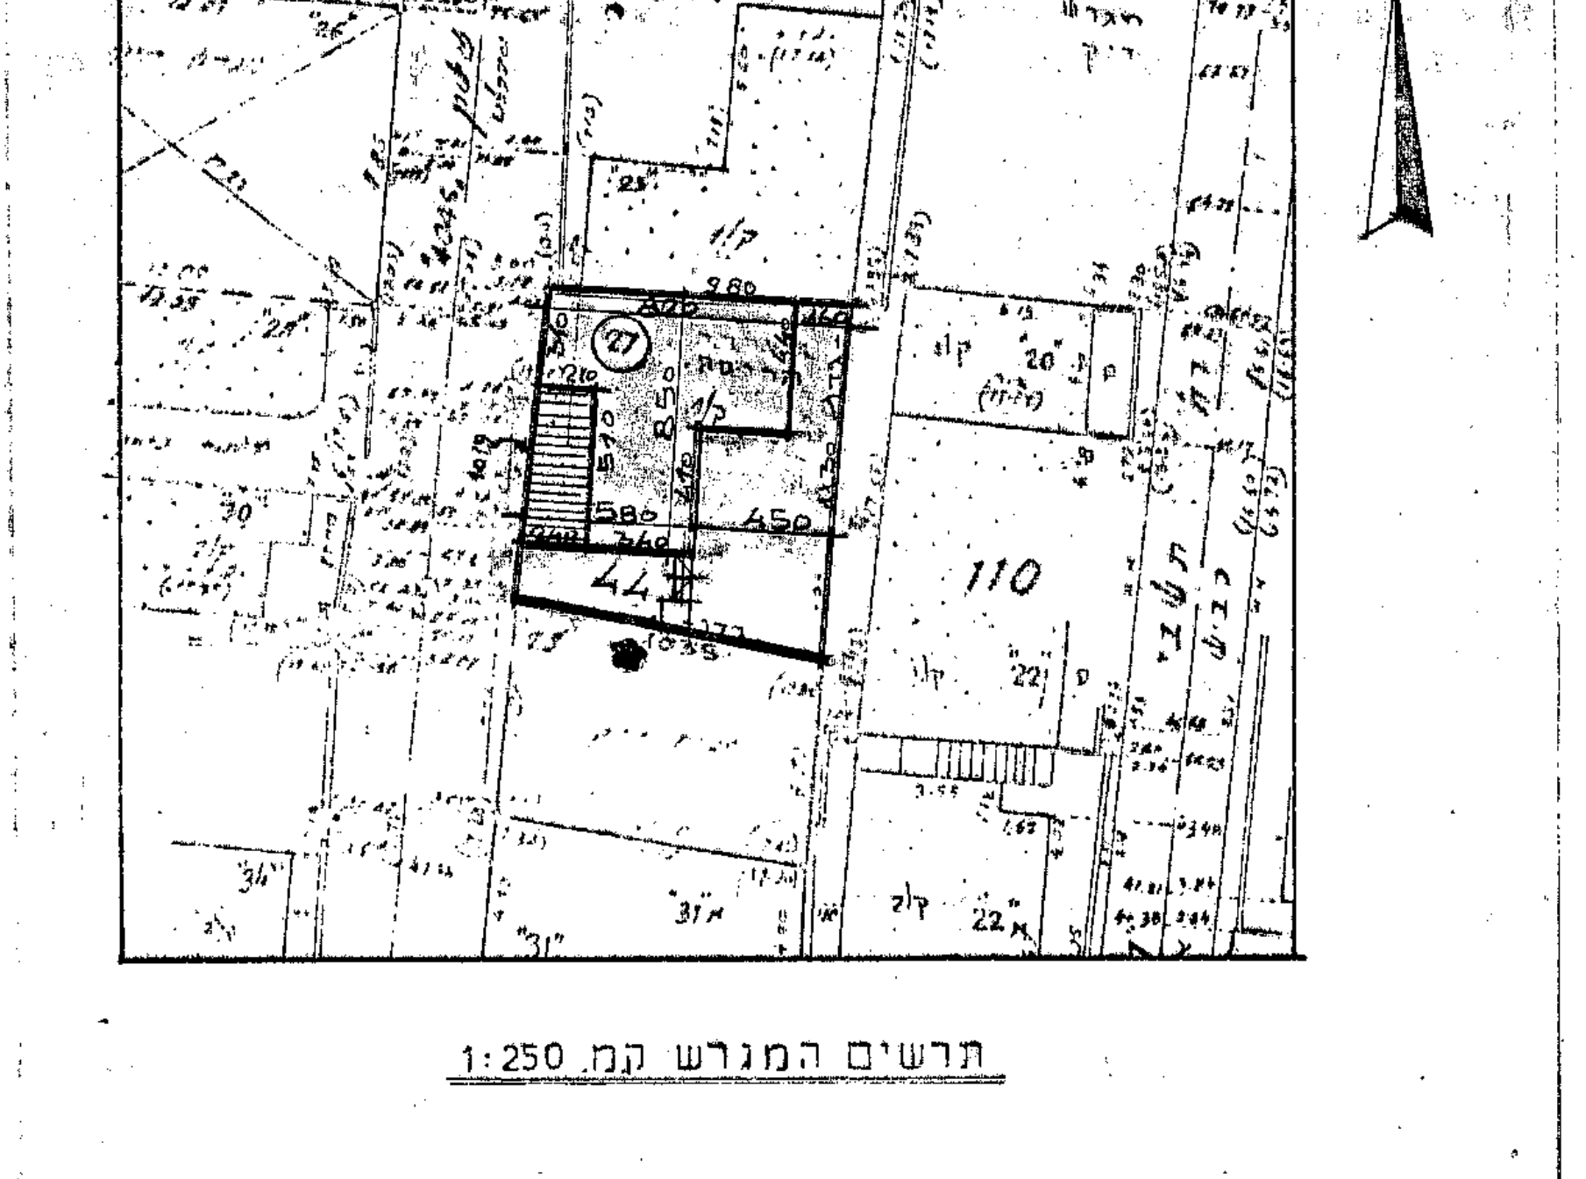

תרשים המגרש קנ"מ 1:250

3

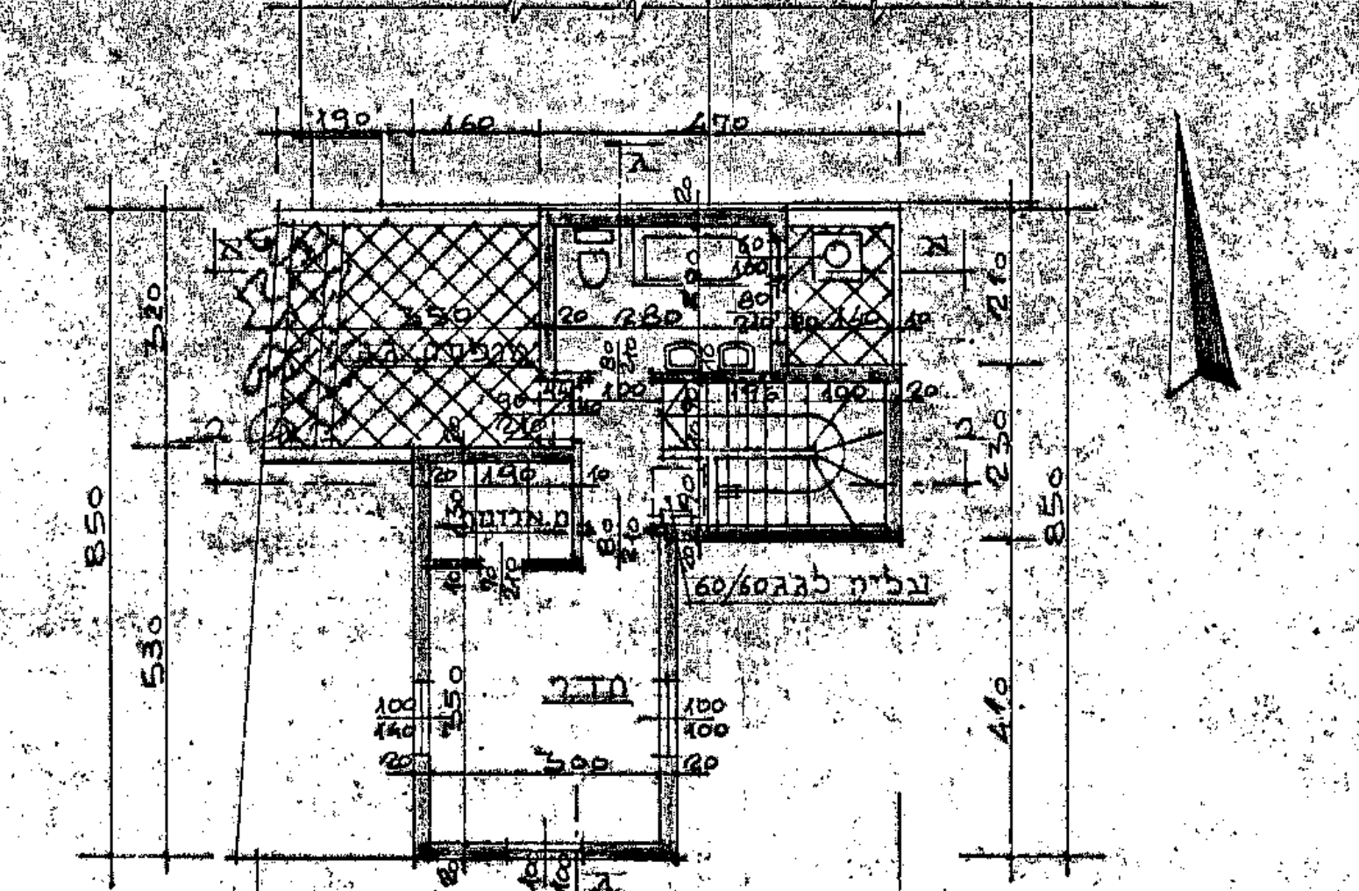

תכנית קומה ב' קנ"מ 1:100

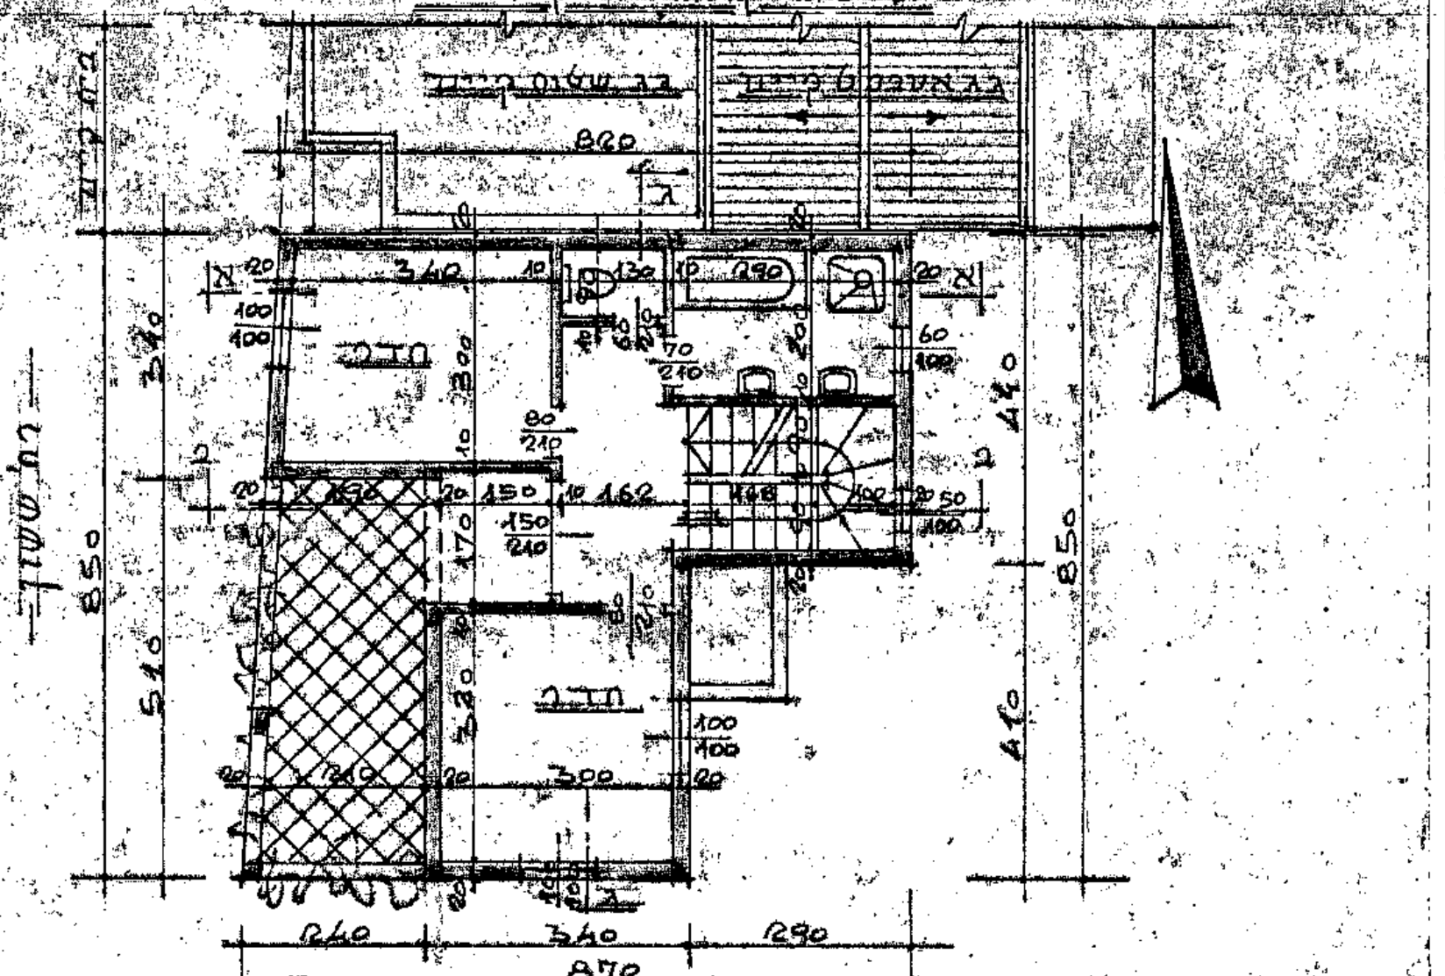

תכנית קומה א' קנ"מ 1:100

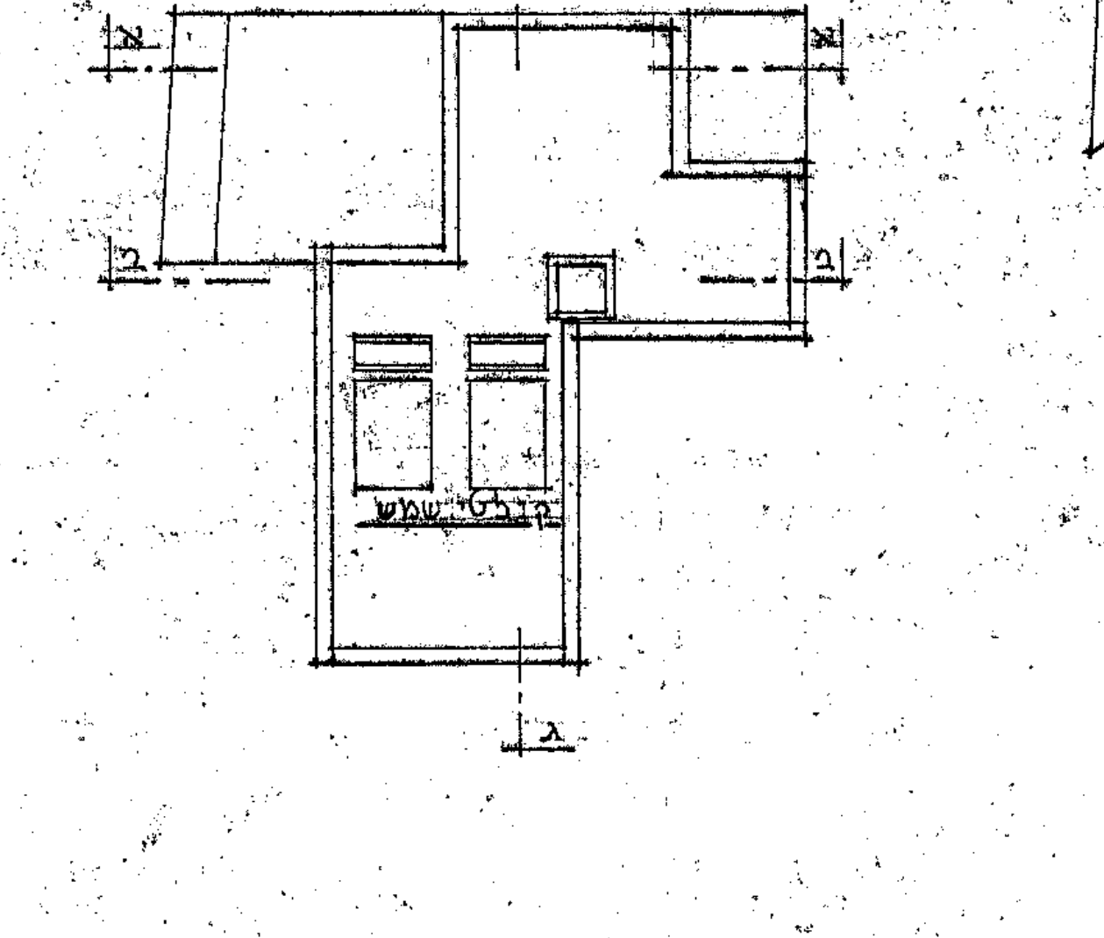

תכנית הגג קנ"מ 1:100

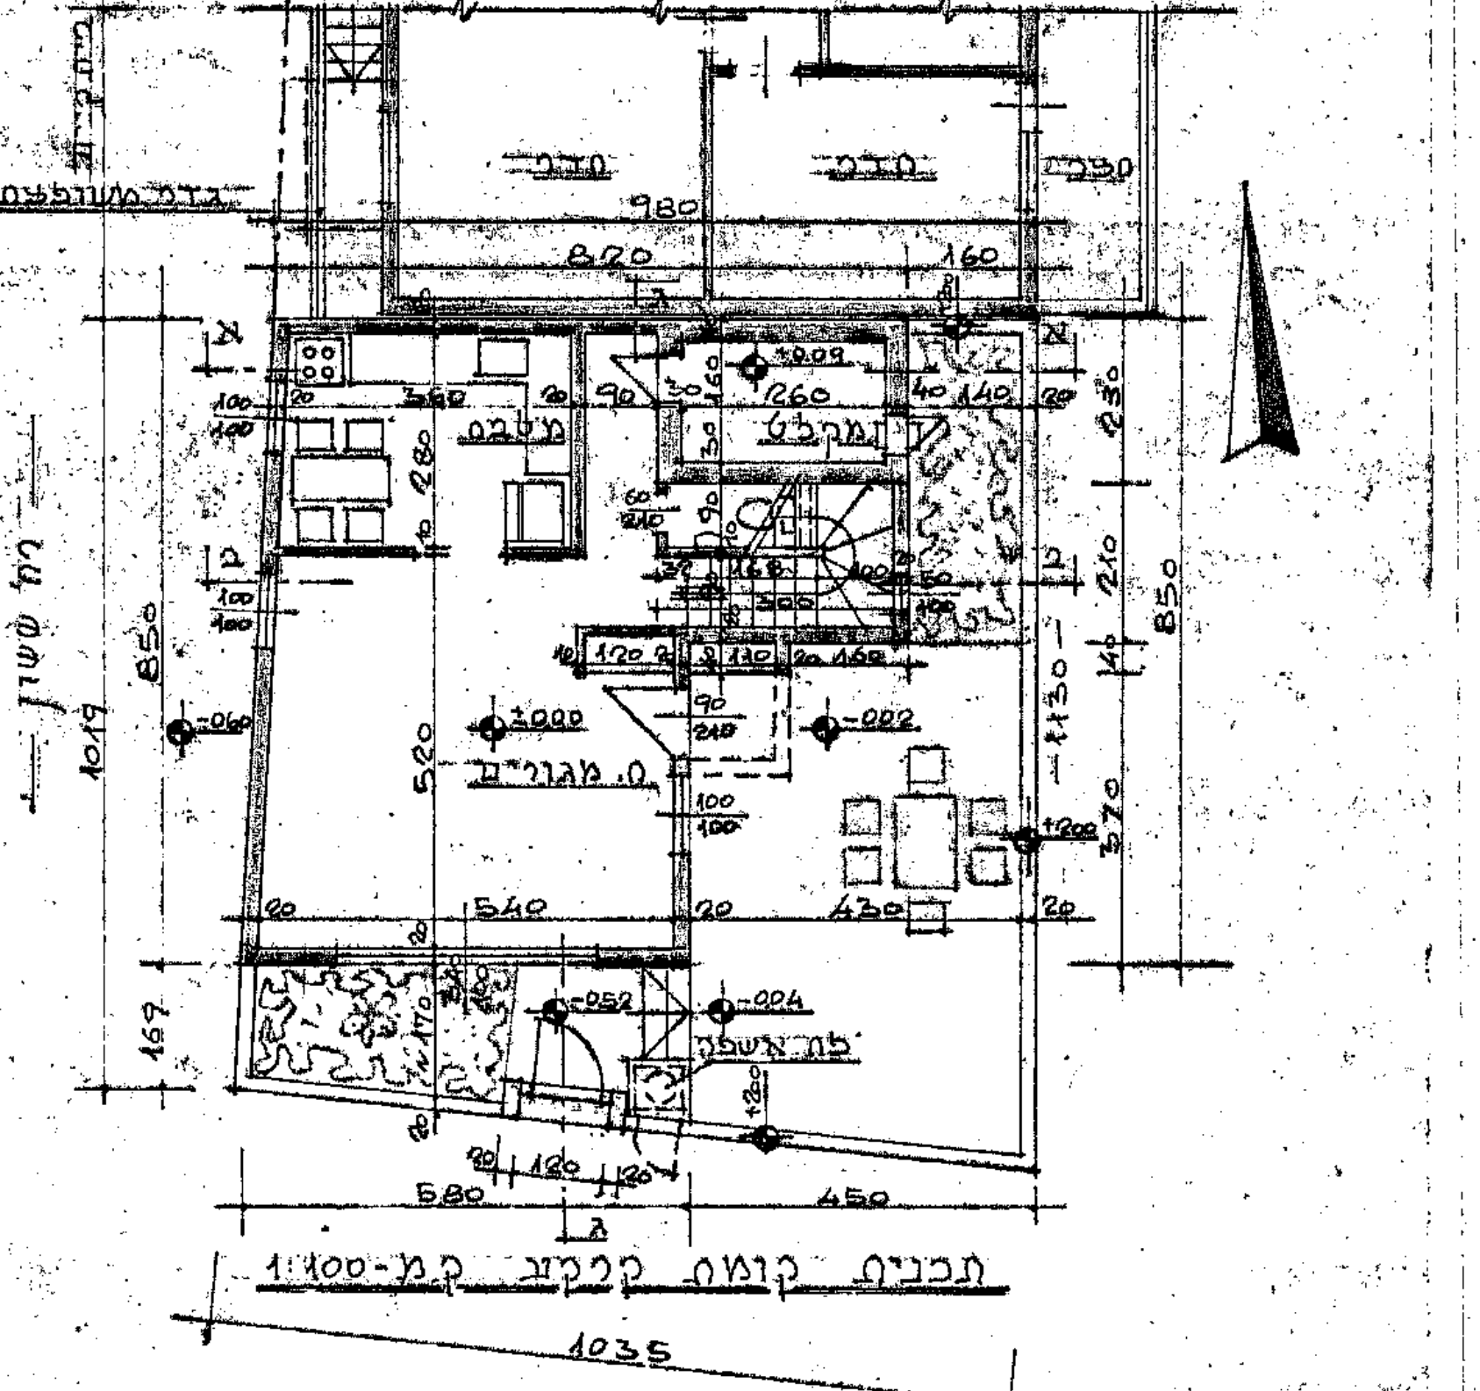

תכנית קומה קרקע קנ"מ 1:100

סגלוביץ רח' ששון 27

4

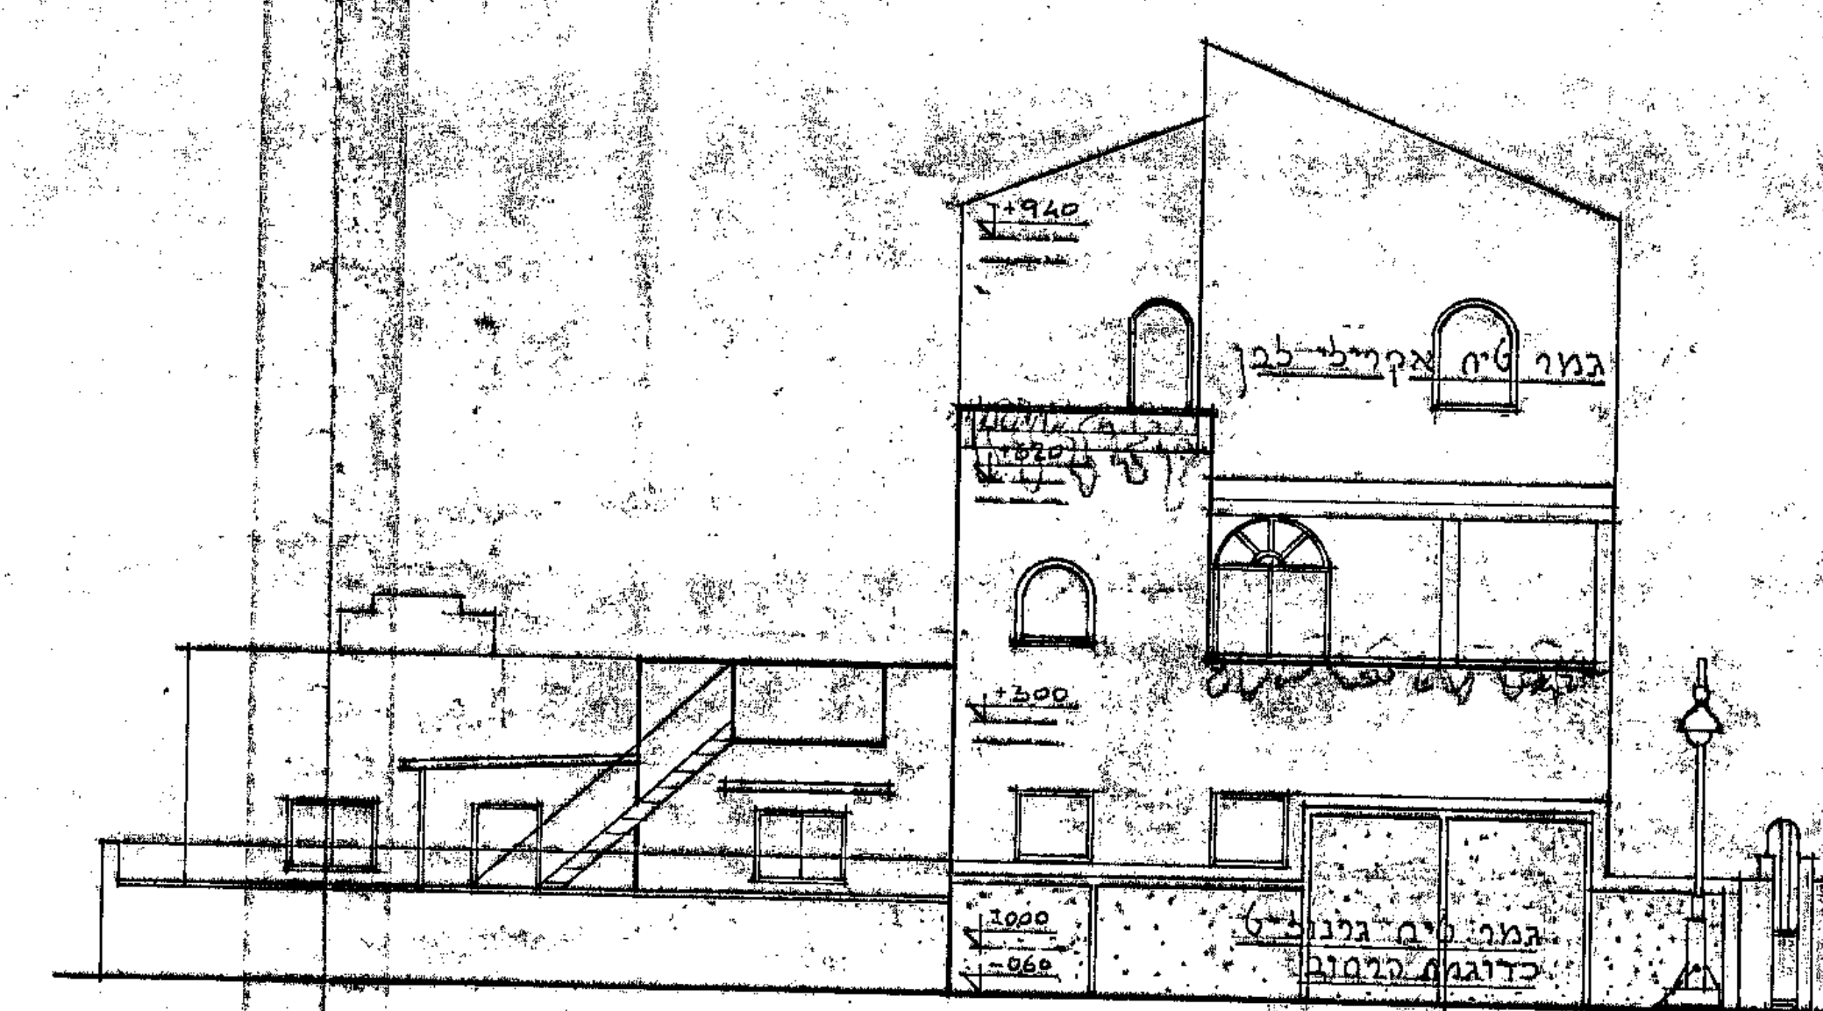

חזית מערבית ק.מ 1:100

אדניות ועמוד מאורה לפי תכנית פיתוח מאושרת רח' ששון - בביצוע

סורגים פרימיטיביים בגוון לבן בלבד

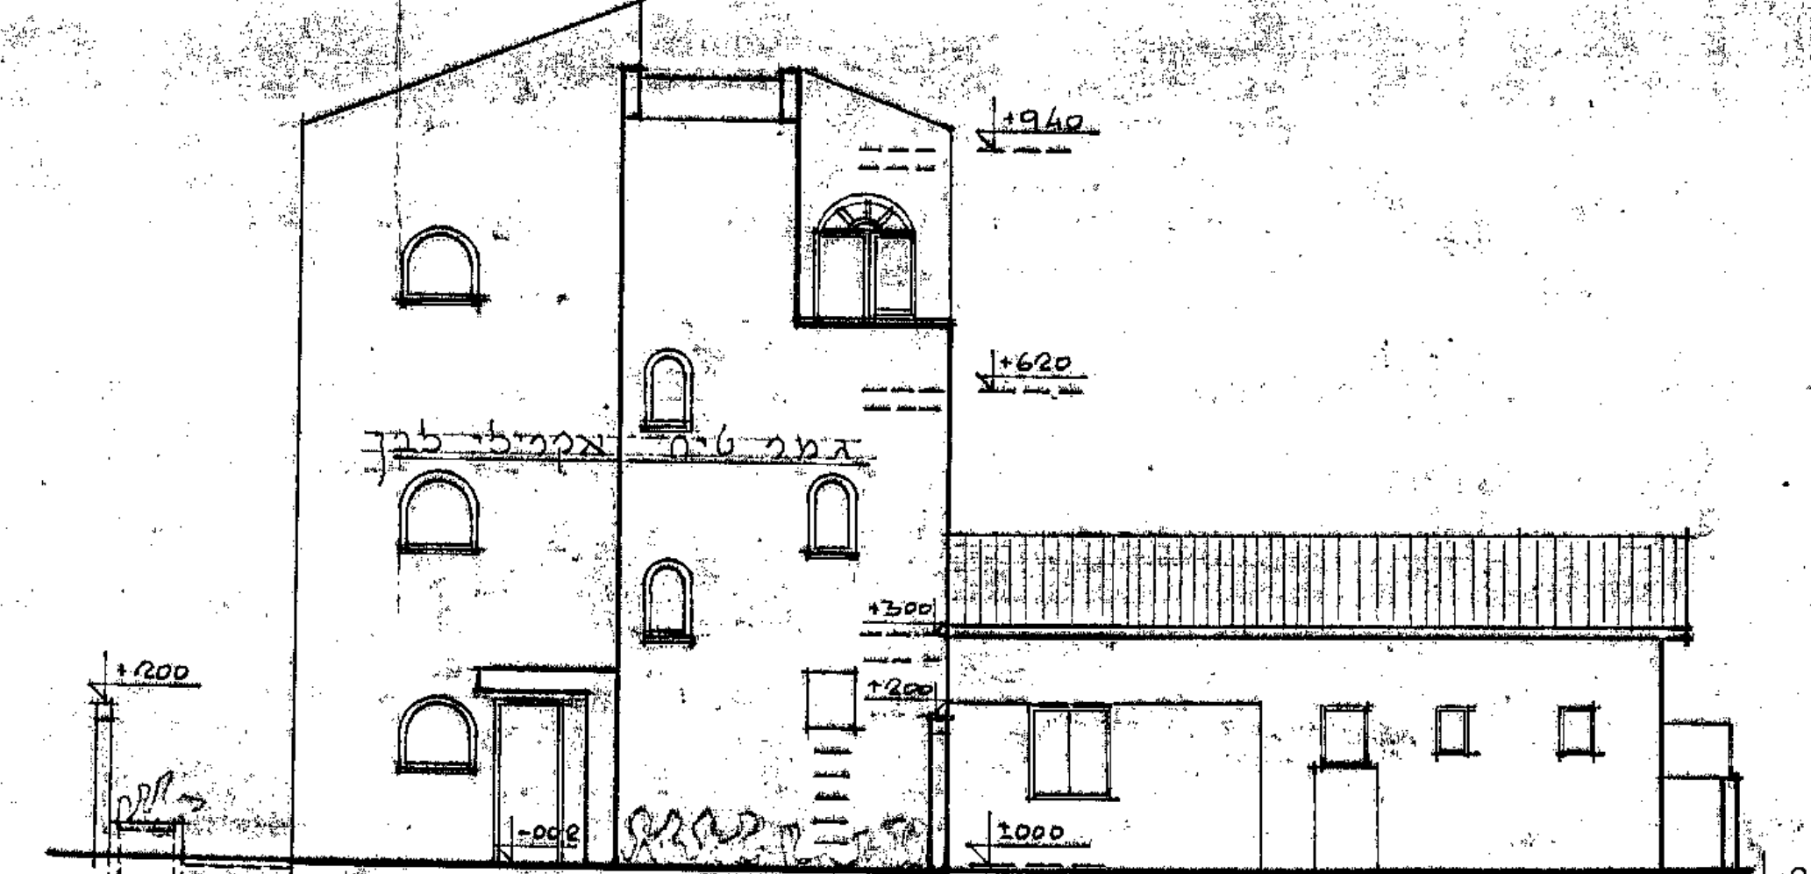

חזית מזרחית ק.מ. 1:100

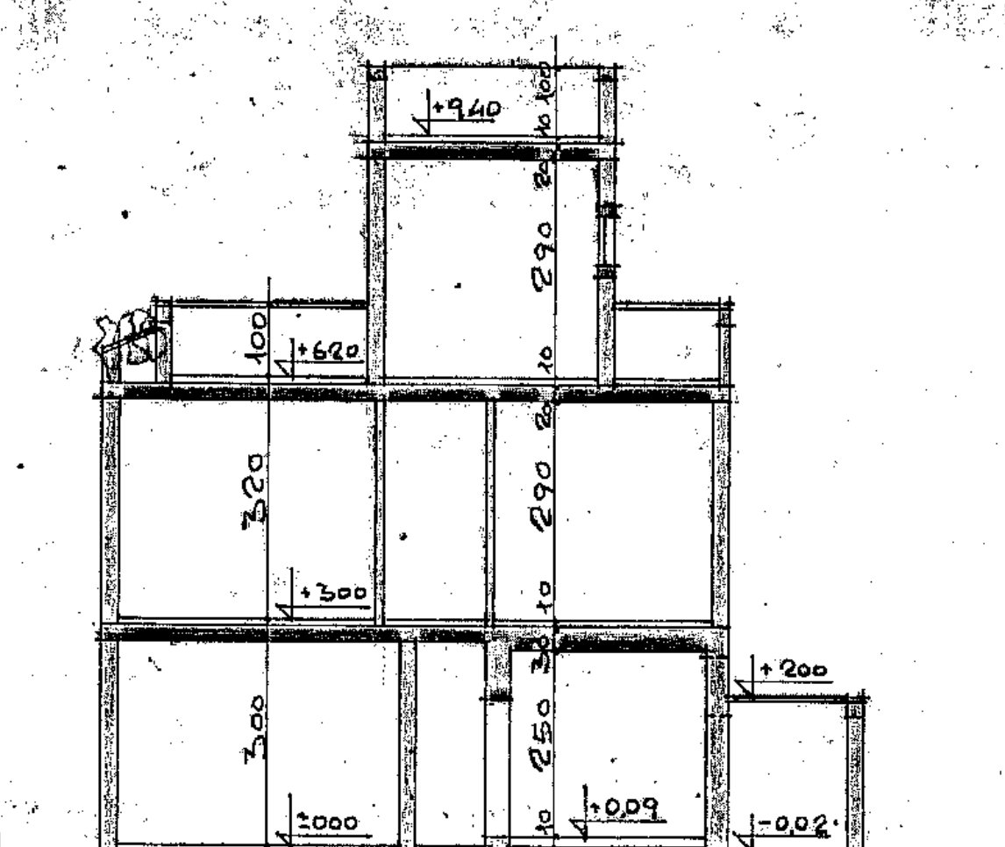

חתך א-א ק.מ. 1:100

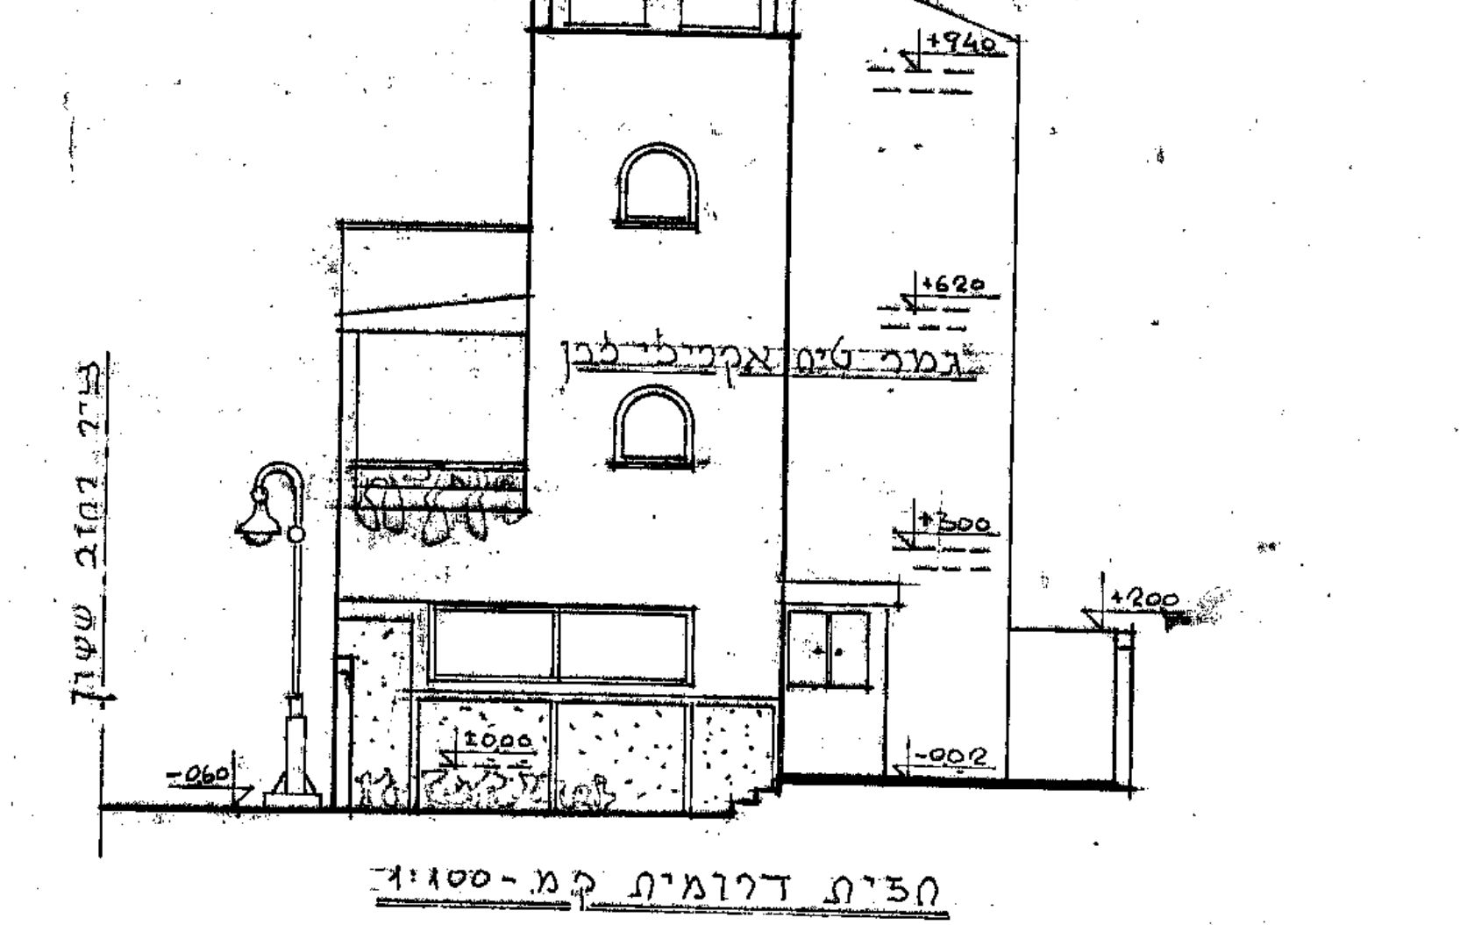

חזית דרומית ק.מ. 1:100

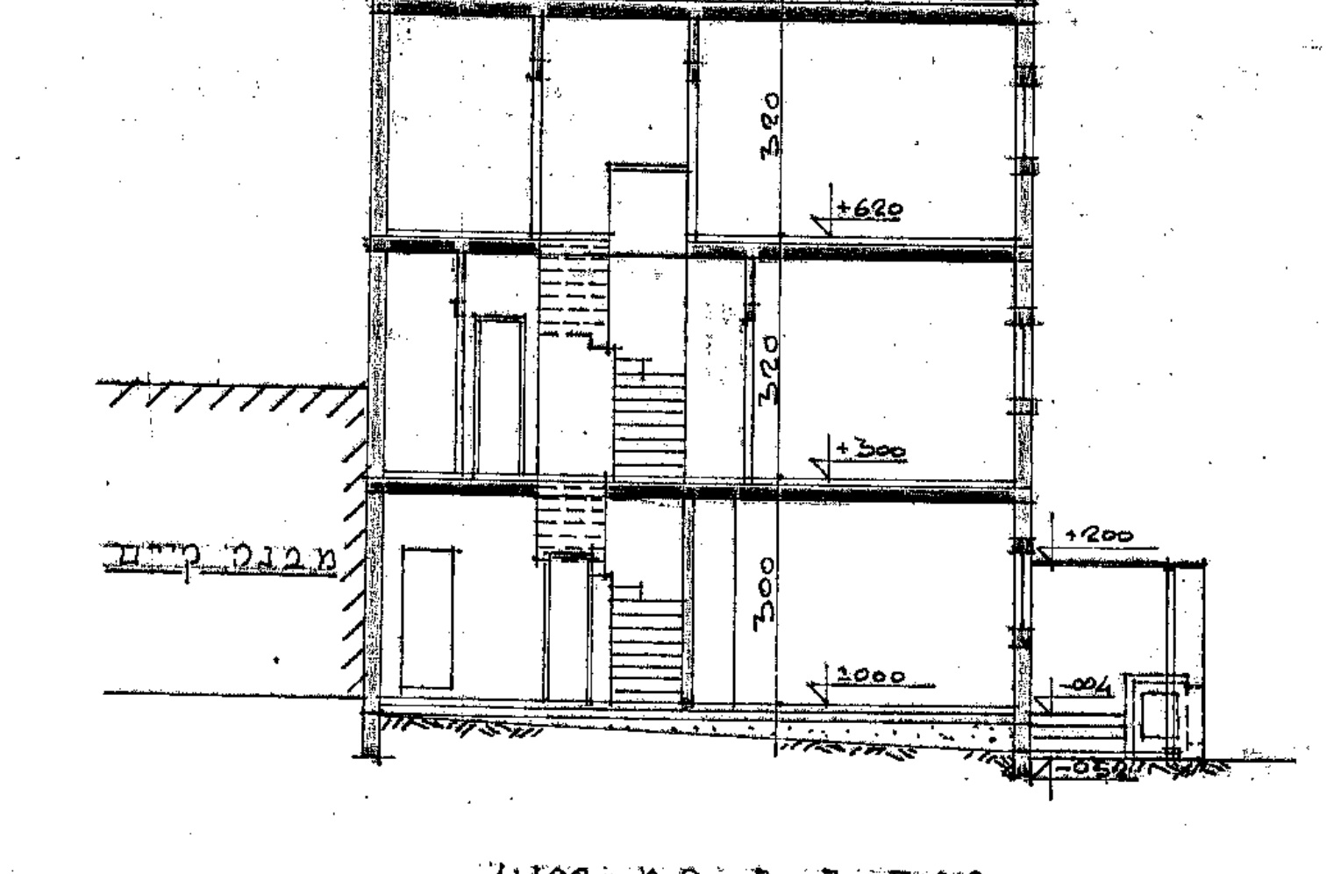

חתך ג-ג ק.מ. 1:100

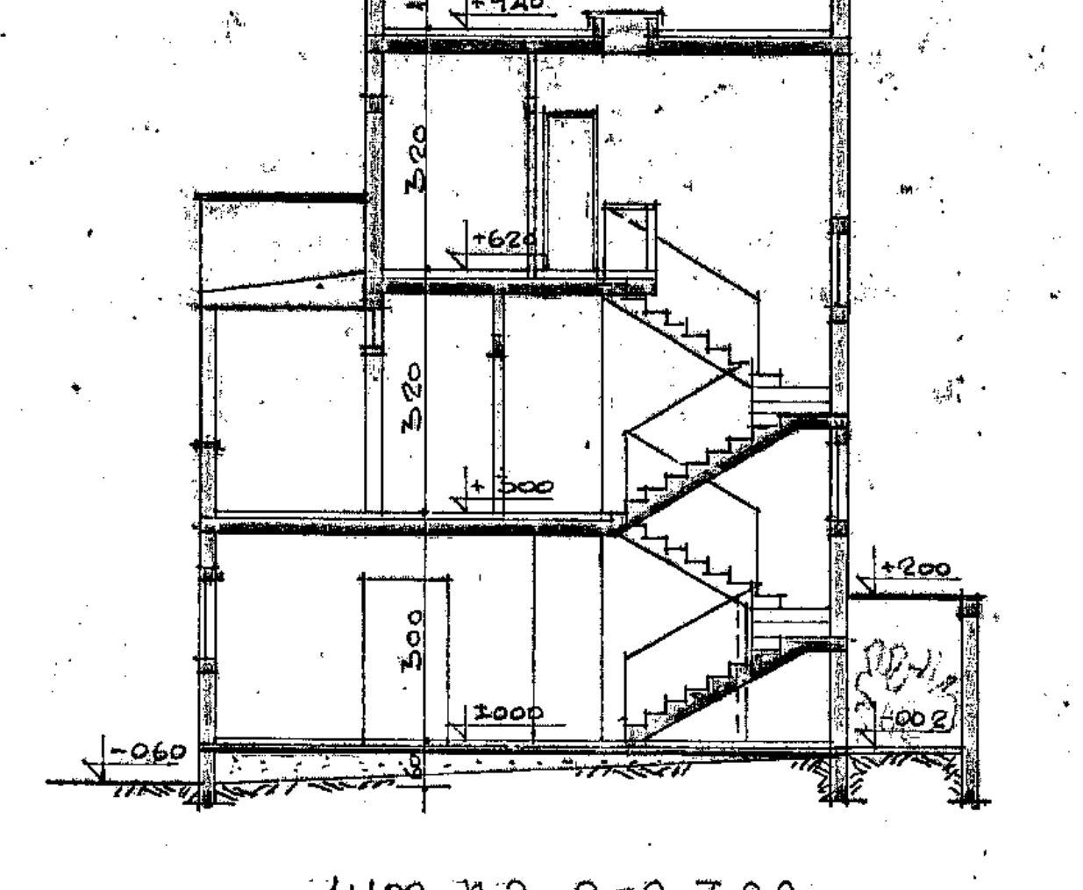

חתך ב-ב ק.מ. 1:100

סגלוביץ רח' ששון 27

6

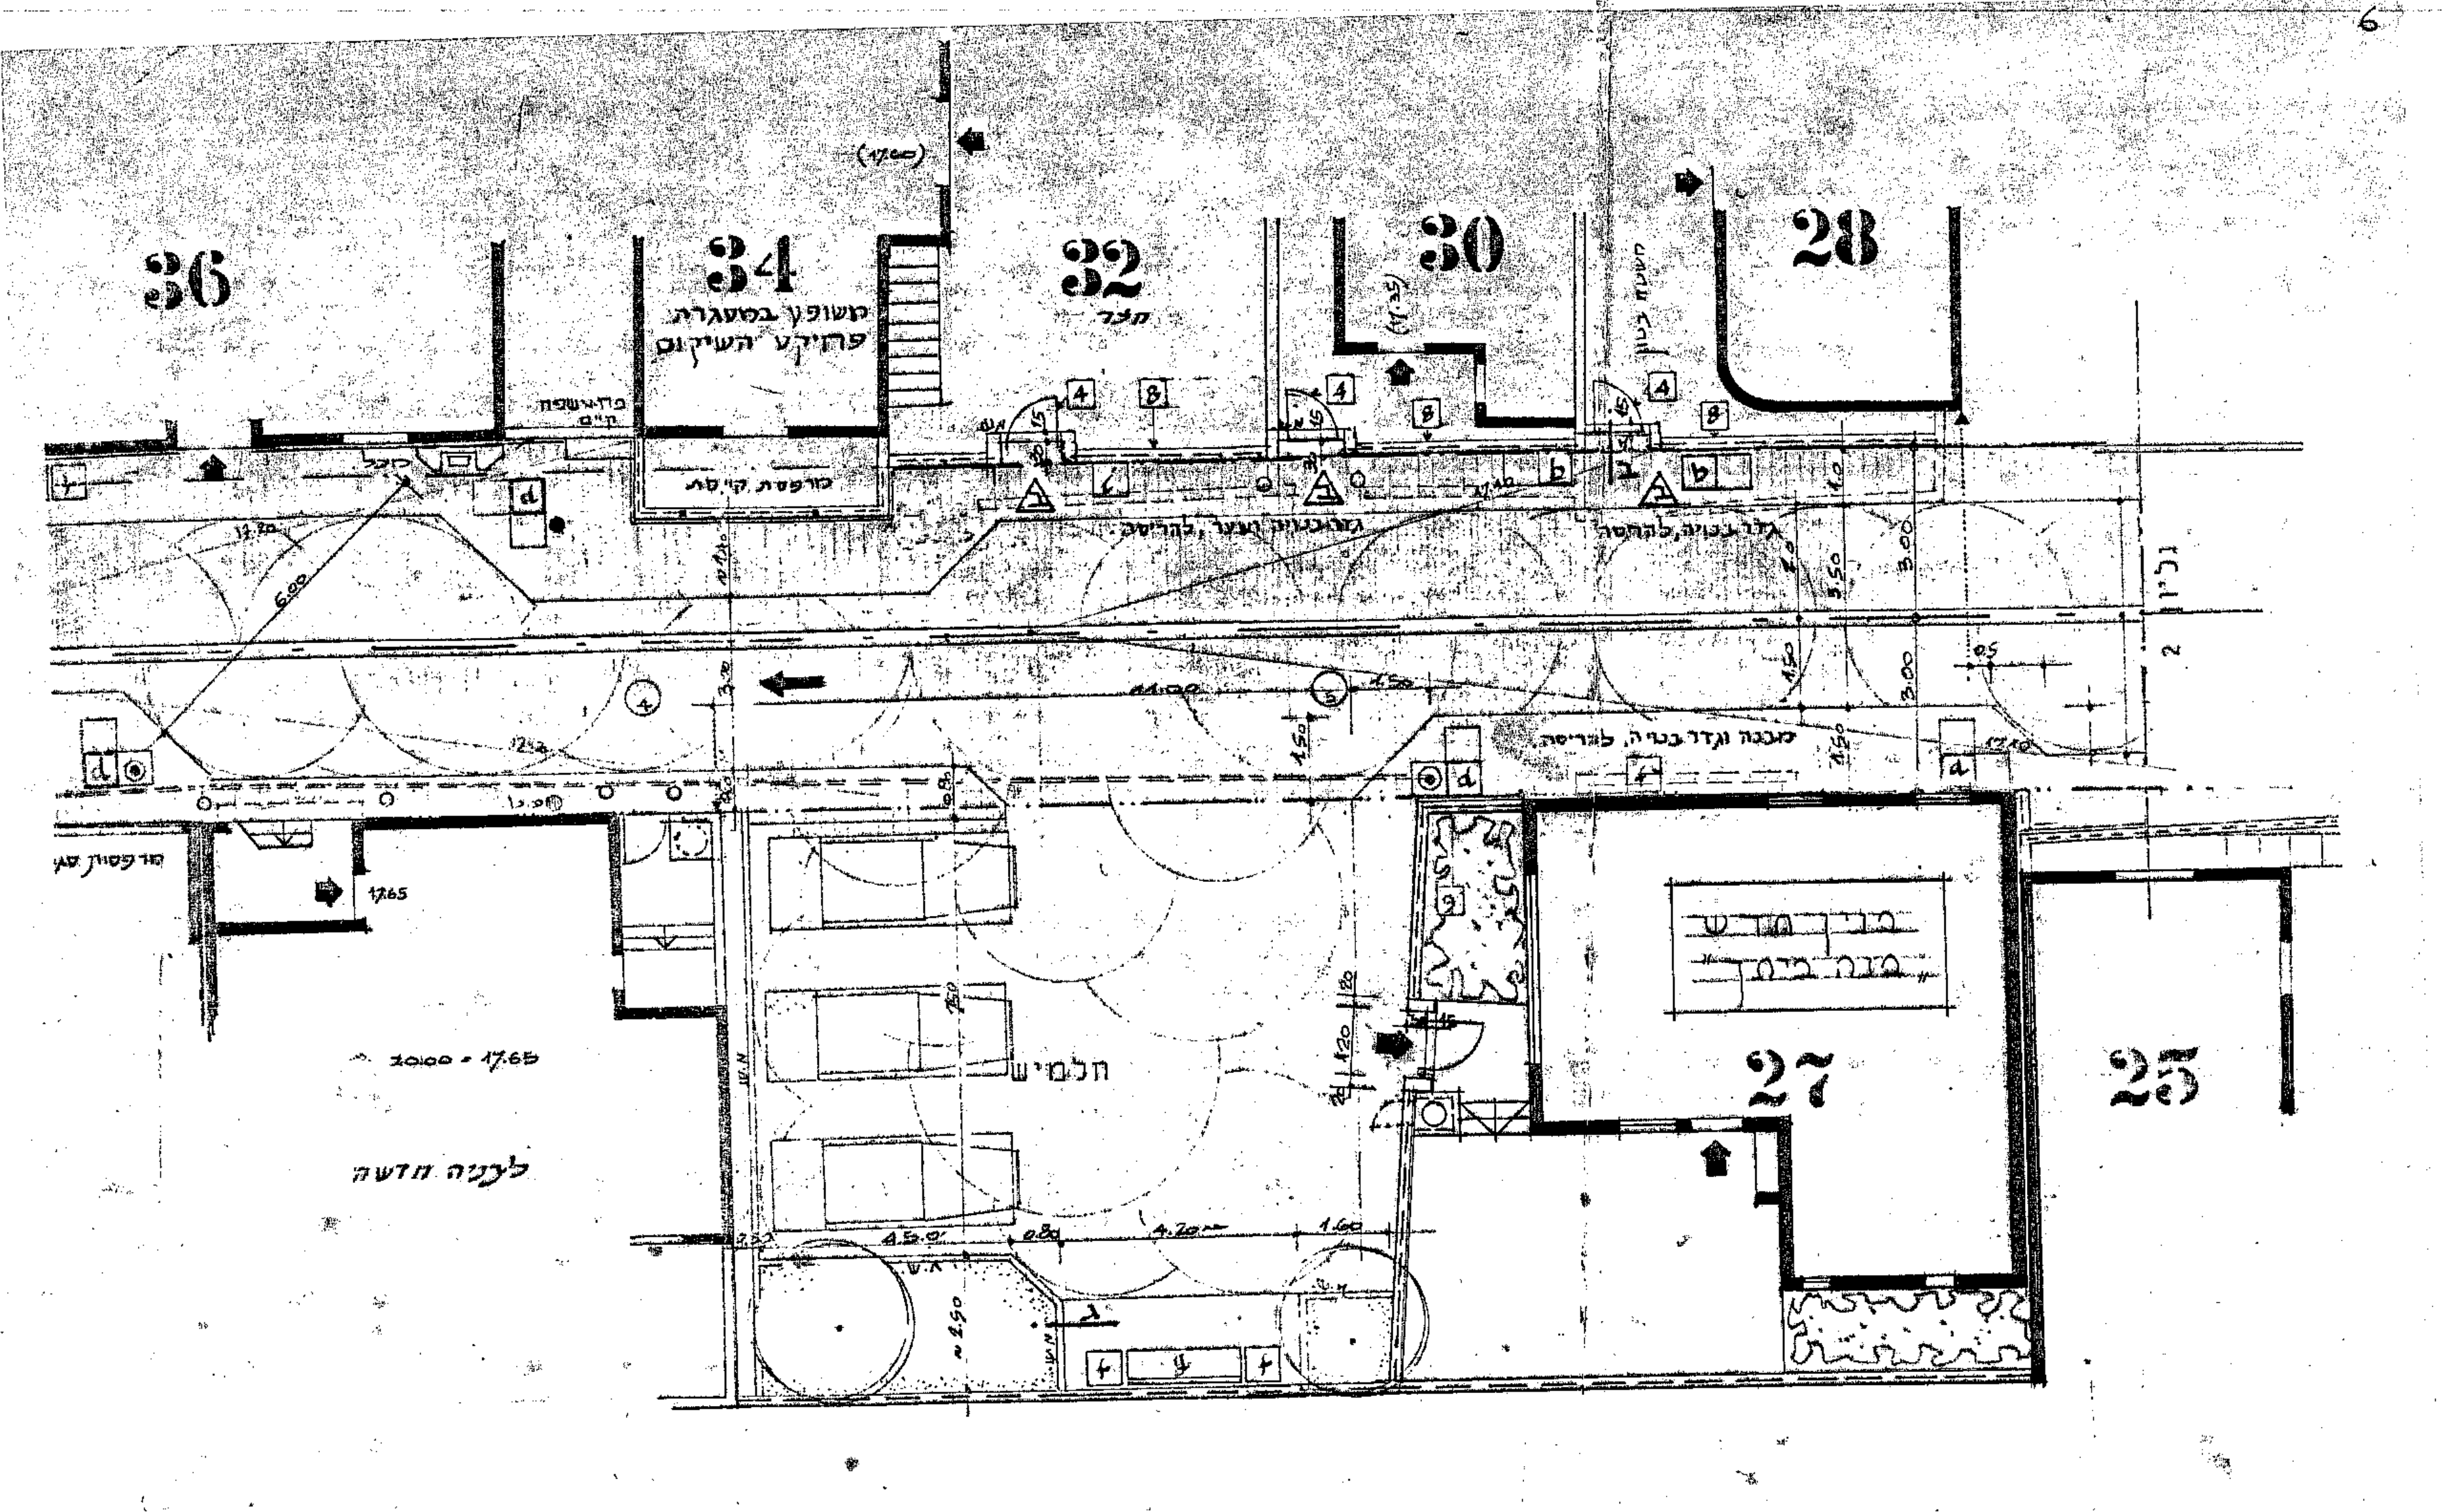

תכנית פיתוח קנ"מ 1:100

5

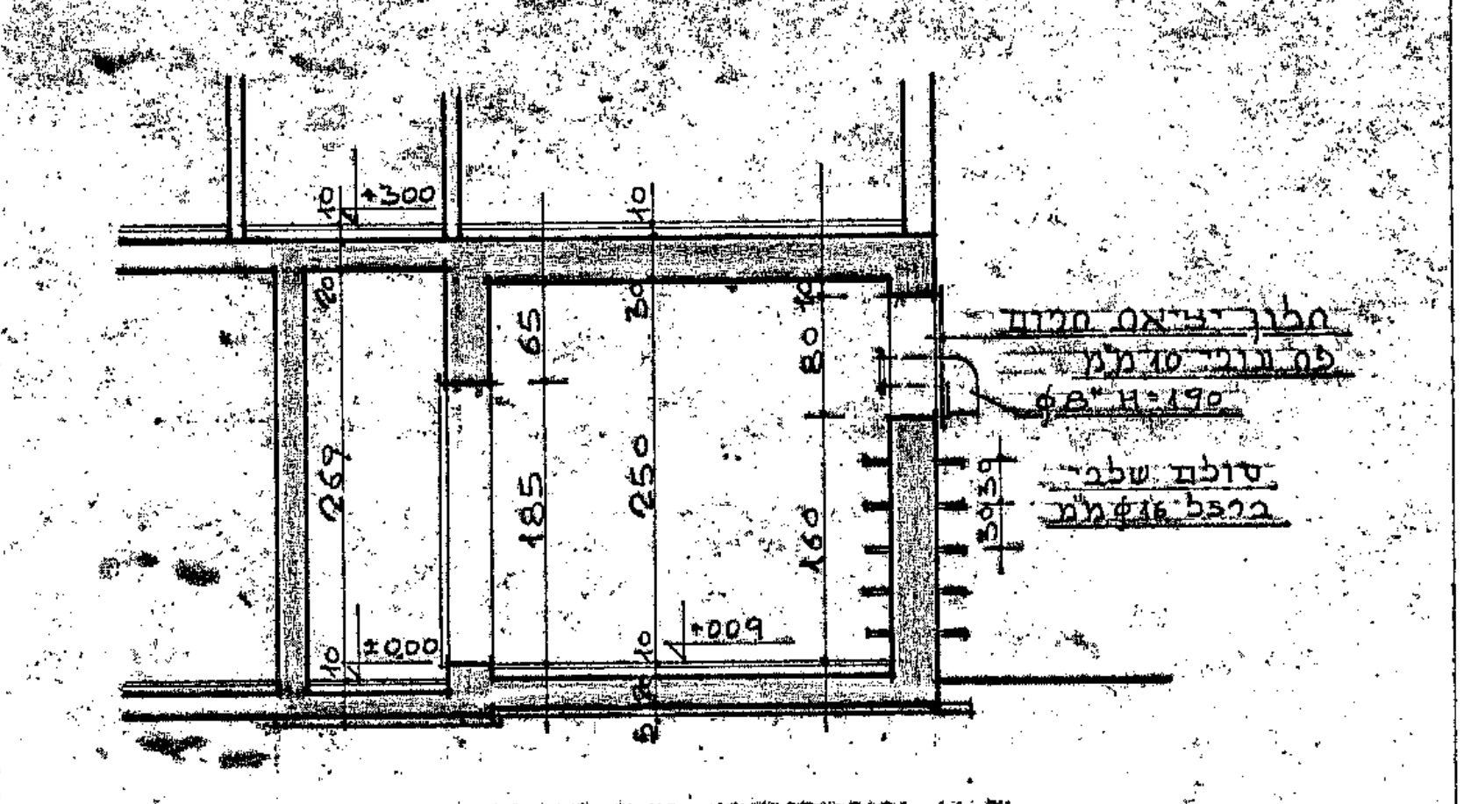

חתך 1-1 1:50

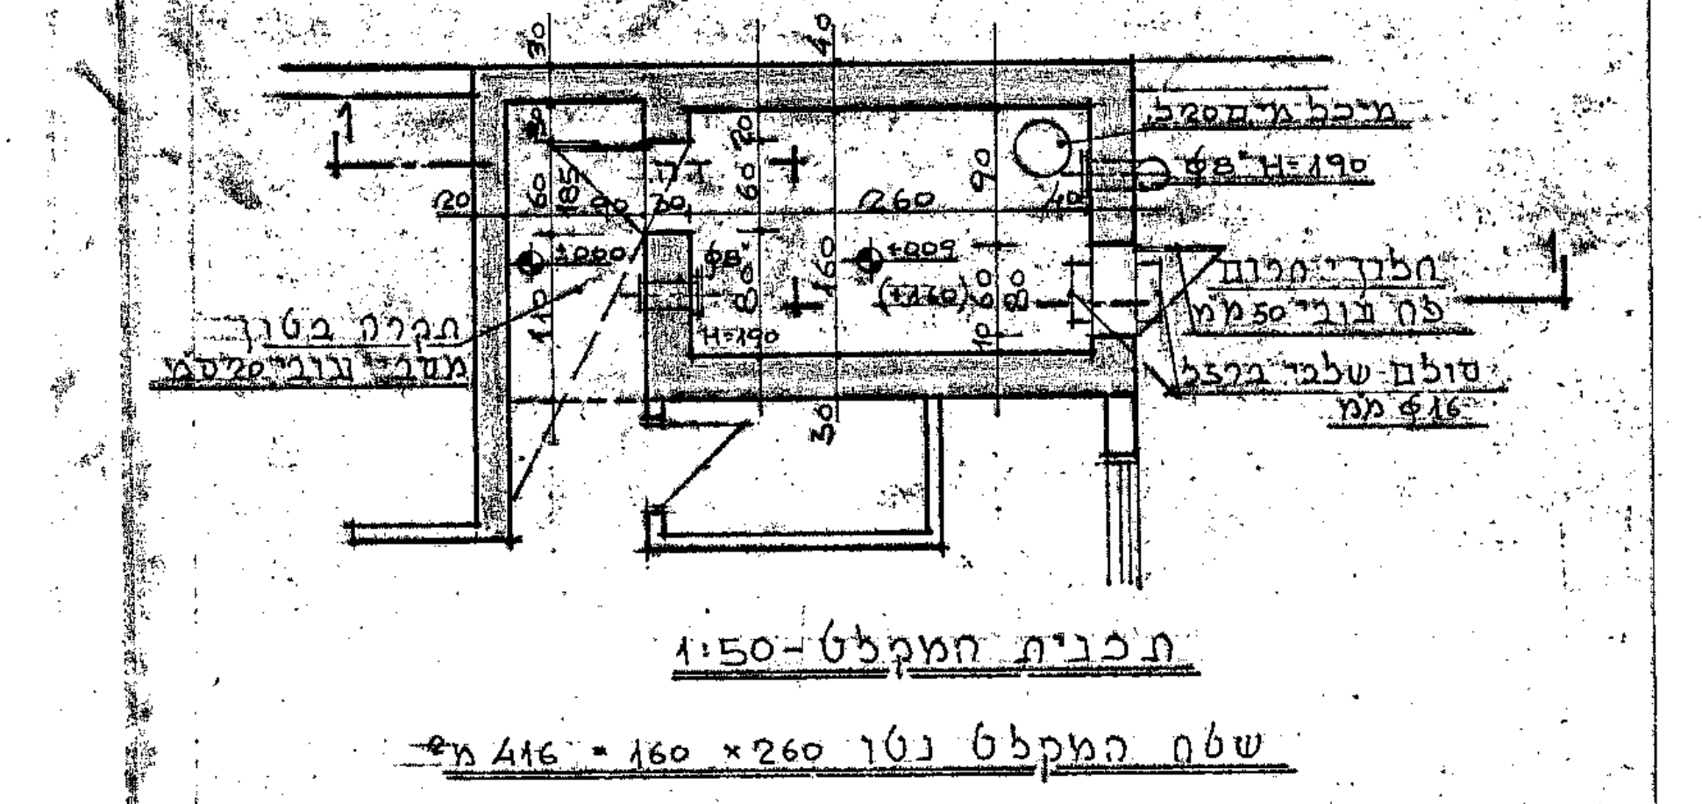

תכנית המקלט 1:50

שטח המקלט נטו 260 × 160 = 4.16 מ"ר

סגלוביץ רח' ששון 27

הוראות ביצוע למקלט

א. ב-150 – תשתית בטון מתחת לרצפה.

ב. בטון המקלט ב-300 לפי תקן ישראלי 118 שנבדק ע"י מכון התקנים או מוסד מוסמך אחר.

ג. פלדת הזיון לפי תקן ישראלי כמפורט במפרט הכללי למקלטים (58).

ד. בידוד הרצפה והקירות יש לבצע בהתאם למפרט הכללי למקלטים, להלן פירוט מערכת ביטומנית, לאחר שהמקלט יבנה בתנאי סביבה רגילה (ללא מי תהום או אדמה חרסית בעלת פלסטיות גבוהה):-

1. רצפה פריימר זפת חם 75/25, שתי שכבות סיבאסט עם שכבת זפת חם 75/25 ביניהם, שכבת זפת חם 75/25 עם נייר טול 4 פליי.
2. קירות חוץ פריימר זפת חם 75/25, ארג זכוכית, זפת חם 75/25, קלקר 2.5 ס"מ.

ה. לא יבוצעו טיח קירות + תקרה או כל ציפוי אחר במקלט ובדרך הגישה אליו.

ו. היציקות יש לבצע בתבניות מדיקטים או לוחות ממתכת בלבד.

על הקבלן/המבקש להזמין את המהנדס האחראי על ביצוע השלד ולקבל אישור לביצוע כל שלבי המקלט, יש להזמין את המפקח מטעם הרשות המקומית לבדיקת שלבי בנית המקלט, על הרשות המקומית להקפיד על מסירה לועדה המקומית תצהיר של האחראי לביצוע השלד בהתאם לקובץ התקנות 3892 מיום 21.9.78 לחוק התכנון והבניה תשכ"ה – 1965 תקנות בדבר תצהיר על הקמת שלד מקלט.