26

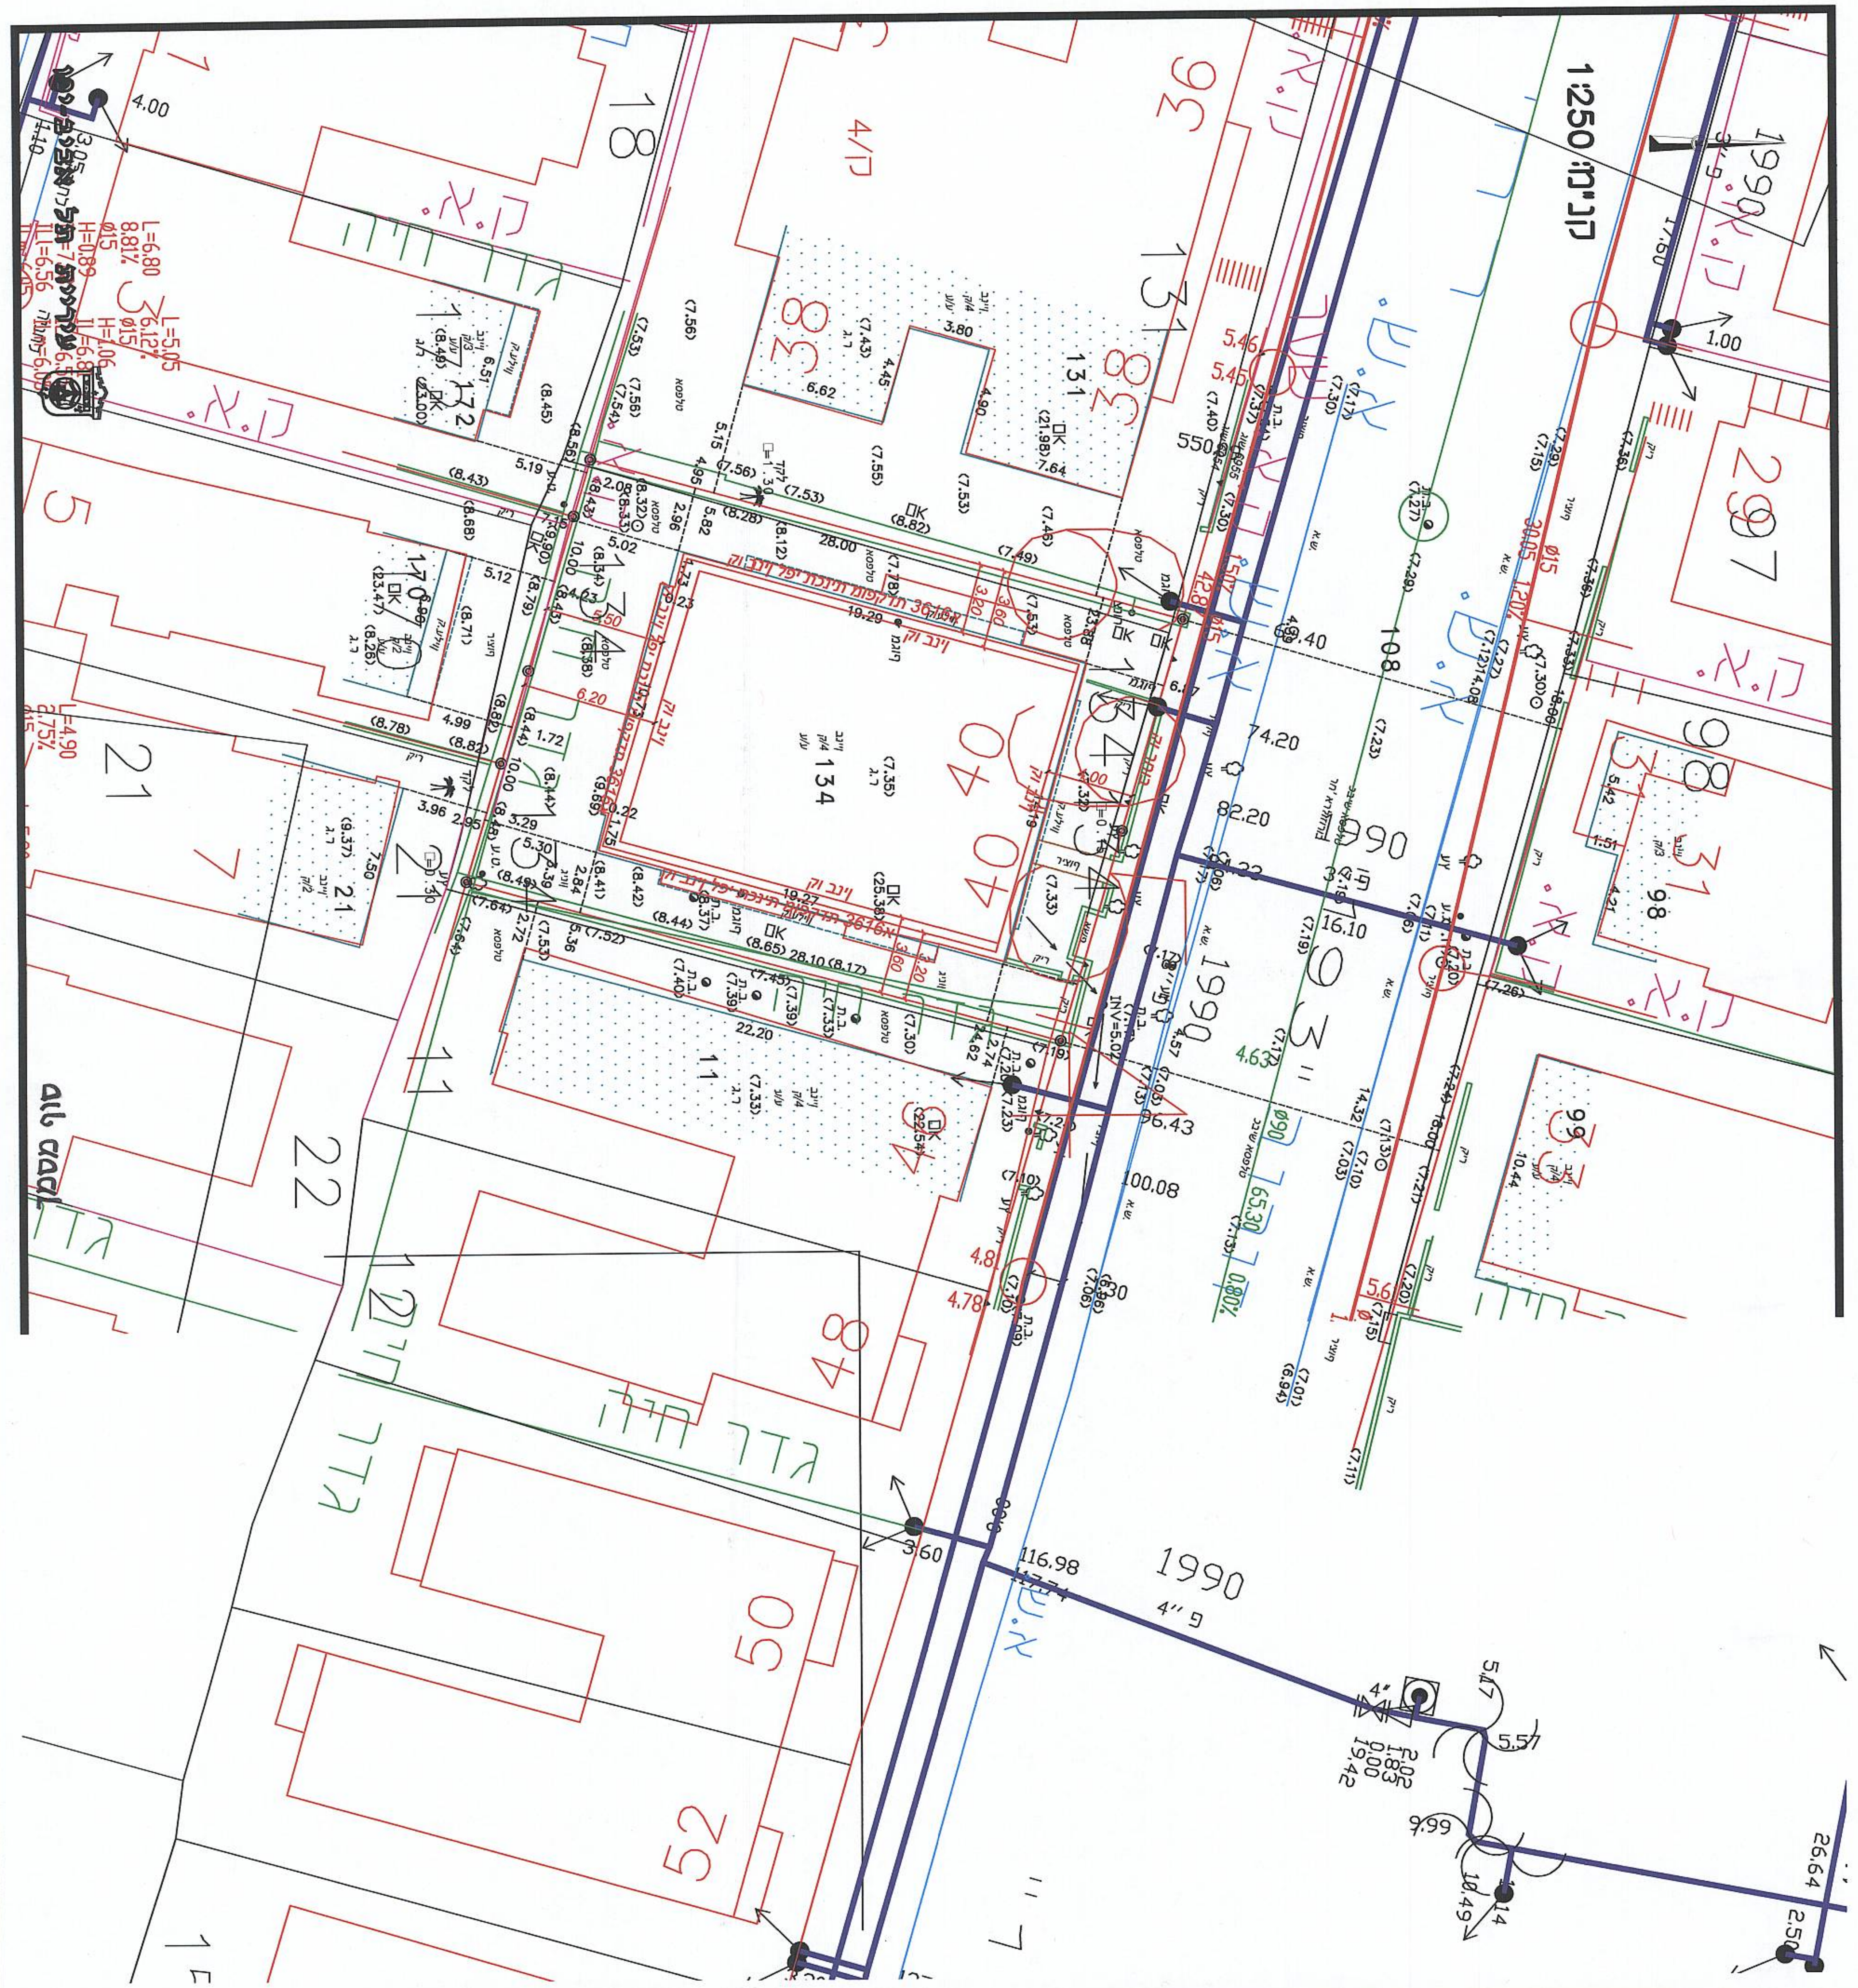

תל אביב

מפה טופוגרפית

מספר סידורי: 2010-77E1

קנה מידה 1:250

גוש: 6135
חלקה: 44 (חלק)
כתובת: רחוב ששון 30
הוכן: עבור אלפרט סרגיי
שם הבעלים כרשום בנסח: טאבו אלפרט סרגיי ת.ז. 317312379.
חיימוב אולג ת.ז. 311006449.
עזרא לילי ליטל ת.ז. 022527212.

מקרא: קווי בניין, קווי בניין, קווי בניין, מים תשתית קיימת, אביזרי מים, כוכי ביוב, חיבור בית-ביוב, ביוב תשתית קיימת, תעול, עמוד תאורה, מאור עילי, מאור עילי, שם רחוב

הערות מחלקת מדידות לגבי קווי הבנין הצדדים
קווי בנין הצדדים עפ"י תב"ע הינם 3.0מ' או0.0מ.'הועדה המקומית תהיה רשאית לאשר קווי בנין לצדדים קטנים מ 2מ'
בהתחשב בגיאומטריה של המגרש המשני ובבניה קיימת ומתוכננת הגובלים בו,
מותנה בפרסום הקלה כחוק

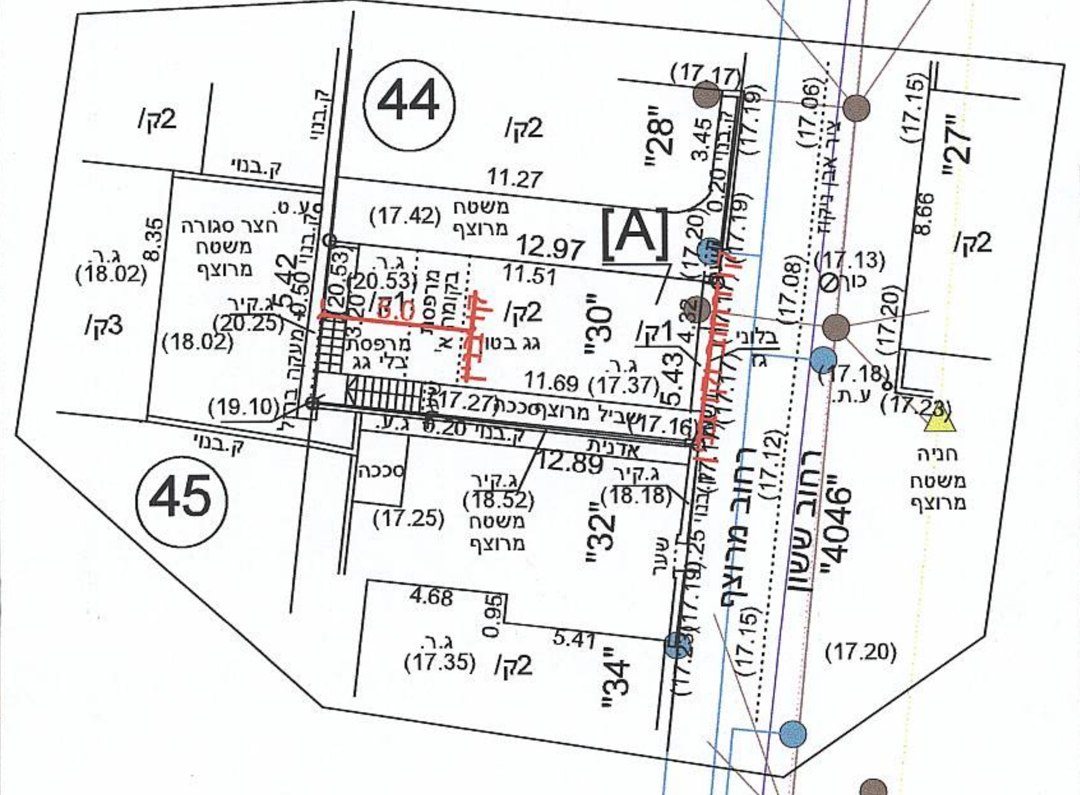

תרשים הסביבה
ק.מ. 1 : 1250

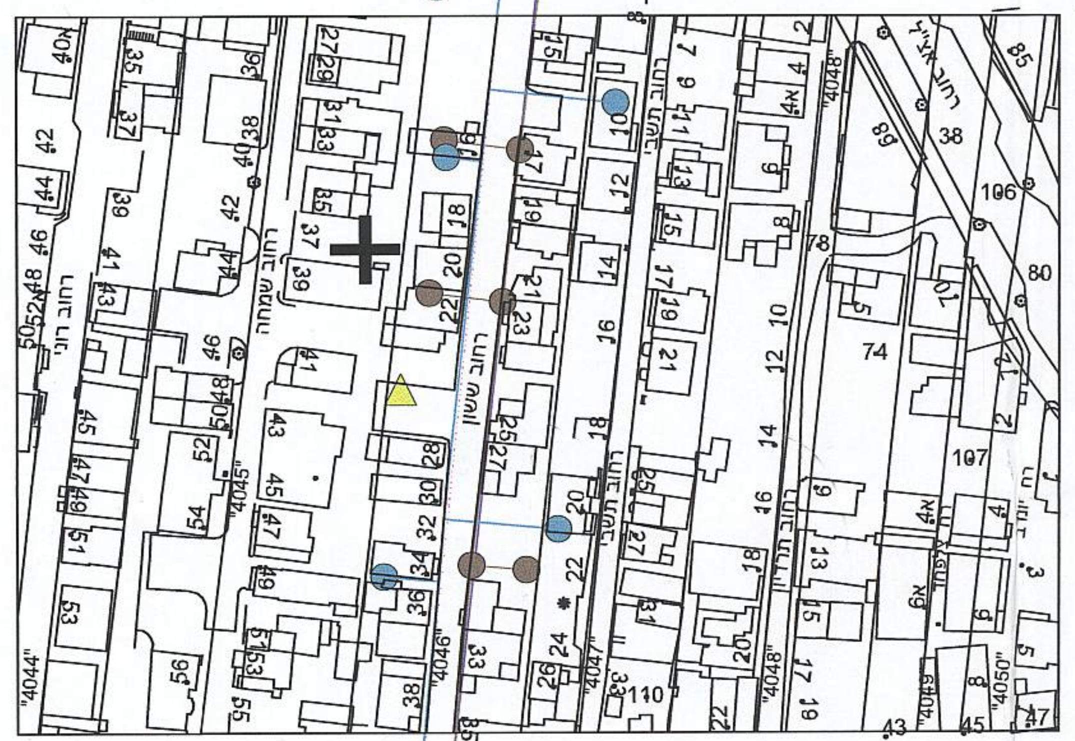

שטח לפי נסח:
שטח החלקה: כולה 11.476 ד"מ
בעלות בחלקים (כרשום בנסח: טאבו)
אלפרט סרגיי (//)24032004 /4711476
חיימוב אולג (//)02702006 /4422952
עזרא לילי ליטל (//)25112008 /62869
בעלות: במ"ר 93
שטח מדוד: (מ"ר) 70
שטח מגרש: משני ד"מ
שטח: להפקעה ד"מ

הנני מצהיר בזה שהמפה נעשתה לפי חוק
התכנון והבניה התקנות וההנחיות
של עירית תל-אביב יפו.

הערות
1. הגבהים קשורים לב. ק 187 של עירית תל אביב
שגובהה 17.550 מ+
2. הגבהים רשומים בסוגריים

חתימה
מ.ר832.

לא לצרכי רישום

המפה עודכנה בתאריך: 10.07.2013
חתימה
מ.ר 832

תאריך: 08.02.2010 MAIL: LLMODED@ZAHAV.NET.IL

ליפמן לאוניד מודד מוסמך. ת.ד9312 . פתח תקווה 49193
טל: 03-9310021, 0522-959820 :פקס0774959820

תאריך הפקת מפה: 10/9/2013

בקשה מספר: 2013-01562 ששון 30 קנ"מ : 1:250