214-466

עיריית תל-אביב-יפו

מינהל ההנדסה, אגף רישוי ופיקוח על הבנייה

שדרות בן-גוריון 68 תל-אביב 64514 (פקס 5231340) טלפון 5217120, 5217045

לכבוד ☐ הוועדה המקומית לתכנון ולבנייה
☒ רשות הרישוי המקומית

24

חוק התכנון והבניה, התשכ"ה-1965
תקנות התכנון והבניה (בקשה להיתר תנאיו ואגרות) (התש"ל-1970)
על פי טופס 1 תקנה 2(א)

בקשה להיתר בנייה או לשימוש במקרקעין

יש להקפיד למלא את כל הפרטים בטופס הבקשה ולצרף מסמכים כמפורט בהוראות התיק המצורפת.

מס' תיק הבניין	מס' בקשה קודמת להיתר בנייה	מס' הבקשה למידע	מתאריך
4046-30			

א. פרטי הנכס והמבקשים

כתובת	רחוב	מס' בית	גוש	חלקה	תת חלקה	מגרש	הוראות התכניות החלות על המגרש
	ששון	30	6135	44			2215

פרטים אישיים	שם משפחה / שם פרטי	מס' זהות/חברה או מס' רישום תאגיד	רחוב ומספר בית / ישוב ומיקוד	מספר טלפון / מספר פקס
מבקש 1	אלפרט סרגיי	317312379	ששון 30	0544929843 ZIVCON7@GMAIL.COM
מבקש 2				
מבקש 3				
בעל הזכות בנכס	אלפרט סרגיי	317312379	ששון 30	0544929843 ZIVCON7@GMAIL.COM
החוכר				
עורך הבקשה הראשי	צבגונסקי אלכס	014687859	שבתאי 17 תל אביב-יפו	0522544457 03 9510030
מתכנן שלד הבניין	צבגונסקי אלכס	014687859	שבתאי 17 תל אביב-יפו	0522544457 03 9510030

ב. מהות הבקשה

☐ בקשה לתוספת בנייה ☐ בקשה להרחבת דיור (במסגרת הרחבת דיור שכונתית)

☐ תוספת ______ קומות לבניין

הכוללות: ☐ ______ יחידות דיור

☐ תוספת בנייה בקומה ______ ☐ לחזית ☐ לאחור ☐ לצד

בשטח של ______ מ"ר

שטח הדירה / המשרד לאחר התוספת יהיה ______ מ"ר

☐ שינויים פנימיים הכוללים ______

☐ אישור מצב קיים: הגבהת גדר קיימת בגבול המגרש האחורי + שיפוץ מדרגות עליה לקומה א' + פרגולה בקומה א' אחור

☒ פרגולה

המקום משמש כיום ל- ______ ☐ בהיתר ☐ בלי היתר

ג. מפרט - תיאור הבקשה

פרט מספר מבנים, גובהם, מקומם, ייעודם וכו': על המגרש קיים בנין 2 קומות 1 יח'

שימוש עיקרי: ☒ מגורים ☐ מלונאות ☐ תעשייה ☐ חקלאי ☐ משרדים ☐ בידור ☐ בניין ציבורי ☐ מלאכה ☐ מסחר ☐ נופש וספורט ☐ שימוש אחר

סוג העבודה והשימושים המוצעים: ☒ תוספת לבניין ☐ הריסה ☐ שינוי בשימוש ☐ שינוי לבניין ☐ תיקונים ☐ ממטרה ______ למטרה ______

הגורם שבמצעות בעבורו הבנייה: ☐ משרד ממשלתי ☐ מוסד ציבורי ☐ בנה ביתך ☐ רשות מקומית ☒ גורם פרטי ☐ אחר:

שטחים	שטח המגרש/החלקה	שטח הבנייה הכולל המבוקש	אחוזי הבנייה
	70 מ"ר	מ"ר	

אם במסגרת הרחבת דיור שכונתית	מספר יחידות דיור מורחבות	מספר תכנית ההרחבה
	1	2215

ד. חומרי הבנייה

סוג הבנייה: ☐ רגילה ☐ בית מכון ☐ מתועשת ☐ אחר

קירות חיצוניים: ☐ בטון מזוין ☐ בלוקים ☐ אבן מבעית ☐ לבנים שרופות ☐ אחר

חומרי גימור: ☐ אבן מלאכותית ☐ אבן טבעית ☐ טיח ☐ זכוכית ☐ אחר

תקרות: ☐ בטון מזוין ☐ עץ ☐ אחר

גג: ☐ בטון מזוין ☐ אסבסט ☐ רעפים ☐ פח ☐ עץ ☐ אחר

גדרות: ☐ אבן טבעית ☐ אבן מלאכותית ☐ בטון ☐ בלוקים ☐ ברזל ☐ רשת ☐ אחר

מקרא חומרים (צבעים): בטון או בטון מזוין ▨ · בלוקים או לבנים סיליקט ▨ · טיח ▨ · אחר ▨ · אבן ▨ · אלומיניום ▨ · זכוכית ▨ · לבנים אדומות ▨ · הריסה ▨ · מתכת ▨ · עץ ▨

ה. השטחים המבוקשים לבנייה

הקומה/המפלס בבניין	שטחי השימוש העיקריים	שטחי השירות	סך כל שטחי הבנייה	שטחים לא מקורים
ק א +3.16		2215		פרגולה 7.64

אין תוספת שטח

י. הצהרת עורך הבקשה הראשי

תאריך 29.2.14 שם צבגונסקי חתימה

יא. חתימות נוספות

	תאריך	שם
המבקש	12.2013	
בעל הזכות בנכס	12.2013	
החוכר	20.02.13	
מתכנן שלד הבניין	12.2013	צבגונסקי

ט. הבקשה מוגשת לאישור

☐ הוועדה המקומית

יג. הצהרות

הצהרת מתכנן שלד הבניין: אני החתום מטה צבגונסקי מהנדס רשוי מס' 15320 ... ת.ז. 014687859 ... תאריך 12.2013

ז. קווי בנייה · ח. מספר יחידות דיור · ו. פרטי הבנייה - לשימוש הלשכה המרכזית לסטטיסטיקה

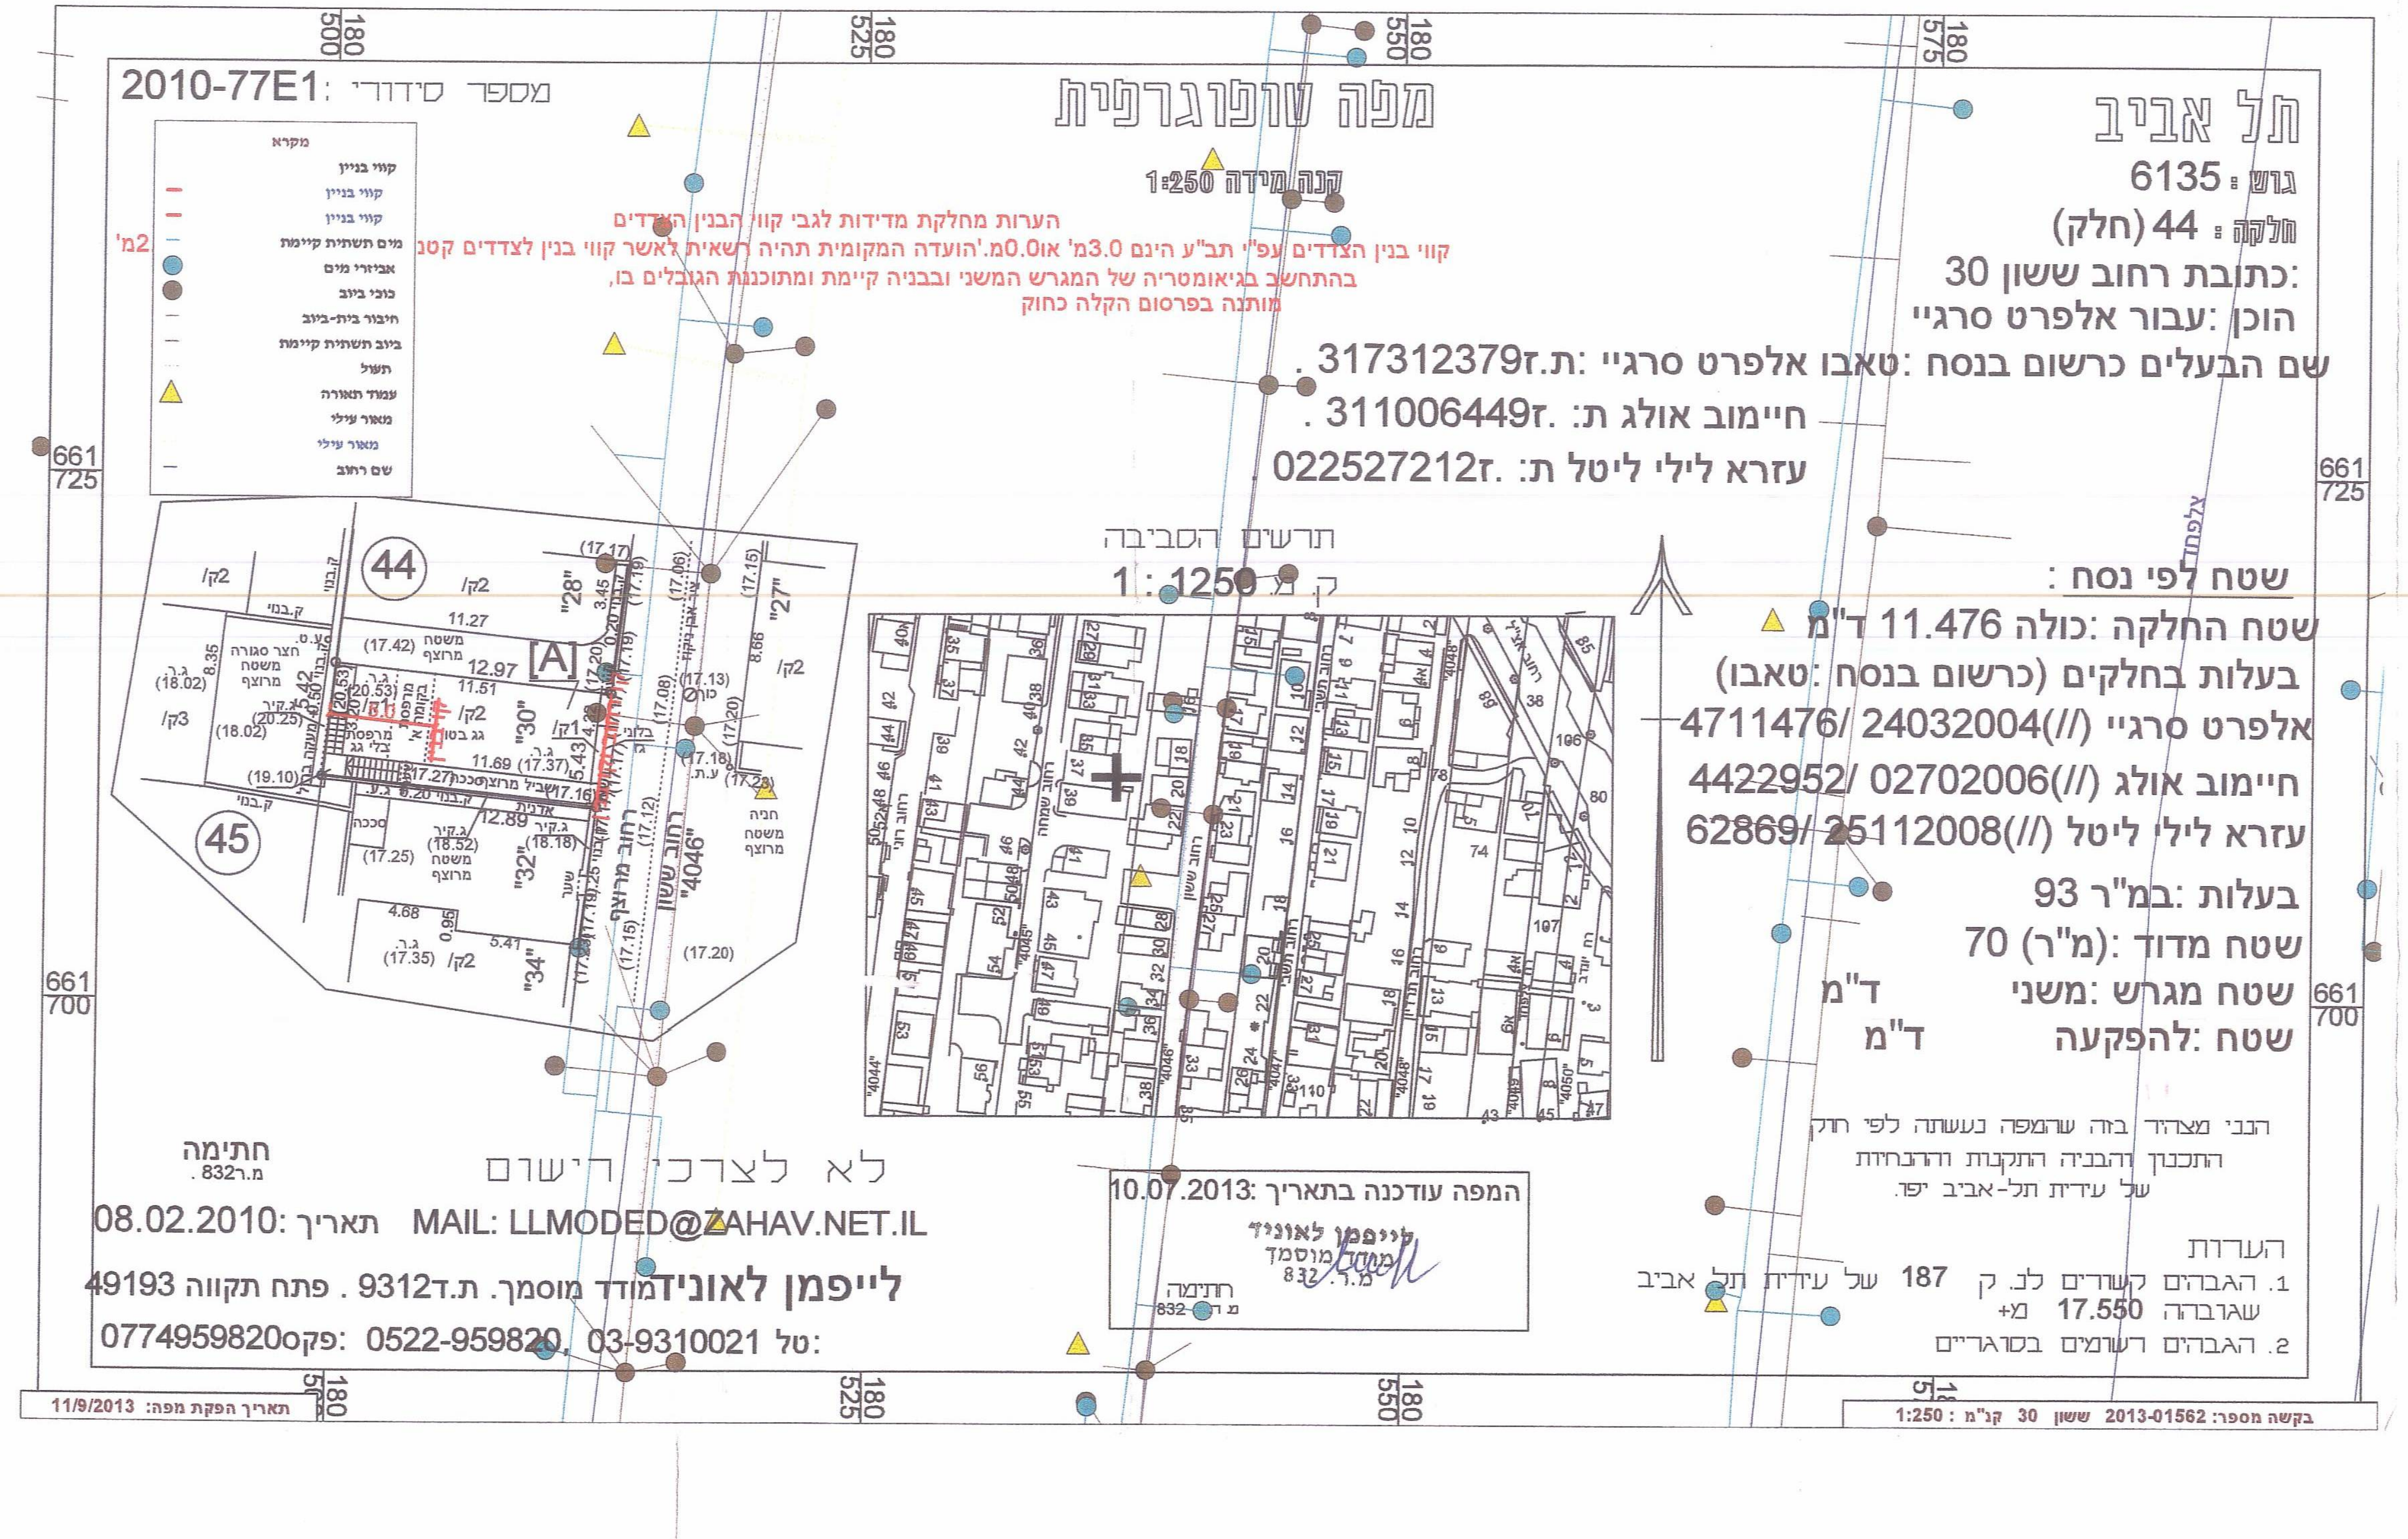

תל אביב

גוש: 6135
חלקה: 44 (חלק)
כתובת: רחוב ששון 30
הוכן: עבור אלפרט סרגיי
שם הבעלים כרשום בנסח: טאבו אלפרט סרגיי ת.ז. 317312379
חיימוב אולג ת.ז. 311006449
עזרא לילי ליטל ת.ז. 022527212

מפה טופוגרפית

קנה מידה 1:250

מספר סידורי: 2010-77E1

הערות מחלקת מדידות לגבי קווי הבנין הצדדים
קווי בנין הצדדים עפ"י תב"ע הינם 3.0מ' או 0.0מ'. הועדה המקומית תהיה רשאית לאשר קווי בנין לצדדים קטנ
בהתחשב בגיאומטריה של המגרש המשני ובבניה קיימת ומתוכננת הגובלים בו,
מותנה בפרסום הקלה כחוק

תרשים הסביבה
ק.מ 1:1250

שטח לפי נסח:
שטח החלקה: כולה 11.476 ד"מ
בעלות בחלקים (כרשום בנסח: טאבו)
אלפרט סרגיי (//) 24032004/ 4711476
חיימוב אולג (//) 02702006/ 4422952
עזרא לילי ליטל (//) 25112008/ 62869
בעלות: במ"ר 93
שטח מדוד: (מ"ר) 70
שטח מגרש: משני ד"מ
שטח: להפקעה ד"מ

הנני מצהיר בזה שהמפה נעשתה לפי חוק התכנון והבניה התקנות וההנחיות של עירית תל-אביב יפו.

הערות
1. הגבהים קשורים לב. ק 187 של עירית תל אביב שגובהה 17.550 מ+
2. הגבהים רשומים בסוגריים

לא לצרכי רישום

חתימה
מ.ר 832

תאריך: 08.02.2010 MAIL: LLMODED@ZAHAV.NET.IL

לייפמן לאוניד מודד מוסמך. ת.ד 9312. פתח תקווה 49193

טל: 03-9310021, 0522-959820 פקס: 0774959820

המפה עודכנה בתאריך: 10.07.2013
לייפמן לאוניד מודד מוסמך מ.ר. 832
חתימה

תאריך הפקת מפה: 11/9/2013

בקשה מספר: 2013-01562 ששון 30 קנ"מ: 1:250

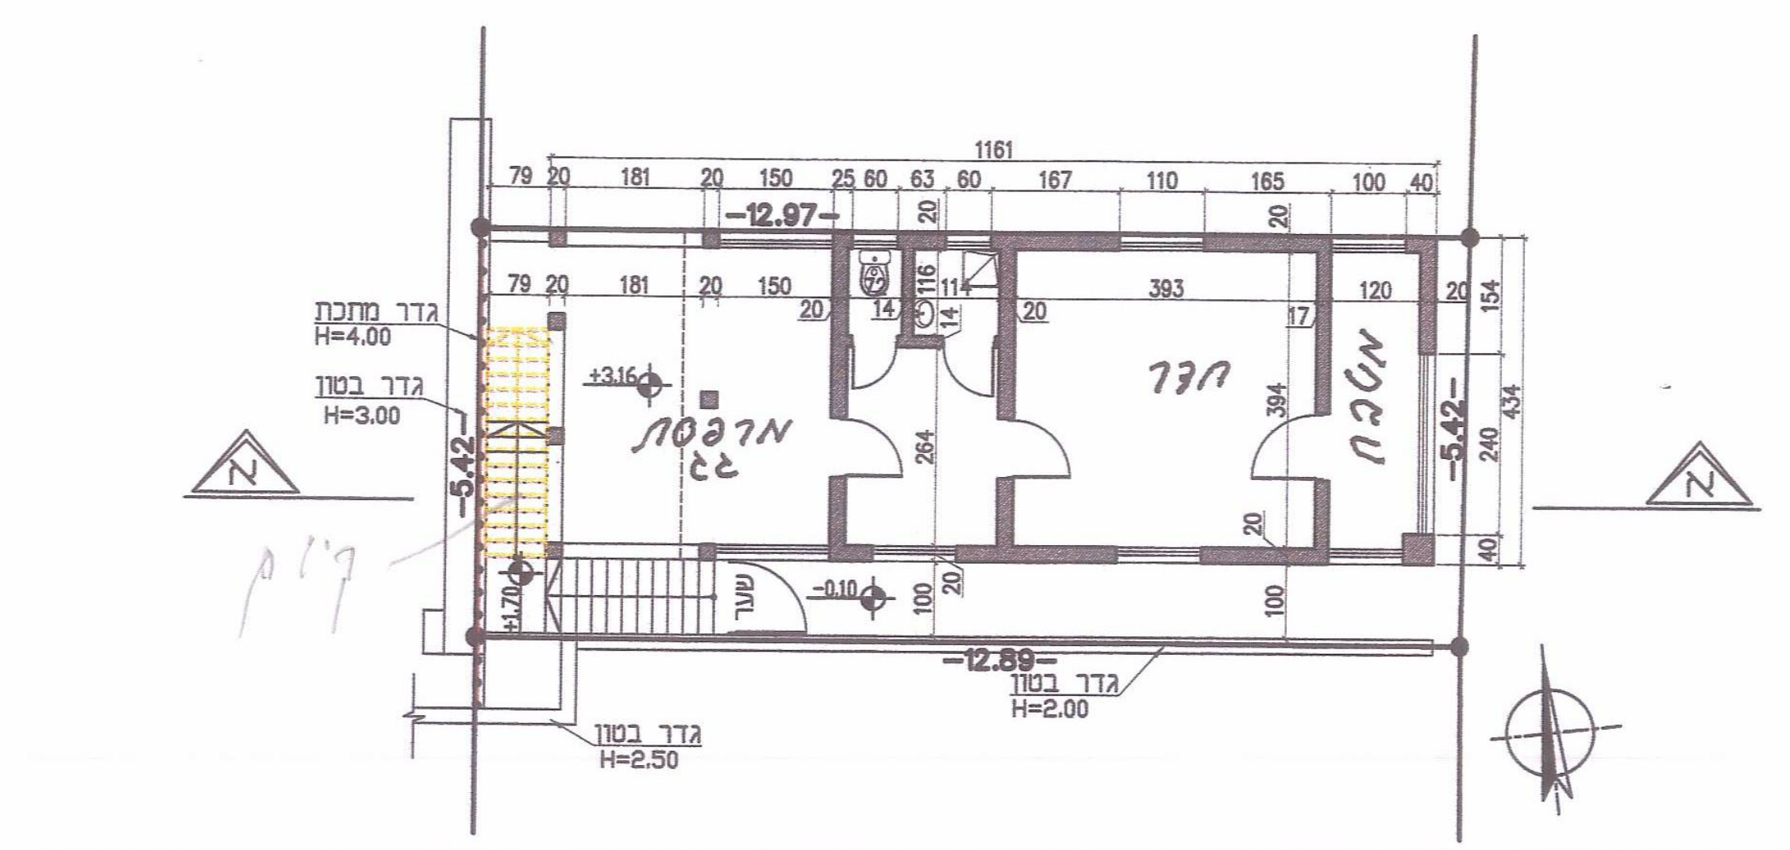

תוכנית קומה א - ק.מ. 1:100

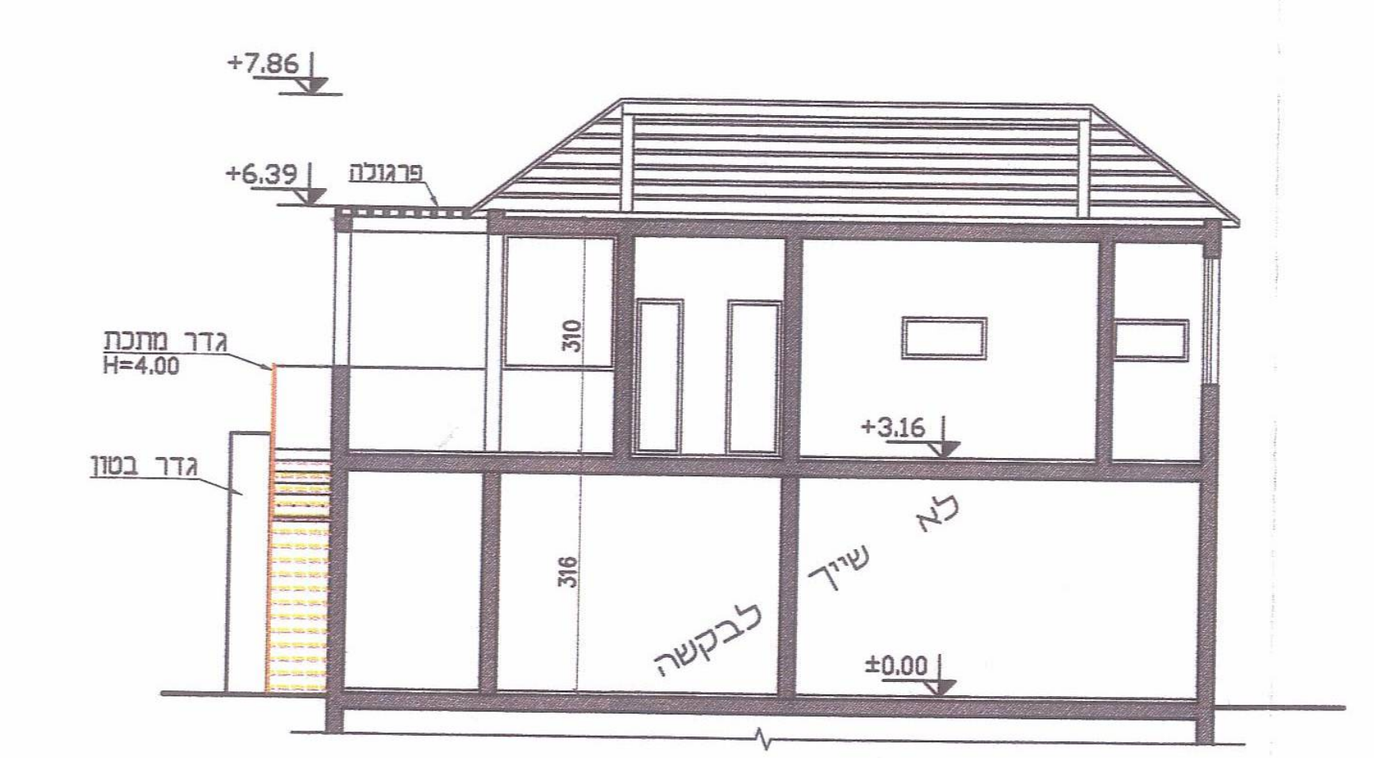

חתך א-א - ק.מ. 1:100

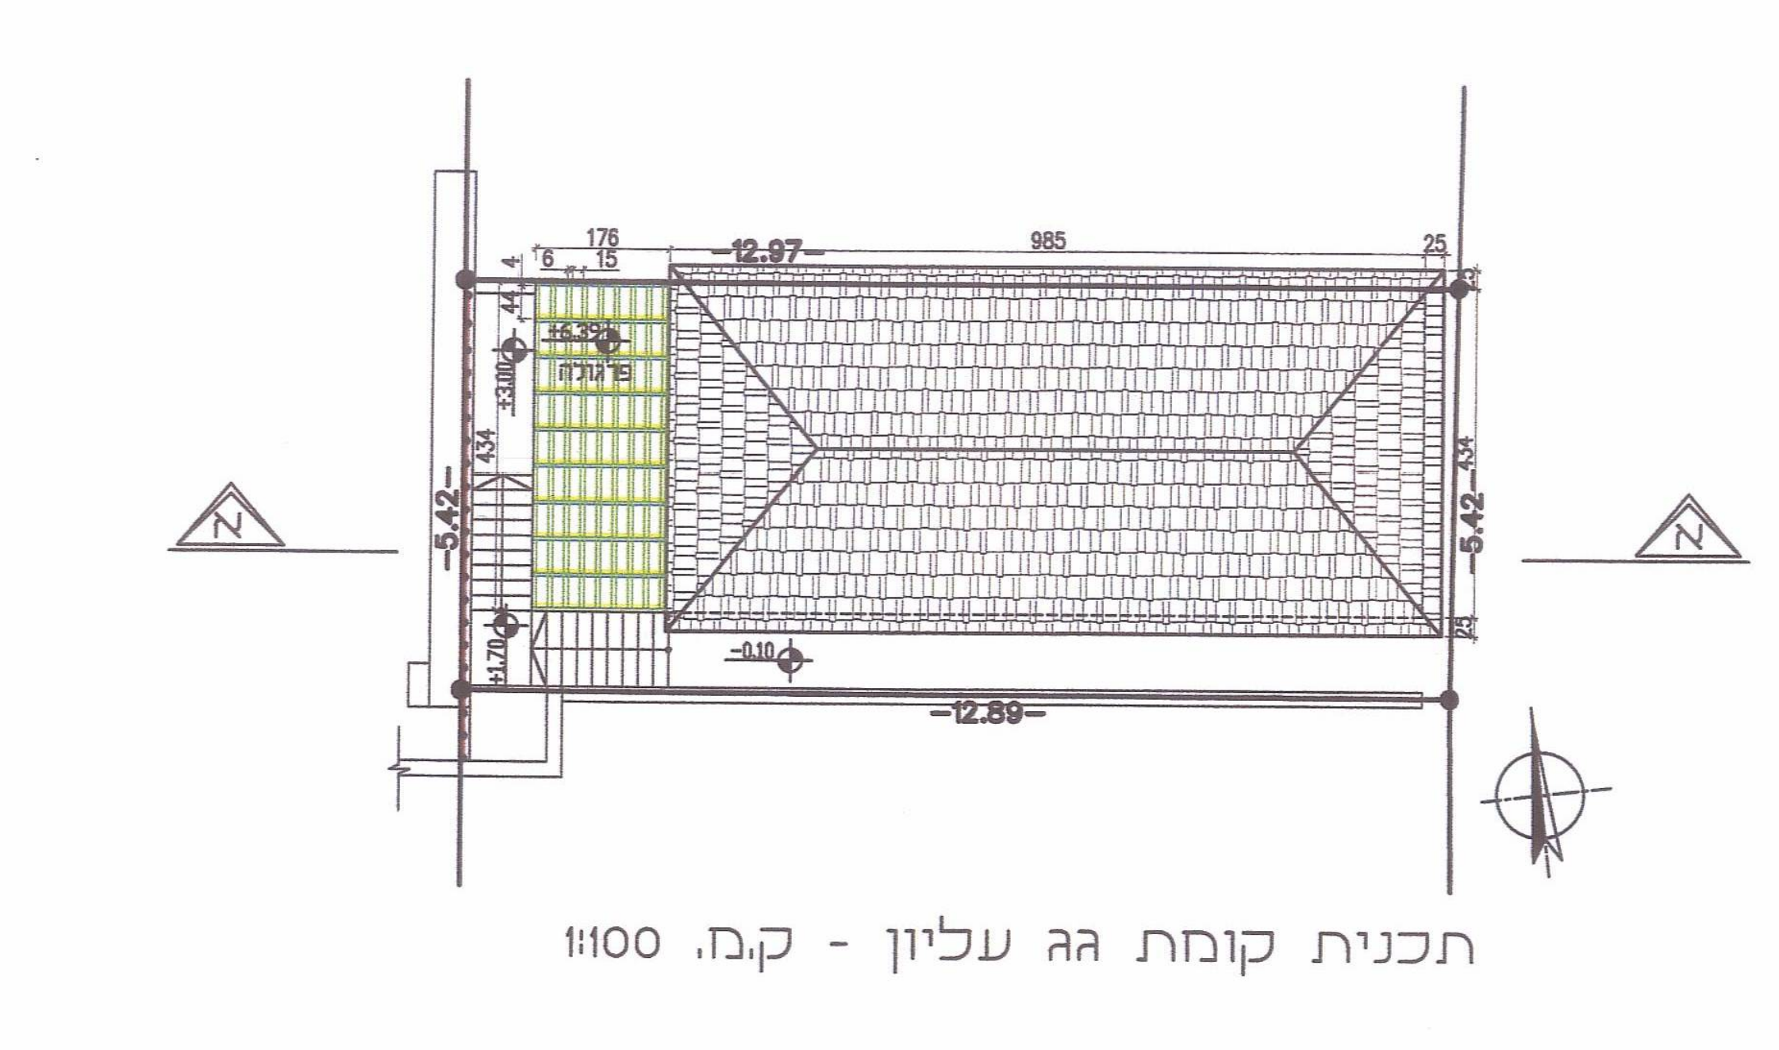

תכנית קומת גג עליון - ק.מ. 1:100

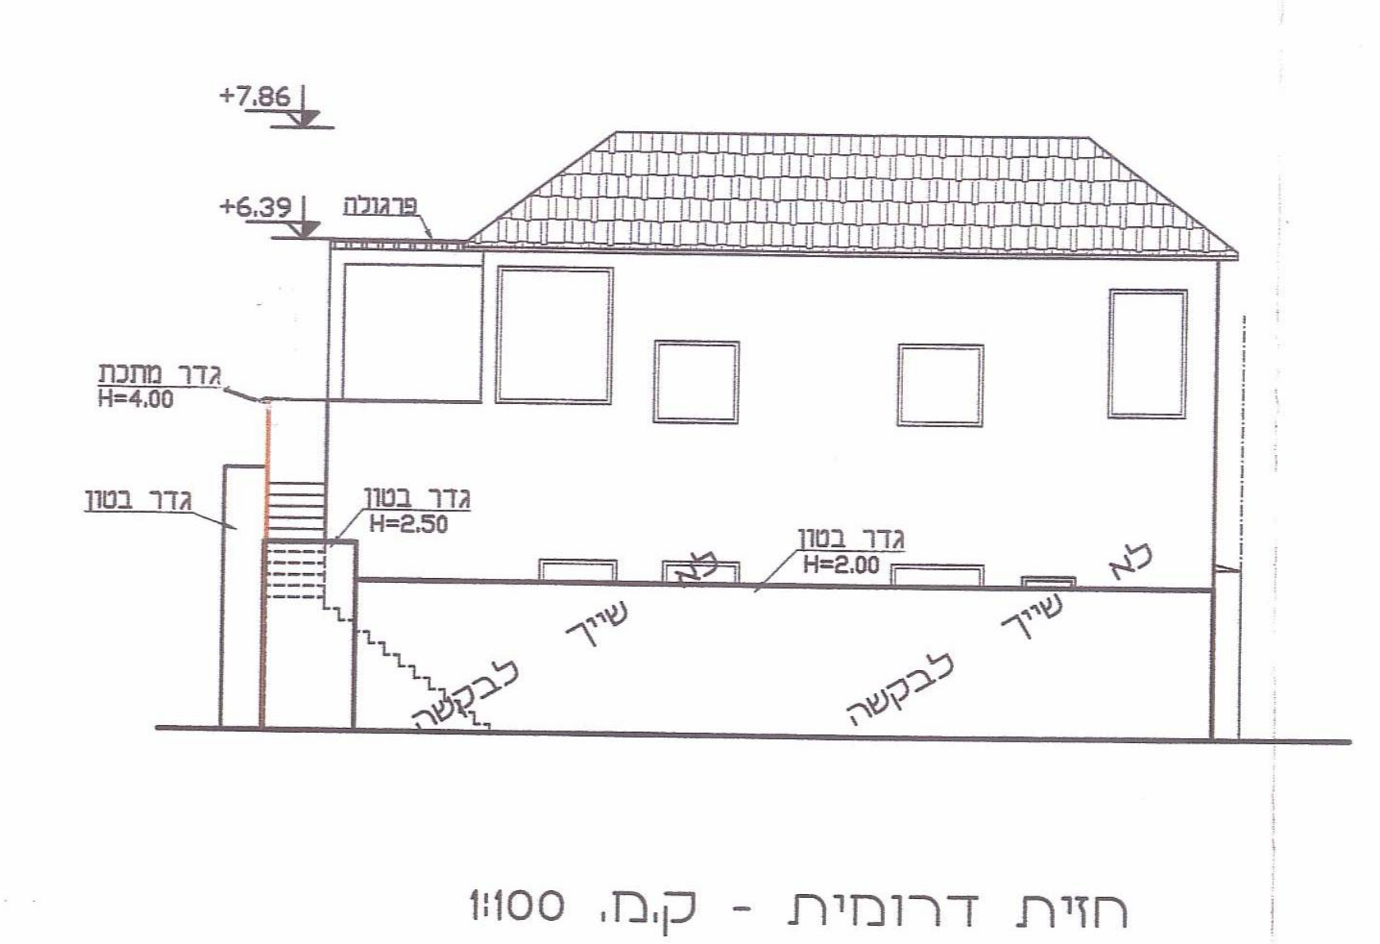

חזית דרומית - ק.מ. 1:100

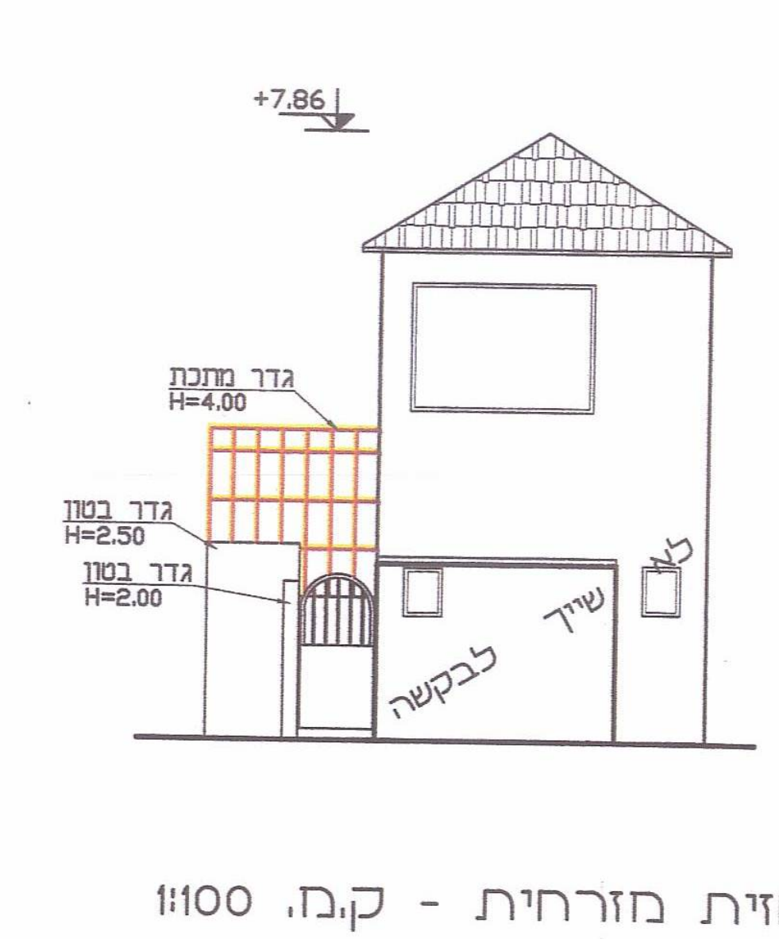

חזית מזרחית - ק.מ. 1:100

02/03/2014

סיכום בדיקה תחנה פיקוח בניה בקשה 20140466 לכתובת ששון 30

החלטת תחנה מ-02/03/2014 : תוכנית תואמת את המצב בשטח

תוכנית תואמת את המצב בשטח המבוקש בנוי חלקית:

טרם נבנה פרגולה. קיים משפט על בנית מדרגות.
בדק ארקדי צימבליסטי.

מטפל: אלי פארי

חישוב שטחים

חישוב שטח פרגולה :

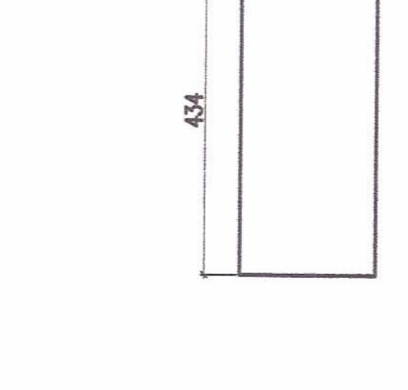

שטח	מס'	חישובים	סה"כ מ"ר
פרגולה		1.76 x 4.34	7.64