14-0466

4046-030

20

עיריית תל-אביב-יפו מח' רישוי בניה - צוות יפו 19-05-2014

אני מצהיר בזה שכל דרישות הוועדה מולאו והוגשו כל האישורים שנדרשו במסגרת תיאום התכנון

חתימה

עיריית תל-אביב-יפו

מינהל ההנדסה, אגף רישוי ופיקוח על הבנייה

שדרות בן-גוריון 68 תל-אביב 64514 טלפון 5217120, 5217045 (פקס 5231340)

חוק התכנון והבנייה, התשכ"ה-1965

תקנות התכנון והבנייה (בקשה להיתר, תנאיו ואגרות) התש"ל-1970

טופס 1 על פי תקנה 2(א)

לכבוד ☐ הוועדה המקומית לתכנון ולבנייה

☒ רשות הרישוי המקומית

בקשה להיתר בנייה או לשימוש במקרקעין

יש להקפיד למלא את כל הפרטים בטופס הבקשה ולצרף מסמכים כמפורט ברשימת התיוג המצורפת.

מס' תיק הבניין	מס' בקשה קודמת להיתר בנייה	מס' הבקשה למידע	מתאריך
4046-30			

א. פרטי הנכס והמבקשים

הכתובת	רחוב	מס' בית	גוש	חלקה	תת חלקה	מגרש	הוראות התכנית החלות על המקום
	ששון	30	6135	44			2215

פרטים אישיים	שם משפחה	שם פרטי / שם חברה או תאגיד	מס' זהות/חברה או מס' רישום תאגיד	רחוב ומספר בית / ישוב ומיקוד	מספר טלפון / מספר פקס
מבקש 1	אלפרט	סרגיי	317312379	ששון 30	0544929843 ZIVCON7@GMAIL.COM
מבקש 2					
מבקש 3					
בעל הזכות בנכס	אלפרט	סרגיי	317312379	ששון 30	0544929843 ZIVCON7@GMAIL.COM
החוכר					
עורך הבקשה הראשי	ז'יבגורסקי	אולגה	014687859	שבתאי 17 תל אביב-יפו	0522544457 03 9510030
מתכנן שלד הבניין	ז'יבגורסקי	אולגה	014687859	שבתאי 17 תל אביב-יפו	0522544457 03 9510030

ב. מהות הבקשה

☐ בקשה לתוספת בנייה ☐ בקשה להרחבת דיור (במסגרת הרחבת דיור שכונתית)

☐ תוספת ____ קומות לבניין

הכוללות: ☐ ____ יחידות דיור ☐ ____

☐ תוספת בנייה בקומה ____ ☐ לחזית ☐ לאחור ☐ לצד

בשטח של ____ מ"ר

שטח הדירה / המשרד לאחר התוספת יהיה ____ מ"ר

☐ שינויים פנימיים הכוללים: ____

☐ אישור מצב קיים הגבהת גדר קיימת בגבול המגרש האחורי + שיפוץ מדרגות עליה לקומה א'

☒ פרגולה

המקום משמש כיום ל- + פרגולה בקומה א' מאחור

☐ בהיתר ☐ בלי היתר

ג. מפרט - תיאור הבקשה

תיאור הקיים על המגרש: על המגרש קיים בנין 2 קומות 2 יח'

שימוש עיקרי: ☒ מגורים ☐ משרדים ☐ מסחר ☐ מלונאות ☐ בידור ☐ נופש וספורט ☐ תעשיה ☐ בנין ציבורי ☐ שימוש אחר ☐ חקלאי ☐ מלאכה

סוג העבודה או השימושים המוצעים: ☒ תוספת לבניין ☐ שינוי לבניין ☐ הריסה ☐ תיקונים ☐ שינוי בשימוש ממטרה ____ למטרה ____

הגורם שמבצעת בעבורו הבנייה: ☐ משרד ממשלתי ☐ רשות מקומית ☐ מוסד ציבורי ☒ גורם פרטי ☐ בנה ביתך ☐ אחר: ____

שטחים: שטח המגרש/החלקה ____ שטח הבנייה הכולל המבוקש 70 מ"ר אחוזי הבנייה ____

אם במסגרת הרחבת דיור שכונתית: מספר יחידות דיור מורחבות 1 מספר תכנית ההרחבה 2215

ד. חומרי הבנייה

סוג הבנייה: ☐ רגילה ☐ בית מוכן ☐ מתועשת ☐ אחר

קירות חיצוניים: ☐ בטון מזוין ☐ בלוקים ☐ אבן טבעית ☐ לבנים שרופות ☐ אחר

חומרי גימור: ☐ אבן טבעית ☐ אבן מלאכותית ☐ טיח ☐ זכוכית ☐ אחר

תקרות: ☐ בטון מזוין ☐ עץ ☐ אחר

גג: ☐ בטון מזוין ☐ רעפים ☐ טיח ☐ אסבסט ☐ אחר

גדרות: ☐ אבן טבעית ☐ אבן מלאכותית ☐ בטון ☐ בלוקים ☐ ברזל ☐ עץ ☐ רשת ☐ אחר

קיימות ____ מ"א מוצעות ____ מ"א סה"כ ____ מ"א

מקרא חומרים (צבעים): בטון או בטון מזוין 🟦 · בלוקים או לבנים מבטון 🟥 · סיליקט או לבנים אדומות ☐ · אבן ☐ · עץ 🟩 · איטונג ☐ · זכוכית ☐ · הריסה 🟨 · אחר ☐ · מתכת 🟫

ה. השטחים המבוקשים לבנייה (על-פי תכנית הבנייה) והמותרים לבנייה (על-פי "אסמכתא": חוק, תקנות, תכנית) בכל מפלס בנפרד ולפי שימוש

הקומה/המפלס בבניין	(א) שטחי השימוש העיקריים: קיים בהיתר	קיים ללא היתר ומבוקש לאשר בדיעבד	בנייה חדשה מוצעת	מותר	ה"אסמכתא" לשטחים המותרים לשימושים העיקריים ולשטחי השירות	(ב) שטחי השירות	(ג) סך כל שטחי הבניין	משטחים לא מקורים
ק. N +3.16		42.79			2215			פרגולה 7.64
ס"ה מעל לקרקע								
ס"ה מתחת לקרקע								
סה"כ								

אין תוספת שטח

האגף לתכנון מבנים ומפעלות מינהל הכספים עיריית תל-אביב-יפו מח' שומה והשבחה

ו. פרטי הבנייה - לשימוש הלשכה המרכזית לסטטיסטיקה

הייעוד	שטח הבנייה ברוטו - לפי ייעוד	גודל הדירות לפי מספר חדרים
למגורים 1		
לאירוח 2		
לעסקים ולמסחרים 3		
לבנייני ציבור 4		
לתעשייה ולמלאכה 5		
למשק חקלאי 6		
למקלט או למחסן		
למבני עזר		
סך כל שטח הבנייה		סה"כ

מספר היתר הבנייה · תאריך היתר הבנייה · תאריך התחלת הבנייה · תאריך גמר הבנייה (שנה, חודש)

מספר הקומות כולל קומת עמודים מפולשת

ז. קווי בנייה

הכיוון	מוצע	מותר	קווי בניה (במטר) הסטייה במטר	ב-%
לרחוב (שם)				
לרחוב (שם)				
לצד				
לאחור				

ח. מספר יחידות דיור

אם השימוש המבוקש הוא מגורים - רשום להלן: מספר הדירות הקיימות ____ מספר הדירות המבוקשות ____ מספר הדירות המותרות ____

ט. הבקשה מוגשת לאישור

☐ הוועדה המקומית

הבקשה כוללת בקשה להקלה - כלהלן:

פירוט הבקשה להקלה	נימוקי הבקשה להקלה
1.	
2.	
3.	

☐ רשות הרישוי המקומית

☐ רשות הרישוי המקומית באמצעות מורשה להיתר

י. הצהרת עורך הבקשה הראשי

אני מצהיר על נכונות הפרטים בסעיפים א עד ט.

תאריך 05.2014 שם ז'יבגורסקי חתימה

יא. חתימות נוספות

המבקש: תאריך 05.2014 שם אלפרט סרגיי חתימה

בעל הזכות בנכס/בעל הנכס/החוכר: תאריך 05.2014 שם אלפרט סרגיי חתימה

מתכנן שלד הבניין: תאריך 05.2014 שם ז'יבגורסקי חתימה

שימוש משרד: הערות · התוכנית תואמת את המצב בשטח ☐ כן ☐ לא · הוכן דוח לתביעה משפטית · הוגשה תביעה משפטית · הוגשה תביעה חוזרת · מס' הדוח/התביעה · תאריך הדוח/התביעה · הנדון בדוח / הנדון בתביעה · הערות · תאריך · שם · חתימה

יב. מינויים מטעם מבקש ההיתר - נתמנה אדם אחד ליותר מתפקיד אחד, ימולאו פרטיו ליד כל אחד מהתפקידים שהוא ממלא על פי הוראות כל דין.

מינוי עורך הבקשה הראשי: אני ממנה בזה את ____ בעל/ת מס' זהות ____ הרשום בסעיף א' להיות עורך הבקשה הראשי להיתר, ולייצגני לפני מוסדות התכנון והרשויות המוסמכות בכל הנוגע לטיפול בבקשה להיתר ולקבלתו, לרבות התיקונים ככל שידרש הרשויות המוסמכות.

מינוי עורכי בקשה לפי תחומים: אני ממנה בזה את הרשומים להלן להיות עורכי הבקשה להיתר בתחום הפעולה כרשום לצד שמם, ולייצגני בתחום פעולתם לפני מוסדות התכנון והרשויות המוסמכות בכל הנוגע לטיפול בבקשה להיתר ולקבלתו, לרבות התיקונים ככל שידרשו הרשויות המוסמכות.

שם משפחה ושם פרטי	תחום פעולה	המען	מספר טלפון	מספר פקס
1.	מתכנן האינסטלציה הסניטרית			
2.				

מינוי מתכנן שלד הבניין: אני ממנה בזה את ____ בעל/ת מס' זהות ____ הרשום בסע' א' להיות אחראי לתכנון שלד הבנין שבעבורו מבקש ההיתר, להגיש לוועדה לרשות הרישוי המקומית את החישובים לגבי הבניה שבעבורה מבקש היתר ולפקח פיקוח עליון על הקמת השלד.

מינוי הקבלן האחראי לבנייה: ☐ אני ממנה בזה את ____ בעל/ת מס' זהות ____ ובעל תעודת רישום בפנקס הקבלנים מספר ____ במדור ____ ובעל ____ לביצוע עבודה בהיקף עד ____ לבצע את העבודה הנדונה בהיתר כמתחייב לפי כל דין.

☐ אני מצהיר, כי טרם מסרתי את ביצוע העבודה הנדונה בהיתר לידי קבלן, ומתחייב כי אמסור אותה לידי קבלן רשום בפנקס הקבלנים, כמתחייב על פי כל דין, והודיע על כך לרשות הרישוי המקומית טרם התחלת ביצוע העבודה, וחתימתו של הקבלן תצורף להודעה המפרטת את פרטי רישומו של הקבלן.

מינוי האחראי לביצוע שלד הבניין: ☐ אני ממנה בזה את ____ בעל/ת מס' זהות ____ כתובת ____ טלפון ____ פקס ____ הרשום לעיל להיות אחראי לביצוע שלד ____.

☐ אני מצהיר, כי טרם מיניתי אחראי/ת לביצוע עבודות בתחומים האלה: ____ ומתחייב לעשות זאת כמפורט בתקנות, ולהודיע על כך לרשות הרישוי המקומית טרם התחלת ביצוע העבודה.

מינוי אחראים לביקורת: ☐ אני ממנה בזה את הרשומים להלן להיות אחראים לביקורת על ביצוע עבודות בתחום הפעולה כרשום ליד שמם.

שם משפחה ושם פרטי	תחום פעולה	המען	מספר טלפון	מספר פקס
1.	אחראי ראשי			
2.				
3.				

☐ אני מצהיר כי טרם מיניתי אחראי/ם לביקורת על ביצוע עבודות את כולם או את קצתם בתחומים האלה: ____ ומתחייב לעשות זאת כמפורט בתקנות, ולהודיע על כך לרשות הרישוי המקומית טרם התחלת ביצוע העבודה.

X ____ חתימת המבקש על המינויים X

יג. הצהרות

הצהרת עורכי הבקשה: אנו החתומים מטה מצהירים בזה:

1) כל אחד מאיתנו מאשר שהאמור בנוגע לו ברשימה שבסעיף ? לעיל הוא נכון.
2) כל אחד מאיתנו מסכים לקבל עליו את התפקיד המיועד לו בסעיף ? לעיל.
3) אנו מצהירים, כל אחד בנוגע לתחום פעולתו, שיש לנו כישורים מקצועיים לערוך בקשה זו וכי בדקנו את המסמכים הנוגעים לבקשה, לרבות כל תכנית הנוגעת לבקשה, וידוע לנו כי אם הצהרה זו אינה נכונה, הרי היא תיחשב מסירת ידיעה שהיא כוזבת או מטעה בפרט חשוב, כמשמעותה בסעיף 214 לחוק, וצפויים לנו העונשים הקבועים לפי כל דין.

אני ____ (עורך בקשה ראשי) אחראי/ת לכך שהבקשה, ובכלל זה נספחיה, נערכה לפי מיטב הידיעה המקצועית ובהתאם לכל חיקוק החל על ____ או העבודה המוצעת, שכל הנתונים שנמסרו על ידי בבקשה זו נכונים ושהתכנון המוצע תואם את כל התכניות, פרט לסטיות שפורטו לעיל.

☐ אני עורך הבקשה מתכנן האינסטלציה הסניטרית, מצהיר בזאת ואחראי לכך שתכניות הבקשה בכל הנוגע לסידורים הסניטריים נערכו כדין וכי קיימתי בהן הוראות החוק וההוראות למתקני תברואה התש"ל 1970 (הל"ת) לעניין זה, לרבות בדיקת לחץ המים הקיים בבניין ותיכנון בהתאם.

	תאריך	שם משפחה ושם פרטי	מספר רישיון	חתימה
עורך בקשה ראשי		ז'יבגורסקי אולגה	15320	
עורך בקשה 1 מתכ' האינס' הסניט'				
עורך בקשה 2				

הצהרת מתכנן שלד הבניין: אני החתום מטה (שם משפחה ושם פרטי) ____ מס' זהות ____ מהנדס רשוי מס' ____ /הנדסאי בעל רישיון מס' ____ ("למבנה פשוט") מצהיר בזאת כדלקמן:

1) אני מסכים להיות מתכנן שלד הבניין הנדון בבקשה ולפקח פיקוח עליון על הקמת השלד.
2) אני מתחייב להגיש לפני מתן ההיתר, נושא הבקשה את החישובים הסטטיים בבדבר ____ ש בעבודה ההיתר.
3) ידוע לי, שאם אחרי הגשת הנתונים הסטטיים יתגלה צורך בשינוי מהותי בהם, אני מתחייב להגיש חישובים סטטיים מתוקנים מיד עם גילוי הצורך בכך.
4) אני מצהיר, כי יש לי כישורים מקצועיים לערוך בקשה זו ובדקתי את כל המסמכים הנוגעים לבקשה, לרבות כל תכנית הנוגעת לבקשה, וידוע לי כי אם הצהרה זו אינה נכונה, הרי היא תיחשב מסירת ידיעה שהיא כוזבת או מטעה בפרט חשוב, כמשמעותה בסעיף 214 לחוק, וצפויים לי העונשים הקבועים לפי כל דין.
5) ידוע לי כי עלי לשמור את תכניות הקונסטרוקציה לתקופה של לא פחות מ-10 שנים לאחר גמר הבנייה.

X ____ חתימה 05.2014 תאריך

הצהרת האחראי לביצוע שלד הבניין (כאשר מונה): אני החתום מטה (שם משפחה ושם פרטי) ____ מס' זהות ____ מהנדס רשוי מס' ____ /הנדסאי בעל רישיון מס' ____ ("למבנה פשוט") מצהיר בזאת כדלקמן:

1) אני מסכים להיות האחראי לביצוע שלד הבניין.
2) אני מצהיר, כי יש לי כישורים מקצועיים להיות אחראי לביצוע שלד ____, ואני מתחייב לדאוג לביצוע שלד ____ על פי תוכניות והוראות של מתכנן השלד כפי ____ בכתב וכן למלא את תפקידי על פי שנקבע בכל חיקוק הנוגע לכך.

תאריך ____ חתימה ____

הצהרת אחראים לביקורת (כאשר מונו): אנו החתומים מטה מצהירים בזה:

1) כל אחד מאיתנו מאשר שהאמור בנוגע לו ברשימה שבסעיף י"ב לעיל הוא נכון.
2) כל אחד מאיתנו מסכים לקבל עליו את התפקיד המיועד לו בסעיף י"ב.
3) אנו מצהירים כל אחד בנוגע לתחום פעולתו, שיש לנו כישורים מקצועיים לערוך את הביקורת ולדקות את כל המסמכים ____ ולדווח על תוצאותיה לרשות הרישוי המקומית כמתחייב על פי כל דין.

אני ____ (עורך הביקורת הראשי) אחראי/ת לכך שהביקורת תיערך על פי מיטב הידיעה המקצועית, ושכל הדיווחים לרשות הרישוי המקומית ייערכו על פי כל דין.

תאריך	שם משפחה ושם פרטי	מספר רישיון	חתימה

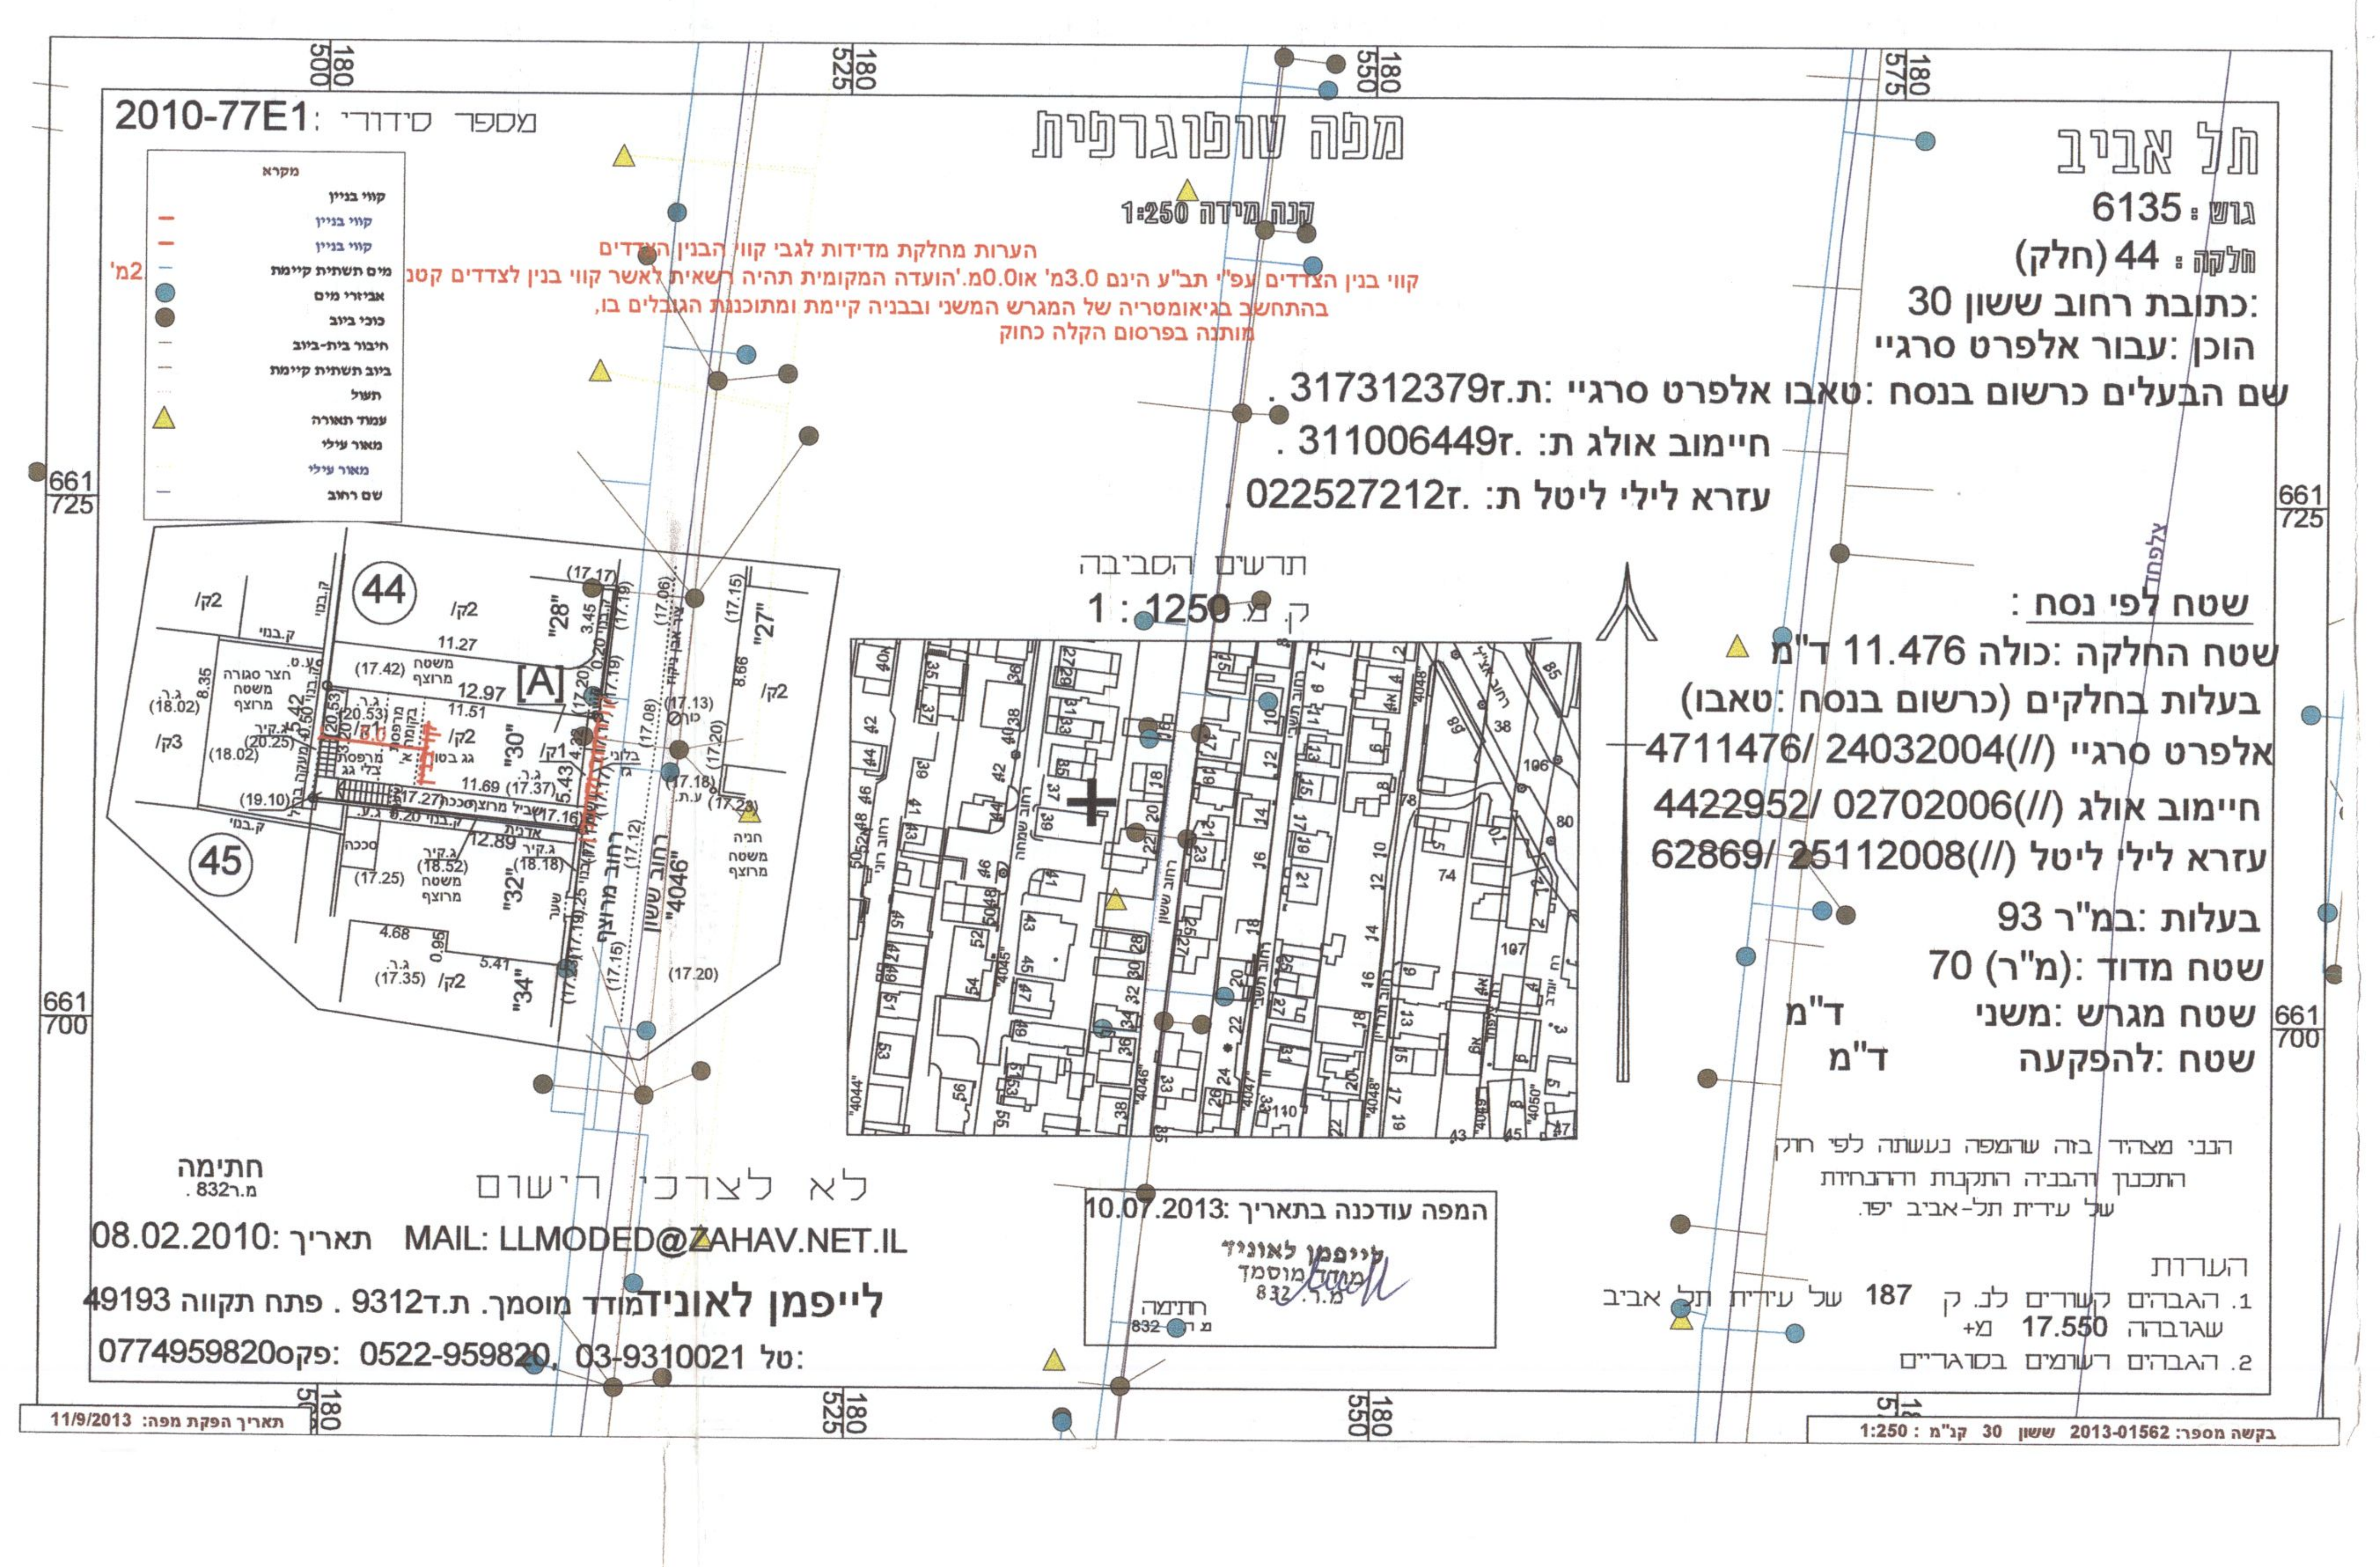

תל אביב

מפה טופוגרפית

קנה מידה 1:250

מספר סידורי: 2010-77E1

גוש: 6135

חלקה: 44 (חלק)

כתובת: רחוב ששון 30

הוכן: עבור אלפרט סרגיי

שם הבעלים כרשום בנסח: טאבו אלפרט סרגיי: ת.ז317312379 .

חיימוב אולג ת: ת.ז311006449 .

עזרא לילי ליטל ת: ת.ז022527212 .

שטח לפי נסח:

שטח החלקה: כולה 11.476 ד"מ

בעלות בחלקים (כרשום בנסח: טאבו)

אלפרט סרגיי (//)4711476/ 24032004

חיימוב אולג (//)4422952/ 02702006

עזרא לילי ליטל (//)62869/ 25112008

בעלות: במ"ר 93

שטח מדוד: (מ"ר) 70

שטח מגרש: משני ד"מ

שטח: להפקעה ד"מ

הנני מצהיר בזה שהמפה נעשתה לפי חוק התכנון והבניה התקנות וההנחיות של עירית תל-אביב יפו.

הערות

1. הגבהים קשורים לנ. ק 187 של עירית תל אביב שגובהה 17.550 מ+
2. הגבהים רשומים בסוגריים

הערות מחלקת מדידות לגבי קווי הבנין הצדדים

קווי בנין הצדדים עפ"י תב"ע הינם 3.0מ' או0.0מ.'הועדה המקומית תהיה רשאית לאשר קווי בנין לצדדים קטנ ... 2מ' בהתחשב בגיאומטריה של המגרש המשני ובבניה קיימת ומתוכננת הגובלים בו, מותנה בפרסום הקלה כחוק

תרשים הסביבה

ק. מ. 1 : 1250

לא לצרכי רישום

המפה עודכנה בתאריך: 10.07.2013

לייפמן לאוניד מודד מוסמך מ.ר. 832

חתימה מ.ר832 .

תאריך: 08.02.2010 MAIL: LLMODED@ZAHAV.NET.IL

לייפמן לאוניד מודד מוסמך. ת.ד9312 . פתח תקווה 49193

טל: 03-9310021 ,0522-959820 :פקס0774959820

תאריך הפקת מפה: 11/9/2013

בקשה מספר: 2013-01562 ששון 30 קנ"מ : 1:250

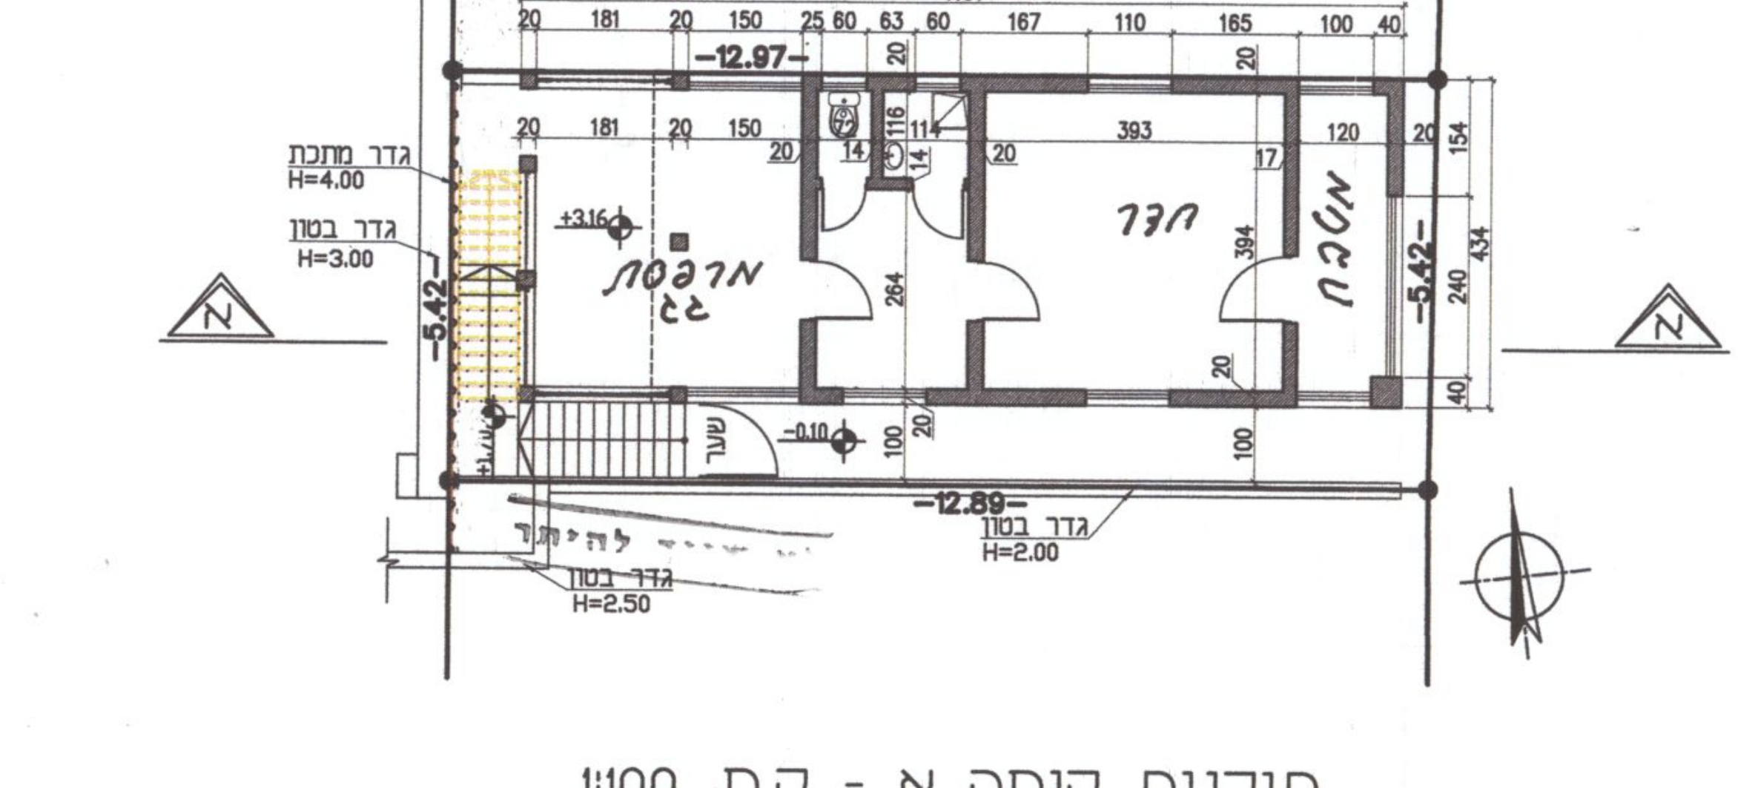

תוכנית קומה א - ק.מ. 1:100

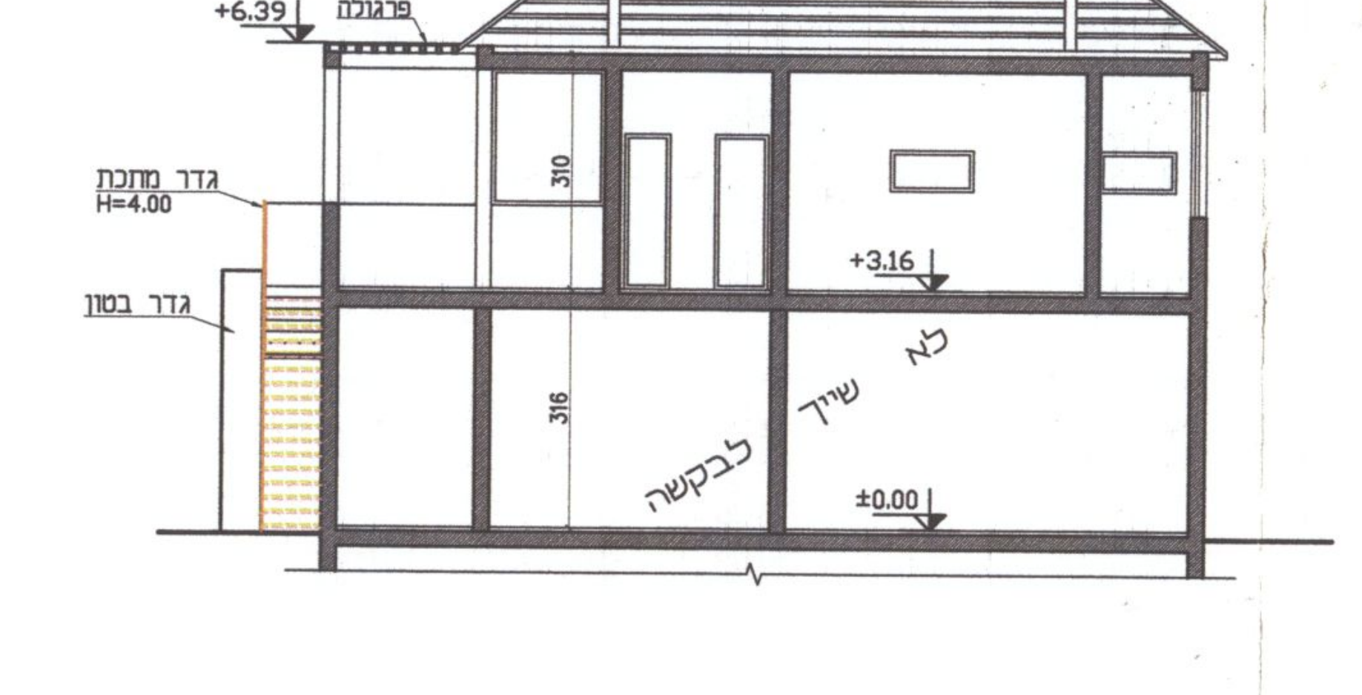

חתך א-א - ק.מ. 1:100

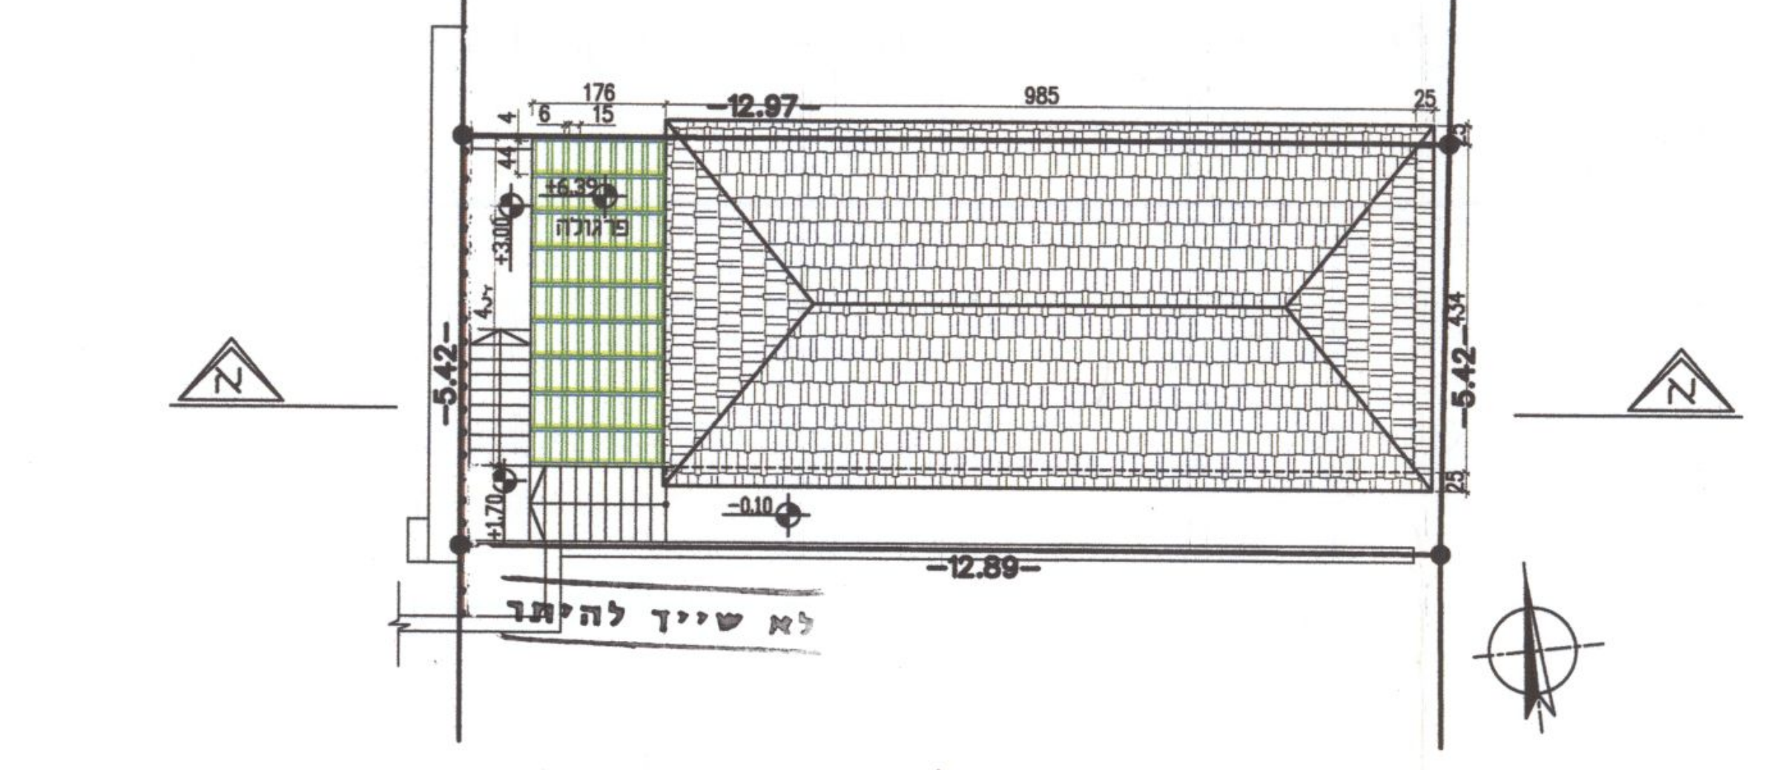

תכנית קומת גג עליון - ק.מ. 1:100

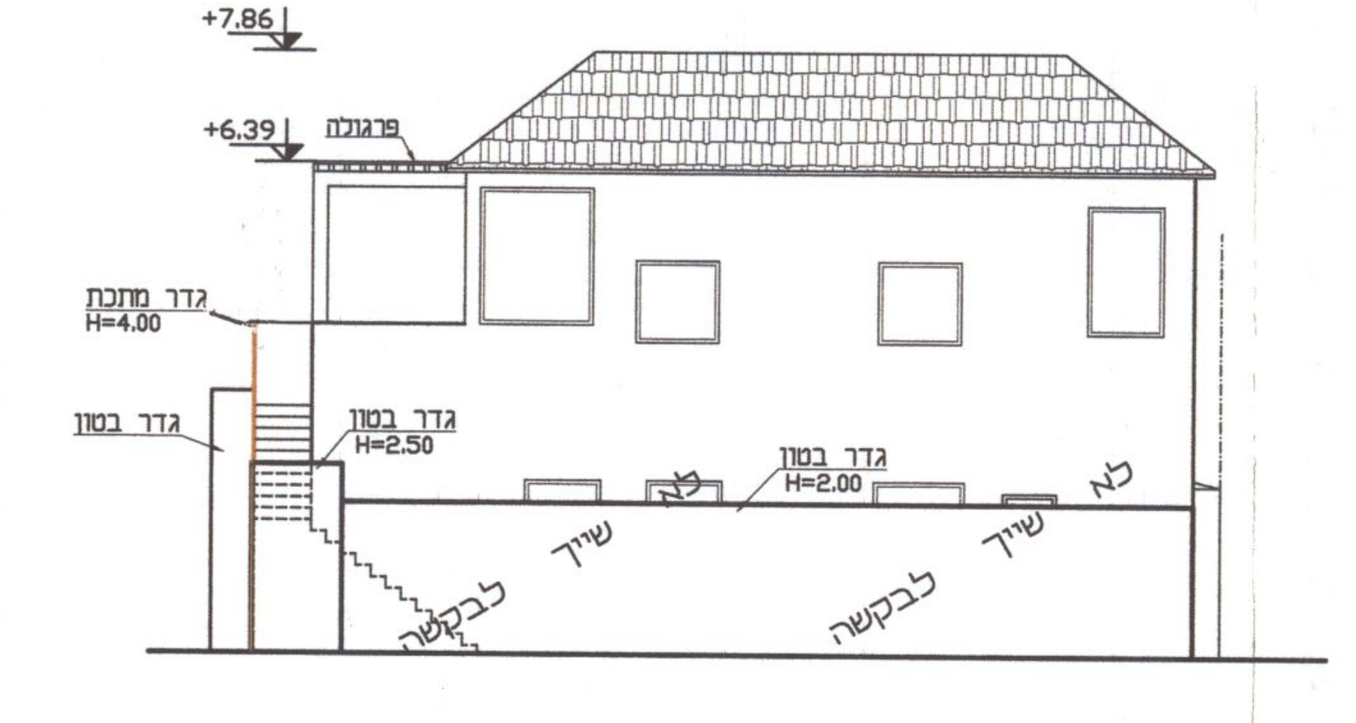

חזית דרומית - ק.מ. 1:100

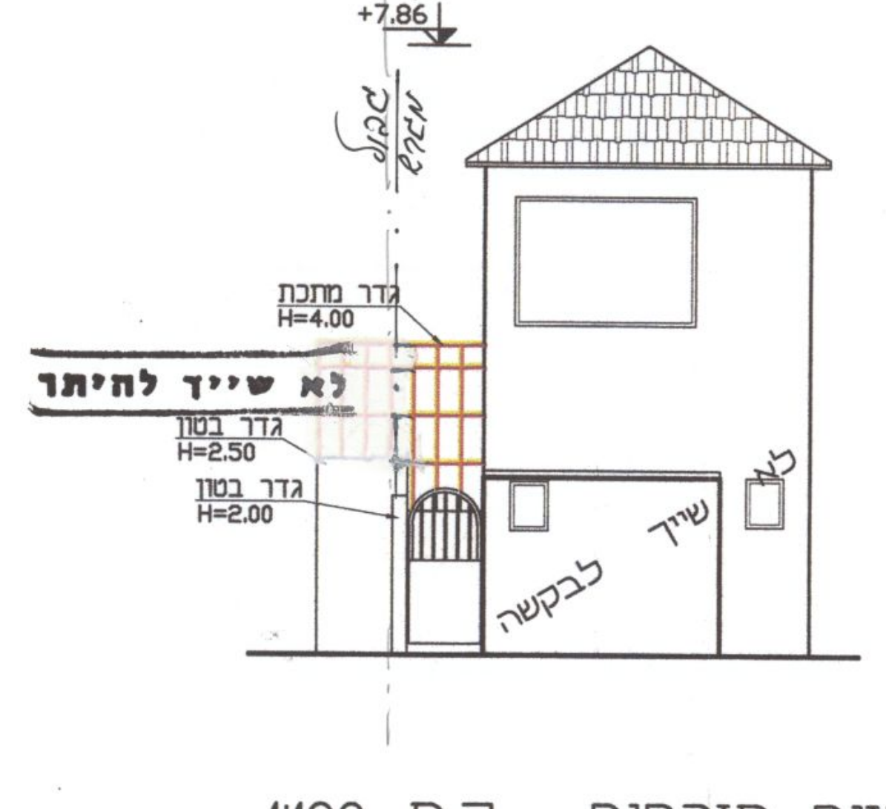

חזית מזרחית - ק.מ. 1:100

רשות רישוי מקומית לתכנון ולבניה למרחב תכנון תל-אביב-יפו

בהתאם לסעיף 30 לחוק התכנון והבניה ולסעיף 13 (ב) לחוק התכנון והבניה (בקשה להיתר, תנאים ואגרות) תש"ל 1970 ... מס' ... ומהווה חלק בלתי נפרד ממנו.

מהנדס העיר 02-06-2014

מינהל ההנדסה אגף הרישוי העתק מאושר חתימה

חישוב שטחים

חישוב שטח פרגולה:

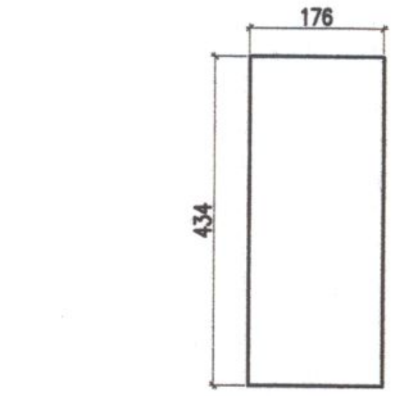

שטח	מס'	חישובים	סה"כ מ"ר
פרגולה		1.76 x 4.34	7.64