20 862213 002

תניה 11/11/86

[illegible] אופיר

במסגרת פרויקט "בנה ביתך" בשכונת התקוה

חוק התכנון והבניה, התשכ"ה–1965
תקנות התכנון והבניה (בקשה להיתר, תנאיו ואגרות), התש"ל–1970

טופס 2 (תקנה 2(א))

תיק מס 24240

מיפרט

הוועדה המקומית לתכנון ולבניה
תל-אביב

עיריית תל-אביב-יפו מנהל ההנדסה 24-09-1986 נתקבל באגף הרישוי

א. תיאור הבנין

1. המקום	הרחוב	מס'	גוש	חלקה	תכנית מיתאר מקומית או מפורטת	מגרש
ש' התקוה	ששון	33	6135	44 חל'	2215	

	השם	המען	מס' הטלפון
2. המבקש	דוד וחיה בוסני	רח' ששון 33 ש' התקוה ת"א.	33 82 91
3. בעל הזכות בנכס	—"—	—"—	
4. עורך הבקשה *	פרח: אדריכלים בע"מ	אדם הכהן 16 ת"א.	23 99 97
5. האחראי לביצוע השלד	י. לעני מהנדס	רח' ציון 22 ר"ג.	73 70 60

6. אזור הבניה: ● מגורים ☐ מסחר ☐ תעשיה ☐ בנין ציבורי ☐ חקלאי ☐ ....

7. שטח: המגרש/החלקה: 211.65 מ"ר. אחוז הבניה המותר: 140 %

8. מטרת הבנין: ● מגורים ☐ הארחה ☐ עסקים ☐ תעשיה ☐ חקלאי ☐ ציבורי ☐ ....

9. מהות הבנין ותכליתו: הריסת יח"ד קיימת ובנית יח"ד חדשה על מגרש דו-משפחתי

10. תיאור העבודה המוצעת: ☐ בנין חדש ☐ תוספת לבנין קיים ☐ הריסה ☐ תיקונים ☐ שינוי בבנין ☐ .... ☐ שינוי בשימוש ממטרה: .... למטרה: ....

11. האם הבניה היא בעד: ☐ משרד ממשלתי ☐ הרשות המקומית ☐ הסוכנות היהודית

ב. היקף הבניה

קומה					שטח כולל של בניה (מ"ר)								מס' חדרים	
	קיים	מוצע	סך הכל	אחוז הבניה	מגורים בדירות					עסק: הארחה וכו'	ציבורי	שונות	קיים	מוצע
					עד 45 מ"ר	עד 65 מ"ר	עד 90 מ"ר	עד 100 מ"ר	מעל 100 מ"ר					
1	2	3	4	5	6	7	8	9	10	11	12	13	14	15
מרתף														
קרקע	68.68	59.40	128.08	60%										
א		67.96	67.96	32%										
ב		17.22	17.22	8%										
ג														
ד														
ה														
ו														
ז														
הבניה הקובעת לבנין														
חדרי מדרגות														
בניני עזר														
סך הכל	68.68	144.58	213.26	100%										

הנפח המוצע: של הבנין העיקרי .... מ"ק. של בנין עזר .... מ"ק.

עיריית תל-אביב-יפו מינהל ההנדסה מחלקת פקוח על הבניה 158 24.10.86 המהנדס אזורי

ראה הערת מ' אופיר מהנדסת 21/8/86

ג. השימוש בבנין

1. הבניה המוצעת למגורים

דירות בנות:	שטח כל דירה מ"ר	מספר דירות מכל סוג	כל הדירות	שטחים - מ"ר מזה: רצפות חדרי דיור בלבד, ומרפסות מקורות	רצפות חדרי שירות ופרוזדורים בלבד	רצפות של מרפסות בלתי מקורות	מספר חדרים: דיור	מטבחים	אמבטיות	בתי שימוש	אחרים
1	2	3	4	5	6	7	8	9	10	11	12
חדר אחד	ראה תשריט סכימטי של שטחי הבניה בכל קומה, המציין מספר החדרים ושטח כל דירה.										
2 חדרים											
3 חדרים											
4 חדרים											
5 חדרים											
6 חדרים											
7 חדרים ויותר											
חדרים נוספים לדירות קיימות											
בניני עזר											
סך הכל											

איכות נמוכה

נסרק

2. הבניה הקיימת והמוצעת לתעשיה ולמלאכה

פרטים	קיים				מוצע				סך הכל			הערות
	שטח	גובה	נפח	% הבניה	שטח	גובה	נפח	% הבניה	שטח	נפח	% הבניה	
1	2	3	4	5	6	7	8	9	10	11	12	13
אולמי מלאכה												
משרדים												
חדרי שירות												
סככות												
בניני עזר												
חדרי מדרגות												
סך הכל												

3. הבניה המוצעת למטרות אחרות (הארחה, עסקים ומשרדים, בניני ציבור, בניני משק חקלאי, מטרות שונות).

השימוש המיועד	שטחים - מ"ר: סך הכל מ"ר	מזה: חדרים	אולמות	אחסנה	חדרי שירות	מספר חדרים, אולמות וכו': חדרים	אולמות	אחסנה	חדרי שירות
1	2	3	4	5	6	7	8	9	10
בניני עזר (למעט אלה המפורטים ב־ג(4))									

4. חלקי בנין אחרים – הבניה המוצעת, שטח במ"ר.

חדרי מדרגות	מרפסות שלא נכללו לעיל	מעליות	חדרי הסקה	חדרי כביסה	מקלטים	קומת עמודים מפולשת	מחסנים	מוסכים	בניני עזר נוספים	סך הכל
1	2	3	4	5	6	7	8	9	10	11
					9.61					

ד. חומר הבניה

קירות חיצוניים	☐ בטון מזוין	☒ לבני בטון או בלוקים	☐ לבני סיליקט	☐ לבנים שרופות	☐ אבן טבעית
	☐ אבן מלאכותית	☐ איטונג	☐ עץ	☐ ברזל	☐ חמרים אחרים
תקרות	☒ בטון מזוין	☐ עץ	☐ חומר אחר		
גג	☒ בטון מזוין	☐ רעפים	☐ אסבסט	☐ פח	☐ חומר אחר ....

ה. גדרות קיימות.......... מ"א מוצעות.......... מ"א .... מ"א

ו. מקרא

🟦 בטון או בטון מזוין	☐ אבן	☐ עץ	☐ איטונג
🟥 בלוקים או לבנים מבטון	☐ סיליקט או לבנים אדומות	☐ חומר אחר	🟨 להריסה

הערות:

הנני מאשר כי הנתונים הנ"ל נכונים

תאריך 20.8.86 חתימת המבקש בוסני דוד חתימת עורך הבקשה * י. פרח

חתימת האחראי לביצוע השלד לעני יעקב חתימת בעל הזכות בנכס בוסני דוד

לשימוש הועדה המקומית בלבד	מס' ההיתר	תאריך ההיתר	תאריך התחלת הבניה	תאריך גמר הבניה

אישורים של רשויות חוץ:

חותמת הועדה המקומית

* היו מספר עורכי בקשה, כאמור בתקנה 2ה'. יבוא במקום כל אלה. הראשון שברשימת עורכי הבקשה, כאמור בטופס 1.

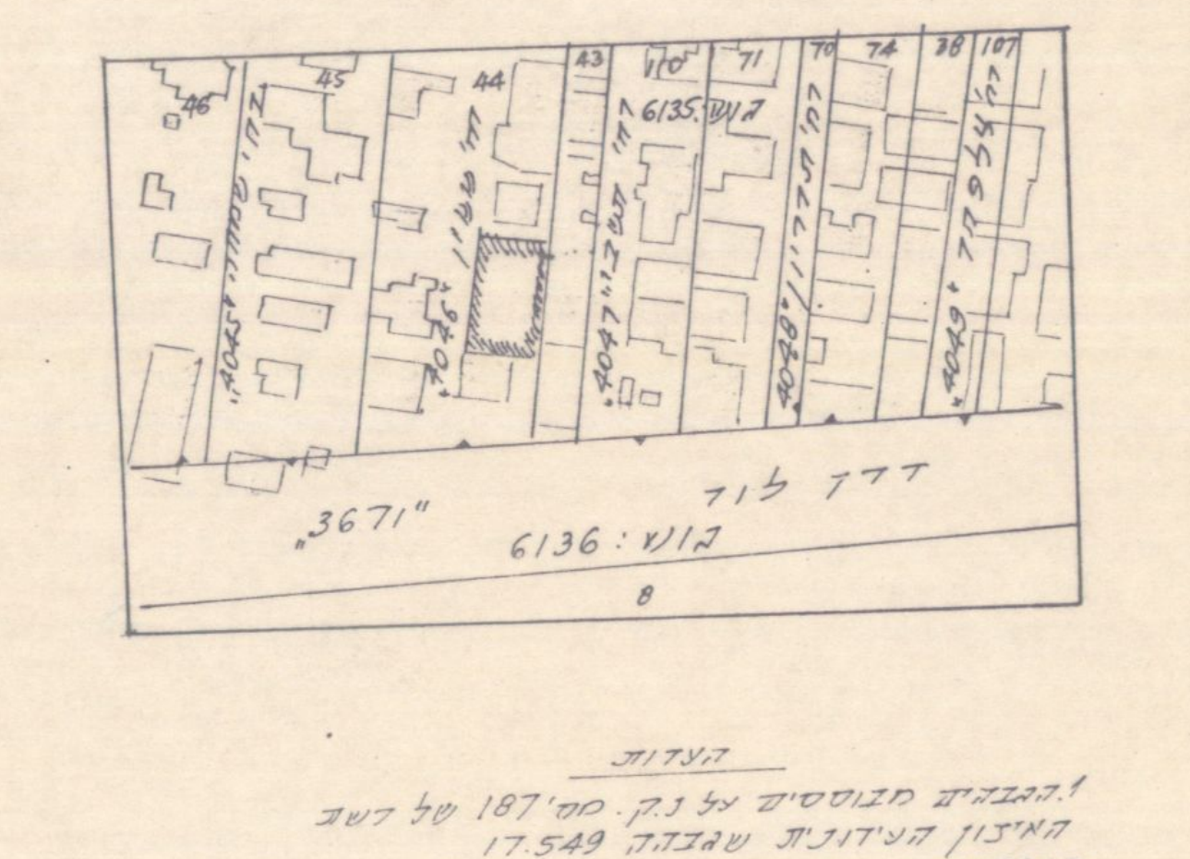

תרשים הסביבה: 1:1250

הערות:
1. הגבהים מבוססים על נק. מס' 187 של רשת האיזון העירונית שגבהה 17.549
2. הגבהים נרשמו בסוגריים

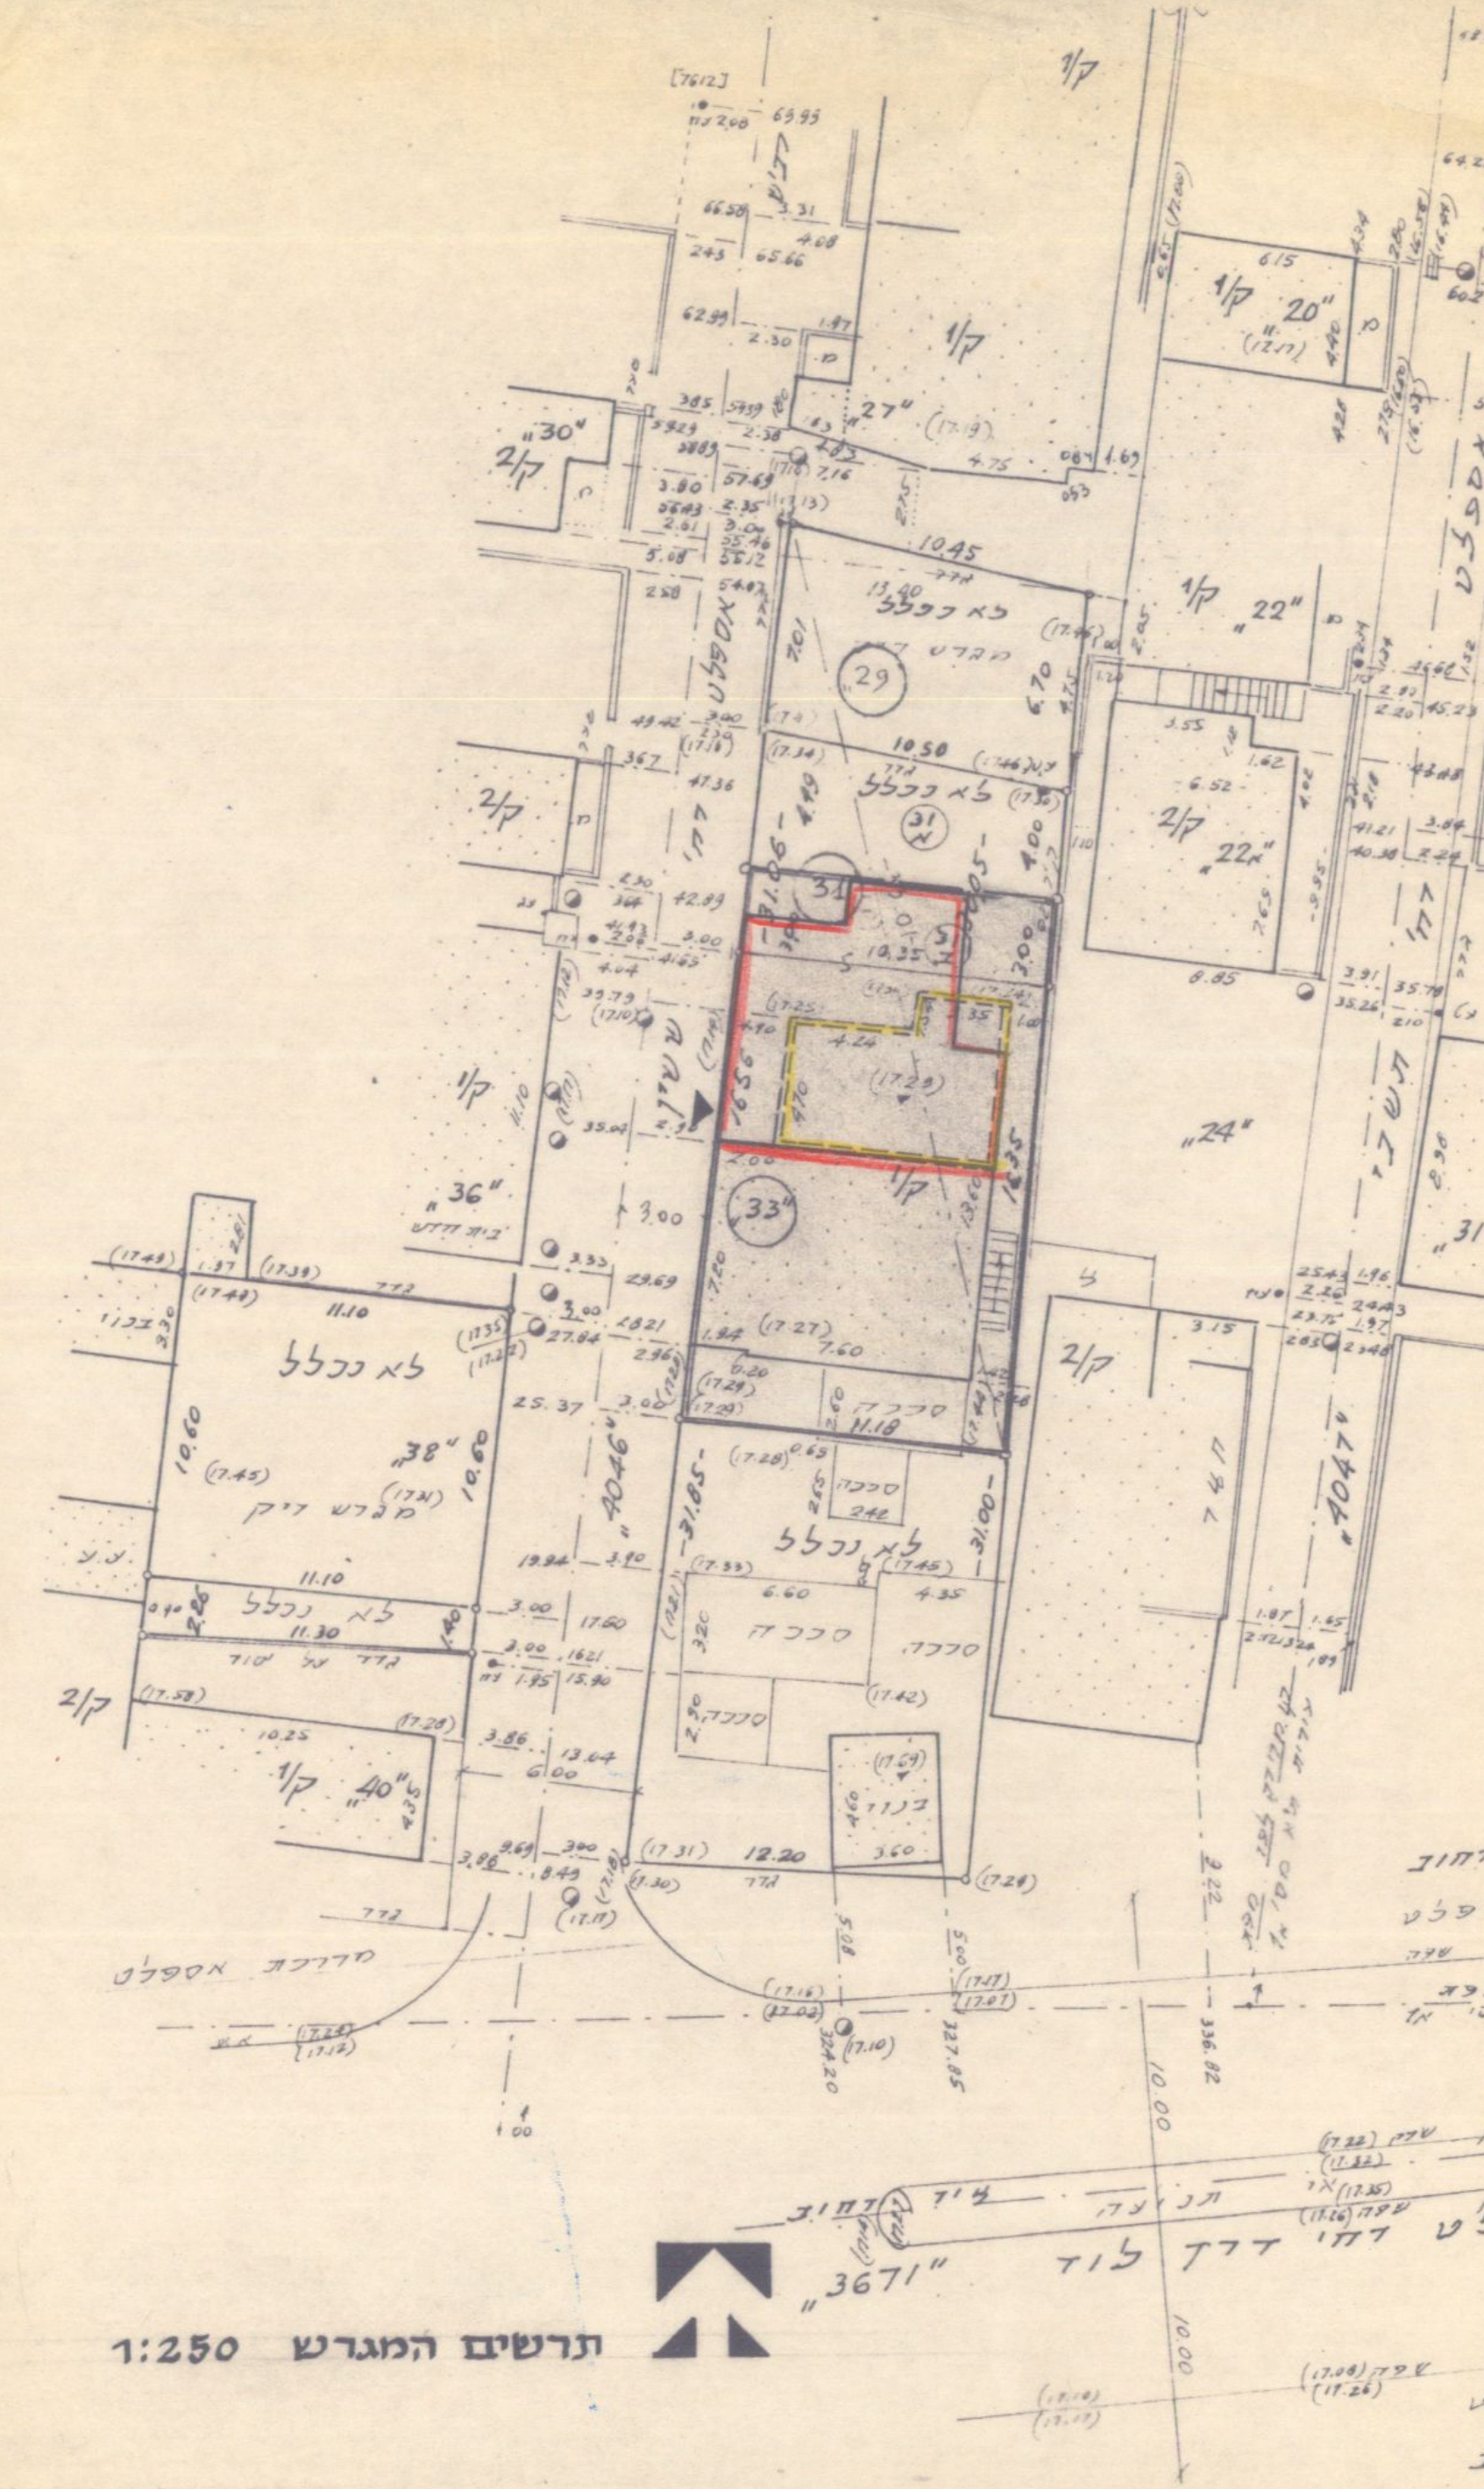

תרשים המגרש 1:250

חשוב שטח:

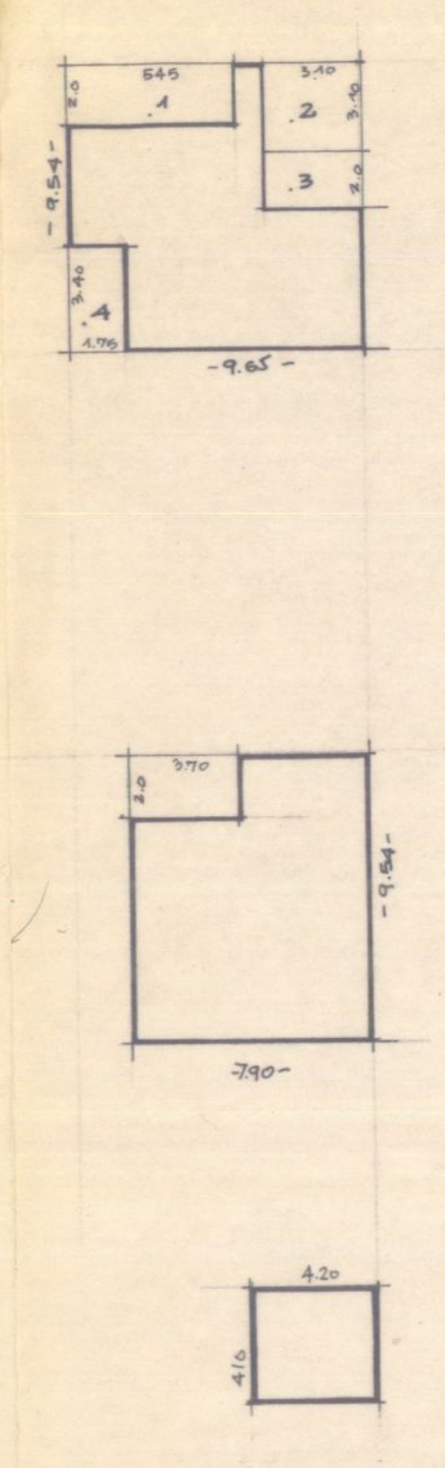

ק. קרקע
מסגרת 9.65 x 9.54 = 92.06
1. 5.45 x 2.00 = 10.90
2: 3.10 x 3.10 = 9.61
3: 3.10 x 2.00 = 6.20
4: 1.75 x 3.40 = 5.95
ס"ה הורדות 32.66
ס"ה שטח הקומה 59.40

ק. עליונה
מסגרת 7.90 x 9.54 = 75.36
הורדה 3.70 x 2.00 = 7.40
ס"ה שטח הקומה 67.96

ח. כביסה
4.20 x 4.10 = 17.22

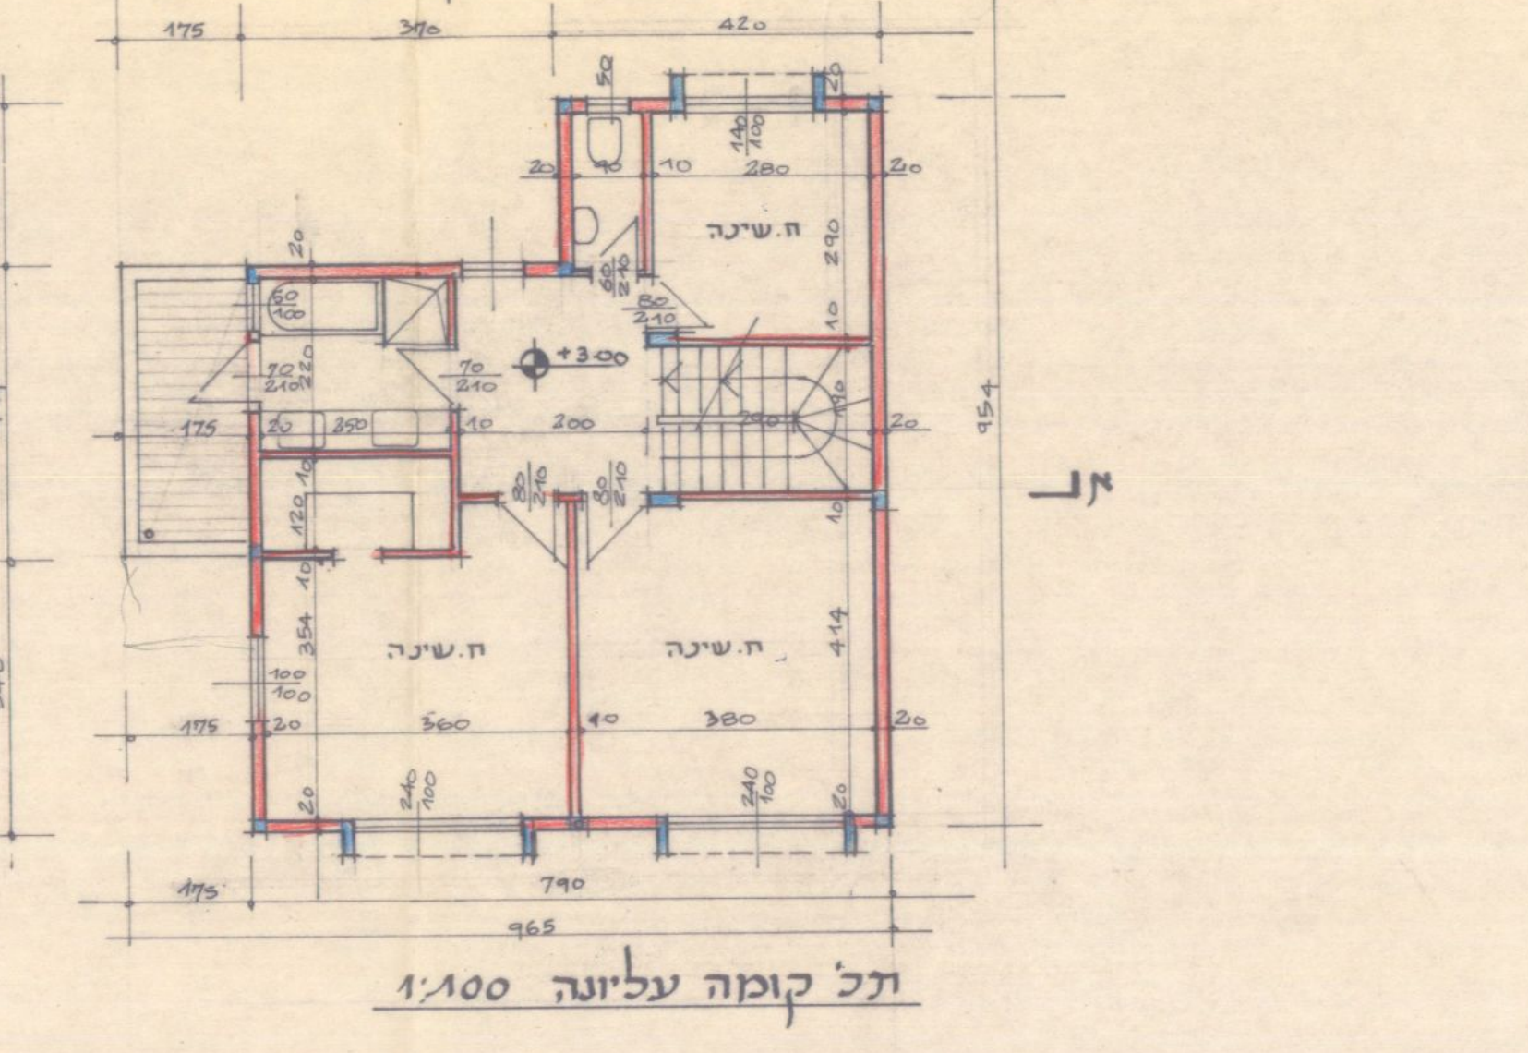

תכ' קומה עליונה 1:100

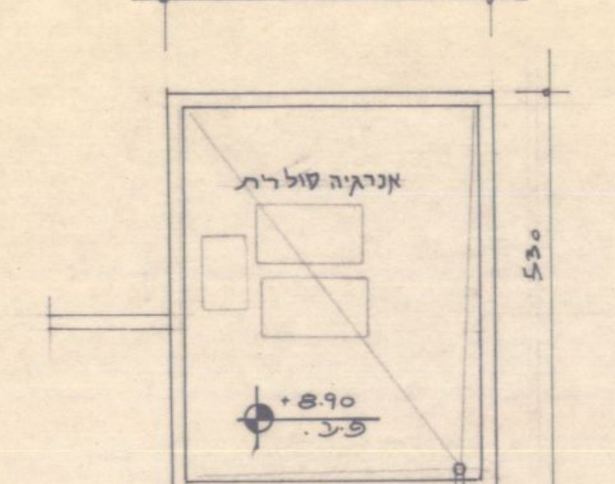

תכ' גג ח. מדרגות 1:100

עיריית תל-אביב-יפו / מנהל הנדסה / אגף הרישוי
אשור מס' 428/86
נתן אשור לכלי אשפה במקום ובמבנה שצויינו בתכנית בתנאי:
1) מתקן כלי אשפה יבנה בצורת ארון קיר בעל 1 דלתות ברזל הנושאים מיכלים פלסטיים של 76 ליטר, עם מכסה צמוד מדגם מאושר על ידי אגף התברואה.
2) ברז מים ובריכה ייקבעו החל במתקן בעל 2 כלי אשפה ויותר והם יחוברו להספקת המים הכללית ולרשת הביוב של הבית.
3) ....
בכל מקרה של שינויים בתכנית הבניה יש לקבל אישור מחדש מאגף הרישוי על סוג, כמות, צורת ומספר כלי האשפה.
תאריך.......... חתימה..........
10 נוב' 1986
לאחר גמר בנית הבנין, נא לתאם קשר עם מדור תכנון מתקנים במנהל ההנדסה/אגף הרישוי לשם בדיקת התנאים הנ"ל.
רק לאחר ביצוע התנאים - נוכל לשחרר את הפקדון.

אין להשתמש בבטונדה לפתחי אשפה ואין לפתוח שערים ודלתות כלפי דרך ציבורית

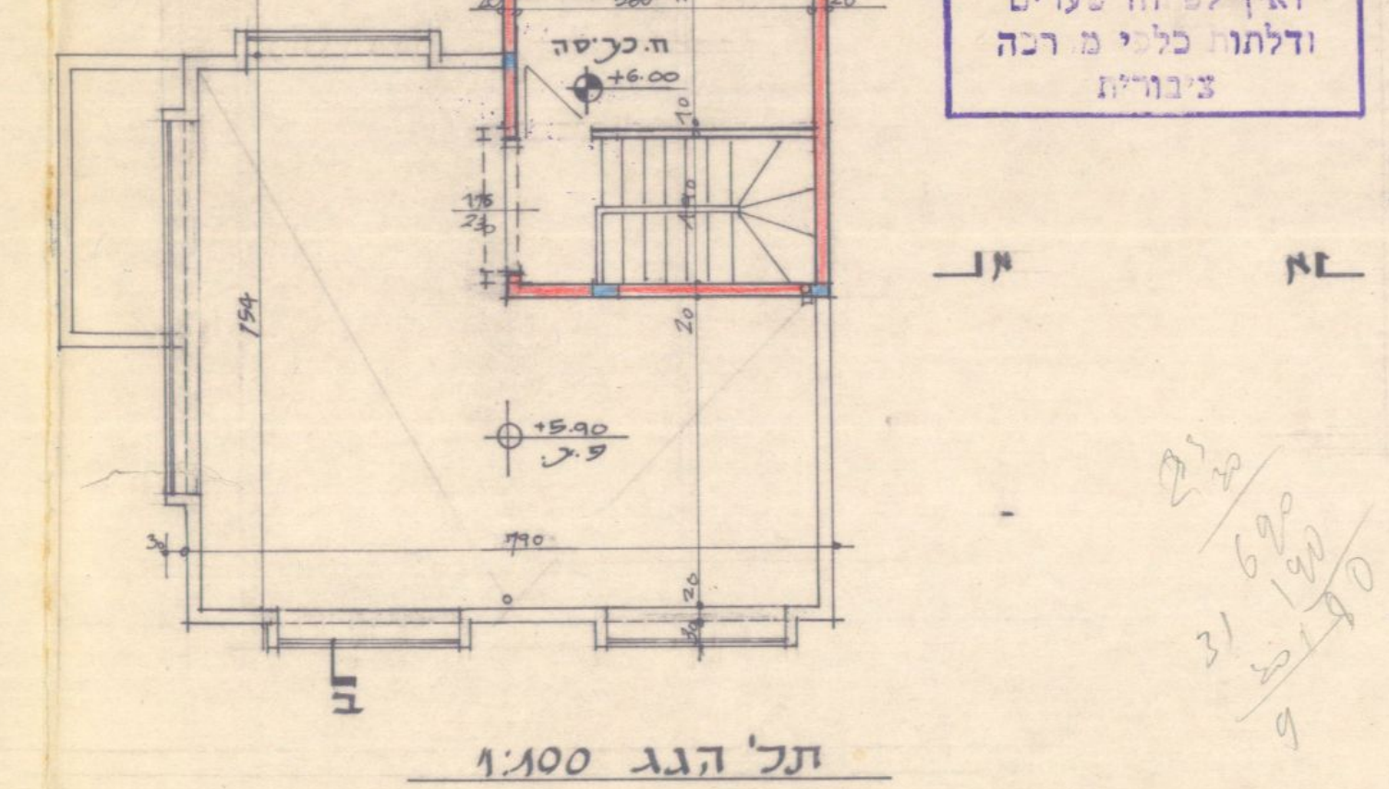

תכ' הגג 1:100

אסור חניה

אין [illegible] חניה מעבר הבנין בשטח התקוה.

51/187

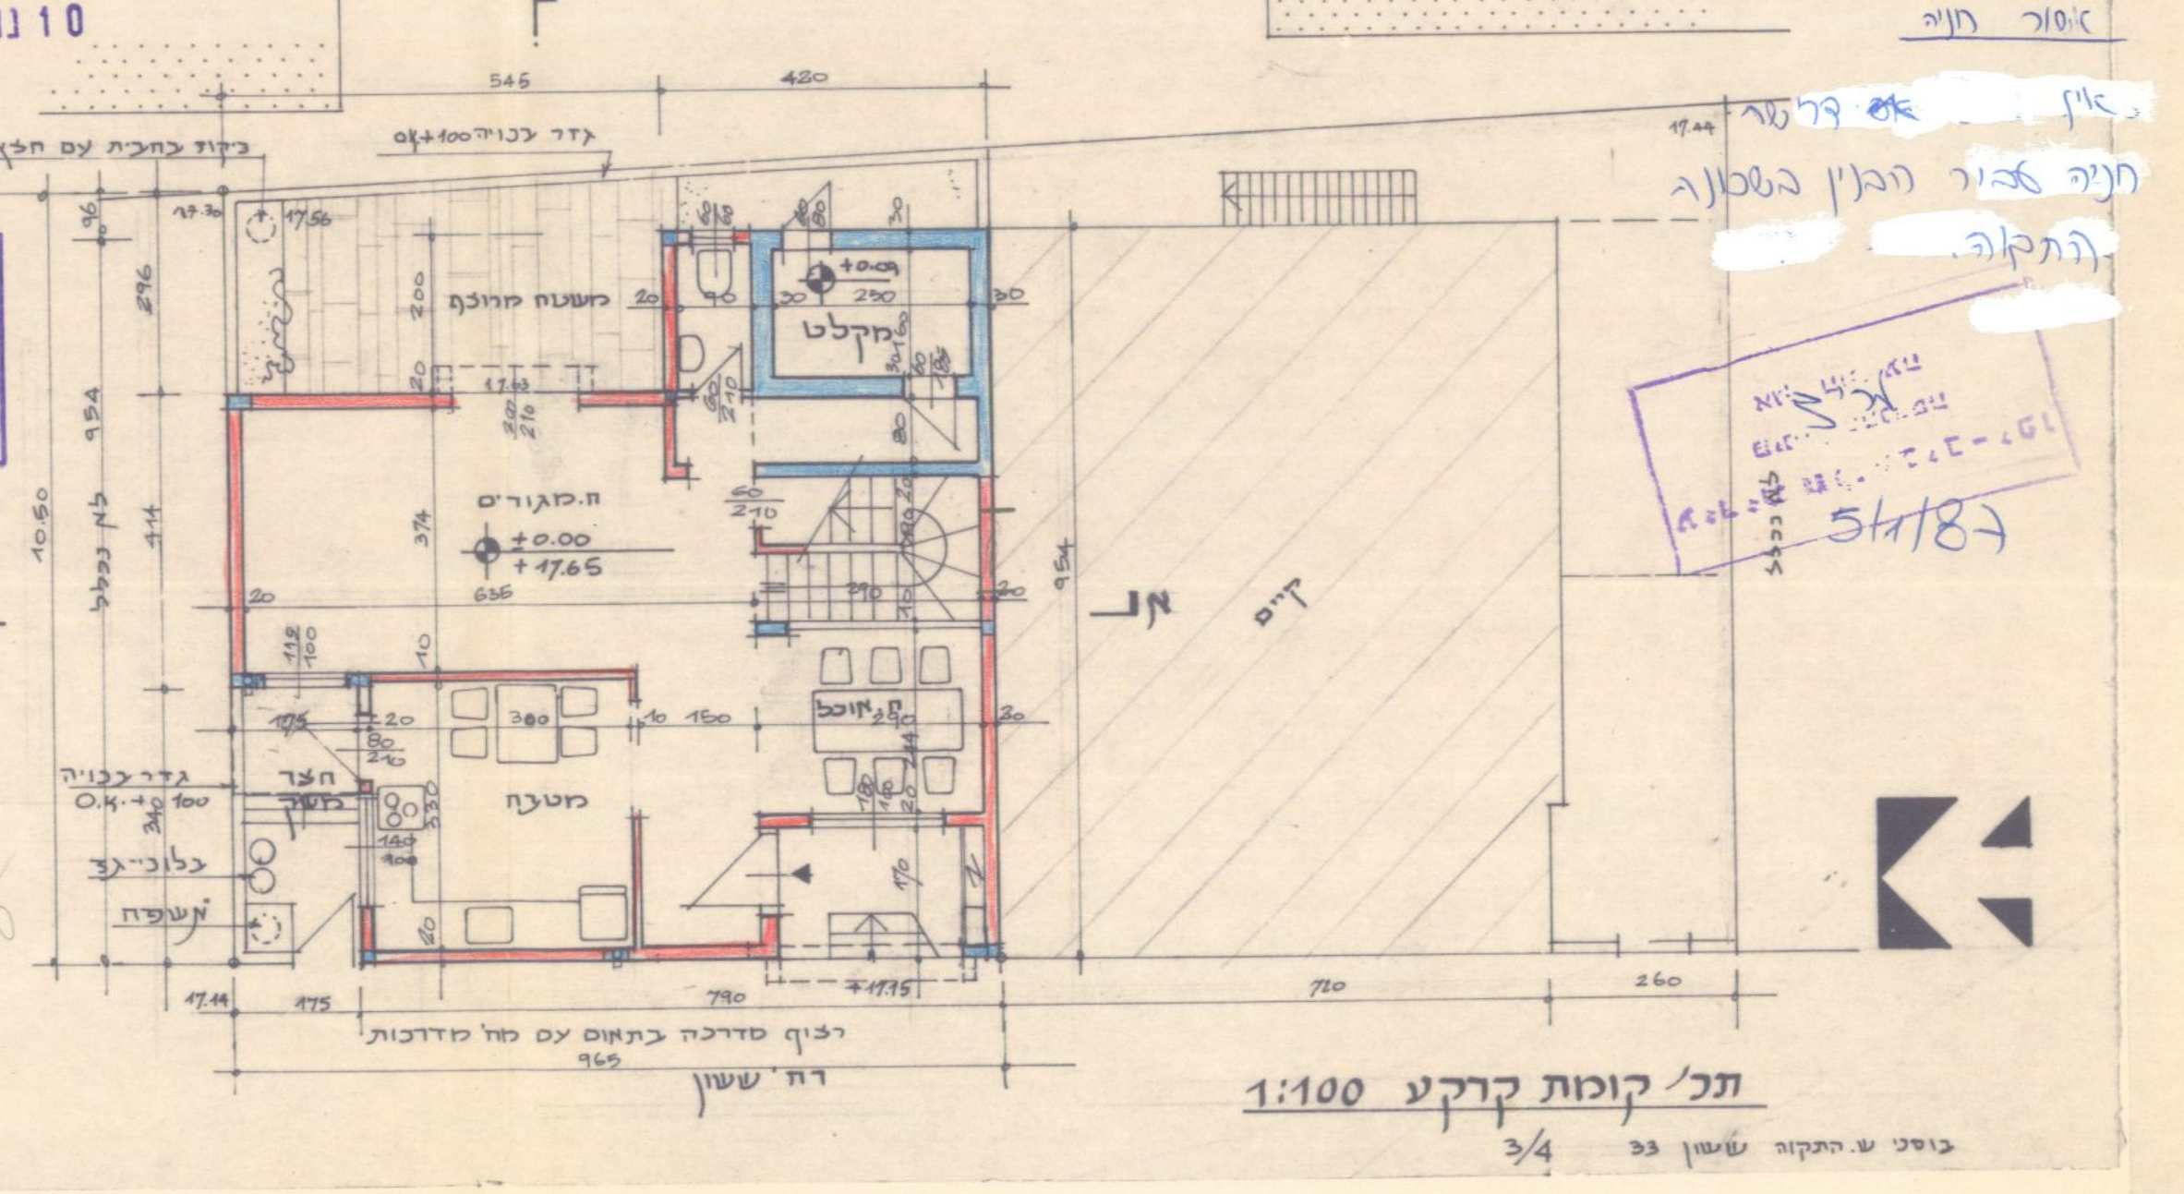

תכ' קומת קרקע 1:100

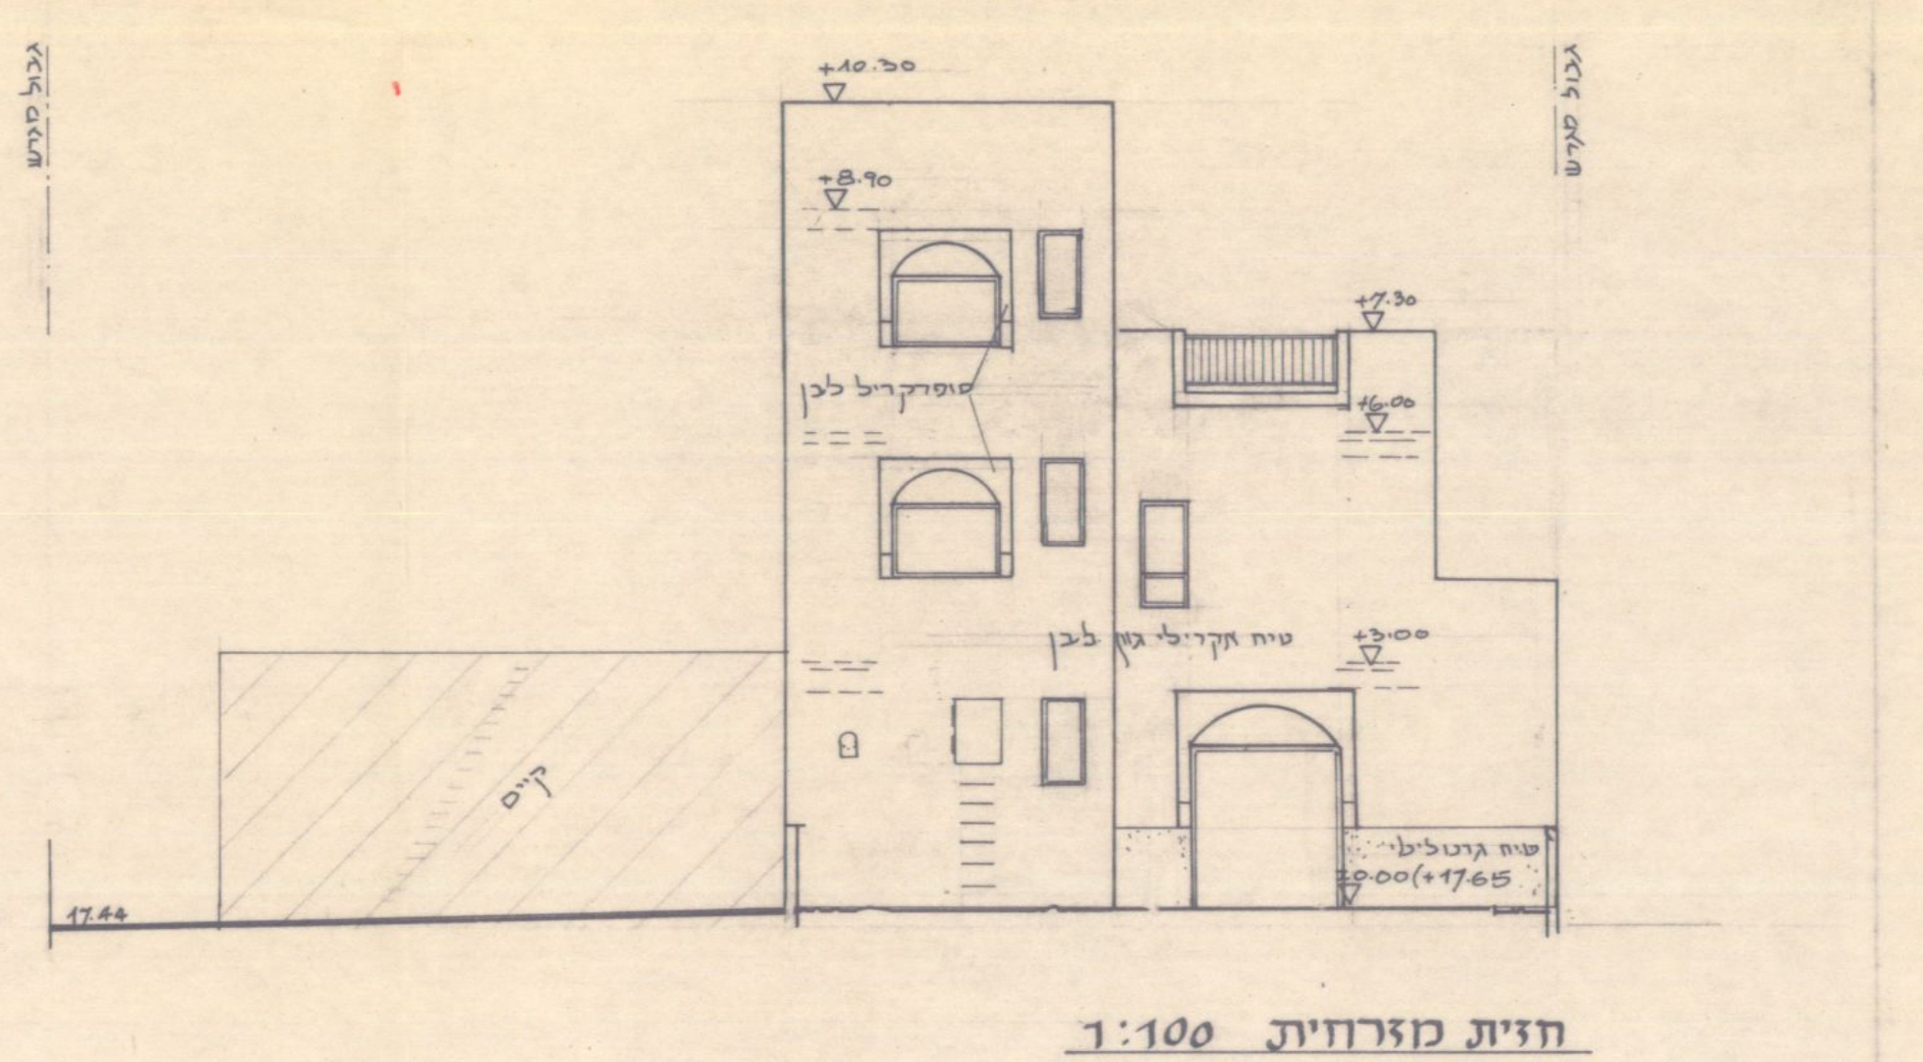

חזית מזרחית 1:100

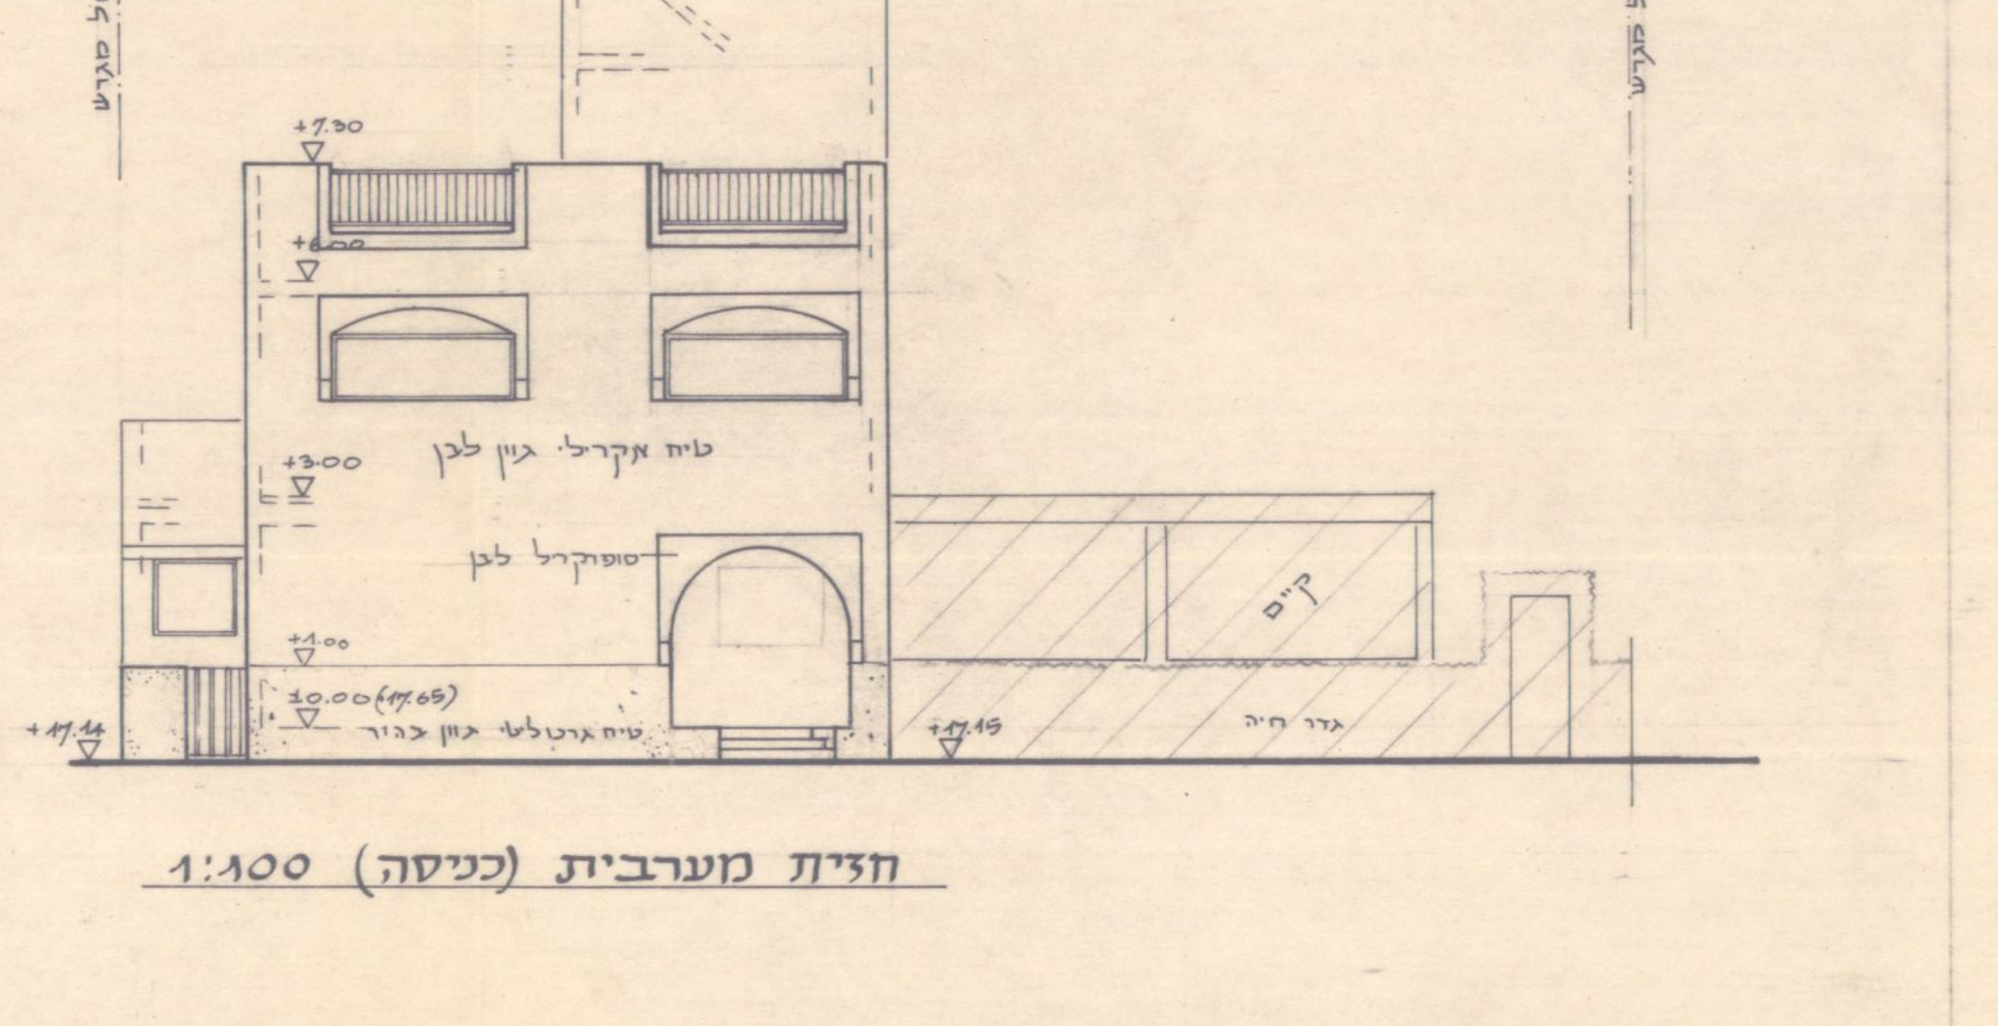

חזית מערבית (כניסה) 1:100

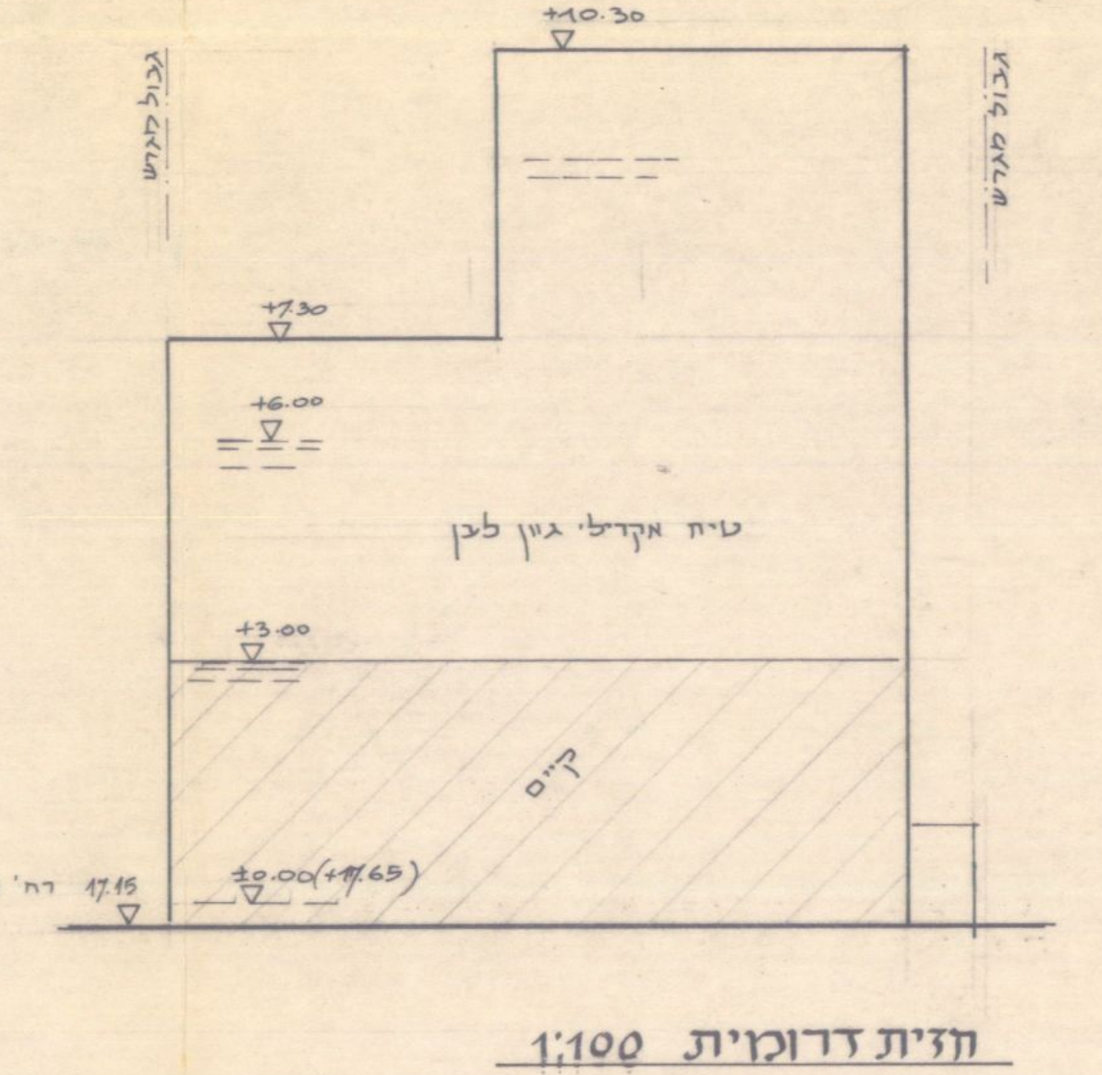

חזית דרומית 1:100

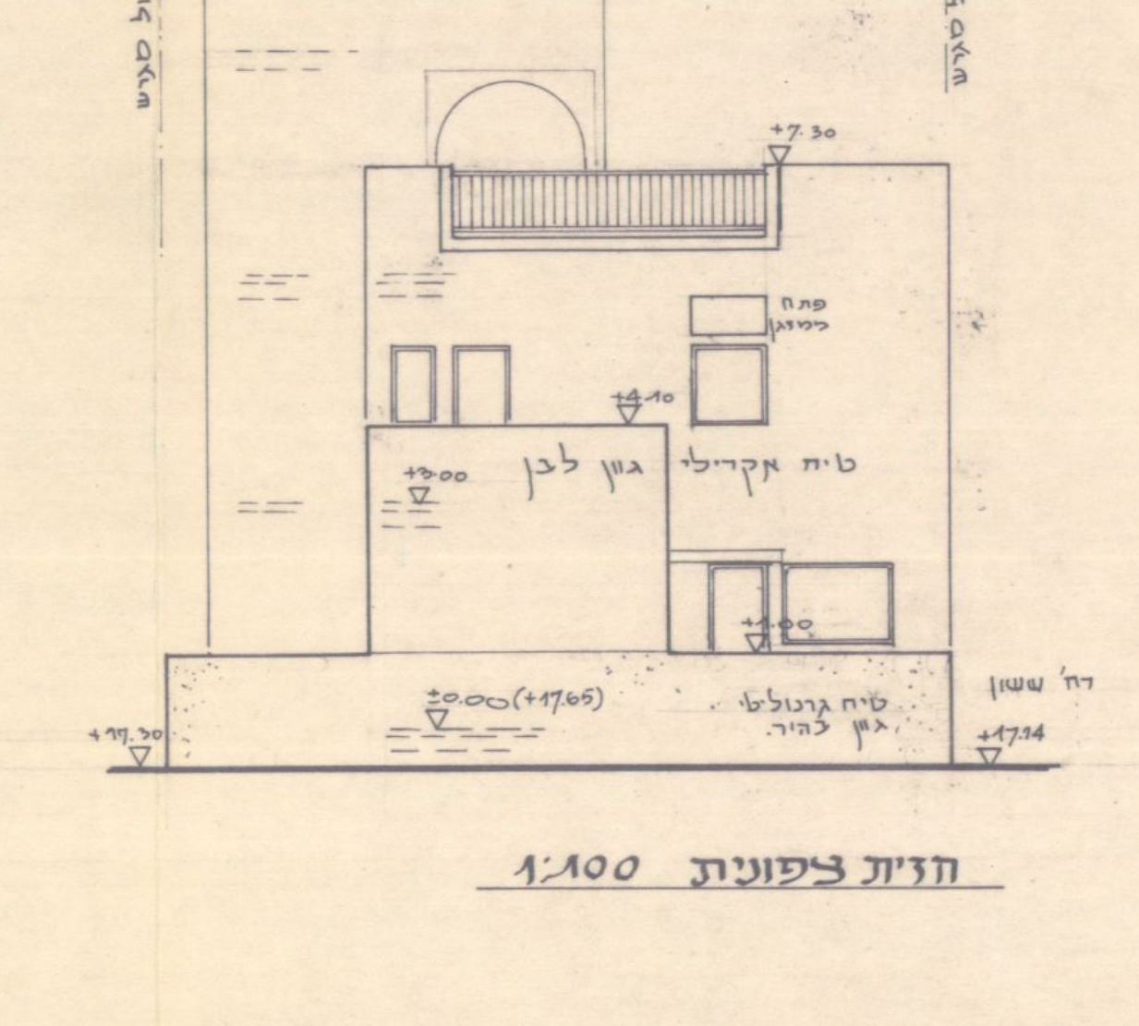

חזית צפונית 1:100

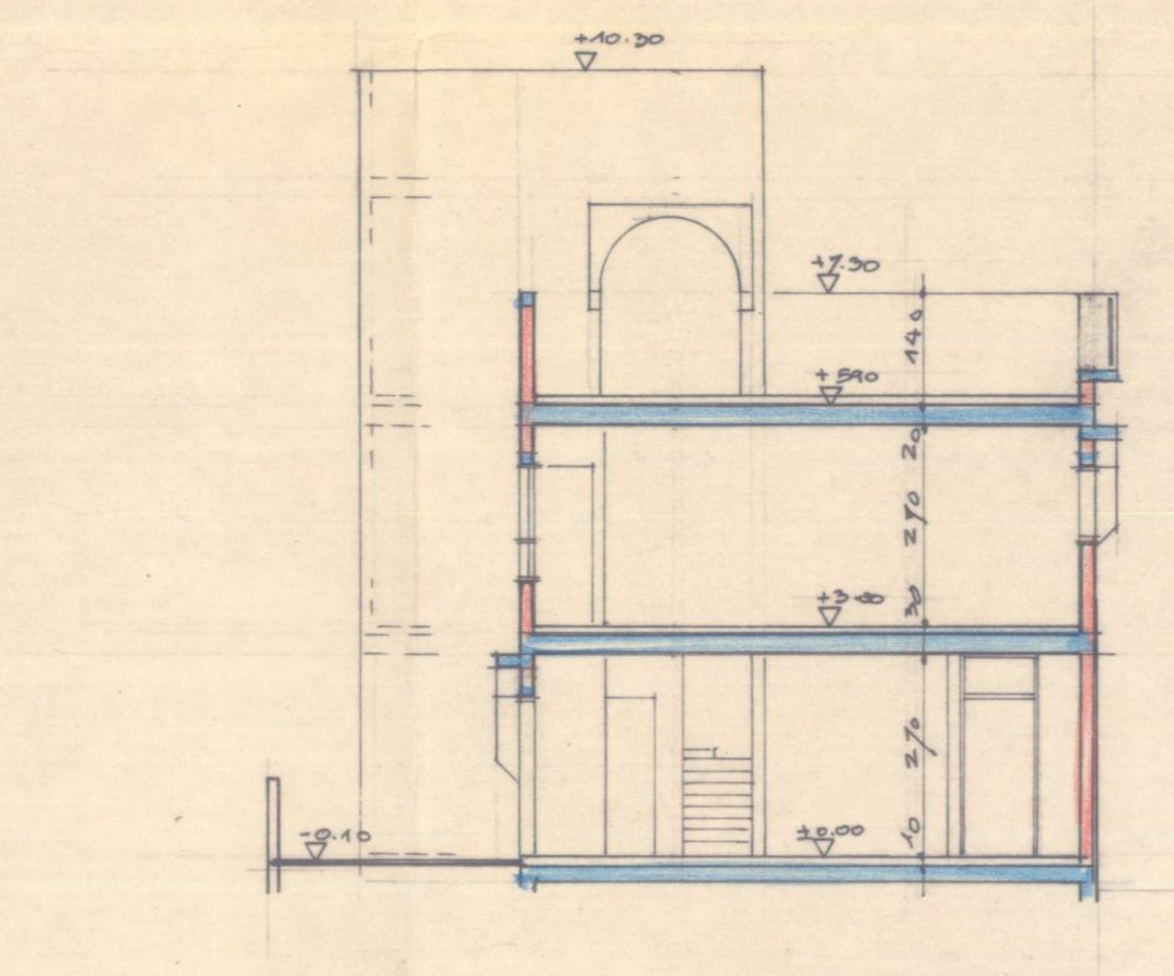

חתך ב-ב 1:100

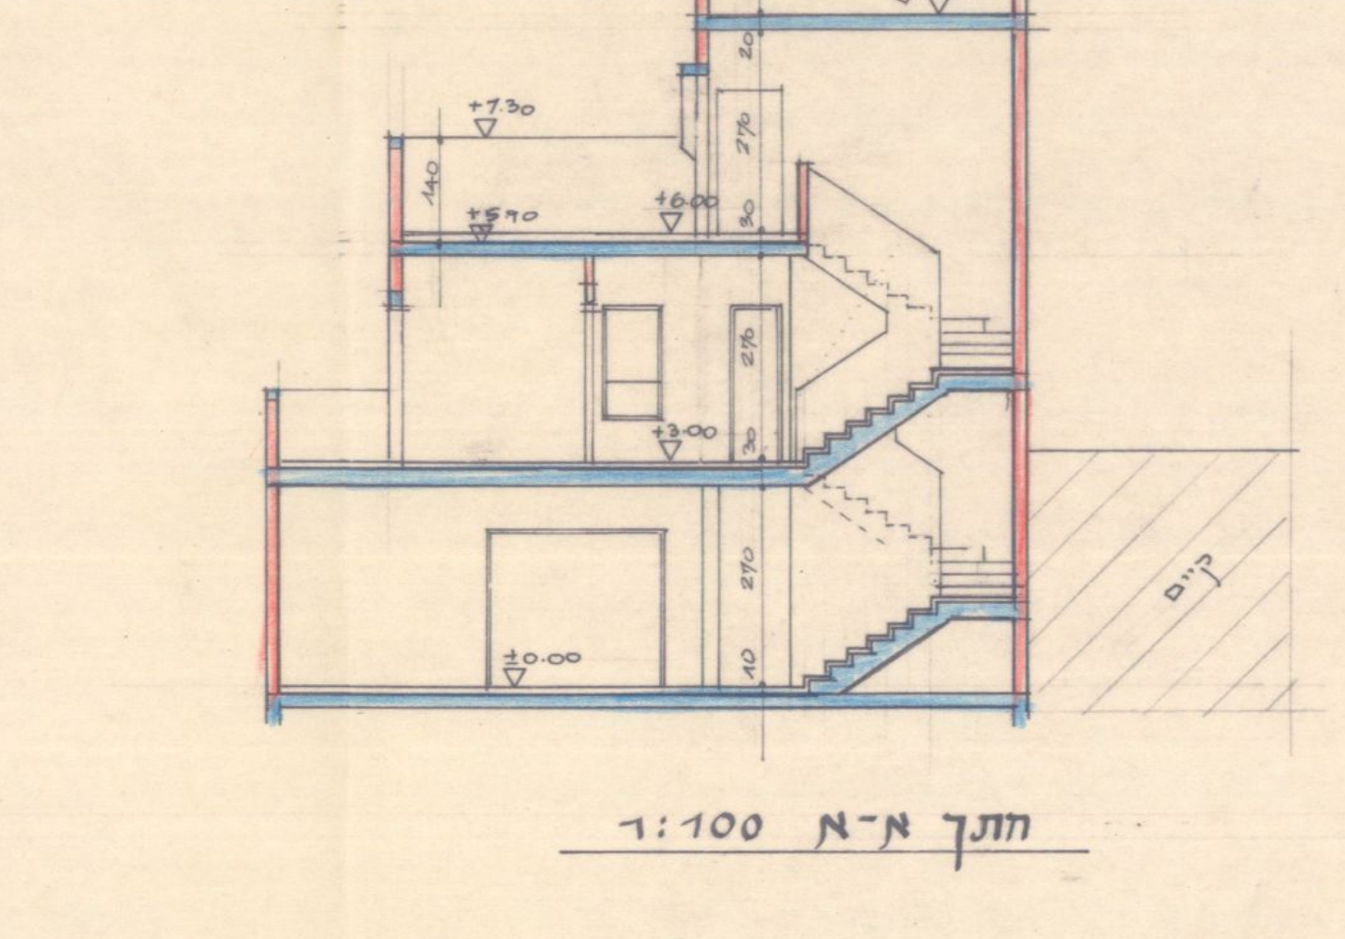

חתך א-א 1:100

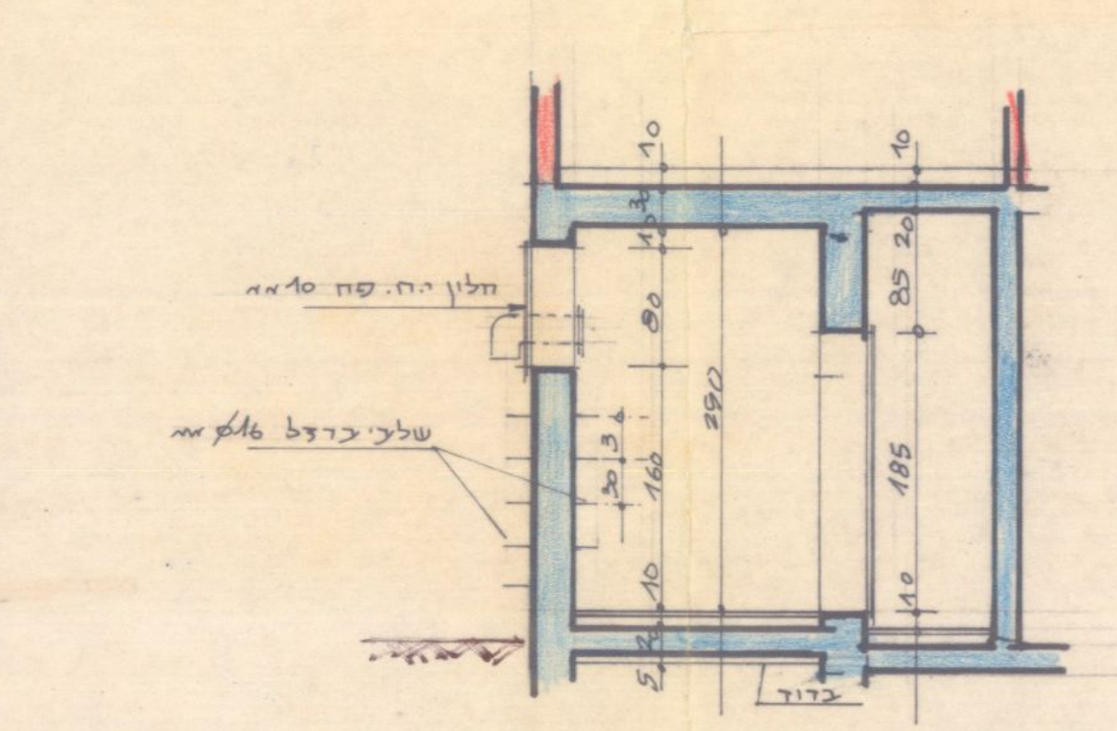

חתך 1:1 1:50

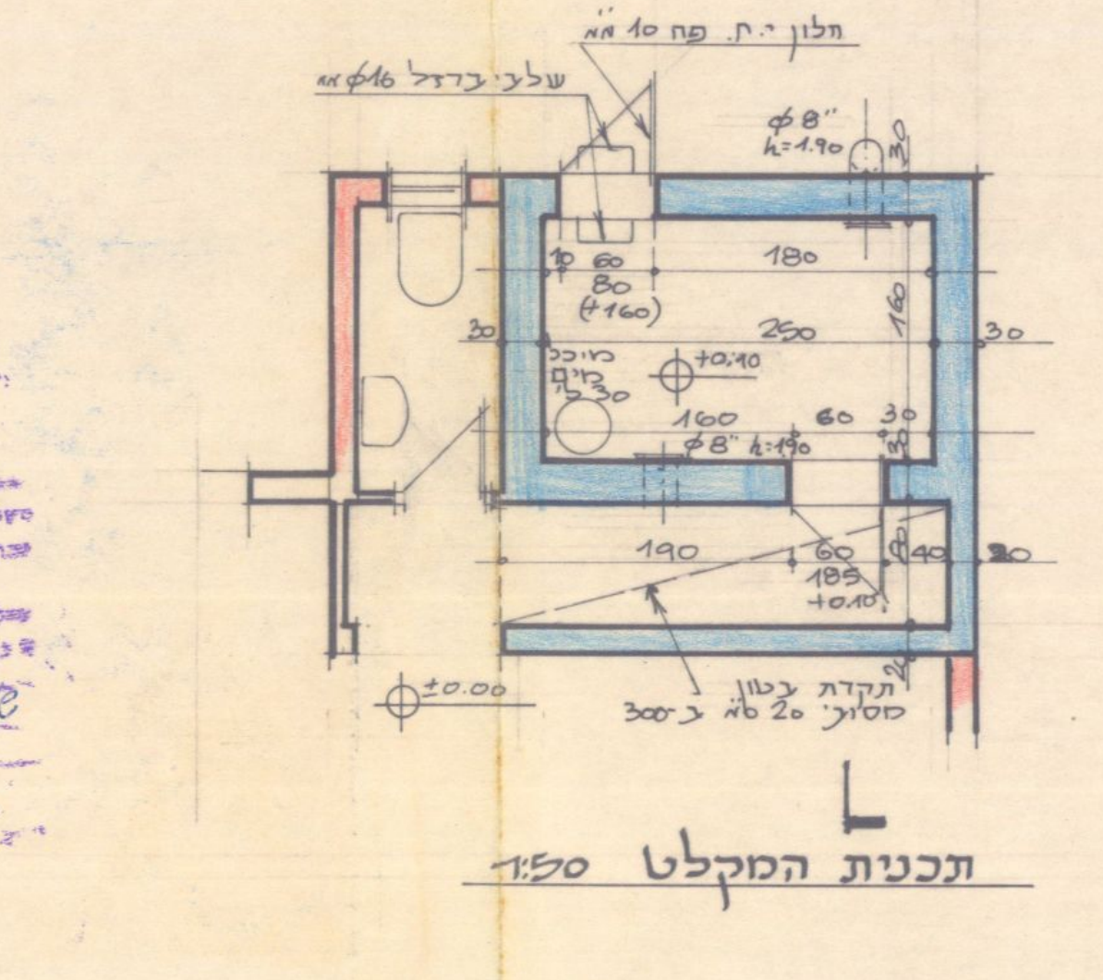

תכנית המקלט 1:50

הוראות ביצוע למקלט על-קרקעי

בטון רזה ב-150. תשתית בטון מתחת לרצפה.

בטון המקלט ב-300 - לפי התקן הישראלי 118 שנבדק ע"י מכון התקנים הישראלי או מוסד מוסמך אחר.

פלדת הזיון לפי תקן ישראלי ~~לפי, 580, 893, 739,~~ כמפורט במפרט הכללי למקלטים (58)

~~לפי המפורט במפרט הכללי למקלטים (56).~~

על הקבלן / המבקש להזמין את המהנדס האחראי על ביצוע השלד ולקבל אישור לביצוע כל שלבי המקלט.

~~עבודות הבידוד יש לבצע בהתאם למפרט הכללי למקלטים (58).~~

יש להזמין את המפקח מטעם הרשות המקומית לבדיקת שלבי בניית המקלט.

על הרשות המקומית להקפיד על מסירתה לועדה המקומית תצהיר של האחראי לביצוע השלד - בהתאם לקובץ התקנות ~~8392~~ 3892 מיום 21.9.78 (חוק התכנון והבניה תשכ"ה - 1965, תקנות בדבר תצהיר על הקמת שלד מקלט).

יש להזמין בדיקה באמצעות מכון התקנים לפי מפמ"כ מס' 20 - אינסטלציה כמתחייב מ-ה"ח 4111 מאפריל 1980.

סוף מסמך

הועדה המקומית לתכנון ולבניה [illegible]
מס' 61 20.1.87
המהנדס העיר
תאריך 19-12-1986

מפקדת ראש הג"א — ענף הנדסה ומיגון
את הבטון, פלדת הזיון, החסימה נגד מים ורטיבות, הגנת הקירות, המסגרות, המתקנים התברואתיים והחשמליים, הניקוז, הציפוי והצביעה של הקירות והסימונים יש לבצע לפי תקנות ההתגוננות האזרחית והמפרט הכללי למקלטים פרק 58 (1981). הקבלן חייב להחזיק תכנית מאושרת של המקלט באתר הבניה עד לסיום הבניה.
0884

תיק בנה ביתך 24240
9.9.86

אישור רשות מוסמכת מטעם ראש הג"א
התכנית נבדקה ונמצאה מתאימה לדרישות תקנות ההתגוננות האזרחית (מפרטים לבנית מקלטים), לבנית מקלט ציבורי/עורפי
תאריך 9.9.86
אישור מס' 04-1159
האישור בתוקף עד תאריך 9.9.87