20 תכנית מתוקנת לתנאים הירוקים

מינהל ההנדסה תל-אביב-יפו
2 -03- 1983
נתקבל באגף הרישוי
רישום

חוק התכנון והבניה, תשכ"ה—1965
תקנות התכנון והבניה (בקשה להיתר, תנאיו ואגרות), תש"ל—1970

טופס 2 (תקנה 2(א))

תיק מס' 27987

מפרם

הועדה המקומית לתכנון ולבניה ת"א

א· תיאור הבנין

מגרש	תכנית מיתאר מקומית או מפורטת	חלקה	גוש	מס'	הרחוב	1. המקום
	2215	44	6135	36א	ששון	ת"א

מס' הטלפון	המען	השם	
	רח' ששון 36א שכונת התקוה ת"א	יוסף-פור ראשה ותבורה	2. המבקש
		ה.מ.י	3. בעל הנכס
03-479858	קהילת סופיה 10 ת"א	אבינעם לוין - אדריכל	4. עורך הבקשה
03-250548	ה' באייר 48 ת"א	לינגר, הורוביץ, בנק	5. המהנדס האחראי לביצוע השלד

6. אזור הבניה: ☒ מגורים ☐ מסחר ☐ תעשיה ☐ בנין ציבורי ☐ חקלאי ☐ ……………

7. שטח המגרש/החלקה: 196 מ"ר. אחוז הבניה המותר: 140 %

8. מטרת הבנין: ☒ מגורים ☐ הארחה ☐ עסקים ☐ תעשיה ☐ חקלאי ☐ ציבורי ☐ ……………

9. מהות הבנין ותכליתו: תוספת בקומה לבית מגורים קיים

10. תיאור העבודה המוצעת: ☐ בנין חדש ☒ תוספת לבנין קיים ☐ הריסה ☐ תיקונים ☐ שינוי בבנין ☐ …………… ☐ שינוי בשימוש ממטרה: ……………למטרה: ……………

11. האם הבניה היא בעד: ☐ משרד ממשלתי ☐ הרשות המקומית ☐ הסוכנות היהודית

ב· היקף הבניה

קומה	קיים	מוצע	סך הכל	אחוז הבניה	עד 45 מ"ר	עד 65 מ"ר	עד 90 מ"ר	מעל 90 מ"ר	עסק ; הארחה ; וכו'	ציבורי	שונות	מס' חדרים קיים	מס' חדרים מוצע
					מגורים בדירות								
1	2	3	4	5	6	7	8	9	10	11	12	13	14
מרתף													
הכניסה הקובעת לבנין	68.36	7.58	75.94	39									
א		28.33	28.33	15									
ב													
ג													
ד													
ה													
ו													
ז													
חדרי מדרגות													
בניני עזר	(4.90)		(4.90)	2.5									
סך הכל	68.36	35.91	109.17	56.5%									

הגובה המסומן: של הבנין העיקרי ……………מ"ק. של בנין עזר ……………מ"ק.

מינהל ההנדסה אגף הרישוי העתק מאושר חתימה

ג· השימוש בבנין

1. הבניה המוצעת למגורים

דירות בנות:	שטח כל דירה מ"ר	מספר דירות מכל סוג	שטחים—מ"ר כל הדירות	מזה רצפות חדרי דיור בלבד, ושרפסות מקורות	רצפות חדרי שירות ושרותים בלבד	רצפות של מרפסת בלתי מקורות	מספר החדרים דיור	מטבחים	אמבטיות	בתי שימוש	אחרים
1	2	3	4	5	6	7	8	9	10	11	12
חדר אחד											
2 חדרים											
3 חדרים											
4 חדרים											
5 חדרים											
6 חדרים											
7 חדרים ויותר											
חדרים נוספים לדירות קיימות											
בניני עזר											
סך הכל											

נסרק

---

2. הבניה הקיימת והמוצעת לתעשיה ולמלאכה

פרטים	קיים שטח	קיים גובה	קיים נפח	קיים % הבניה	מוצע שטח	מוצע גובה	מוצע נפח	מוצע % הבניה	סך הכל שטח	סך הכל נפח	סך הכל % הבניה	הערות
1	2	3	4	5	6	7	8	9	10	11	12	13
אולמי מלאכה												
משרדים												
חדרי שירות												
סככות												
בניני עזר												
חדרי מדרגות												
סך הכל												

3. הבניה המוצעת למטרות אחרות (הארחה, עסקים ומשרדים, בניני ציבור, בניני משק חקלאי, מטרות שונות).

השימוש המיועד	שטחים—מ"ר סך הכל מ"ר	מזה חדרים	מזה אולמות	מזה אחסנה	מזה חדרי שירות	מספר חדרים, אולמות וכו' חדרים	אולמות	אחסנה	חדרי שירות
1	2	3	4	5	6	7	8	9	10
בניני עזר (למעט אלה המפורטים ב"ג(4))									

4. חלקי בנין אחרים — הבניה המוצעת, שטח במ"ר.

חדרי מדרגות	מרפסות שלא נכללו לעיל	מעליות	חדרי הסקה	חדרי כביסה	מקלטים	קומת עמודים מפולשת	מחסנים	מוסכים	בניני עזר נוספים	סך הכל
1	2	3	4	5	6	7	8	9	10	11
(7.58)							(4.90)			

ד· חומר הבניה

קירות חיצוניים	☐ בטון מזוין	■ לבני בטון או בלוקים	☐ לבני סיליקט	☐ לבנים שרופות	☐ אבן טבעית
	☐ אבן מלאכותית	☐ איטונג	☐ עץ	☐ ברזל	☐ חמרים אחרים
תקרות	■ בטון מזוין	☐ עץ	☐ חומר אחר……………		
גג	■ בטון מזוין	☐ רעפים	☐ אסבסט	☐ פח	☐ חומר אחר……………

ה· גדרות קיימות 5 מ"א מוצעות 25 מ"א

ו· מקרא

בטון או בטון מזוין	🟦	אבן	☐	עץ	☐	איטונג	☐
בלוקים או לבנים מבטון	🟥	סיליקט או לבנים אדומות	☐	חומר אחר	☐	להריסה	🟨

הערות:

הנני מאשר כי הנתונים הנ"ל נכונים

תאריך______ חתימת המבקש______ חתימת עורך הבקשה______

חתימת המהנדס האחראי לביצוע השלד לינגר א. חתימת בעל הנכס יוסף פור משה ותבורה

לשימוש הועדה המקומית בלבד	מס' ההיתר	תאריך ההיתר	תאריך התחלת הבניה	תאריך גמר הבניה

אישורים של רשויות חוץ:

חתימת הועדה המקומית

95 5

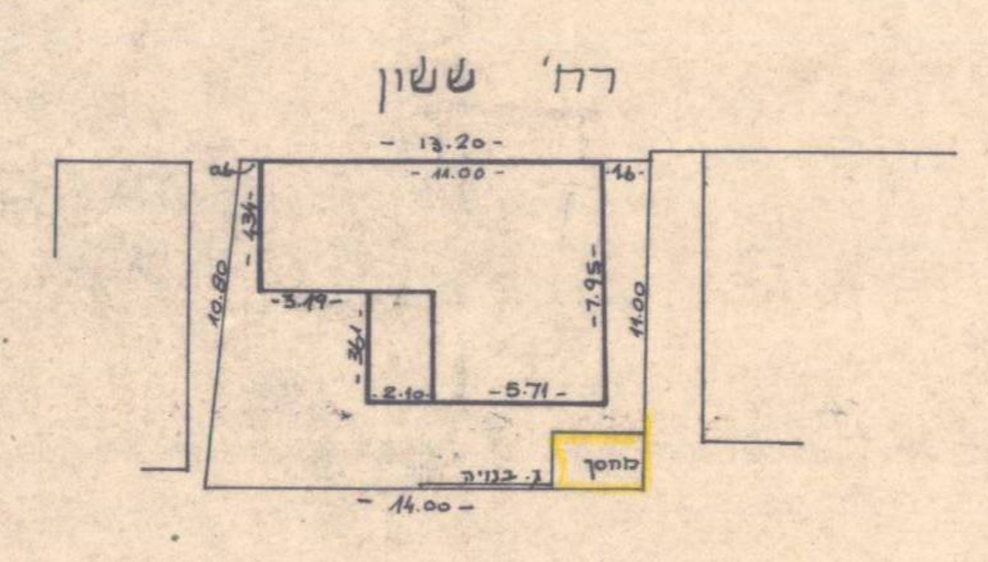

מפה מצבית ק.מ. 1:250

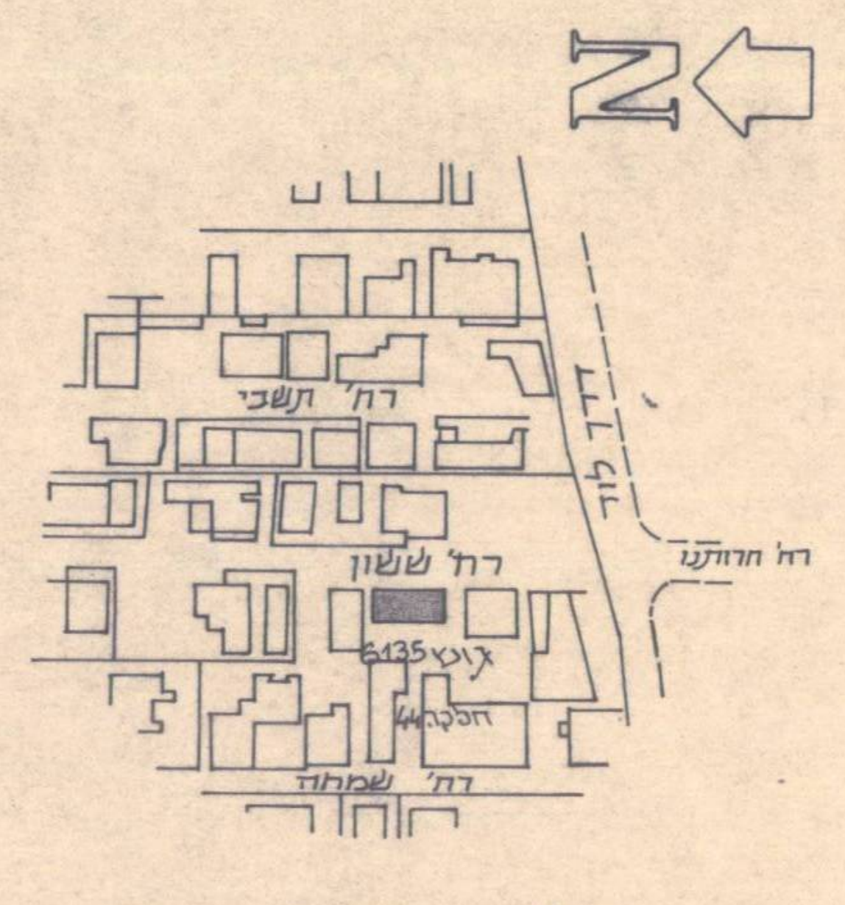

תרשים הסביבה ק.מ. 1:1250

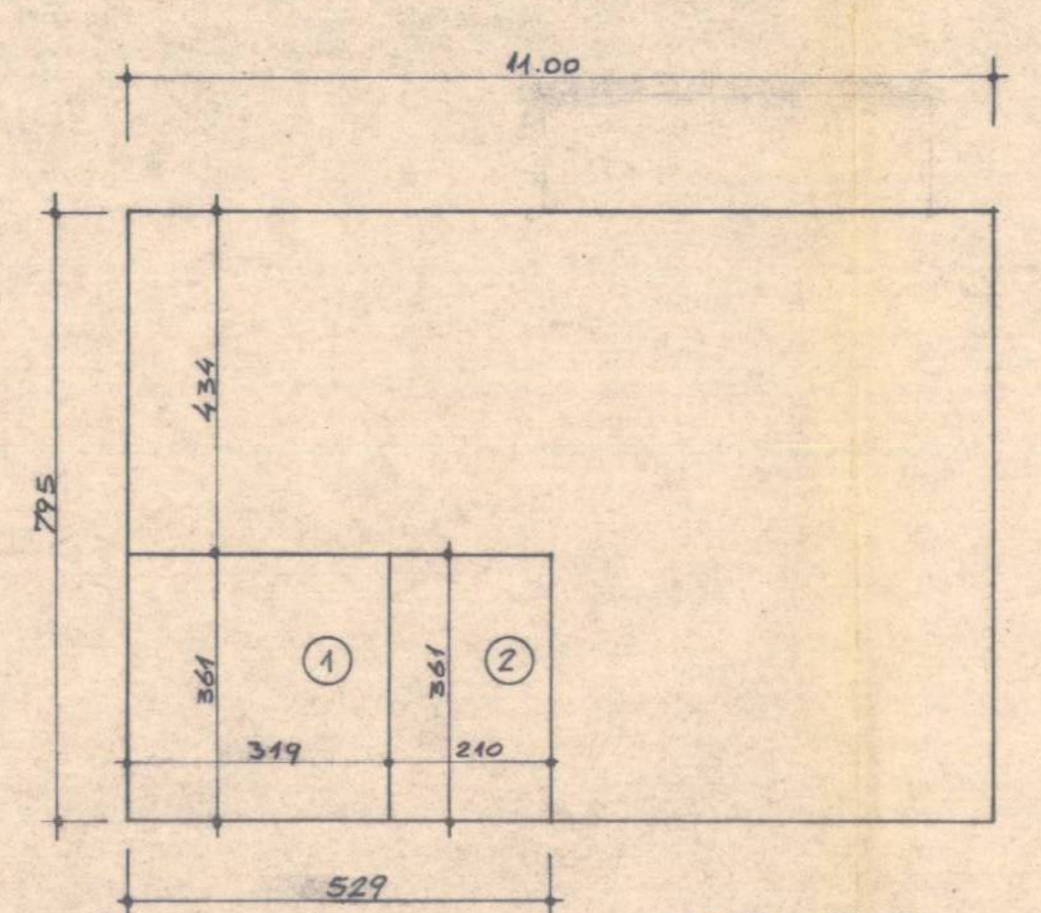

קומת קרקע

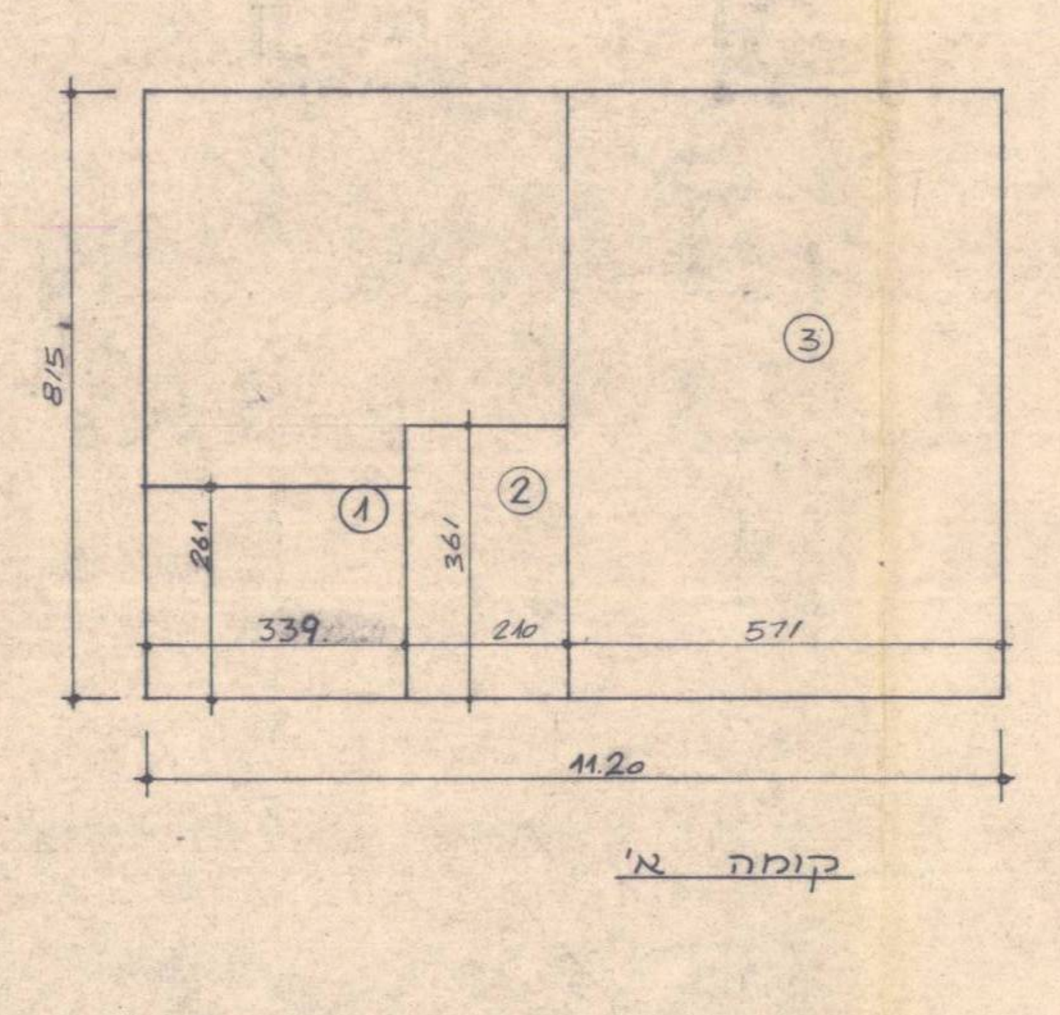

קומה א'

חישוב שטחים

קומת קרקע:
שטח המסגרת 87.45 = 7.95 × 11.00
הורדות
1. חצר 19.09 = 3.61 × 5.29
סה"כ שטח קיים: 68.36
תוספות
2. חדר מדרגות 7.58 = 3.61 × 2.10
סה"כ שטח קומת קרקע 75.94 מ"ר

קומה א':
שטח המסגרת 91.28 = 8.15 × 11.20
הורדות
1. 8.84 = 3.39 × 2.61
2. מדרגות 7.58 = 3.61 × 2.10
3. מרפסת 46.53 = 5.71 × 8.15
סה"כ שטח קומה א' 28.33 מ"ר
סה"כ שטח שתי הקומות 104.27 מ"ר
מבנה עזר קיים 4.90 = 280 × 175
סה"כ שטח בנוי 109.17 מ"ר

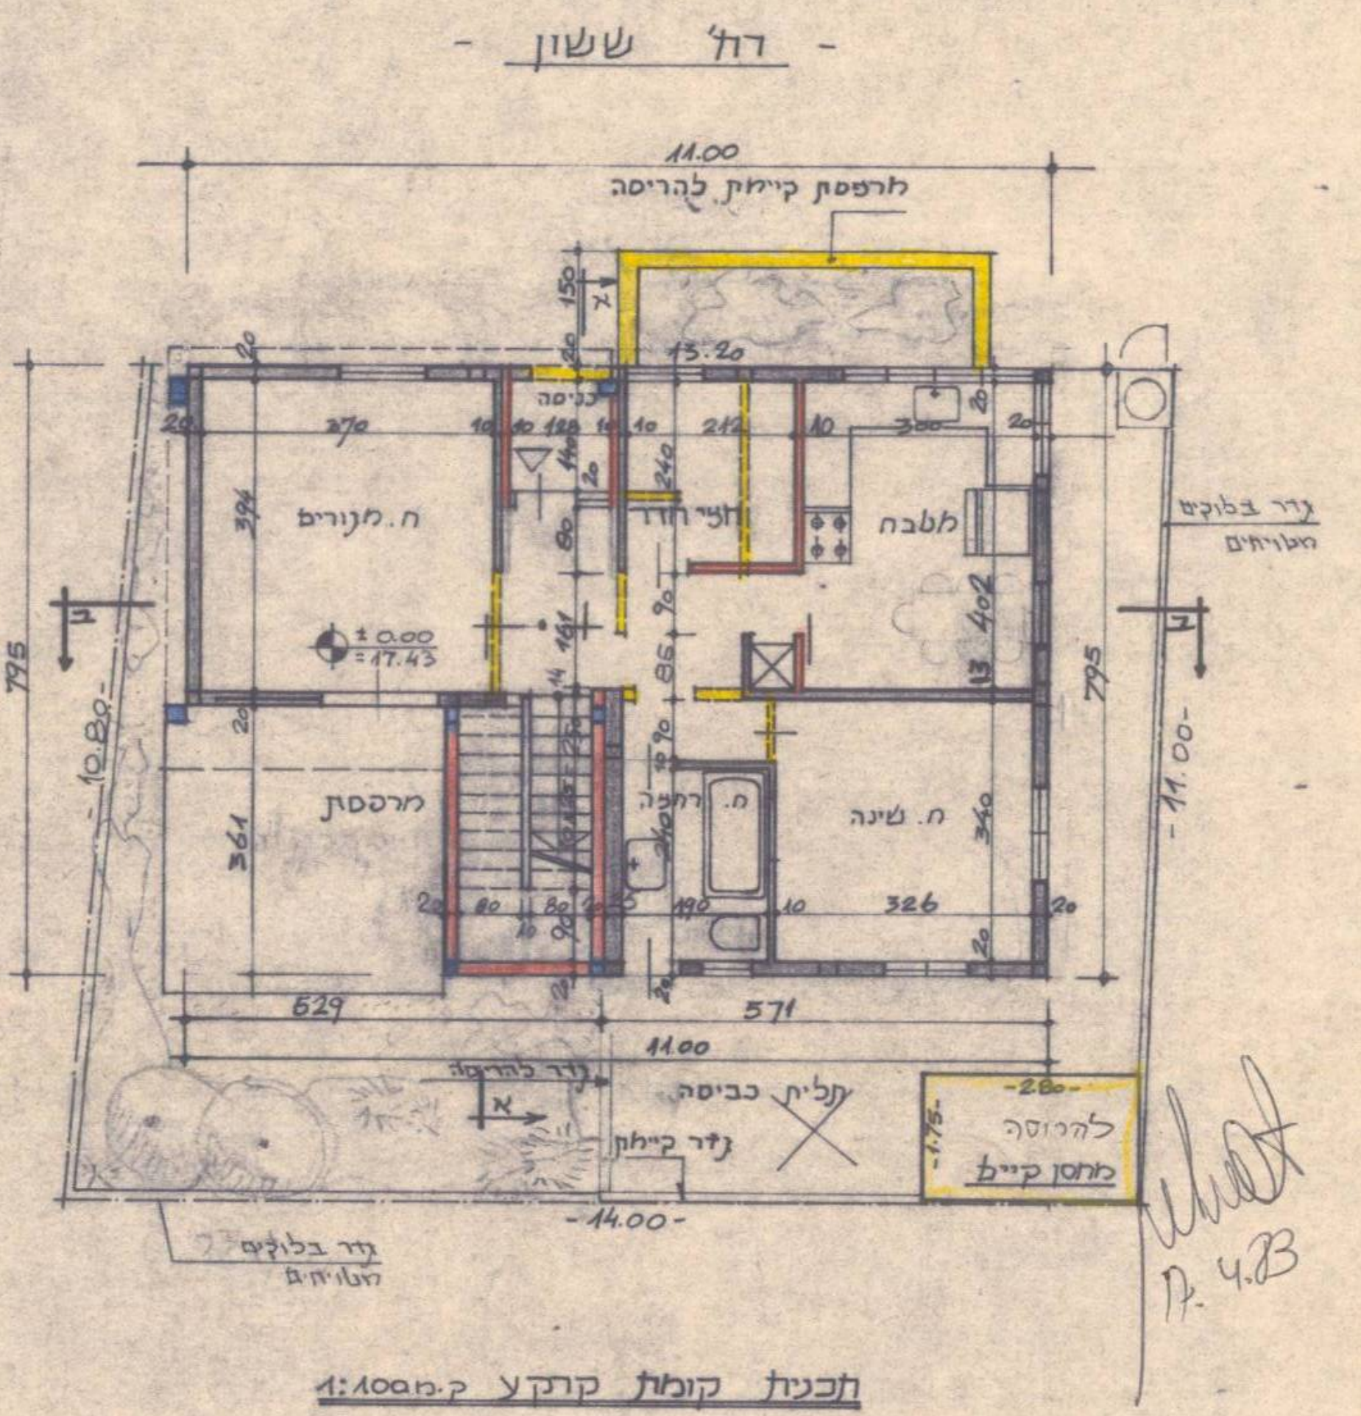

ת. 4.83

תכנית קומת קרקע ק.מ. 1:100

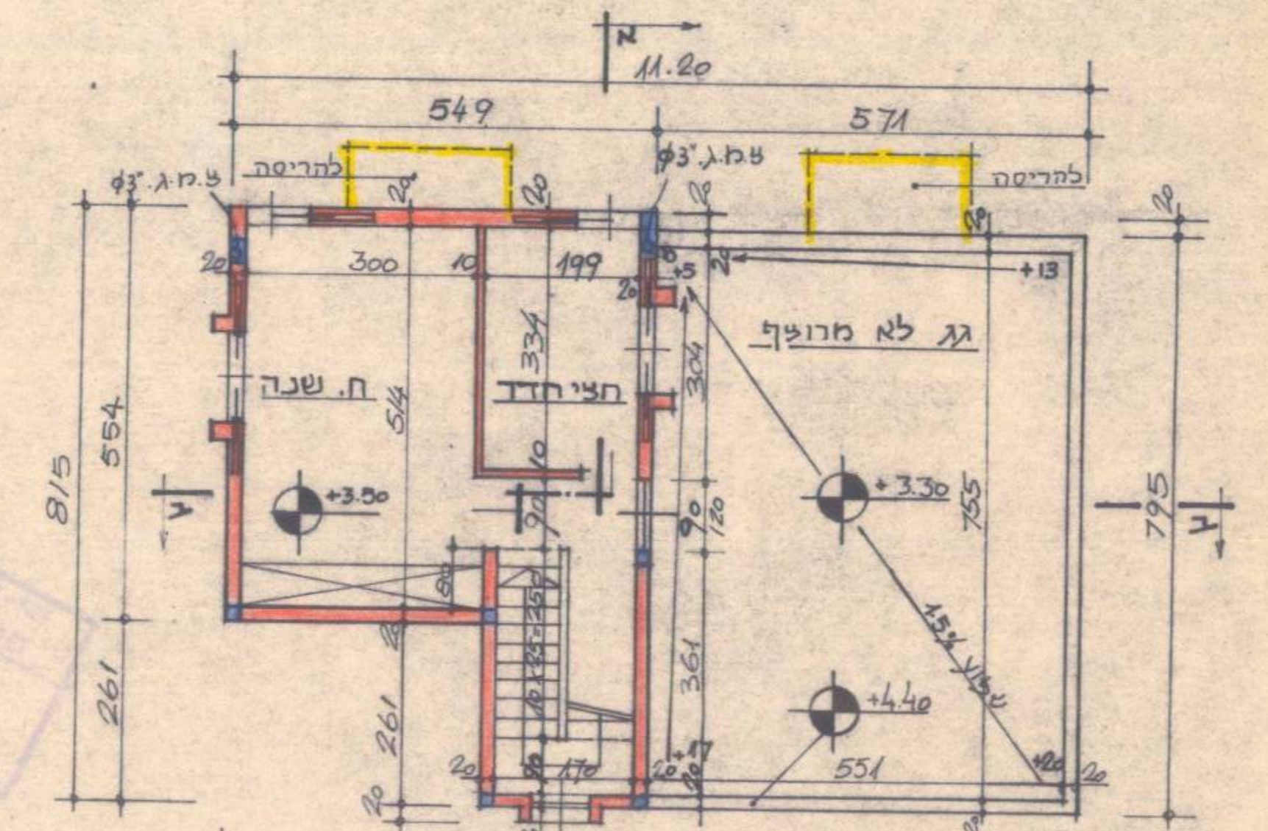

תכנית קומה א' 1:100

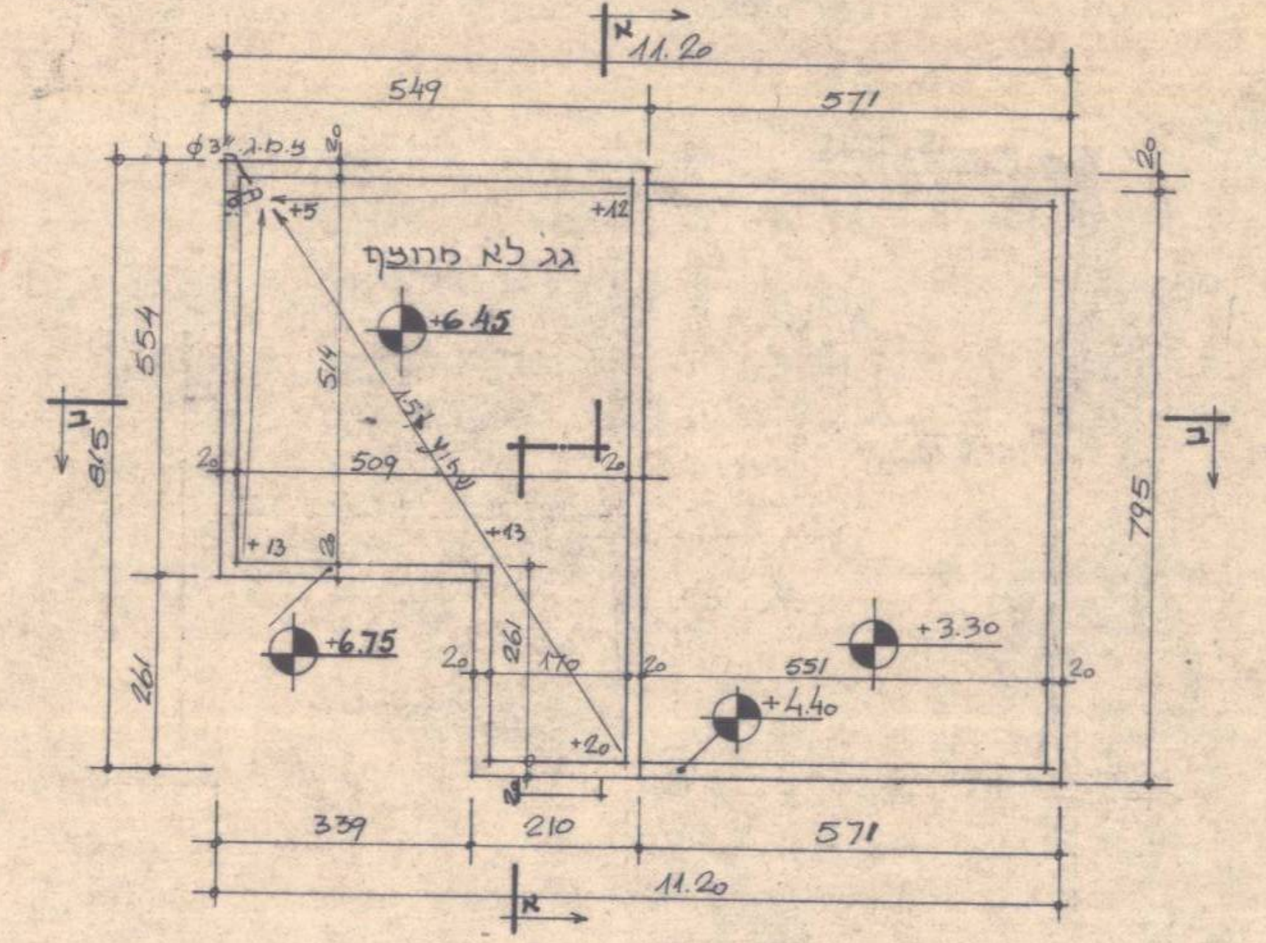

תכנית הגג 1:100

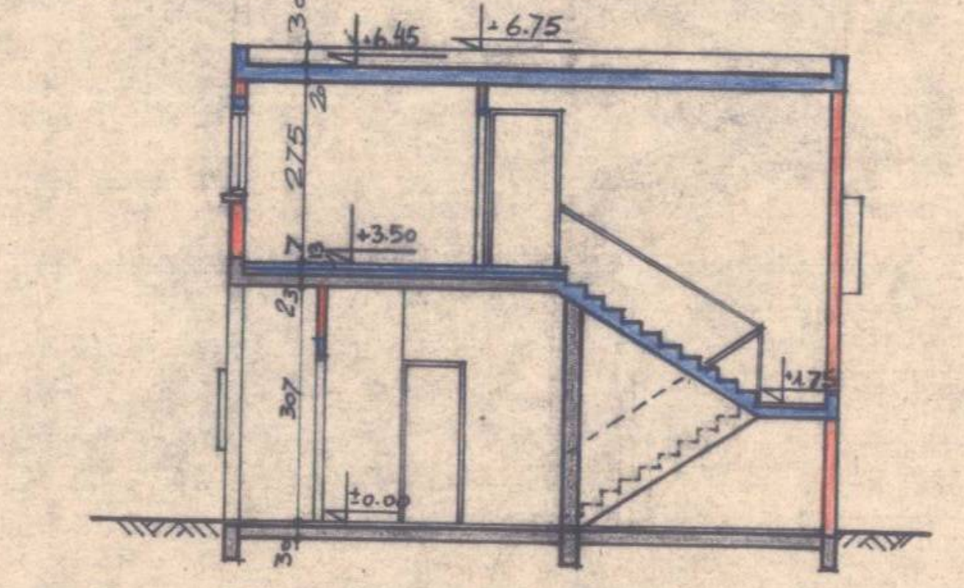

חתך א-א 1:100

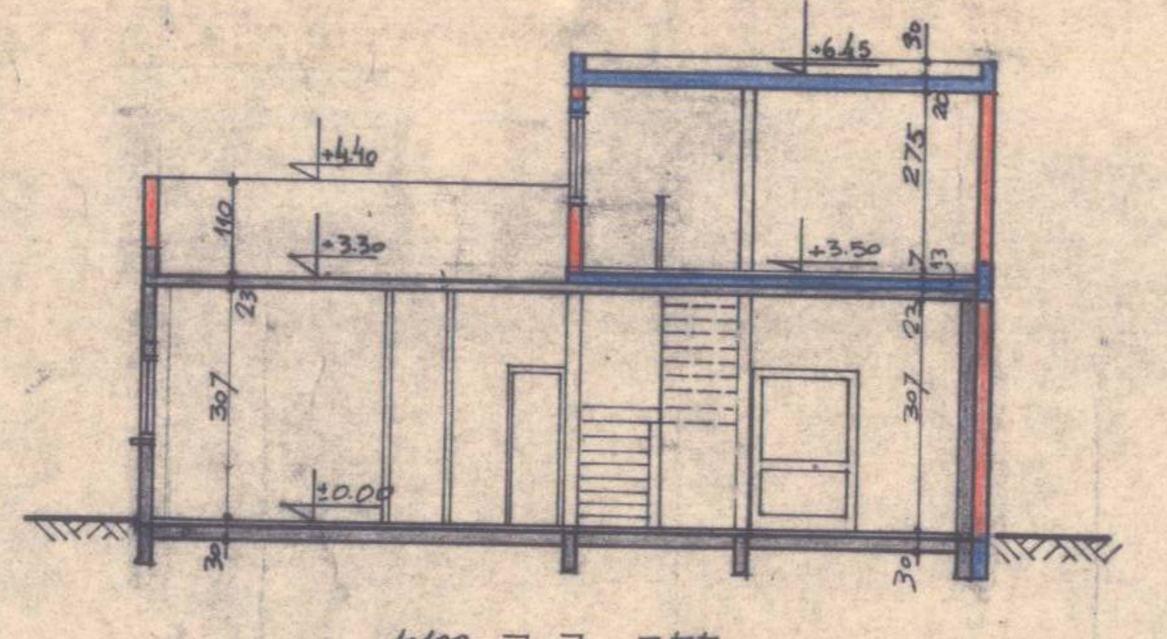

חתך ב-ב 1:100

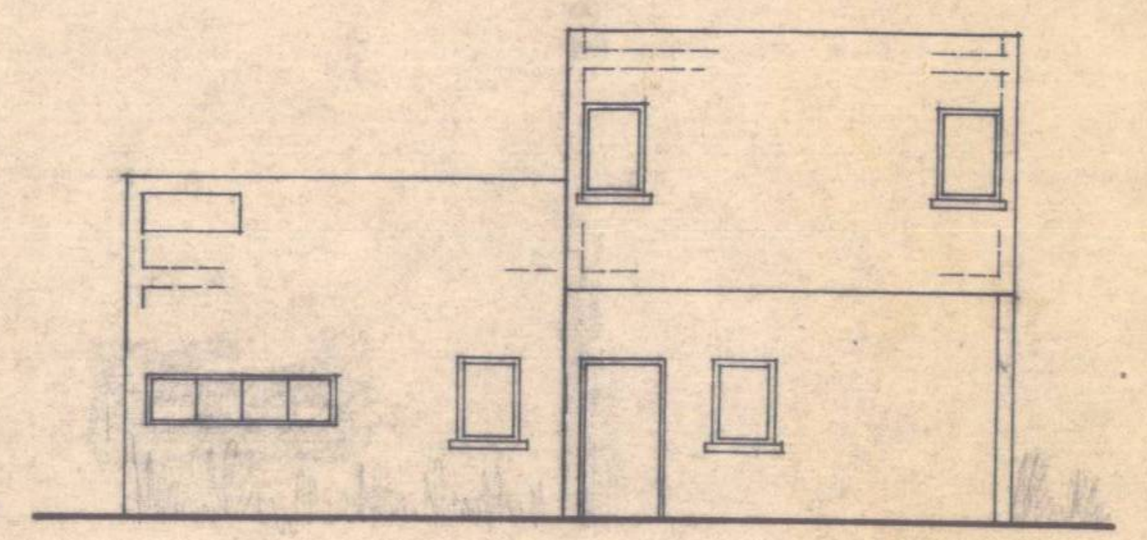

חזית מזרחית ק.מ. 1:100

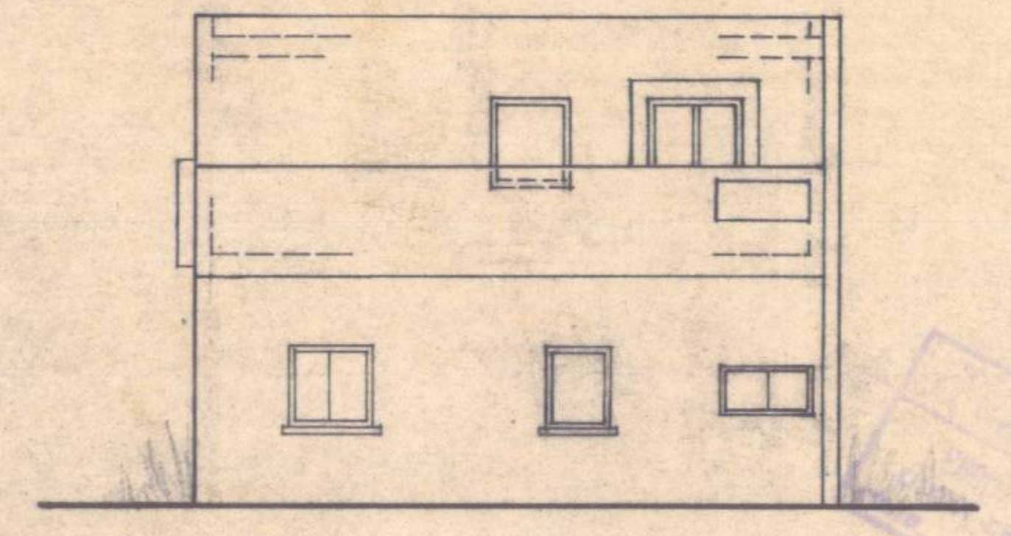

חזית דרומית 1:100

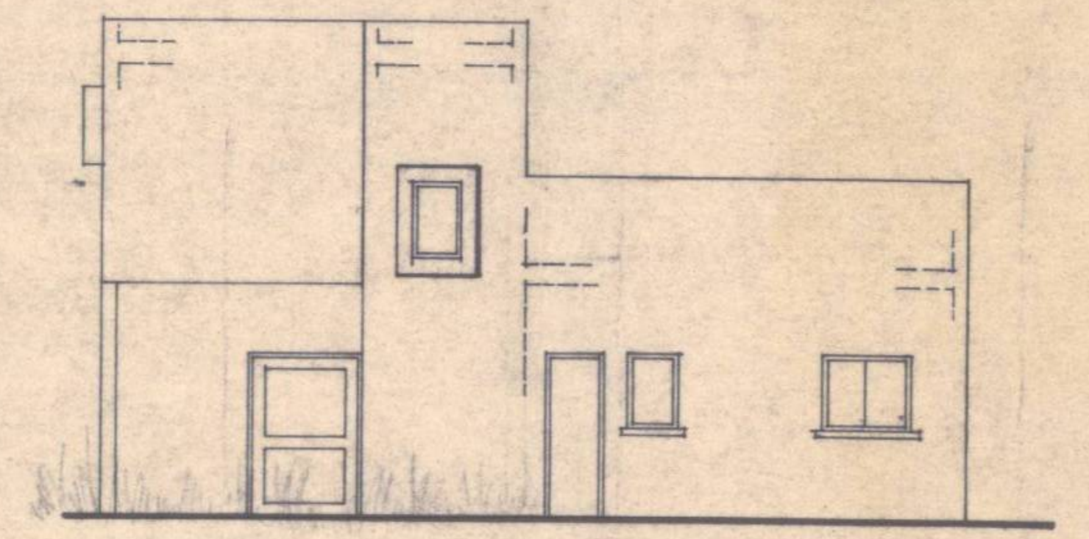

חזית מערבית ק.מ. 1:100

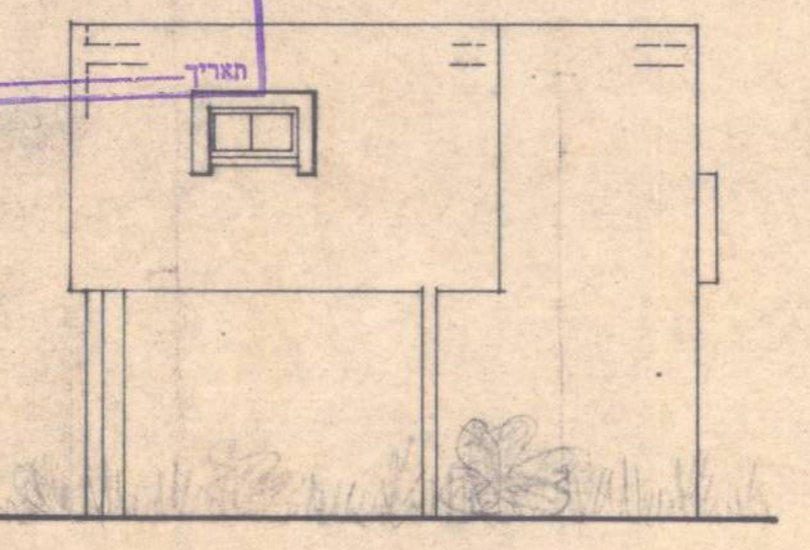

חזית צפונית 1:100

הועדה המקומית לתכנון ולבניה תל-אביב-יפו
בהתאם לסעיף 18 (ב) לתקנות התכנון והבניה (בקשה להיתר, תנאיו ואגרות) תש"ל-1970 הריני לאשר כי לטפח זה צורף היתר בניה/שימוש מס' 4/28
מיום, 5.7.83 ומהווה חלק בלתי נפרד ממנו.
מהנדס העיר
תאריך

סוף מסמך