22

004

עיריית תל-אביב-יפו
מינהל ההנדסה
2 -08- 1982
נתקבל באגף הרשוי
רישום
תיק

חוק התכנון והבניה, תשכ"ה—1965
תקנות התכנון והבניה (בקשה להיתר, תנאיו ואגרות), תש"ל—1970

טופס 2 (תקנה 2(א))

תיק מס' 27987

מיפרט

הוועדה המקומית לתכנון ולבניה ת"א 4/50

א' תיאור הבנין

1. הישוב	הרחוב	מס'	גוש	חלקה	תכנית מיתאר מקומית או מפורטת	מגרש
ת"א	ששון	36א	6135	44	2215	

	השם	המען	מס' הטלפון
2. המבקש	יוסף-פור ראשה ודבוה	רח' ששון 36א שכונת התקוה ת"א	
3. בעל הנכס	כנ"ל		
4. עורך הבקשה	אברהם לוין-אדריכל	קהלת מוסף 10 ת"א	03-479858
5. המהנדס האחראי לביצוע השלד	[illegible] הורוביץ	ה' באייר 48 ת"א	03-250548

6. אזור הבניה: ☒ מגורים ☐ מסחר ☐ תעשיה ☐ בנין ציבורי ☐ חקלאי ☐ ......

7. שטח: המגרש/החלקה: 196 מ"ר, אחוז הבניה המותר: 140 %

8. מטרת הבנין: ☒ מגורים ☐ הארחה ☐ עסקים ☐ תעשיה ☐ חקלאי ☐ ציבורי ☐ ......

9. מטרת הבניה המבוקשת: תוספת קומה לבנין מגורים קיים

10. תיאור העבודה המוצעת: ☐ בנין חדש ☒ תוספת לבנין קיים ☐ הריסה ☐ תיקונים ☐ שינוי בבנין ☐ ......
☐ שינוי בשימוש ממטרה: ...... למטרה: ......

11. האם הבניה היא בעד: ☐ משרד ממשלתי ☐ הרשות המקומית ☐ הסוכנות היהודית

ב' היקף הבניה

קומה	שטח כולל של בניה (מ"ר): קיים	מוצע	סך הכל	אחוז הבניה	מגורים בדירות: עד 45 מ"ר	עד 65 מ"ר	עד 90 מ"ר	מעל 90 מ"ר	עסק (הארחה וכו')	ציבורי	שונות	מס' חדרים: קיים	מוצע
1	2	3	4	5	6	7	8	9	10	11	12	13	14
מרתף													
הכניסה [illegible] לבנין	68.36	7.58	75.94	39									
א		28.33	28.33	15									
ב													
ג													
ד													
ה													
ו													
ז													
חדרי מדרגות													
בניני עזר	(4.90)		4.90	2.5									
סך הכל	68.36	35.91	109.17	56.5%									

עיריית תל-אביב-יפו
מינהל ההנדסה
מחלקת פקוח על הבניה
חבל מזרח
תכנית מס' 669
נבדקה ביום 06.06.82
מהנדס אזורי

להתאים לתכנית לפי [illegible]
22-7-82

הנפח המוצע: של הבנין העיקרי ...... מ"ק, של בנין עזר ...... מ"ק.

ג' השימוש בבנין

1. הבניה המוצעת למגורים

דירות בנות:	שטח כל דירה מ"ר	מספר דירות מכל סוג	כל הדירות	שטחים—מ"ר, מזה: רצפות חדרי דיור בלבד, והרפסות מקורות	רצפות חדרי שירות ופרוזדורים בלבד	רצפות של מרפסות בלתי מקורות	מספר חדרים: דיור	מטבחים	אמבטיות	בתי שימוש	אחרים
1	2	3	4	5	6	7	8	9	10	11	12
חדר אחד											
2 חדרים											
3 חדרים											
4 חדרים											
5 חדרים											
6 חדרים											
7 חדרים ויותר											
חדרים נוספים לדירות קיימות											
בניני עזר											
סך הכל											

נסרק

2. הבניה הקיימת והמוצעת לתעשיה ולמלאכה

סוג	קיים: שטח	גובה	נפח	% הבניה	מוצע: שטח	גובה	נפח	% הבניה	סך הכל: שטח	נפח	% הבניה	הערות
1	2	3	4	5	6	7	8	9	10	11	12	13
אולמי מלאכה												
משרדים												
חדרי שירות												
סככות												
בניני עזר												
חדרי מדרגות												
סך הכל												

3. הבניה המוצעת למטרות אחרות (הארחה, עסקים ומשרדים, בניני ציבור, בניני משק חקלאי, מטרות שונות)

השימוש המיועד	סך הכל מ"ר	שטחים—מ"ר, מזה: חדרים	אולמות	אחסנה	חדרי שירות	מספר חדרים, אולמות וכו': חדרים	אולמות	אחסנה	חדרי שירות
1	2	3	4	5	6	7	8	9	10
בניני עזר (למעט אלה המפורטים ב־ג(4))									

4. חלקי בנין אחרים—הבניה המוצעת, שטח במ"ר

חדרי מדרגות	מרפסות שלא נכללו לעיל	מעליות	חדרי הסקה	חדרי כביסה	מקלטים	קומת עמודים מפולשת	מחסנים	מוסכים	בניני עזר נוספים	סך הכל
1	2	3	4	5	6	7	8	9	10	11
(7.58)							(4.90)			

ד' חומר הבניה

קירות חיצוניים	☐ בטון מזוין ■ לבני בטון או בלוקים ☐ לבני סיליקט ☐ לבנים שרופות ☐ אבן טבעית ☐ אבן מלאכותית ☐ איסוג ☐ עץ ☐ ברזל ☐ חמרים אחרים
תקרות	■ בטון מזוין ☐ עץ ☐ חומר אחר ......
גג	■ בטון מזוין ☐ רעפים ☐ אסבסט ☐ פח ☐ חומר אחר ......

ה' גדרות: קיימות 5 מ"א, מוצעות ...... מ"א

ו' מקרא:
▨ בטון או בטון מזוין
▨ בלוקים או לבנים מבטון
☐ אבן
☐ סיליקט או לבנים אדומות
☐ עץ
☐ חומר אחר
☐ איסוג
☐ להריסה

הערות: ......

הנני מאשר כי הנתונים הנ"ל נכונים

תאריך ...... חתימת המבקש ...... חתימת עורך הבקשה ......
חתימת המהנדס האחראי לביצוע השלד ...... חתימת בעל הנכס ......

מהנדסי בנין
רח' ה' באייר 48, תל-אביב

לשימוש הועדה המקומית בלבד	מס' ההיתר	תאריך ההיתר	תאריך התחלת הבניה	תאריך גמר הבניה

אישורים של רשויות חוץ:

חתימת הועדה המקומית

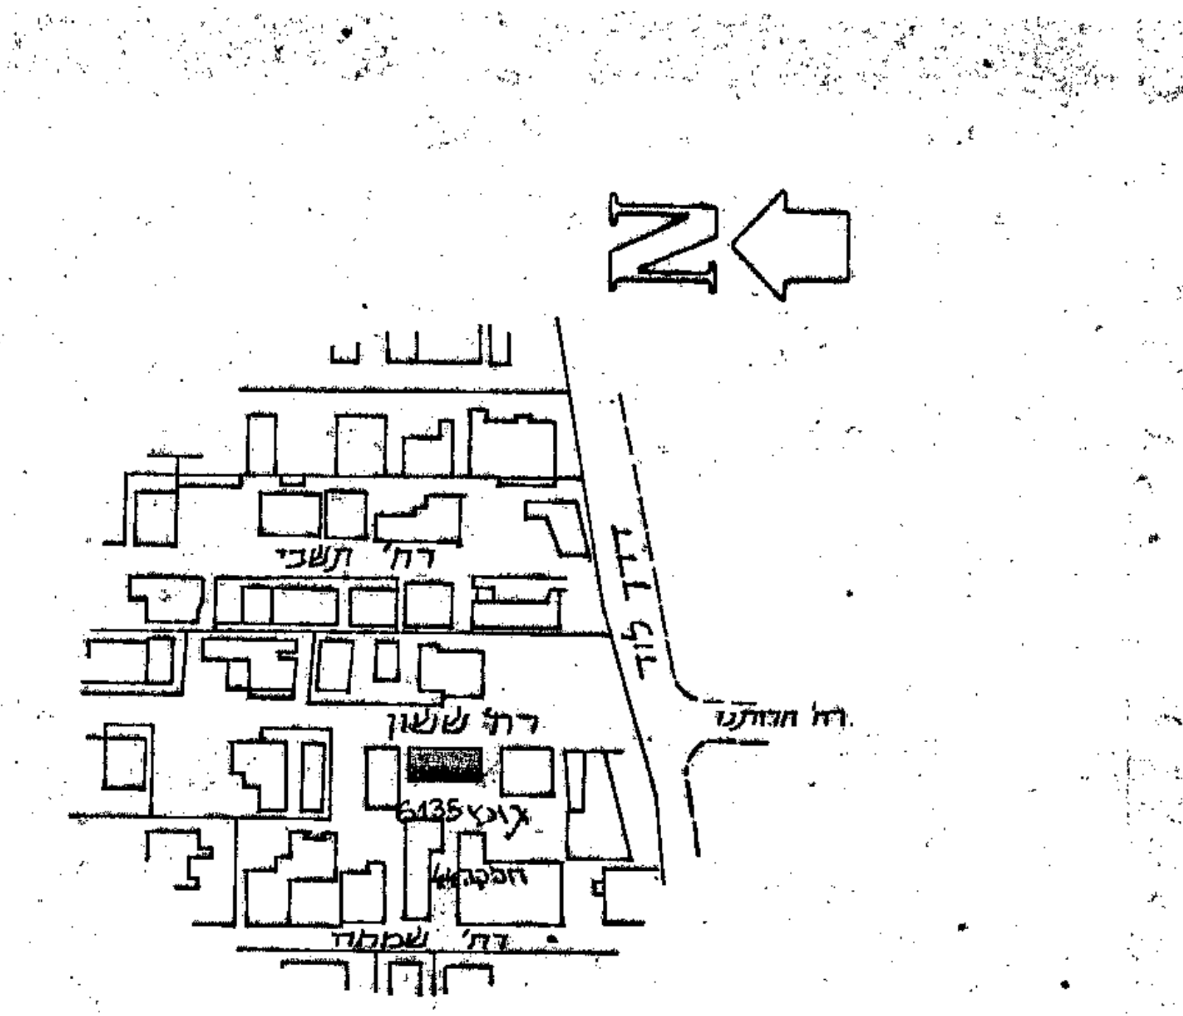
N
רח' תשבי
רח' חוכמה
רח' ששון
גוש 6135
רח' שמלה
דרך לוד
הסקה

תרשים הסביבה ק.מ. 1:1250

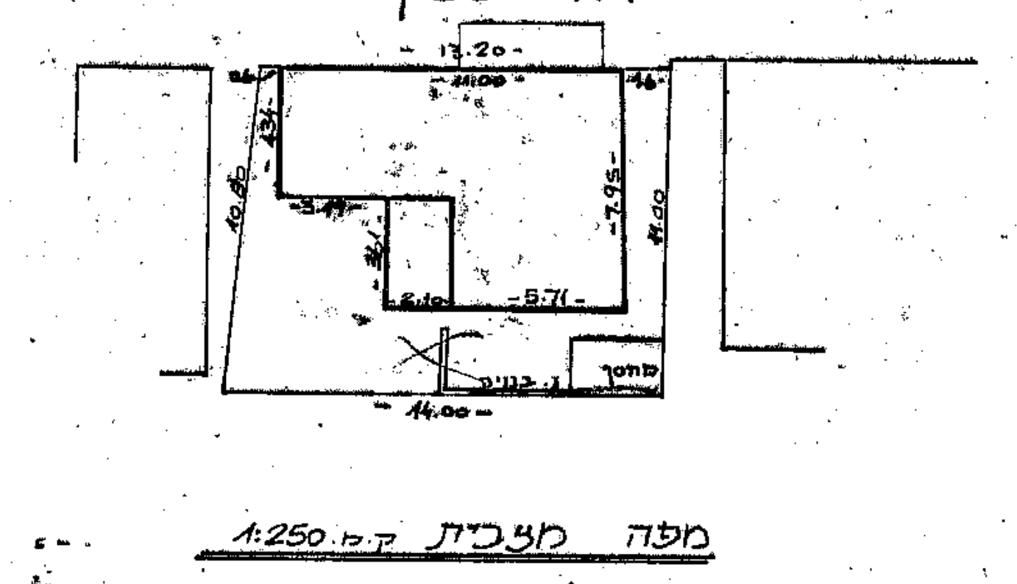
רח' ששון
13.20
11.00
10.80
7.95
8.00
14.00
מחסן

מפה מצבית ק.מ. 1:250

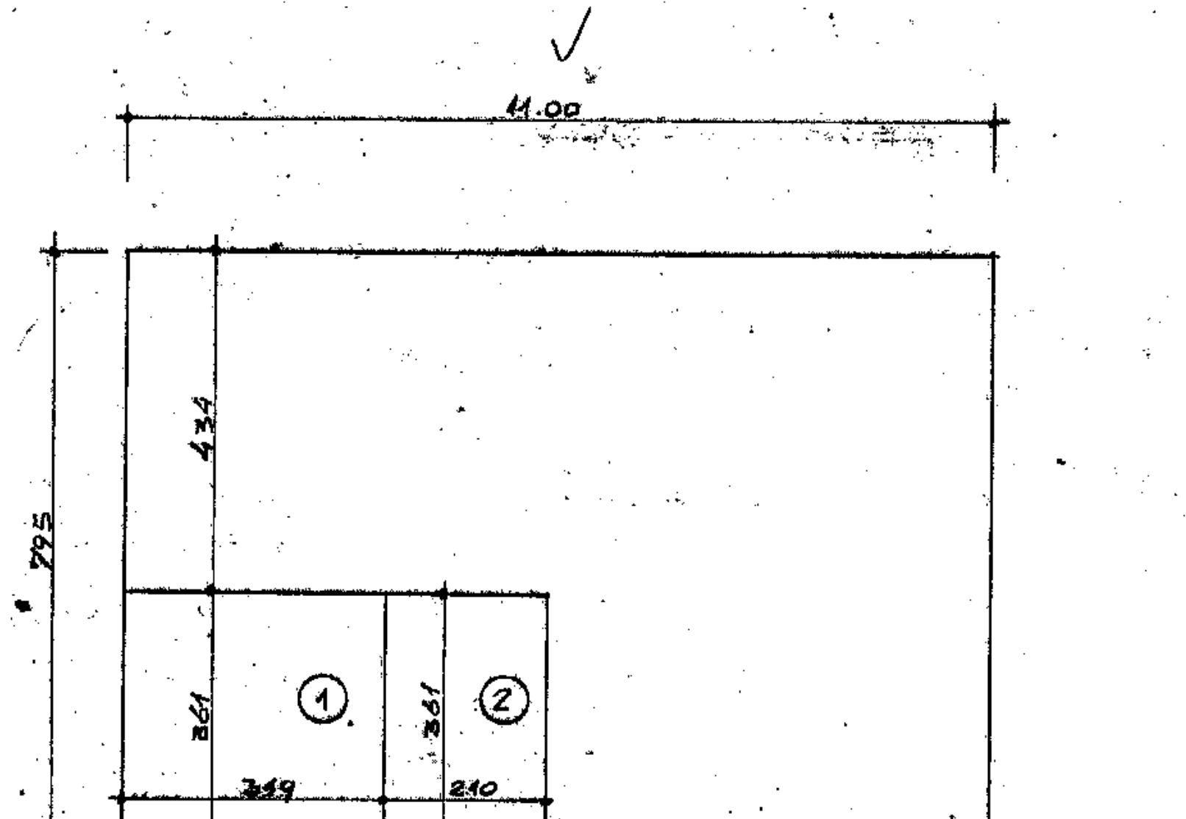
11.00
795
434
361
①
②
339
210
529

קומת קרקע

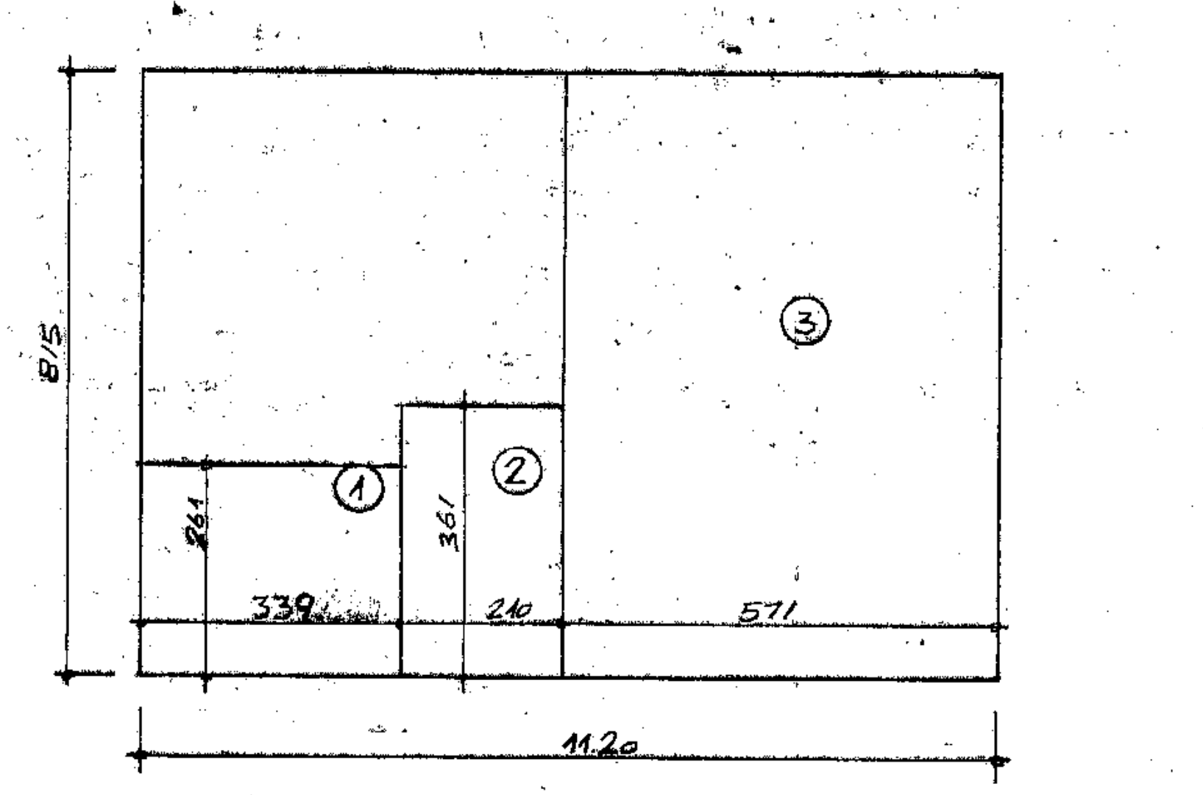
815
261
361
①
②
③
339
210
571
11.20

קומה א'

חישוב שטחים

קומת קרקע:
שטח המסגרת 87.45 = 7.95 × 11.00
הורדות
1. חצר ~~19.09 = 3.61 × 5.29~~
סה"כ שטח קיים: ~~68.36~~
תוספות
2. חדר מדרגות 7.58 = 3.61 × 2.10

סה"כ שטח קומת קרקע 75.94 מ"ר

87,44

87,45
11,51
75,94 = 76.

קומה א':
שטח המסגרת 91.28 = 8.15 × 11.20
הורדות
1. 8.84 = 3.39 × 2.61
2. מדרגות 7.58 = 3.61 × 2.10
3. מרפסת 46.53 = 5.71 × 8.15

סה"כ שטח קומה א' 28.33 מ"ר

סה"כ שטח שתי הקומות 104.27 מ"ר

מבנה עזר קיים 4.90 = 280 × 175

סה"כ שטח בנוי 109.17 מ"ר

~~87,44~~
~~28,33~~
~~115,77~~

ג' 110

87.45

עיריית תל-אביב-יפו
מינהל ההנדסה
מחלקת פקוח על הבניה
חבל מזרח
תכנית מס' 669
נבדקה ביום 06.06.82
מהנדס אזורי

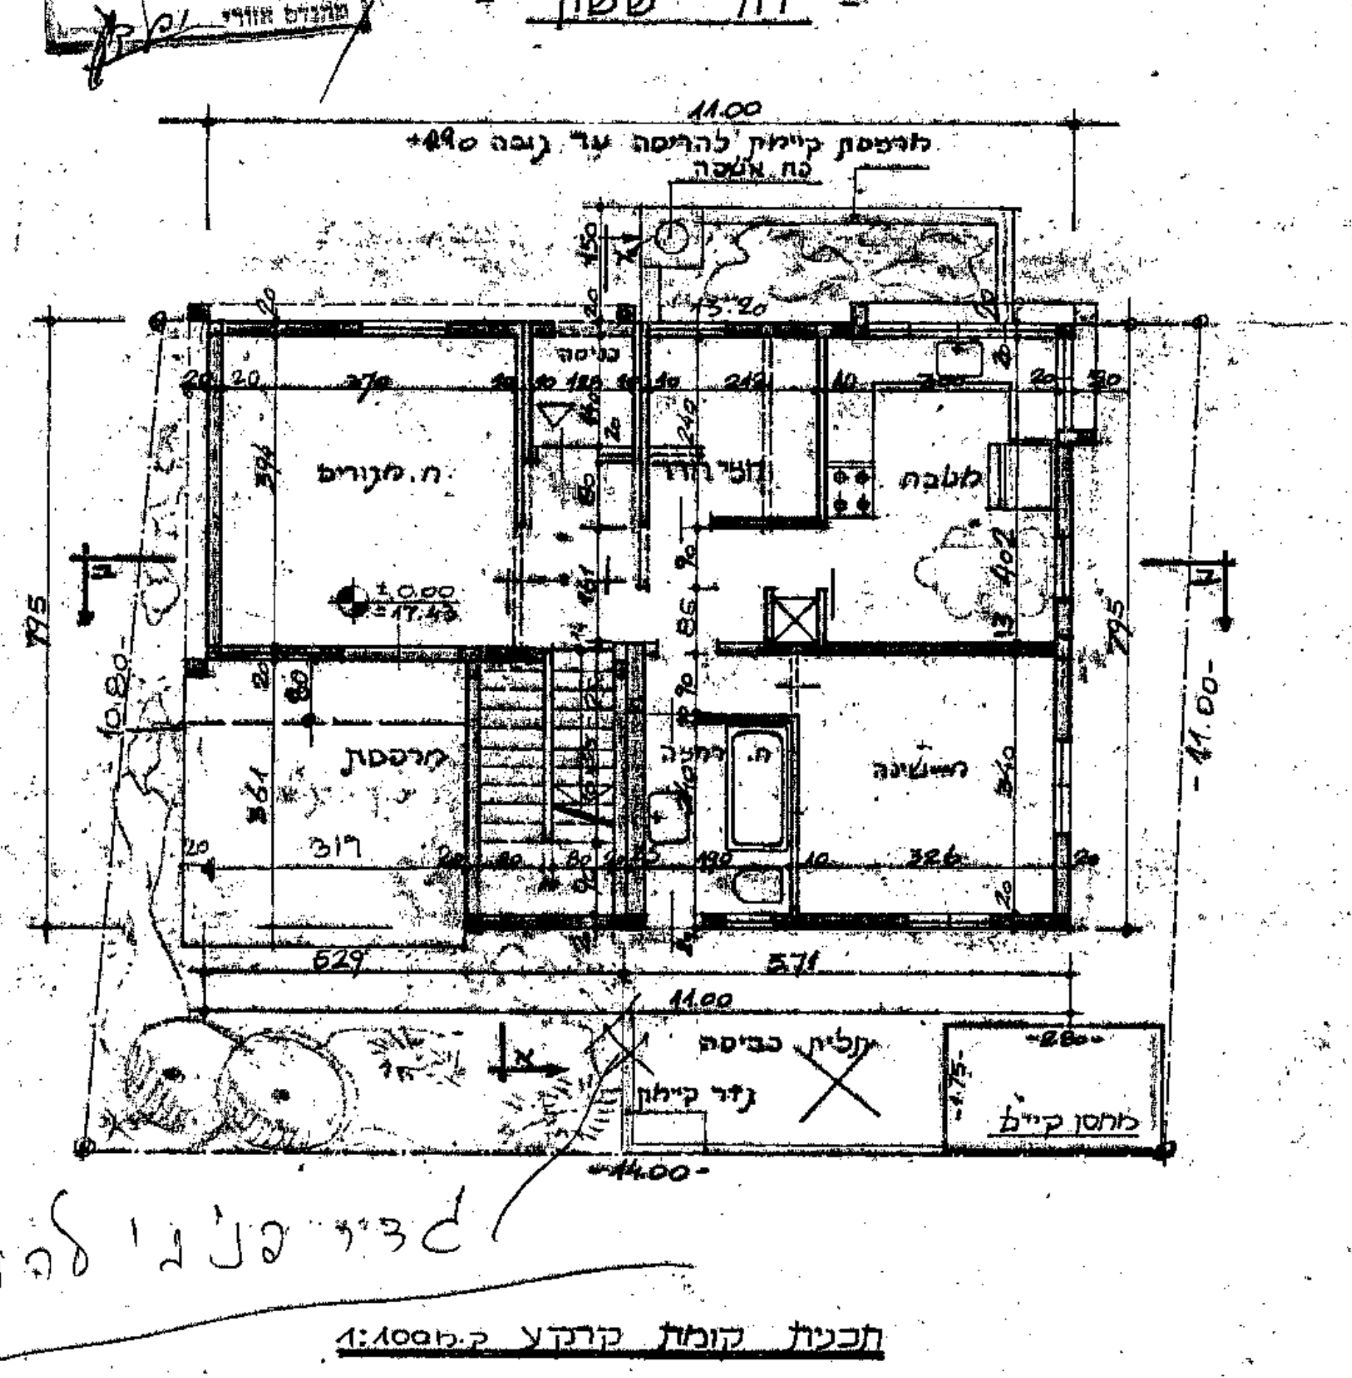
רח' ששון
11.00
מרפסת קיימת להריסה עד גובה 90+
גג מטבח
ח. מגורים
כניסה
מטבח
חצר
מרפסת
משפחה
מקלחת
תליית כביסה
גדר קיימת
מחסן קיים
629
571
14.00
795
11.00

לגדר פנ'גי להורס

תכנית קומת קרקע ק.מ. 1:100

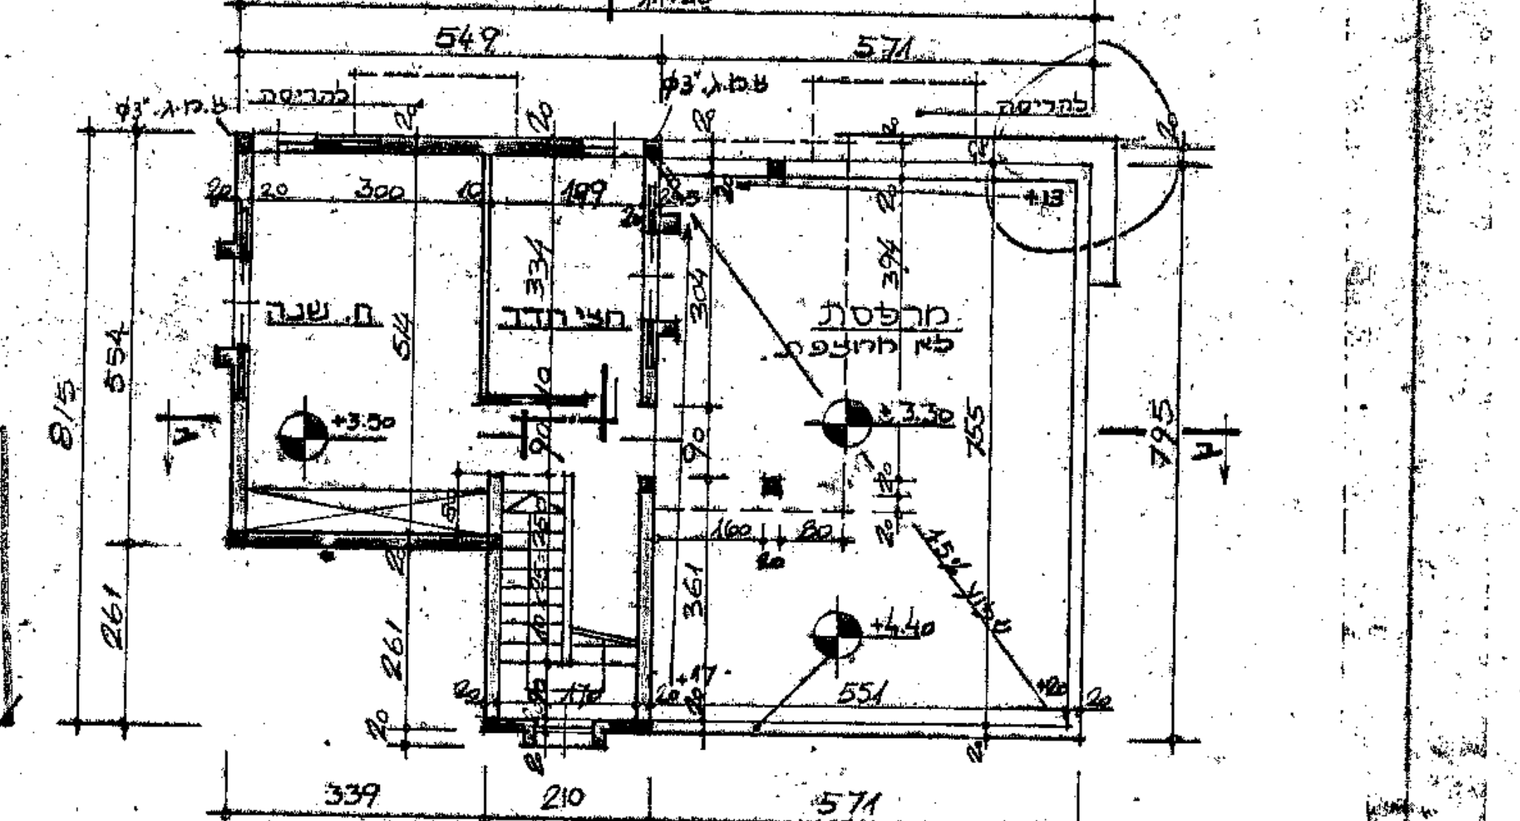
11.20
549
571
להריסה
ח. שנה
מרפסת
לא מקורה
מזרחה
+3.50
+3.30
+4.40
554
815
261
795
339
210
571

תכנית קומה א' 1:100

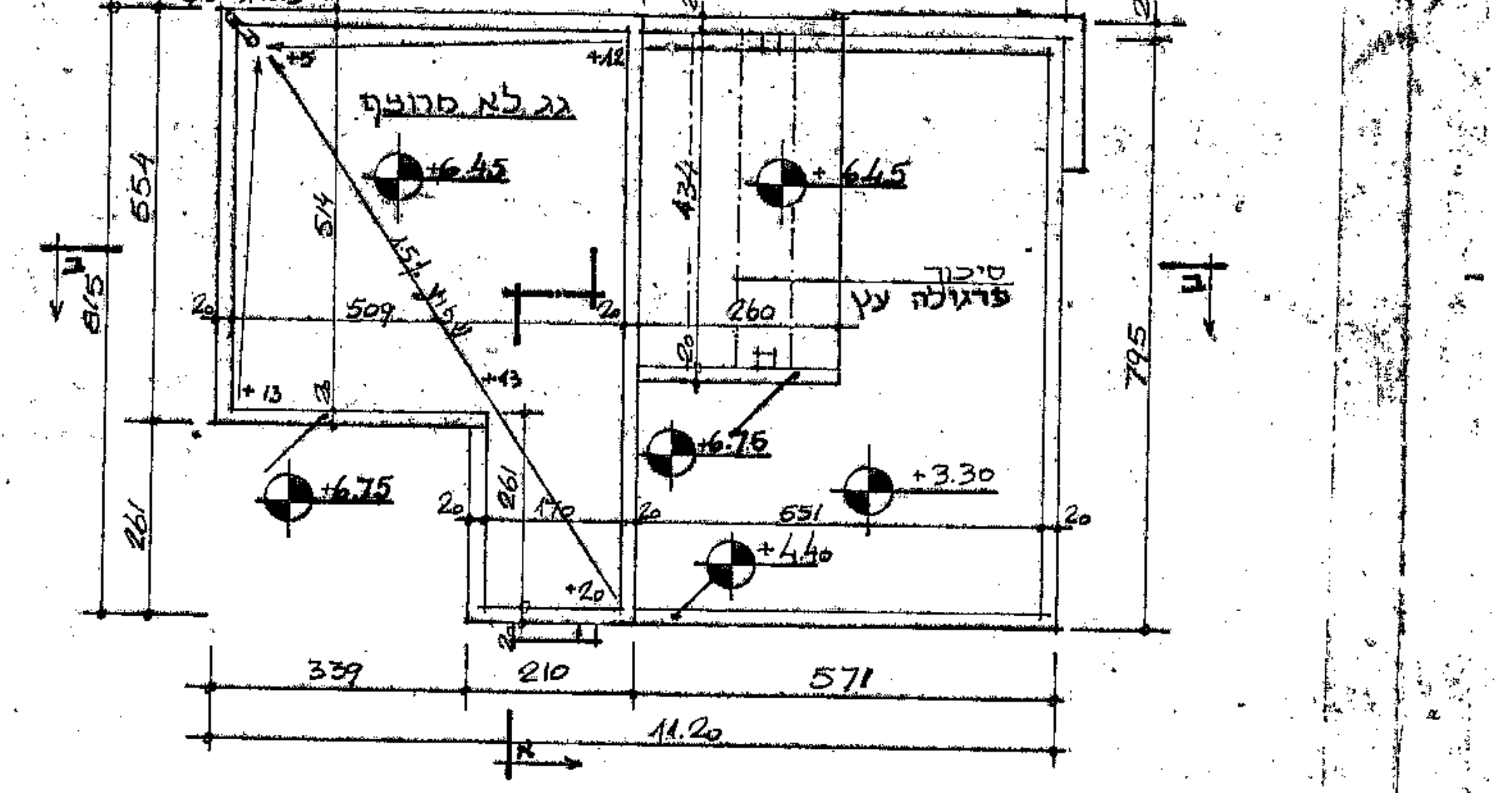
11.20
549
571
גג לא מרוצף
+6.45
+6.75
פרגולה עץ
+3.30
+4.40
554
815
261
795
339
210
571

תכנית הגג 1:100

עיריית תל-אביב-יפו
מינהל ההנדסה
מחלקת פקוח על הבניה
חבל מזרח
תכנית מס' 669
נבדקה ביום 06.06.82
מהנדס אזורי

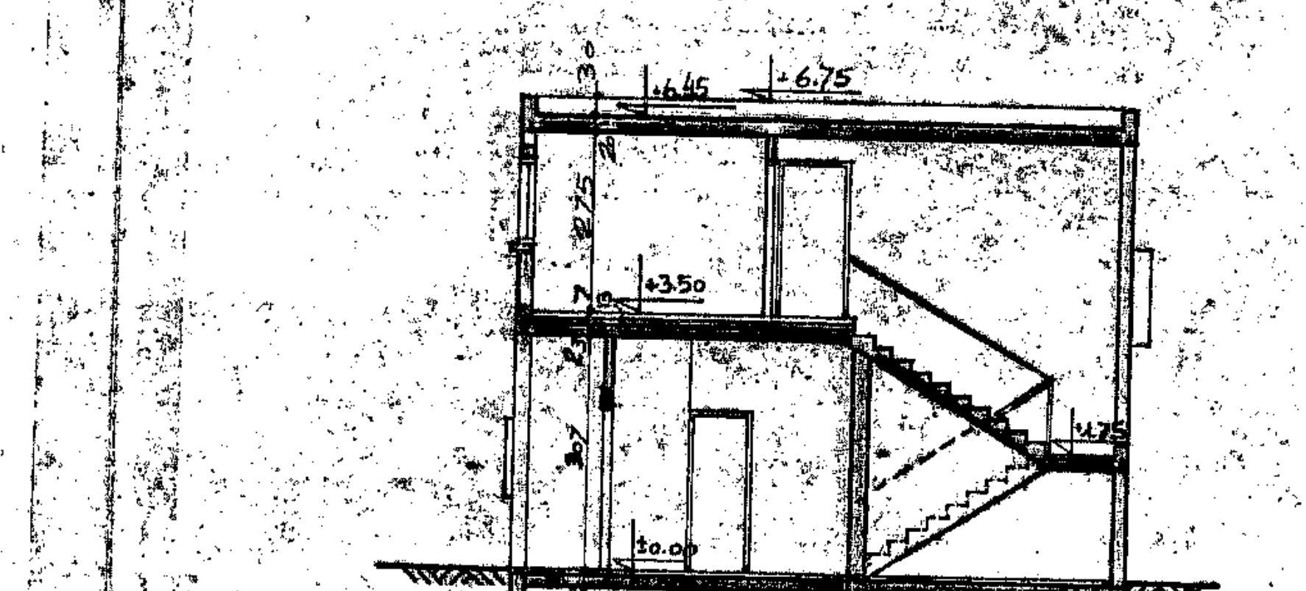
+6.45
+6.75
+3.50
+4.75
±0.00

חתך א-א 1:100

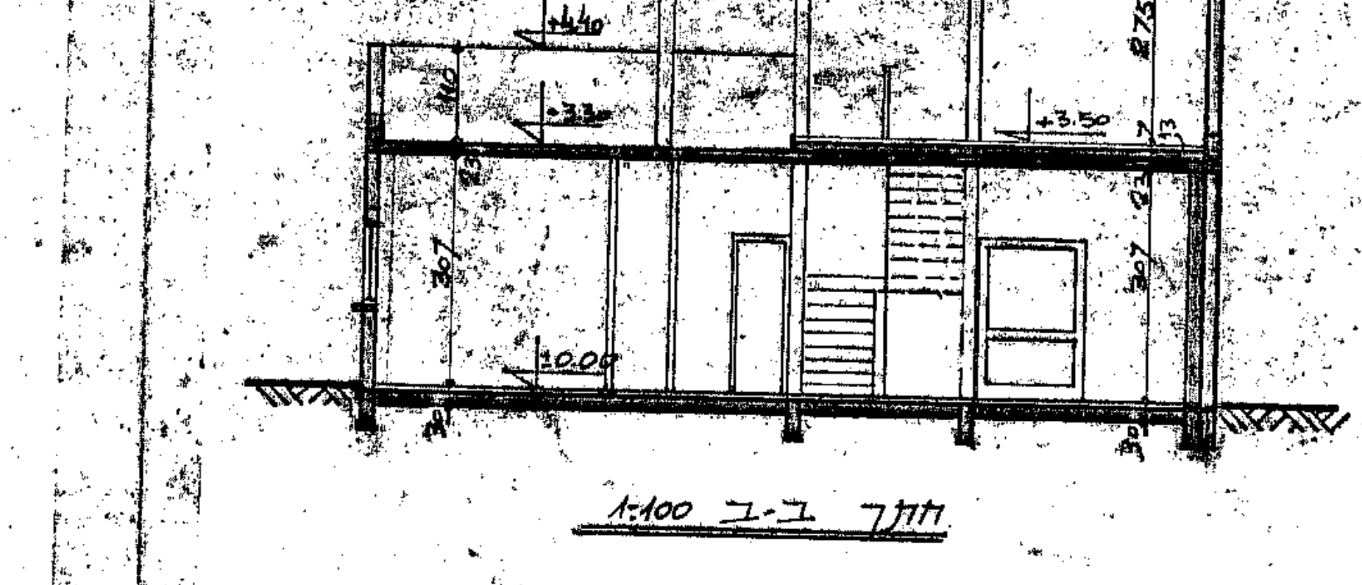
+6.45
+4.40
+3.30
+3.50
±0.00

חתך ב-ב 1:100

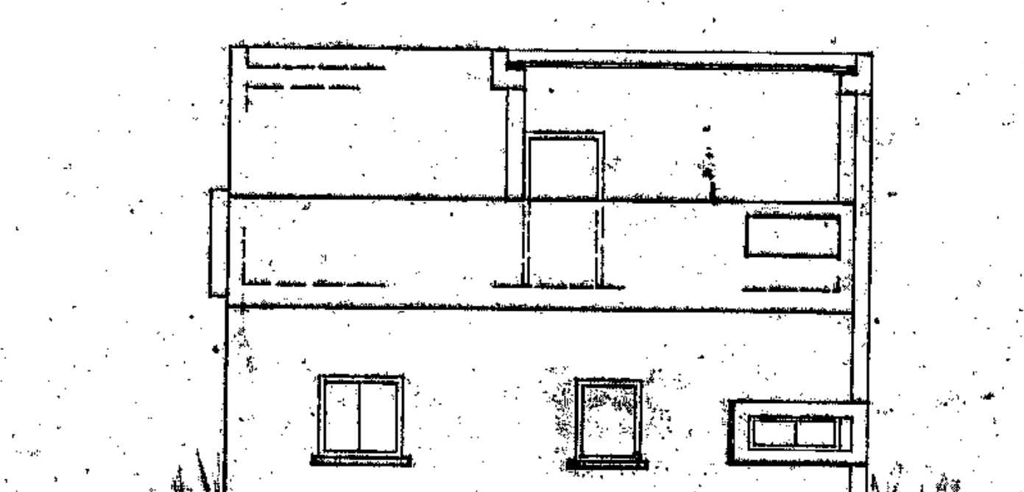

חזית דרומית 1:100

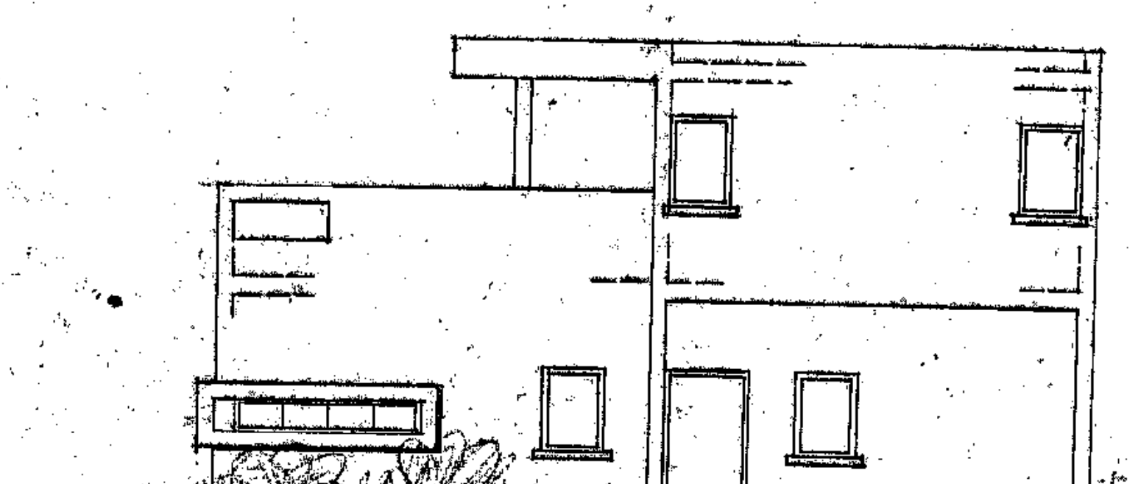

חזית מזרחית ק.מ. 1:100

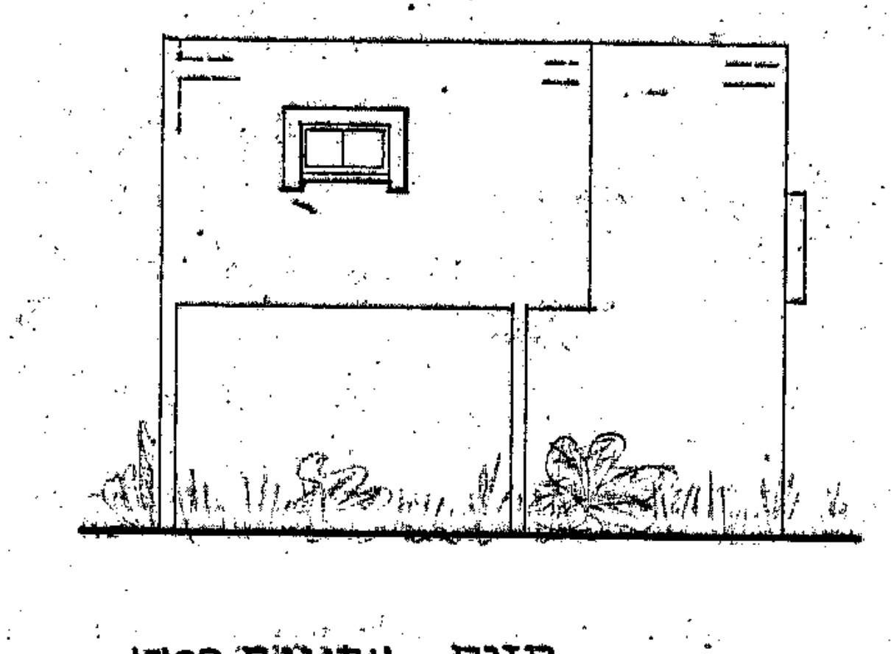

חזית צפונית 1:100

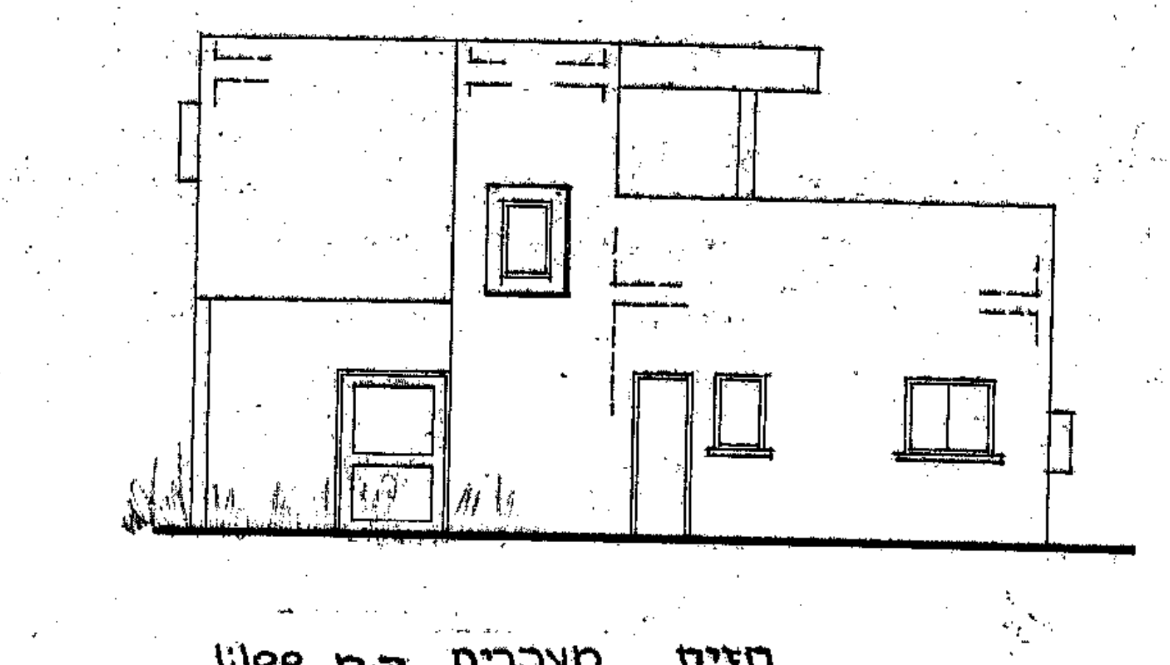

חזית מערבית ק.מ. 1:100

סוף מסמך