סוף מסמך

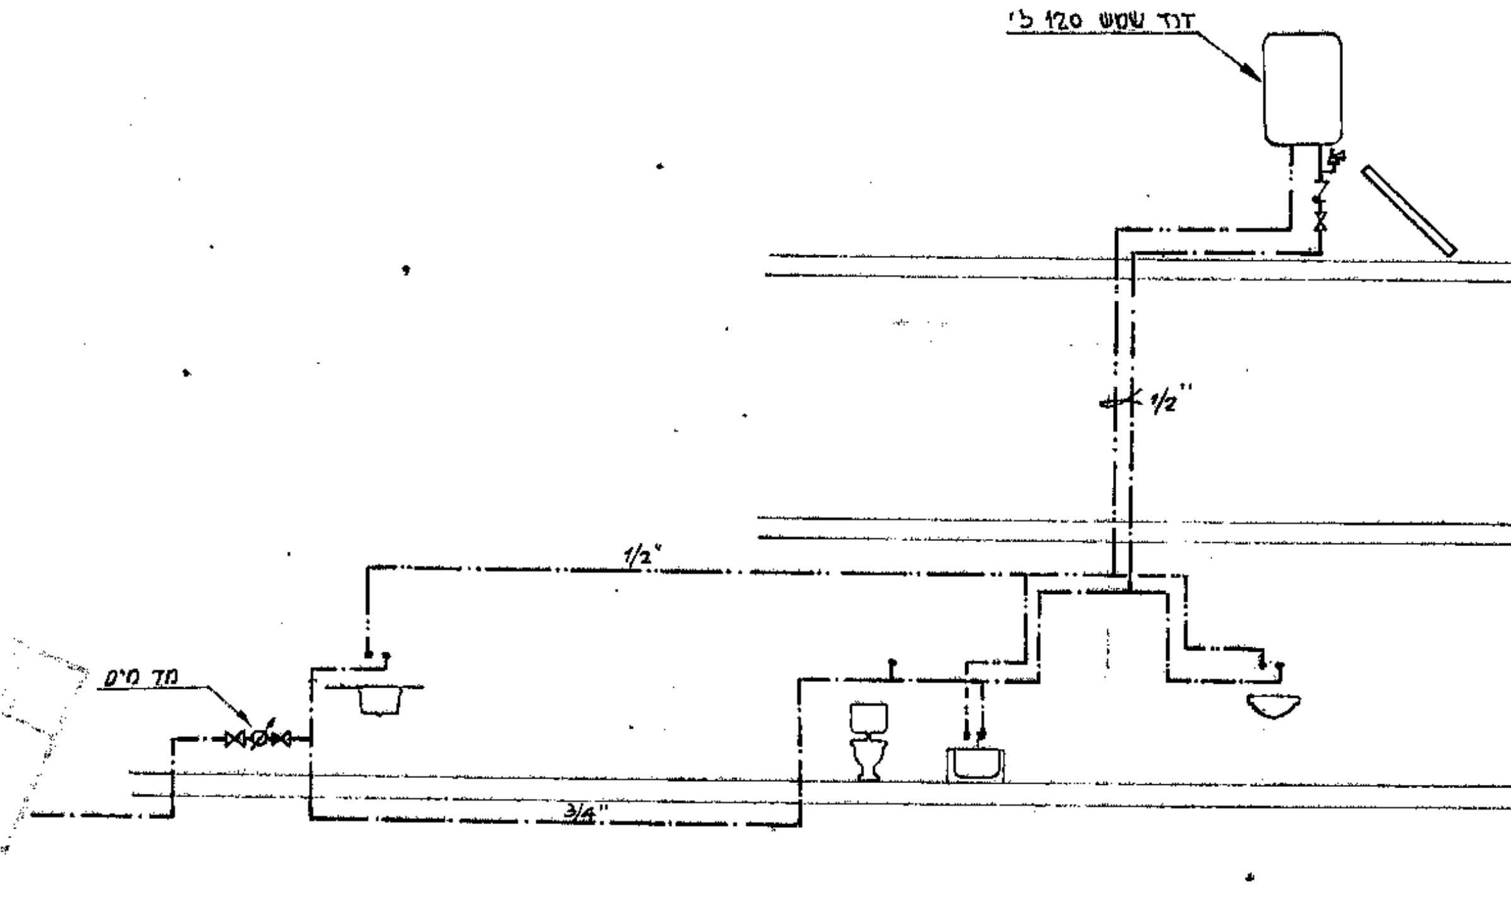

דוד שמש 120 ל׳
+6.45
1/2"
+3.30
1/2"
מד מים
±0.00
3/4"

סכמת מים חמים וקרים

האשור מחייב
שמיתקני התברואה
יבוצעו בהתאם להוראות
למיתקני תברואה ...
ובהתאם לשביעות ...
של מח"י —

עיריית תל־אביב־יפו
מינהל ההנדסה - אגף הרישוי
המדור להנדסת תברואה
3 - 03 - 1983
18197/8

חתך לאורך קו ביוב
ק.מ. לאורך 1:250
ק.מ. לגובה 1:50

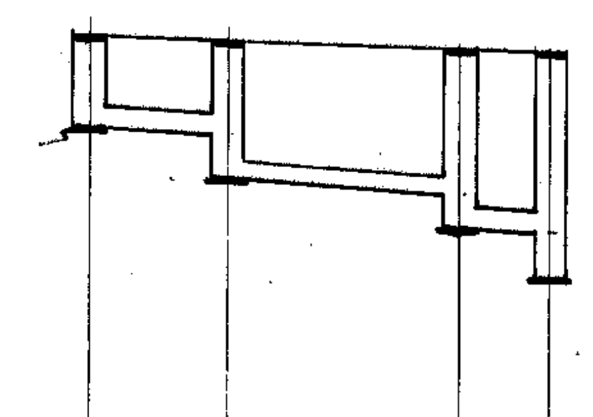

קיים	1	2	3	מספר תא בקורת
	3.00	7.50	4.50	מרחקים ביניים
15.00	12.00	4.50	0.00	מרחקים מסוכמים
17.35	17.38	17.39	17.43	גובה פני הקרקע
16.15 15.85	16.40 16.18	16.78 16.48	16.83	גובה תחתית הצנור
קיים	ø80 1.20	ø80 0.91	ø60 0.60	עומק וקוטר התא
1%			6"	קוטר ושפוע הצנור

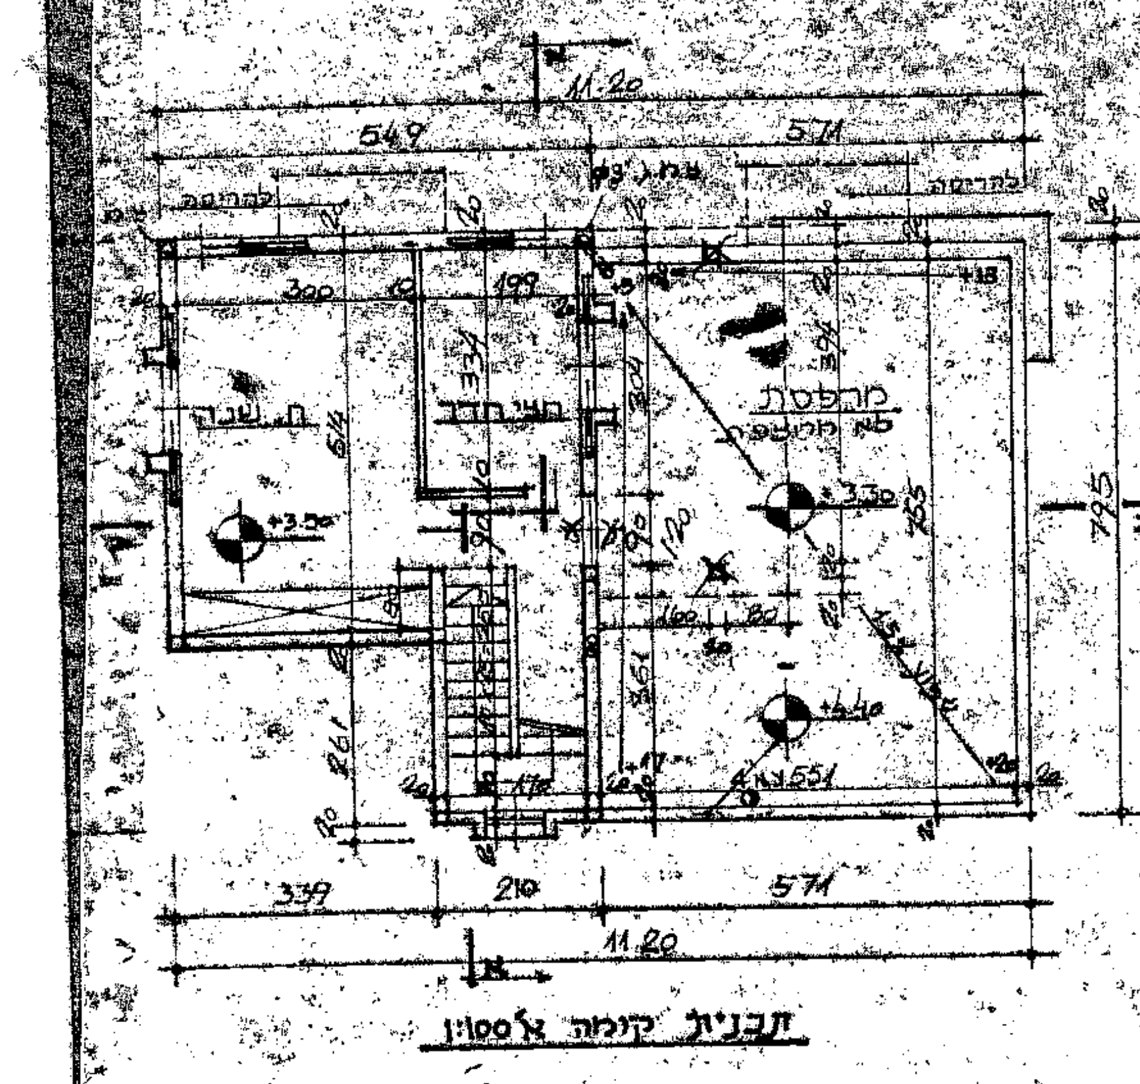

11.20
549
571
להריסה
ח. שינה
חצי חדר
מרפסת
לא מקורה
+3.30
+3.50
+4.40
339
210
571
11.20

תכנית קומה א׳ 1:100

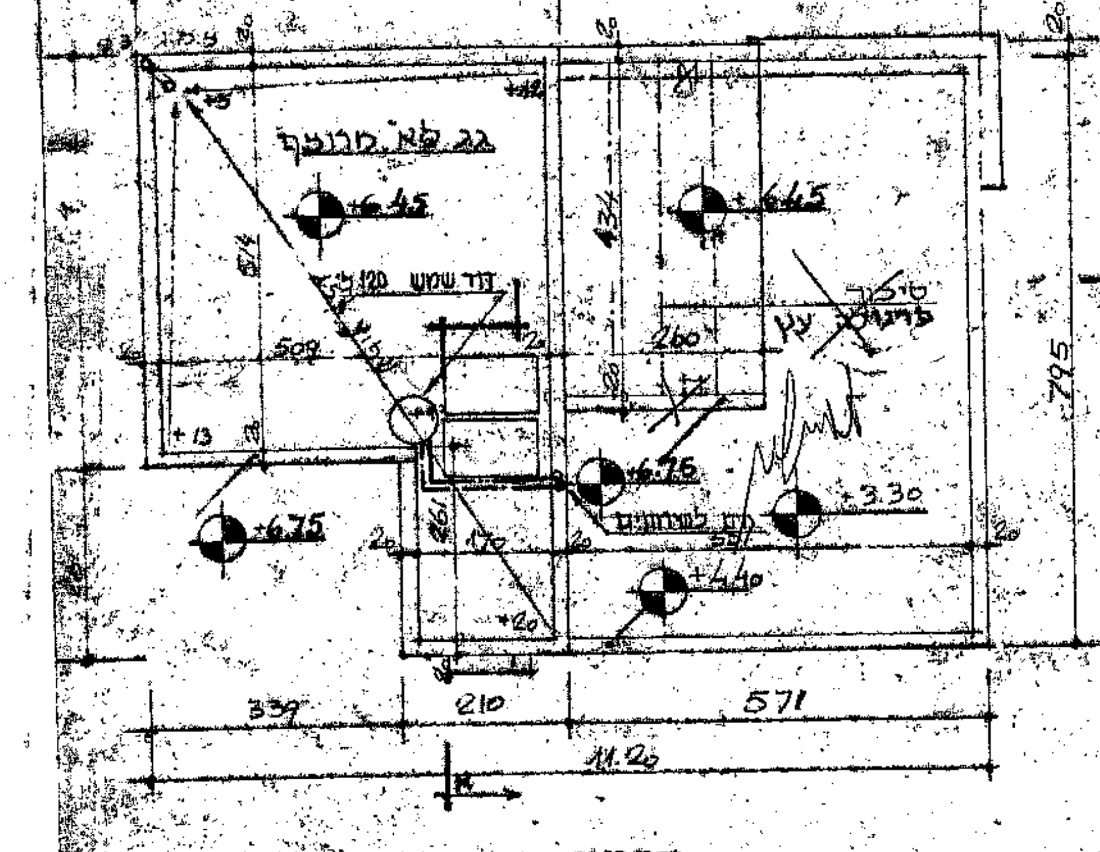

11.20
549
571
גג לא מרוצף
+6.45
+6.45
דוד שמש 120 ל׳
+6.76
+6.75
+3.30
+4.40
339
210
571
11.20

תכנית הגג 1:100

עיריית תל־אביב־יפו / מנהל הנדסה / אגף הרישוי
אשור מס׳ 48/82
נתן אשור לכלי אשפה כמ״ז וכמבנה שצויינו בתכניה בתנאי:
1) שיוצב/ו 1 כלי אשפה כל-סיים 1 ליש, עם מכסה צמוד מדגם מאושר ע״י אגף התברואה, על גבי תושבות ברזל 30 ס״מ מהרצפה ו־20 מכל קיר.
2) ברז מים וכריכה ייקבעו החל מפתקן בעל 2 כלי אשפה ויותר והם יחוברו להספקת המים הכללית ולרשת הביוב של הבית.
3)

בכל מקרה של שינויים בתכנית הבניה יש לקבל אשור מחדש מאגף הרישוי על סוג, מיקום צורת ומספר כלי אשפה.
התאריך ______ התיפור
2 מרס 1983

לאחר גמר בנית הבנין, נא להתקשר עם מדור תכנון מתקנים במנהל ההנדסה/אגף הרישוי לשם בדיקת הביצוע הנ״ל. רק לאחר ביצוע התנאים - ניתן לשחרר את הפקדון.

אין להשתמש בכטונדה לפני אשפה

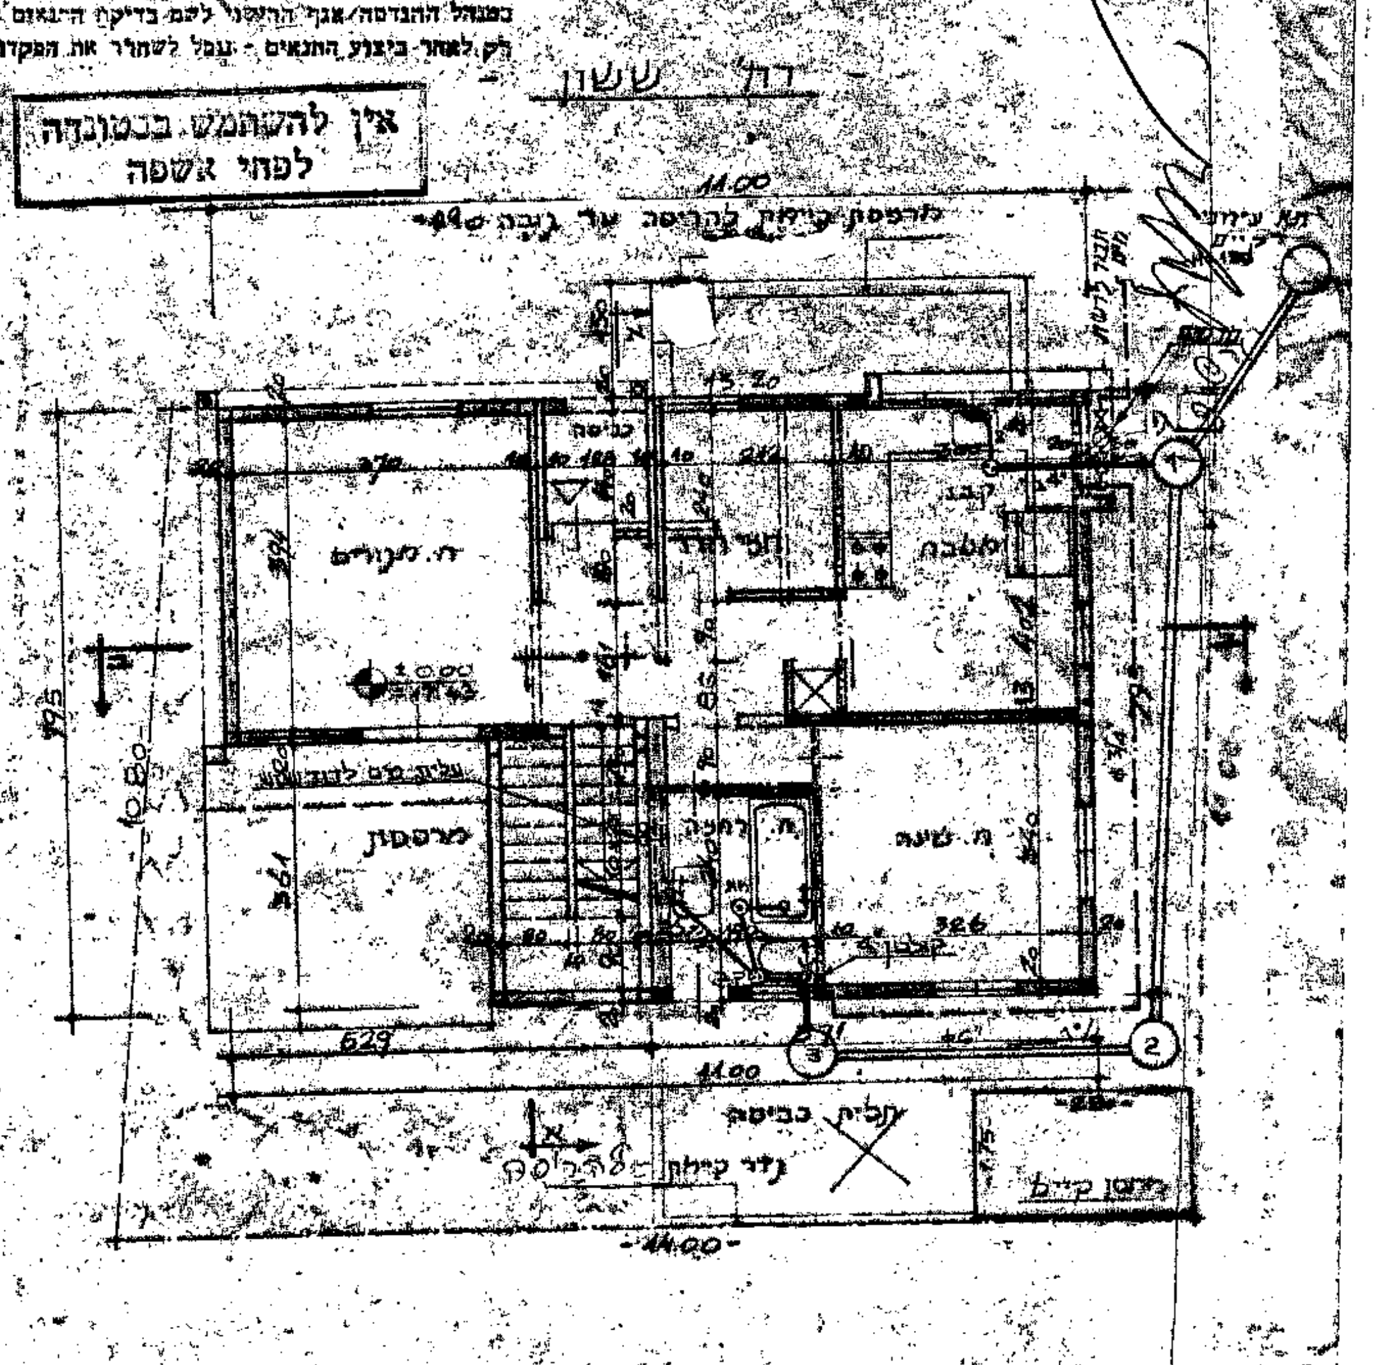

דרך ששון
להפסק עירות להריסה עד גובה
14.00
ח. מגורים
חצי חדר
מטבח
±0.00
כניסה
ח. שינה
פרוזדור
מרפסת
שירות
629
11.00
2
3
תא עירוני קיים
חלות כביסה
גדר קיימת להריסה
14.00

תכנית קומת קרקע 1:100

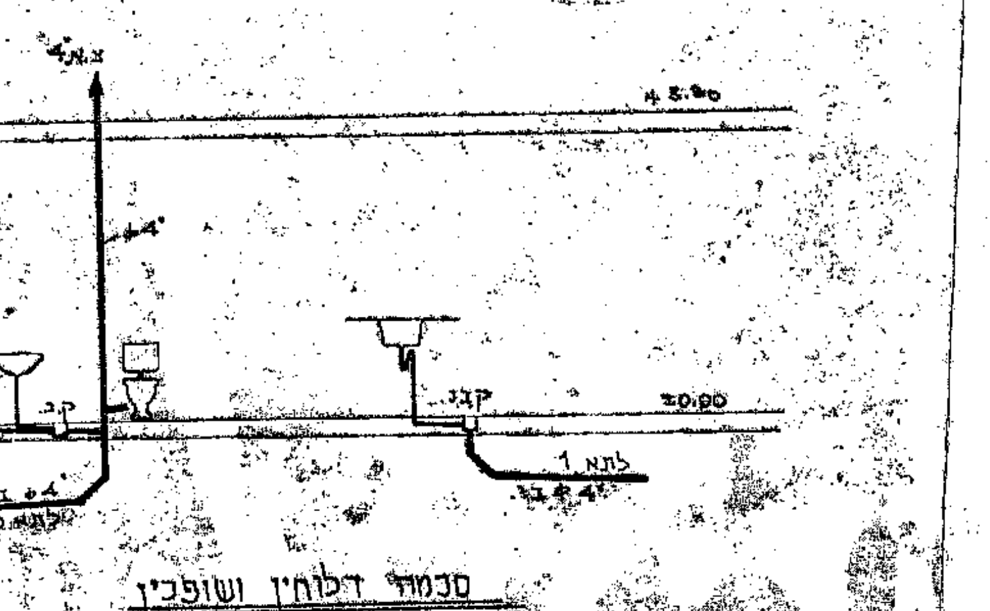

צ.א. 4"
+3.30
±0.00
ק.ב.
לתא 1
4"
לתא 3

סכמת דלוחין ושופכין

תרשים הסביבה 1:1250

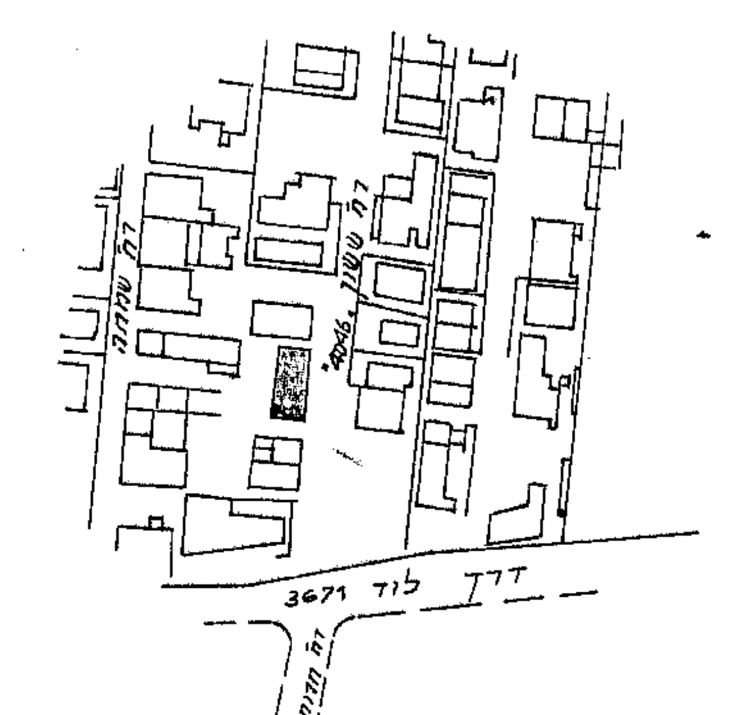

רח׳ ששון
רח׳ שמחה
דרך לוד 3671
רח׳ חנוחמה

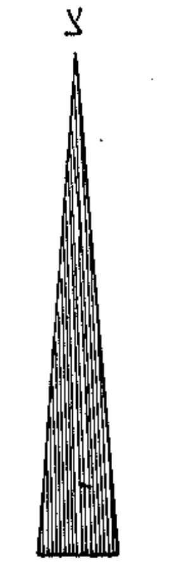

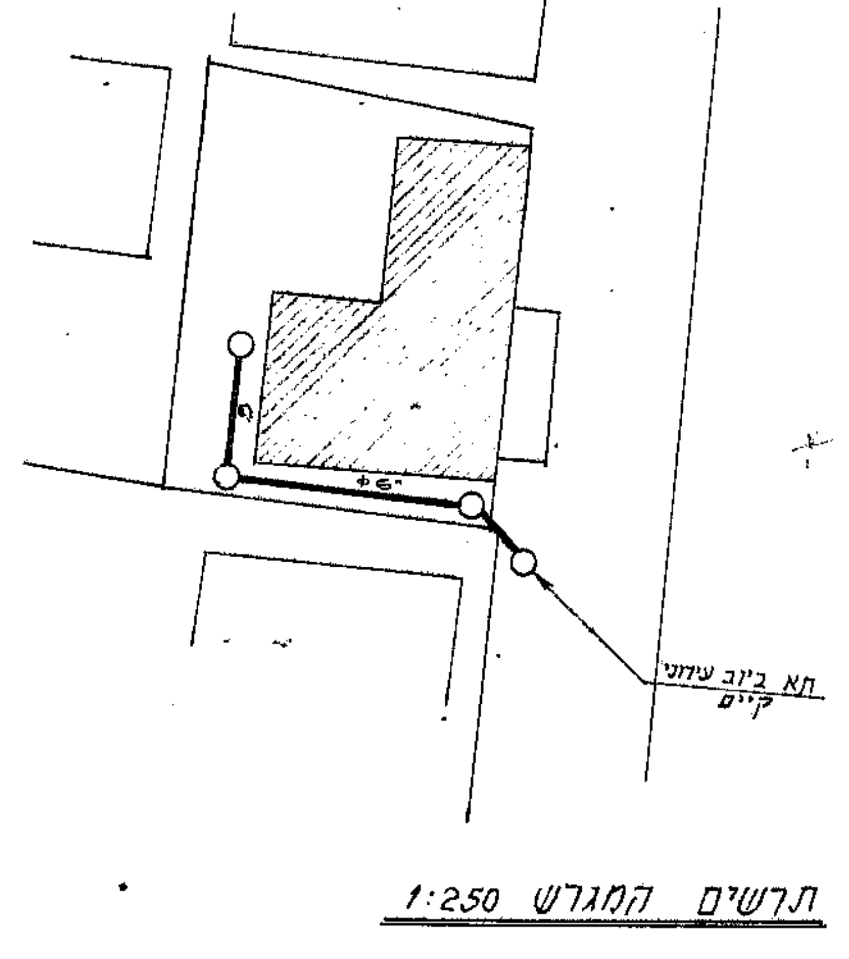

6"
4"
תא ביוב עירוני קיים

תרשים המגרש 1:250

22

אינסטלציה סניטרית

ג. רוה מהנדס יועץ
רחוב אלעזר 69 רעננה 43206
טל. 052-22133

חוק התכנון והבניה, תשכ״ה—1965
תקנות התכנון והבניה (בקשה להיתר, תנאיו ואגרות), תש״ל—1970

טופס 2 (תקנה 2(א))

תיק מס׳ 27987

מ י פ ר ם

הועדה המקומית לתכנון ולבניה ת״א

א׳ תיאור הבנין

1. הישוב: ת״א | השכונה: ששון | רחוב/מס׳: 36 | גוש: 6135 | חלקה: 44 | תכנית מיתאר מקומית או מפורטת: 2215

2. המבקש: יוסף־פור, לאה וזבוה רח׳ ששון 36 שכונת התקוה ת״א
3. בעל הנכס: כנ״ל
4. עורך הבקשה: אבנעם לוין־ארכיב׳ | קהלת מוסה 10 ת״א | 03-479858
5. המהנדס האחראי לביצוע השלד: שגב הורוביץ | ה׳ באייר 48 ת״א | 03-250548
6. אזור הבניה: ☒ מגורים ☐ מסחר ☐ תעשיה ☐ בנין ציבורי ☐ חקלאי ☐ ...
7. שטח: ... 142 ... 196 ...
8. מטרת הבנין: ☒ מגורים ☐ הארחה ☐ עסקים ☐ תעשיה ☐ חקלאי ☐ ציבורי ☐ ...
9. מהות הבנין המבוקש: תוספת קומה לבנין מגורים קיים
10. תיאור העבודה המבוקשת: ☐ בנין חדש ☒ תוספת לבנין קיים ☐ הריסה ☐ תיקונים ☐ שינוי בבנין ☐ ...
☐ שינוי בשימוש ממטרה: ... למטרה: ...
11. האם הבניה היא בעד: ☐ משרד ממשלתי ☐ הרשות המקומית ☐ הסוכנות היהודית

ב׳ חישוב השטחים

קומה	קיים	מוצע	סך הכל	אחוזי הבניה
מרתף				
הכניסה / קומת עמודים	68.36	7.58	75.94	39
א		28.33	28.33	15
בנייני עזר	(4.90)		(4.90)	2.5
סך הכל	68.36	35.91	109.17	56.5%

חלקי בנין אחרים—הבניה המוצעת, שטח במ״ר: (7.58) ... (4.90)

עיריית תל־אביב־יפו
אגף מפעל המים
אישור לאספקת מים
בתוקף מיום 13-3-83
עד יום
החתימה

ד׳ חומרי הבניה: קירות חיצוניים: ☐ בטון מזוין ☒ לבני בטון או בלוקים ☐ לבני סיליקט ☐ לבנים שרופות ☐ אבן טבעית ☐ אבן מלאכותית ☐ אסבסט ☐ עץ ☐ ברזל ☐ חמרים אחרים
תקרות: ☒ בטון מזוין ☐ עץ ☐ חומר אחר
גג: ☒ בטון מזוין ☐ רעפים ☐ אסבסט ☐ פח ☐ חומר אחר

ה׳ גדרות: ... 5 ...

הערות:

הנני מאשר כי הנתונים הנ״ל נכונים
תאריך ______ חתימת המבקש ______ חתימת עורך הבקשה ______
חתימת המהנדס האחראי לביצוע השלד ______ חתימת בעל הנכס ______

אישורים של רשויות חוץ:

נסרק

אומת כמוכח