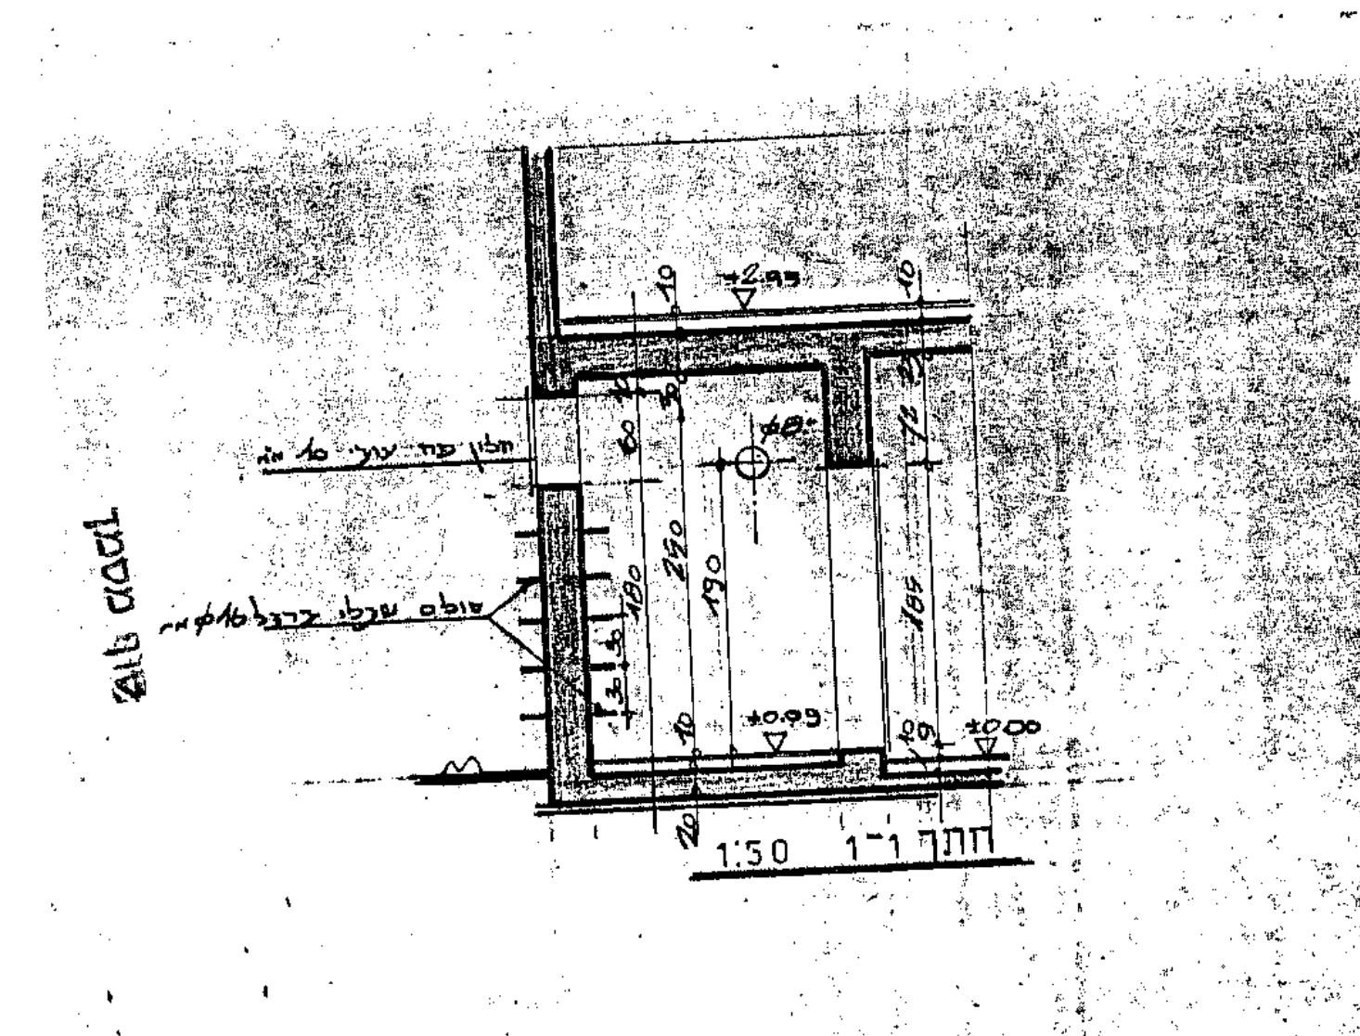
חלון קיפ עיל 40/40
מסגרות
חתך ו'-ו' 1:50

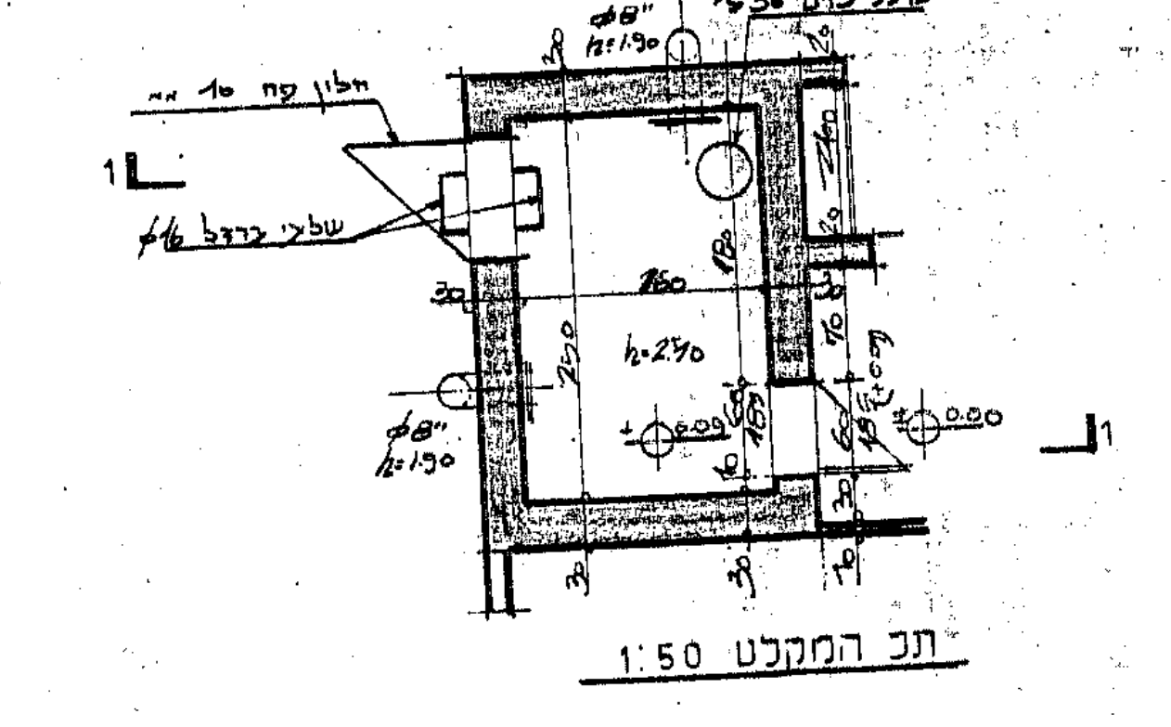
חלון קח 40/40
שלבי ברזל
h-240

תכ' המקלט 1:50

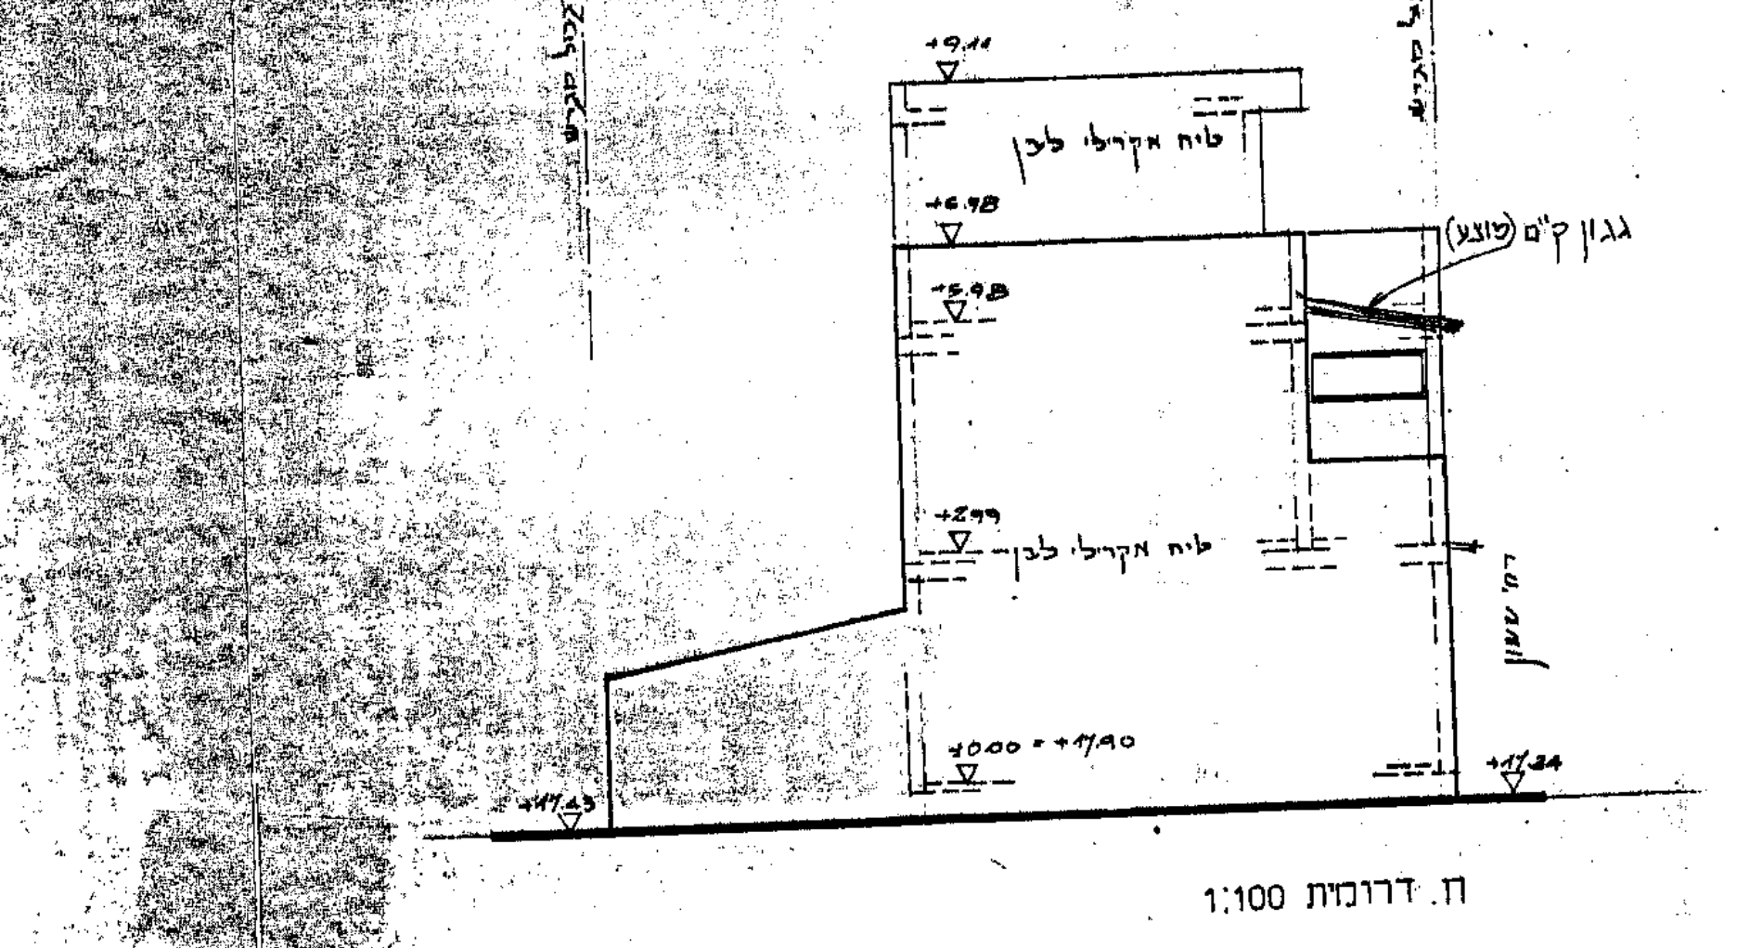
קו בניין
+9.11
טיח אקרילי לבן
+6.98
גגון קיים (מוצע)
+2.99
טיח אקרילי לבן
0.00=+17.90

ח. דרומית 1:100

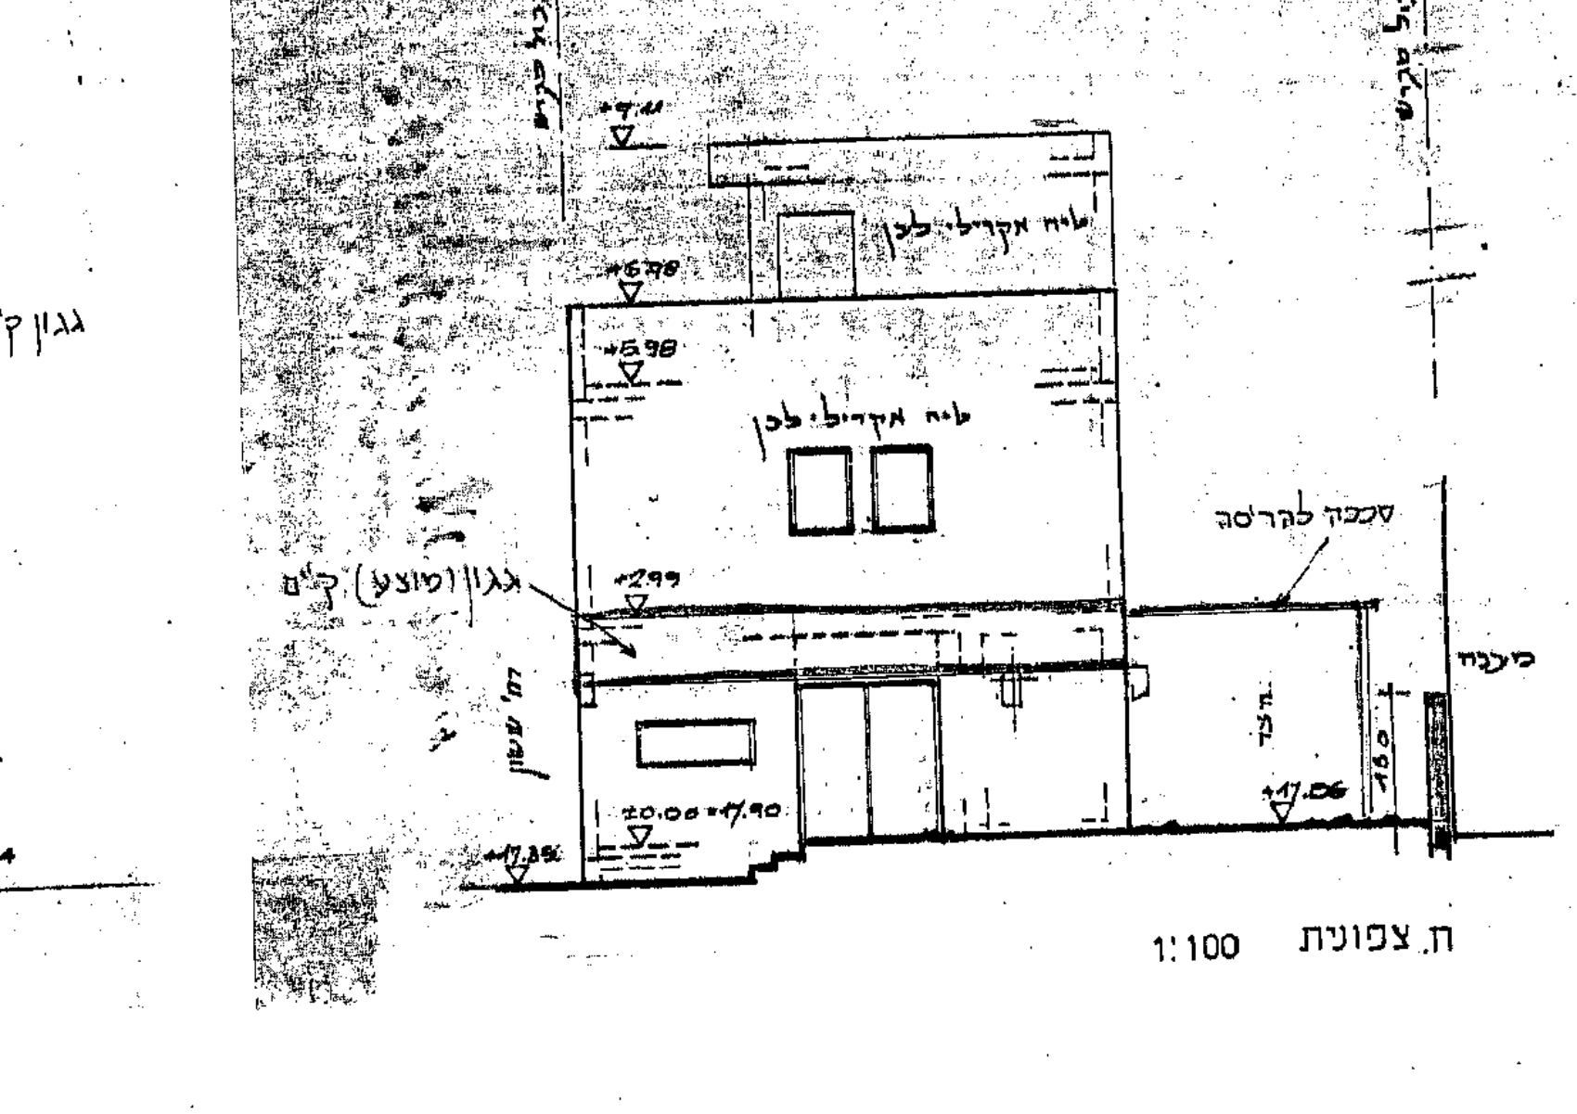
קו בניין
+9.11
טיח אקרילי לבן
+6.98
גגון (מוצע) קיים
סככה להריסה

ח. צפונית 1:100

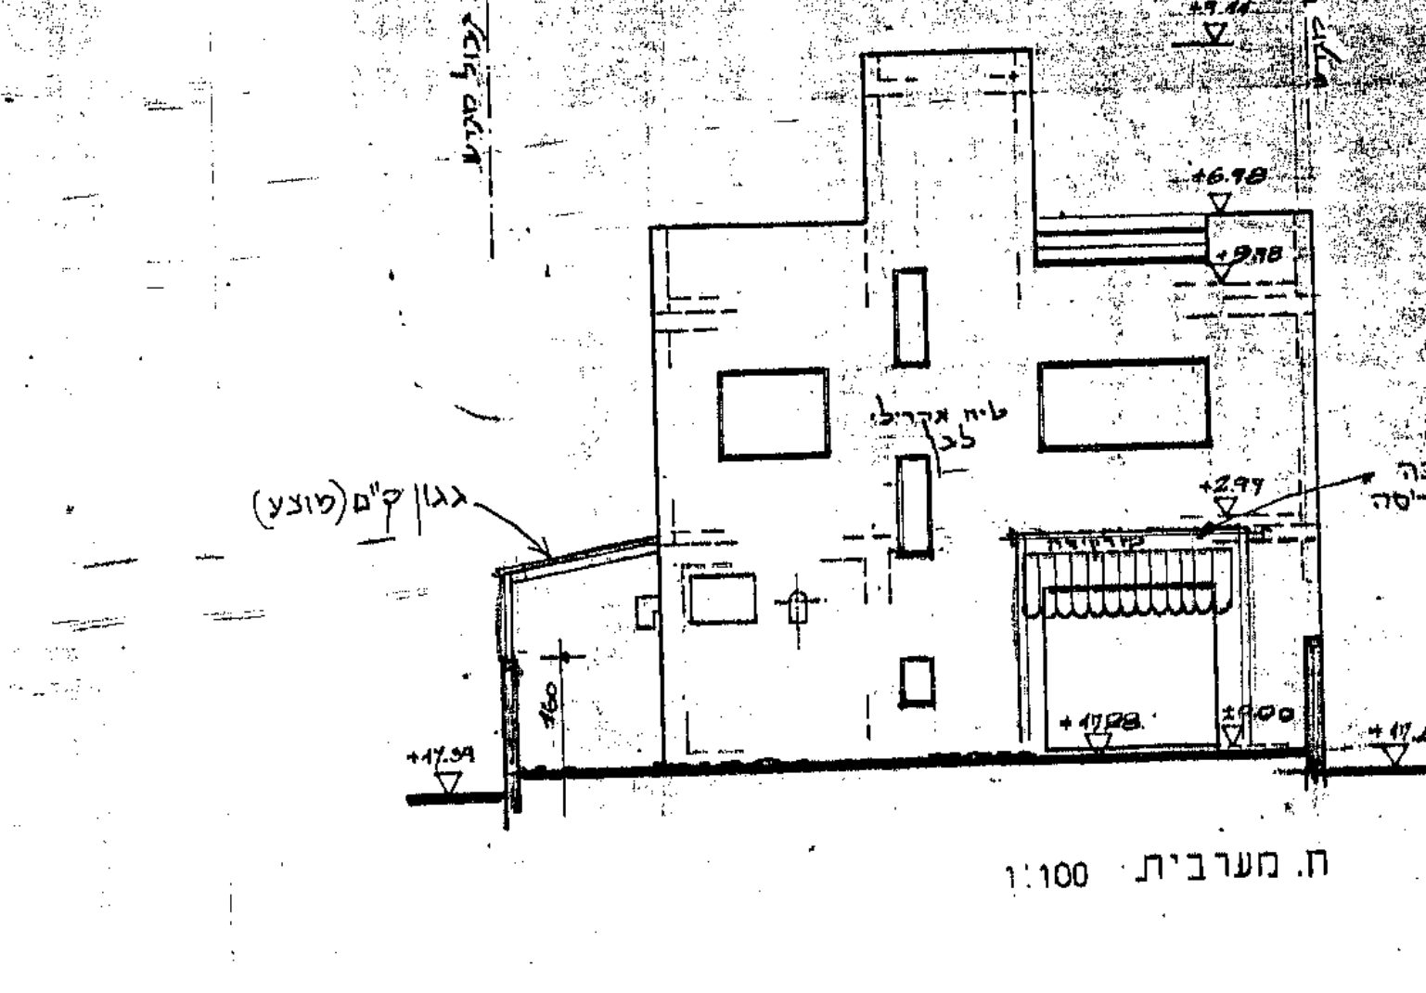
קו בניין
+9.11
+6.98
טיח אקרילי לבן
גגון קיים (מוצע)
סככה להריסה

ח. מערבית 1:100

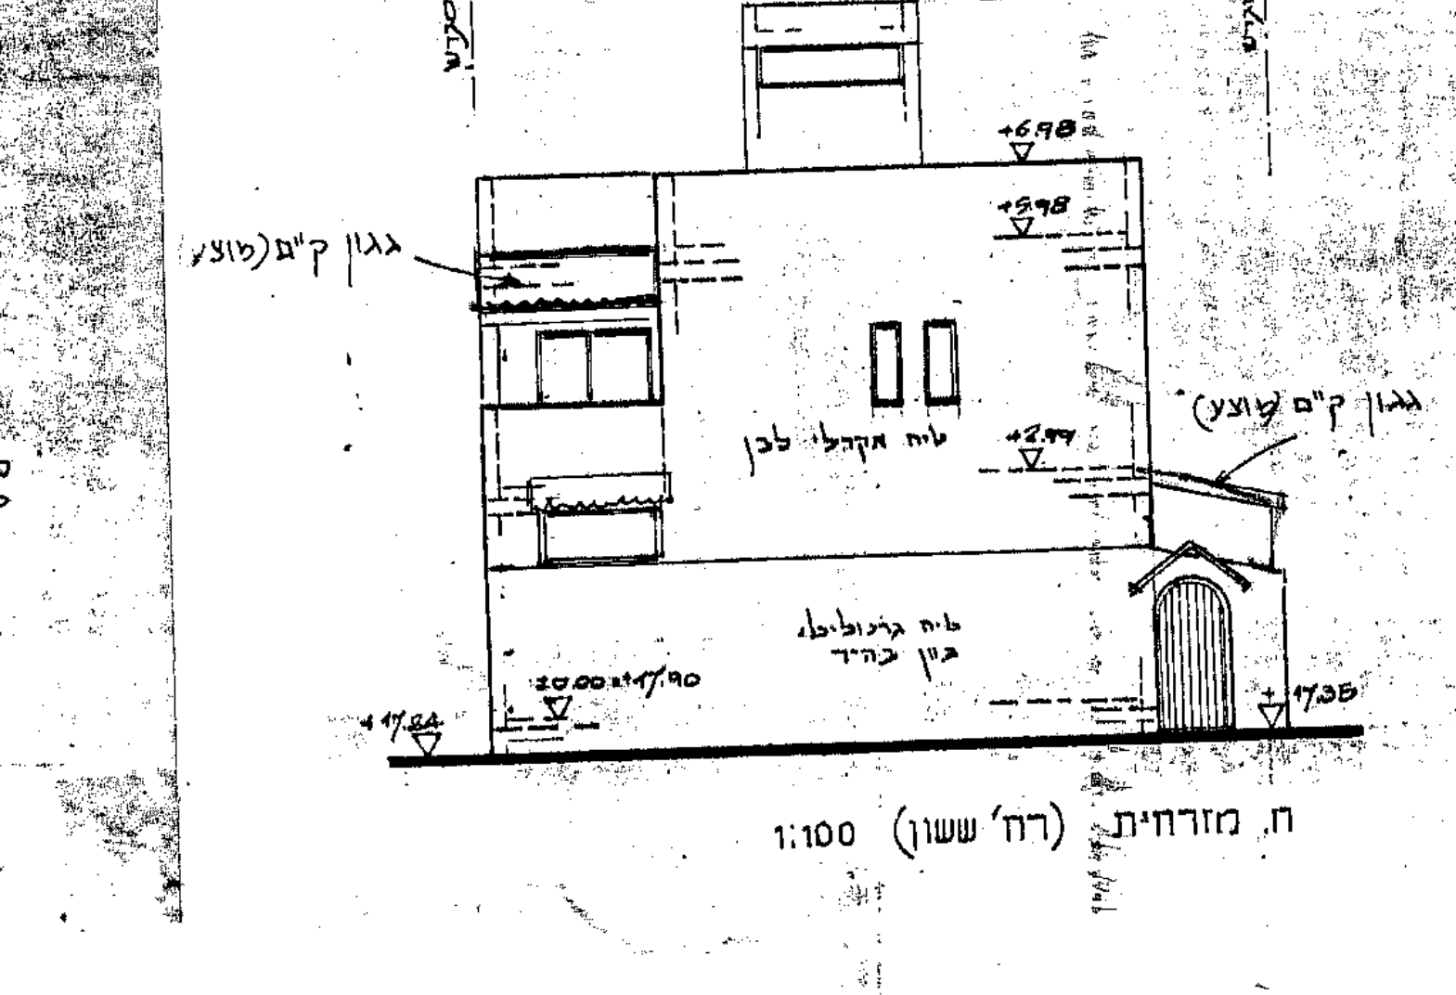
+9.11
+6.98
גגון קיים (מוצע)
גגון קיים (מוצע)
טיח אקרילי לבן
טיח גרנוליט, גוון בהיר

ח. מזרחית (רח' ששון) 1:100

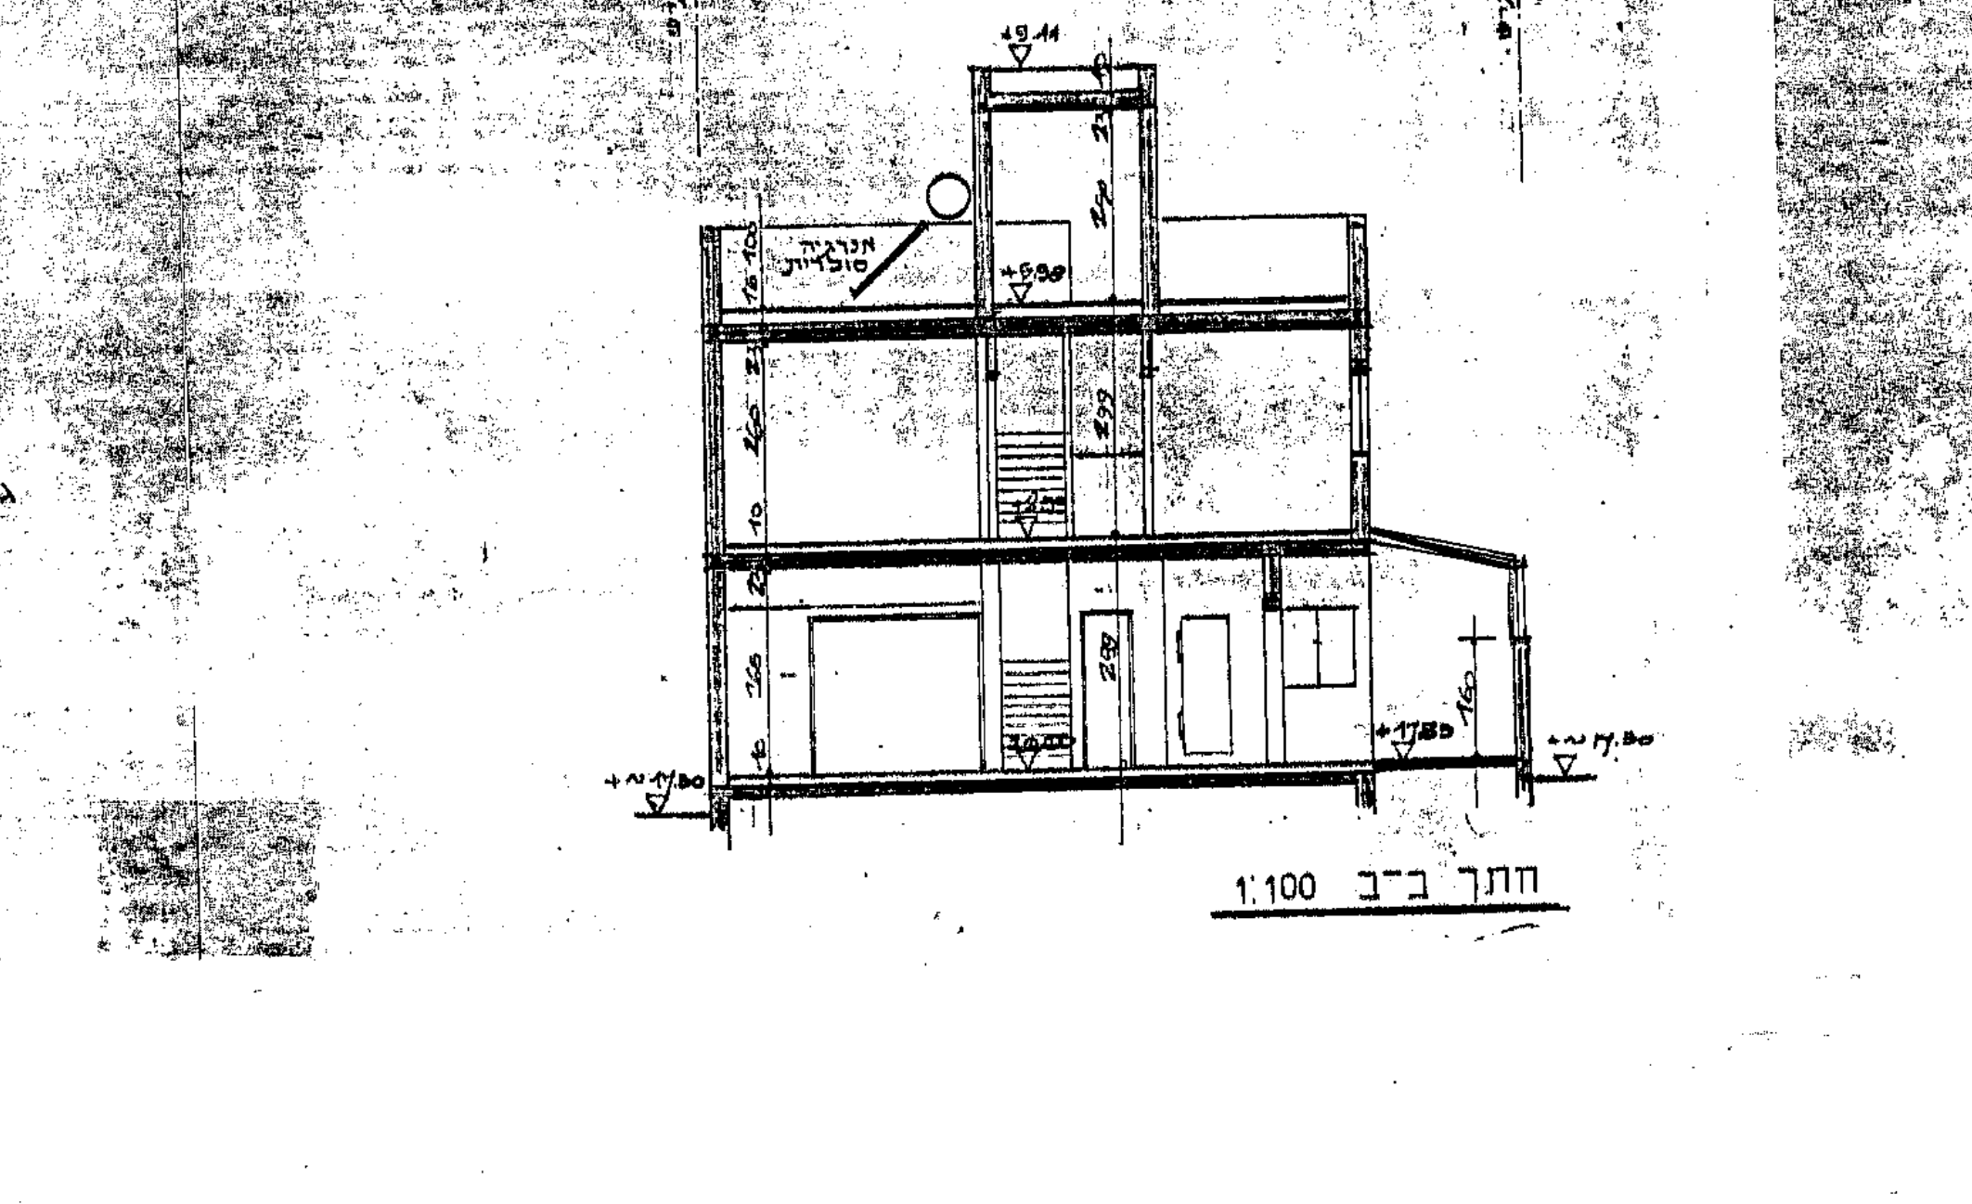
קו בניין
+9.11
מערכת סולרית

חתך ב-ב 1:100

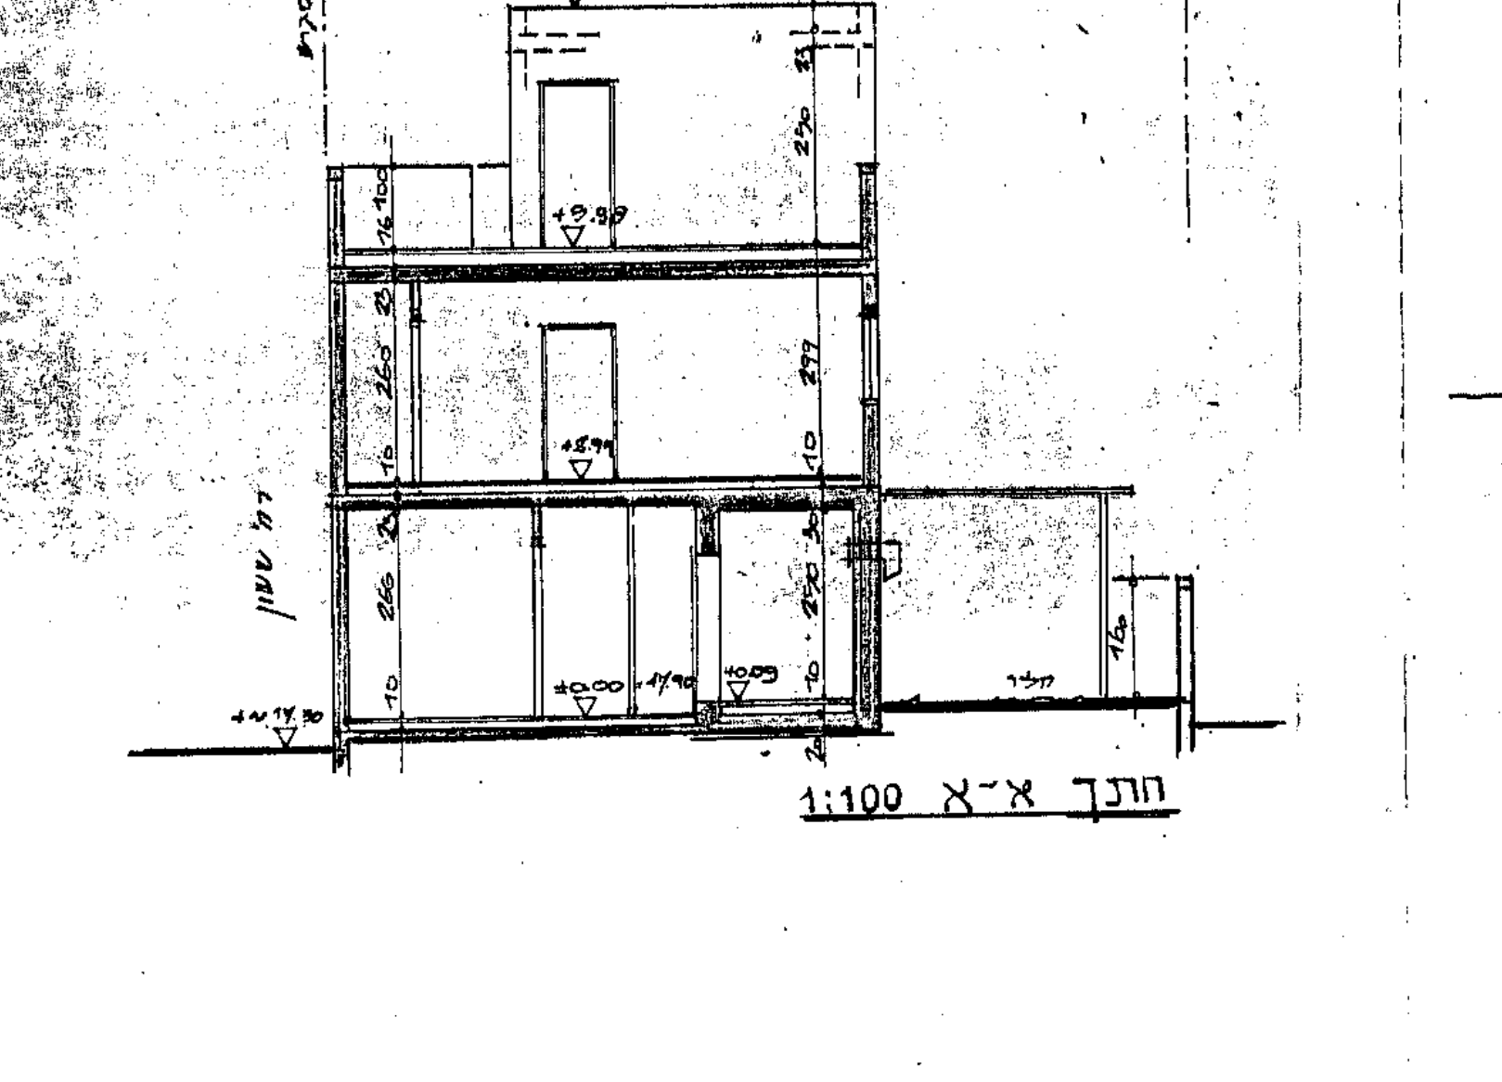
קו בניין
+9.11
+6.98
+2.99
רח' ששון

חתך א-א 1:100

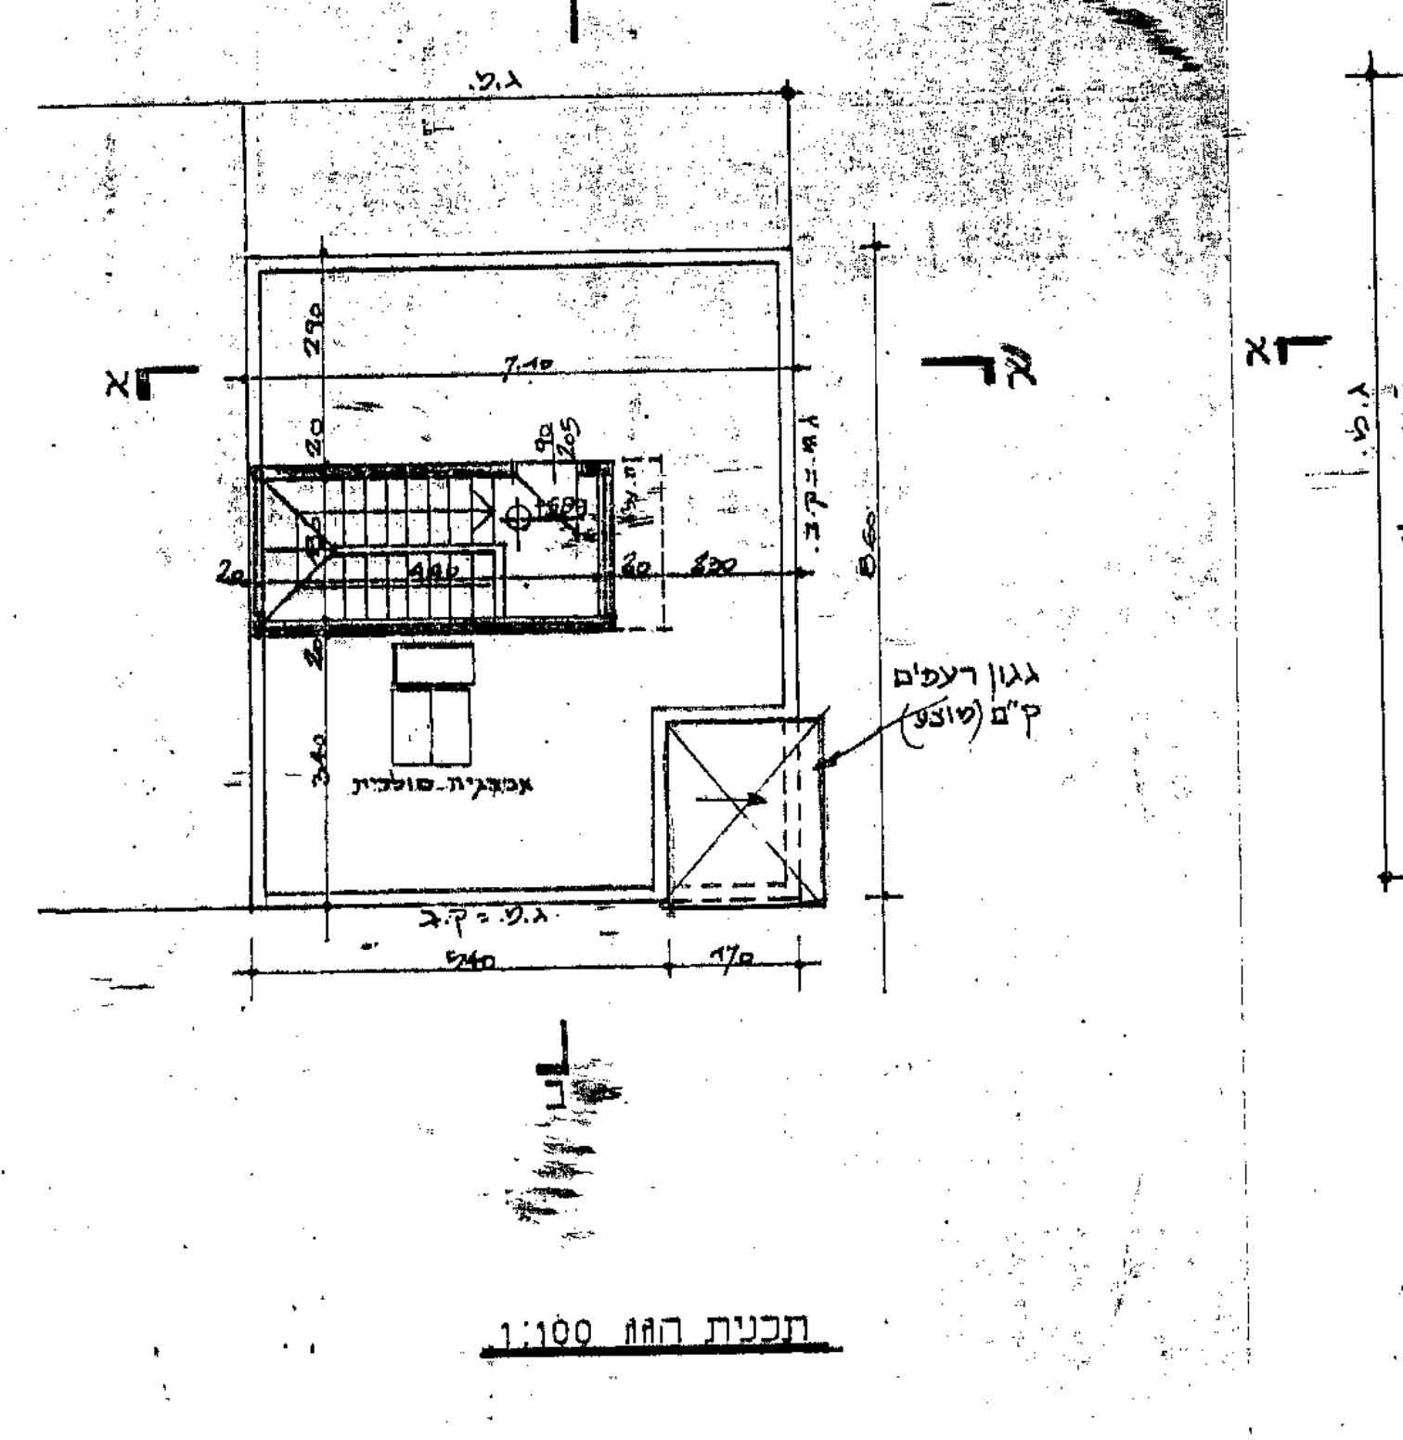
ב
א
גגון רעפים ק"מ (מוצע)
מערכת סולרית

תכנית הגג 1:100

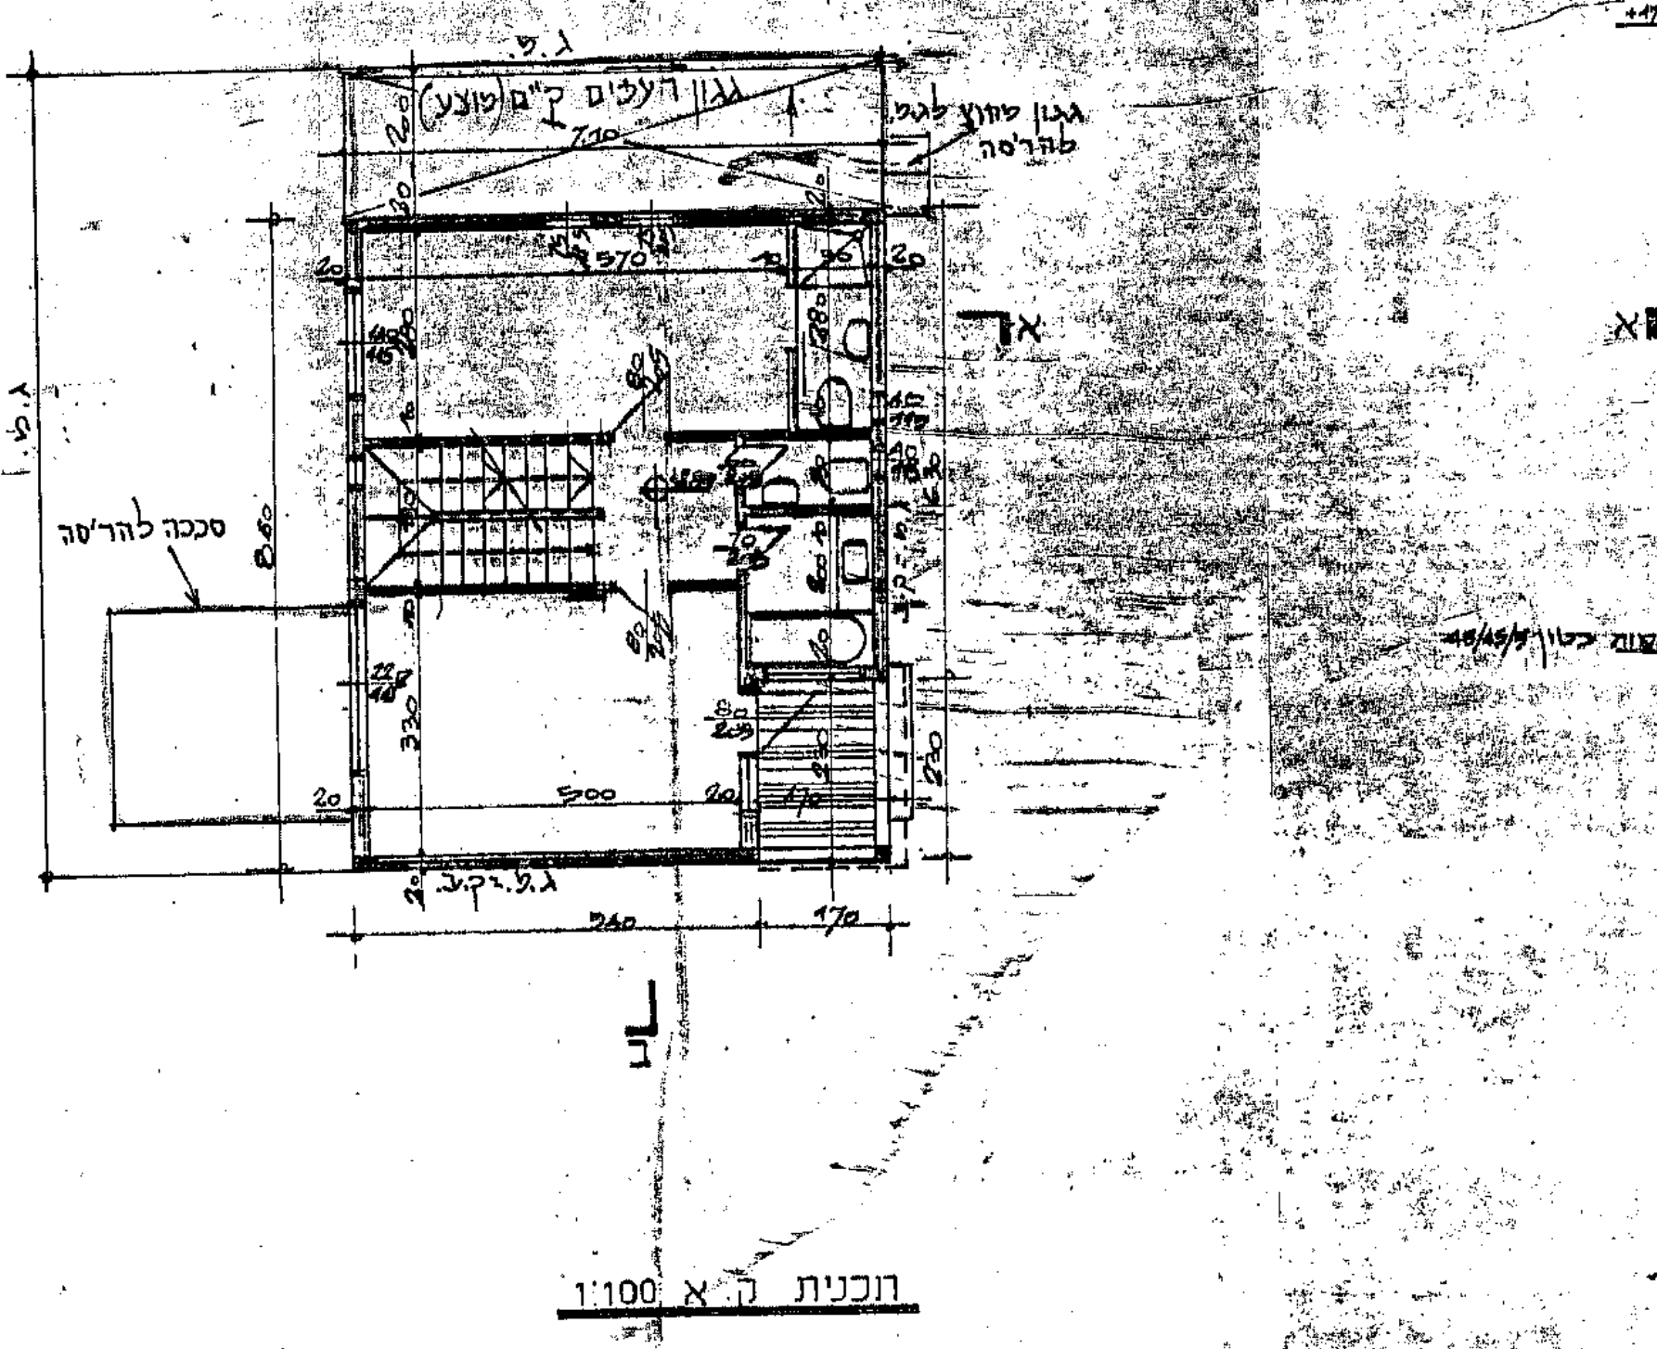
ב
א
גגון רעפים ק"מ (מוצע)
גגון שקוף ק.ג. להריסה
סככה להריסה

תכנית ק' א' 1:100

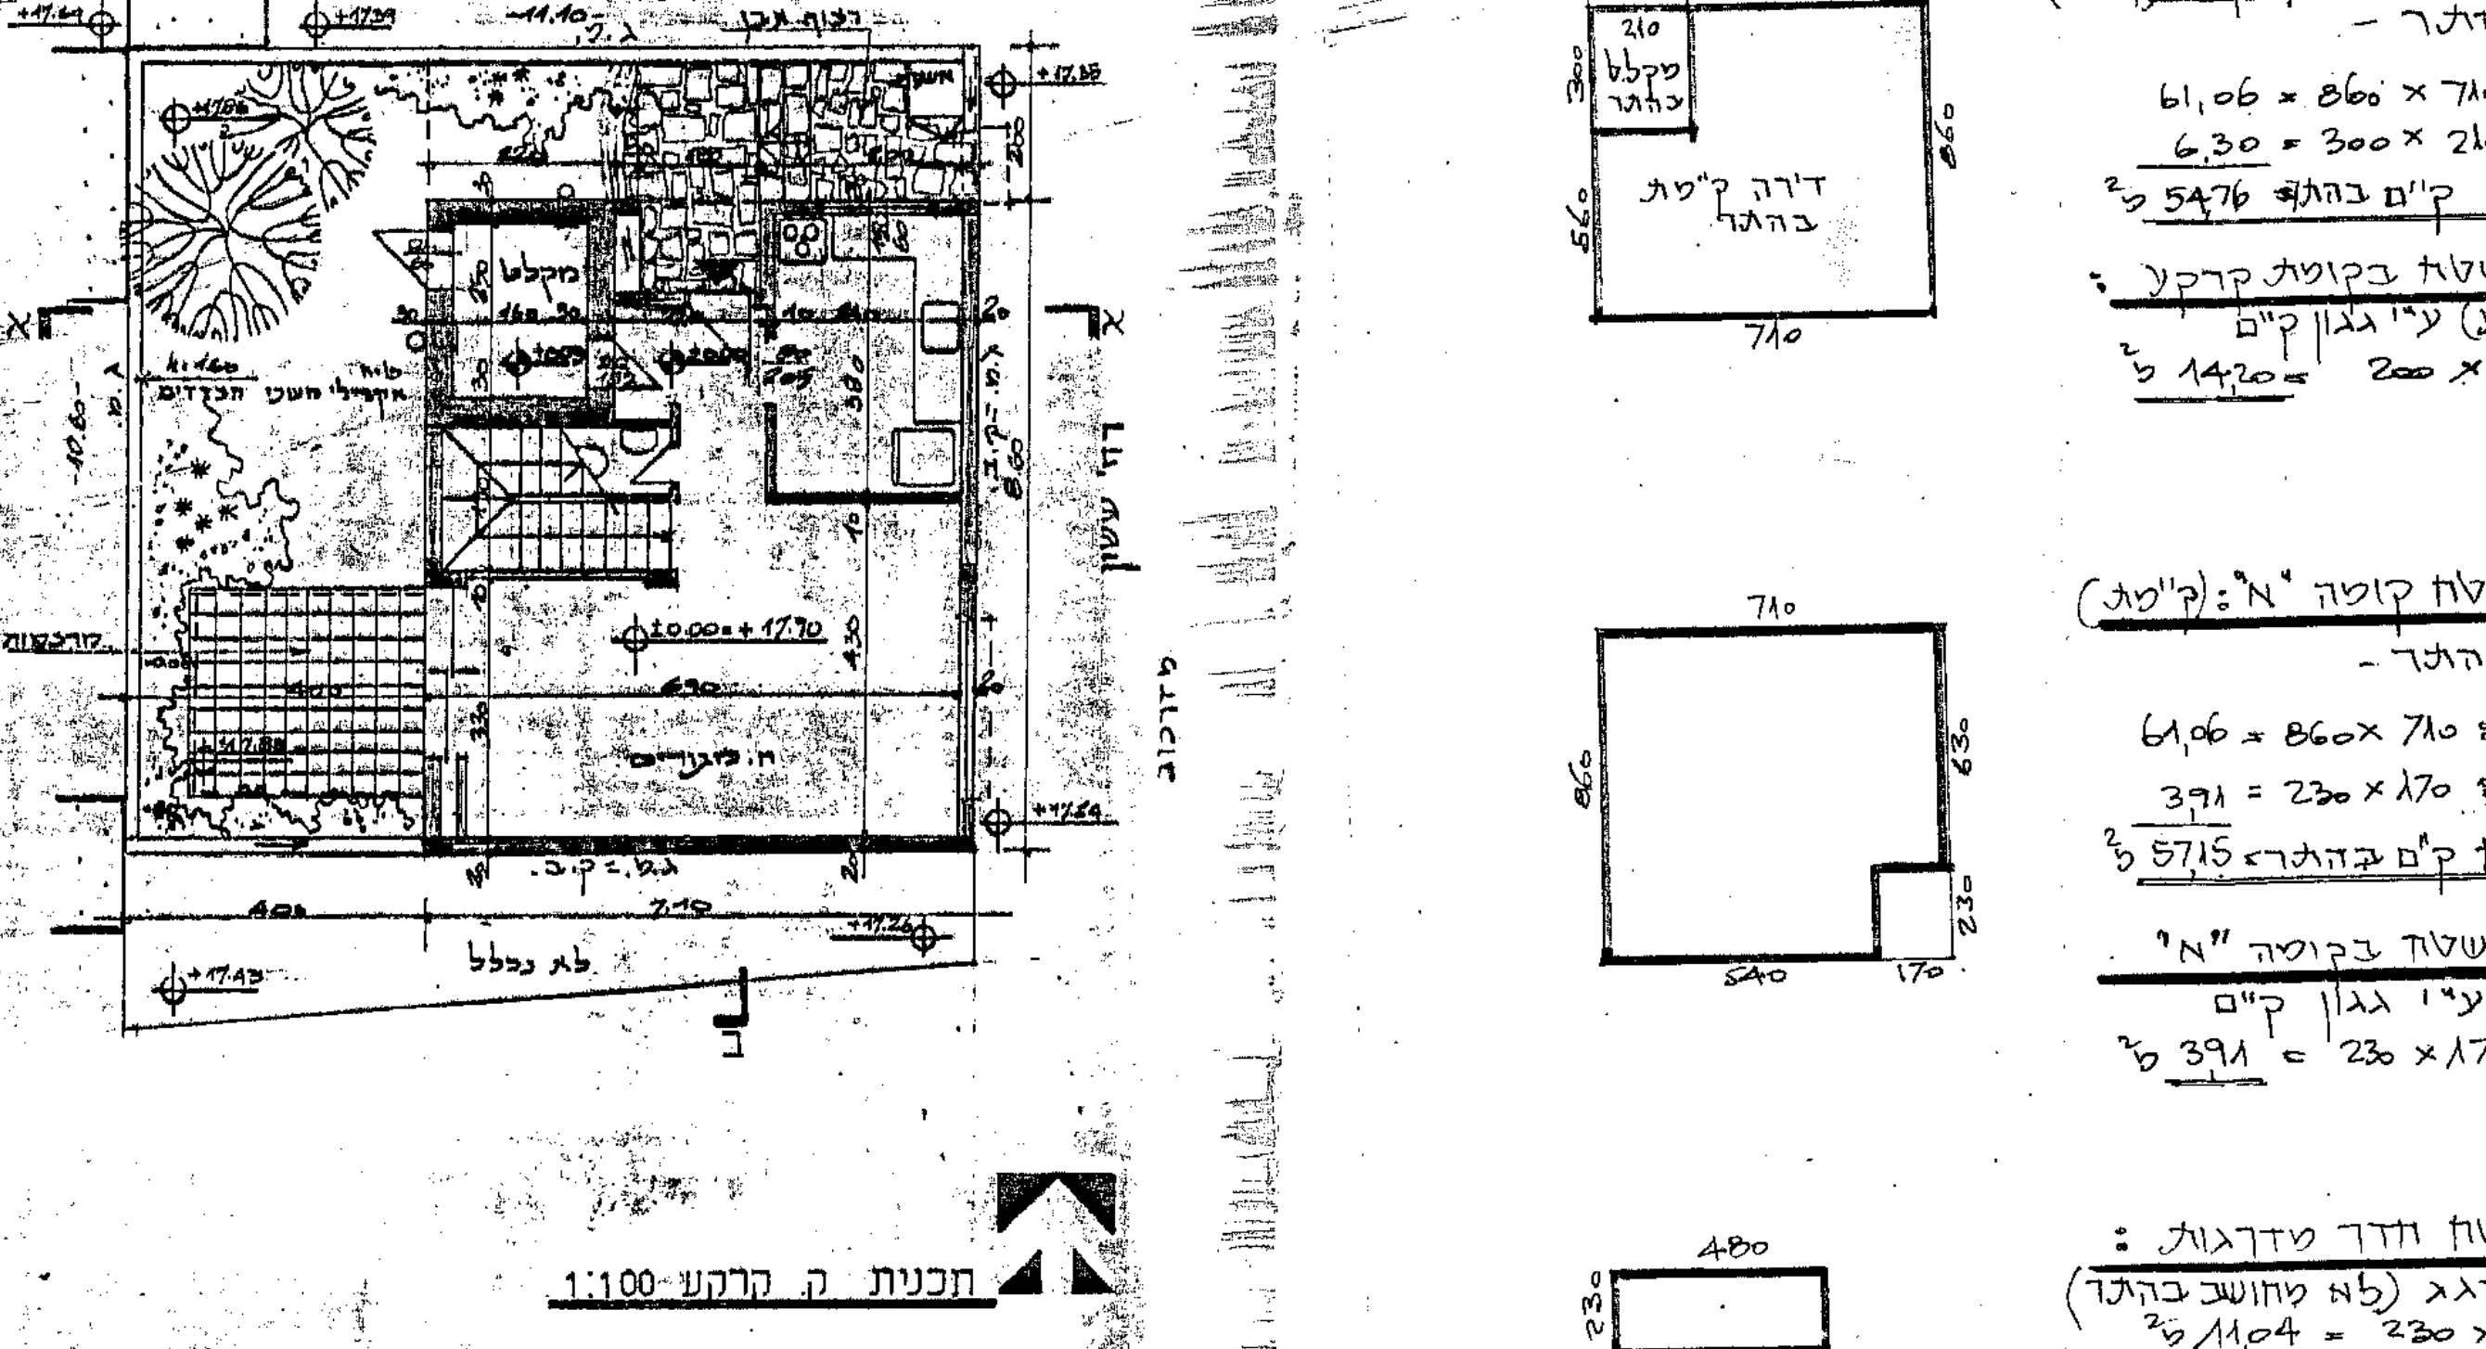
ב
א
רח' ששון
מדרכה
לא נכלל

תכנית ק' קרקע 1:100

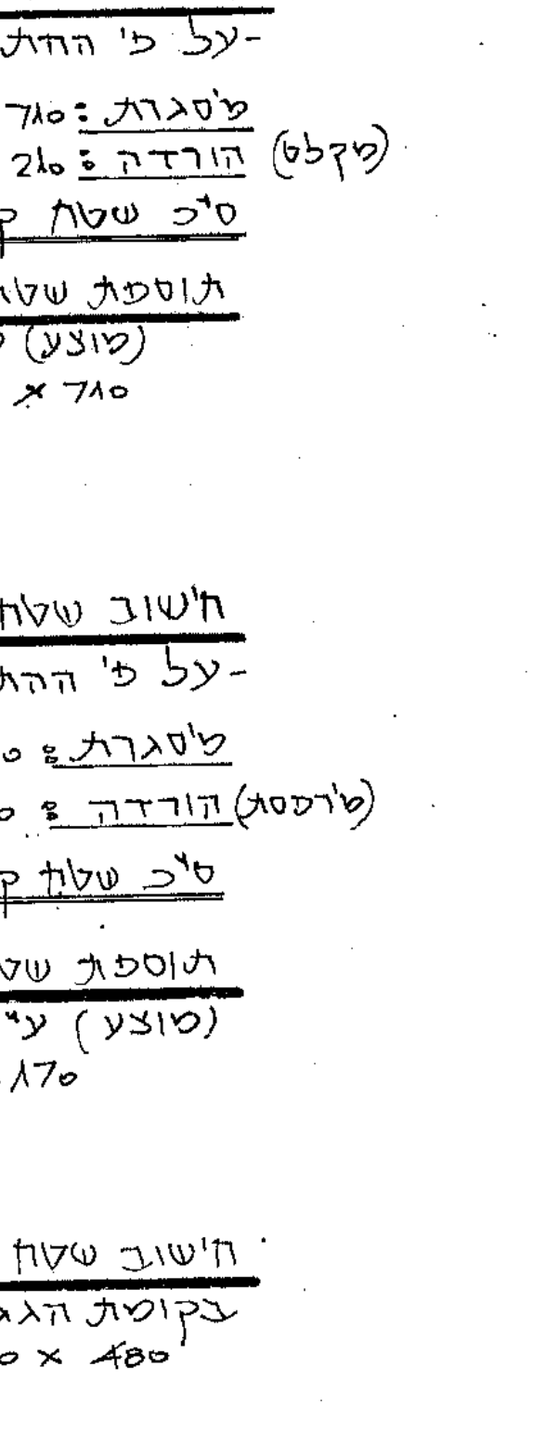
710
גגון מוצע (ק"מ)
מקלט בהתר
דירה ק"מת בהתר
860
710
630
540
170
230
480

חישוב שטח קומת קרקע (ק"מת):
-על פי ההתר-
מסגרת: 710 × 860 = 61,06
(מקלט) הורדה: 210 × 300 = 6,30
ס"כ שטח ק"ם בהתר 54,76 מ"ר

תוספת שטח בקומת קרקע:
(מוצע) ע"י גגון ק"ם
710 × 200 = 14,20 מ"ר

חישוב שטח קומה "א" (ק"מת):
-על פי ההתר-
מסגרת: 710 × 860 = 61,06
(מרפסת) הורדה: 170 × 230 = 3,91
ס"כ שטח ק"ם בהתר 57,15 מ"ר

תוספת שטח בקומה "א"
(מוצע) ע"י גגון ק"ם
170 × 230 = 3,91 מ"ר

חישוב שטח חדר מדרגות:
בקומת הגג (לא מחושב בהתר)
480 × 230 = 11,04 מ"ר

מפה טופוגרפית
1:250

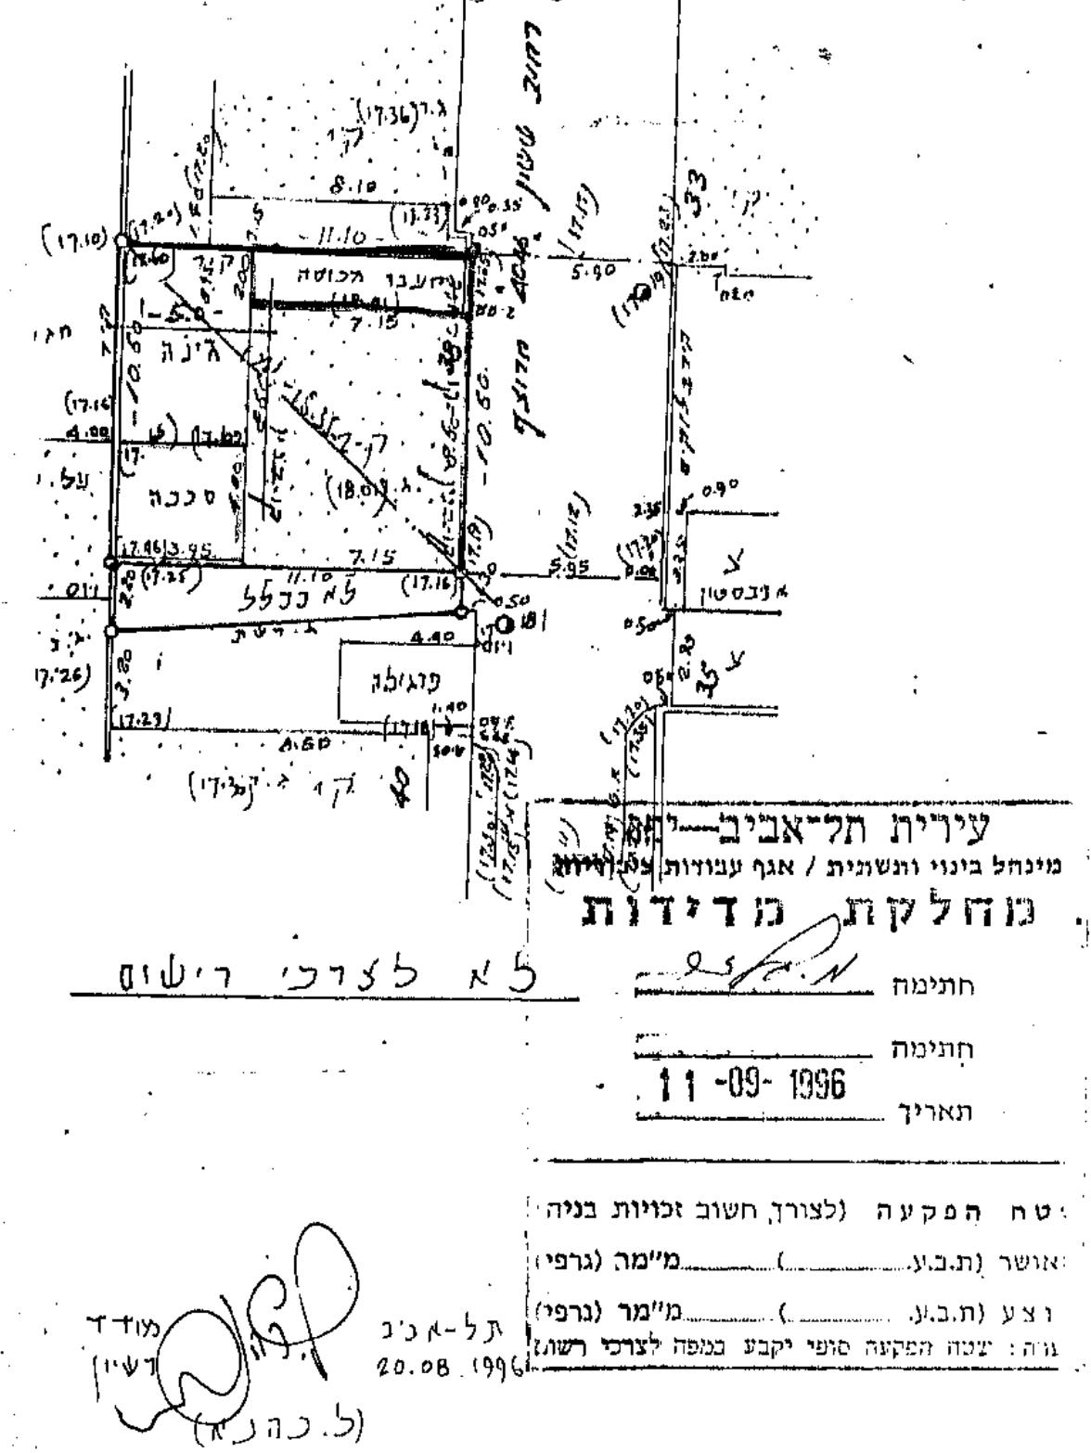
רחוב ששון
גינה
סככה
מכושה
לא נכלל
פרגולה
קו בניין

לא לצרכי רישום

תל-אביב-יפו
גוש 6135
חלקה 44 (חלק)
שטח מדוד 117.6 מ"ר
שטח לפי נסח 147.6 מ"ר

הוכן בשביל: ביתן
מהות הבקשה- היתר לתוספת בניה

תרשים הסביבה - 1:1250

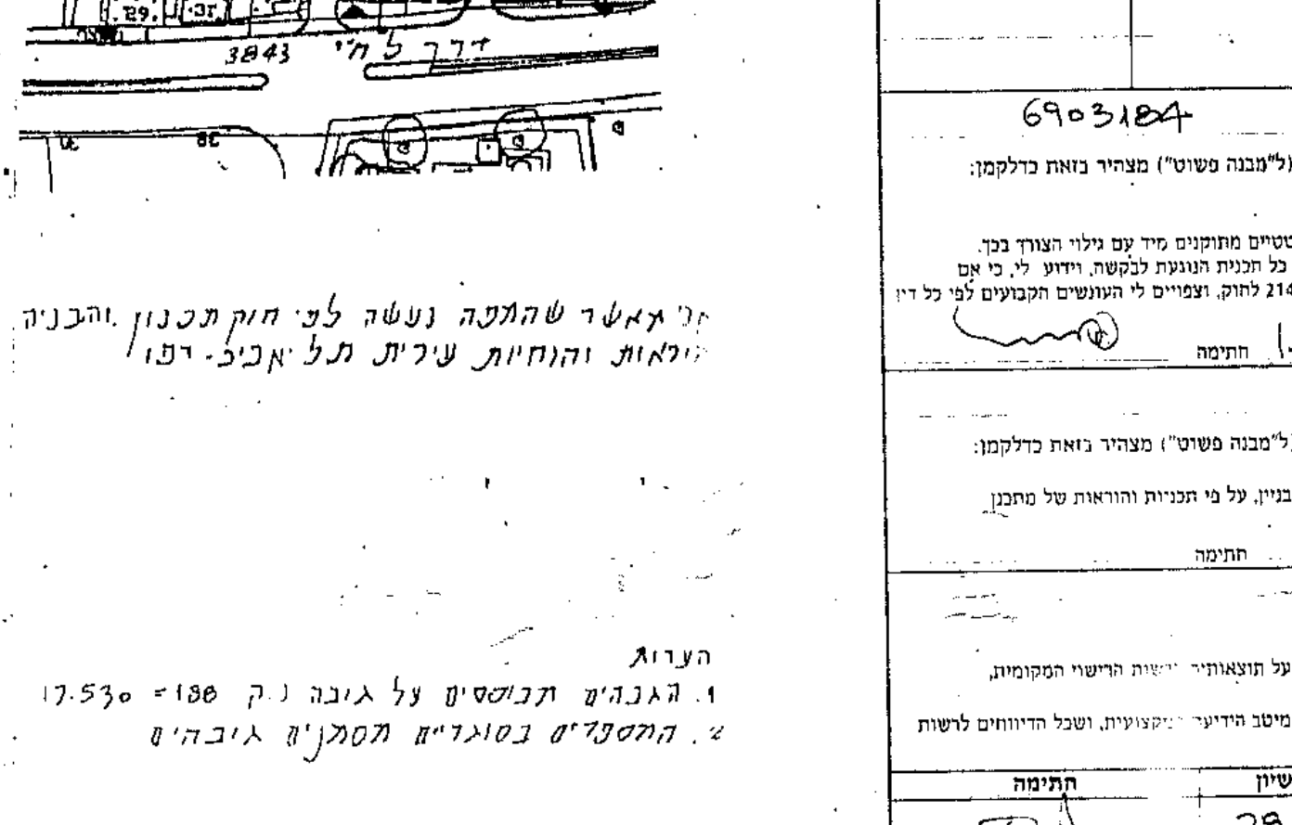
44
45
43
3843
דרך לחי

עיריית תל-אביב-יפו
מינהל בינוי ותשתית / אגף עבודות ציבוריות
מחלקת מדידות
חתימה
חתימה
תאריך 11-09-1996

שטח הפקעה (לצורך חשוב זכויות בניה)
אושר (ת.ב.ע. ......) מ"מה (גרפי)
ביצוע (ת.ב.ע. ......) מ"מר (גרפי)

הערה: שטח הפקעה סופי יקבע במפה לצרכי רשום.

מודד רשיון
(ל. כהנא)
תל-אביב
20.08.1996

לאון כהנא
משרד טכני למדידות, תכנון ופיקוח בע"מ
רח' ז'בוטינסקי 152 ת"א טל. 03-6957234

הנני מאשר שהמפה נעשה לפי חוק תכנון והבניה
ולתקנות והוראות עיריית תל-אביב-יפו

הערות
1. הגבהים מבוססים על גובה נ.ק 180 = 17.530
2. המספרים בסוגריים מסמנים גובהים

עיריית תל-אביב-יפו
מינהל ההנדסה, אגף רישוי ופיקוח על הבנייה
שדרות בן-גוריון 68 תל-אביב 64514 (פקס 5231340) טלפון 5217120, 5217045

22

חוק התכנון והבנייה, התשכ"ה-1965
תקנות התכנון והבנייה (בקשה להיתר תנאיו ואגרות), התש"ל-1970

על פי טופס 1 תקנה 2(א)

לכבוד ☐ הוועדה המקומית לתכנון ולבנייה
☐ רשות הרישוי המקומית

797 - 1991

בקשה להיתר בנייה או לשימוש במקרקעין

יש להקפיד למלא את כל הפרטים בטופס הבקשה ולצרף מסמכים כמפורט ברשימת התיוג המצורפת.

מתאריך	מס' הבקשה למידע	מס' בקשה קודמת להיתר בנייה	מס' תיק הבניין
7.10.96	N96-2003		3843-038

א. פרטי הנכס והמבקשים

הכתובת	רחוב	מס' בית	גוש	חלקה	תת חלקה	מגרש	הוראות התכניות החלות על המקום
	ששון	38	6135	44			2215

פרטים אישיים	שם משפחה / שם חברה / שם פרטי	מס' זהות/חברה או מס' רישום תאגיד	רחוב ומספר בית / ישוב ומיקוד	מספר טלפון / מספר פקס
מבקש 1	ביטון אילנה	057242620	ששון 38 ת"א	6876118
מבקש 2				
מבקש 3				
בעל הזכות בנכס	תב חלמיש			
החוכר				
עורך הבקשה הראשי	פוך דניאל	16310195	שד' בן גוריון 63 בת-ים	5079592 5075475
מתכנן שלד הבניין	סגל מיכאל	6903184	שטנד 12 ת"א	5230071 5821786

ב. מהות הבקשה

☒ בקשה לתוספת בנייה ☐ בקשה להרחבת דיור (במסגרת הרחבת דיור שכונתית)

☐ תוספת ... קומות לבניין

הכוללות: ☐ יחידות דיור ☒ תוספת שטח

☒ תוספת בנייה בקומה ק+א ☒ לחזית ☒ לאחור ☒ לצד

בשטח של 18,11 מ"ר

שטח הדירה/המשרד לאחר התוספות יהיה 147,36 מ"ר

☐ שינויים פנימיים הכוללים:

☐ אישור מצב קיים

☐

המקום משמש כיום ל- דירת מגורים

☒ בהיתר ☐ בלי היתר

ג. מפרט - תיאור הבקשה

תיאור הקיים על המגרש: בית פרטי, קרקע, ק"א + חדר מדרגות בלבד בקומה "ב" (קומת הגג) מגורים

שימוש עיקרי: ☒ מגורים ☐ מלונאות ☐ תעשייה ☐ חקלאי ☐ משרדים ☐ בידור ☐ בניין ציבורי ☐ מלאכה ☐ מסחר ☐ נופש וספורט ☐ שימוש אחר, פרט:

סוג העבודה או השימושים המוצעים: ☒ תוספת לבניין ☐ תיקונים ☐ שינוי בשימוש ממטרה למטרה ☐ שינוי לבניין ☐ הריסה

הגורם שמבוצעת בעבורו הבנייה: ☐ משרד ממשלתי ☐ מוסד ציבורי ☐ בנה ביתך ☐ רשות מקומית ☒ גורם פרטי ☐ אחר

שטחים	שטח המגרש/החלקה	שטח הבנייה הכולל המבוקש	אחוזי הבנייה
	117,6 מ"ר	147,36 מ"ר	125,28%

אם במסגרת הרחבת דיור שכונתית: מספר יחידות דיור מורחבות 1; מספר תכנית ההרחבה 2215

ד. חומרי הבנייה

סוג הבנייה: ☒ רגילה ☐ בית מוכן ☐ מתועשת ☐ אחר

קירות חיצוניים: ☐ בטון מזוין ☐ בלוקים ☐ אבן טבעית ☐ לבנים שרופות ☐ אחר

חומרי גימור: ☐ אבן מלאכותית ☐ אבן טבעית ☐ טיח ☐ זכוכית ☐ אחר

תקרות: ☐ בטון מזוין ☐ עץ ☐ אחר

גג: ☐ בטון מזוין ☐ אסבסט ☐ רעפים ☒ טיח ☐ אחר

גדרות: ☐ אבן טבעית ☐ בלוקים ☐ רשת ☐ אבן מלאכותית ☐ ברזל ☐ אחר ☐ בטון ☐ עץ

ה. השטחים המבוקשים לבנייה (על פי תכנית הבנייה) והמותרים לבנייה (על פי "אסמכתא": חוק, תקנות, תכנית) בכל מפלס בנפרד ולפי שימוש

הקומה/המפלס בבניין	(א) קיים בהיתר	קיים ללא היתר ומבוקש לאישור בדיעבד	בנייה חדשה מוצעת	מותר	סך כל שטחי הבנייה העיקריים מ"ר	% משטח המגרש	סך כל השטחים המותרים	מקלט	(ב) סך כל שטחי השירות מ"ר	% משטח המגרש	סך כל השטחים המותרים	(ג) סך כל שטחי הבניין מ"ר	% משטח המגרש	סך כל השטחים המותרים
ק ±0.00	54,76	14,20		70,56	68,96	58,63	70,56	6,30	6,30	5,35	11,76	75,26	63,98	82,32
א +2.99	57,15	3,91			61,06	51,92						61,06	51,92	
ב +5.98	11,04				11,04	9,38						11,04	9,38	
ס"ה מעל הקרקע	122,95	18,11		70,56	141,06	119,93	70,56	6,30	6,30	5,35		147,36	125,28	(700)+164,64
ס"ה מתחת לקרקע														
סה"כ	122,95	18,11		70,56	141,06	119,93	70,56	6,30	6,30	5,35		147,36	125,28	164,64

ו. פרטי הבנייה – לשימוש הלשכה המרכזית לסטטיסטיקה

מספר היתר הבנייה 4181

תאריך היתר הבנייה: שנה 86 חודש 2

החלטת רשות מוסמכת
מאשר מתן פטור מבניית מקלט עבור תוספת בניה בשטח 18 מ"ר
הפטור מותנה בתקינות המקלט הקיים בבניין

ז. קווי בנייה

הכיוון	מוצע	מותר	הסטייה במטר	ב-%
לרחוב (שם) ששון	0,00	0,00	—	—
לרחוב (שם)				
לצד	0,00	0,00 3,00		
לאחור	4,00	5,00		

ח. מספר יחידות דיור

☐ אם השימוש המבוקש הוא מגורים – רשום להלן:

מספר דירות קיימות 1 → מספר הדירות המבוקשות → מספר הדירות המותרות 1

ט. הבקשה מוגשת לאישור

☐ הוועדה המקומית
☒ רשות הרישוי המקומית
☐ רשות הרישוי המקומית באמצעות מורשה להיתר

י. הצהרת עורך הבקשה הראשי

יא. חתימות נוספות

	תאריך	שם	חתימה
המבקש	15.11.96	דניאל פוך	X
בעל הזכות בנכס / החוכר			
מתכנן שלד הבניין	15.11.96	מיכאל סגל	

יב. מינויים מטעם מבקש ההיתר

	שם משפחה ושם פרטי	מספר טלפון	מספר פקס
עורך הבקשה הראשי 1.	פוך דניאל	שד' בן גוריון 63 בת-ים 5079592	5075475

אני מצהיר, כי טרם מינויו אחראי/ים לביקורת על ביצוע עבודות הבנייה את כולם או את קצתם בתחומים האלה:

חתימת המבקש על המינויים X

יג. הצהרות

הצהרת עורכי הבקשה: אני עורך בקשה ראשי דניאל פוך

	תאריך	שם משפחה ושם פרטי	מספר רישיון
עורך בקשה ראשי	15.11.96	פוך דניאל	29948

הצהרת מתכנן שלד הבניין: אני החתום מטה סגל מיכאל, מספר זהות 6903184, מהנדס רשוי מס' 09036

תאריך 15.11.96

הצהרת אחראים לביקורת: אני דניאל פוך

תאריך	שם משפחה ושם פרטי	מספר רישיון
15.11.96	פוך דניאל	29948

ניתן פטור מחובת לבניית מקלט
15/11/96

גיל אאורל - ברוק
מהנדס העיר
יגאל מ. בן-ישי, מהנדס
מ"א 2244046
מפקח מחוז דן

נסרק

ארכות נמוכה