

1020-22

מפה מצבית + טופוגרפית



1:250

עיריית תל-אביב
מינהל ההנדסה
מחלקת מדידות

המפה עברה במחלקות:

- ☒ דרכים
- ☒ מים
- ☒ כביש
- ☒ הנחיות צוות
- ☐ אשפה
- ☐ חניה
- ☐ נחיתת אילן
- ☒ **עיריית תל-אביב**
- ☒ **מחלקת מדידות**
- ☒ **מנהל המסד**

תרשים הסביבה 1:250

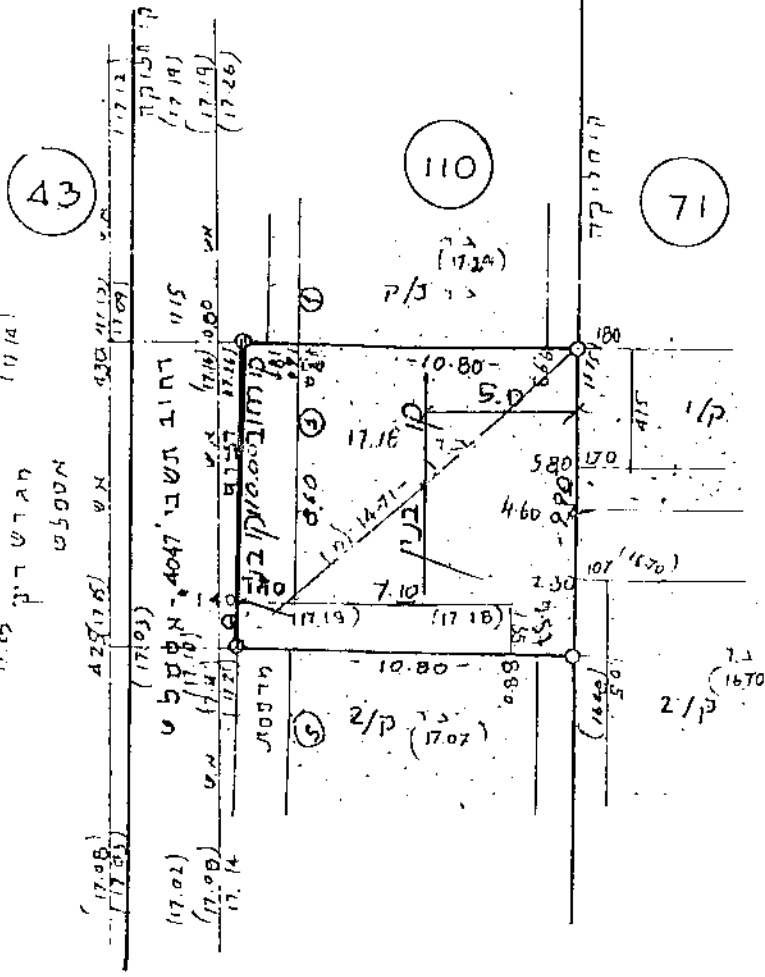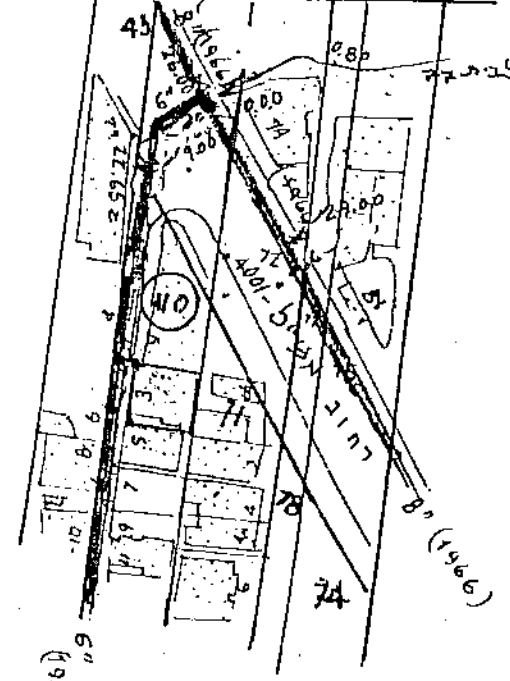

לא לצרכי רישום!

תל-אביב
 תאריך: 18.4.01
 חודד מוטמך
 רשיון מס' 317

א. פגירסקי רחל רחל 33
 050-330470

ענני הגביר קטורים 5 א"מ מס' 187 = 17.54

תל-אביב-יפו

גוש 6035

חלקה 100 (חלק)

השטח מדוד 80 מ"ר

השטח לפי נסח 146 מ"ר

רחוב תשבי מס' 3

הוכן עבור: משומר

מהות הבקשה קבלת היתר למבנה חרש

עיריית תל-אביב-יפו
 מינהל בניין ותשתית / אנף עבודות עיבודיות
 מחלקת מדידות

חתימה: _____
 חתימה: _____
 תאריך: 19.06.2001

שם המפקח (לצורך חשבוני זכויות בניה): _____
 (ת.ב.ע.) (מ"מור (גרפיק))

עיריית תל-אביב-יפו / מינהל הנדסה
מחלקת המדידות


אישור כתובת

רחוב: תשבי מס' 3
 דוכן: מס'
 רחוב: מס'
 תאריך: 19.4.01 חתימה: _____

26



1:250

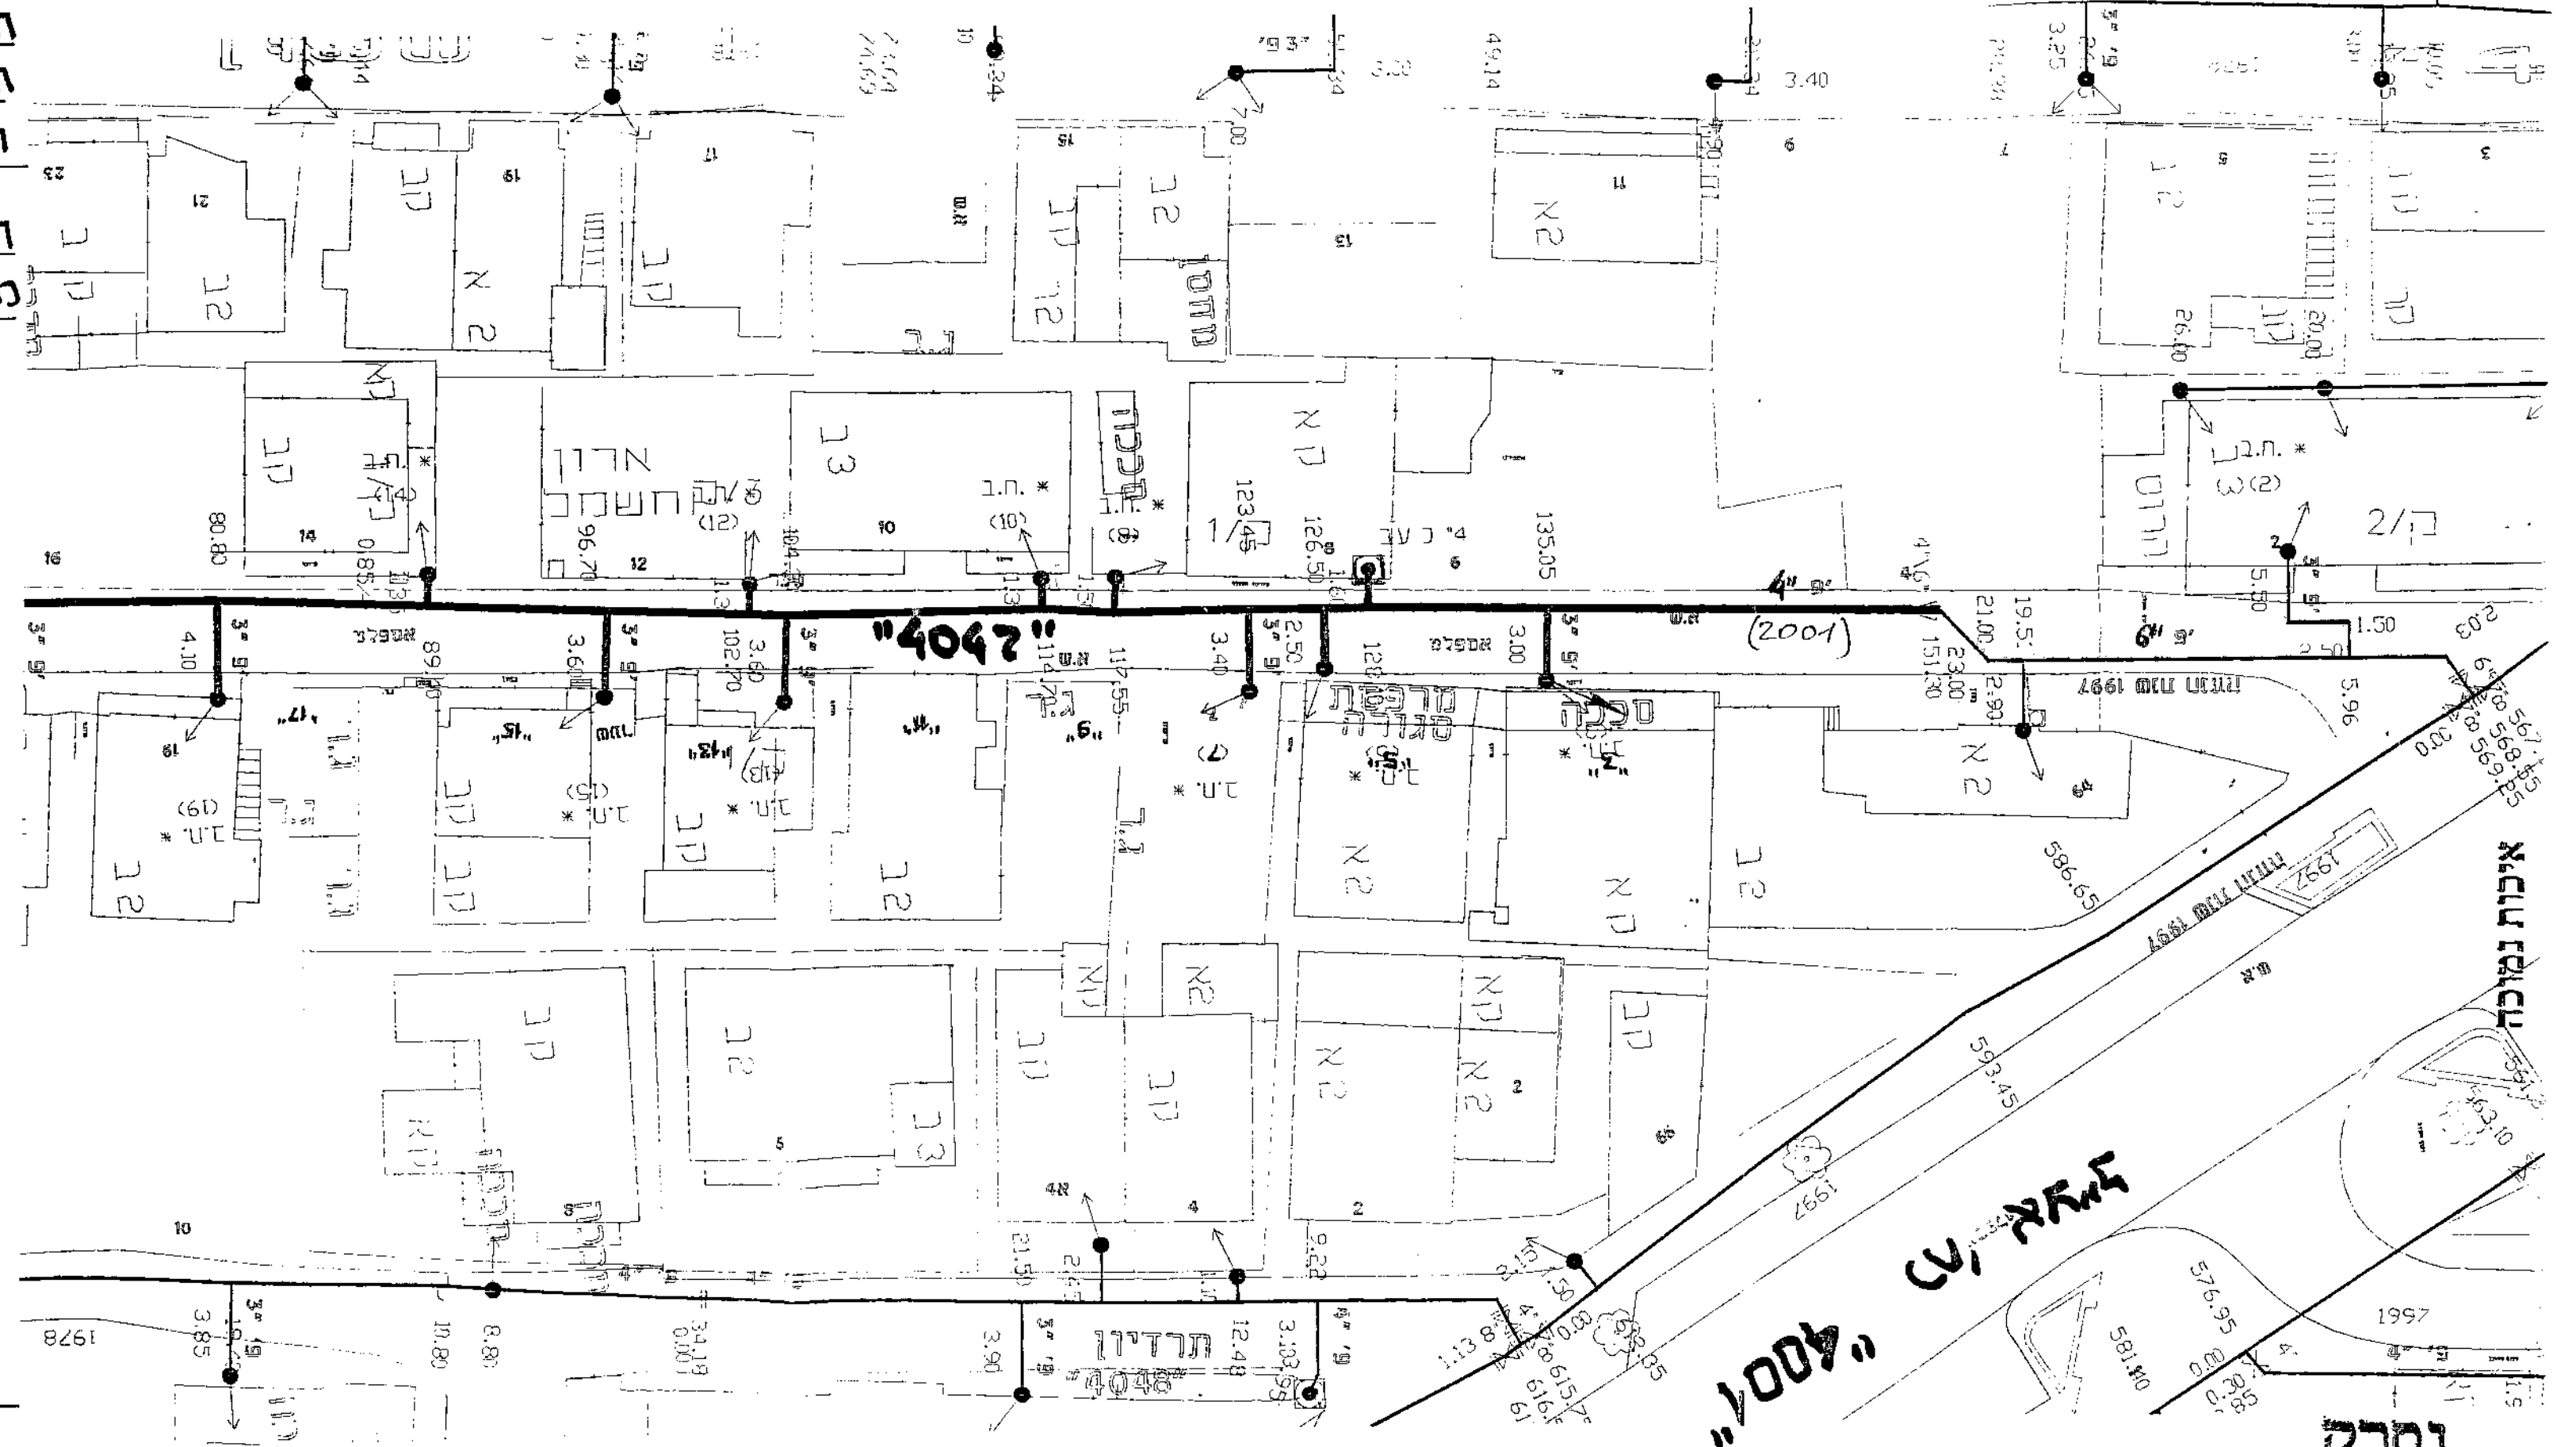

4001
 4047

נסרק