סוף מסמך

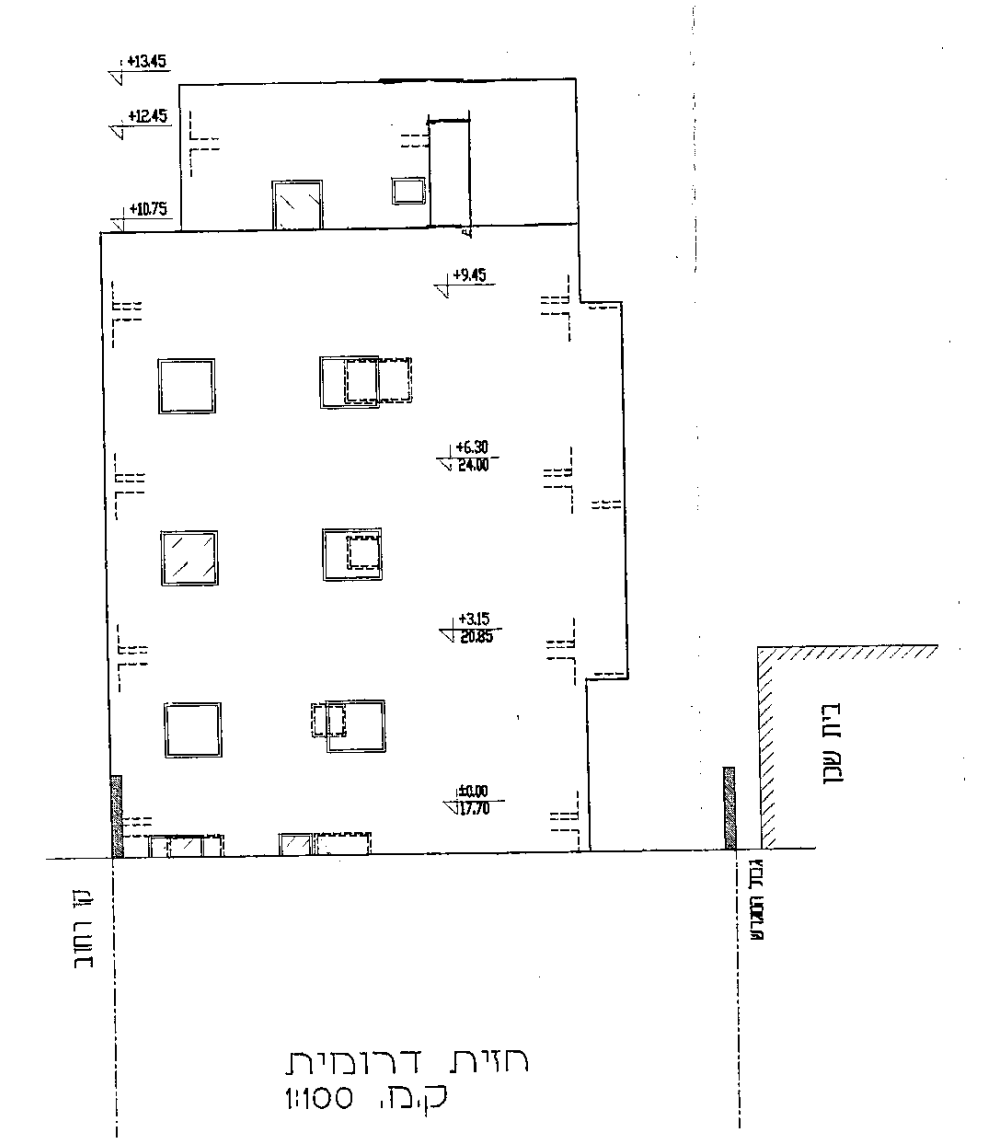
7 קומות
גמר טיח חלק בגוון בהיר
רחוב
בית שכן
קו רחוב
גבול מגרש
חזית דרומית
ק.מ. 1:100

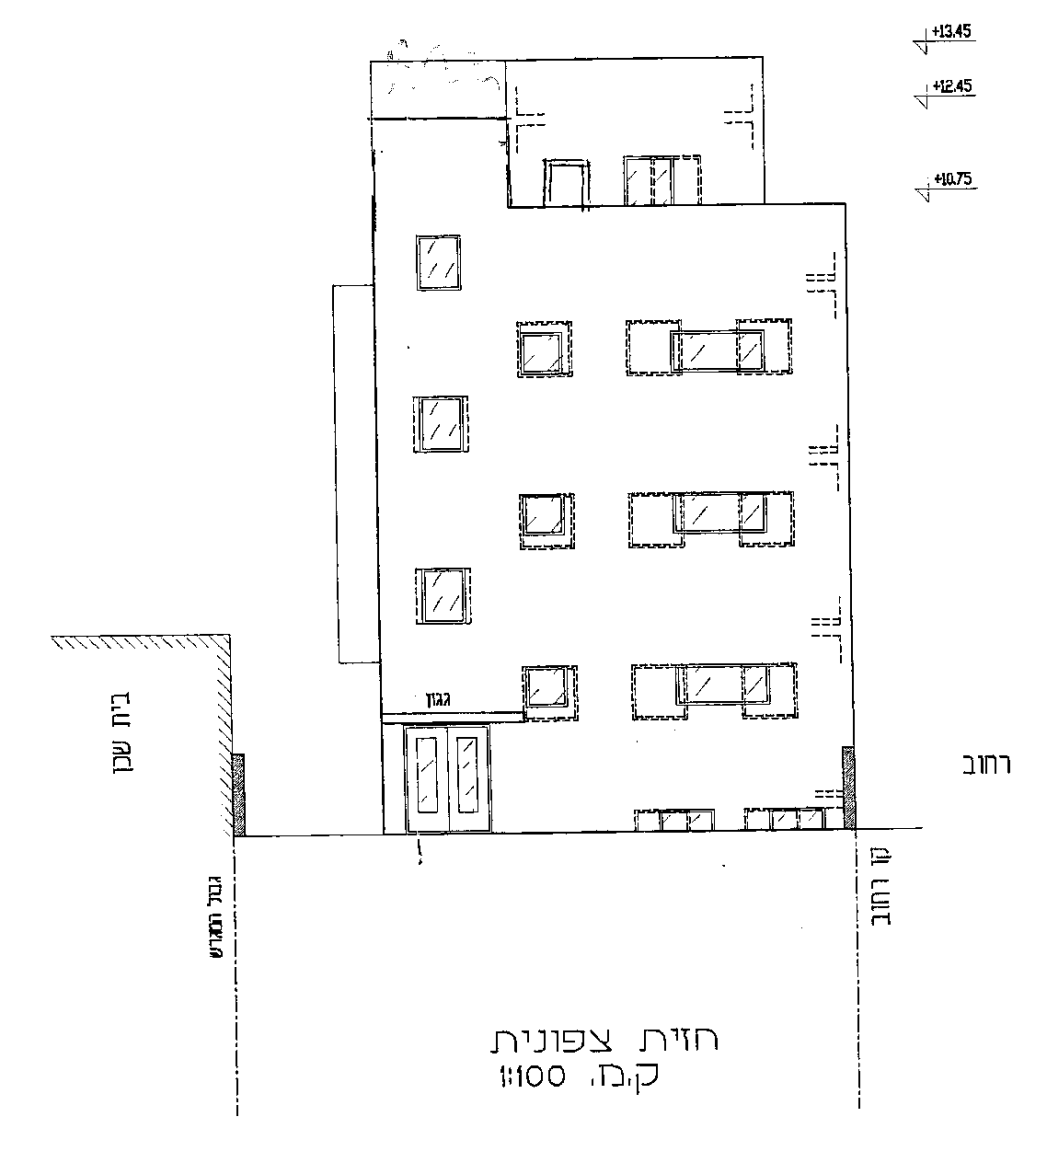
גמר טיח חלק בגוון בהיר
רחוב
בית שכן
קו רחוב
גבול מגרש
חזית צפונית
ק.מ. 1:100

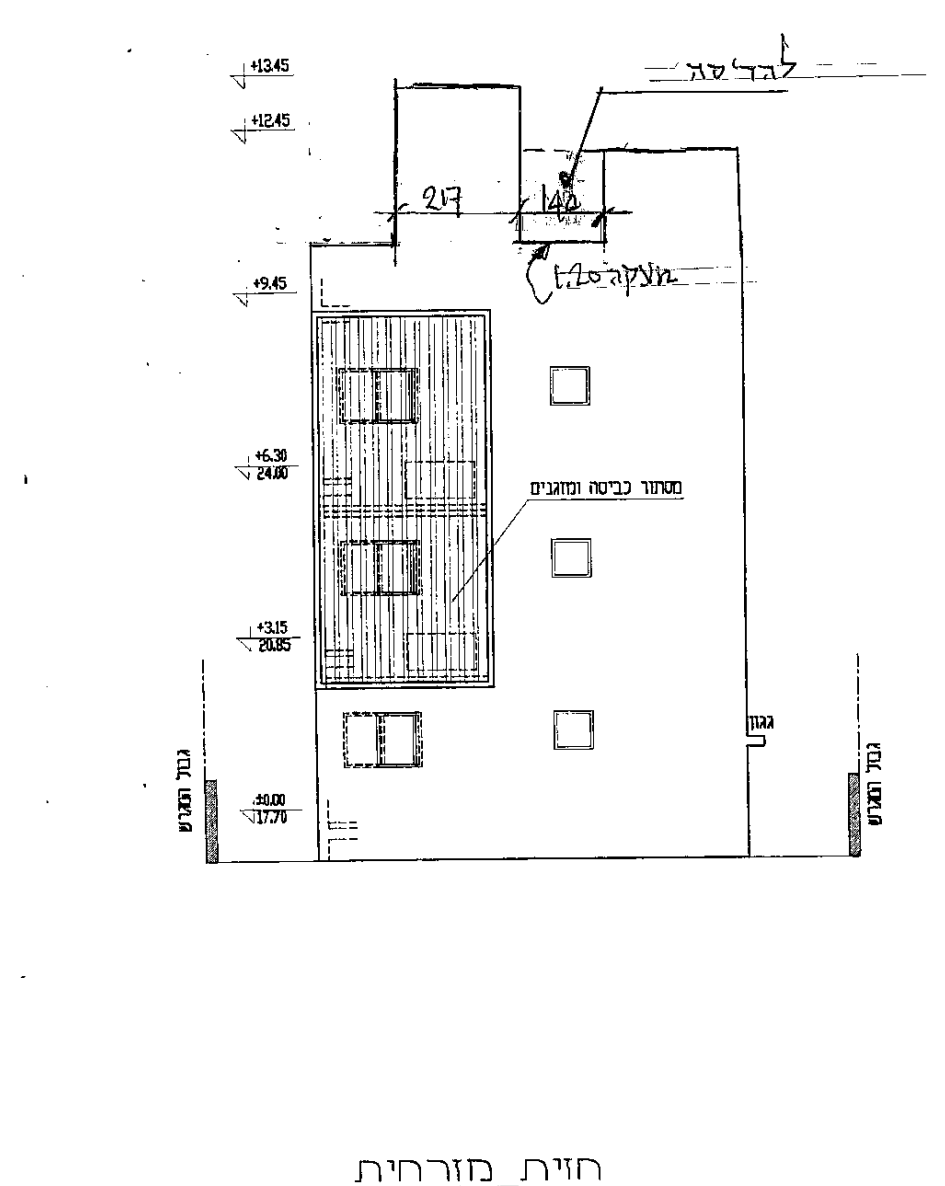
להריסה
מעקה
מסתור כביסה ומזגנים
גבול מגרש
חזית מזרחית
ק.מ. 1:100

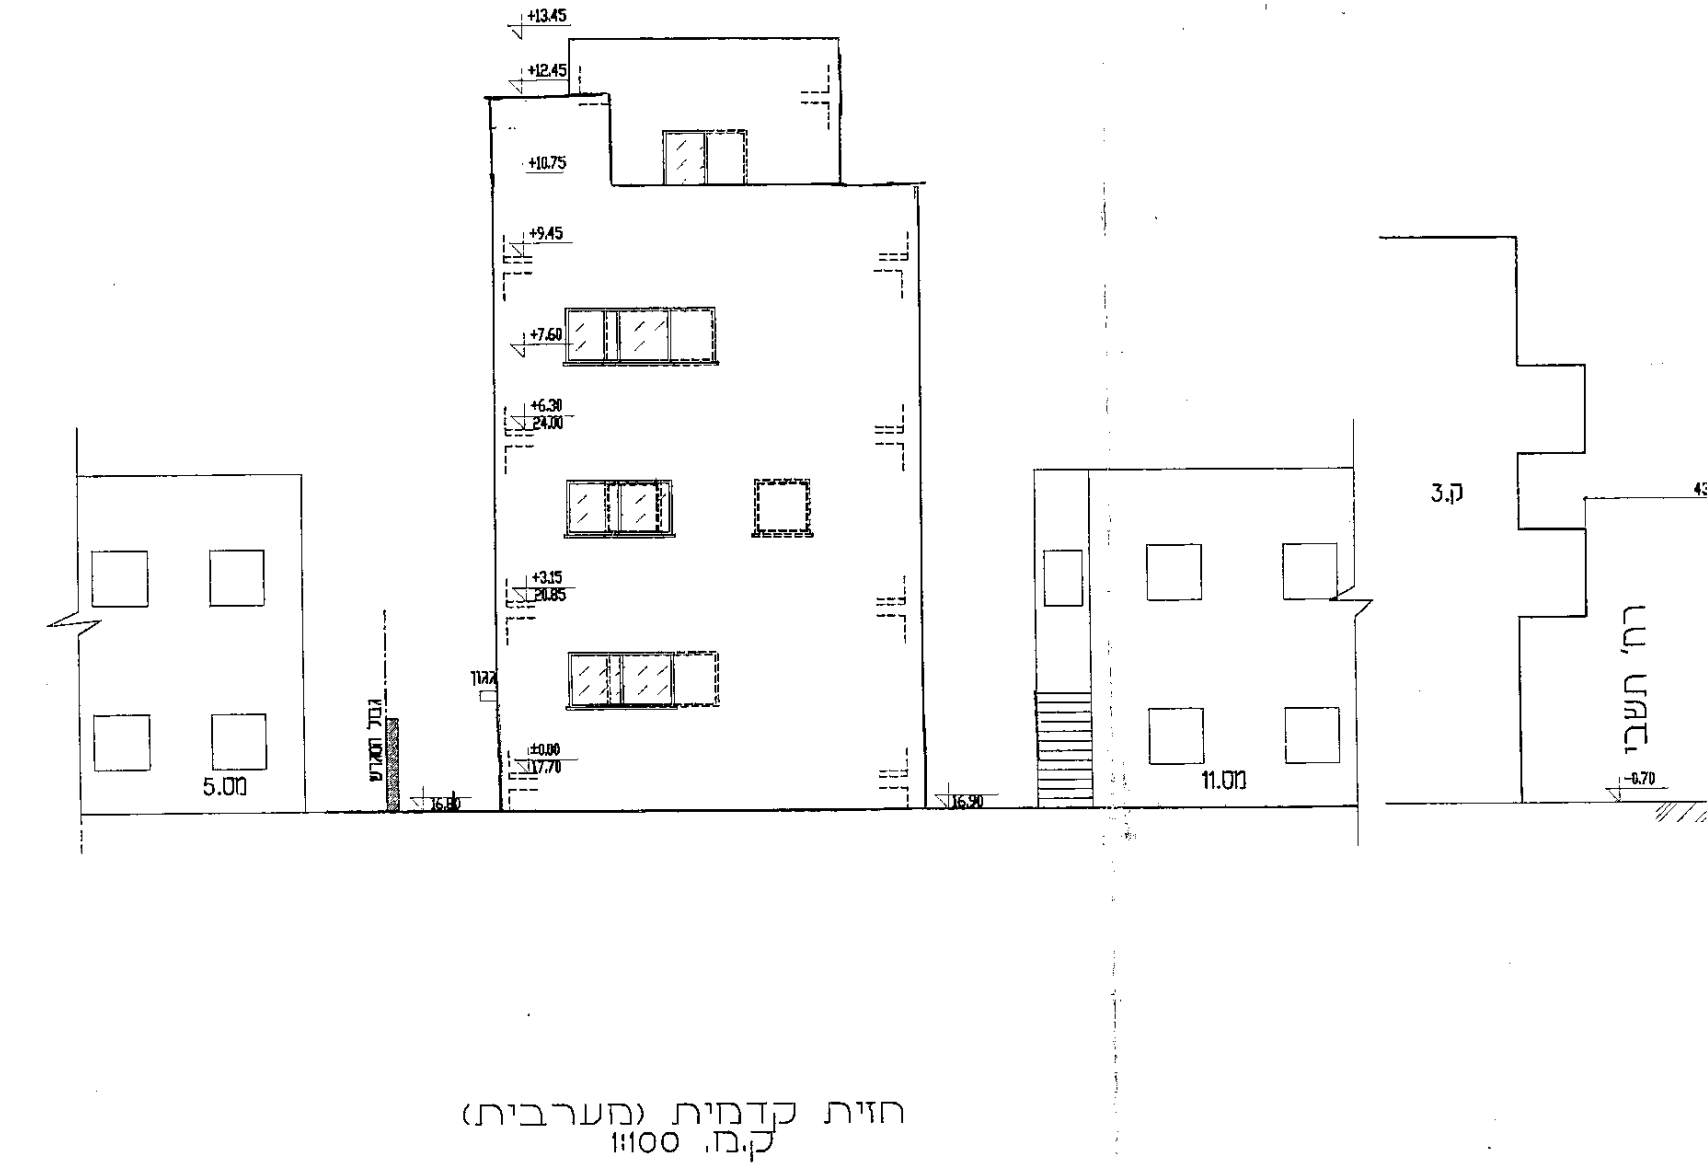
5.00
11.00
גבול מגרש
חזית קדמית (מערבית)
ק.מ. 1:100

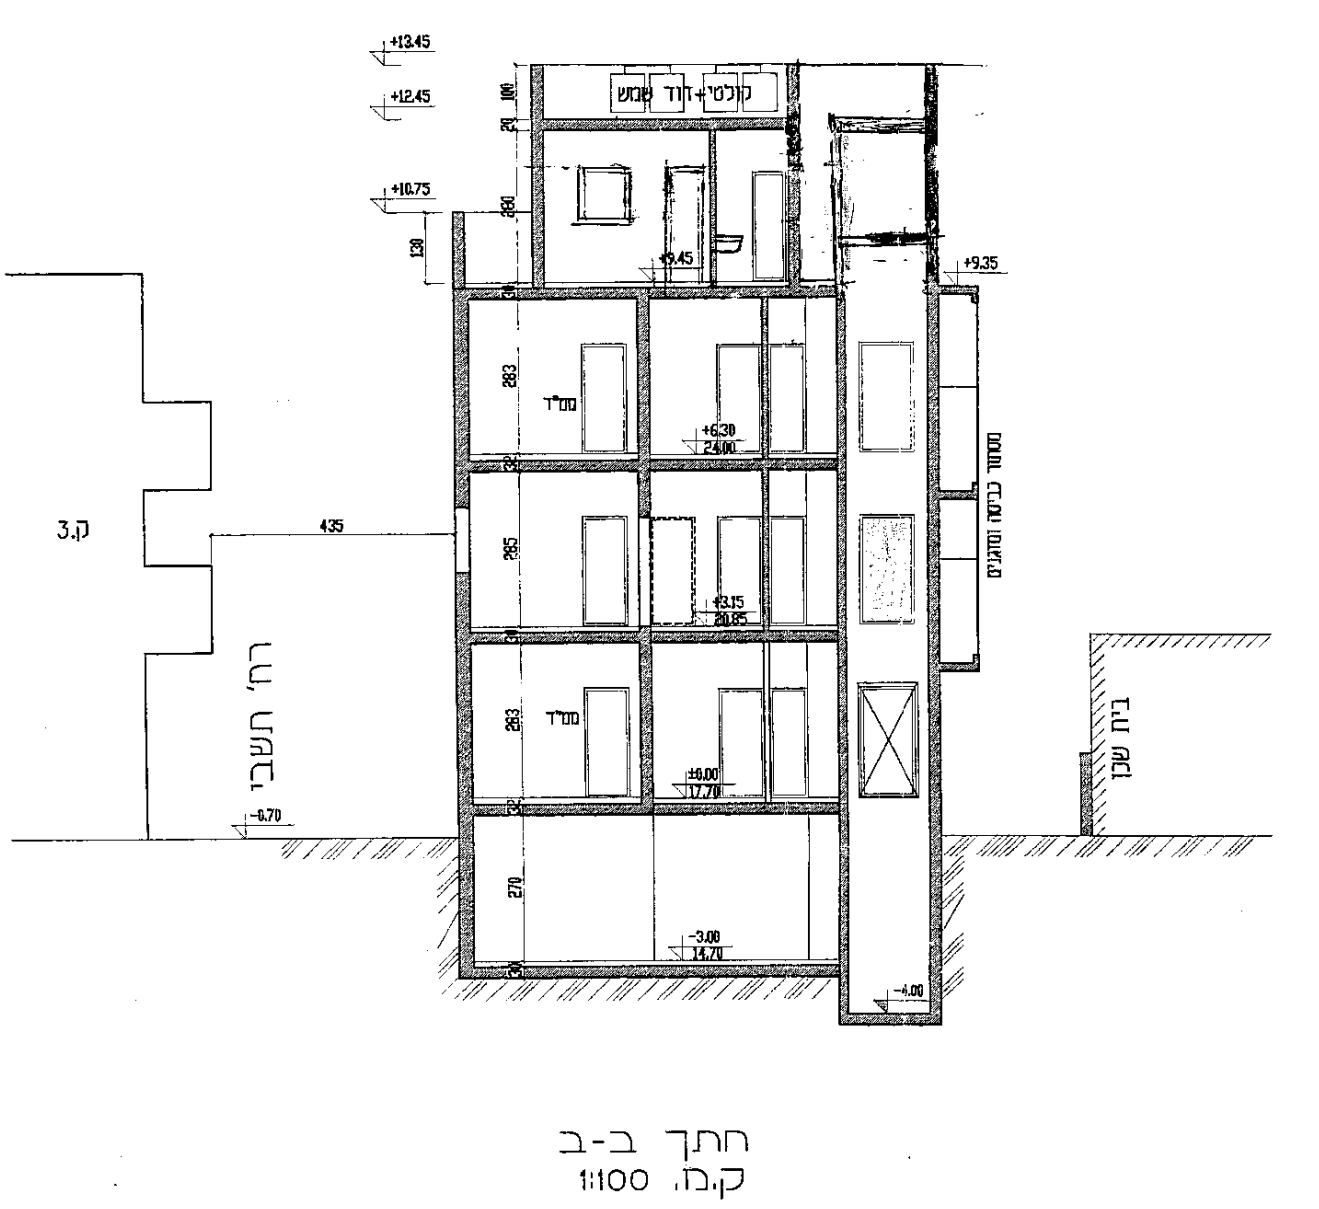
ק.3
רח' תשבי
חדר מכונות
בית שכן
חתך ב-ב
ק.מ. 1:100

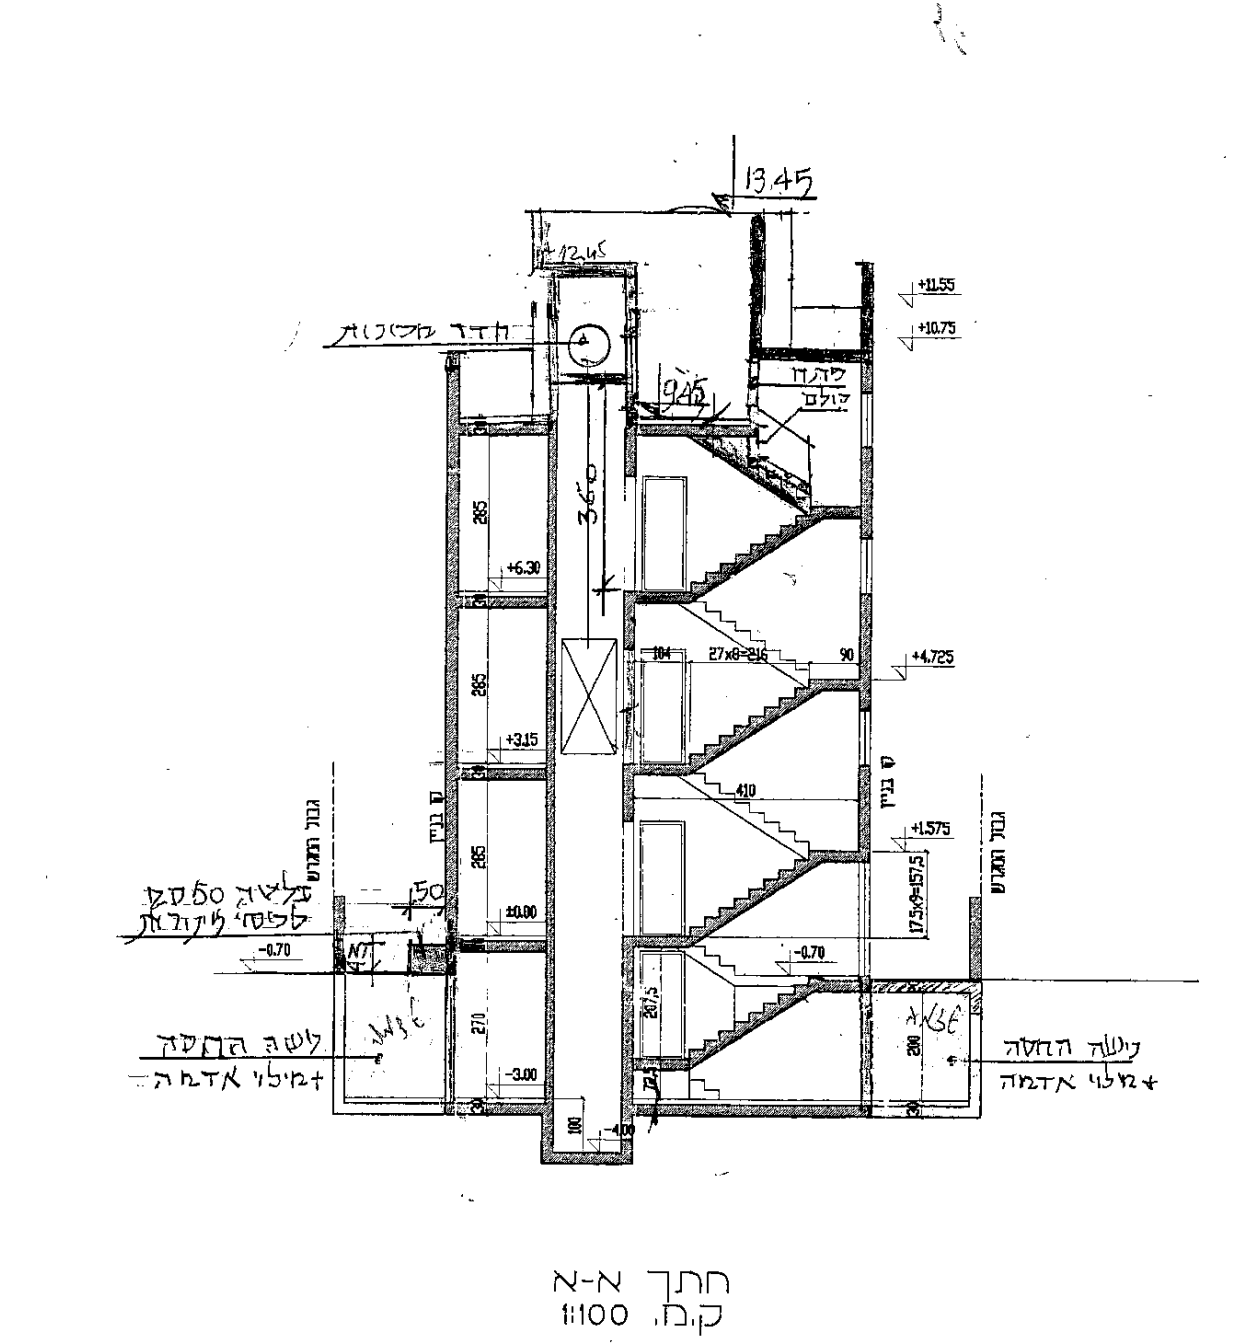
13.45
חדר מכונות
יציאה לגג
גבול מגרש
שכבת 60 ס"מ
קלסורי לניקוז
לישה התקנה
+מילוי אדמה
חתך א-א
ק.מ. 1:100

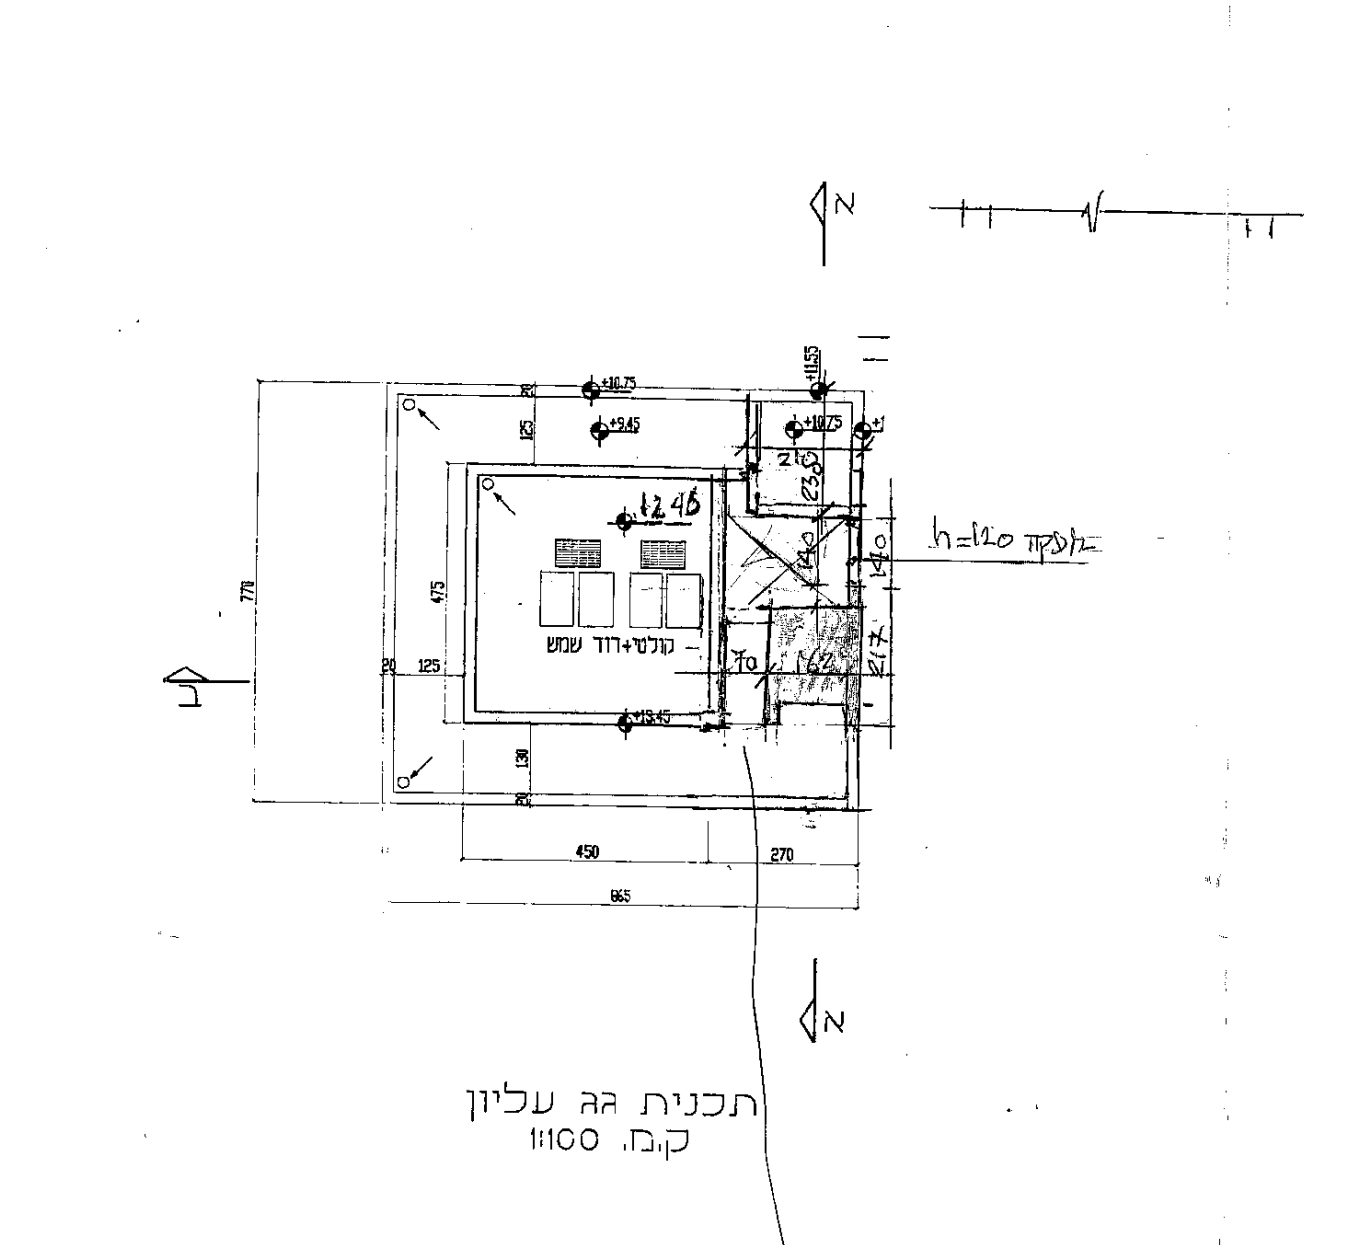
h=1.60 מעקה
קולטי שמש
תכנית גג עליון
ק.מ. 1:100

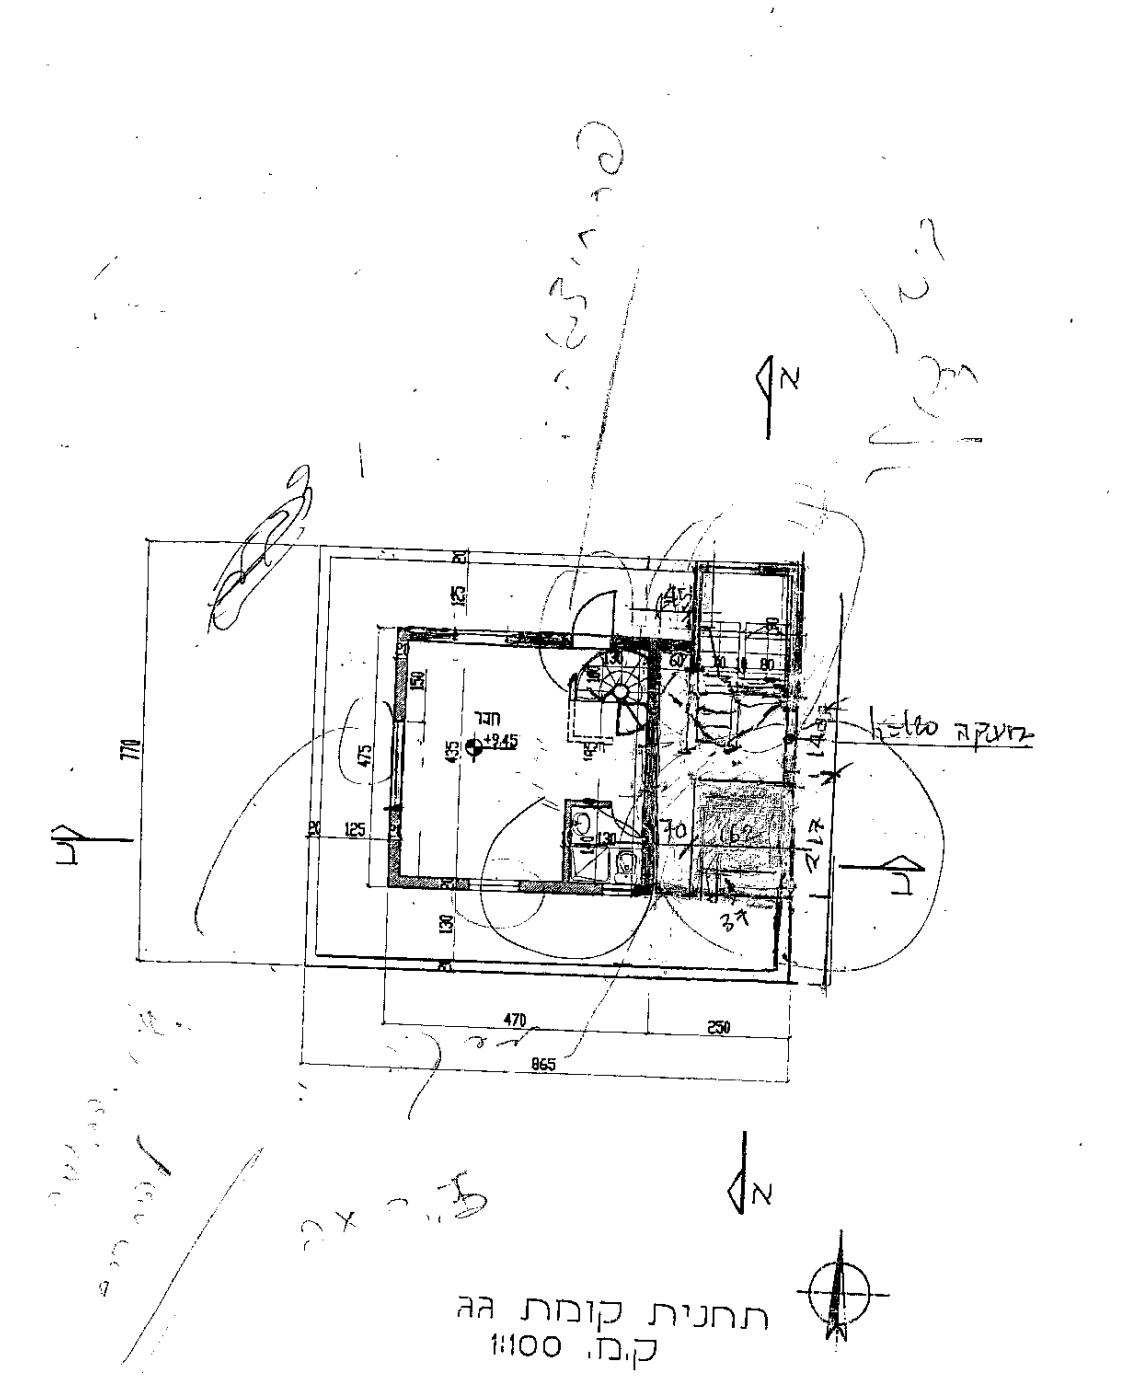

תכנית קומת גג
ק.מ. 1:100

3.5×
1.7×2

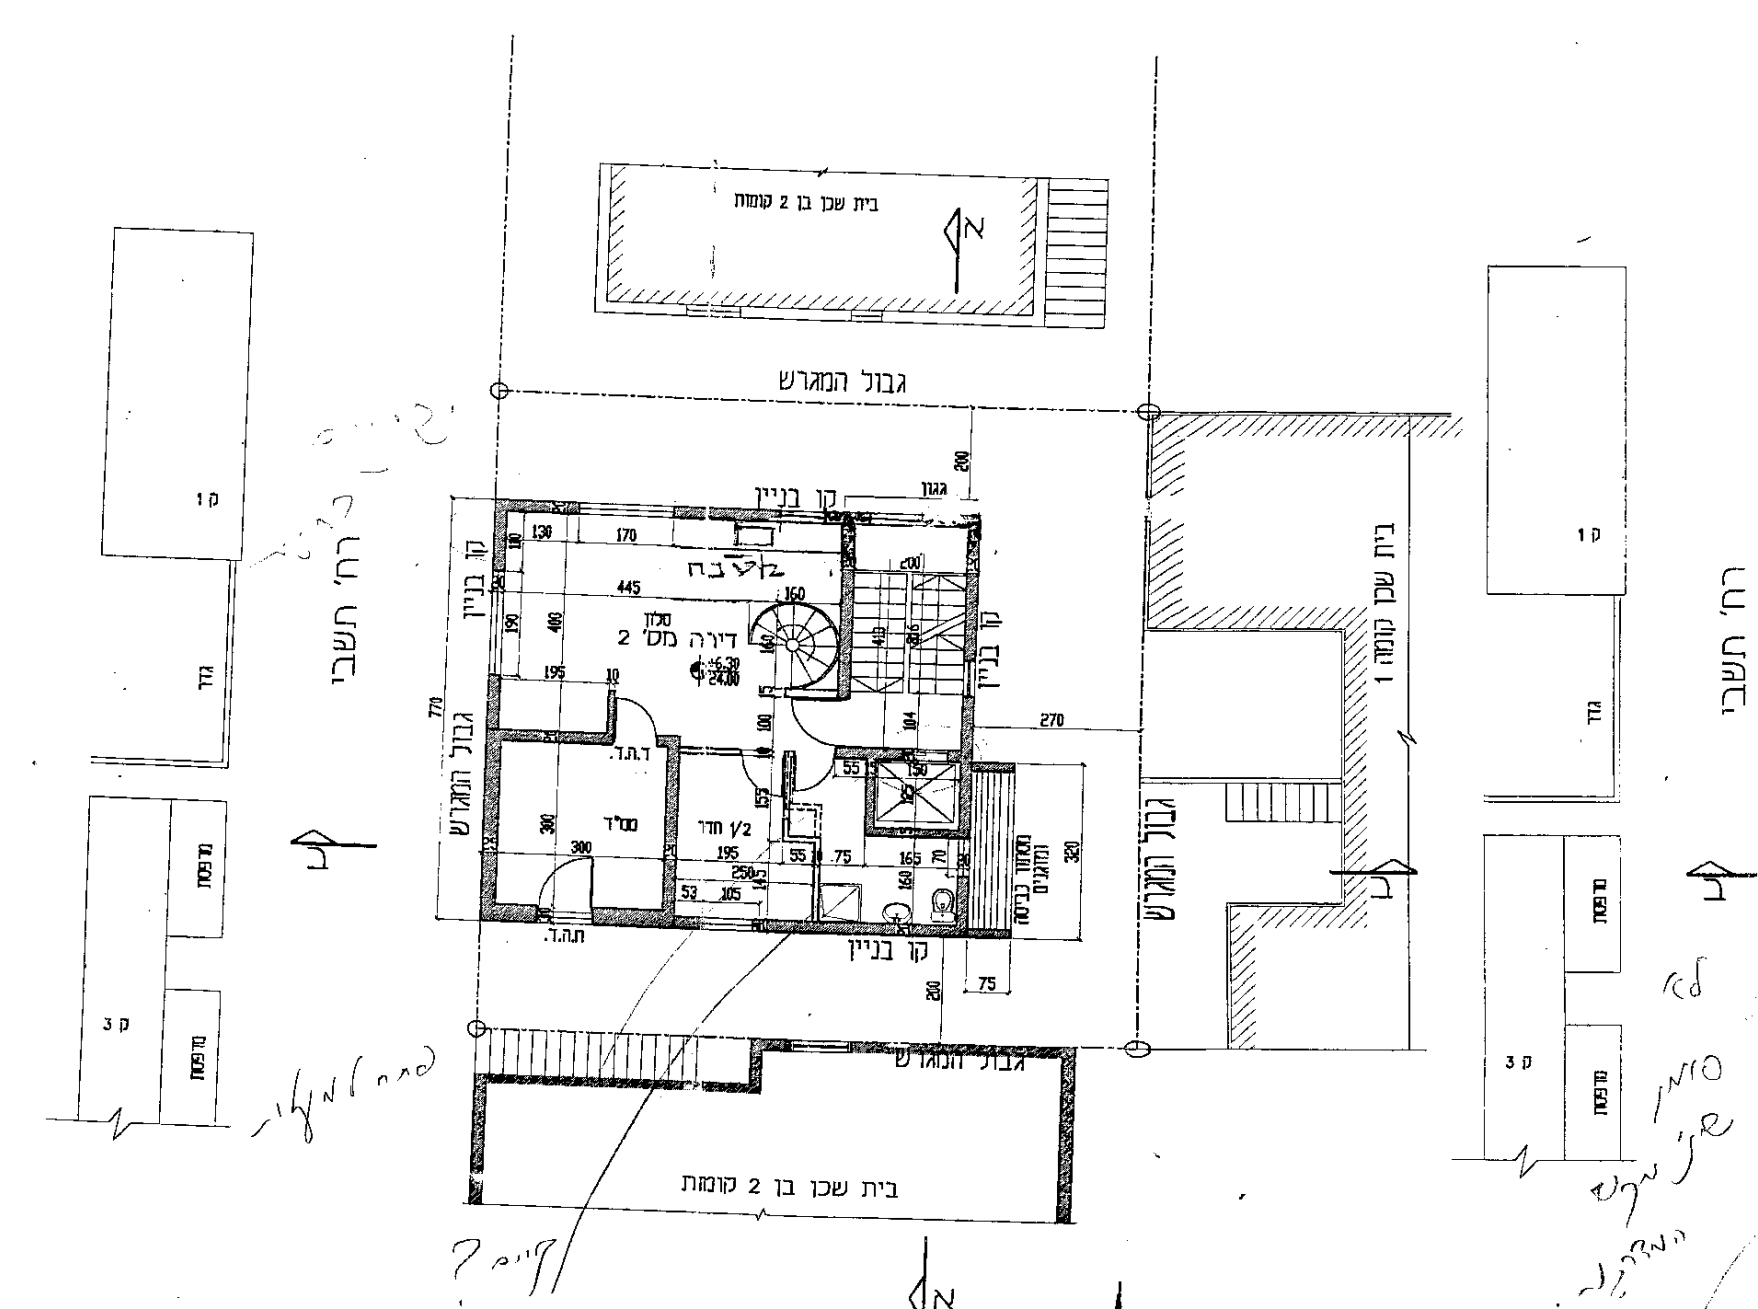
בית שכן בן 2 קומות
גבול המגרש
קו בניין
מטבח
דירה מס' 2
רח' תשבי
בית שכן בן 2 קומות
תכנית קומה ג'
ק.מ. 1:100

לאי סימון של השינויים בהריסה קודמת

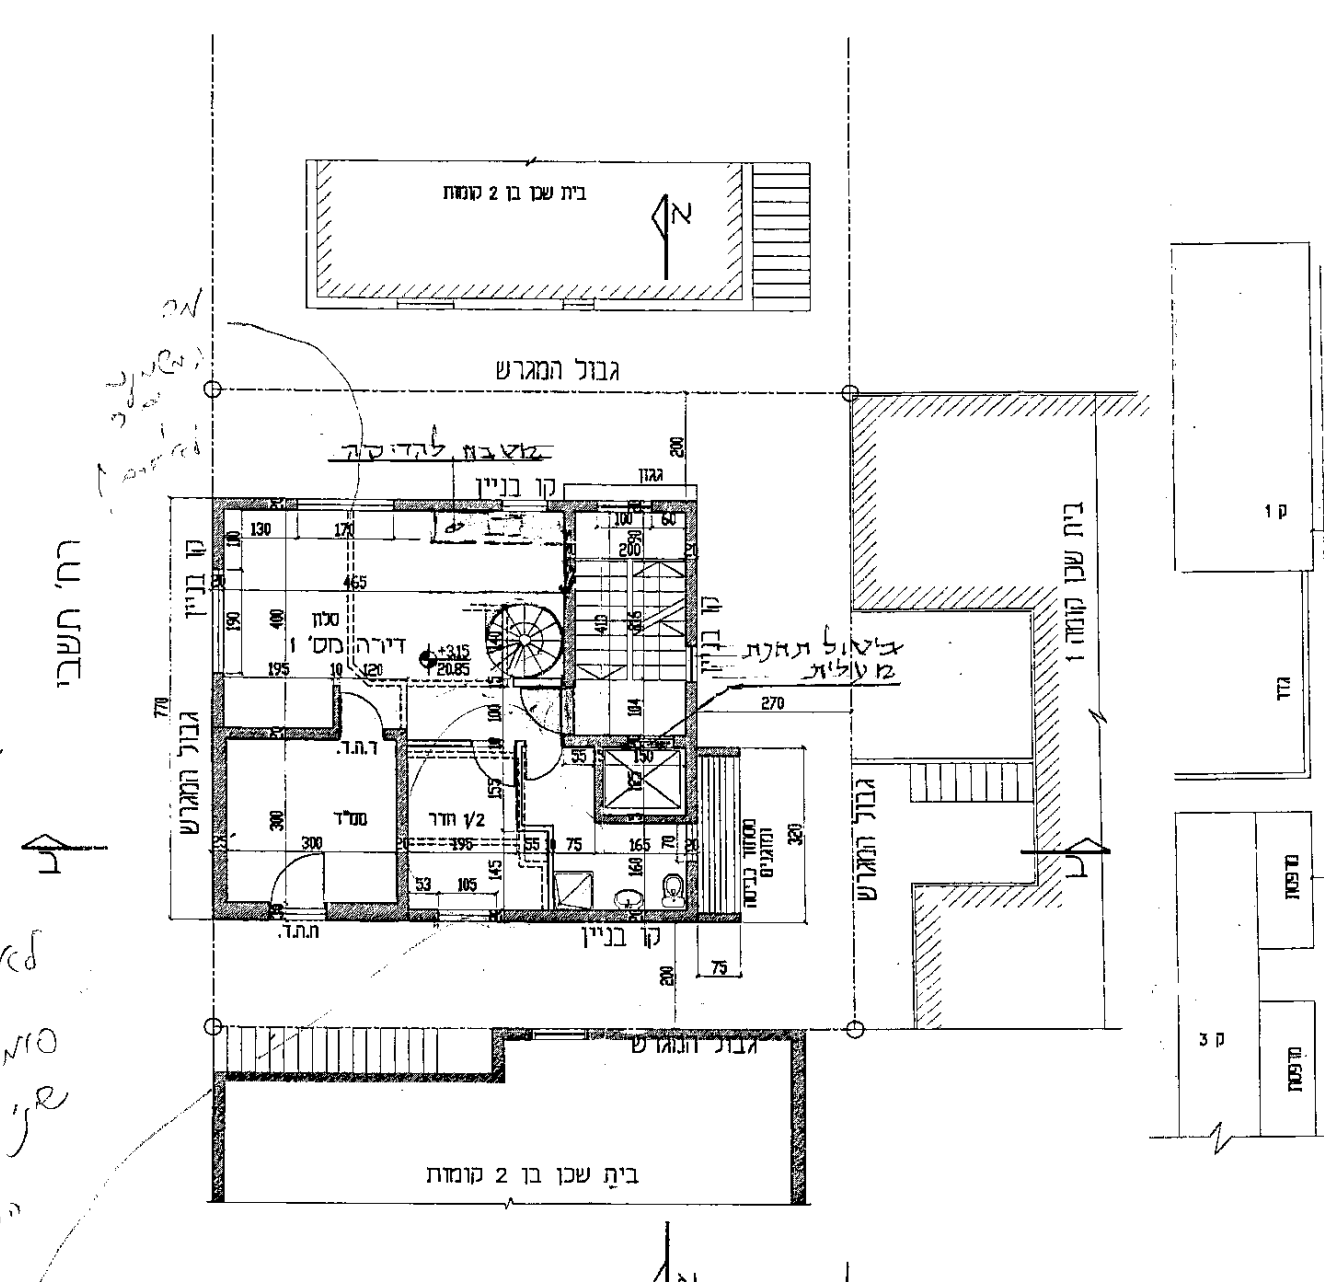
בית שכן בן 2 קומות
גבול המגרש
קו בניין
דירה מס' 1
רח' תשבי
בית שכן בן 2 קומות
תכנית קומה ב'
ק.מ. 1:100

לאי סימון של השינויים בהריסה קודמת

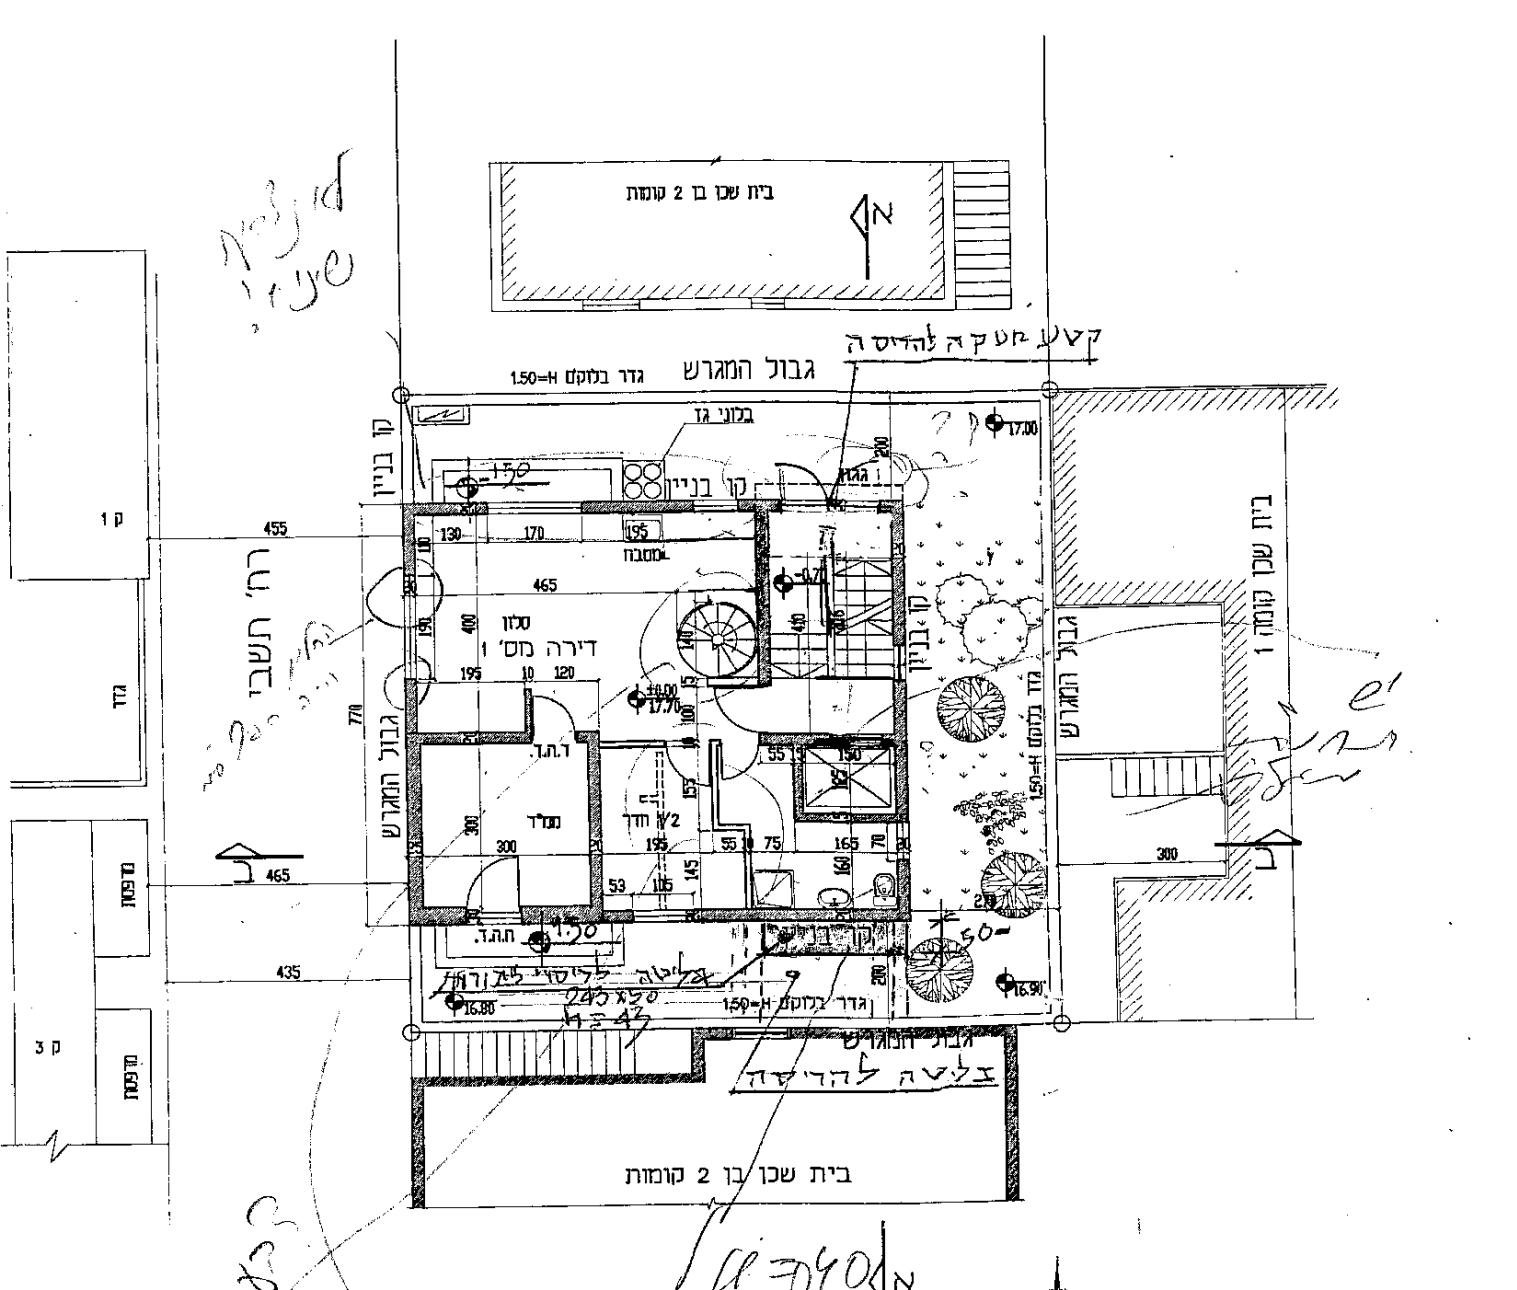
בית שכן בן 2 קומות
קטע חצר לשימוש הדירה
גבול המגרש
דירה מס' 1
רח' תשבי
מרפסת להריסה
בית שכן בן 2 קומות
תכנית קומה א' (קרקע)
ק.מ. 1:100

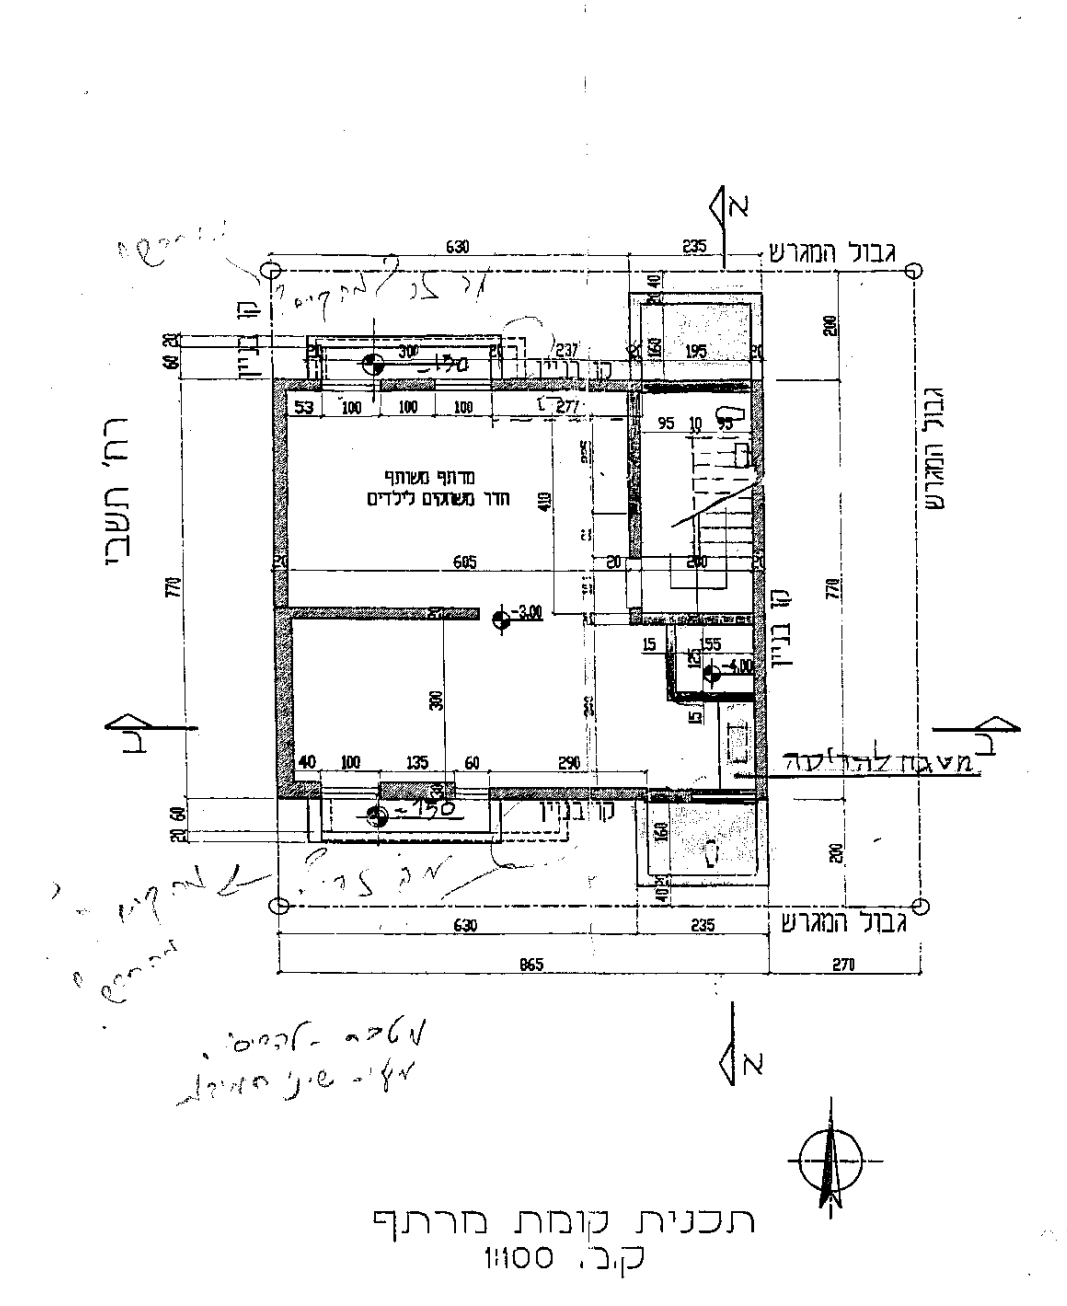
גבול המגרש
מרחב מוגן
חדר משחקים לילדים
רח' תשבי
מעבר לחניה
תכנית קומת מרתף
ק.מ. 1:100

חישוב שטחים

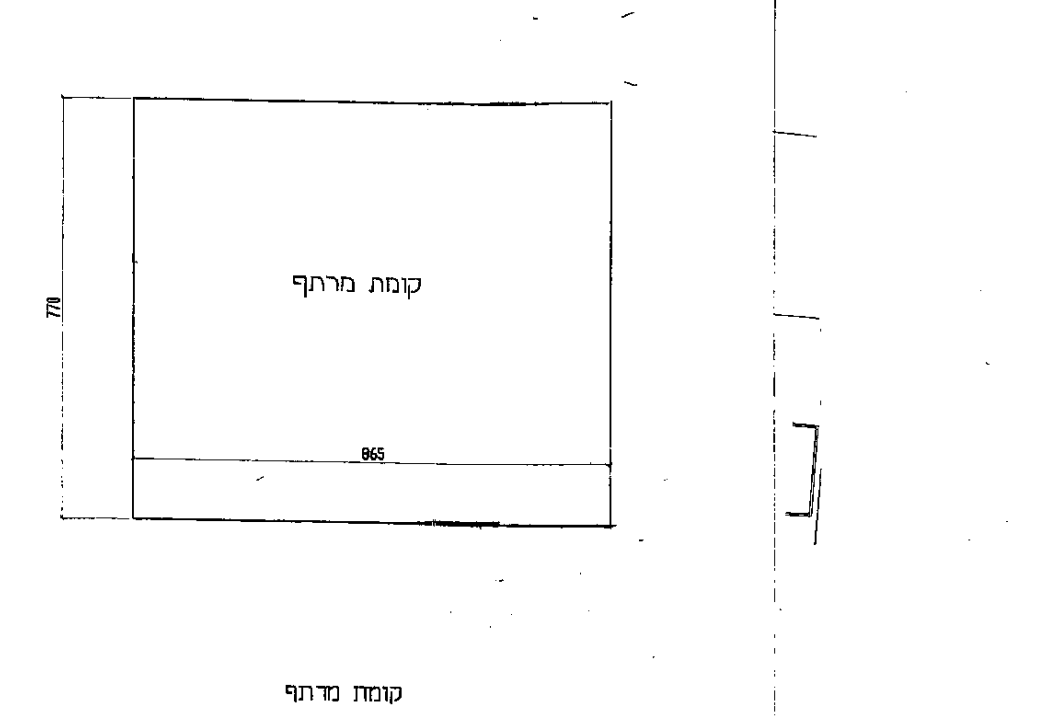

קומת מרתף

טיח בתחום:
7.70×8.65=66.60

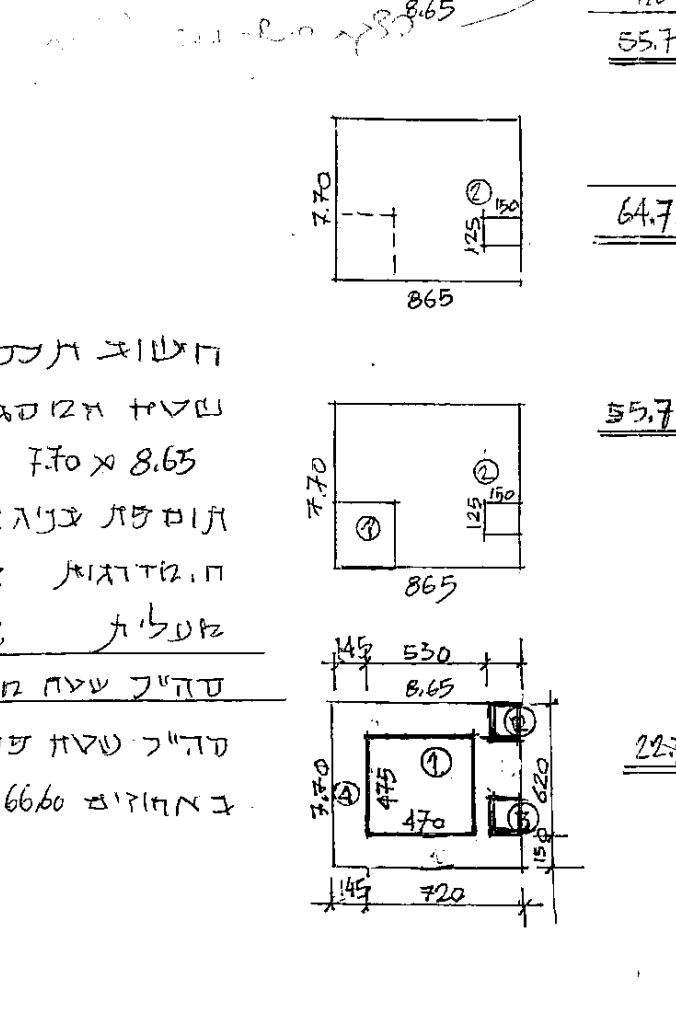

קומה א

66.60 = 66.60 = 7.70 × 8.65

הורדות

−9.00 = 3.00×3.0 ממ"ד ①

−1.87 = 1.50×1.25 מעלית ②

55.72 סה"כ

קומה ב

66.60 = שטח מסגרת

−1.87 הורדה מעלית ②

64.73 סה"כ

קומה ג

55.72 ראה קומה א

קומת גג

22.32 = שטח תוספת
4.75×4.70

חישוב תכסית הגג

שטח מסגרת
66.60 = 7.70 × 8.65

22.32 = 22.32 : תוספת בנייה

4.83 = 2.10×2.30 : חדר מדרגות

4.00 = 2.00×2.00 : מעלית

31.15 = סה"כ שטח מקורה

31.15 סה"כ שטח פנוי

46.6% = 31.15 : 66.60 באחוזים

תל-אביב-יפו

גוש: 6135

חלקה: 110 (חלק)

כתובת: תשבי 7,9

הוכן עבור: מר דנחי ראובן

מטרת התכנית: היתר בניה

הבעלים: דנחי ראובן ת.ז. 0061622-7

שטח לפי נסח : שטח החלקה כולה (מ"ר) 2443

בעלות בחלקים (כרשום בנסח טאבו) 84\2443

בעלות בחלקים (כרשום בנסח טאבו) 12\349

שטח בבעלות במ"ר: 168

שטח מחושב במ"ר: 132

תשריט מצב קיים
קנ.מ. 1:250

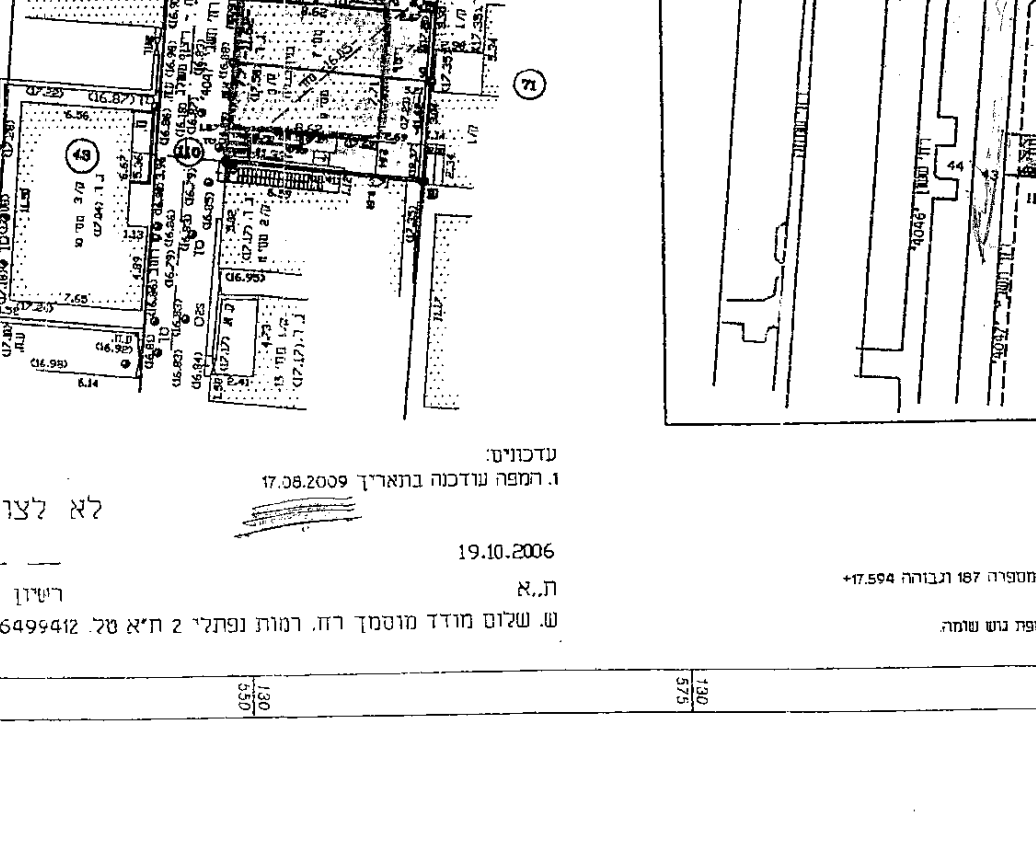
43
44
45
64
אדמה
110

לא לצורכי רישום

רישיון מס. 613

03-6499412 ת"א

תרשים סביבה
ק.מ. 1:1250

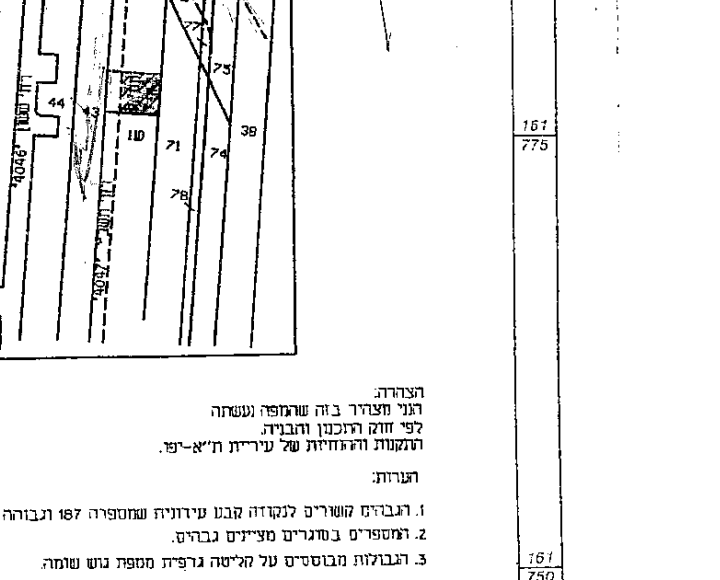
45
109
44
43
110
71
72
73
74
77
78
38

הצהרה:
הנני מצהיר בזה שהמפה נעשתה
לפי חוק התכנון והבנייה.
התקנות וההנחיות של עיריית ת"א-יפו.

הערות:
1. הגבהים קשורים לנקודה קבע עירונית שמספרה 187 ובגובה +17.594
2. המספרים בסוגריים מציינים גבהים.
3. הגבולות מבוססים על קליטה גרפית ממפת גוש שומה.

19.10.2006

22

ר.10.0937

עיריית תל-אביב - יפו
מח' רישוי בנייה
13-06-2010
נתקבל

13/06/10 תוספת הגשה

עיריית תל-אביב-יפו

מינהל ההנדסה, אגף רישוי ופיקוח על הבנייה

שדרות בן-גוריון 68 תל-אביב 64514 (פקס 5231340) טלפון 5217120, 5217045

לכבוד ☒ הוועדה המקומית לתכנון ולבנייה

☐ רשות הרישוי המקומית

חוק התכנון והבניה, התשכ"ה 1965

תקנות התכנון והבניה (בקשה להיתר תנאיו ואגרות) התש"ל-1970

בקשה להיתר בנייה או לשימוש במקרקעין

יש להקפיד למלא את כל הפרטים בטופס הבקשה ולצרף מסמכים כמפורט ברשימת התיוג המצורפת.

מס' תיק הבניין: 20-1904

מס' בקשה קודמת להיתר בנייה: 221234 / 23-140

מס' הבקשה למידע: 2003-0518

תאריך: 26/05/03

א. פרטי הנכס והמבקשים

הכתובת	רחוב: תישבי	מס' בית: 7	גוש: 6135	חלקה: 110	תת חלקה	מגרש	הוראות התכניות החלות על המקום: 2215

פרטים אישיים	שם משפחה / שם פרטי	מס' זהות	רחוב ומספר בית, ישוב ומיקוד	מספר טלפון / מספר פקס
מבקש 1	דנחי ראובן	6162217	הגולן 40 ת"א	0509286058 036493988
מבקש 2				
מבקש 3				
	דנחי ראובן	6162217	הגולן 40 ת"א	03-6493988
		64298557	בית אל 43 ת"א	036470151 0507345688
	שמעון ברזי	02370774	מנחם בגין 10 נתניה	0528390193

ב. מהות הבקשה

☒ בקשה לתוספת בנייה ☐ בקשה להרחבת דיור (במסגרת הרחבת דיור שכונתית)

☒ תוספת בנייה בקומה

☒ שינויים פנימיים הכוללים: שינוי חזיתות, תוספת חדר מכונות

☒ אישור מצב קיים

המבנה משמש כיום ל- מגורים

☒ בהיתר ☐ בלי היתר

ג. מפרט - תיאור הבקשה

תיאור הקיים על המגרש: קיים בניין בן 3 קומות

שימוש עיקרי: ☒ מגורים

סוג העבודה: ☒ הריסה

הגורם שבמצעות בעבודת הבנייה: ☒ גורם פרטי

שטח המגרש: 132.80 מ"ר

מספר תכנית התוספה: 2215

מספר יחידות דיור מורחבות: 1

ד. חומרי הבנייה

סוג הבנייה: ☒ רגילה

קירות חיצוניים: ☒ בטון מזוין ☒ בלוקים

חומרי גימור: ☒ זכוכית ☒ אבן טבעית ☒ טיח

תקרות: ☒ בטון מזוין

גג: ☒ בטון מזוין

	שטח (מ"ר)
מרתף	66.60
ע'	55.72
	64.73
	55.72
א'	22.32
סה"כ	198.51

15% 198.51

66.60

ט. הבקשה מוגשת לאישור

ביטול נסיגה 1.20 מ' בק' גג בגלל ח. מכונות מעלית

ז. קווי בניין

הכיוון	מוצע	מותר
לרחוב (שם) תישבי		0.00
לרחוב (שם)		
לצד	2.00	2.00
לאחור	2.70	2.70

ח. מספר יחידות דיור

י. הצהרת עורך הבקשה הראשי

תאריך 13/05/10 שם משה אשכנזי

משה אשכנזי אדריכלות-בינוי

יא. החתימות הנוספות

המבקש: דנחי ראובן

בעל הזכות בנכס: דנחי ראובן

שמעון ברזי 13/06/10

21/06/2010

נסרק

סיכום בדיקה תחנה פיקוח בניה בקשה 20100937 לכתובת תשבי 7

החלטת תחנה מ-21/06/2010 : תוכנית תואמת את המצב בשטח

תוכנית תואמת את המצב בשטח המבוקש בנוי במלואו הוגשה תביעה משפטית מס' 01/07/0013624

מטפל: מיכאל שטמלריס