פרטי הבקשה להיתר:
מספר פנייה: 6015
כתובת: תשבי 12
תאריך הדפסה: 11/06/2017

20

תצהיר

אני החתום/ה מטה מרלי מירב
בעל/ת ת.ז. 032150583
מצהיר/ה כי :

1. ביום 18/08/2016 הגשתי לעיריית תל אביב קבצי המחשב במסגרת הגשת בקשה להיתר בניה בפניה שמספרה 6015
2. את הקבצים הניל, המפורטים ברשימה להלן, חתמתי בעצמי בחתימתי האלקטרונית.
3. רשימת הקבצים :

100_Tishbi12-Plans.dwfx
150_Tishbi12.dwg
1600_nispach migun.pdf
200_Tishbi12-kk.dwfx
2100_hazit-back.jpg
2100_hazit-front.jpg
2100_hazit-side.jpg
2100_hazit-side2.jpg
2100_rechov.jpg
2200_rishayon.pdf
2200_tabo.pdf
2200_tz.pdf
2300_2b.pdf
2300_2b-shachen.pdf
2300_pirsum-iton.pdf
2300_tabo.pdf
2300_tzhir.pdf
2500_hesder-migrash1.pdf
2500_hesder-mogrash2.pdf
2600_i-pitzul.jpg
2600_meshutaf.jpg
300_Hamada.dwfx
5800_TAKANA-27.dwf
900_nispach9.pdf
900_rishayon-sheled.pdf
900_tofes9.pdf
900_tshhbe.pdf

4. השוותי בין התכנית המצויה בקבצים הניל לבין התכנית המצויה בגיליון הנייר עליו מודבק תצהיר זה ומצאתי כי התכנית זהה בשניהם (בקבצים ובנייר).

חתימה	תאריך	שם
	18/6/17	מירב מרלי

פניה 6015
תאריך יצירה 11.06.2017
בקשה 16-1642

א. פרטי הנכס והמבקשים

בקשת מידע: 2016-01053
תיק בניין: 4047-012

כתובת
רחוב תשבי
בית 12
גוש/חלקה 43/6135
שטח מגרש/חלקה: 119.00 מ״ר
אחוז בניה: 223.00

תכניות החלות על המקום והן מקור לשטחים מבוקשים
2215
2215א1
2691
3954
4053
9001
9002
9007
9010
9017
9021
9024
ג
ג3
ח
צ
תמ״א/10/ד/12
תמ״א10ד10
תמ״א18
תמ״א/38/2
תמ״א/4/2
תמ״א23
תמ״א/23א/4
תמ״א/38/3
תמ״א/34ב/4
תמ״א/36א/א
תמ״א/4/18
תמ״מ5
תמא3

פרטים אישיים	שם משפחה שם פרטי שם חברה או תאגיד	רחוב / מספר בית ישוב מיקוד
מבקש	דנחי יוסף	נועם אלימלך 7ב בני ברק 5154615
בעל זכות בנכס	דנחי יוסף	נועם אלימלך 7ב בני ברק 5154615
עורך ראשי	מרלי מירב	הרצל 108 תל אביב - יפו 66554
מתכנן שלד	שתיוי מועאד	ארלוזורוב 62 תל אביב - יפו 62488

ב. מהות הבקשה

סוג הבקשה
תוספות בניה / תוספות בניה שונות (כולל קומת קרקע)

שימוש
מגורים

ג. מפרט תאור הבקשה

פירוט המבוקש לתוספת
קומה בה מתבצעת התוספת: גג
שטח התוספת (מ״ר): 11.01
שטח דירה/משרד לאחר תוספת (מ״ר): 103.75
כיוון התוספת: לצד
מבוקשים שינויים פנימיים הכוללים: שינויים במידות פנים של הבניין, בין חדרי מדרגות קיימים ודירות קיימות (עפ״י היתר

מס)15-1175 , ללא שינוי סה״כ השטח. עקב מדידת פנים (ע״י מודד מוסמך

.)הגדלת חדר על הגג עפ״י ג3-

תוספת אחרת: שינוים כלפי היתר 15-1175 .1

. ביטול מרתף.2

. העברת נישת בלוני גז, פילר חשמל ועמוד חשמל. לאחר תיאומים ואישורים מול

חברת חשמל.3

. בקשה לתוספת של 11.01 מ״ר , עפ״י ג3 ובקשת הקלה

.

שימוש המקום כיום: בהיתר היתר מספר 15-1175

פירוט המבוקש לתוספת בניה בקומת הגג
כיוון התוספת: לצד
שטח התוספת (מ״ר): 11.01
הדירה, לרבות הבנייה על הגג קיימת בהיתר משנת: 2015
השימוש בתוספת המבוקשת: למגורים
גובה המבנה הקיים (מטר): 12.57
נסיגה מהמעקה מצד אחד (מטר): 1.2

הגורם עבורו מתבצעת העבודה
גורם פרטי

ד. חומרי הבנייה

סוג הבניה
רגילה

קירות חיצוניים
בטון מזוין
בלוקים

חומרי גימור
טיח

תקרות
בטון מזוין

גג
בטון מזוין
טיח

מקרא חומרים (צבעים)
בטון או בטון מזוין: כחול
בלוקים או לבנים: אדום
עץ: חום
זכוכית: סגול
הריסה: צהוב
בניה קיימת: אפור

ו. קווי בנייה

לרחוב תשבי מוצע: 0
לצד מוצע: 2.95
לאחור מוצע: 3 מותר: 3
לצד 2 מוצע: 0

ז. מספר יחידות דיור

מספר יחידות הדיור הקיימות: 2
מספר יחידות הדיור לביטול/הריסה:
מספר יחידות הדיור המבוקשות ששטחן עד 120 מ״ר:
מספר יחידות הדיור המבוקשות ששטחן מעל 120 מ״ר:
מספר יחידות הדיור המותרות: 2

ח. פרטי הבנייה - לשימוש הלשכה המרכזית לסטטיסטיקה

שטח הבניה ברוטו לפי היעוד
למגורים: מגורים שטח: 265.48
סך כל שטחי הבניה: 265.48

גודל הדירות לפי מספר חדרים
חדר 5: מספר דירות: 2 מספר מגורים: 2
סה״כ מספר דירות: 2
סה״כ מספר מגורים: 2

התשכ״ה- 1965
(בקשה להיתר תנאיו ואגרות) התש״ל - 1970
)א(2

ט. הבקשה מוגשת לאישור

פירוט הבקשה להקלה	נימוקי הבקשה להקלה
הקלה מנסיגה בבניה על הגג ובניה במרחק של 0 מ,׳ במקום 1.2 בחזית צדדית דרומית	בניה בקיר משותף עתידי - 0
הקלה מקו בנין אחורי מ- 7 מטר ל- 4 מ,׳	עפ״י קו בניה קיים של חדר יציאה לגג, טרם אישור ג3

ה. השטחים המבוקשים (על-פי תכני תכנית הבנייה) והמותרים לבנייה (על-פי ״אסמכתא״ : חוק, תקנות, תכניות) בכל מפלס בנפרד ולפי שימוש

מבנה	הקומה	מפלס	מגורים בהיתר	מגורים ללא היתר	מגורים מבוקש	מגורים מותר	ממ״ד/ ממ״ק/ מקלט שטח שירות לשמוש מגורים בהיתר	ממ״ד/ ממ״ק/ מקלט שטח שירות לשמוש מגורים ללא היתר	ממ״ד/ ממ״ק/ מקלט שטח שירות לשמוש מגורים מבוקש	ממ״ד/ ממ״ק/ מקלט שטח שירות לשמוש מגורים מותר	אחסנה לשמוש מגורים בהיתר	אחסנה לשמוש מגורים ללא היתר	אחסנה לשמוש מגורים מבוקש	אחסנה לשמוש מגורים מותר	עיקרי: סה״כ	עיקרי: % משטח המגרש	עיקרי: סה״כ מותרים	אסמכתא: תכנית ראשית/ אחר	שירות: סה״כ	שירות: מותר	שירות: % משטח המגרש	סה״כ קומה: עיקרי+שירות	סה״כ: עיקרי+שירות נוסף לא נכלל	סה״כ קומה: % משטח המגרש	סה״כ קומה: מותר	סה״כ קומה: שטחים לא מקורים
		±0.00 = +17.50																								
1	מרתף -1	-3.22									34.9816								34.9816		29.40	34.9816		29.40		
1	קרקע 0	0.00	54.8834				10.7040								54.8834	46.12			10.7040		8.99	65.5874	1.1238	55.12		3.5791
1	קומה 1	2.89	65.5860												65.5860	55.11						65.5860		55.11		3.4009
1	קומה 2	5.78	53.1060				12.4800								53.1060	44.63			12.4800		10.49	65.5860		55.11		3.4009
1	קומה 3	8.67	22.7360		11.0024										33.7384	28.35						33.7384		28.35		26.1426
	מתחת לקרקע																		34.98		29.40	34.98		29.40		
	מעל הקרקע														207.31	174.21			23.18		19.48	230.50	1.12	193.70		36.52
	סה״כ														207.31	174.21			58.17		48.88	265.48	1.12	223.09		36.52

י. הצהרת עורך הבקשה הראשי

אני מצהיר על נכונות הפרטים בסעיפים א עד ט

תאריך 18/6/17 שם: מרלי מירב חתימה

יא. חתימות נוספות

תפקיד	שם	תאריך	חתימה
מבקש	דנחי יוסף	12/6/17	
בעל זכות בנכס	דנחי יוסף	12/6/17	
מתכנן שלד	שתיוי מועאד	14/6/17	שתיוי מועאד מתכנן קונסטרוקציה מס׳ רשיון 26359

לתשומת לב החותם על תכנית הבקשה להיתר:

1) אין לחתום על תכנית הבקשה להיתר, אלא אם היא חלק מהדפסה רציפה (גרמוקשה / הרמוניקה) בנייר הכוללת את טופס1(פרטים ונתונים מילוליים ומספריים של הבקשה להיתר, חתום בחותמת מים של עיריית תל אביב) תרשים חישוב השטחים(חתום בחותמת מים של עיריית תל אביב) ותכנית הבקשה להיתר (תכניות, חתכים, חזיתות וכד׳).

2) לאחר שתפתח בקשת רישוי במחלקת רישוי בניה תשלח אליך הודעה עם מספר הבקשה להיתר. לאחר קבלתה, עליך להכנס לתיק הבניין בגנזך ההנדסה האינטרנטי באתר עיריית תל אביב ולוודא שהתכנית הנוכחית עליה חתמת כאן זהה למסמכי הבקשה להיתר כפי שהם מופיעים בתיק הבניין האינטרנטי.

יב. מינויים מטעם מבקש ההיתר

מינוי עורך הבקשה הראשי

אני ממנה בזה את מרלי מירב בעל/ת מס׳ זהות 032150583
הרשום בסעיף א להיות עורך הבקשה הראשי להיתר, וליצגני לפני מוסדות התיכנון והרשויות המוסמכות בכל הנוגע לטיפול בבקשה להיתר ולקבלתו, לרבות התיקונים ככל שידרשו הרשויות המוסמכות.

מינוי עורכי בקשה לפי תחומים

אני ממנה את הרשומים להלן להיות עורכי הבקשה להיתר בתחום הפעולה כרשום ליד שמם, וליצגני בתחום פעולתו לפני מוסדות התכנון והרשויות המוסמכות בכל הנוגע לטיפול בבקשה להיתר ולקלתו, לרבות התיקונים ככל שידרשו הרשויות המוסמכות.

	שם משפחה שם פרטי	תחום פעילות	המען	פרטי התקשרות
1.	מירב מרלי	אדריכלות	הרצל 108 ת״א	052-6706039
2.				
3.				

מינוי מתכנן שלד הבניין

אני ממנה בזה את שתיוי מועאד בעל/ת מס׳ זהות 029862331
הרשום בסעיף א להיות אחראי לתכנון שלד הבניין שבעבורו מבוקש ההיתר, להגיש לוועדה המקומית לרשות הרישוי המקומית את החישובים לגבי הבניין שבעבורה מבוקש היתר ולפקח פיקוח עליון על הקמת השלד.

מינוי הקבלן האחראי לבנייה

☐ אני ממנה בזה את ______ בעל/ת מס׳ זהות ______
ובעל תעודת רישום בפנקס קבלנים מספר ______ במדור ______
ובעל רישיון לביצוע עבודה בתוקף עד ______ לבצע את העבודה הנדונה בהיתר כמתחייב לפי כל דין.

☐ אני מצהיר, כי טרם מסרתי את ביצוע העבודה הנדונה בהיתר לידי קבלן, ומתחייב למסור אותה לידי קבלן רשום בפנקס הקבלנים, כמתחייב על פי כל דין, ולהודיע על כך לרשות הרישוי המקומית טרם התחלת ביצוע העבודה, וחתימתו של הקבלן תצורף להודעה המפרטת את פרטי רישומו של הקבלן.

מינוי האחראי לביצוע שלד הבניין

☐ אני ממנה בזה את ______ בעל/ת מס׳ זהות ______
כתובת ______ טלפון ______ מייל ______
הרשום לעיל להיות אחראי לביצוע שלד הבניין.

☐ אני מצהיר, כי טרם מיניתי אחראי/ת לביצוע עבודות הבנייה בתחומים אלה: ______
ומתחייב לעשות זאת כמפורט בתקנות, ולהודיע על כך לרשות הרישוי המקומית טרם התחלת ביצוע העבודה.

מינוי אחראים לביקורת

☐ אני ממנה בזה את הרשומים להלן להיות אחראים לביקורת על ביצוע עבודות בתחום הפעולה כרשום ליד שמם

	שם משפחה שם פרטי	תחום פעילות	המען	פרטי התקשרות
1.				
2.				
3.				

אני מצהיר כי טרם מיניתי אחראי/ת לביקורת על ביצוע עבודות הבנייה את כולם או את קצתם בתחומים האלה: ______
ומתחייב לעשות זאת כמפורט בתקנות, ולהודיע על כך לרשות הרישוי המקומית טרם התחלת ביצוע העבודה.

חתימת המבקש על המינויים יוסף דנחי

יג. הצהרות

הצהרות עורכי הבקשה כולל הצהרות עורך הבקשה על לחץ המים

אנו החתומים מטה מצהירים בזה:
1) כל אחד מאתנו מאשר שהאמור בנוגע לרשימה שבסעיף י״ב לעיל הוא נכון.
2) כל אחד מאתנו מסכים לקבל עליו את התפקיד המיועד לו בסעיף י״ב לעיל.
3) אנו מצהירים, כל אחד בנוגע לתחום פעולתו, שיש לנו כישורים מקצועיים לערוך *בקשה זו וכי בדקנו את המסמכים הנדרשים לבקשה, לרבות כל תכנית הנוגעת לבקשה,* וידוע לנו כי אם הצהרה זו אינה נכונה, הרי היא תיחשב מסירת ידיעה שהיא כוזבת או מטעה בפרט חשוב, כמשמעותה בסעיף 214 לחוק, וצפויים לנו העונשים הקבועים לפי כל דין.
אני מרלי מירב (עורך בקשה ראשי) אחרי/ת לכך שהבקשה, ובכלל זה נספחיה, נערכה לפי מיטב הידיעה המקצועית ובהתאם לכל חיקוק החל על הבניין או העבודה המוצעת, שכל הנתונים שנמסרו על ידי בבקשה זו נכונים ושהתכנון המוצע תואם את כל התכניות, פרט לסטיות שפורטו לעיל.

☐ אני עורך הבקשה מתכנן האינסטלציה הסניטרית, מצהיר בזאת ואחרי לכך שתכניות הבקשה בכל הנוגע לסידורים הסניטרים נערכו כדין וכי קויימו בהן הוראות החוק וההוראות למתקני תברואה התש״ל 1970 (הל״ת) לעניין זה, לרבות בדיקת לחץ המים הקיים בבניין ותיכנון בהתאם.

	תאריך	שם משפחה שם פרטי	מספר רישיון	חתימה
עורך ראשי	18/6/17	מרלי מירב	48359	

הצהרת מתכנן שלד הבניין

אני החתום מטה (שם משפחה ושם פרטי) שתיוי מועאד מס׳ זהות 029862331
מהנדס רשוי מס׳ ______
או הנדסאי בעל רישוי מס׳ 26359 (ל״מבנה פשוט״) מצהיר בזאת כדלקמן:
1) אני מסכים להיות מתכנן שלד הבניין הנדון בבקשה ולפקח פיקוח עליון על הקמת השלד.
2) כל אחד מאתנו מסכים לקבל עליו את התפקיד המיועד לו בסעיף י״ב לעיל.
3) ידוע לי, שאם אחרי הגשת הנתונים הסטטיים יתגלה צורך בשינוי מהותי בהם, אני מתחייב להגיש חישובים סטטיים מתוקנים מיד עם גילוי הצורך בכך.
4) אני מצהיר, כי יש לי כישורים מקצועיים לערוך בקשה זו וכי בדקתי את כל המסמכים הנוגעים לבקשה, לרבות כל תכנית הנוגעת לבקשה, וידוע לי כי אם הצהרה זו אינה נכונה, הרי היא תיחשב מסירת ידיעה שהיא כוזבת או מטעה בפרט חשוב, כמשמעותה בסעיף 214 לחוק, וצפויים לי העונשים הקבועים לפי כל דין.
5) ידוע לי כי עלי לשמור את תכנית הקונסטרוקציה לתקופה של לא פחות מ-7 שנים לאחר גמר הבניה.
תאריך 14/6/17 חתימה ______

שתיוי מועאד
מתכנן קונסטרוקציה
מס׳ רשיון 26359

הצהרת האחראי לביצוע שלד הבניין (כאשר מונה)

אני החתום מטה (שם משפחה ושם פרטי) ______ מס׳ זהות ______
מהנדס רשוי מס׳ ______ או הנדסאי בעל רישוי מס׳ ______ (ל״מבנה פשוט״)
מצהיר בזאת כדלקמן:
1) אני מסכים להיות האחראי לבצוע שלד הבניין.
2) אני מצהיר, כי יש לי כישורים מקצועיים להיות אחראי לבצוע שלד הבניין, ואני מתחייב לדאוג לביצוע שלד הבניין על פי תוכניות והוראות של מתכנן השלד כפי שייתנו בכתב וכן למלא את תפקידי על פי שנקבע בכל חיקוק הנוגע להן.
תאריך ______ חתימה ______

הצהרת אחראים לביקורת (כאשר מונו)

אנו החתומים מטה מצהירים בזה:
1) כל אחד מאיתנו מאשר שהאמור בנוגע לו ברשימה שבסעיף י״ב לעיל הוא נכון.
2) כל אחד מאיתנו מסכים לקבל עליו את התפקיד המיועד לו בסעיף י״ב.
3) אנו מצהירים כל אחד בנוגע לתחום פעולתו, שיש לנו כישורים מקצועיים לערוך את הביקורת כהלכה ולדווח על תוצאותיה לרשות הרישוי המקומית, כמתחייב לפי כל דין.
אני ______ (עורך הביקורת הראשי) אחראי/ת לכך שהביקורת תיערך על פי מיטב הידיעה המקצועית, ושכל הדיווחים לרשות הרישוי המקומית ייערכו על פי כל דין.

תאריך	שם משפחה שם פרטי	מספר רישיון	חתימה
___ / ___ / ___			
___ / ___ / ___			
___ / ___ / ___			
___ / ___ / ___			

שטחי מיגון ומרפסות בדירה

הקומה	מבנה	מפלס	דירה	מרפסת מקורה	מרפסת לא מקורה	גזוזטרה	פרגולה	גג טכני	ממ״ד/ ממ״ק/ מקלט עיקרי	ממ״ד/ ממ״ק/ מקלט שירות	ממ״ד/ ממ״ק/ מקלט קירות
קרקע 0	1	0.00	1								
קומה 1	1	2.89	1								
קומה 2	1	5.78	2								
קומה 3	1	8.67	2								
מתחת לקרקע											
מעל הקרקע											
סה״כ											

אסמכתאות לקומות

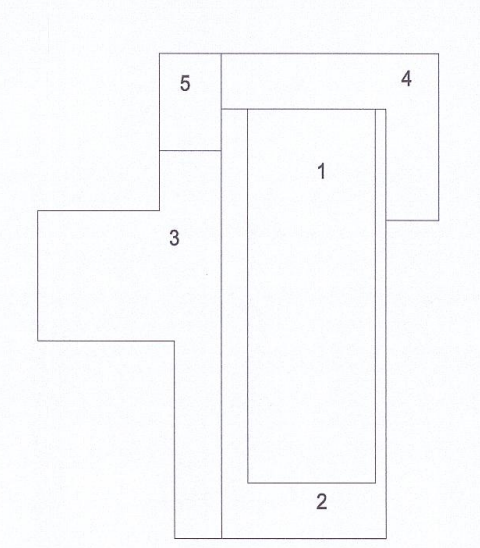

קומה	גובה		שטח	בניין
3	2.89		62.75	1

דירה	היתר	שטח	גובה	תיאור יעוד	קוד	מספר
2	קיים בהיתר	22.7360	2.89	מגורים	1	1
2	מבוקש	11.0024	2.89	מגורים	1	2
2	קיים בהיתר	17.6094	2.89	מרפסת גג	2002	3
2	קיים בהיתר	8.5332	2.89	מרפסת גג	2002	4
2	קיים בהיתר	2.8700	2.89	חלל	-1	5

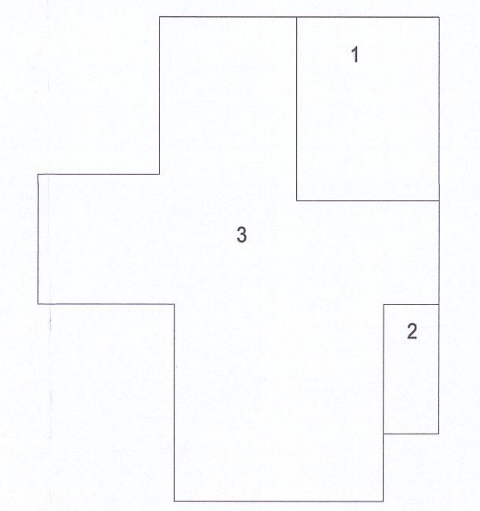

קומה	גובה		שטח	בניין
2	2.89		68.99	1

דירה	היתר	שטח	גובה	תיאור יעוד	קוד	מספר
2	קיים בהיתר	12.4800	2.89	ממ״ד.ממ״ק.מקלט-שטח שירות - לשמוש מגורים	1001	1
2	קיים בהיתר	3.4009	2.89	גזוזטרא	2004	2
2	קיים בהיתר	53.1060	2.89	מגורים	1	3

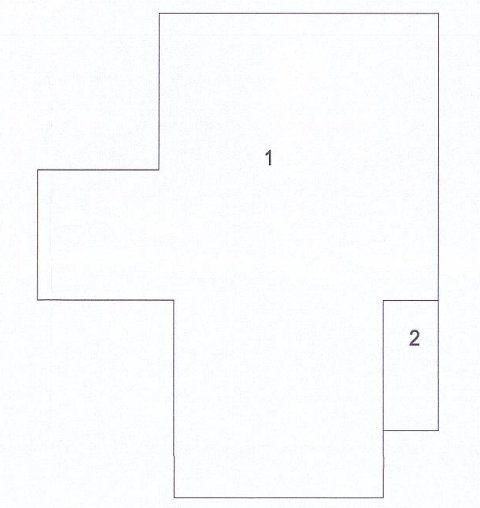

קומה	גובה		שטח	בניין
1	2.89		68.99	1

דירה	היתר	שטח	גובה	תיאור יעוד	קוד	מספר
1	קיים בהיתר	65.5860	2.89	מגורים	1	1
1	קיים בהיתר	3.4009	2.89	גזוזטרא	2004	2

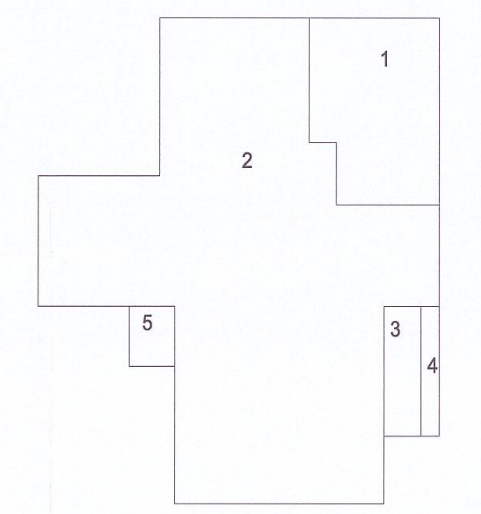

קומה	גובה		שטח	בניין
0	2.89		70.29	1

דירה	היתר	שטח	גובה	תיאור יעוד	קוד	מספר
1	קיים בהיתר	10.7040	2.89	ממ״ד.ממ״ק.מקלט-שטח שירות - לשמוש מגורים	1001	1
1	קיים בהיתר	54.8834	2.89	מגורים	1	2
1	קיים בהיתר	2.2757	2.89	גזוזטרא	2004	3
1	קיים בהיתר	1.1238	2.89	בליטות - לשמוש מגורים	1008	4
1	קיים בהיתר	1.3034	2.89	מרפסת גג	2002	5

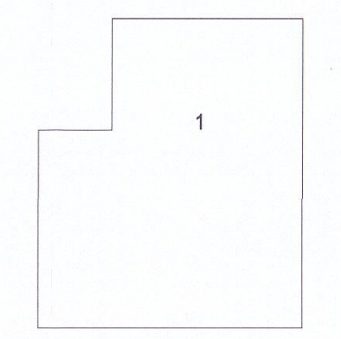

קומה	גובה		שטח	בניין
-1	3.22		34.98	1

דירה	היתר	שטח	גובה	תיאור יעוד	קוד	מספר
	קיים בהיתר	34.9816	3.22	אחסנה - לשמוש מגורים	1003	1

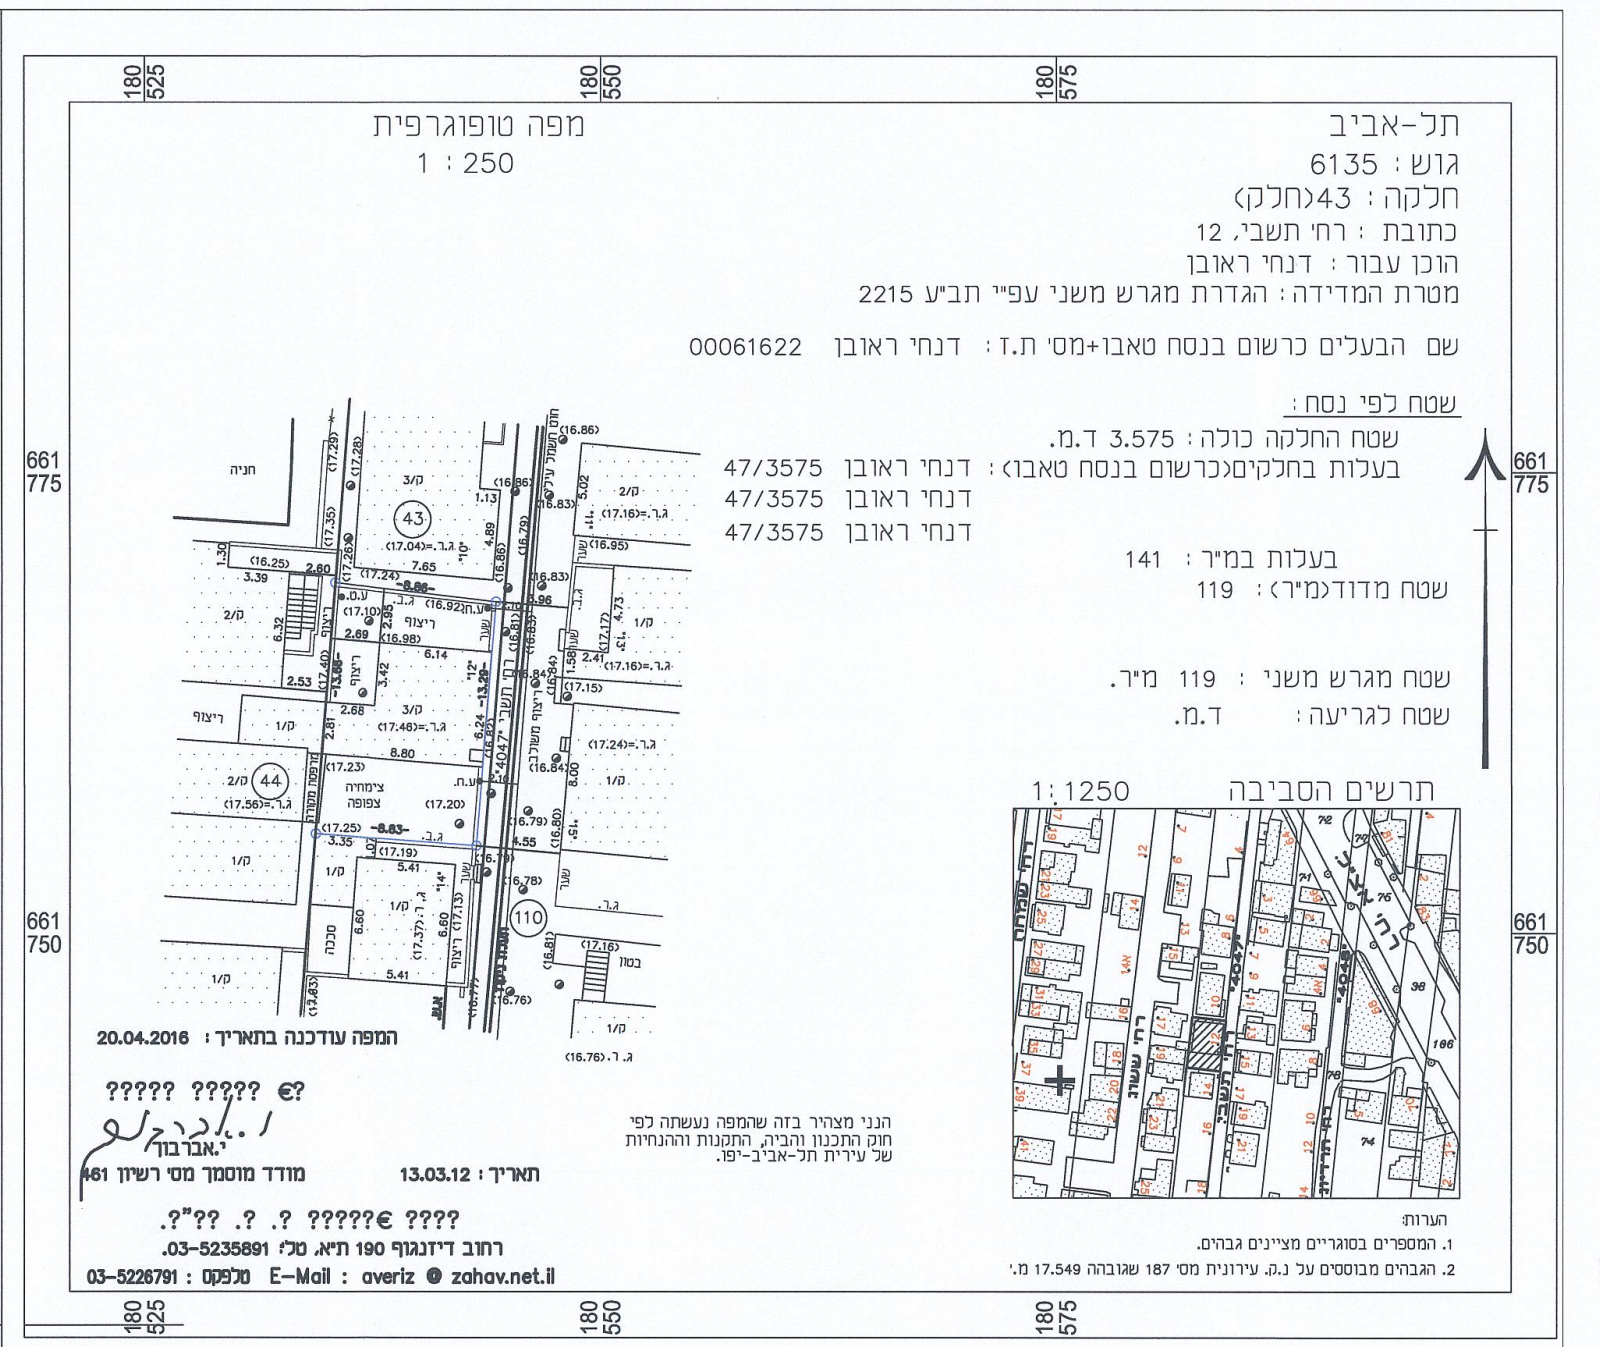
מפה טופוגרפית
1 : 250
תל-אביב
גוש : 6135
חלקה : 43(חלק)
כתובת : רח׳ תשבי, 12
הוכן עבור : דנחי ראובן
מטרת המדידה : הגדרת מגרש משני עפ״י תב״ע 2215
שם הבעלים כרשום בנסח טאבו+מס׳ ת.ז : דנחי ראובן 00061622
שטח לפי נסח :
שטח החלקה כולה : 3.575 ד.מ.
בעלות בחלקים(כרשום בנסח טאבו) : דנחי ראובן 47/3575
דנחי ראובן 47/3575
דנחי ראובן 47/3575
בעלות במ״ר : 141
שטח מדוד(מ״ר) : 119
שטח מגרש משני : 119 מ״ר.
שטח לגריעה : ד.מ.
תרשים הסביבה 1:1250
המפה עודכנה בתאריך : 20.04.2016
הנני מצהיר בזה שהמפה נעשתה לפי חוק התכנון והביה, התקנות וההנחיות של עיריית תל-אביב-יפו.
י.אברבוך
מודד מוסמך מס׳ רשיון 461
תאריך : 13.03.12
רחוב דיזנגוף 190 ת״א, טל׳: 03-5235891
טלפקס : 03-5226791 E-Mail : averiz @ zahav.net.il
הערות:
1. המספרים בסוגריים מציינים גבהים.
2. הגבהים מבוססים על נ.ק. עירונית מס׳ 187 שגובהה 17.549 מ׳.

מפת מודד

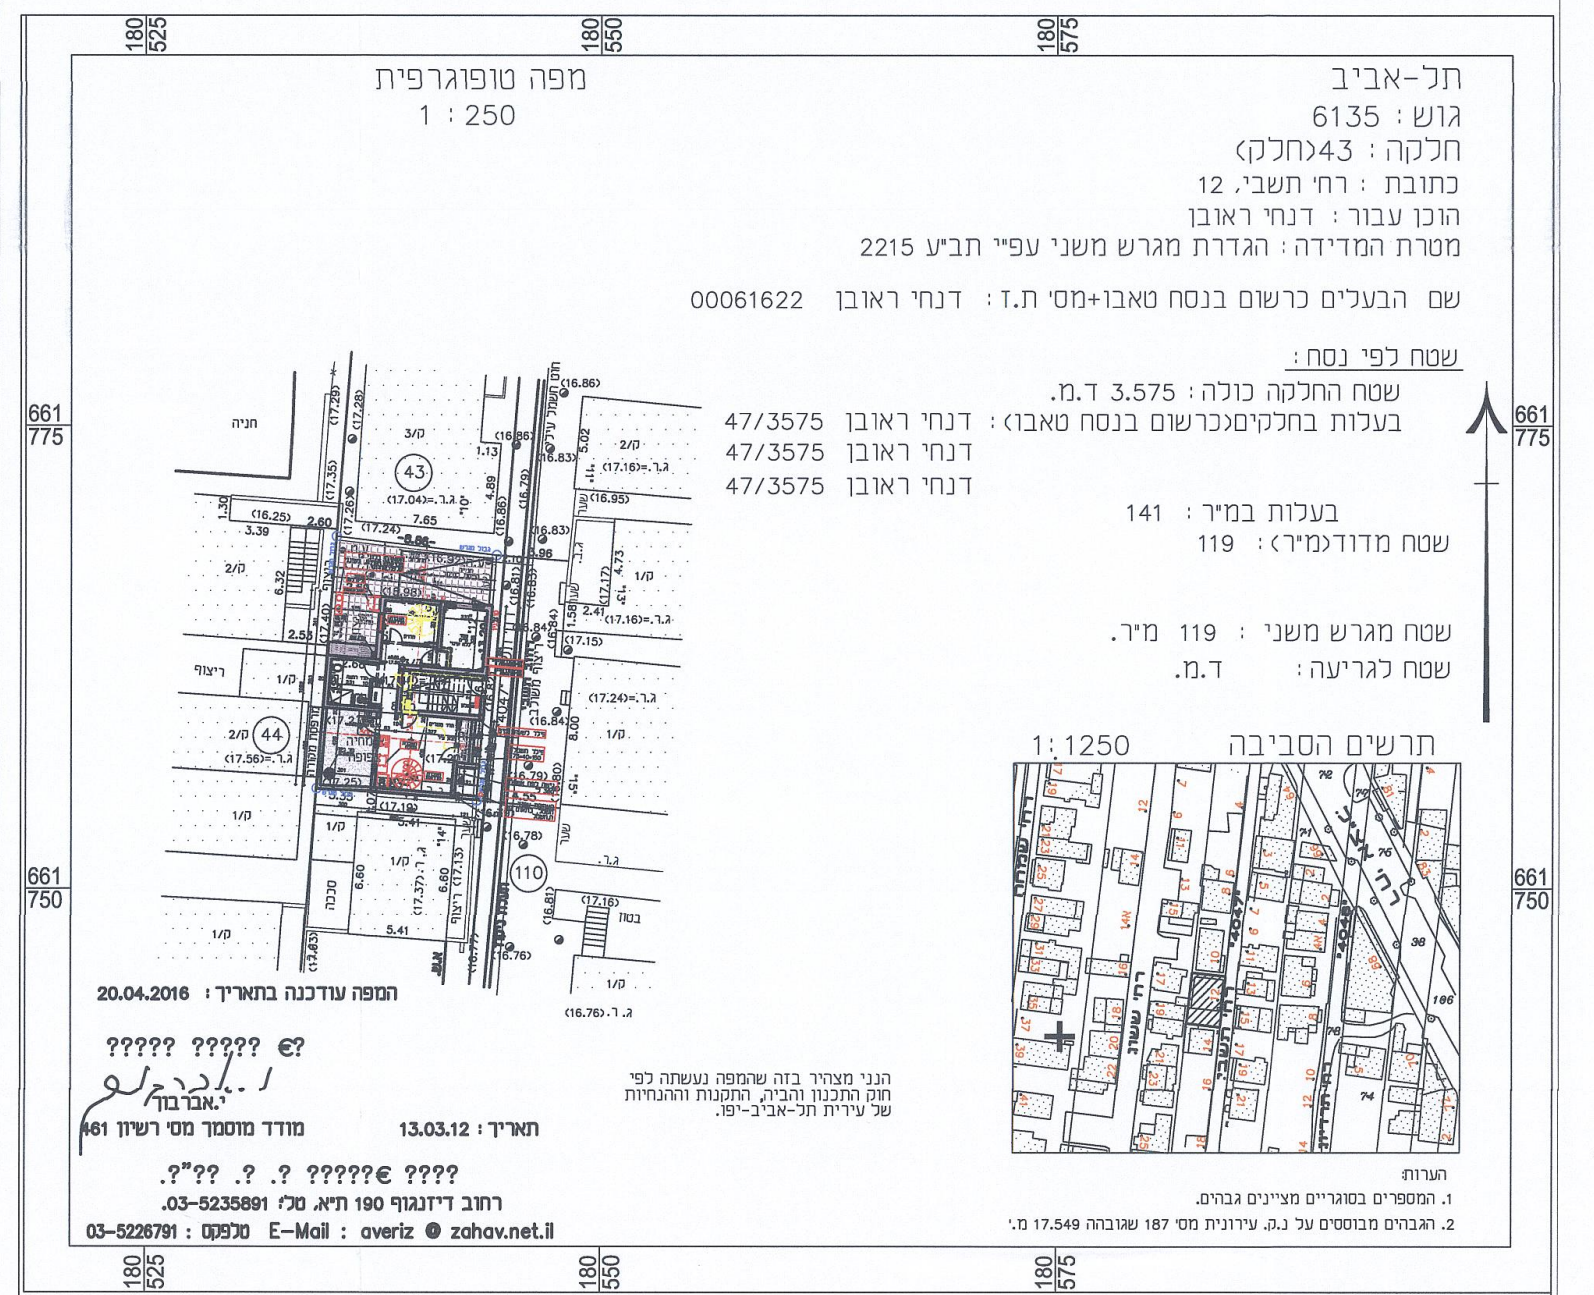

מפת העמדה

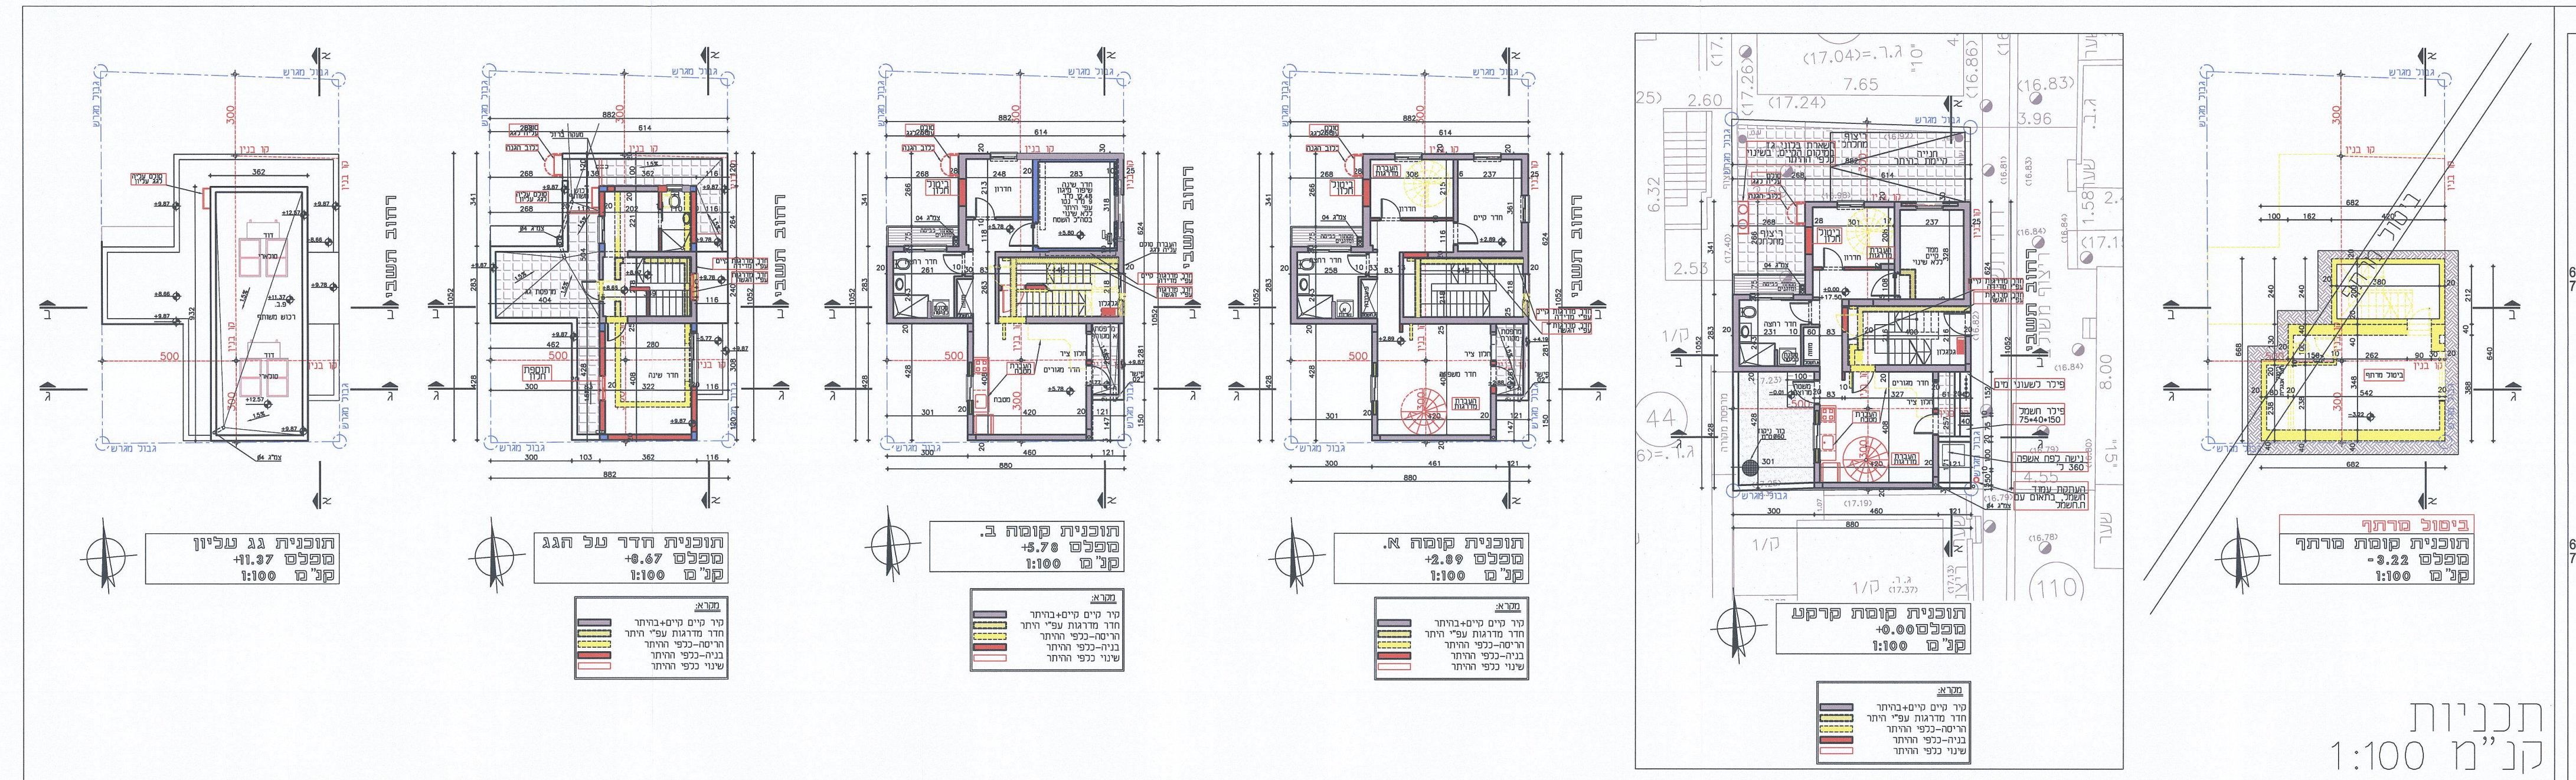

תכניות קנ״מ 1:100

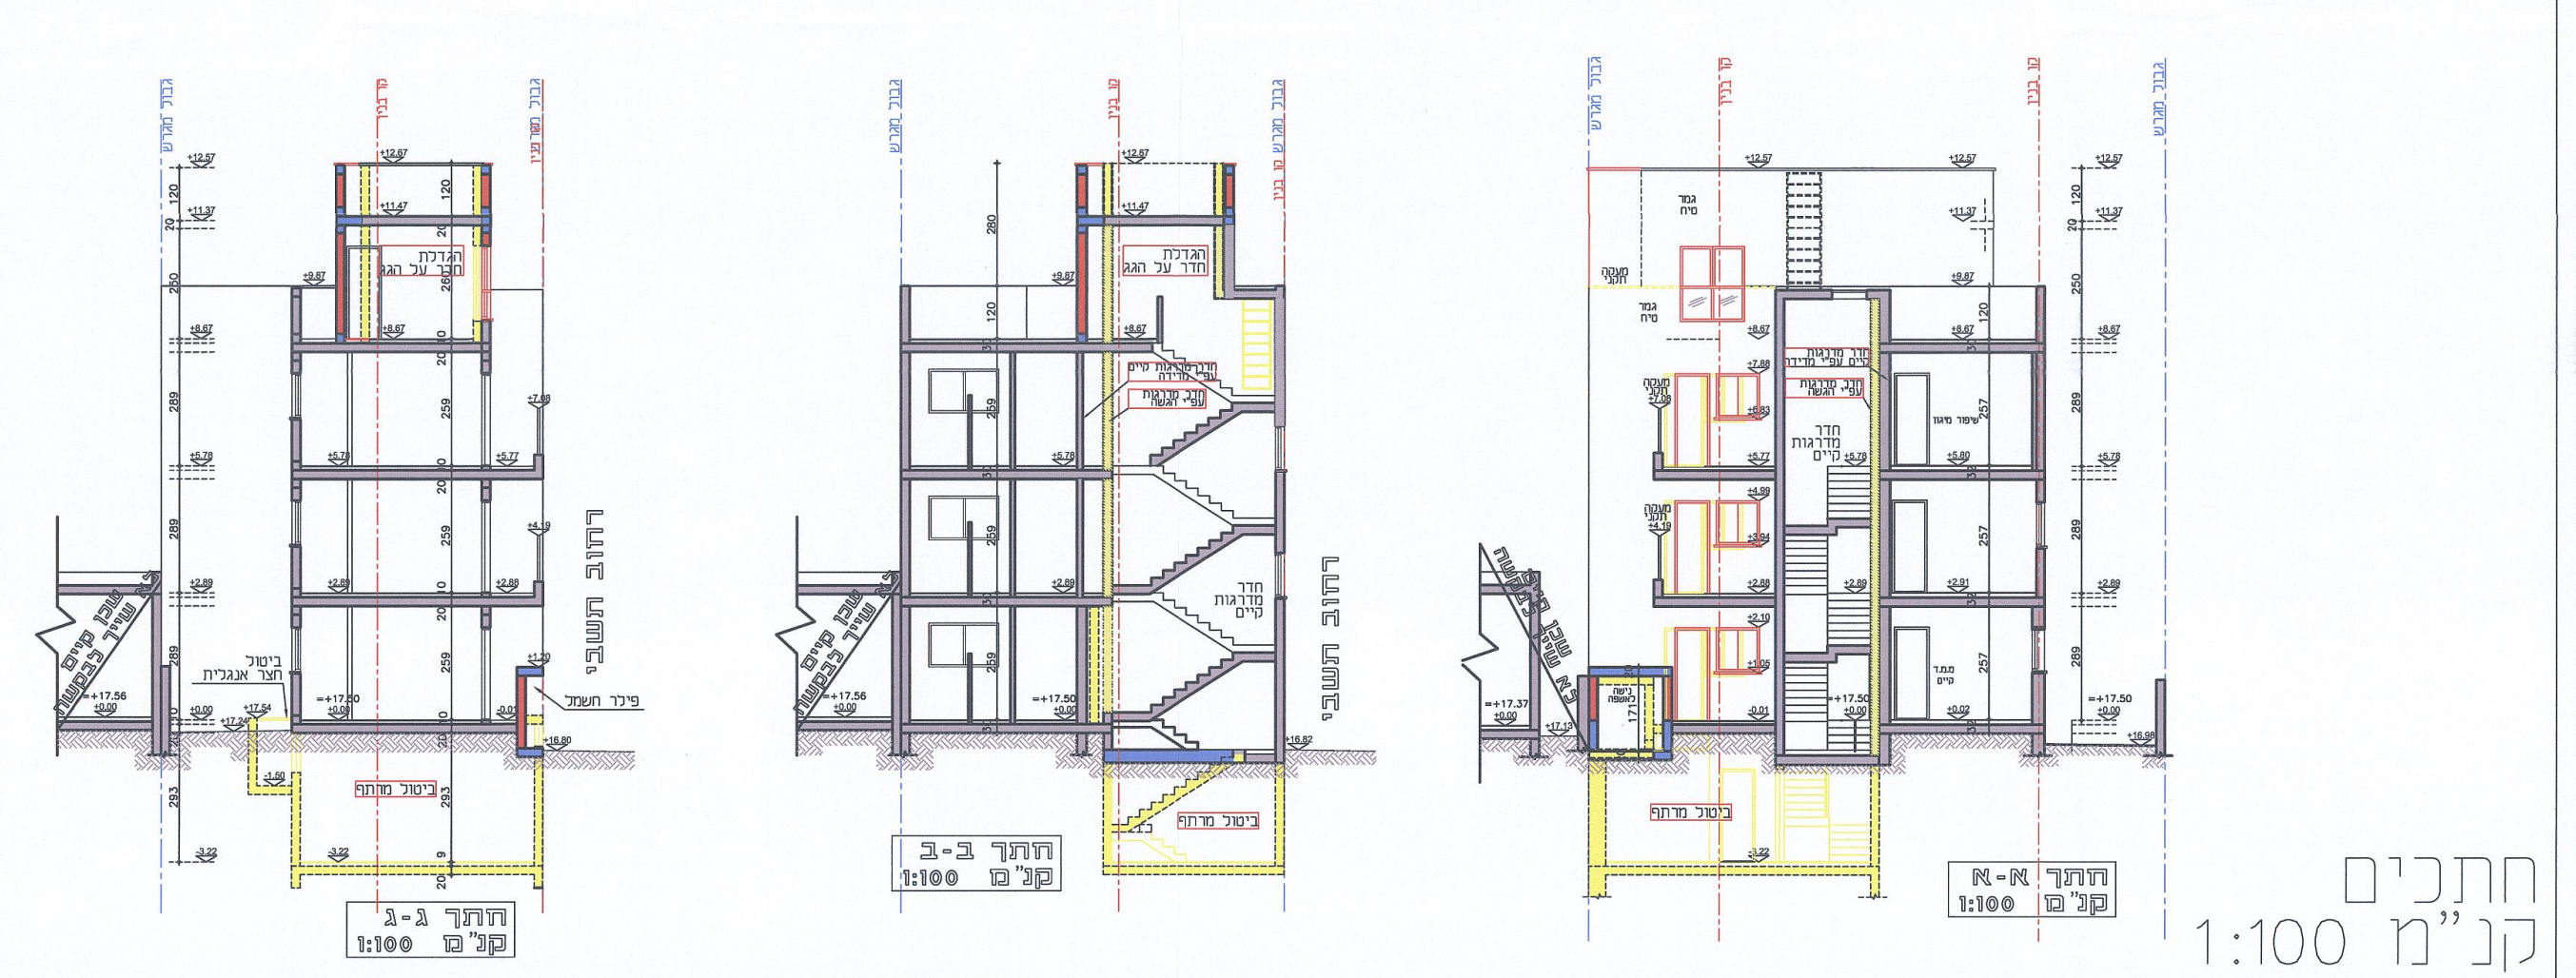

חתכים קנ״מ 1:100

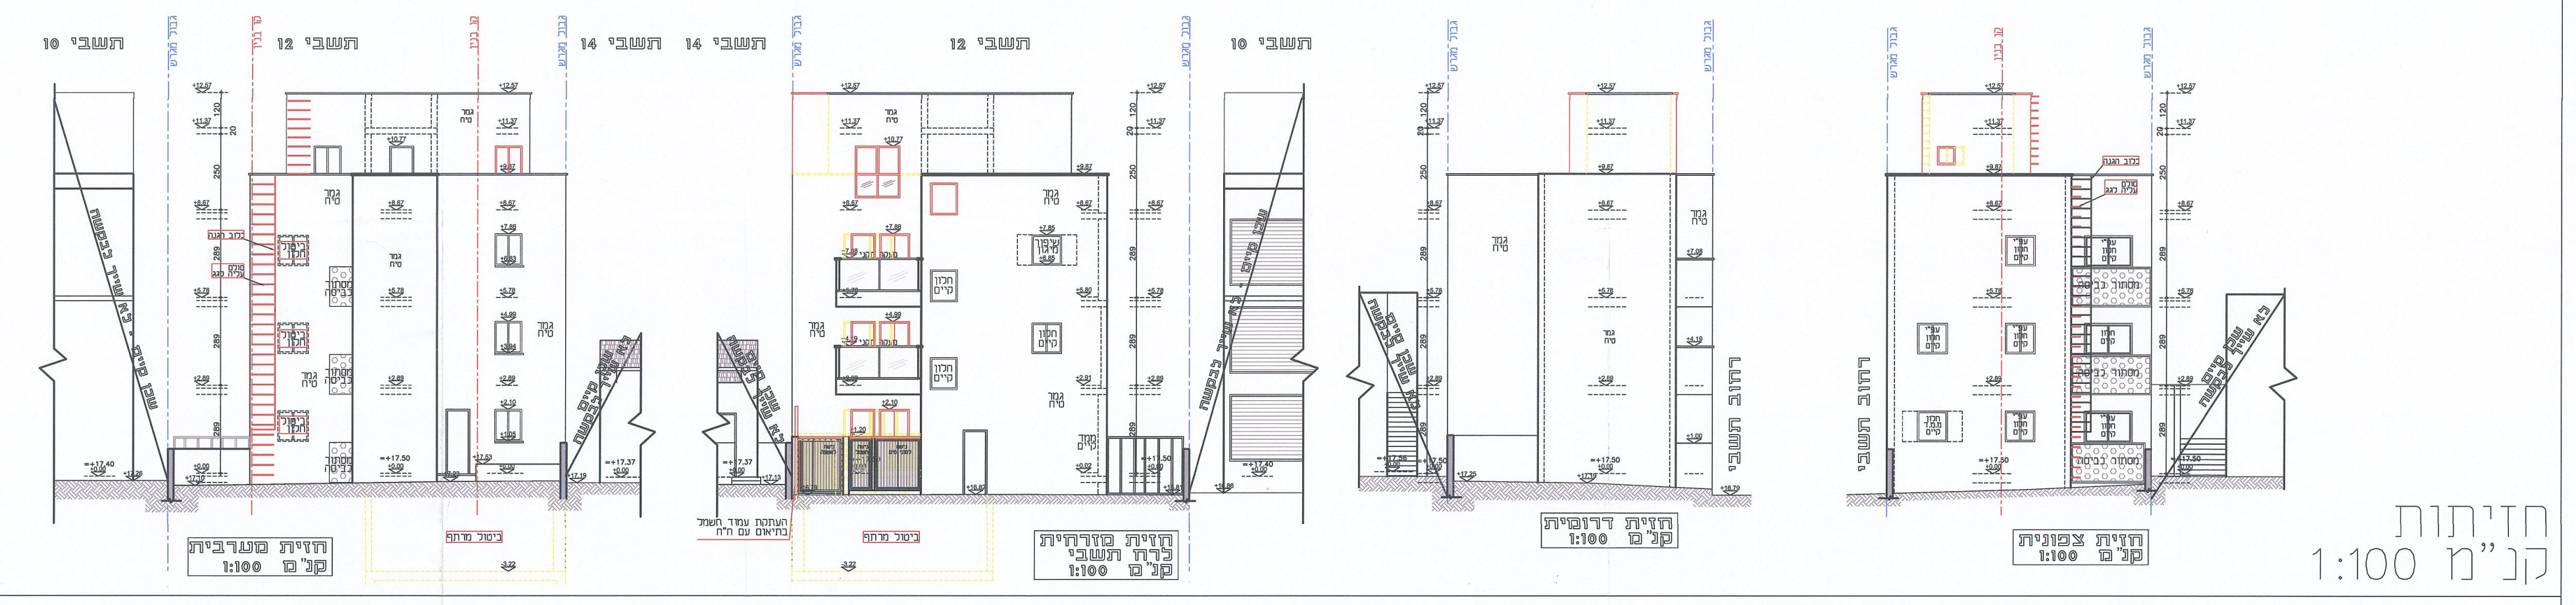

חזיתות קנ״מ 1:100

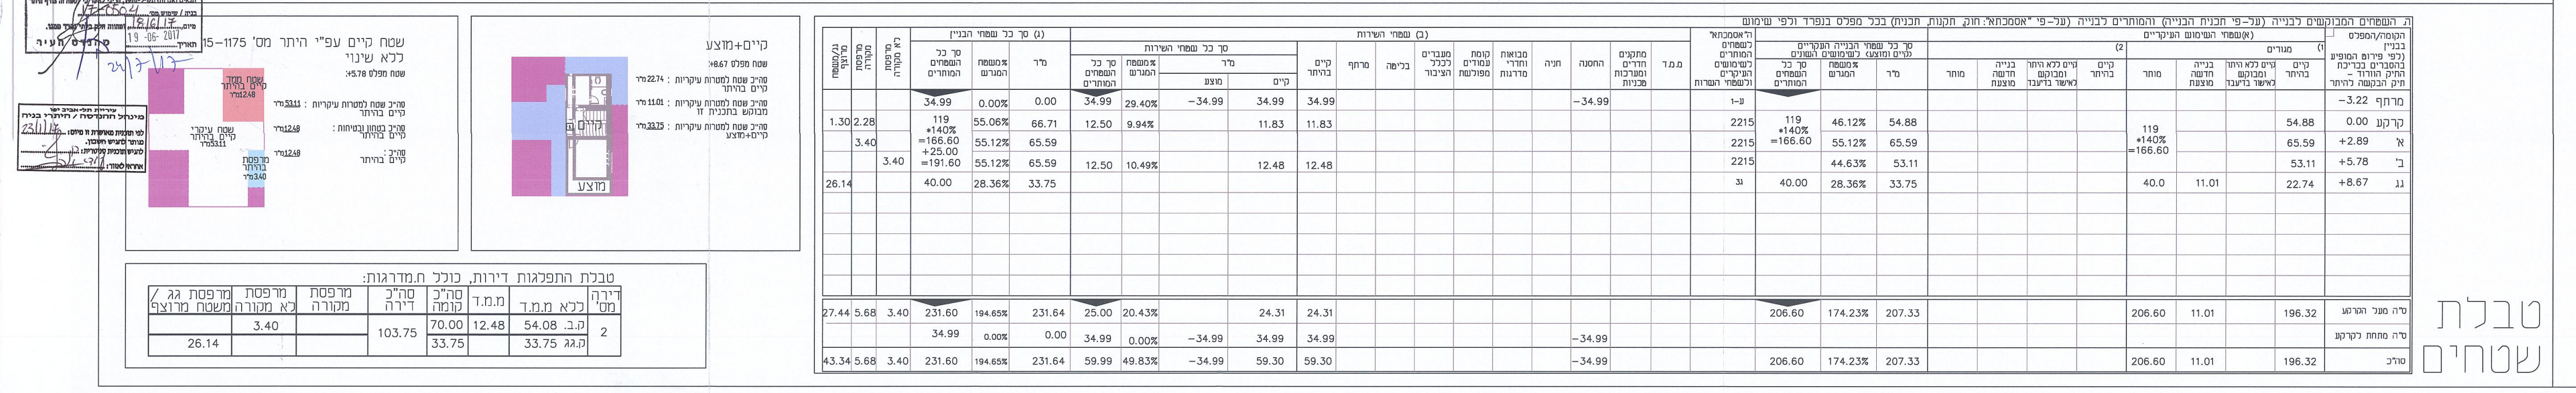

טבלת שטחים