תיק רישוי מס' 240344
הגשה
22

עיריית תל-אביב-יפו
מינהל ההנדסה, אגף רישוי ופיקוח על הבנייה
שדרות בן-גוריון 68 תל-אביב 64514 (פקס 5231340) טלפון 5217120, 5217045

חוק התכנון והבנייה, התשכ"ה-1965
תקנות התכנון והבנייה (בקשה להיתר תנאיו ואגרות) התש"ל-1970
בקשה להיתר בנייה או לשימוש במקרקעין
יש להקפיד למלא את כל הפרטים בטופס הבקשה ולצרף מסמכים כמפורט ברשימת התיוג המצורפת.

על פי טופס 1 תקנה 2(א)

מס' תיק הבניין	מס' בקשה קודמת להיתר בנייה	מס' הבקשה למידע	מתאריך
4047-013	N2002-0548	N2004-0042	15.01.04

לכבוד ☒ הוועדה המקומית לתכנון ולבנייה ☐ רשות הרישוי המקומית

א. פרטי הנכס והמבקשים

הכתובת	רחוב	מס' בית	גוש	חלקה	תת חלקה	מגרש	הוראות התכניות החלות על המקום
	תשבי 13	13	6135	110			2215

פרטים אישיים	שם משפחה ושם פרטי / שם חברה או תאגיד	מס' זהות/חברה או מס' רישום תאגיד	רחוב ומספר בית ישוב ומיקוד	מספר טלפון / מספר פקס
מבקש 1	סבן יצחק	005103700	תשבי 13 ת"א	03-7304140 052-672187
מבקש 2				
מבקש 3				
בעל הזכות בנכס	סבן יצחק	005103700	תשבי 13 ת"א	
החוכר				
עורך הבקשה הראשי	ז'בגורסקי אלכס	14687859	רח' רוטשילד 12 בת-ים	9510030 6837771
מתכנן שלד הבניין	ז'בגורסקי אלכס	14687859	רח' רוטשילד 12 בת-ים	052-544457

ב. מהות הבקשה

☐ בקשה לתוספת בנייה ☐ בקשה להרחבת דיור (במסגרת הרחבת דיור שכונתית)

☐ תוספת ______ קומות לבניין
הכוללות: ☐ ______ יחידות דיור
☐ ______
☐ תוספת בנייה בקומה ______ ☐ לחזית ☐ לאחור ☐ לצד
בשטח של ______ מ"ר
שטח הדירה / המשרד לאחר התוספות יהיה ______ מ"ר
☐ שינויים פנימיים הכוללים: ______
☒ אישור מצב קיים
☐ ______
המקום משמש כיום ל- מגורים
☐ בהיתר ☐ בלי היתר

ג. מפרט - תיאור הבקשה

תיאור הקיים על המגרש: פרט מספר מבנים, גובהם, מקומם, ייעודם וכד'
קיים בניין בן קומה 1
1 יח' דיור

שימוש עיקרי: ☒ מגורים ☐ מלונאות ☐ תעשייה ☐ חקלאי ☐ משרדים ☐ בידור ☐ בנין ציבורי ☐ מלאכה ☐ מסחר ☐ נופש וספורט ☐ שימוש אחר

סוג העבודה או השימושים המוצעים: ☐ תוספת לבניין ☐ הריסה ☐ שינוי בשימוש ☐ שינוי לבניין ☐ תיקונים; ממסורה ______ למסורה ______

הגורם שמבוצעת בעבורו הבנייה: ☐ משרד ממשלתי ☐ מוסד ציבורי ☐ בנה ביתך ☐ רשות מקומית ☒ גורם פרטי ☐ אחר: ______

שטחים	שטח המגרש/החלקה	שטח הבנייה הכולל המבוקש	אחוזי הבנייה
	90.00 מ"ר	55.92 מ"ר	62.13%

אם במסגרת הרחבת דיור שכונתית: מספר יחידות דיור מורחבות 1; מספר תכנית ההרחבה 2215

ד. חומרי הבנייה

סוג הבנייה: ☒ רגילה ☐ בית מוכן ☐ מתועשת ☐ אחר ______
קירות חיצוניים: ☐ בטון מזוין ☒ בלוקים ☐ אבן טבעית ☐ לבנים שרופות ☐ אחר ______
חומרי גימור: ☐ אבן מלאכותית ☐ אבן טבעית ☒ טיח ☐ זכוכית ☐ אחר ______
תקרות: ☒ בטון מזוין ☐ עץ ☐ אחר ______
גג: ☒ בטון מזוין ☐ רעפים ☐ אסבסט ☐ טיח ☐ אחר ______
גדרות: ☐ אבן טבעית ☐ אבן מלאכותית ☐ בטון ☐ בלוקים ☐ ברזל ☐ עץ ☐ רשת ☐ אחר ______; קיימות ____מ"א מוצעות ____ מ"א סה"כ ____מ"א
מקרא חומרים (צבעים): בטון או בטון מזוין; בלוקים או לבנים מבטון; סיליקט או לבנים אדומות; אבן; עץ; איטונג; זכוכית; הריסה; אחר

ה. השטחים המבוקשים לבנייה (על-פי תכנית הבנייה) והמותרים לבנייה (על-פי "אסמכתא": חוק, תקנות, תכנית) בכל מפלס בנפרד ולפי שימוש

הקומה/המפלס בבניין (לפי פירוט המופיע בהסברים בכריכת התיק הוורוד - תיק הבקשה להיתר)	(א) שטחי השימוש העיקריים (1) מגורים: קיים בהיתר	קיים ללא היתר ומבוקש לאישור בדיעבד	בנייה חדשה מוצעת	מותר	(2) קיים בהיתר	קיים ללא היתר ומבוקש לאישור בדיעבד	בנייה חדשה מוצעת	מותר	סך כל שטחי הבנייה העיקריים (קיים ומוצע) לשימושים השונים: מ"ר	%משטח המגרש	סך כל השטחים המותרים	ה"אסמכתא" לשטחים המותרים לשימושים העיקריים ולשטחי השירות	(ב) שטחי השירות: מקלט	מתקנים חדרים ומערכות טכניות	החסנה	חניה	מבואות וחדרי מדרגות	קומת עמודים מפולשת	מעברים לכלל הציבור	בליטות	אחר	בנייה קיימת	סך כל שטחי השירות מ"ר: קיים	מוצע	%משטח המגרש	סך כל השטחים המותרים	(ג) סך כל שטחי הבניין מ"ר	%משטח המגרש	סך כל השטחים המותרים	משטחים לא מקורים
ק.ק. 00.0	55.92								55.92	62.13	70.00	2215															55.92	62.13	70.00	
סה"כ מעל לקרקע	55.92								55.92	62.13	70.00	2215															55.92	62.13	70.00	
סה"כ מתחת לקרקע																														
סה"כ	55.92								55.92	62.13	70.00	2215															55.92	62.13	70.00	

עיריית תל-אביב-יפו
מחלקת בקרה ותיוק
23-03-2004
התקבל

ו. פרטי הבנייה - לשימוש הלשכה המרכזית לסטטיסטיקה

היעוד	שטח הבנייה ברוטו - לפי ייעוד: פירוט הייעוד (כגון דירות למגורים, בתי מלון וכו')	השטח על פי ההיתר	גודל הדירות לפי מספר חדרים: מספר חדרים	מספר דירות	מספר מגורים	מספר היתר הבנייה
למגורים			1			תאריך היתר הבנייה: שנה חודש
להארחה			2			
לעסקים ולמשרדים			3			תאריך התחלת הבנייה: שנה חודש
לבנייני ציבור			4			
לתעשייה ולמלאכה			5			תאריך גמר הבנייה: שנה חודש
למשק חקלאי			6			
למקלט או למרתף						מספר הקומות כולל קומת עמודים מפולשת
למבני עזר						
סך כל שטח הבנייה			סה"כ			

ז. קווי בנייה

הכיוון		מוצע	מותר	קווי בנייה (מטר) הסטייה במטר	ב-%
לרחוב (שם)	תשבי	0.00	0.00	-	.
לרחוב (שם)					
לצד		0.00	0.00		
לאחור		1.00	5.00		

ח. מספר יחידות דיור

אם השימוש המבוקש הוא מגורים - רשום להלן:
מספר הדירות קיימות ______ מספר הדירות המבוקשות ______ מספר הדירות המותרות ______

ט. הבקשה מוגשת לאישור

☐ הוועדה המקומית
הבקשה כוללת בקשה להקלה - כלהלן:

	פירוט הבקשה להקלה	נימוקי הבקשה להקלה
.1		
.2		
.3		

☐ רשות הרישוי המקומית
☐ רשות הרישוי המקומית באמצעות מורשה להיתר

י. הצהרת עורך הבקשה הראשי

אני מצהיר על נכונות הפרטים בסעיפים א עד ט.
תאריך 16.03.04 שם ז'בגורסקי א. חתימה X

יא. חתימות נוספות

	תאריך	שם	חתימה
המבקש	16.03.04	סבן יצחק	X סב
בעל הזכות בנכס/בעל הנכס/החוכר	16.03.04	סבן יצחק	סבן
מתכנן שלד הבניין	16.03.04	ז'בגורסקי	

לשימוש המשרד	הערות הפיקוח	התכנית תואמת את המצב בשטח: ☐ כן ☒ לא	☐ הוכן דוח ☐ לתביעה משפטית ☐ הוגשה תביעה משפטית ☐ הוגשה תביעה חוזרת	מס' הדוח/התביעה; תאריך הדוח/התביעה	הנדון בדוח / הנדון בתביעה	הערות
						מבוקש בניה קיימת ללא היתר
						תאריך 21.03.2004 שם ג'ני

אינג' אמיל פרידמן
מהנדס על הבנייה
מח' פיקוח על הבנייה
עיריית תל-אביב-יפו

437
29.03.2004

יב. מינויים מטעם מבקש ההיתר - נתמנה אדם אחד ליותר מתפקיד אחד, ימלא פרטיו ליד כל אחד מהתפקידים שהוא ממלא על פי הוראות כל דין.

מינוי עורך הבקשה הראשי: אני ממנה בזה את ז'בגורסקי אלכס בעל/ת מס' זהות 14687859 הרשום בסעיף א' להיות עורך הבקשה הראשי להיתר, ולייצגני לפני מוסדות התכנון והרשויות המוסמכות בכל הנוגע לטיפול בבקשה להיתר ולקבלתו, לרבות התיקונים ככל שידרשו הרשויות המוסמכות.

מינוי עורכי בקשה לפי תחומים: אני ממנה בזה את הרשומים להלן להיות עורכי הבקשה להיתר בתחום הפעולה הרשום ליד שמם, ולייצגני בתחום פעולתם לפני מוסדות התכנון והרשויות המוסמכות בכל הנוגע לטיפול בבקשה להיתר ולקבלתו, לרבות התיקונים ככל שידרשו הרשויות המוסמכות.

	שם משפחה ושם פרטי	תרום פעולה	המען	מספר טלפון	מספר פקס
.1		מתכנן האינסטלציה הסניטרית			
.2					

מינוי מתכנן שלד הבניין: אני ממנה בזה את ז'בגורסקי אלכס בעל/ת מס' זהות 14687859 הרשום בסעי' א' להיות אחראי לתיכנון שלד הבניין שבעבורו מבוקש ההיתר, להגיש לוועדה המקומית לרשות הרישוי המקומית את החישובים לגבי הבנייה שבעבורה מבוקש היתר ולפקח פיקוח עליון על הקמת השלד.

מינוי הקבלן האחראי לבניית: ☐ אני ממנה בזה את ______ בעל/ת מס' זהות ______ ובעל תעודת רישום בפנקס הקבלנים מספר ______ בסוג ______ ובעל ______ לביצוע עבודה בהיקף עד ______ לבצע את העבודה הנדונה בהיתר כמתחייב לפי כל דין.
☐ אני מצהיר, כי טרם מסרתי את ביצוע העבודה הנדונה בהיתר לידי קבלן, ומתחייב כי אמסור אותה לידי קבלן רשום בפנקס הקבלנים, כמתחייב על פי כל דין, והודיע על כך לרשות הרישוי המקומית טרם התחלת ביצוע העבודה, וחתימתו של הקבלן תצורף להודעה המפרטת את פרטי רישומו של הקבלן.

מינוי האחראי לביצוע שלד הבניין: ☐ אני ממנה בזה את ______ בעל/ת מס' זהות ______ כתובת ______ טלפון ______ פקס ______ הרשום לעיל להיות אחראי לביצוע שלד.
☐ אני מצהיר, כי טרם מיניתי אחראי/ת לביצוע עבודות בתחומים האלה: ______ ומתחייב לעשות זאת כמפורט בתקנות, ולהודיע על כך לרשות הרישוי המקומית טרם התחלת ביצוע העבודה.

מינוי אחראים לביקורת: ☐ אני ממנה בזה את הרשומים להלן להיות אחראים לביקורת על ביצוע עבודות בתחום הפעולה כרשום ליד שמם.

	שם משפחה ושם פרטי	תרום פעולה	המען	מספר טלפון	מספר פקס
.1		אחראי ראשי			
.2					
.3					

☐ אני מצהיר כי טרם מיניתי אחראי/ם לביקורת על ביצוע עבודות את כלם או את קצתם בתחומים האלה: ______ ומתחייב לעשות זאת כמפורט בתקנות, ולהודיע על כך לרשות הרישוי המקומית טרם התחלת ביצוע העבודה.

X סב חתימת המבקש על המינויים X

יג. הצהרות

הצהרת עורכי הבקשה: אנו החתומים מטה מצהירים בזה:
1) כל אחד מאתנו מאשר שהאמור בנוגע לרשימה שבסעיף "לעיל הוא נכון.
2) כל אחד מאתנו מסכים לקבל עליו את התפקיד המיועד לו בסעיף "לעיל.
3) אנו מצהירים, כל אחד בנוגע לתחום פעולתו, שיש לנו כישורים מקצועיים לערוך בקשה זו וכי בדקנו את המסמכים הנוגעים לבקשה, לרבות כל תכנית הנוגעת לבקשה, וידוע לנו כי אם הצהרה זו אינה נכונה, הרי היא תיחשב מסירת ידיעה שהיא כוזבת או מטעה בפרט חשוב, כמשמעותה בסעיף 214 לחוק, וצפויים לנו העונשים הקבועים לפי כל דין.

כולל הצהרת עורך הבקשה על לחץ המים: אני ז'בגורסקי אלכס (עורך בקשה ראשי) אחראי/ת לכך שהבקשה, ובכלל זה נספחות, נערכה לפי מיטב הידיעה המקצועית ובהתאם לכל חיקוק החל על או העבודה המוצעת, שכל הנתונים שנמסרו על ידי בבקשה זו נכונים ושהתכנון המוצע תואם את כל התכניות, פרט לסטיות שפורטו לעיל.
☐ אני עורך הבקשה מתכנן האינסטלציה הסניטרית, מצהיר בזאת ואחראי לכך שתכניות הבקשה בכל הנוגע לסידורים הסניטריים נערכו כדין וכי קויימו בהן הוראות החוק וההוראות כמתקני תברואה התש"ל 1970 (הל"ת) לענין זה, לרבות בדיקת לחץ המים הקיים בבנין ותיכנון בהתאם.

	תאריך	שם משפחה ושם פרטי	מספר רישיון	חתימה
עורך בקשה ראשי	16.03.04	ז'בגורסקי אלכס	15320	
עורך בקשה 1 מתכ' האינס הסניס'				
עורך בקשה 2				

הצהרת מתכנן שלד הבניין: אני החתום מטה (שם משפחה ושם פרטי) ז'בגורסקי אלכס מס' זהות 14687859 מהנדס רשוי מס' 15320 /הנדסאי בעל רישיון מס' ______ ("מבנה פשוט") מצהיר בזאת כדלקמן:
1) אני מסכים להיות מתכנן שלד הנדון בבקשה ולפקח פיקוח עליון על הקמת השלד.
2) אני מתחייב להגיש לפני מתן ההיתר, נושא הבקשה את החישובים הסטטיים בדבר ש בעבורה ההיתר.
3) ידוע לי, שאם אחרי הגשת הנתונים הסטטיים יתגלה צורך בשינוי מהותי בהם, אני מתחייב להגיש חישובים סטטיים מתוקנים מיד עם גילוי הצורך בכך.
4) אני מצהיר, כי יש לי כישורים מקצועיים לערוך בקשה זו וכי בדקתי את כל המסמכים הנוגעים לבקשה, לרבות כל תכנית הנוגעת לבקשה, וידוע לי כי אם הצהרה זו אינה נכונה, הרי היא תיחשב מסירת ידיעה שהיא כוזבת או מטעה בפרט חשוב, כמשמעותה בסעיף 214 לחוק, וצפויים לי העונשים הקבועים לפי כל דין.
5) ידוע לי כי עלי לשמור את תכניות הקונסטרוקציה לתקופה של לא פחות מ-10 שנים לאחר גמר הבניה.
X ______ חתימה 16.03.04 תאריך

הצהרת האחראי לביצוע שלד הבניין (כאשר מונה): אני החתום מטה (שם משפחה ושם פרטי) ______ מס' זהות ______ מהנדס רשוי מס' ______ /הנדסאי בעל רישיון מס' ______ ("מבנה פשוט") מצהיר בזאת כדלקמן:
1) אני מסכים להיות האחראי לביצוע שלד הבניין
2) אני מצהיר, כי יש לי כישורים מקצועיים להיות אחראי לביצוע שלד ______, ואני מתחייב לדאוג לביצוע שלד ______ על פי תוכניות והוראות של מתכנן השלד כפי ______ בכתב וכן למלא את תפקידי על פי שנקבע בכל חיקוק הנוגע לכך.
______ חתימה ______ תאריך

הצהרת אחראים לביקורת (כאשר מונו): אנו החתומים מטה מצהירים בזה:
1) כל אחד מאיתנו מאשר שהאמור בנוגע לו ברשימה שבסעיף י"ב לעיל הוא נכון.
2) כל אחד מאיתנו מסכים לקבל עליו את התפקיד המיועד לו בסעיף י"ב.
3) אנו מצהירים כל אחד בנוגע לתחום פעולתו, שיש לנו כישורים מקצועיים לערוך את הביקורת כהלכה ולדווח על תוצאותיה לרשות הרישוי המקומית כמתחייב על פי כל דין.
אני ______ (עורך הביקורת הראשי) אחראי/ת לכך שהביקורת תיערך על פי מיטב הידיעה המקצועית, ושכל הדיווחים לרשות הרישוי המקומית ייערכו על פי כל דין.

תאריך	שם משפחה ושם פרטי	מספר רישיון	חתימה

מקום: שכונת התקוה

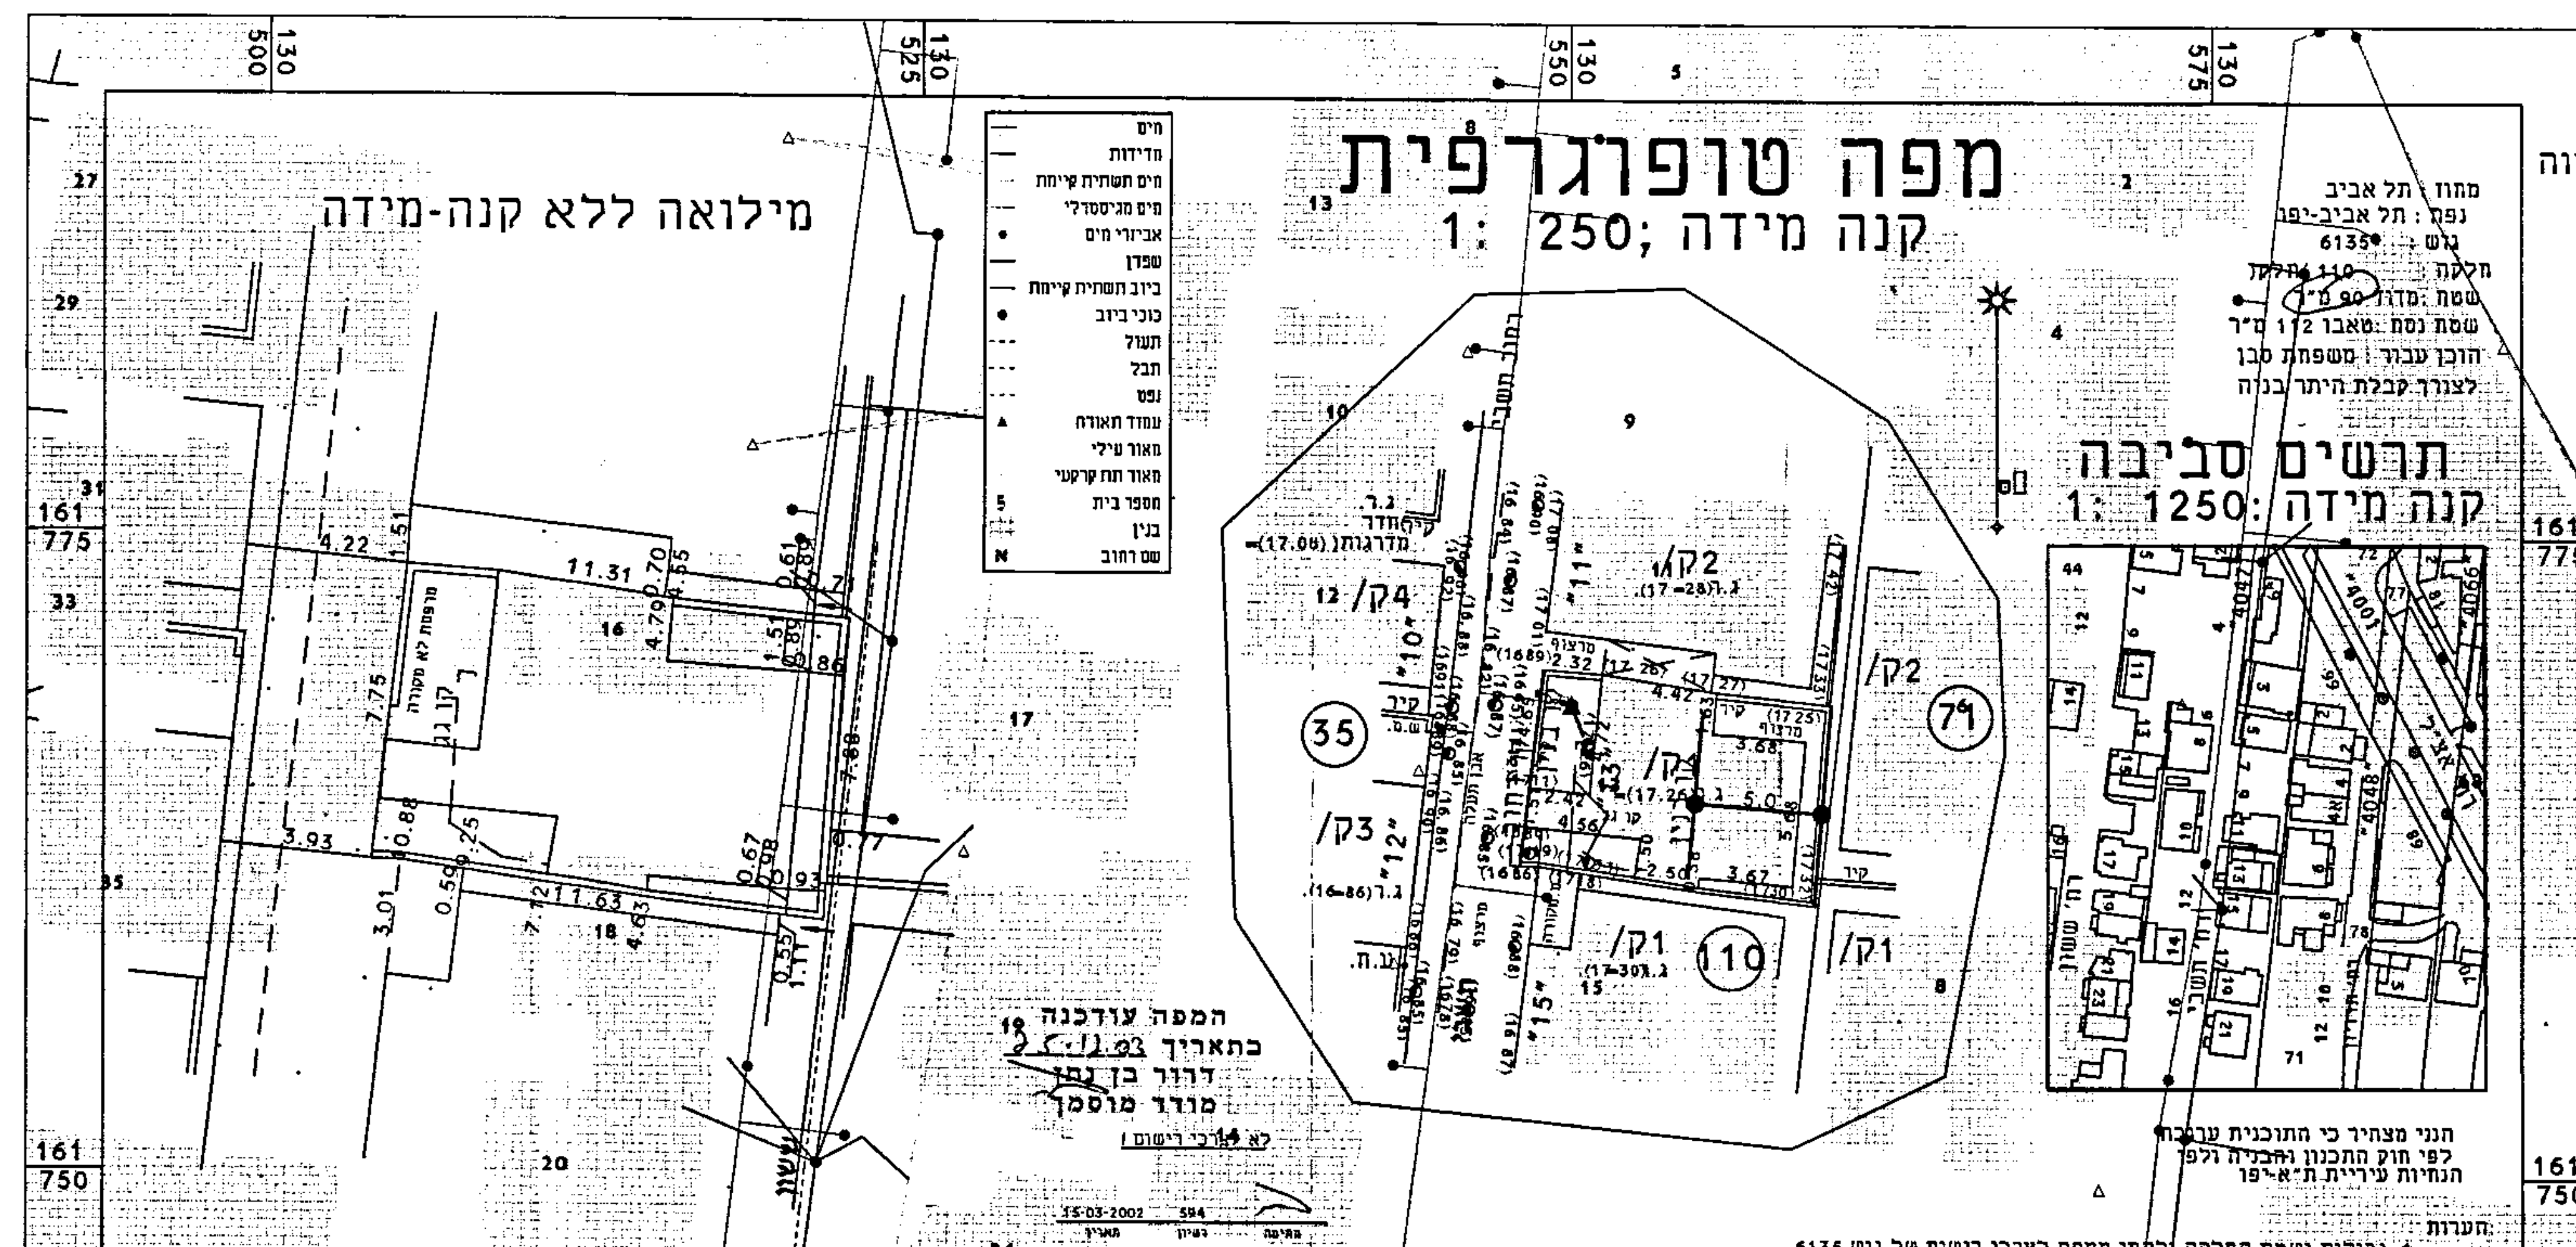

מפה טופוגרפית
קנה מידה 1: 250

מחוז: תל אביב
נפה: תל אביב-יפו
גוש: 6135
חלקה 110
שטח מדוד 90 מ"ר
שטח נסח טאבו 112 מ"ר
הוכן עבור: משפחת סבן
לצורך קבלת היתר בניה

המפה עודכנה בתאריך 15.01.04
דרור בן נתן
מודד מוסמך
לא לצרכי רישום

הנני מצהיר כי התוכנית ערוכה לפי חוק התכנון והבניה ולפי הנחיות עיריית ת"א-יפו

הערות:
1. גבולות ושטח החלקה נלקחו ממפת לצרכי רישום של גוש 6135
2. המספרים בסוגריים מסמנים גבהים אבסולוטיים
3. הגבהים מבוססים על BM4870 שגובהו 17.549

דרור בן נתן - מודד מוסמך

בקשה מספר: 2002-00548 תשבי 13 קנ"מ : 1 : 250

חישוב שטחים
ק.מ. 1:100

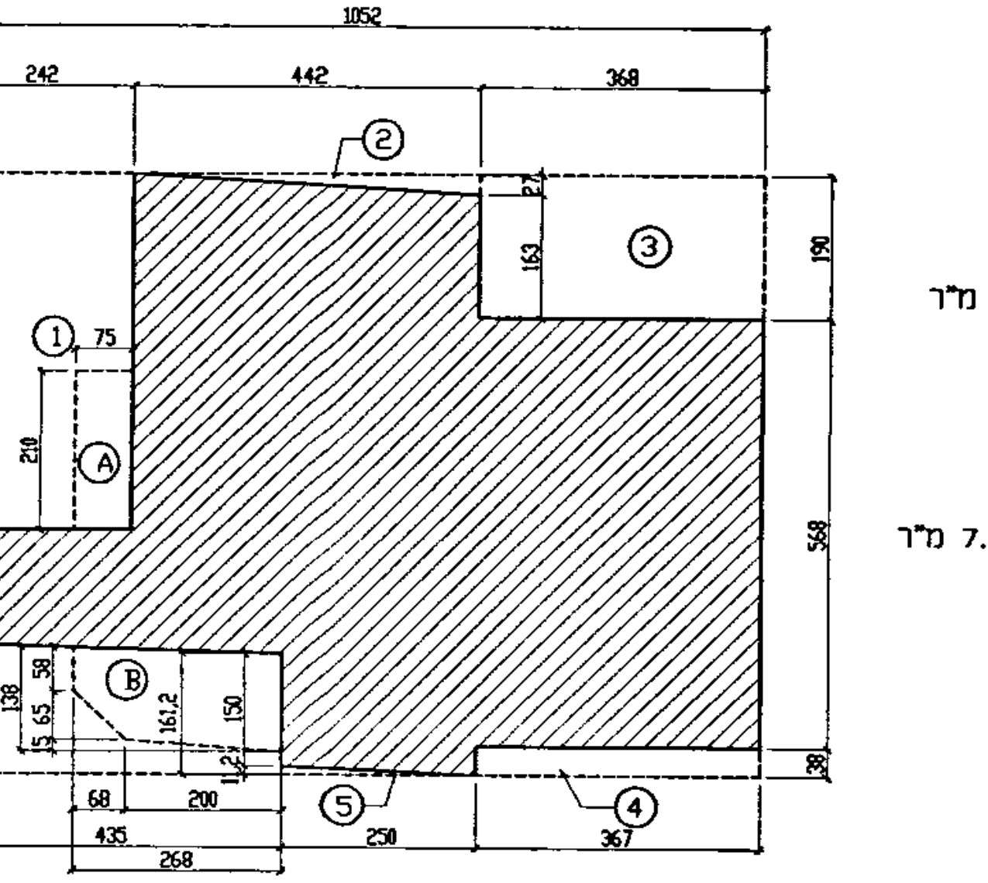

שטח קיים:
המסגרת: 83.74=7.96*10.52 מ"ר

2) 0.60=0.27*4.42/2 מ"ר
3) 7.00=1.90*3.68 מ"ר
4) 1.40=0.38*3.67 מ"ר
5) 0.14=2.50*0.11/2 מ"ר
6) 7.26=(1.61+1.73)*4.35/2 מ"ר
סה"כ: 27.82 מ"ר
שטח דירה: 55.92 מ"ר

שטח גגון:
A) 1.57=2.10*0.75 מ"ר
B) 3.70=1.38*2.68 מ"ר
פחות: 0.22=0.65*0.68/2 מ"ר
פחות: 0.15=2.00*0.15/2 מ"ר
סה"כ: 4.90 מ"ר

חישוב תכסית:
0.67=(4.90+55.92)/90

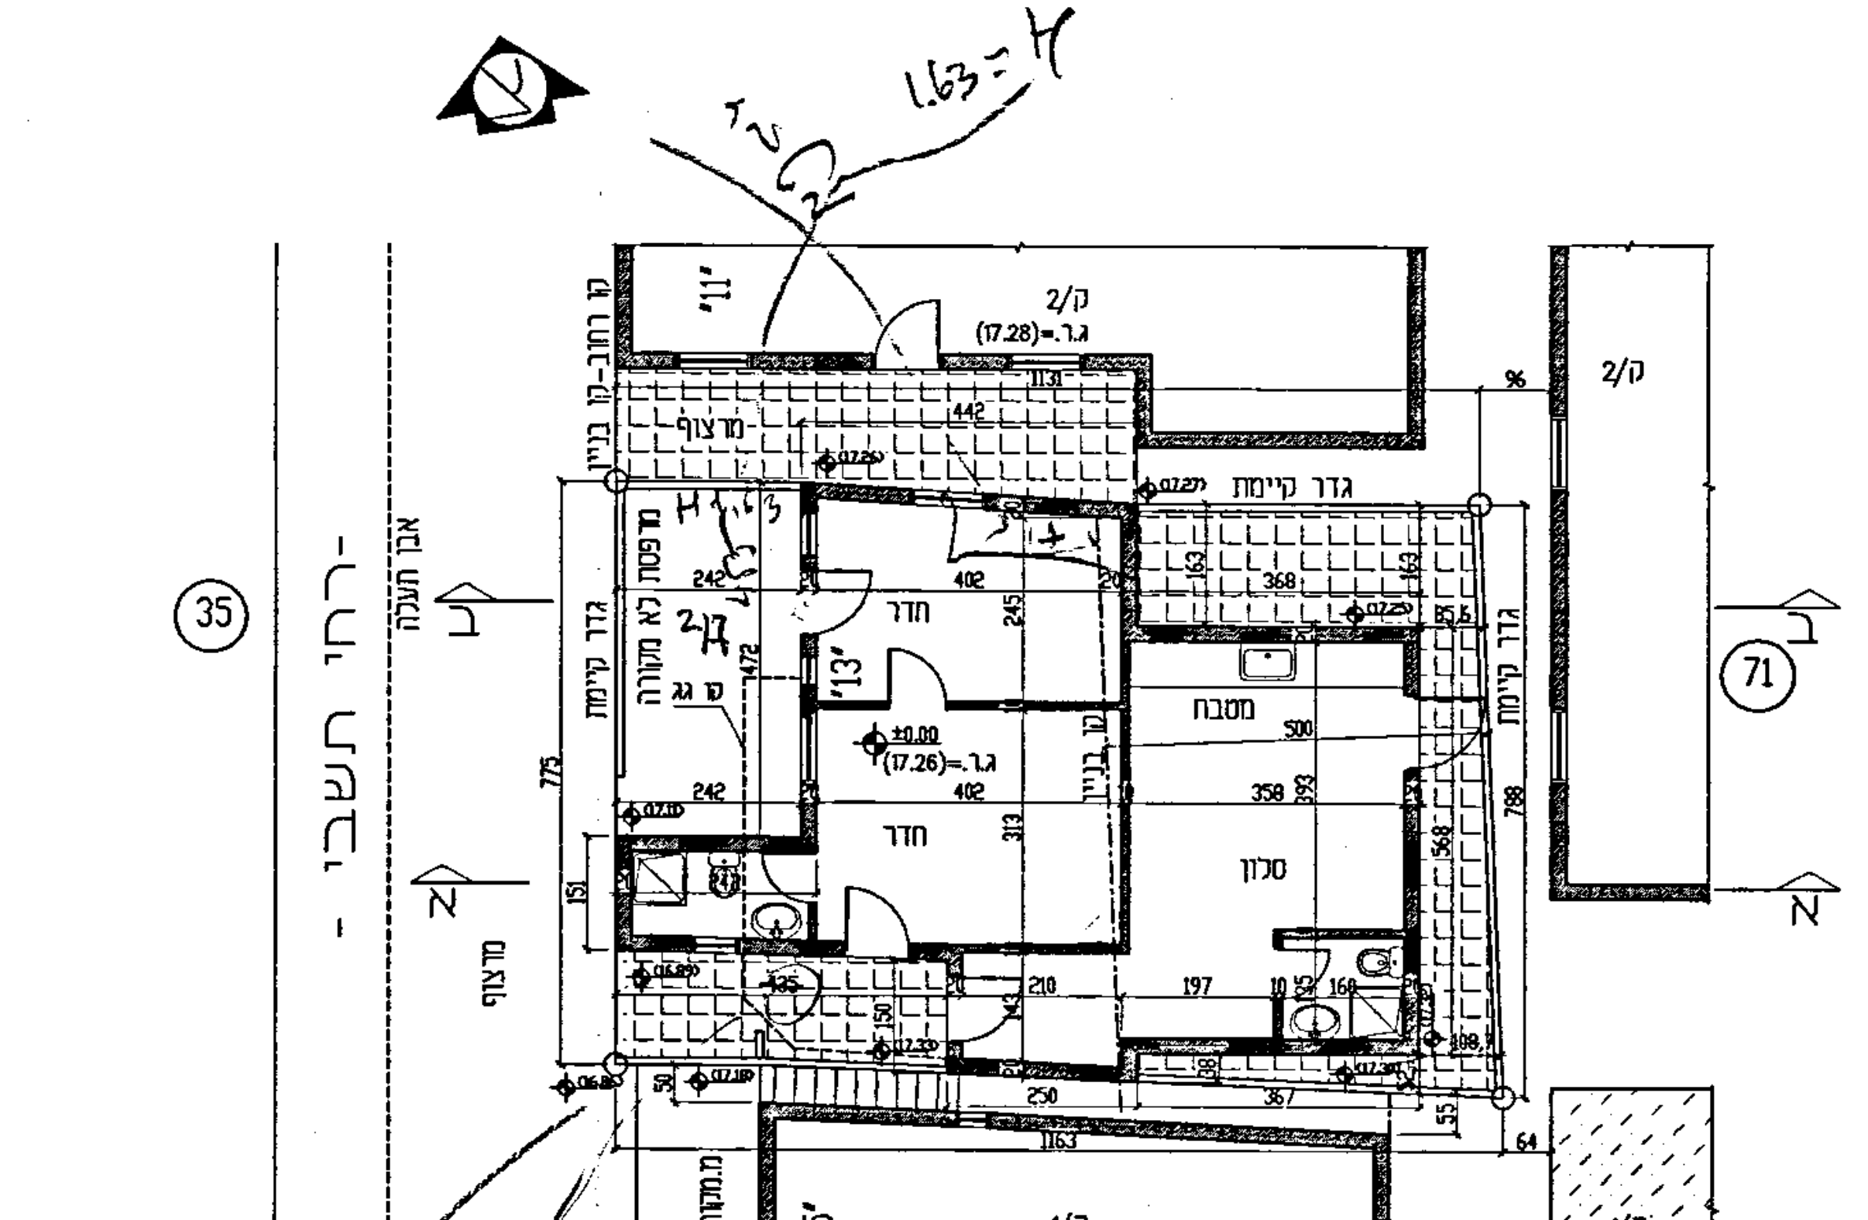

תכנית קומת קרקע
ק.מ. 1:100

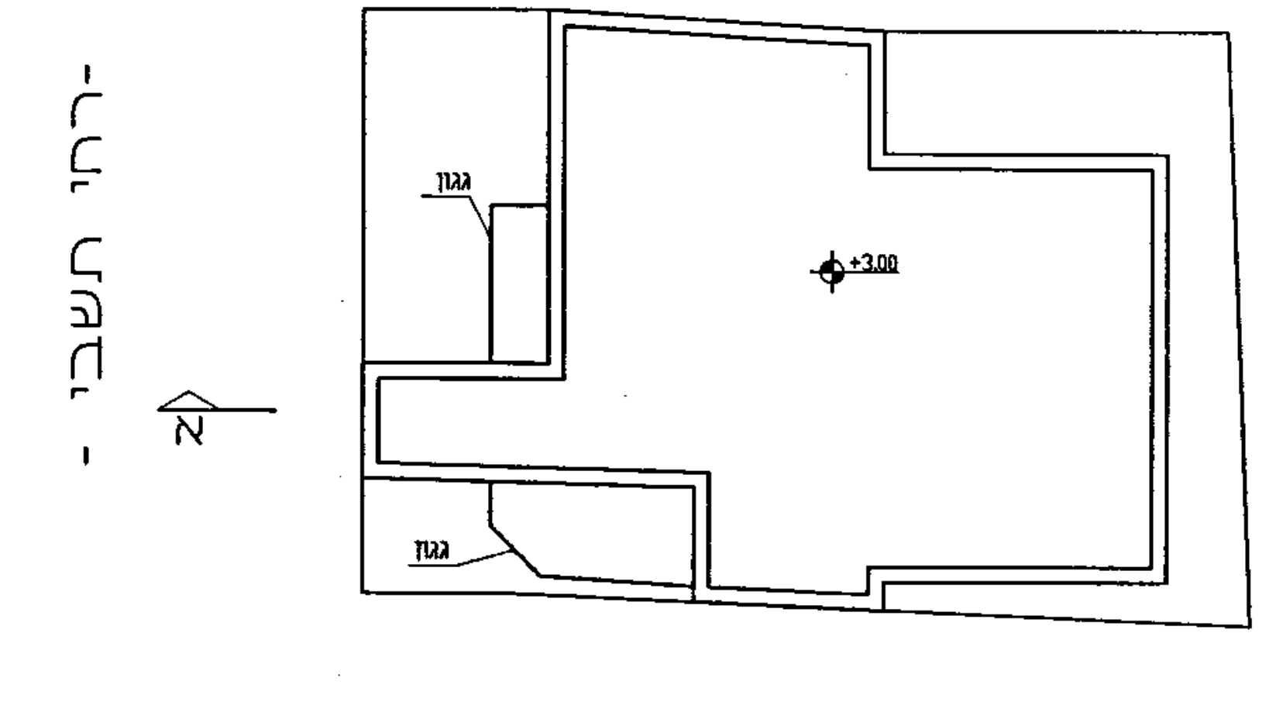

תכנית גג
ק.מ. 1:100

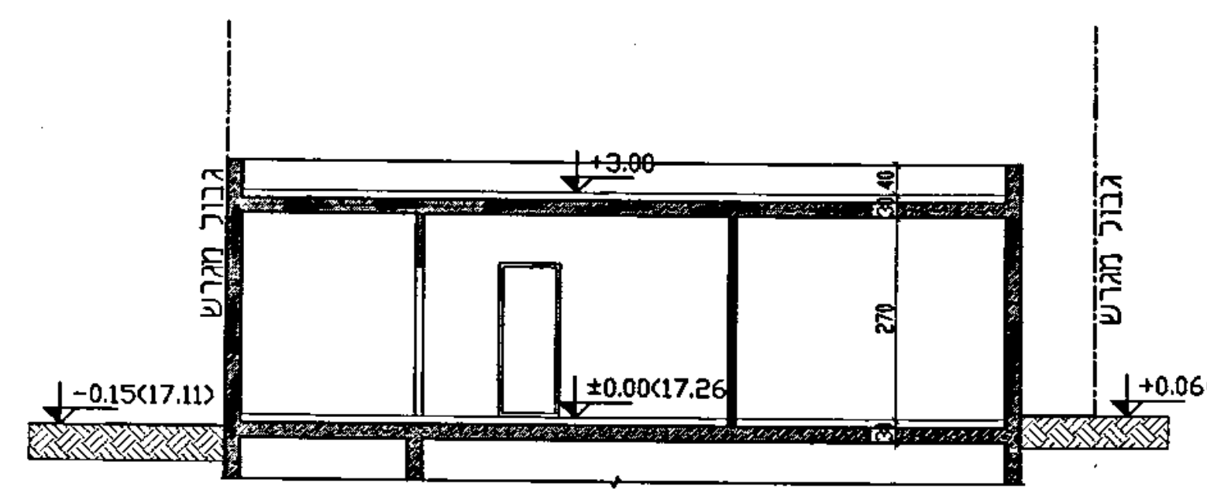

חתך א-א
ק.מ. 1:100

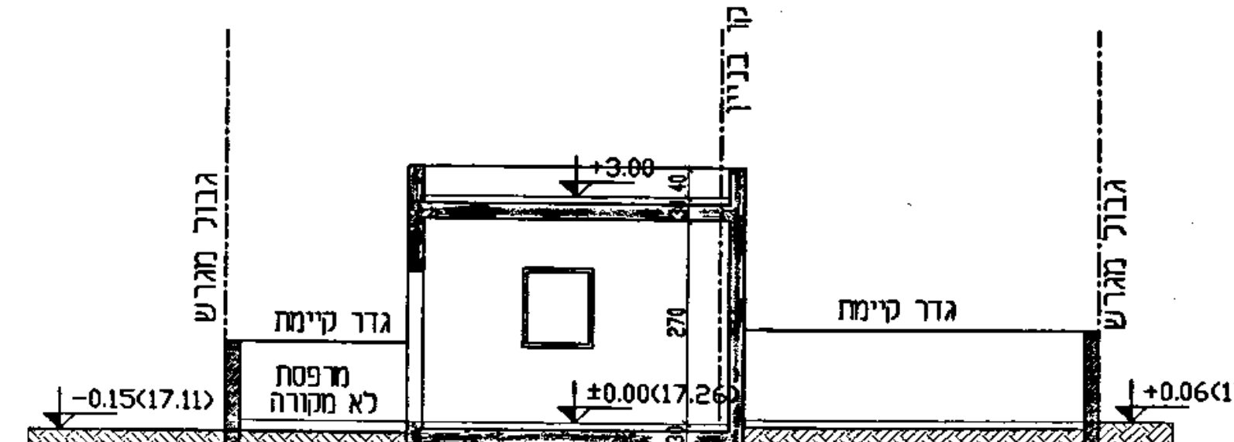

חתך ב-ב
ק.מ. 1:100

סוף מגרש

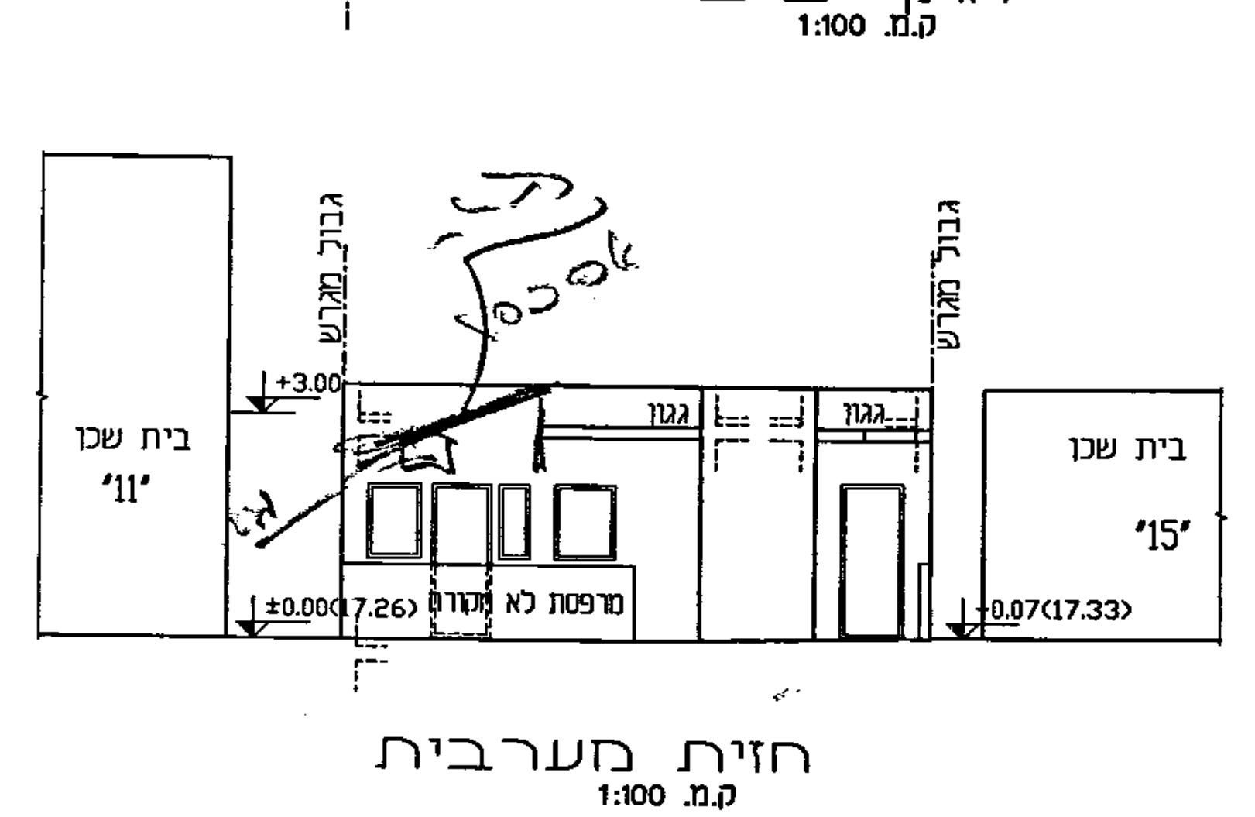

חזית מערבית
ק.מ. 1:100

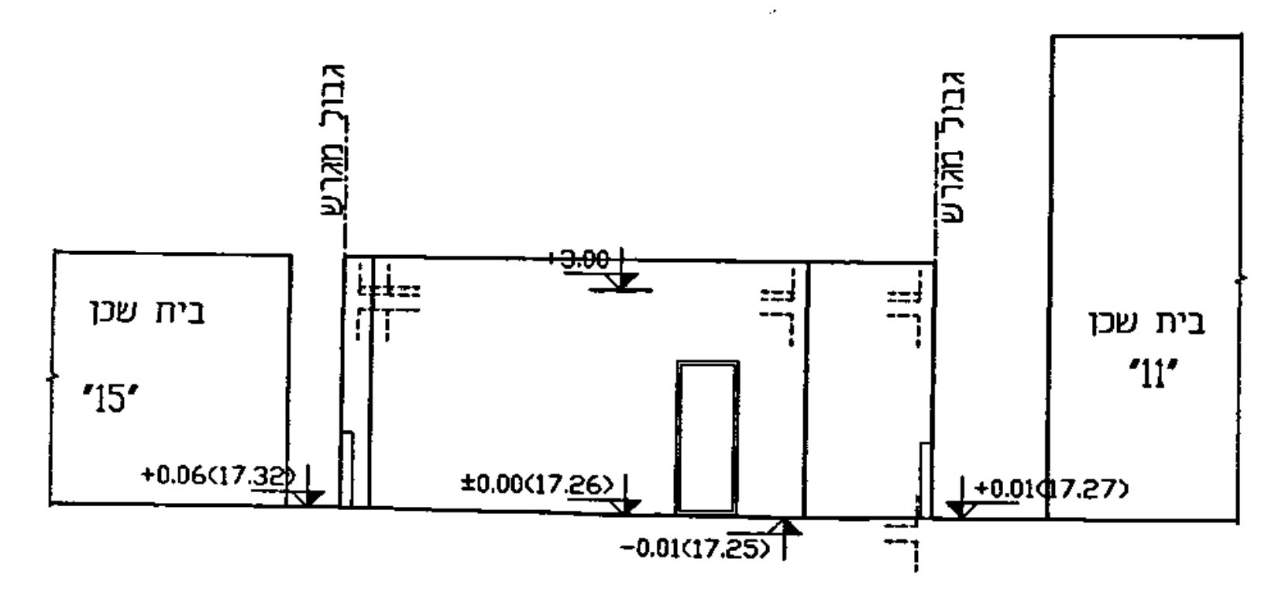

חזית מזרחית
ק.מ. 1:100

איכות נמוכה