22
7240344

004

16-05-2004

עיריית תל-אביב-יפו

מינהל ההנדסה, אגף רישוי ופיקוח על הבנייה
שדרות בן-גוריון 68 תל-אביב 64514 (פקס 5231340) טלפון 5217120, 5217045

לכבודם
○ הוועדה המקומית לתכנון ולבנייה
○ רשות הרישוי המקומית

חוק התכנון והבניה, התשכ"ה-1965
תקנות התכנון והבנייה (בקשה להיתר תנאיו ואגרות) התש"ל-1970
בקשה להיתר בנייה או לשימוש במקרקעין
יש להקפיד למלא את כל הפרטים בטופס הבקשה ולצרף מסמכים כמפורט ברשימת התיוג המצורפת.

על פי טופס 1 תקנה 2(א)

מס' תיק הבניין	מס' בקשה קודמת להיתר בנייה	מס' הבקשה למידע	מתאריך
4047-013	N2002-0548	N2004-0042	15.01.04

א. פרטי הנכס והמבקשים

הכתובת	רחוב	מס' בית	גוש	חלקה	תת חלקה	מגרש	הוראות התכניות החלות על המקום
	תישבי	13	6135	110			2215

פרטים אישיים	שם משפחה	שם פרטי או תאגיד	מס' זהות/חברה או מס' רישום תאגיד	רחוב ומספר בית, ישוב ומיקוד	מספר טלפון / מספר פקס
מבקש 1	סבן יצחק		005103700	תשבי 13 ת"א	03-7304140 052-672187
מבקש 2					
מבקש 3					
בעל הזכות בנכס	סבן יצחק		005103700	תשבי 13 ת"א	
החוכר					
עורך הבקשה הראשי	ד'בגורסקי אלכס		14687859	רח' רוטשילד 12 בת-ים	9510030 6837771
מתכנן שלד הבניין	ד'בגורסקי אלכס		14687859	רח' רוטשילד 12 בת-ים	052-544457

ב. מהות הבקשה

☐ בקשה לתוספת בנייה ☐ בקשה להרחבת דיור (במסגרת הרחבת דיור שכונתית)
☐ תוספת ____ קומות בבניין הכוללות: ____ יחידות דיור ☐ ☐
☐ תוספת בנייה בקומה ____ ☐ לחזית ☐ לאחור ☐ לצד בשטח של ____ מ"ר
שטח הדירה / המשרד לאחר התוספות יהיה ____ מ"ר
☐ שינויים פנימיים הכוללים: ____
☒ אישור מצב קיים
☐
המקום משמש כיום ל- מגורים ☐ בהיתר ☐ בלי היתר

ג. מפרט - תיאור הבקשה

פרט מספר מבנים, גובהם, מקומם, ייעודם וכו'

תיאור הקיים על המגרש	קיים בניין בן קומה 1 1 יח' דיור
שימוש עיקרי	☒ מגורים ☐ מלונאות ☐ תעשיה ☐ חקלאי ☐ משרדים ☐ בידור ☐ בנין ציבורי ☐ מלאכה ☐ מסחר ☐ נופש וספורט ☐ שימוש אחר
סוג העבודה או השימושים המוצעים	☐ תוספת לבניין ☐ הריסה ☐ שינוי בשימוש ☐ שינוי לבניין ☐ תיקונים ____ ממטרה ____ למטרה
הגורם שבמוצעת עבורו הבנייה	☐ משרד ממשלתי ☐ מוסד ציבורי ☐ בנה ביתך ☐ רשות מקומית ☒ גורם פרטי ☐ אחר:
שטחים	שטח המגרש/ החלקה 90.00 מ"ר; שטח הבנייה הכולל המבוקש 55.92 מ"ר; אחוזי הבנייה 62.13%
אם במסגרת הרחבת דיור שכונתית	מספר יחידות דיור מורחבות 1; מספר תכנית ההרחבה 2215

ד. חומרי הבנייה

סוג הבנייה	☒ רגילה ☐ בית מוכן ☐ מתועשת ☐ אחר
קירות חיצוניים	☐ בטון מזוין ☒ בלוקים ☐ אבן טבעית ☐ לבנים שרופות ☐ אחר
חומרי גימור	☐ אבן מלאכותית ☐ אבן טבעית ☒ טיח ☐ זכוכית ☐ אחר
תקרות	☒ בטון מזוין ☐ עץ ☐ אחר
גג	☒ בטון מזוין ☐ אסבסט ☐ רעפים ☐ טיח ☐ אחר
גדרות	☐ אבן טבעית ☐ אבן מלאכותית ☐ בלוקים ☐ ברזל ☐ בטון ☐ עץ ☐ רשת ☐ אחר; קיימות ____ מ"א מוצעות ____ מ"א סה"כ ____ מ"א
מקרא חומרים (צבעים)	בטון או בטון מזוין / בלוקים או לבנים מבטון / סיליקט או לבנים אדומות / אבן / עץ / איטונג / זכוכית / הריסה / אחר

ה. השטחים המבוקשים לבנייה (על-פי תכנית הבנייה) והמותרים לבנייה (על-פי "אסמכתא": חוק, תקנות, תכנית) בכל מפלס בנפרד ולפי שימוש

הקומה/המפלס	(א) שטחי השימוש העיקריים: 1) מגורים – קיים בהיתר	קיים ללא היתר ומבוקש לאישור בייעוד	בנייה חדשה מוצעת	מותר	2) – קיים בהיתר	קיים ללא היתר	בנייה חדשה	מותר	סך כל שטחי הבנייה העיקריים לשימושים השונים: מ"ר	% משטח המגרש	סך כל השטחים המותרים	ה"אסמכתא" לשטחים המותרים	(ב) שטחי השירות: מקלט	מתקנים	החסנה	חניה	מבואות וחדרי מדרגות	קומת עמודים מפולשת	מעברים לכלל הציבור	בליטות	אחר	בנייה קיימת	סך כל שטחי השירות: מ"ר קיים / מוצע	% משטח המגרש	סך כל השטחים המותרים	(ג) סך כל שטחי הבניין: מ"ר	% משטח המגרש	סך כל השטחים המותרים	משטחים לא מקורים
ק.ק. 00.0		55.92							55.92	62.13	70.00	2215														55.92	62.13	70.00	11.42
ס"ה מעל לקרקע		55.92							55.92	62.13	70.00	2215														55.92	62.13	70.00	
ס"ה מתחת לקרקע																													
סה"כ		55.92							55.92	62.13	70.00	2215														55.92	62.13	70.00	

ו. פרטי הבנייה - לשימוש הלשכה המרכזית לסטטיסטיקה

הייעוד	פירוט הייעוד (כגון דירות למגורים, בתי מלון וכו')	השטח על פי ההיתר	מספר חדרים	מספר דירות	מספר חדרים למגורים
למגורים			1		
להארחה			2		
לעסקים ולמשרדים			3		
לבנייני ציבור			4		
לתעשיה ולמלאכה			5		
למשק חקלאי			6		
למקלט או למרתף					
למבני עזר					
סך כל שטח הבנייה			סה"כ		

מספר היתר הבנייה ____
תאריך היתר הבנייה: שנה ____ חודש ____
תאריך התחלת הבנייה: שנה ____ חודש ____
תאריך גמר הבנייה: שנה ____ חודש ____
מספר הקומות כולל קומת עמודים מפולשת ____

ז. קווי בנייה

הכיוון		מוצע	מותר	קווי בנייה (מטר) הסטייה במטר	ב- %
לרחוב (שם)	תשבי	0.00	0.00		
לרחוב (שם)					
לצד		0.00	0.00		
לאחור		1.00	5.00		

ח. מספר יחידות דיור

אם השימוש המבוקש הוא מגורים – רשום להלן:
מספר הדירות קיימות ____ מספר הדירות המבוקשות ____ מספר הדירות המותרות ____

ט. הבקשה מוגשת לאישור

☐ הוועדה המקומית
הבקשה כוללת בקשה להקלה – כלהלן:

	פירוט הבקשה להקלה	נימוקי הבקשה להקלה
.1		
.2		
.3		

☐ רשות הרישוי המקומית
☐ רשות הרישוי המקומית באמצעות מורשה להיתר

י. הצהרת עורך הבקשה הראשי

אני מצהיר על נכונות הפרטים בסעיפים א עד ט.
תאריך 16.03.04 שם ד'בגורסקי א. חתימה X

יא. חתימות נוספות

המבקש	תאריך 16.03.04	שם סבן יצחק	חתימה X
בעל הזכות בנכס/ בעל הנכס/ החוכר	תאריך 16.03.04	שם סבן יצחק	חתימה
	תאריך	שם	חתימה
מתכנן שלד הבניין	תאריך 16.03.04	שם ד'בגורסקי א.	חתימה

ד'בגורסקי אלכס
מהנדס בנין
15320

לשימוש המשרד	התוכנית תואמת את המצב בשטח		מס' הדו"ח/ התביעה	הנדון בדוח / הנדון בתביעה	הערות
הערות הפיקוח	☒ כן ☐ לא	☐ הוכן דוח לתביעה משפטית ☒ הוגשה תביעה משפטית ☐ הוגשה תביעה חוזרת	299/01	תוספת	

תאריך 11.05.2004
אינג' אמיר פרידמן
מהנדס אזור
מח' פיקוח על הבניה
עיריית תל-אביב-יפו

456

11.05.2004
אינג' אמיר פרידמן
מהנדס איזור
מח' פיקוח על הבניה
עיריית תל-אביב-יפו

יב. מינויים מטעם מבקש ההיתר - נתמנה אדם אחד ליותר מתפקיד אחד, ימולא פרטיו ליד כל אחד מהתפקידים שהוא ממלא על פי הוראת כל דין.

מינוי עורך הבקשה הראשי: אני ממנה בזה את ד'בגורסקי אלכס בעל/ת מס' זהות 14687859 הרשום בסעיף א' להיות עורך הבקשה הראשי להיתר, ולייצגני לפני מוסדות התכנון והרשויות המוסמכות בכל הנוגע לטיפול בבקשה להיתר ולקבלתו, לרבות התיקונים ככל שידרשו הרשויות המוסמכות.

מינוי עורכי בקשה לפי תחומים: אני ממנה בזה את הרשומים להלן להיות עורכי הבקשה להיתר בתחום הפעולה כרשום ליד שמם, ולייצגני בתחום פעולתם לפני מוסדות התכנון והרשויות המוסמכות בכל הנוגע לטיפול בבקשה להיתר ולקבלתו, לרבות התיקונים ככל שידרשו הרשויות המוסמכות.

	שם משפחה ושם פרטי	תחום פעולה	המען	מספר טלפון	מספר פקס
.1		מתכנן האינסטלציה הסניטרית			
.2					

מינוי מתכנן שלד הבניין: אני ממנה בזה את ד'בגורסקי אלכס בעל/ת מס' זהות 14687859 הרשום בסעי' א' להיות אחראי לתיכנון שלד הבנין שבעבורו מבוקש ההיתר, להגיש לוועדה המקומית לרשות הרישוי המקומית את החישובים לגבי הבניה שבעבורה מבוקש היתר ולפקח פיקוח עליון על הקמת השלד.

מינוי הקבלן האחראי לבנייה:
☐ אני ממנה בזה את ____ בעל/ת מס' זהות ____ ובעל תעודת רישום בפנקס הקבלנים מספר ____ במדור ____ ובעל ____ לביצוע עבודה בהיקף עד ____ לבצע את העבודה הנדונה בהיתר כמתחייב לפי כל דין.
☐ אני מצהיר, כי טרם מסרתי את ביצוע העבודה הנדונה בהיתר לידי קבלן, ומתחייב כי אמסור אותה לידי קבלן רשום בפנקס הקבלנים, כמתחייב על פי כל דין, והודיע על כך לרשות הרישוי המקומית טרם התחלת ביצוע העבודה, ותחימתו של הקבלן תצורף להודעה המפרטת את פרטי רישומו של הקבלן.

מינוי האחראי לביצוע שלד הבניין:
☐ אני ממנה בזה את ____ בעל/ת מס' זהות ____ כתובת ____ טלפון ____ פקס ____ הרשום לעיל להיות אחראי לביצוע שלד
☐ אני מצהיר, כי טרם מיניתי אחראי/ת לביצוע עבודות בתחומים האלה: ____ ומתחייב לעשות זאת כמפורט בתקנות, ולהודיע על כך לרשות הרישוי המקומית טרם התחלת ביצוע העבודה.

מינוי אחראים לביקורת:
☐ אני ממנה בזה את הרשומים להלן להיות אחראים לביקורת על ביצוע עבודות בתחום הפעולה כרשום ליד שמם.

	שם משפחה ושם פרטי	תחום פעולה	המען	מספר טלפון	מספר פקס
.1		אחראי ראשי			
.2					
.3					

☐ אני מצהיר כי טרם מיניתי אחראי/ם לביקורת על ביצוע עבודות את כולם או את קצתם בתחומים האלה: ____ ומתחייב לעשות זאת כמפורט בתקנות, ולהודיע על כך לרשות הרישוי המקומית טרם התחלת ביצוע העבודה.

חתימת המבקש על המינויים X ____ X

יג. הצהרות

הצהרת עורכי הבקשה:
אנו החתומים מטה מצהירים בזה:
1) כל אחד מאתנו מאשר שהאמור בנוגע לרשימה שבסעיף "לעיל הוא נכון.
2) כל אחד מאתנו מסכים לקבל עליו את התפקיד המיועד לו בסעיף "לעיל.
3) אנו מצהירים, כל אחד בנוגע לתחום פעולתו, שיש לנו כישורים מקצועיים לערוך בקשה זו וכי בדקנו את המסמכים הנוגעים לבקשה, לרבות כל תכנית הנוגעת לבקשה, וידוע לנו כי אם הצהרה זו אינה נכונה, הרי היא תיחשב מסירת ידיעה שהיא כוזבת או מטעה בפרט חשוב, כמשמעותה בסעיף 214 לחוק, וצפויים לנו העונשים הקבועים לפי כל דין.

כולל הצהרת עורך הבקשה על לחץ המים: אני ד'בגורסקי אלכס (עורך בקשה ראשי) אחראי/ת לכך שהבקשה, ובכלל זה נספחיה, נערכה לפי מיטב הידיעה המקצועית ובהתאם לכל חיקוק החל על ____ או העבודה המוצעת, שכל הנתונים שנמסרו על ידי בבקשה זו נכונים ושהתכנון המוצע תואם את כל התכניות, פרט לסטיות שפורטו לעיל.
☐ אני עורך הבקשה מתכנן האינסטלציה הסניטרית, מצהיר בזאת ואחראי לכך שתכניות הבקשה בכל הנוגע לסידורים הסניטריים נערכו בדין וכי קויימו בהן הוראות החוק וההוראות למתקני תברואה התש"ל 1970 (הל"ת) לעניין זה, לרבות בדיקת לחץ המים הקיים בבנין ותיכנון בהתאם.

	תאריך	שם משפחה ושם פרטי	מספר רישיון	חתימה
עורך בקשה ראשי	16.03.04	ד'בגורסקי אלכס	15320	ד'בגורסקי אלכס מהנדס בנין רשיון מס'
עורך בקשה 1 מתכ' האינס הסניט'				
עורך בקשה 2				

הצהרת מתכנן שלד הבניין:
אני החתום מטה (שם משפחה ושם פרטי) ד'בגורסקי אלכס מס' זהות 14687859 מהנדס רשוי מס' 15320 /הנדסאי בעל רישיון מס' ____ ("למבנה פשוט") מצהיר בזאת כדלקמן:
1) אני מסכים להיות מתכנן שלד הנדון בבקשה ולפקח פיקוח עליון על הקמת השלד.
2) אני מתחייב להגיש לפני מתן ההיתר, נושא הבקשה את החישובים הסטטיים בדבר ש בעבורה ההיתר.
3) ידוע לי, שאם אחרי הגשת הנתונים הסטטיים יתגלה צורך בשינוי מהותי בהם, אני מתחייב להגיש חישובים סטטיים מתוקנים מיד עם גילוי הצורך בכך.
4) אני מצהיר, כי יש לי כישורים מקצועיים לערוך בקשה זו וכי בדקתי את כל המסמכים הנוגעים לבקשה, לרבות כל תכנית הנוגעת לבקשה, וידוע לי כי אם הצהרה זו אינה נכונה, הרי היא תיחשב מסירת ידיעה שהיא כוזבת או מטעה בפרט חשוב, כמשמעותה בסעיף 214 לחוק וצפויים לי העונשים הקבועים לפי כל דין.
5) ידוע לי כי עלי לשמור את תכניות הקונסטרוקציה לתקופה של לא פחות מ-10 שנים לאחר גמר הבנייה.
תאריך 16.03.04 חתימה ____

הצהרת האחראי לביצוע שלד הבניין (כאשר מונה):
אני החתום מטה (שם משפחה ושם פרטי) ____ מס' זהות ____ מהנדס רשוי מס' ____ /הנדסאי בעל רישיון מס' ____ ("למבנה פשוט") מצהיר בזאת כדלקמן:
1) אני מסכים להיות האחראי לביצוע שלד הבניין
2) אני מצהיר, כי יש לי כישורים מקצועיים להיות אחראי לביצוע שלד ____, ואני מתחייב לדאוג לביצוע שלד ____ על פי תוכניות והוראות של מתכנן השלד כפי ____ בכתב וכן למלא את תפקידי על פי שנקבע בכל חיקוק הנוגע להן.
תאריך ____ חתימה ____

הצהרת אחראים לביקורת (כאשר מונו):
אנו החתומים מטה מצהירים בזה:
1) כל אחד מאיתנו מאשר שהאמור בנוגע לו ברשימה שבסעיף י"ב לעיל הוא נכון.
2) כל אחד מאיתנו מסכים לקבל עליו את התפקיד המיועד לו בסעיף י"ב.
3) אנו מצהירים כל אחד בנוגע לתחום פעולתו, שיש לנו כישורים מקצועיים לערוך את הביקורת כהלכה ולדווח על תוצאותיה לרשות הרישוי המקומית כמתחייב על פי כל דין.
אני ____ (עורך הביקורת הראשי) אחראי/ת לכך שהביקורת תיערך על פי מיטב הידיעה המקצועית, ושכל הדיווחים לרשות הרישוי המקומית ייערכו על פי כל דין.

תאריך	שם משפחה ושם פרטי	מספר רישיון	חתימה

נבדק ע"י: רשות הרישוי
תאריך 31.05.04
שם ____ חתימה ____

אישור נמסר

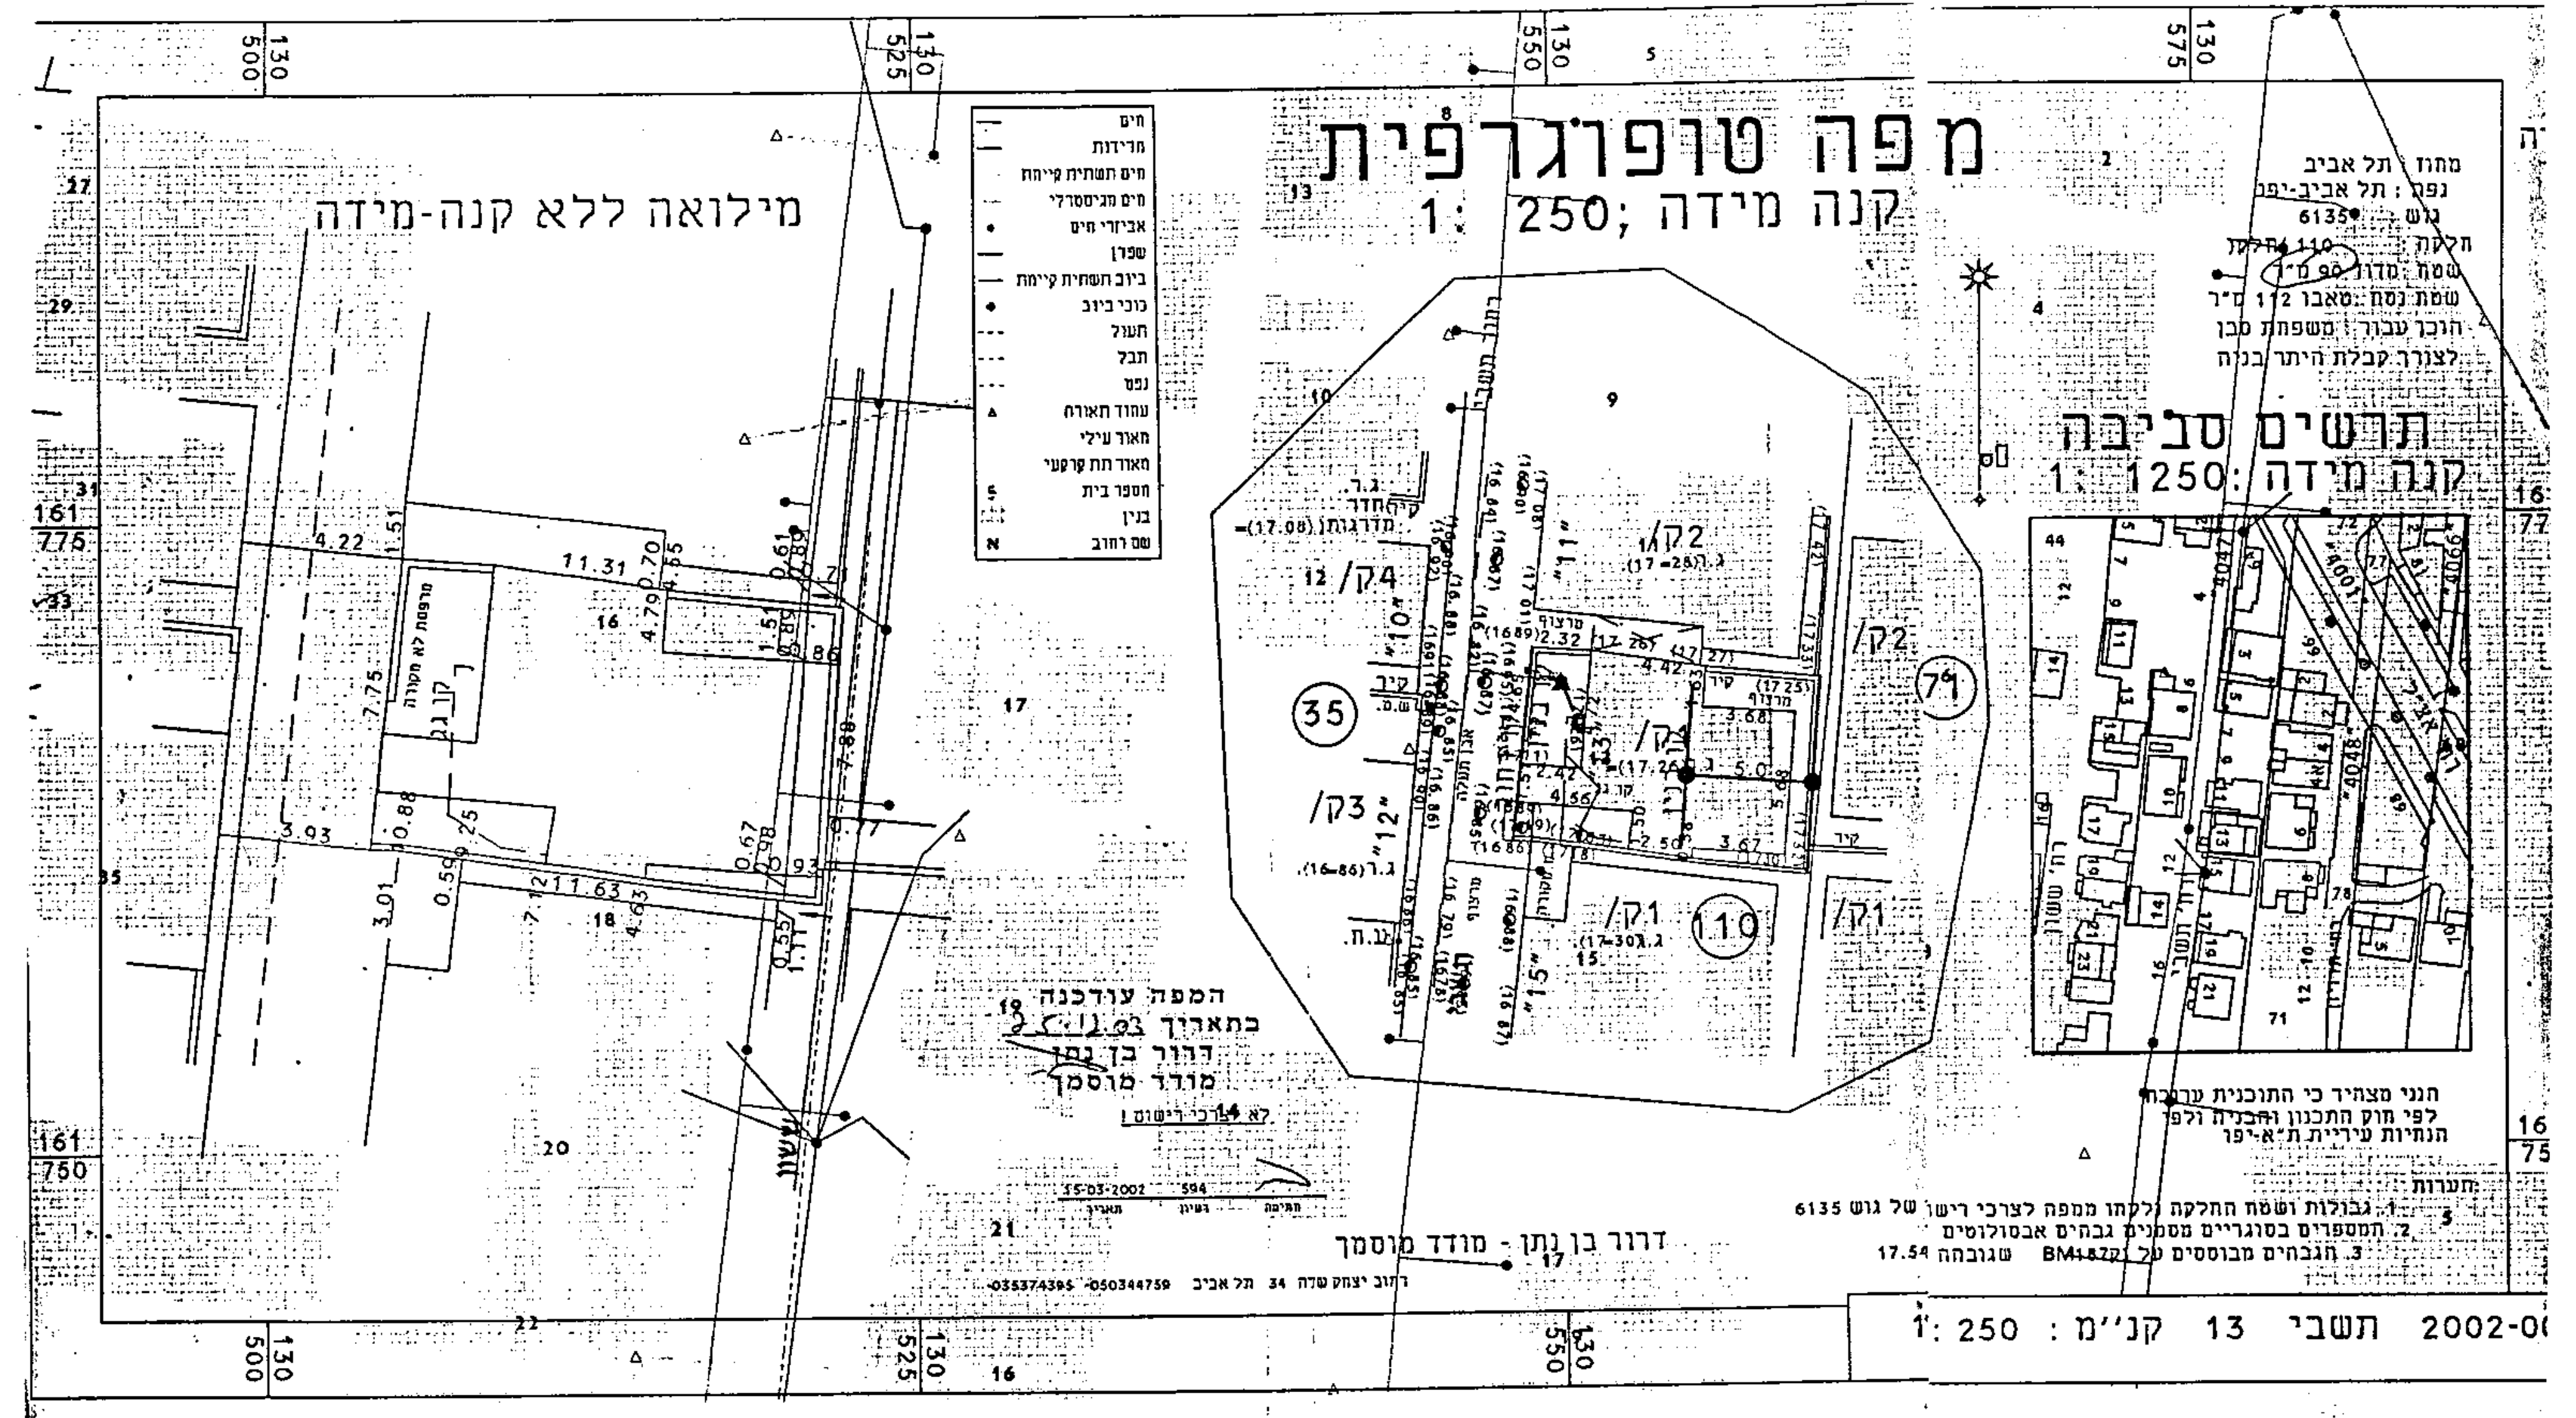
מפה טופוגרפית
קנה מידה 1:250
מילואה ללא קנה-מידה
תרשים סביבה
קנה מידה 1:1250
מחוז: תל אביב
נפה: תל אביב-יפו
גוש: 6135
חלקה: 110
שטח מדוד: 90 מ"ר
שטח נסח: טאבו 112 מ"ר
הוכן עבור: משפחת סבן
לצורך קבלת היתר בניה
המפה עודכנה בתאריך
דרור בן נתן
מודד מוסמך
הנני מצהיר כי התוכנית ערוכה לפי חוק התכנון והבניה ולפי הנחיות עיריית ת"א-יפו
הערות:
1. גבולות ושטח החלקה נלקחו ממפה לצרכי רישום של גוש 6135
2. המספרים בסוגריים מסמנים גבהים אבסולוטיים
3. הגבהים מבוססים על BM4827 שגובהה 17.54
דרור בן נתן - מודד מוסמך
רחוב יצחק שדה 34 תל אביב 035374395 050344759
תשבי 13 קנ"מ: 250 :1 2002-0
רח' תשבי
35
71
110
7/1
12

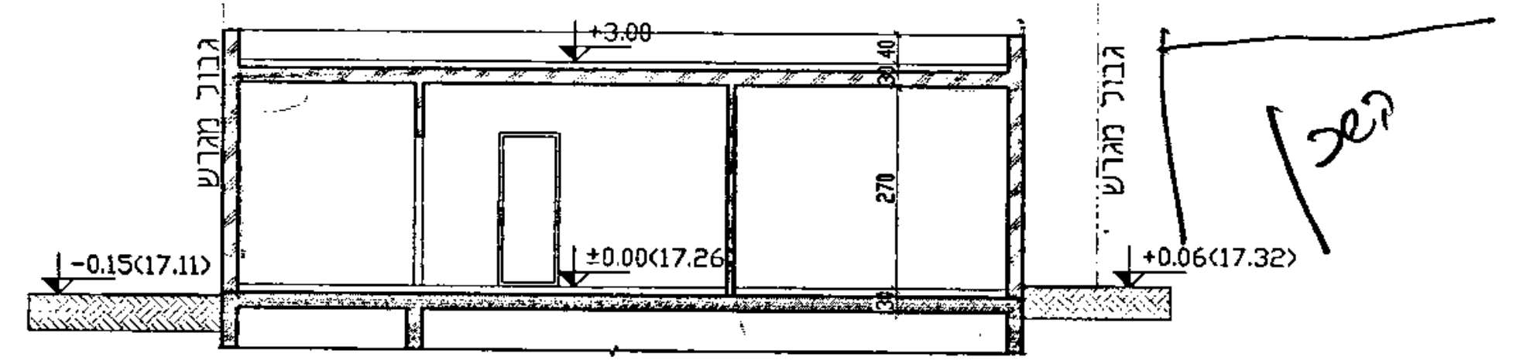
חתך א-א
ק.מ. 1:100

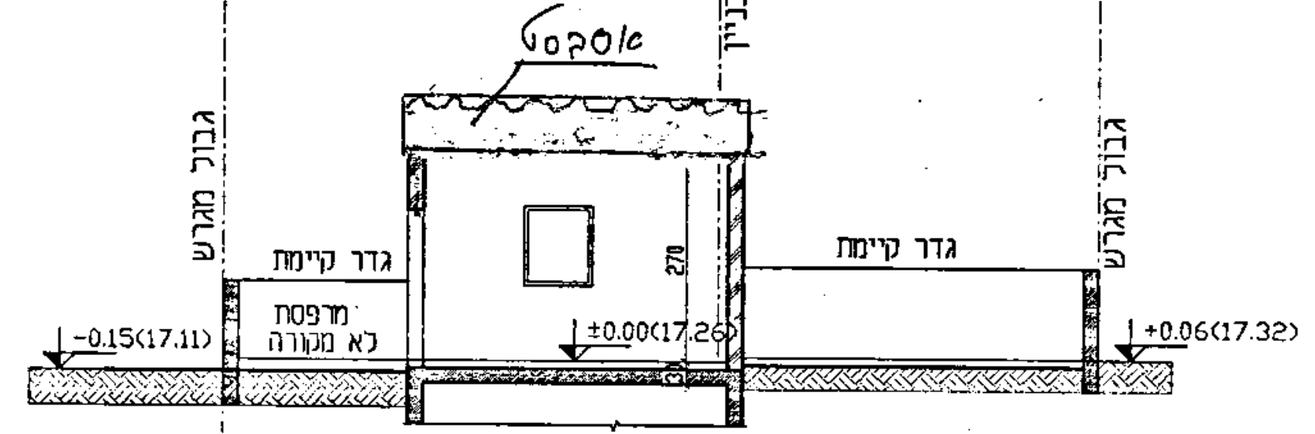
חתך ב-ב
ק.מ. 1:100

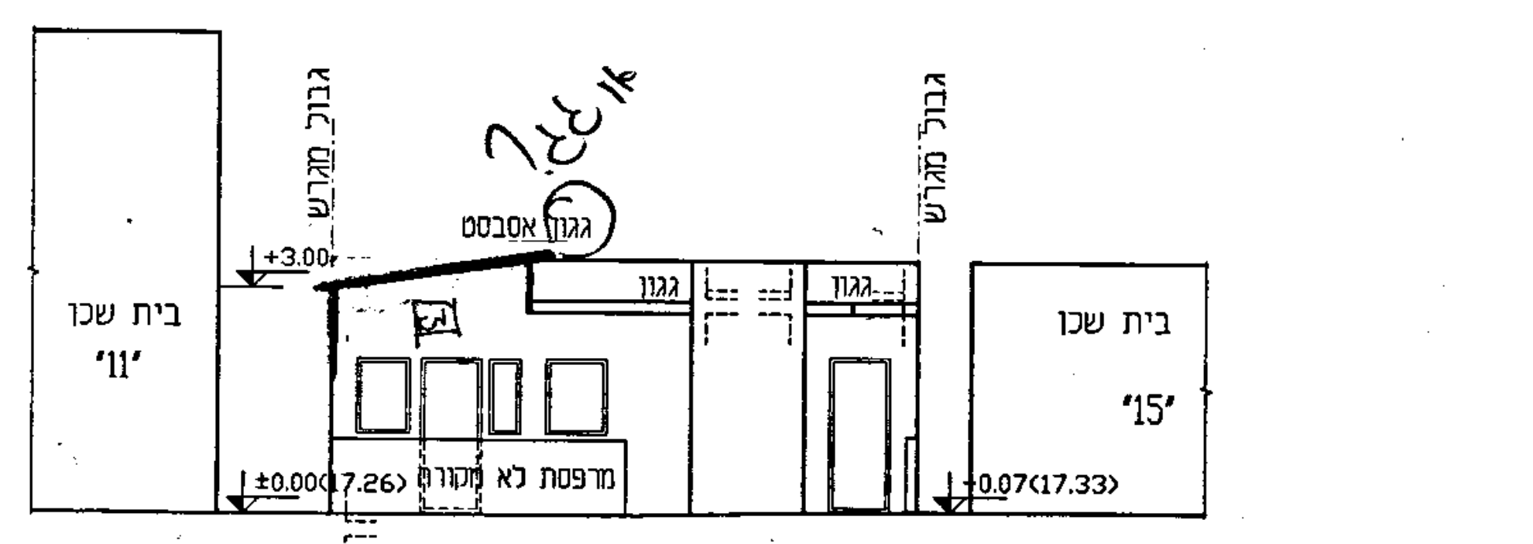
חזית מערבית
ק.מ. 1:100

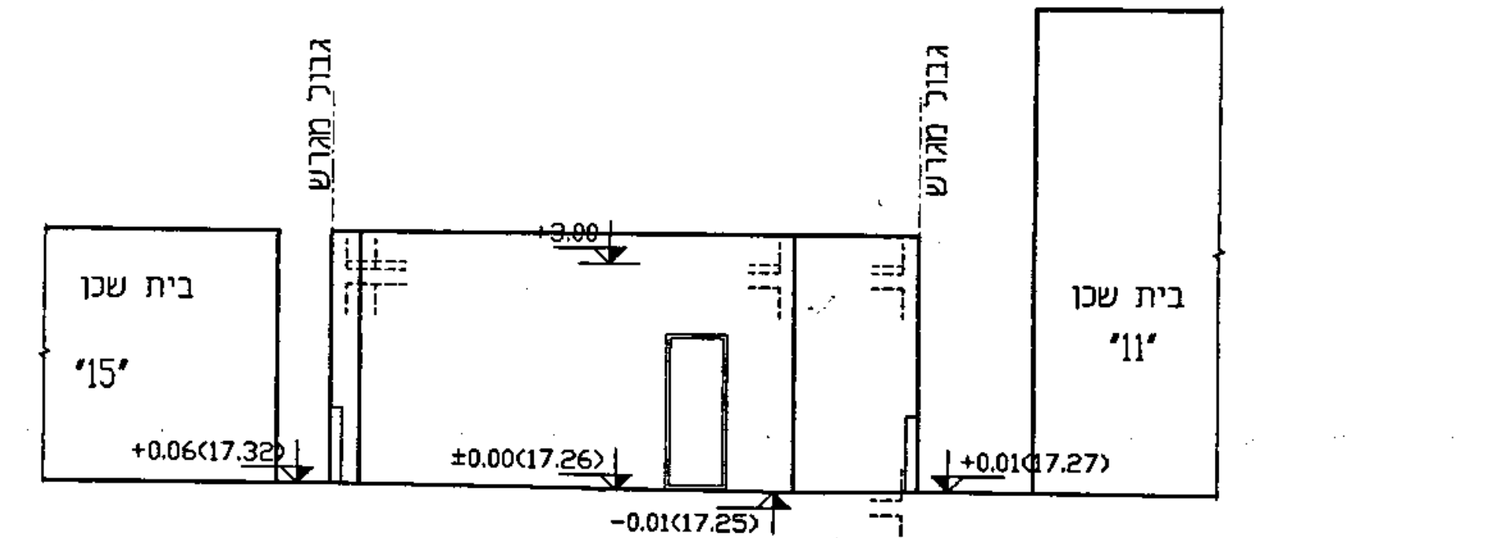
חזית מזרחית
ק.מ. 1:100

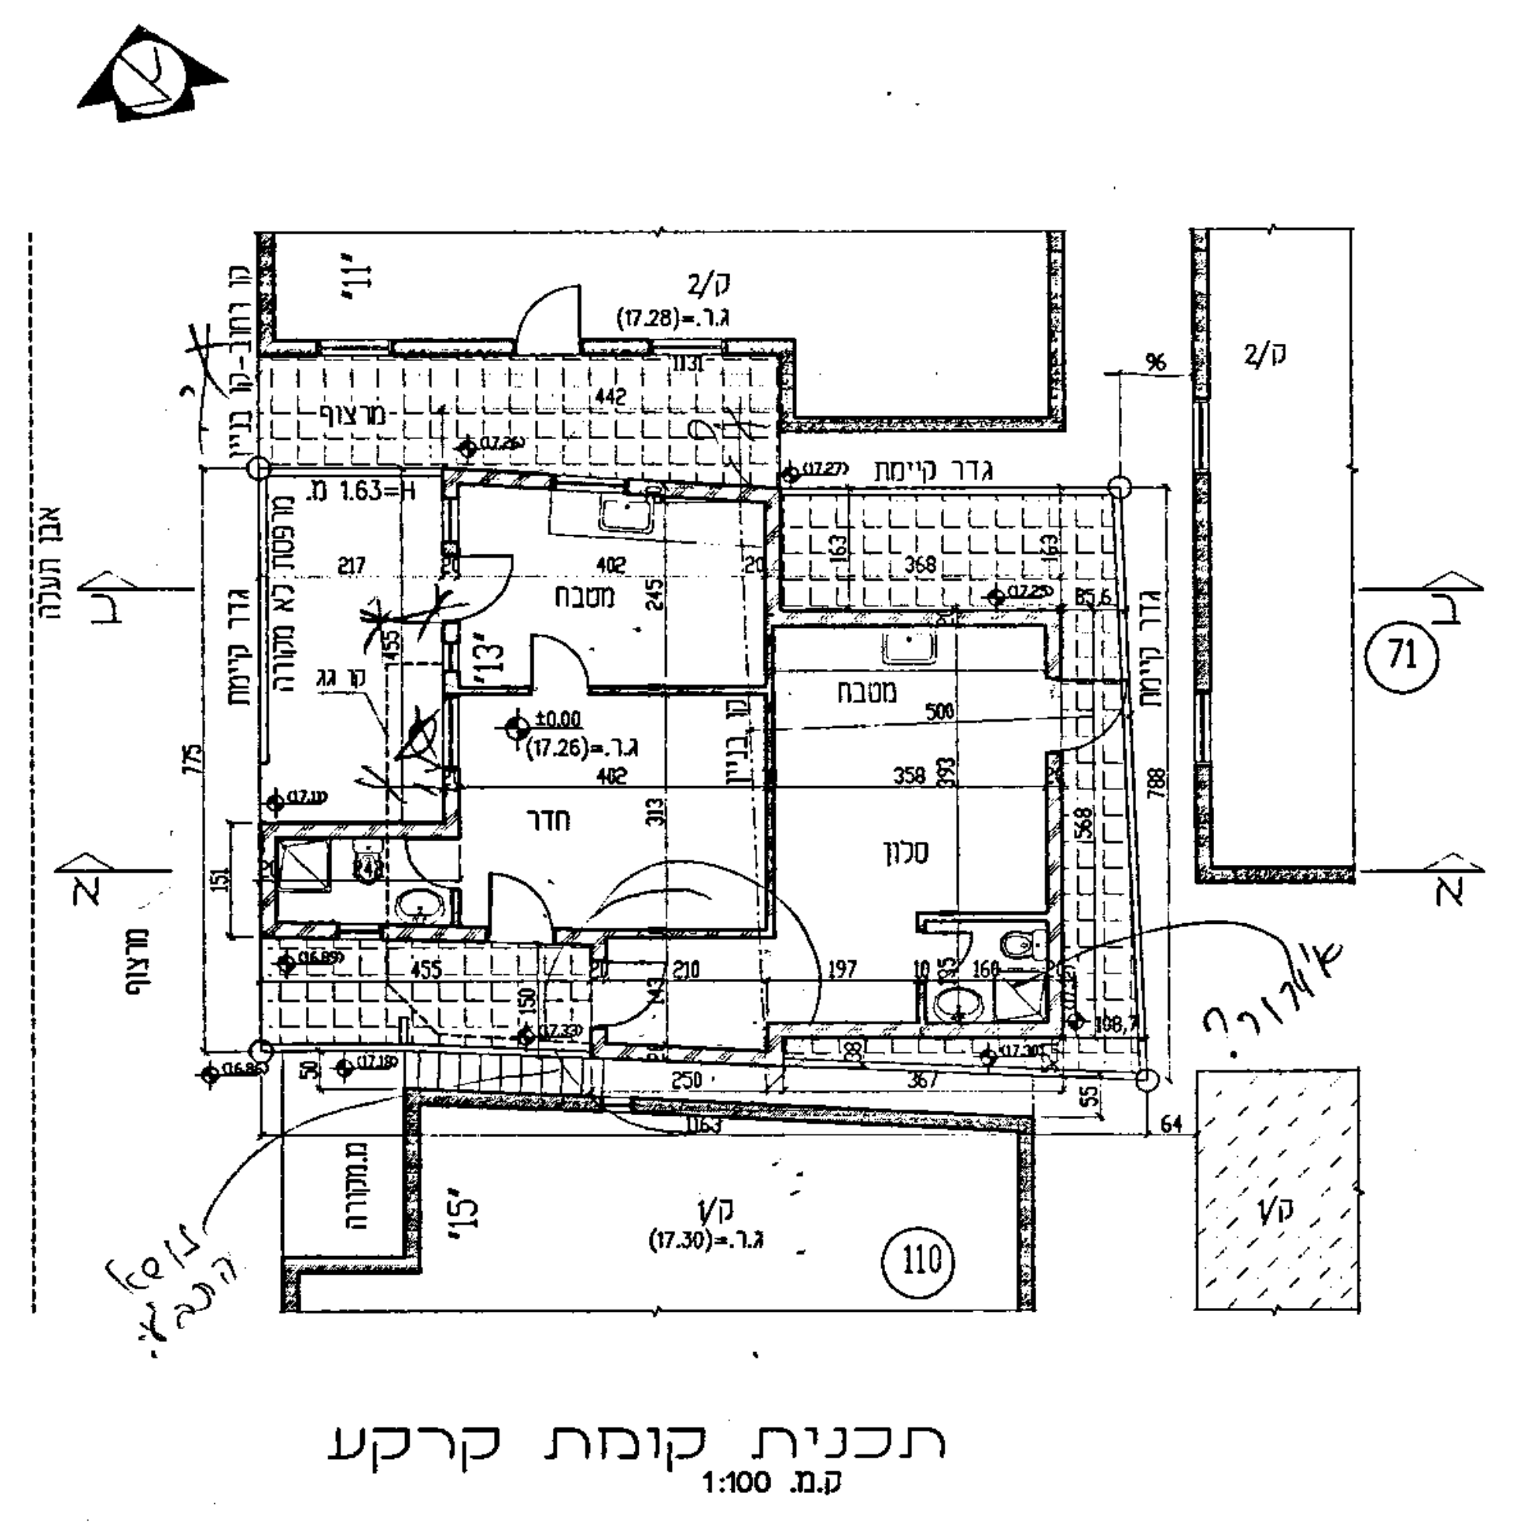
תכנית קומת קרקע
ק.מ. 1:100

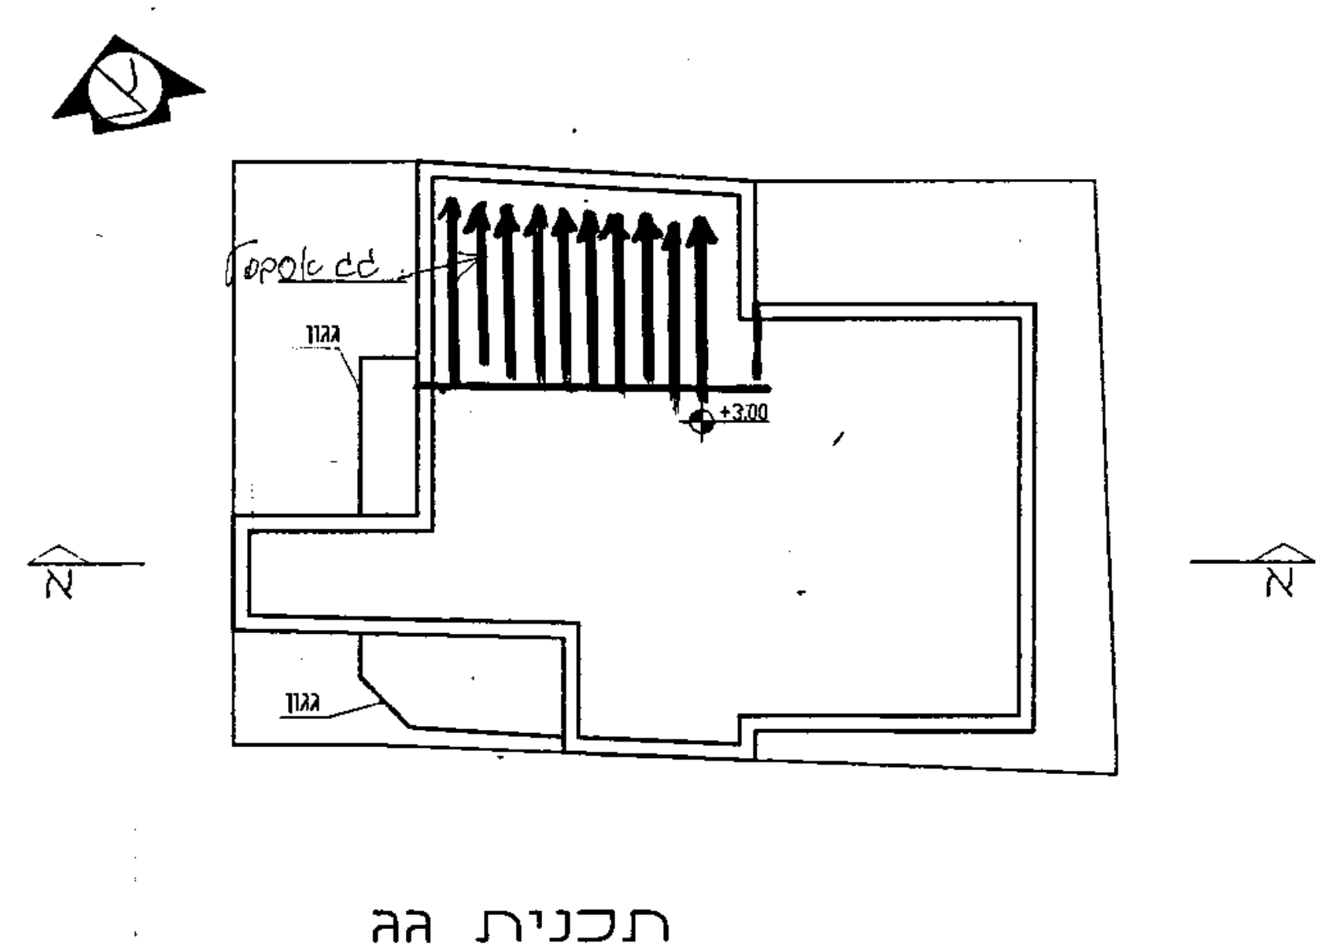
תכנית גג
ק.מ. 1:100

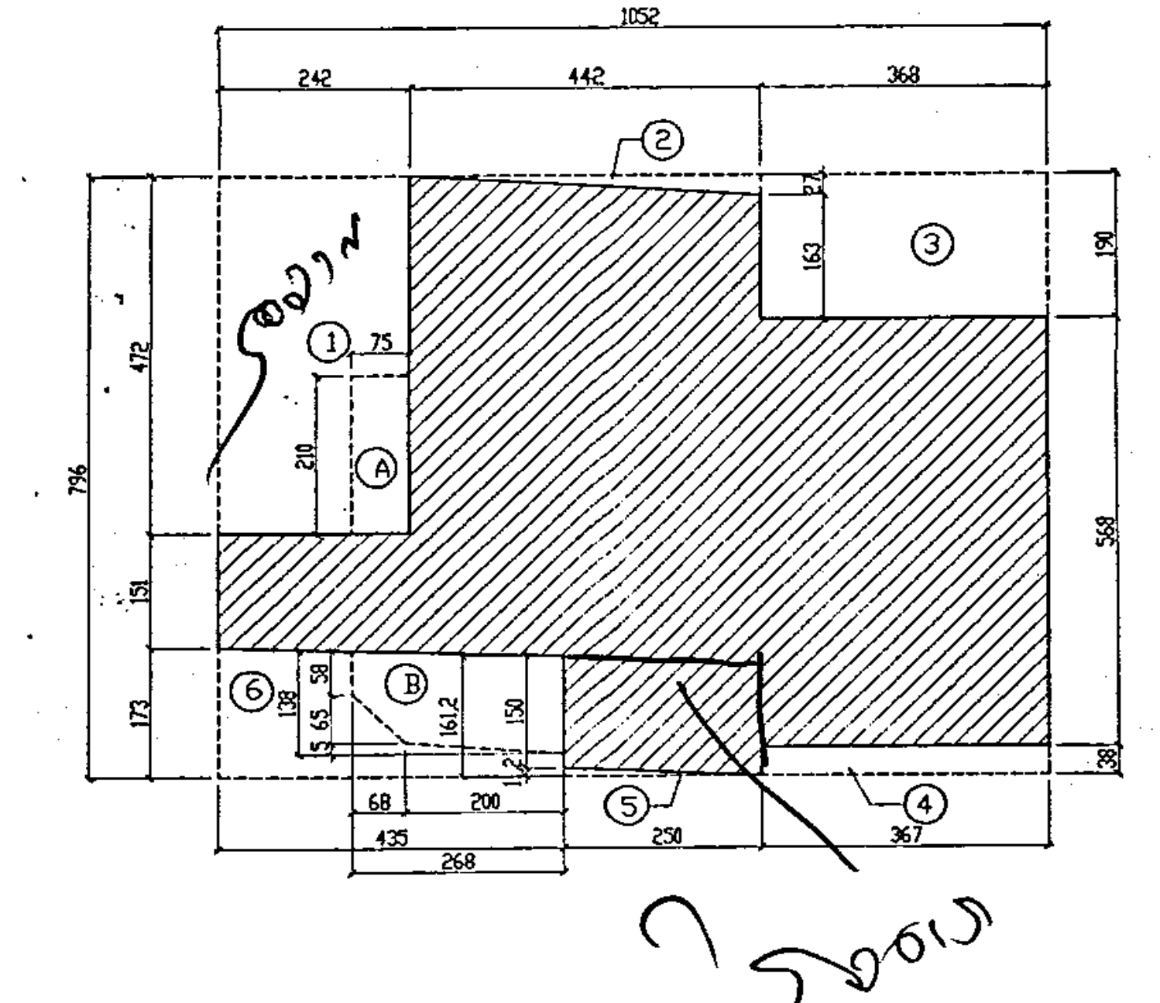
חישוב שטחים
ק.מ. 1:100

שטח קיים:
המסגרת: 83.74=7.96*10.52 מ"ר
קונטור:
2) 0.60=0.27*4.42/2 מ"ר
3) 7.00=1.90*3.68 מ"ר
4) 1.40=0.38*3.67 מ"ר
5) 0.14=2.50*0.11/2 מ"ר
6) 7.26=(1.61+1.73)*4.35*/2 מ"ר
סה"כ: 27.82 מ"ר
שטח דירה: 55.92 מ"ר
שטח גגון:
A) 1.57=2.10*0.75 מ"ר
B) 3.70=1.38*2.68 מ"ר
פחות: 0.22=0.65*0.68/2 מ"ר
פחות: 0.15=2.00*0.15/2 מ"ר
סה"כ: 4.90 מ"ר
חישוב תכסית: