



איכות נמוכה

מחוז : תל-אביב
 מפה : תל-אביב - יפו
 מקום : תל-אביב (שכונת התקווה)
 גוש : 6135
 חלקה : 43 (חלק)
 כתובת : רח' תשבי 16
 מתרת המדידה : הגדרת מגרש משני עפ"י תב"ע 2215

שם הבעלים כרשום בנסח הטאבו : חלימש חברה ממשלתית לייצור לשיקום הדיור ת"א יפו בע"מ
 חברה 520023920
 שטח לפי נסח : שטח חלקה כולה (מ"ר) : 3575.00
 בעלות בחלקים (כרשום בנסח טבאו) : 1. מחלק בנסח 715/35750
 2. החלק בנסח 715/35750

בעלות במ"ר : 715
 שטח ברוטו (מ"ר) : 120.961
 שטח מגרש משני :
 שטח לגרענה :



מקרא :
 גבולות גושים חלקות
 גבול מגרש
 שטח מגרש / תת מגרש שבוצע לגביו סקר עפ"י נתוני חברת חלימש

- הערות
1. המטרה לשמור הוכנה המפה : היתר בניה.
 2. שיטת המדידה : דיסטומט GPS+.
 3. המדידה קשורה לרשת קואורדינטות ארצית באמצעות נקודות טריאנגולציה TELA : 1688W.
 4. הגבהים במפה מתבססים על נקודת קבע ממשלתית שמספרה 1688W וגובהה 24.29.
 5. גבולות ושטח המגרש נלקחו מתכנית לצרכי רישום שלי.
 6. שטח סופי של המגרש יקבע לאחר רישום תצ"ר.

מפה טופוגרפית

קנה מידה 1 : 250

תרשים סביבה 1 : 1250

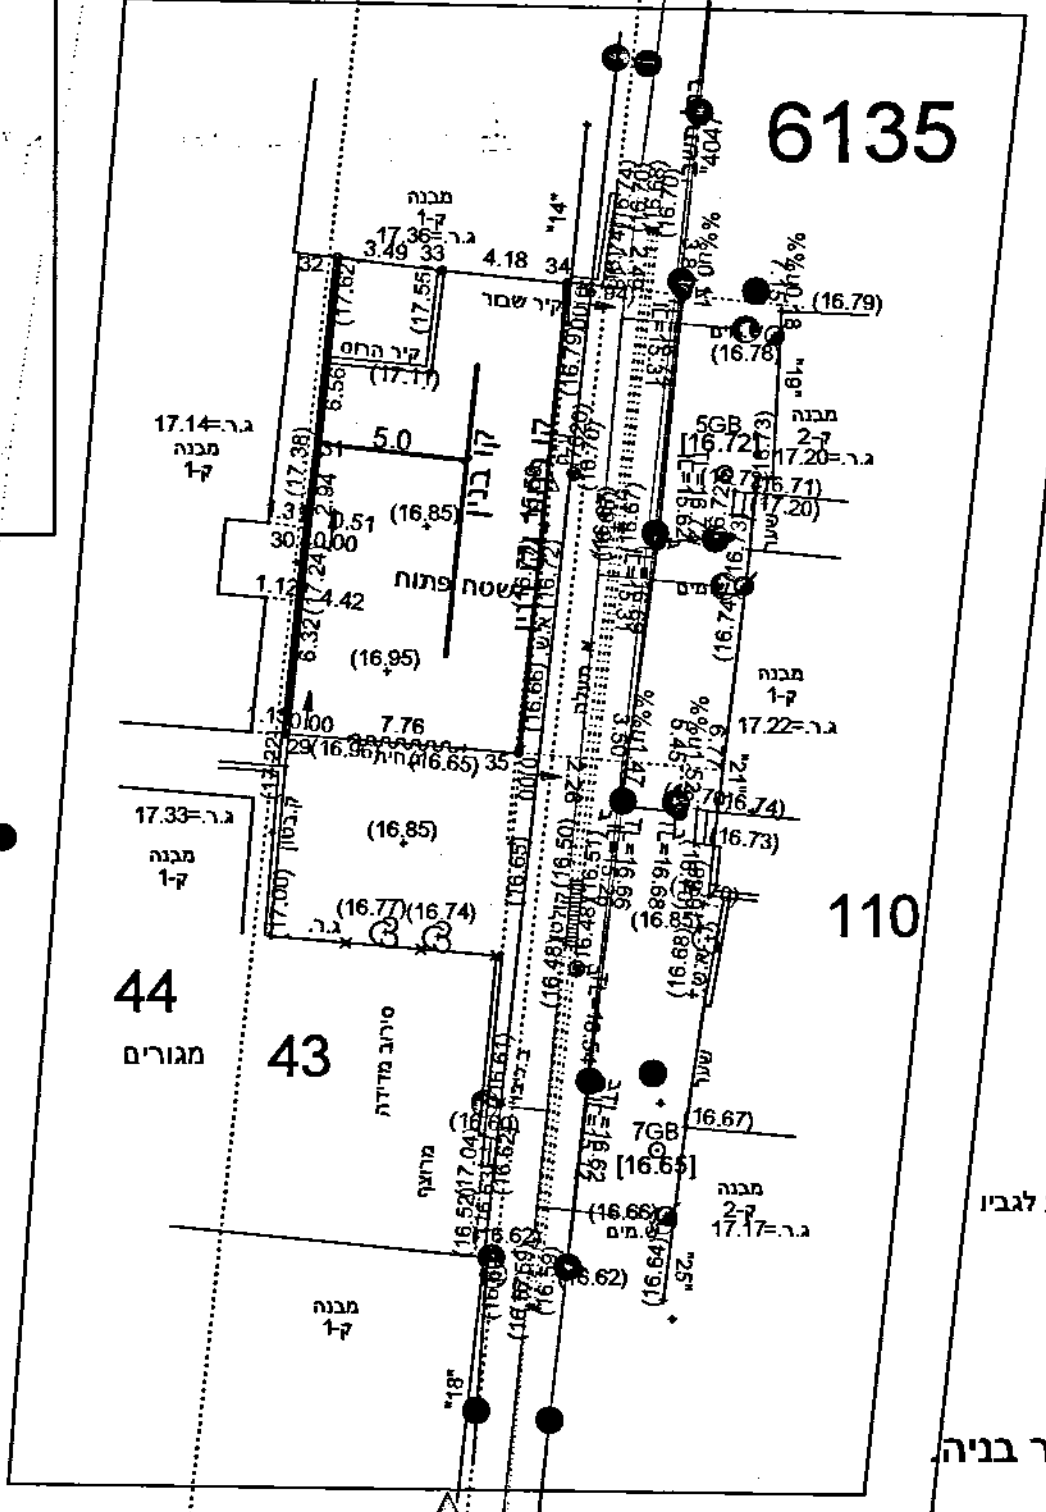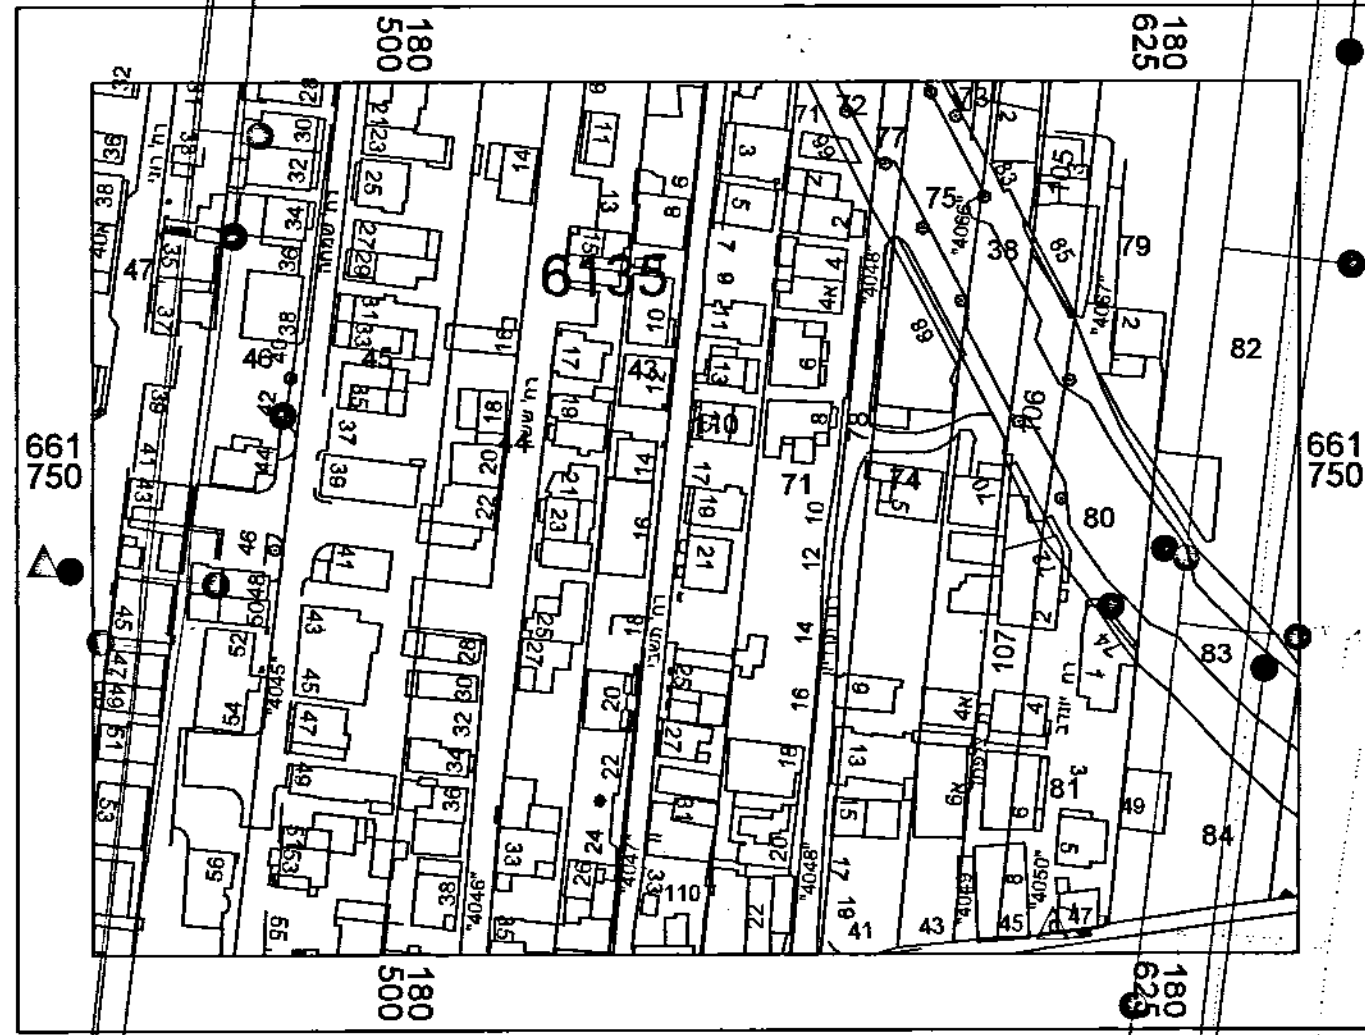

רשימת קואורדינטות

נק. בגבול החלקה	Y	X
661731.89	29	180532.37
661738.18	30	180533.02
661741.10	31	180533.40
661747.62	32	180534.08
661747.19	33	180537.54
661746.77	34	180541.69
661731.26	35	180540.11

- מקרא
- קווי בניין
 - קווי בניין
 - מים תשתית קיימת
 - אביזרי מים
 - כוכי ביו
 - ביו
 - תעול
 - עמוד תאורה
 - מאור עילי
 - מאור עילי
 - שם רחוב

לא לצרכי רישום

הנני מצהיר בזה שהמפה נעשתה לפי חוק התכנון והבניה התקנות וההנחיות של עיריית תל אביב - יפו

תאריך : 26/11/07

גטניו ברני
 שם המודד

570
 מס' רישיון

חתימה

גטניו ושות' מוודדים מוסמכים בע"מ

רח' היצירה 14, רמת-ג 52521 טל 03-5759681 פקס 03-7516356

עיריית תל-אביב יפו - מנהל הנדסה ופיקוח המדידות

אישור כתובת

רחוב מס'

רחוב מס'

רחוב מס'

תאריך חתימה