1

תכנית מאושרת ע' צוות מרכז וחתומה ע' יד השכן

חוק התכנון והבניה, התשכ"ה-1965

תקנות התכנון והבניה (בקשה להיתר, תנאיו ואגרות), התש"ל-1970

איכות נמוכה

הוועדה המקומית לתכנון ולבניה

טופס 2 (תקנה 2(א))

תיק מס 4047-020

מיפרט 014

א. תיאור הבנין

1. המקום	הרחוב	מס'	גוש	חלקה	תכנית מיתאר מקומית או מפורטת	מגרש	
שכ' התקוה	תשבי	20	6135	43	2215	1	

	השם	המען	מס' הטלפון
2. המבקש	שרה ויהודה חזן	תשבי 20 שכ' התקוה	377260
3. בעל הזכות בנכס	-״- -״-	-״- -״-	-״-
4. עורך הבקשה *	פרחי יוסי-אדריכל	אדם הכהן 16 ת"א מיקוד 64585	5243524
5. האחראי לביצוע השלד	לורך יצחק-מהנדס	בלוך 40 ת"א מיקוד 64681	235996

6. אזור הבניה: ● מגורים ☐ מסחר ☐ תעשיה ☐ בנין ציבורי ☐ חקלאי ☐ ....

7. שטח: המגרש/החלקה 138 מ"ר. אחוז הבניה המותר: % 140

8. מטרת הבנין: ● מגורים ☐ הארחה ☐ עסקים ☐ תעשיה ☐ חקלאי ☐ ציבורי ☐ ....

9. מהות הבנין ותכליתו: תוספת קומה לדירה קיימת

10. תיאור העבודה המוצעת: ☐ בנין חדש ● תוספת לבנין קיים ☐ הריסה ☐ תיקונים ☐ שינוי בבנין ☐ .... ☐ שינוי בשימוש ממטרה: .... למטרה: ....

11. האם הבניה היא בעד: ☐ משרד ממשלתי ☐ הרשות המקומית ☐ הסוכנות היהודית

ב. היקף הבניה

קומה	קיים	מוצע	סך הכל	אחוז הבניה	עד 45 מ"ר	עד 65 מ"ר	עד 90 מ"ר	עד 100 מ"ר	מעל 100 מ"ר	עסק; הארחה; וכו'	ציבורי	שונות	מס' חדרים קיים	מס' חדרים מוצע
1	2	3	4	5	6	7	8	9	10	11	12	13	14	15
מרתף														
קרקע	58.05	—	58.05	42.06										
א	—	48.54	48.54	35.17										
ב														
ג														
ד														
ה														
ו														
ז														
הכניסה הקובעת לבנין														
חדרי מדרגות														
בניני עזר														
סך הכל	58.05	48.54	106.59	77.23										

הנפח המוצע: של הבנין העיקרי .... מ"ק. של בנין עזר .... מ"ק.

נים לאשר את התכניות [illegible] 5.12 [illegible] 24-10-91

[illegible] השכן [illegible] 10-12-[illegible]

ג. השימוש בבנין

1. הבניה המוצעת למגורים

דירות בנות:	שטח כל דירה מ"ר	מספר דירות מכל סוג	כל הדירות	רצפות חדרי דיור בלבד, ומרפסות מקורות	רצפות חדרי שירות ופרוזדורים בלבד	רצפות של מרפסות בלתי מקורות	דיור	מטבחים	אמבטיות	בתי שימוש	אחרים
1	2	3	4	5	6	7	8	9	10	11	12
חדר אחד											
2 חדרים											
3 חדרים											
4 חדרים		1	1				4	1	1	2	
5 חדרים											
6 חדרים											
7 חדרים ויותר											
חדרים נוספים לדירות קיימות											
בניני עזר											
סך הכל		1	1				4	1	1	2	

יש לציין את השטחים לפי מספר החדרים ושטח הבניה בכל דירה בכל קומה.

עיריית תל אביב יפו
מינהל ההנדסה
10-03-1992
נתקבל במחי תעוד ובקרת
רישום 92-416 תיק

2

2. הבניה הקיימת והמוצעת לתעשיה ולמלאכה

פרטים	קיים שטח	קיים גובה	קיים נפח	קיים % הבניה	מוצע שטח	מוצע גובה	מוצע נפח	מוצע % הבניה	סך הכל שטח	סך הכל נפח	סך הכל % הבניה	הערות
1	2	3	4	5	6	7	8	9	10	11	12	13
אולמי מלאכה												
משרדים												
חדרי שירות												
סככות												
בניני עזר												
חדרי מדרגות												
סך הכל												

3. הבניה המוצעת למטרות אחרות (הארחה, עסקים ומשרדים, בניני ציבור, בניני משק חקלאי, מטרות שונות).

השימוש המיועד	סך הכל מ"ר	מזה שרים	מזה אולמות	מזה אחסנה	מזה חדרי שירות	חדרים	אולמות	אחסנה	חדרי שירות
1	2	3	4	5	6	7	8	9	10
בניני עזר (למעט אלה המפורטים ב־(4))									

4. חלקי בנין אחרים - הבניה המוצעת, שטח במ"ר.

חדרי מדרגות	מרפסות שלא נכללו לעיל	מעליות	חדרי הסקה	חדרי כביסה	מקלטים	קומת עמודים מפולשת	מחסנים	מוסכים	בניני עזר נוספים	סך הכל
1	2	3	4	5	6	7	8	9	10	11
	5.72									

ד. חומר הבניה

קירות חיצוניים	☐ בטון מזוין	■ לבני בטון או בלוקים	☐ לבני סיליקט	☐ לבנים שרופות	☐ אבן טבעית
	☐ אבן מלאכותית	☐ איטונג	☐ עץ	☐ ברזל	☐ חמרים אחרים
תקרות	■ בטון מזוין	☐ עץ	☐ חומר אחר		
גג	■ בטון מזוין	☐ רעפים	☐ אסבסט	☐ פח	☐ חומר אחר ....

ה. גדרות קיימות .... מ"א מוצעות 39.4 מ"א

ו. מקרא

☐ בטון או בטון מזוין ☐ אבן ☐ עץ ☐ איטונג

☐ בלוקים או לבנים מבטון ☐ סיליקט או לבנים אדומות ☐ חומר אחר ☐ להריסה

הערות:

הנני מאשר כי הנתונים הנ"ל נכונים

תאריך 30.7.91 חתימת המבקש יהודה חזן חתימת עורך הבקשה *

חתימת האחראי לביצוע השלד חתימת בעל הזכות בנכס יהודה חזן שרה

לשימוש הוועדה המקומית בלבד	מס' ההיתר	תאריך ההיתר	תאריך התחלת הבניה	תאריך גמר הבניה

אישורים של רשויות חוץ: חתימת השכן: טגליה משה

חותמת הוועדה המקומית

* היו מספר עורכי בקשה, כאמור בתקנה 2ב(ה), יבוא במקום כל אלה הראשון שברשימת עורכי הבקשה, כאמור בטופס 1.

עיריית תל אביב - יפו
מינהל ההנדסה

הועדה המקומית לתכנון ובניה - ת"א-יפו

בקשה להיתר בניה

לשימוש משרדי	
מס' תיק בקשה	
מס' תיק בנין	
מס' תיק מידע	
מס' בקשה קודמת *	

עורך בקשה נכבד

- הנך מתבקש לקרוא בתשומת לב את הטופס ולמלא את הפרטים הנדרשים בכתב ברור.
- את הטופס המלא יש להגיש בצמוד לטופס (טופס 2).
- טופס מלא, יחד עם תיק צהוב ותיק מידע מאושר, הם בסיס להליכי הרישוי עד למתן ההיתר.

חלק א' - תאור הבקשה (לשימוש עורך הבקשה)

1. סיווג הבקשה (סמן בעיגול את הסוג המתאים)

א. בניה חדשה - מספר קומות מלאות ☐ מס' קומות חלקיות ☐ קומה מפולשת כן / לא

ב. תוספת עד 10 מ"ר - במסגרת הרחבת דיור שכונתית כן / לא מס' יחידות דיור מורחבות ☐
האם הבניה באגף שלם כן / לא

ג. תוספת מעל 10 מ"ר - במסגרת הרחבת דיור שכונתית [✓ כן] לא מס' יחידות דיור מורחבות 1
האם הבניה באגף שלם [✓ כן] לא

ד. הריסה, פרט ....

ה. שיפוצים, פרט שיפוץ קומת הקרקע הקיימת

ו. שינויים בזמן בניה - בהמשך להיתר מס' ☐ מתאריך ☐

ז. בניה על הגג, פרט ח' מדרגות ליציאה לגג

ח. שימוש חורג - משימוש: .... לשימוש: .... בק מה ☐ בשטח ☐ מ"ר

ט. עבודה מצומצמת - תאור העבודה: ....

2. היקף הבניה המוצעת לעומת זכויות מותרות

קומה	קיים בהיתר	קיים ללא היתר	מוצע אישור בניה קיימת	מוצע בניה חדשה	סה"כ	אחוזי בניה עפ"פ הבקשה שטח מחושב **	אחוזי בניה אחוז	מותר לפי תב"ע שטח	מותר לפי תב"ע אחוז	סטיה שטח	סטיה אחוז	סיבת הסטיה/נימוקים
מרתף												
קרקע	58.05			—	58.05		42.06		60			
א	—			48.54	48.54		35.17					
ב												
ג												
ד												
ה												
ו												
ז												
הכניסה הקובעת												
חדרי מדרגות												
בניני עזר												
סה"כ	58.05			48.54	106.59		77.23		140			

** באחוזי בניה

* עבור התלמות שפג תוקפן או בקשות להארכת תוקף היתר

3

3. מהות הבקשה - תאור מילולי (ראה הנחיות למילוי בטופס מצ"ב)

שיפוץ קומת הקרקע הקיימת ותוספת קומה מעל לקיים + יציאה לגג בשטח כולל של 106.59 מ"ר

4. קוי בניה

לרחוב/לצד		קוי בניה (ס') מוצע	קוי בניה (ס') מותר	קוי בניה סטיה ס'	קוי בניה סטיה %	רוחב קולונדה (ס') מוצע	רוחב קולונדה מותר	סטיה ס'	סטיה %
עם רחוב	תשבי	0	0						
עם רחוב									
צד									
אחור									

5. מס' יחידות דיור: מוצע 1 מותר ☐

6. מרתף - עליון: גובה ☐ שימוש ....
- תחתון: גובה ☐ שימוש ....

7. מבנה עזר: גובה ☐ מיקום: א. צדדי ב. אחורי ג. קדמי ד. צמוד לבנין ה. במסגרת הבנין

8. קומה מפולשת: גובה ☐ אחוז בניה בקומה מפוסית (%) ☐

9. בניה על הגג:
א. שטח ☐
ב. גובה מבנה (ברוטו) ☐
ג. נסיגה מהמעקה ☐
ד. אחוז בניה משטח הגג ☐
ה. מיקום קולטי שמש: 1. על גג הבנין (2) על גג עליון
ו. קיימת בניה אחרת על הגג (כן) לא. פרט ח' מדרגות ליציאה לגג.

10. קיים חדר מדרגות כללי: כן [✓ לא]

11. נימוקים לבקשה להקלה

12. תאור הקיים על המגרש

קיים מבנה ישן בן קומה אחת (ראה צילומים מצורפים)

13. אם ניתנה בידך האפשרות לבחור בין מסלול רישוי בדרך מקוצרת ומסלול רישוי בדרך רגילה נא מלא את הר"מ.
אני הח"מ מצהיר כי הבקשה להיתר מוגשת במסלול הרישוי המסומן להלן (סמן ב־x):
☒ רשות רישוי - רישוי בדרך מקוצרת - באחריות עורך הבקשה
☐ רשות רישוי - מסלול רגיל

חלק ב' - הצהרת עורך הבקשה

אני, הח"מ כלול בפנקס המהנדסים מצהיר בזאת שהבקשה הוכנה לפי כל דין ותקנה ובהתאם לתיק המידע אשר נמסר לי.
הפרטים, המסמכים, האישורים, ההצהרות וכל הנספחים לבקשה הינם נכונים וחתומי עליהם יראו אותה כחתימה על הצהיר.

תאריך 30.7.91 שם עורך הבקשה יוסי פרחי מס' רשיון 9840 חתימה

חלק ג' (לשימוש משרדי)

1. מועד קבלת בקשה ☐

2. הערות ....

תאריך חתימה .... שם המטפל .... חתימה ....

4

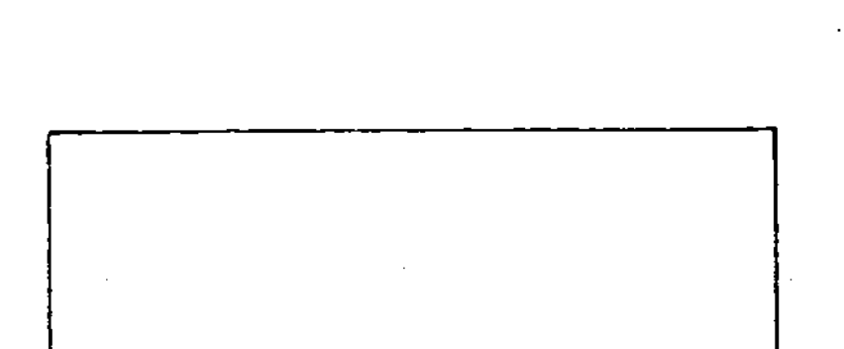

חישובי שטחים

שטח קרקע - קיים

9.60 x 6.60 = 63.36

הורדה:

א 1.80 x 2.95 = 5.31

סה"כ: 58.05 מ"ר

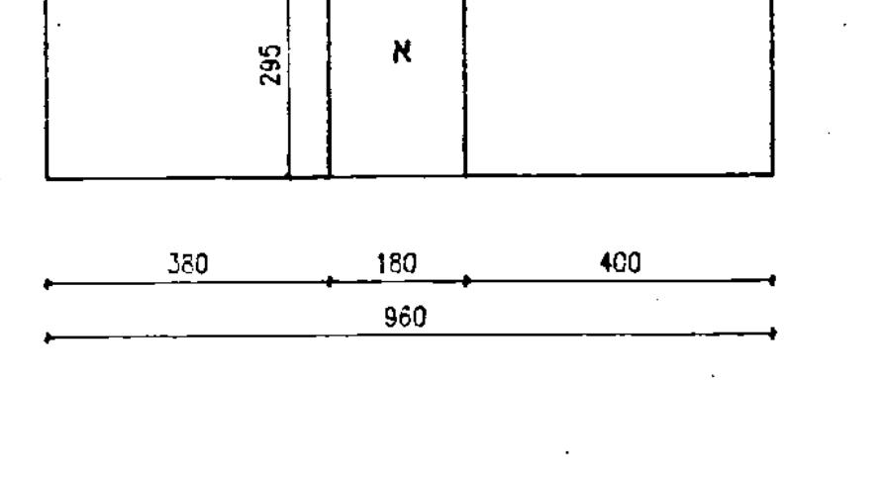

שטח א - תוספת

9.60 x 6.60 = 63.36

הורדה:

ב 3.80 x 2.10 = 7.98

ג 3.26 x 2.10 = 6.84

סה"כ: 48.54

סה"כ שטח קרקע + א:

58.05 + 48.54 = 106.59

תל-אביב-יפו

גוש 6135

חלקה 43 (חלק)

מגרש 1

השטח 0.138 ד.מ. (לפי מדידה בשטח)

0.168 ד.מ. (לפי נסח)

10.5.90

הוכן בשביל: משפי חזן

מהות הבקשה: קבלת היתר בניה

תרשים הסביבה - 1:1250

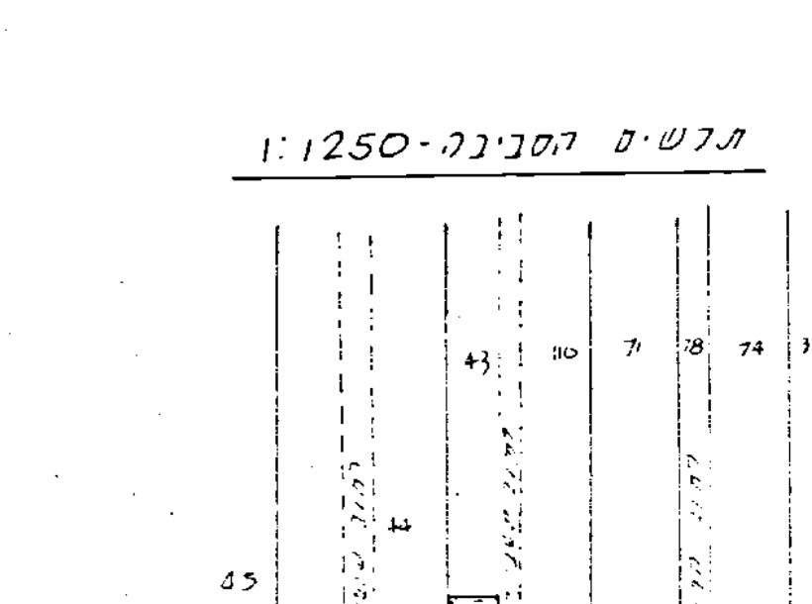

הערות

מפה טופוגרפית

1:250

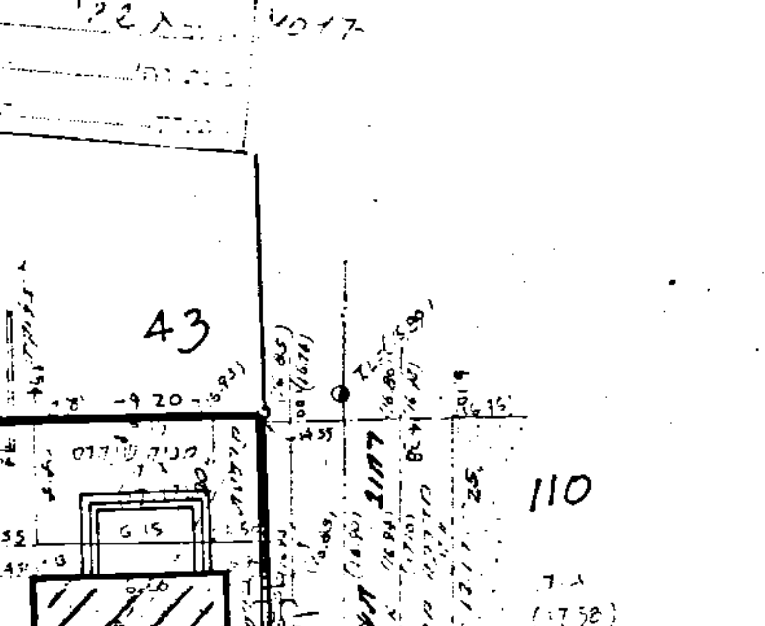

עיריית תל-אביב-יפו
מינהל בנוי ותשתית / אגף עבודות ציבוריות
מחלקת מדידות
חתימה
חתימה
תאריך 16.5.90
שטח הפקעה (לצורך חשוב זכויות ב.ה.)
ואושר (ת.ב.ע.) מ"מ

למא לצד

תל-אביב 18.2.1990

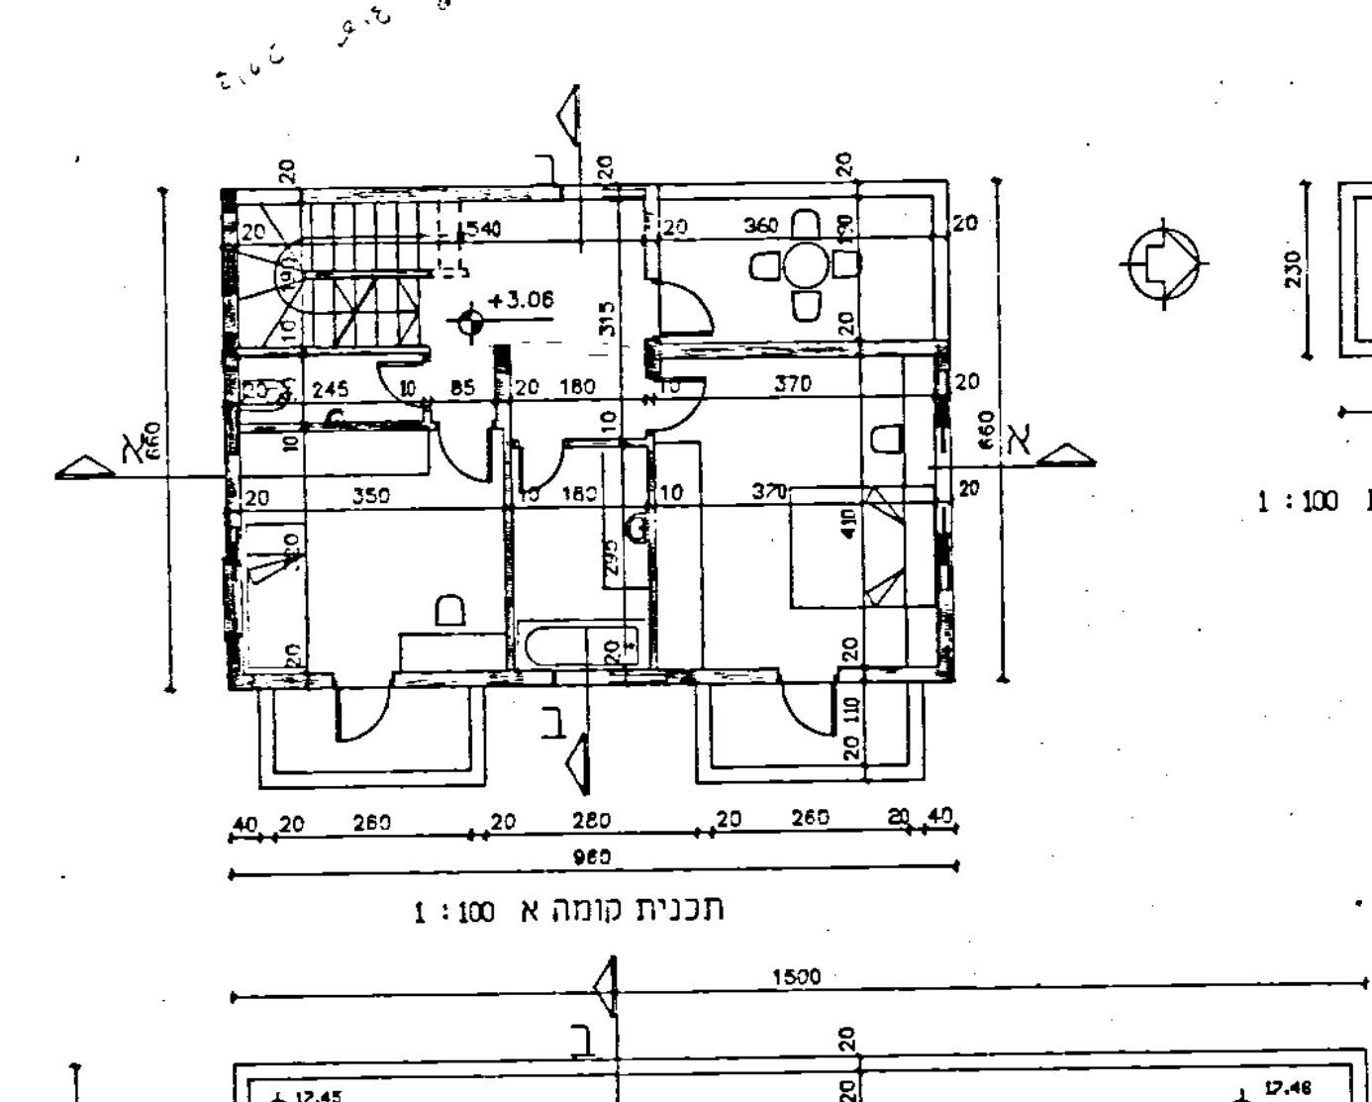

תכנית קומה א 1:100

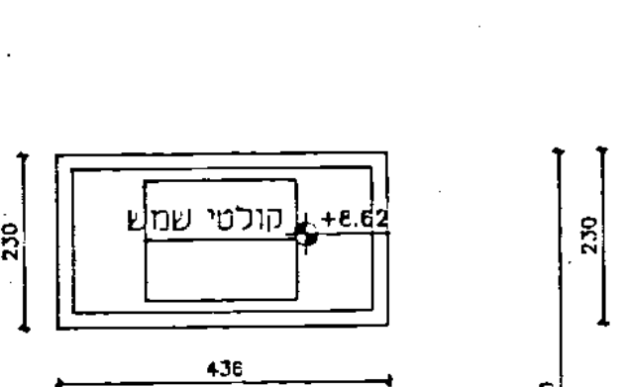

תכנית גג ת. מדרגות 1:100

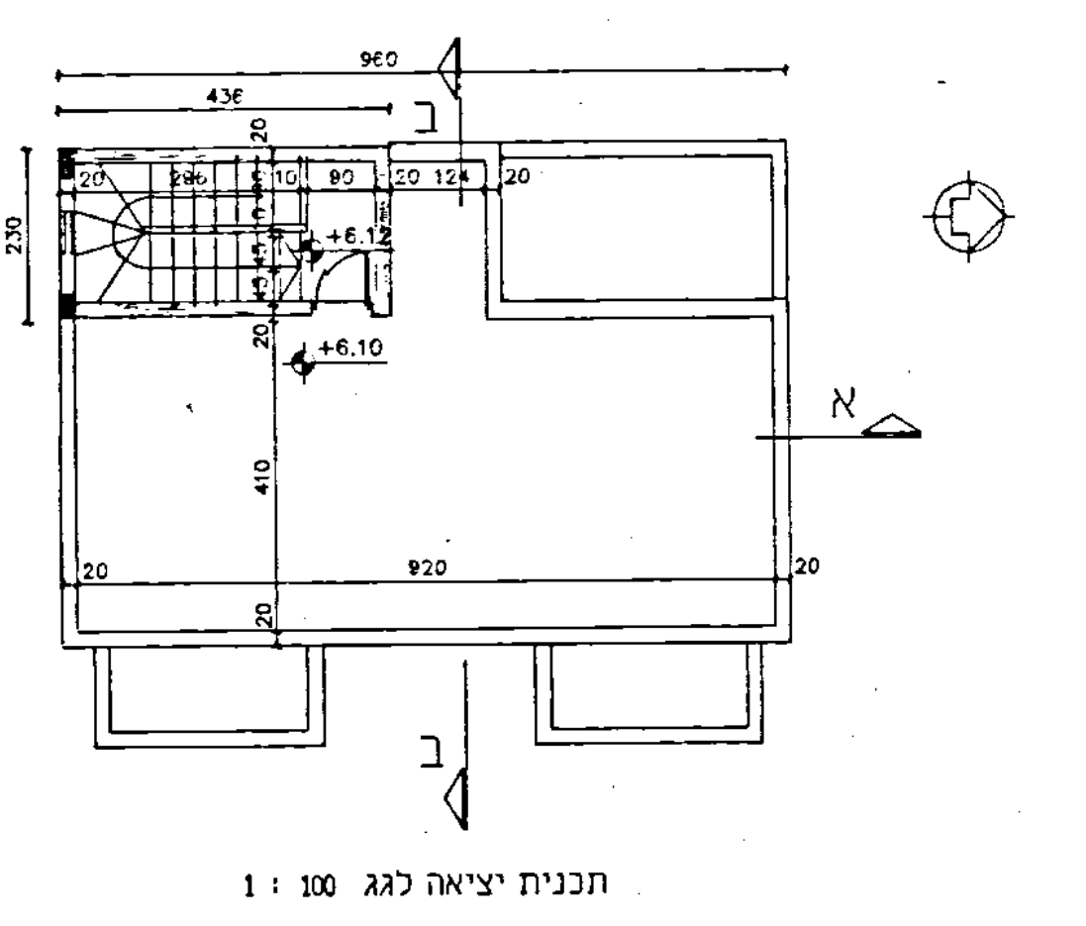

תכנית יציאה לגג 1:100

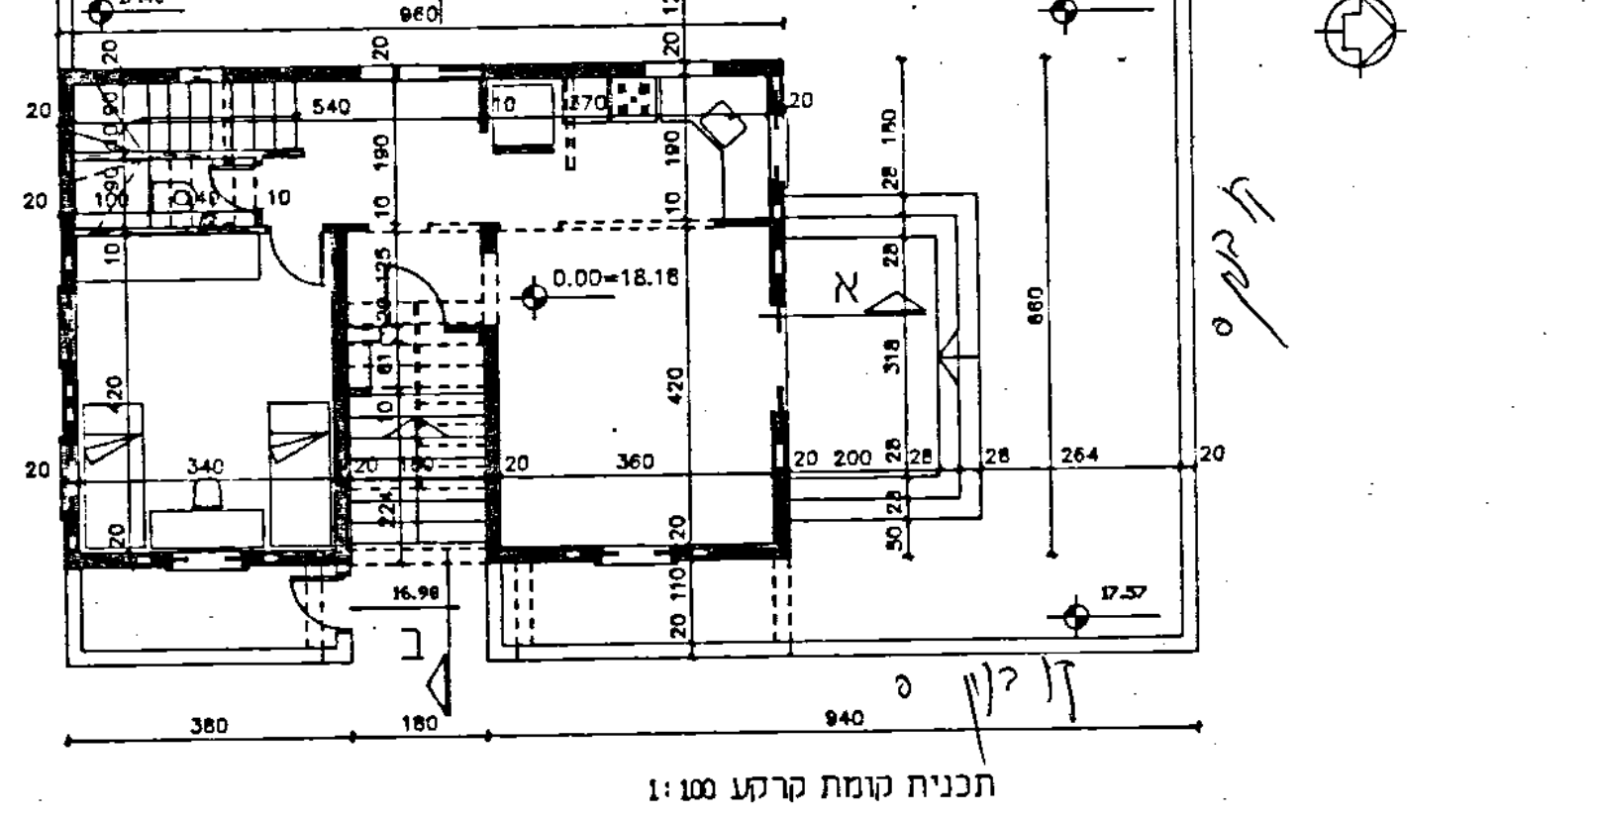

תכנית קומת קרקע 1:100

קו בנין 0

קו בנין אחורי 0
אין חלונות בקו בנין 0
חלוש-מפסק לאלגובה
לבנין עם חלונות
גמל בגדרות לרחוב

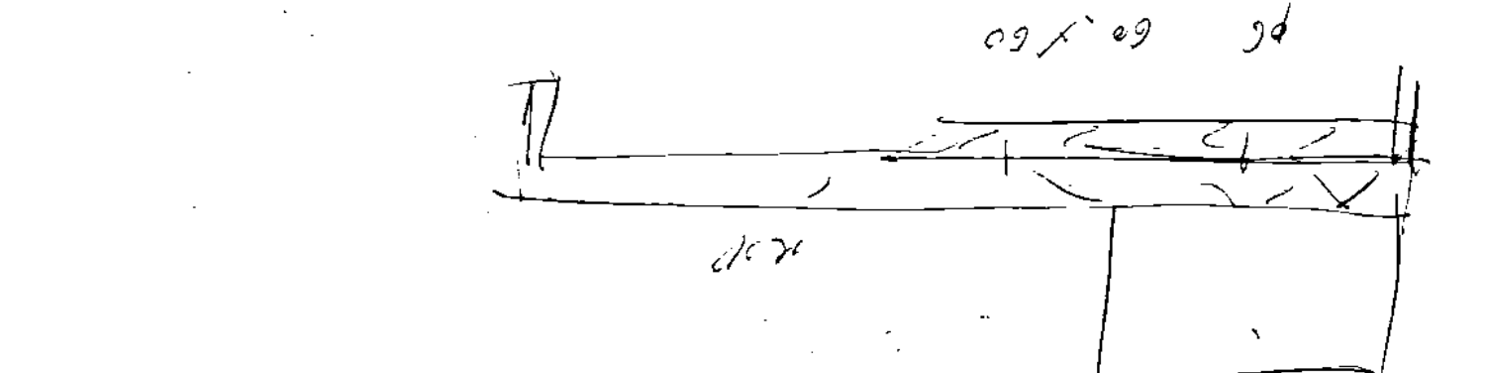

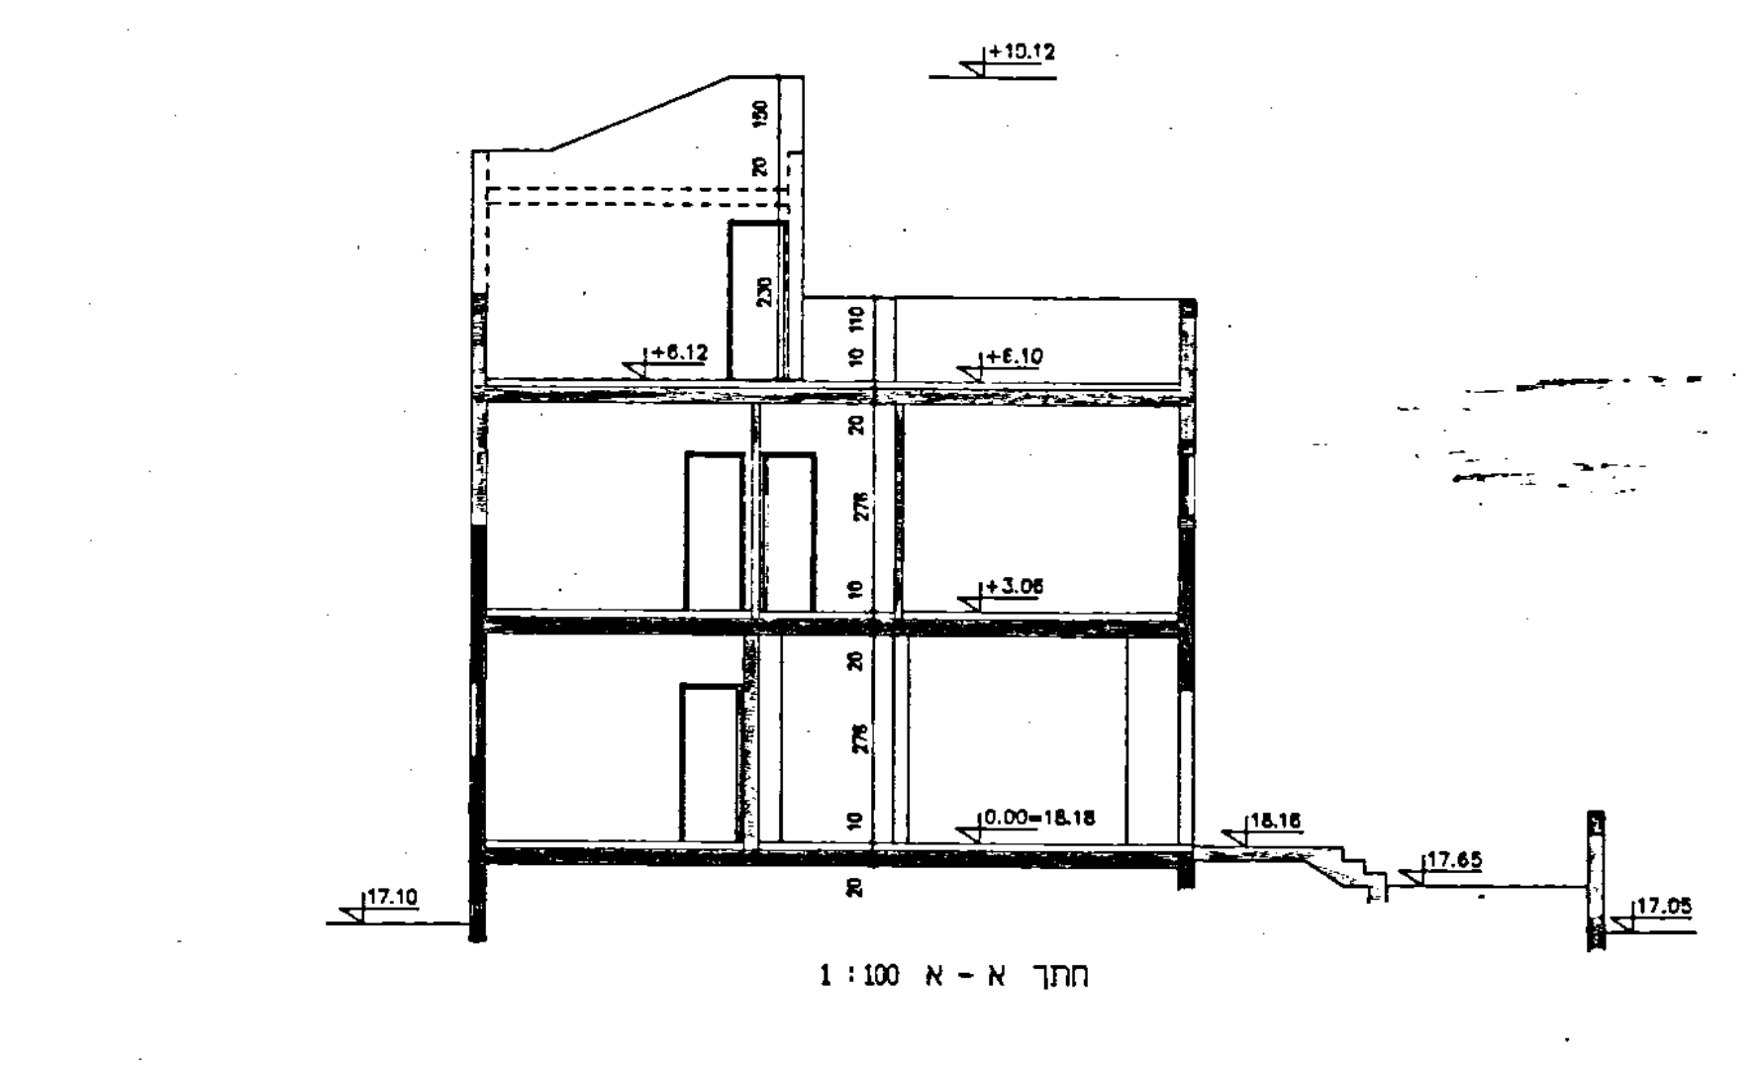

חתך א - א 1:100

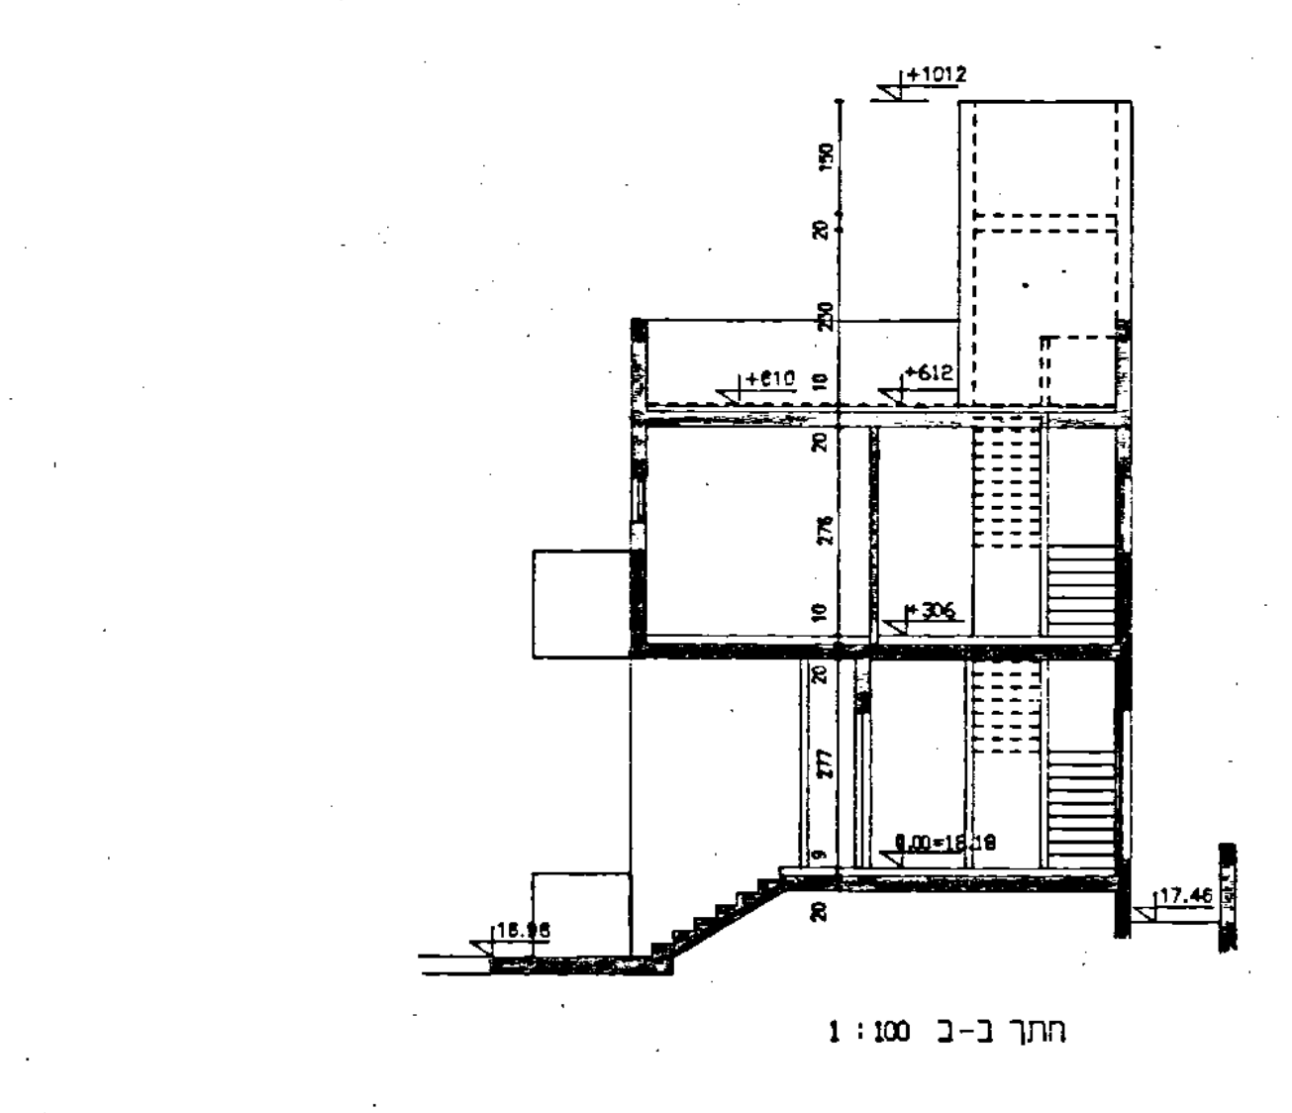

חתך ב - ב 1:100

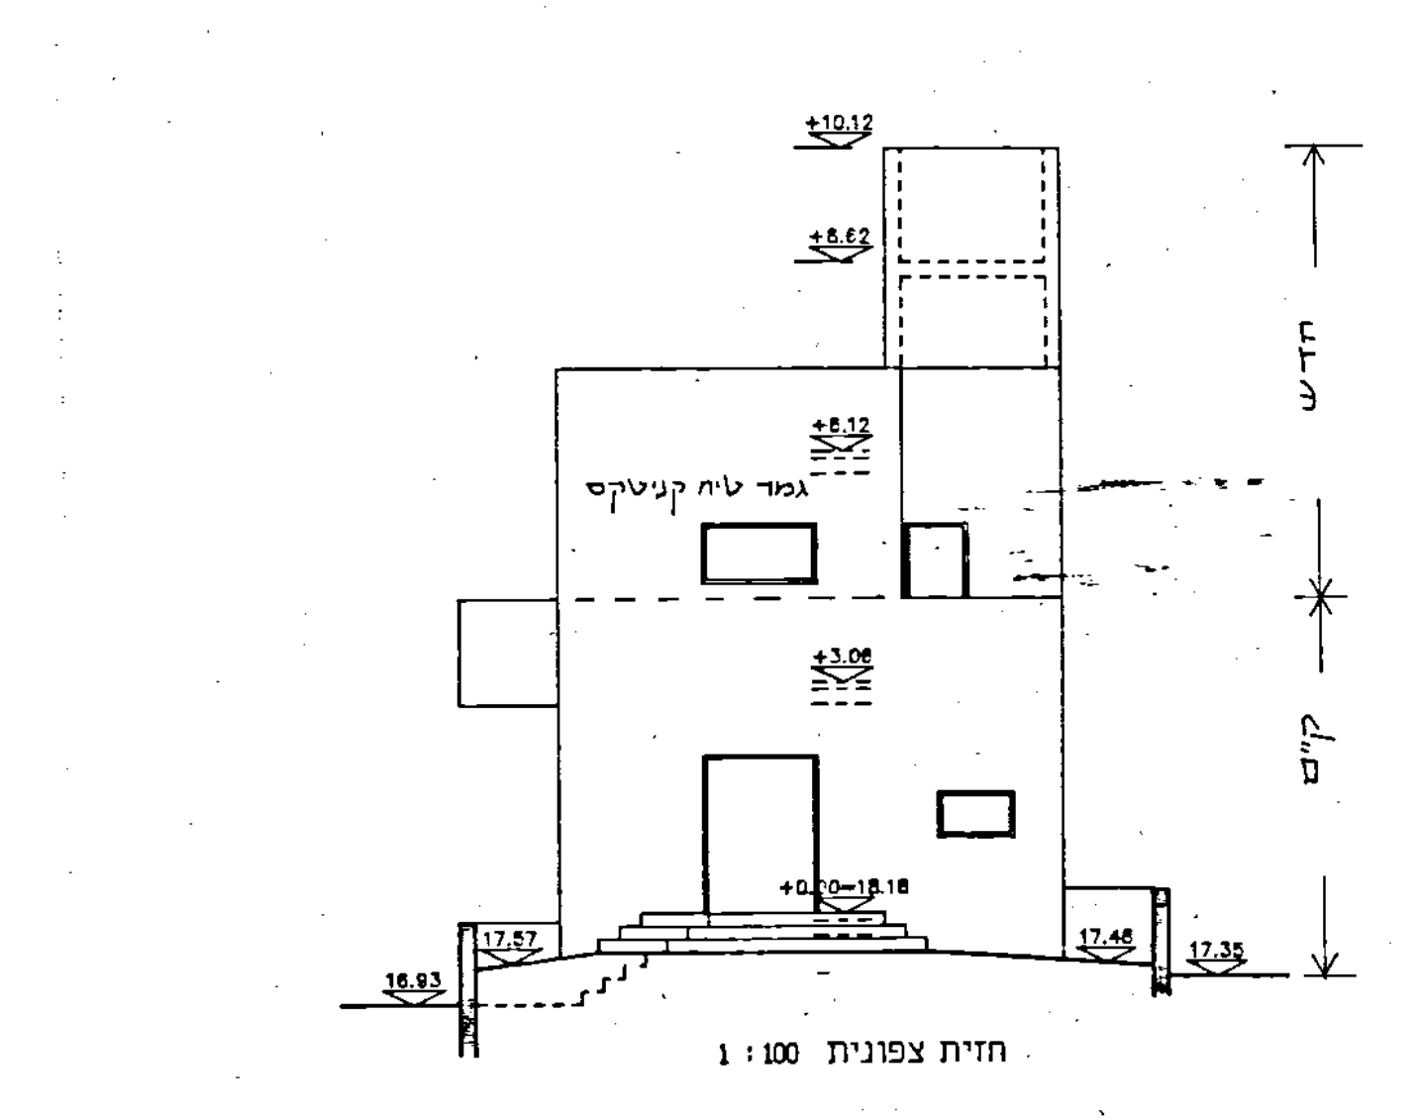

חזית צפונית 1:100

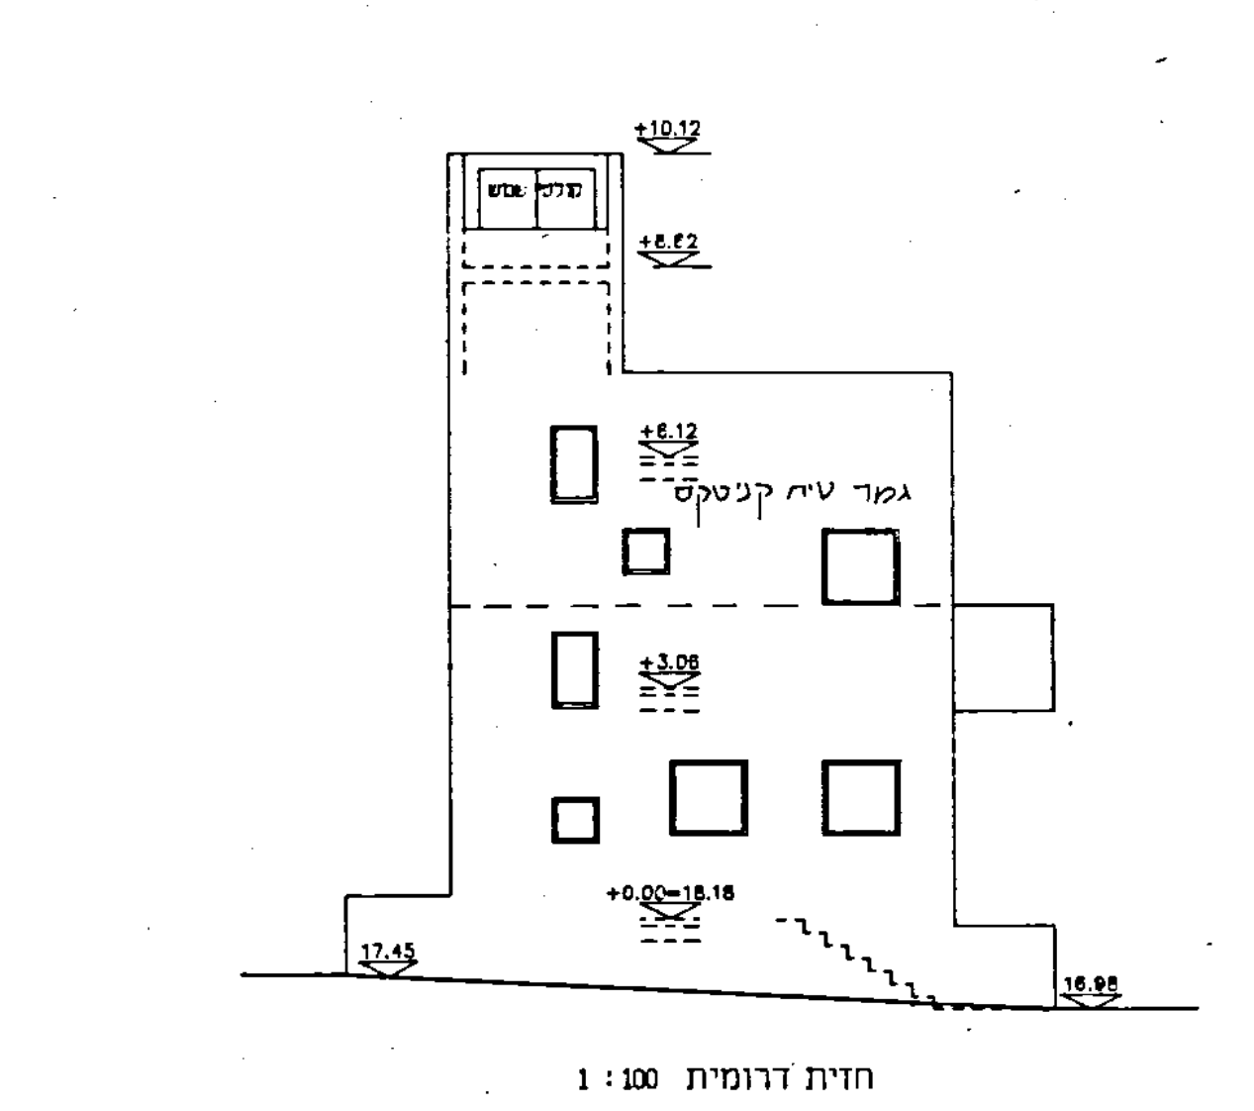

חזית דרומית 1:100

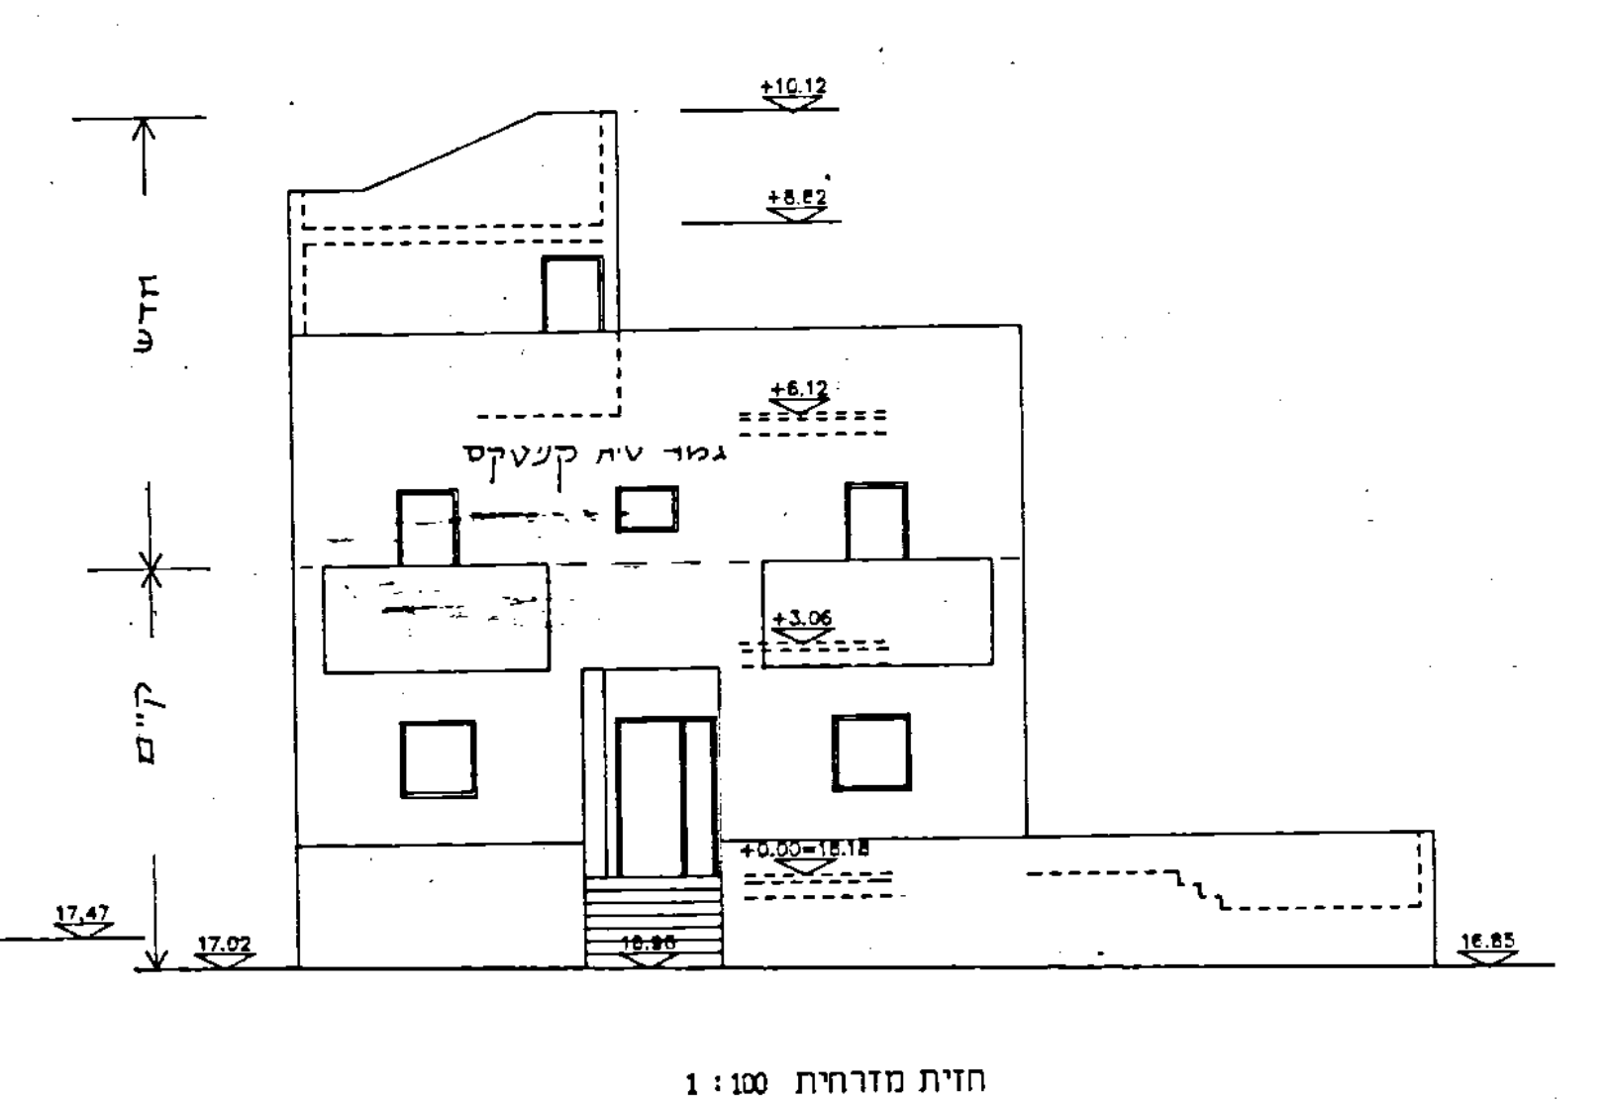

חזית מזרחית 1:100

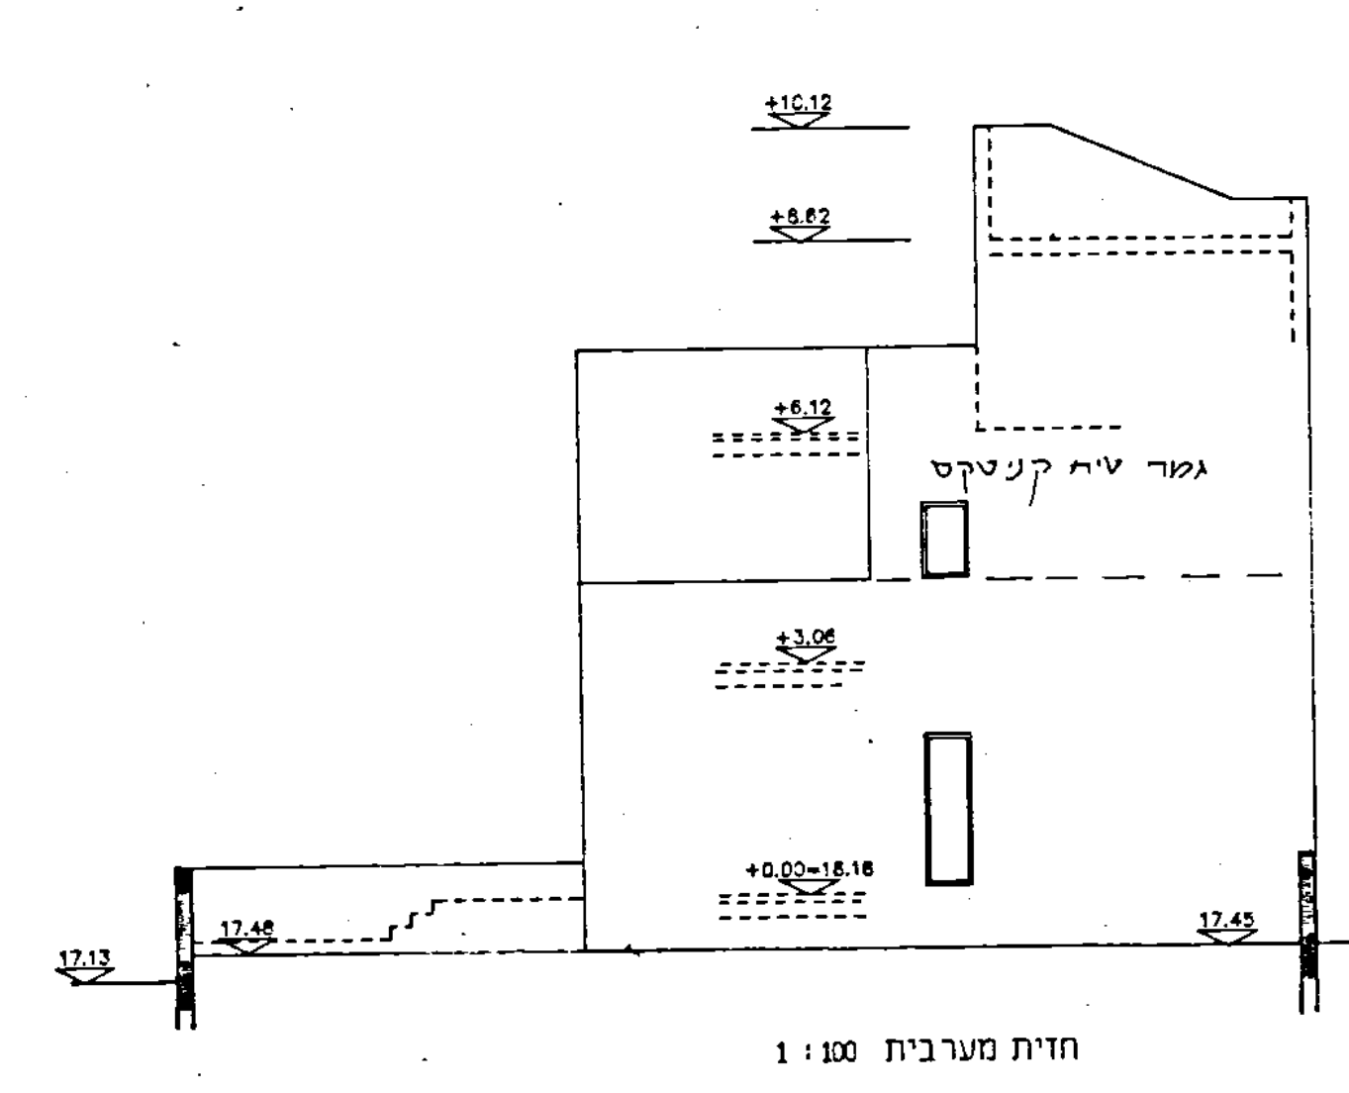

חזית מערבית 1:100

סוף מסמך