איכות נמוכה

ר-920747
292-416

חוק התכנון והבניה, התשכ"ה-1965
תקנות התכנון והבניה (בקשה להיתר, תנאיו ואגרות), התש"ל-1970
טופס 2 (תקנה 2(א))

תיק מס 4047-020

מיפרט

הועדה המקומית לתכנון ולבניה

עירית תל-אביב-יפו
10-03-1992

א. תיאור הבנין

מגרש	תכנית מיתאר מקומית או מפורטת	חלקה	גוש	מס'	הרחוב	1. המקום
1	2215	43	6135	20	תשבי	שכונת התקוה

	השם	המען	מס' הטלפון
2. המבקש	שרה ויהודה חזן	תשבי 20 שכונת התקוה	377260
3. בעל הזכות בנכס	" " "	" " "	"
4. עורך הבקשה *	פרחי יוסי-אדריכל	אדם הכהן 16 תל אביב	5239997
5. האחראי לביצוע השלד	צורף יצחק-מהנדס	בלוך 40 תל אביב	235996

6. אזור הבניה: ■ מגורים ☐ מסחר ☐ תעשיה ☐ בנין ציבורי ☐ חקלאי ☐ ....

7. שטח: המגרש/החלקה: 138 מ"ר. אחוז הבניה המותר: 140 %

8. מטרת הבנין: ■ מגורים ☐ הארחה ☐ עסקים ☐ תעשיה ☐ חקלאי ☐ ציבורי ☐ ....

9. מהות הבנין ותכליתו: תוספת קומה לדירה קיימת

10. תיאור העבודה המוצעת: ☐ בנין חדש ■ תוספת לבנין קיים ☐ הריסה ☐ תיקונים ☐ שינוי בבנין ☐ ....
☐ שינוי בשימוש ממטרה: .... למטרה: ....

11. האם הבניה היא כעד: ☐ משרד ממשלתי ☐ הרשות המקומית ☐ הסוכנות היהודית

ב. היקף הבניה

קומה	קיים	מוצע	סך הכל	אחוז הבניה	מגורים בדירות עד 45 מ"ר	עד 65 מ"ר	עד 90 מ"ר	עד 100 מ"ר	מעל 100 מ"ר	עסקי הארחה וכו'	ציבורי	שונות	מס' חדרים קיים	מס' חדרים מוצע
1	2	3	4	5	6	7	8	9	10	11	12	13	14	15
מרתף														
קרקע	58.05	—	58.05	42.06										
א	—	48.54	48.54	35.17										
ב גג		5.33	5.33	0.04										
ג														
ד														
ה														
ו														
ז														
חדרי מדרגות														
בניני עזר														
סך הכל	58.05	53.87	111.92	77.27										

הנפח המוצע: של הבנין העיקרי .... מ"ק. של בנין עזר .... מ"ק.

עירית תל-אביב-יפו
מ.ה. ההנדסה
מחל. ת פקוח על הבניה
ת.ב
הבניה מס' 292-416
נבדקה ביום 12.3.92
מהנדס אזורי

ג. השימוש בבנין
1. הבניה המוצעת למגורים

דירות בנות:	שטח כל דירה מ"ר	מספר דירות מכל סוג	כל הדירות	רצפות חדרי דיור בלבד, ומרפסות מקורות	רצפות חדרי שירות ופרוזדורים בלבד	רצפות של מרפסות בלתי מקורות	חדרים	מטבחים	אמבטיות	בתי שימוש	אחרים
1	2	3	4	5	6	7	8	9	10	11	12
חדר אחד	ראה השרטוט הסכימתי של שטחי הבניה בכל קומה המציין מספר החדרים ושטח כל דירה.										
2 חדרים											
3 חדרים											
4 חדרים		1	111.92				4	1	1	2	
5 חדרים											
6 חדרים											
7 חדרים ויותר											
חדרים נוספים לדירות קיימות											
בניני עזר											
סך הכל		1	111.92				4	1	1	2	

---

2. הבניה הקיימת המוצעת לתעשיה ולמלאכה

פרטים	קיים שטח	קיים גובה	קיים נפח	קיים % הבניה	מוצע שטח	מוצע גובה	מוצע נפח	מוצע % הבניה	סך הכל שטח	סך הכל נפח	סך הכל % הבניה	הערות
1	2	3	4	5	6	7	8	9	10	11	12	13
אולמי מלאכה												
משרדים												
חדרי שירות												
סככות												
בניני עזר												
חדרי מדרגות												
סך הכל												

3. הבניה המוצעת למטרות אחרות (הארחה, עסקים ומשרדים, בניני ציבור, בניני משק חקלאי, מטרות שונות).

השימוש המיועד	סך הכל מ"ר	מזה: חדרים	אולמות	אחסנה	חדרי שירות	מספר חדרים, אולמות וכו': חדרים	אולמות	אחסנה	חדרי שירות
1	2	3	4	5	6	7	8	9	10
בניני עזר (למעט אלה המפורטים ב-ג(4))									

4. חלקי בנין אחרים – הבניה המוצעת, שטח במ"ר.

חדרי מדרגות	מרפסות שלא נכללו לעיל	מעליות	חדרי הסקה	חדרי כביסה	מקלטים	קומת עמודים מפולשת	מחסנים	מוסכים	בניני עזר נוספים	סך הכל
1	2	3	4	5	6	7	8	9	10	11

ד. חומר הבניה

קירות חיצונים	☐ בטון מזוין	■ לבני בטון או בלוקים	☐ לבני סיליקט	☐ לבנים שרופות	☐ אבן טבעית
	☐ אבן מלאכותית	☐ איטונג	☐ עץ	☐ ברזל	☐ חמרים אחרים
תקרות	■ בטון מזוין	☐ עץ	☐ חומר אחר		
גג	■ בטון מזוין	☐ רעפים	☐ אסבסט	☐ פח	☐ חומר אחר ....

קיימות ..—.. מ"א מוצעות ..39.4.. מ"א

ה. גדרות
ו. בקרא

☐ בטון או בטון מזוין ☐ אבן ☐ עץ ☐ איטונג
☐ בלוקים או לבנים מבטון ☐ סיליקט או לבנים אדומות ☐ חומר אחר ☐ להריסה

הערות:

הנני מאשר כי הנתונים הנ"ל נכונים

תאריך 10.3.92 חתימת המבקש חזן שרה יהודה חתימת עורך הבקשה *
חתימת האחראי לביצוע השלד ______ חתימת בעל הזכות בנכס חזן שרה חזן יהודה

לשימוש הועדה המקומית בלבד	מס' ההיתר	תאריך ההיתר	תאריך התחלת הבניה	תאריך גמר הבניה

חתימת הועדה המקומית

אישורים של רשויות חוץ:

* היו מספר עורכי בקשה, כאמור בתקנה 3ה, יבוא במקום כל אלה, הראשון שברשימת עורכי הבקשה, כאמור בטופס 1.

עירית תל אביב - יפו
מינהל ההנדסה

הועדה המקומית לתכנון ובניה - ת"א-יפו

בקשה להיתר בניה

לשימוש משרדי	
מס' תיק בקשה	
מס' תיק בנין	
מס' תיק מידע	
מס' בקשה קודמת *	

מורך בקשה נכבד
- הנך מתבקש לקרוא בתשומת לב את הטופס ולמלא את הפרטים הדרושים בכתב ברור.
- את הטופס המלא יש להגיש בצמוד למפרט (טופס 2).
- טופס מלא, יחד עם תיק צהוב ותיק מידע מאושר, הם בסיס להליכי הרישוי עד למתן ההיתר.

חלק א' - תאור הבקשה (לשימוש עורך הבקשה)

1. סיווג הבקשה (סמן בעיגול את הסוג המתאים)
   - א. בניה חדשה - מספר קומות מלאות [—] מס' קומות חלקיות [—] קומה מפולשת כן / לא
   - ב. תוספת עד 10 מ"ר - במסגרת הרחבת דיור שכונתית כן / לא מס' יחידות דיור מורחבות [—]
     האם הבניה באגף שלם כן / לא
   - ג. תוספת מעל 10 מ"ר - במסגרת הרחבת דיור שכונתית [✓ כן] / לא מס' יחידות דיור מורחבות [1]
     האם הבניה באגף שלם [✓ כן] / לא
   - ד. הריסת, פרט ....
   - ה. שיפוצים, פרט שיפוץ קומת הקרקע הקיימת
   - ו. שינויים בזמן בניה - בהמשך להיתר מס' [—] מתאריך [/ /]
   - ז. בניה על הגג, פרט חדר מדרגות ליציאה לגג וחדר כביסה
   - ח. שימוש חורג - משימוש: .... לשימוש: .... בקומה [—] בשטח [—] מ"ר
   - ט. עבודה מצומצמת - תאור העבודה: ....

2. היקף הבניה המוצעת לעומת זכויות מותרות

קומה	שטח קיים בהיתר	שטח קיים ללא היתר	שטח מוצע אישור בניה קיימת	שטח מוצע בניה חדשה	סה"כ	אחוזי בניה שטח מאושר **	אחוזי בניה עפ"י הבקשה אחוז	מותר לפי תב"ע שטח	מותר לפי תב"ע אחוז	סטיה שטח	סטיה אחוז	סיבת הסטיה/נימוקים
מרתף												
קרקע	58.05			—	58.05		42.06		60			
א	—			48.54	48.54		35.17					
ב גג				5.33	5.33		0.04					
ג												
ד												
ה												
ו												
ז												
הכניסה הקובעת												
חדרי מדרגות												
בניני עזר												
סה"כ	58.05			53.87	111.92		77.27		140			

** באחוזי בניה
* עבור התלמות שמו תוקפן או בקשה להארכת תוקף היתר

3. מהות הבקשה - תאור מילולי (ראה הנחיות בדף המצורף)
שיפוץ קומת הקרקע הקיימת ותוספת קומה מעל לקיים וכן יציאה לגג בשטח כולל של 111.92 מ"ר

4. קוי בניה

לרחוב/לצד		קוי בניה (מ') מוצע	קוי בניה (מ') מותר	סטיה מ'	סטיה %	רוחב קולונדה (מ') מוצע	רוחב קולונדה (מ') מותר	סטיה מ'	סטיה %
שם רחוב	תשבי	0	0	—	—				
שם רחוב									
צד									
אחור									

5. מס' יחידות דיור: מוצע [ ] מותר [ ]
6. מרתף - עליון גובה [ ] שימוש ....
- תחתון גובה [ ] שימוש ....
7. מבנה עזר: גובה [ ] מיקום: א. צדדי ב. אחורי ג. קדמי ד. צמוד לבנין ה. במסגרת הבנין
8. קומה מפולשת: גובה [ ] אחוז בניה בקומה מפולשת (%) [ ]
9. בניה על הגג:
   - א. שטח [ ]
   - ב. גובה מבנה (ברוטו) [ ]
   - ג. נסיגה מהמעקה [ ]
   - ד. אחוז בניה משטח הגג [ ]
   - ה. מיקום קולטי שמש: 1. על גג הבנין 2. על גג עליון
   - ו. קיימת בניה אחרת על הגג [✓ כן] / לא. פרט חדר מדרגות ליציאה לגג וחדר כביסה
10. קיים חדר מדרגות כללי: כן / [✓ לא]
11. נימוקים לבקשה להקלה
....
12. תאור הקיים על המגרש
קיים מבנה ישן בן קומה אחת (ראה צילומים מצורפים)
13. אם ניתנה בידך האפשרות לבחור בין מסלול רישוי בדרך מקוצרת ומסלול רישוי בדרך רגילה נא מלא את הדו"ם:
אני הח"מ מצהיר כי הבקשה להיתר מוגשת במסלול הרישוי המסומן להלן (סמן ב"x"):
■ רשות רישוי - רישוי בדרך מקוצרת - באחריות עורך הבקשה
☐ רשות רישוי - מסלול רגיל

חלק ב' - הצהרת עורך הבקשה

אני, הח"מ כלול בפנקס המהנדסים מצהיר בזאת שהבקשה הוכנה לפי כל דין ותקנה ובהתאם לתיק המידע אשר נמסר לי. הפרטים, המסמכים, האישורים, ההצהרות וכל הנספחים לבקשה היום וכמו ותיקוני עליהם יראו אותה כחתימה על הצהיר.

תאריך 10.3.92 שם עורך הבקשה יוסי פרחי מס' רשיון 9840 חתימה

חלק ג' (לשימוש משרדי)

1. מועד קבלת בקשה [| | | |]
2. הערות ....

תאריך חתימה .... שם המטפל .... חתימה ....

תל-אביב-יפו
גוש 6135
חלקה 43 (חלק)
מגרש 1
השטח 0.138 ד.מ. (לפי מדידה בשטח)
0.168 ד.מ. (לפי נסח)
הוכן בשביל: משפ' חזן
מהות הבקשה: קבלת היתר בניה

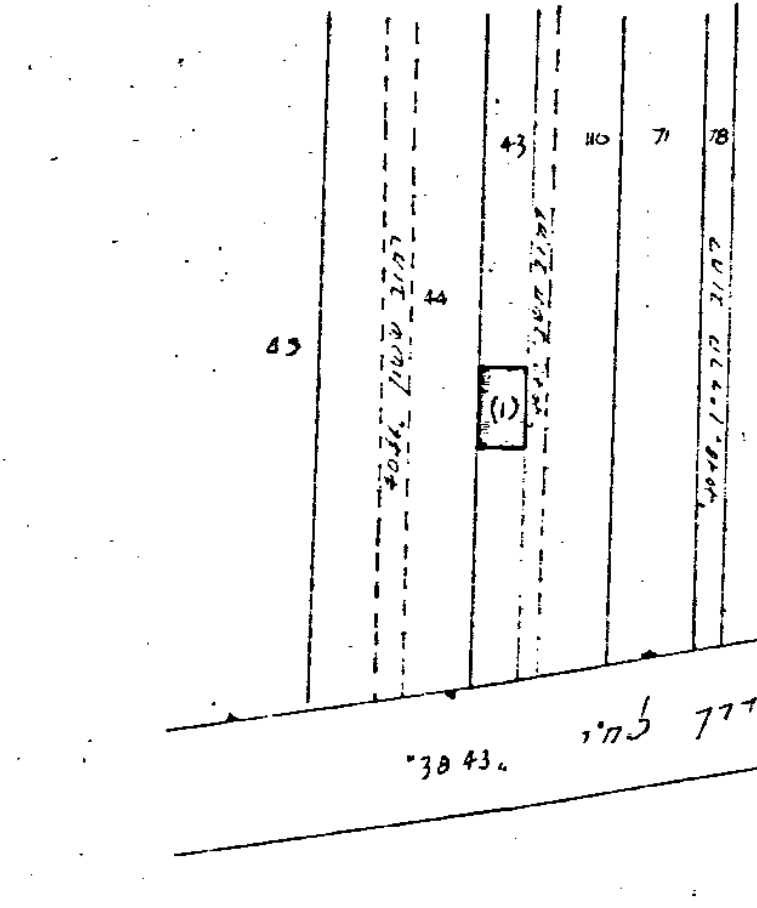

העקות

חישובי שטחים

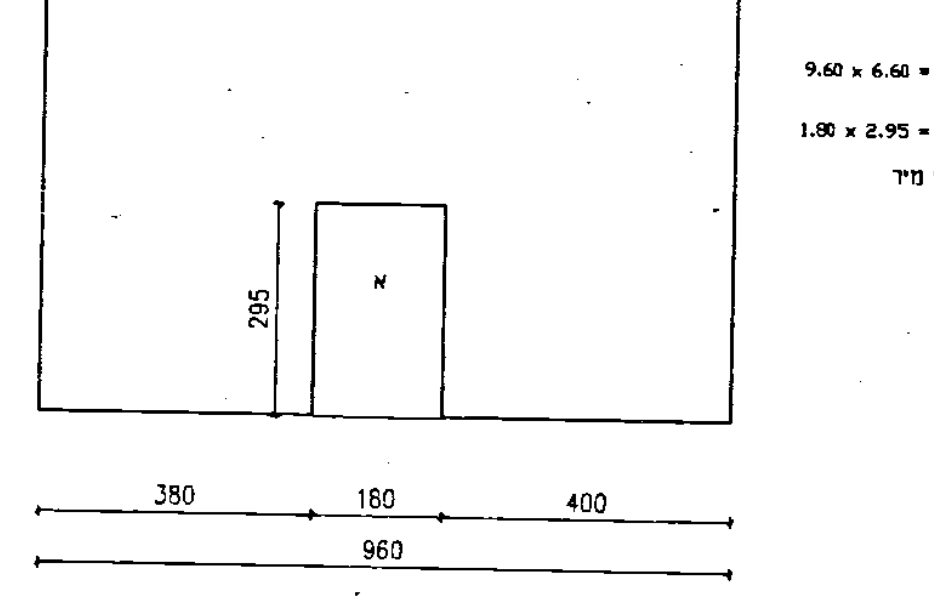

קומת קרקע - קיים
9.60 x 6.60 = 63.36
הורדה
א 1.80 x 2.95 = 5.31
סה"כ: 58.05 מ"ר

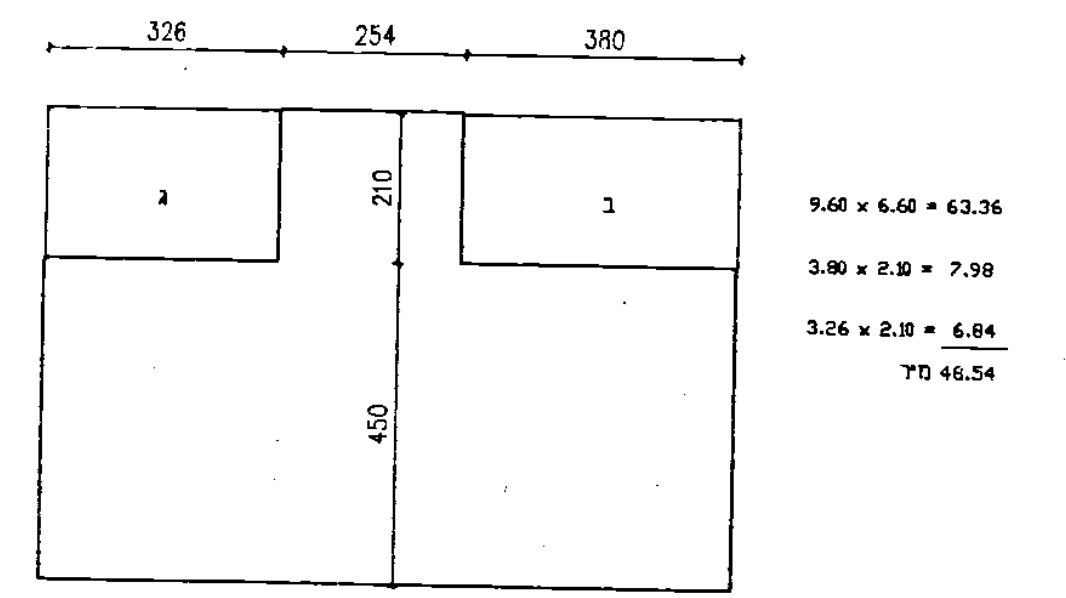

קומה א - תוספת
9.60 x 6.60 = 63.36
הורדה:
ב 3.80 x 2.10 = 7.98
ג 3.26 x 2.10 = 6.84
סה"כ: 48.54 מ"ר

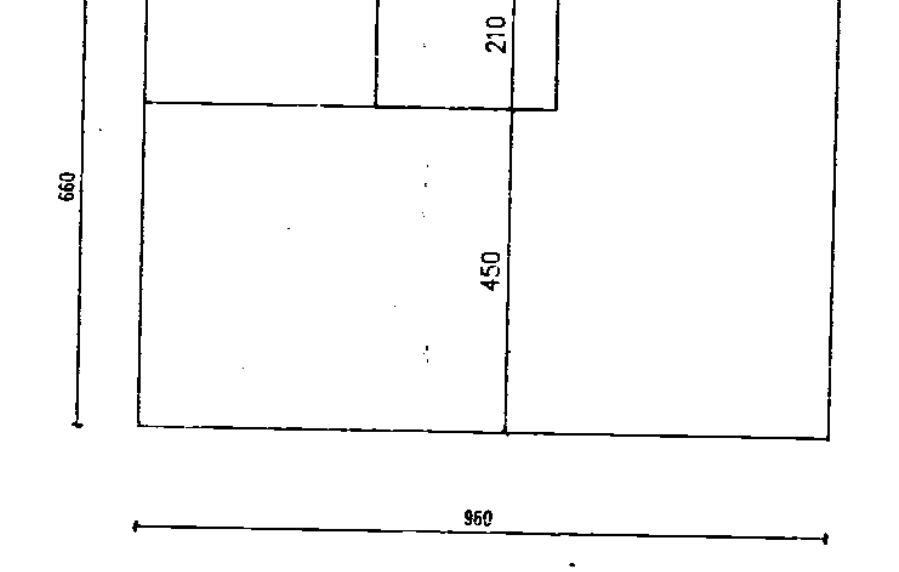

קומת גג -
2.54 x 2.10 = 5.33

סה"כ קומת קרקע + א + גג:
58.05 + 48.54 + 5.33 = 111.92

מפה טופוגרפית
1:250

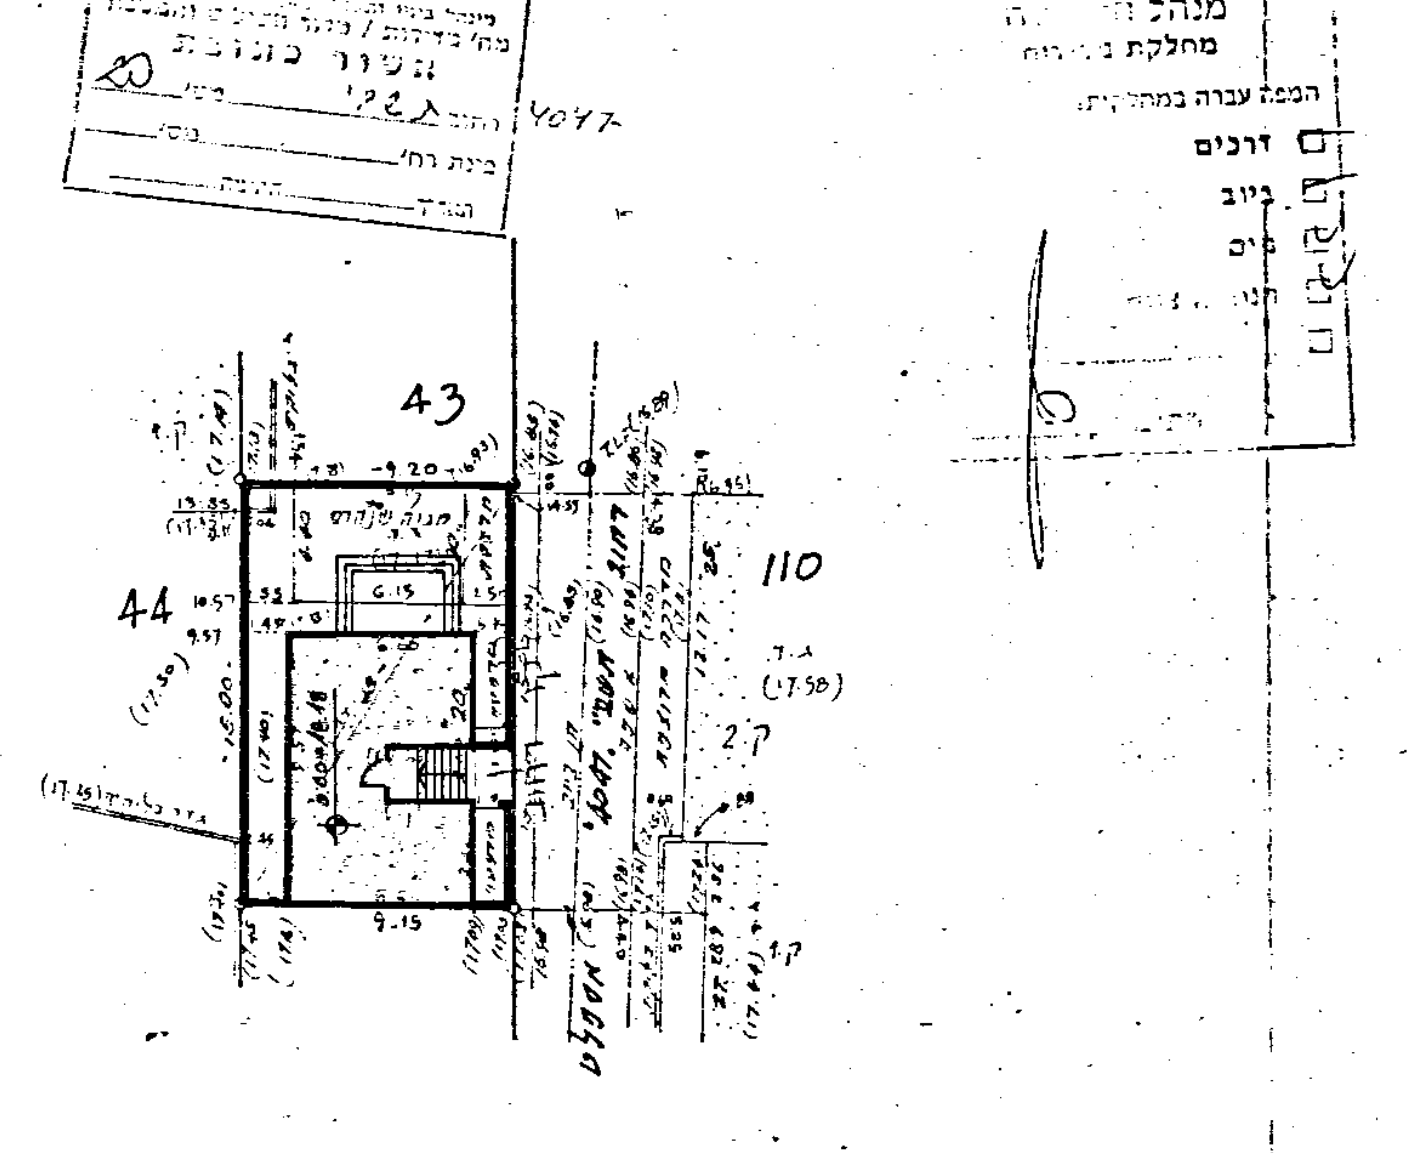

עירית תל-אביב-יפו
מינהל בנוי ותשתית / אגף עבודות ציבוריות
מחלקת מדידות
חתימה
חתימה
תאריך 16.5.90
שטח הפקעה (לצורך חשוב זכויות ב. ה.)
ואושר (ת.ב.ע.) מ"מ

לא לצו

תל-אביב
18.2.1990

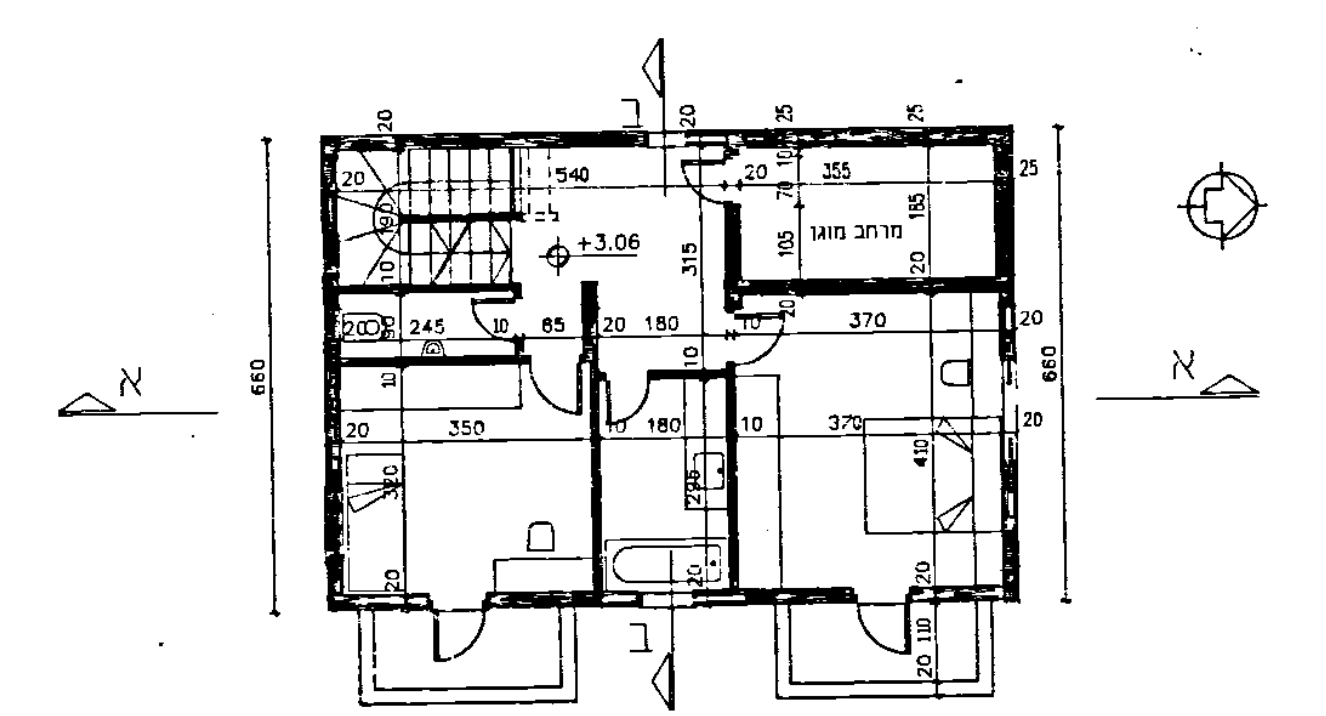

תכנית קומה א 1:100

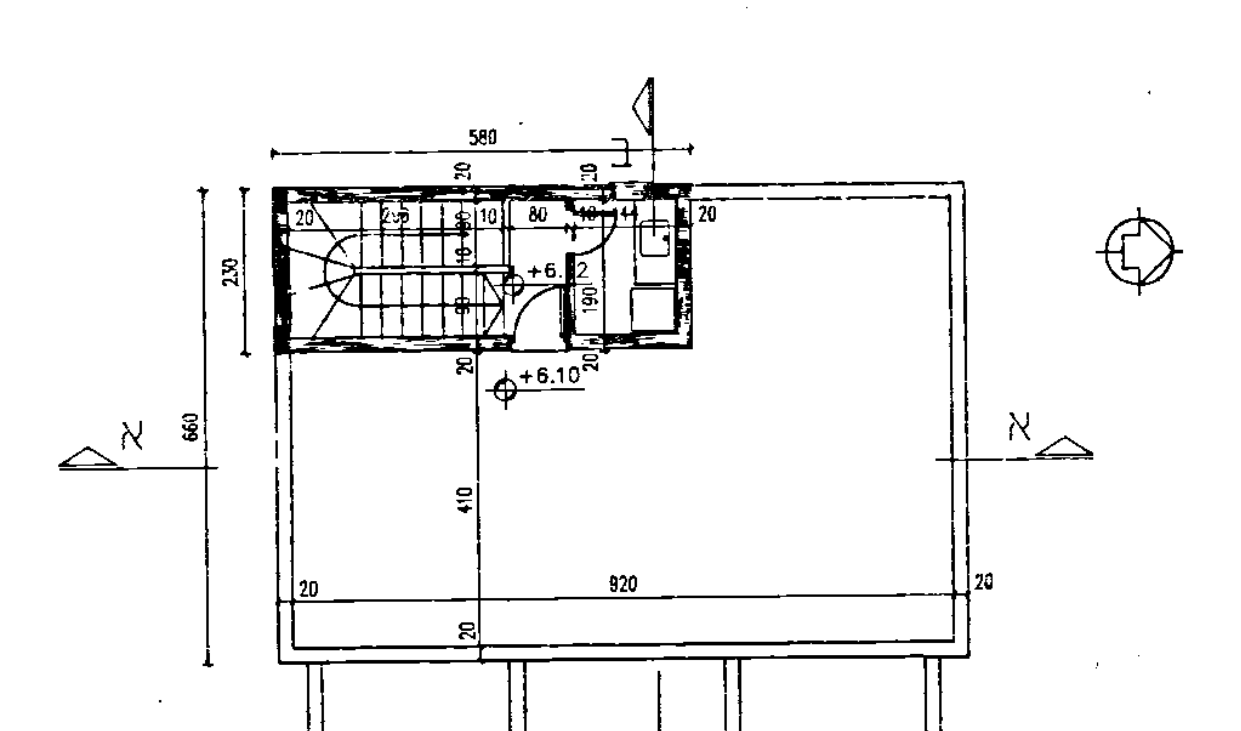

תכנית יציאה לגג 1:100

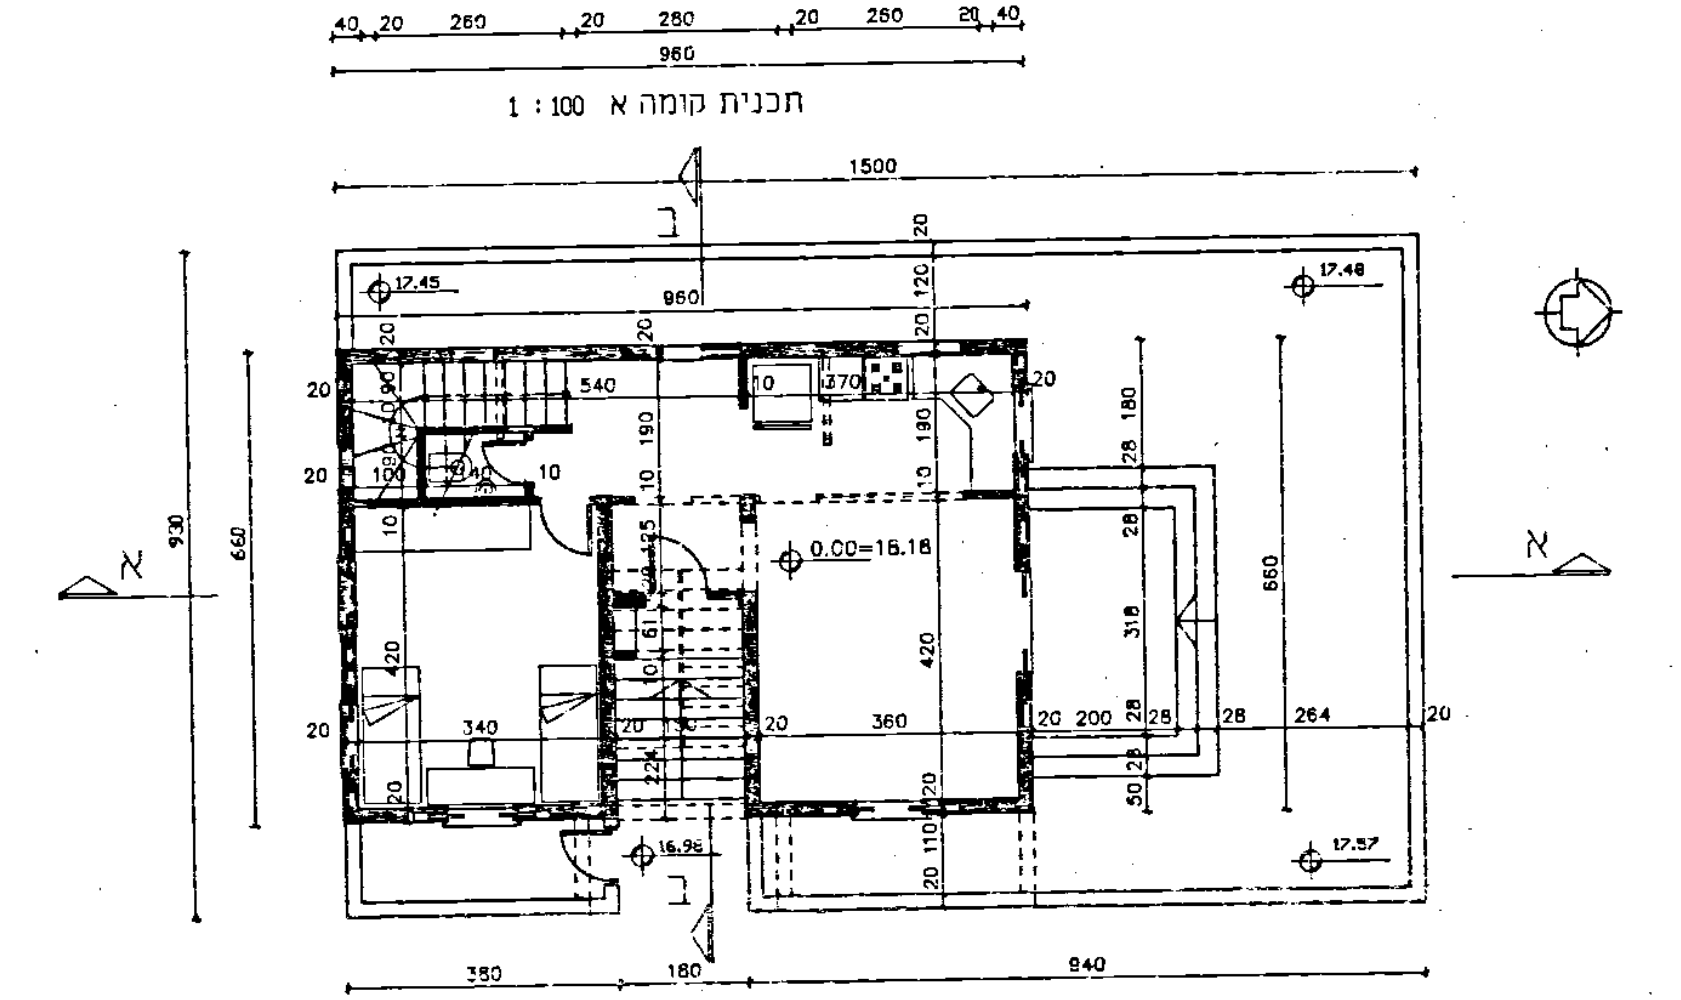

תכנית הקומה ברקע 1:100

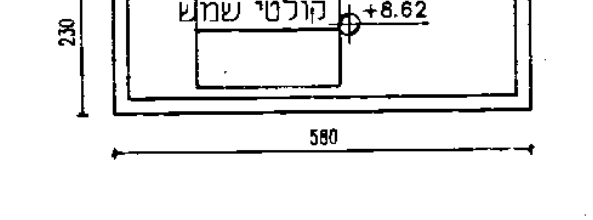

תכנית גג חדר מדרגות 1:100

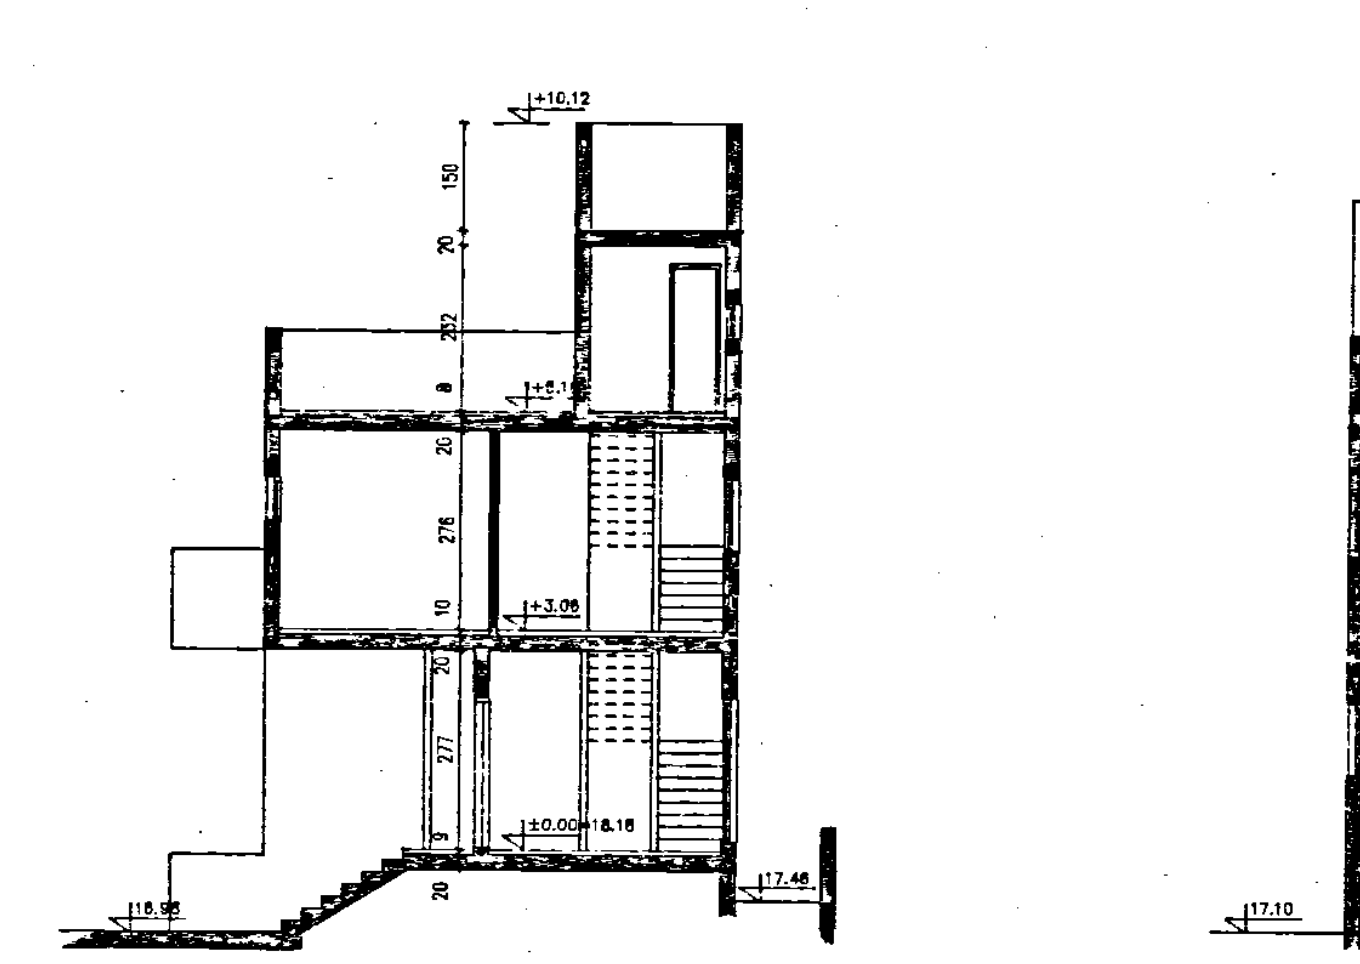

חתך ב-ב 1:100

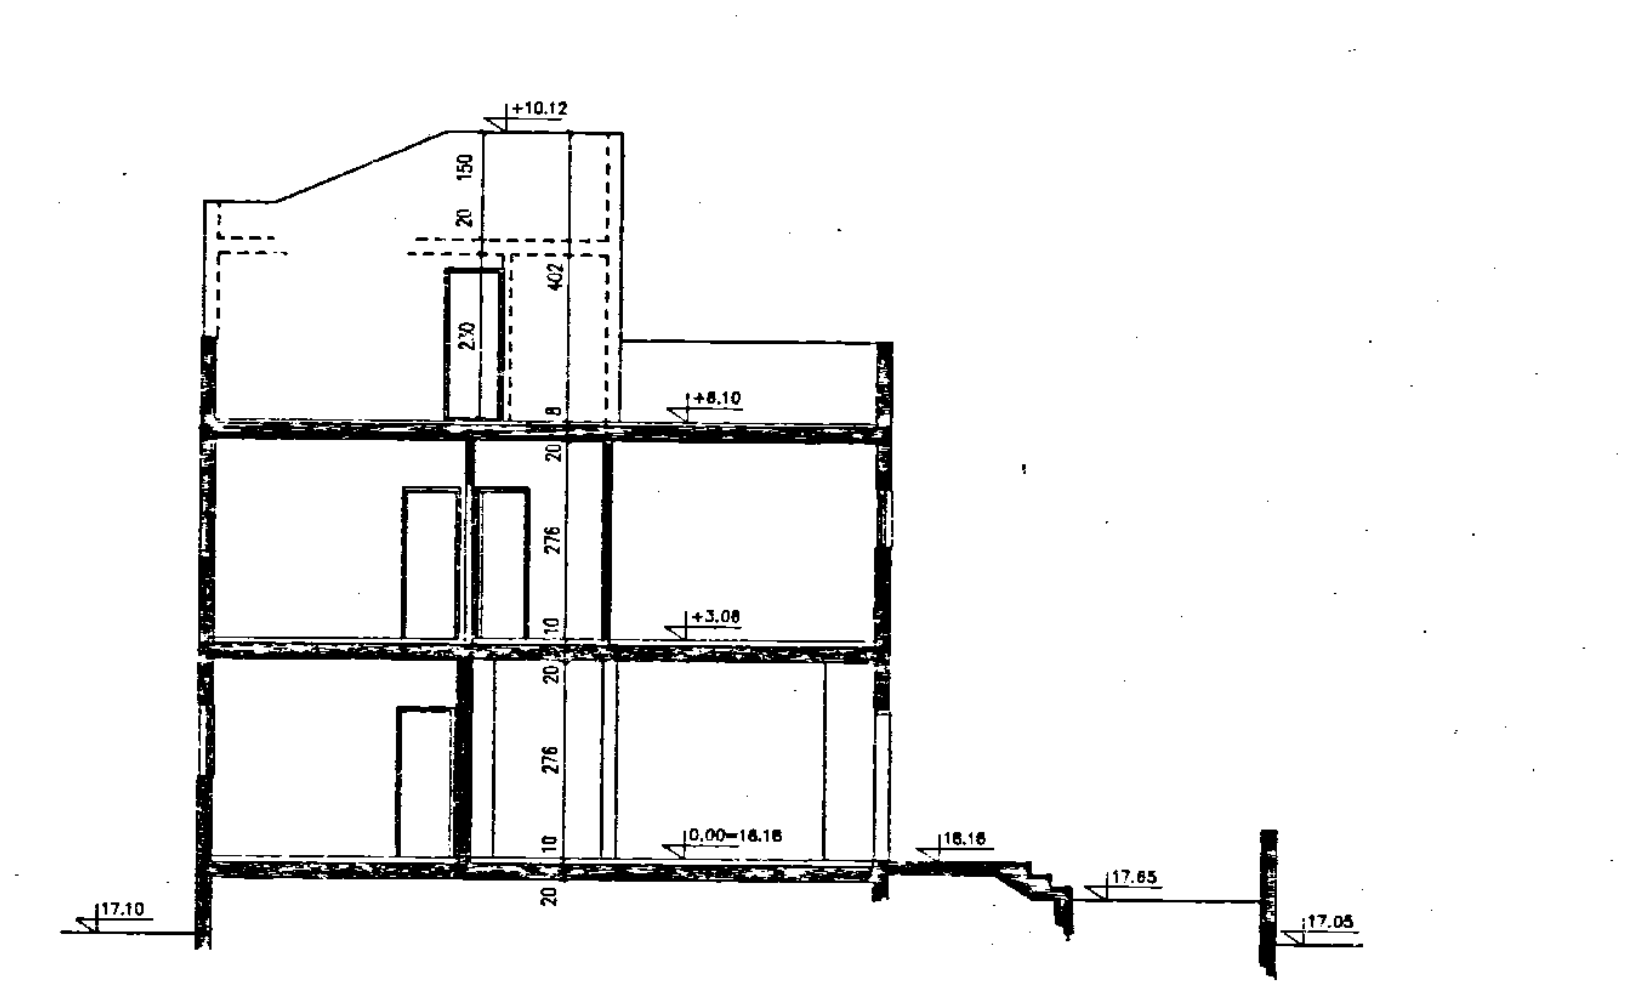

חתך א - א 1:100

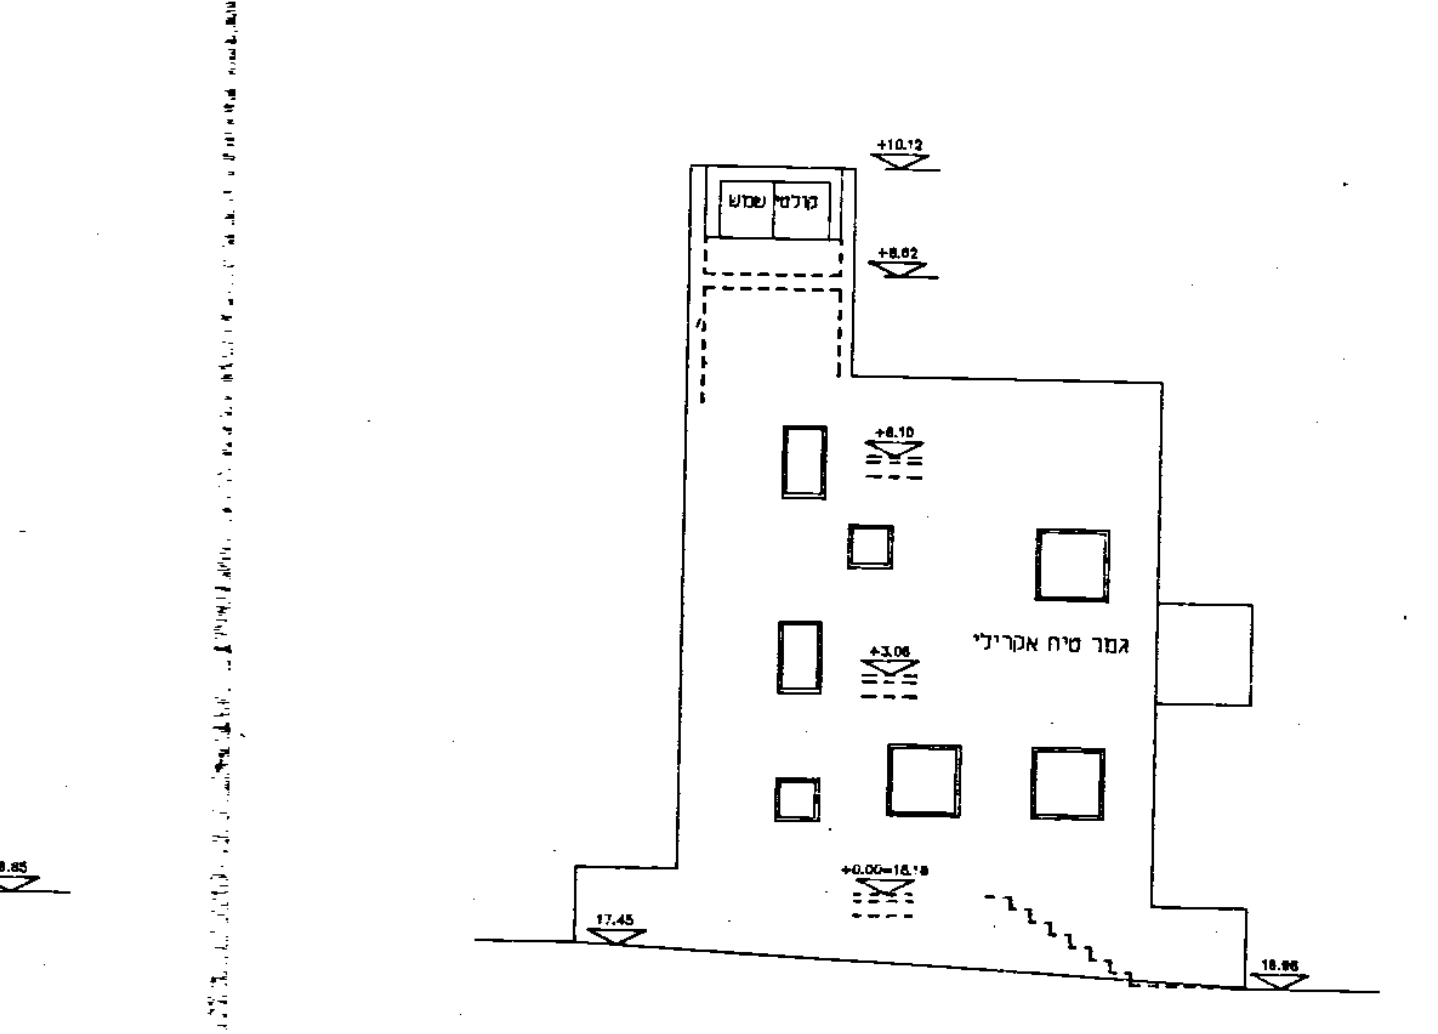

חזית דרומית 1:100

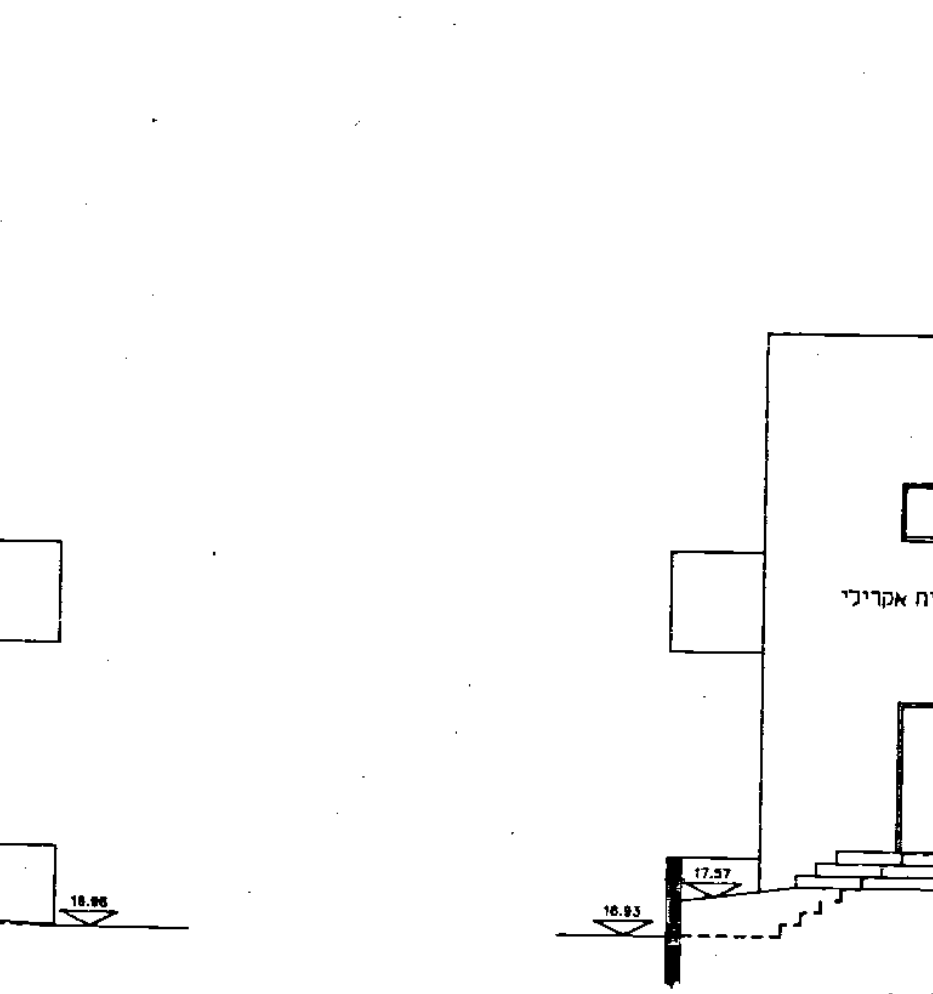

חזית צפונית 1:100

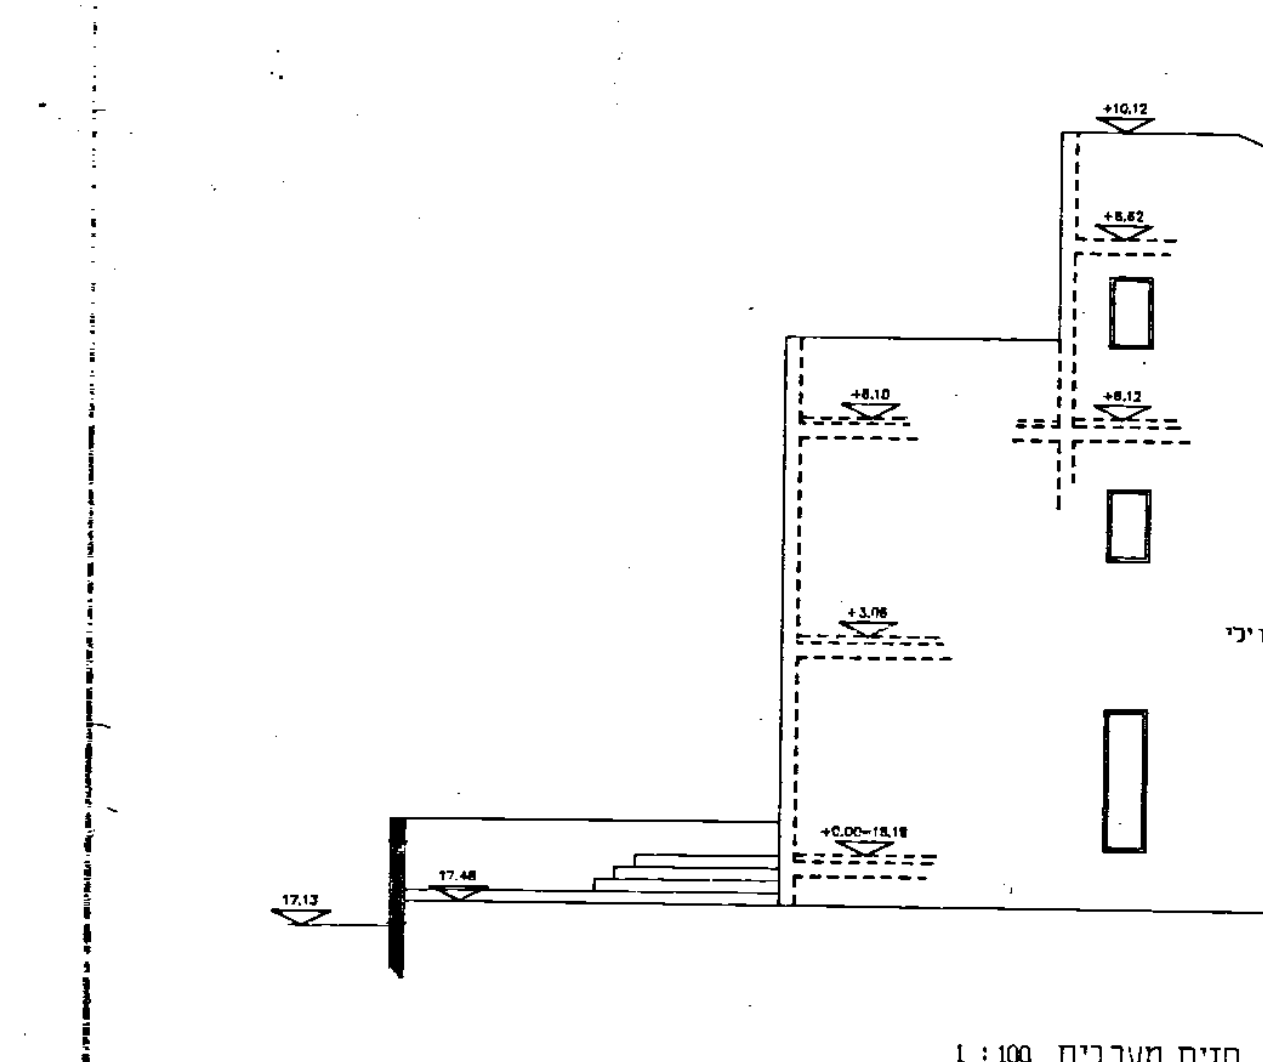

חזית מערבית 1:100

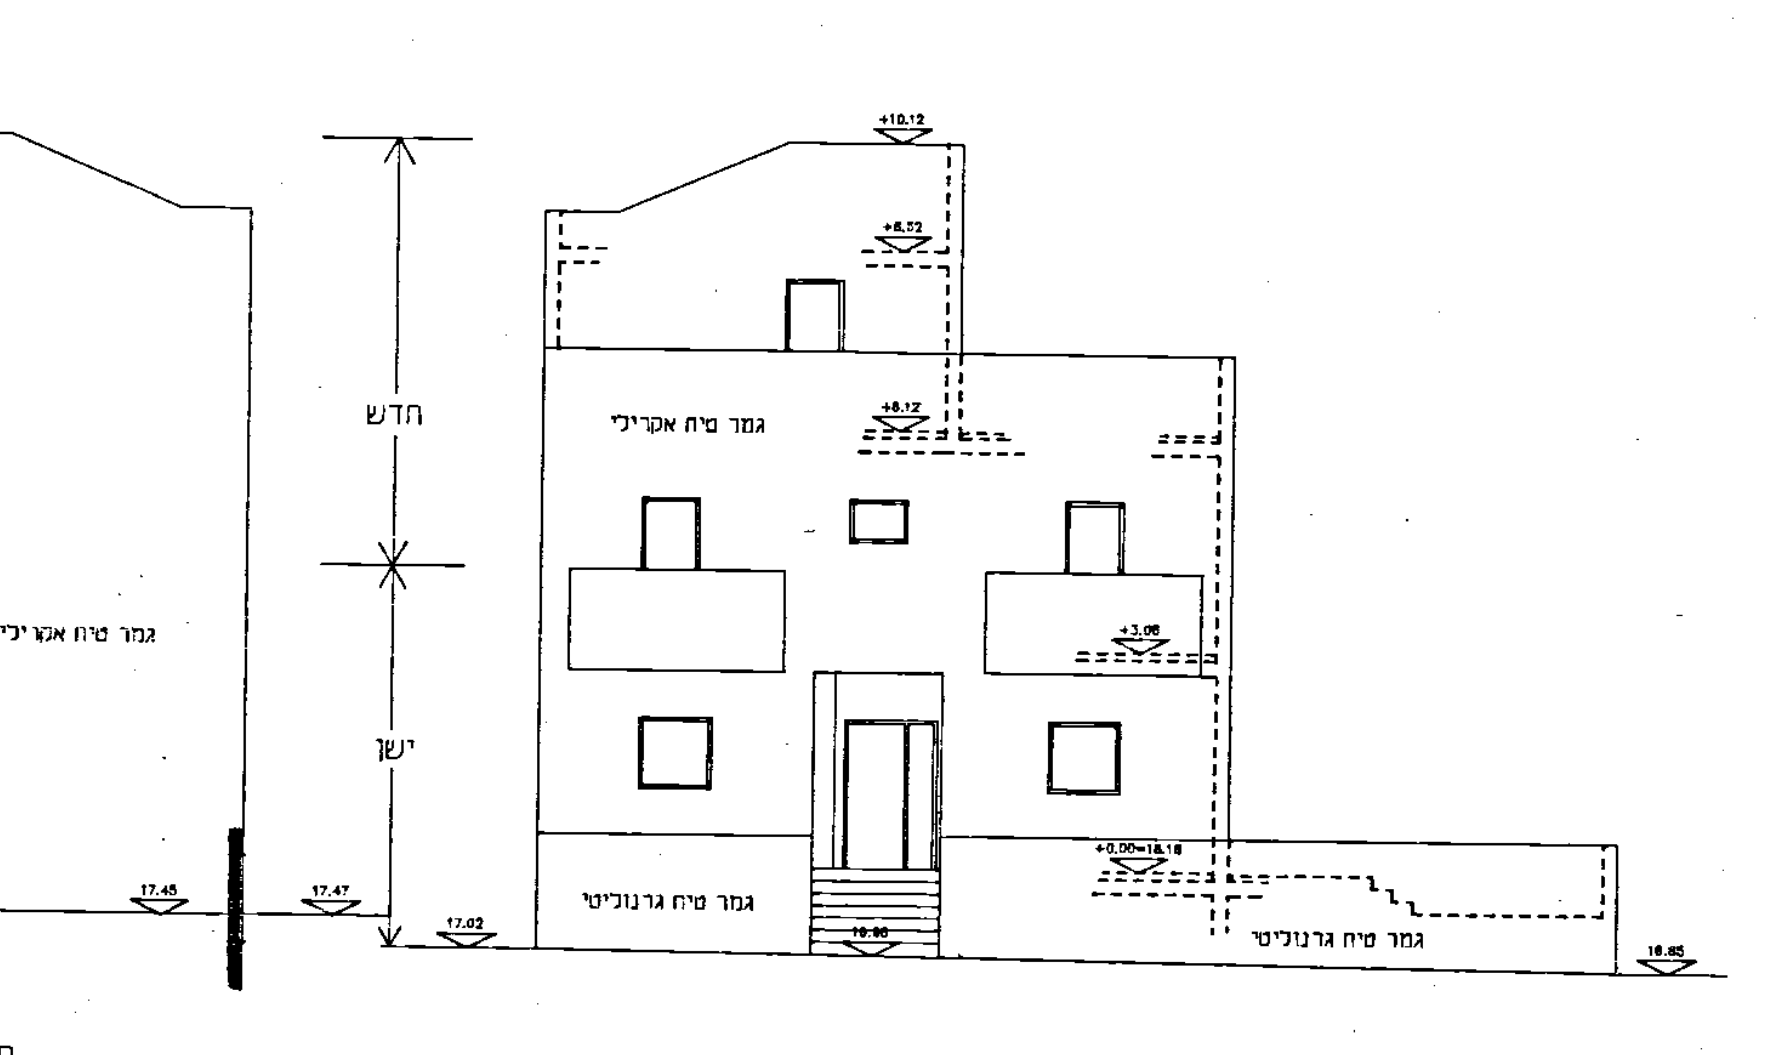

חזית מזרחית 1:100

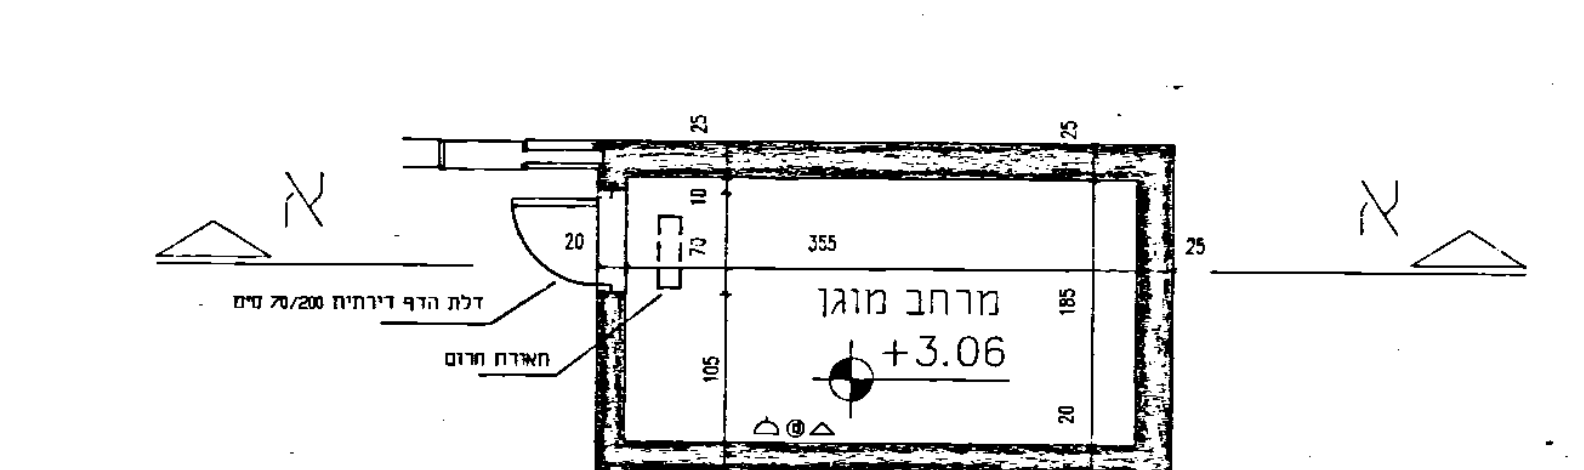

תכנית מרחב מוגן 1 : 50

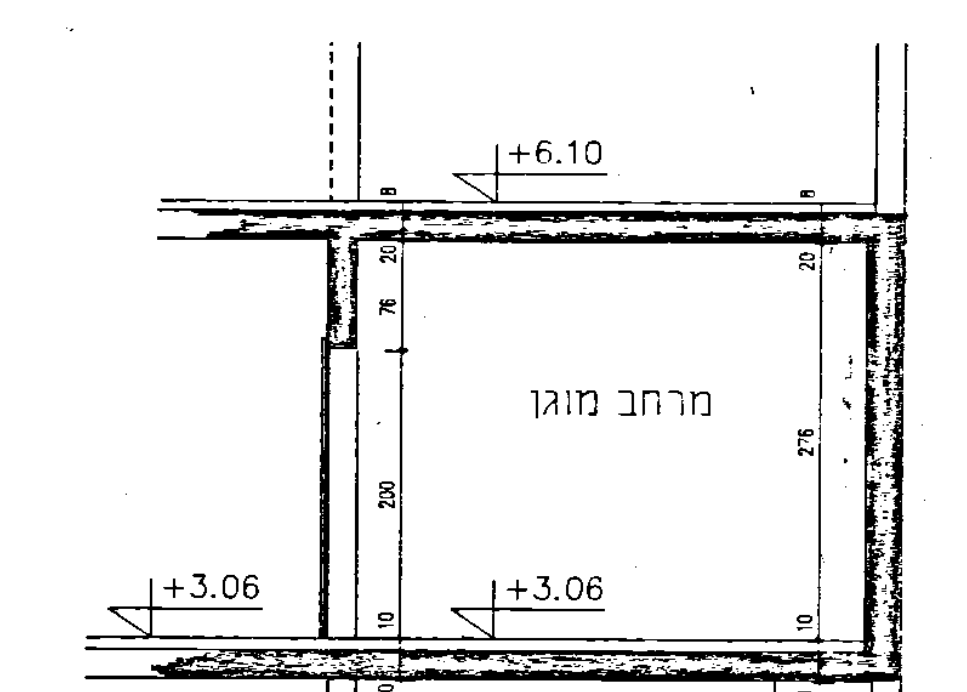

חתך א - א 1 : 50

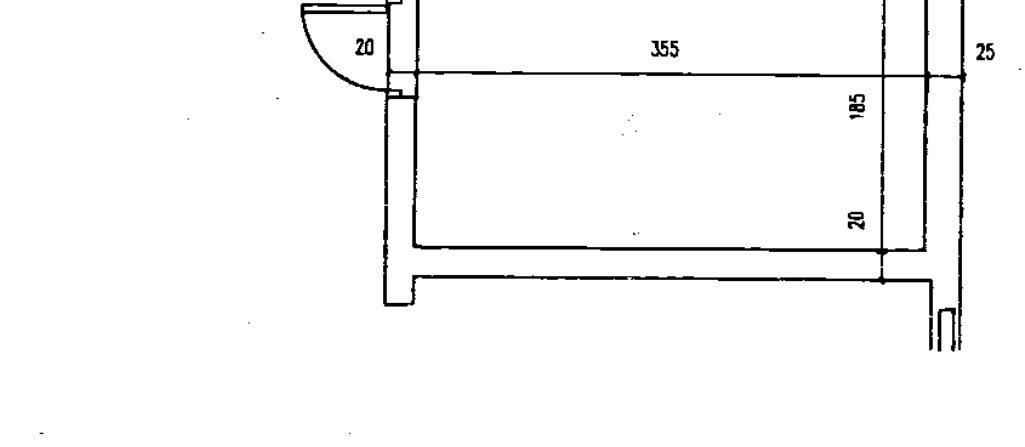חישוב שטח המרחב המוגן :
3.55 x 1.85 = 6.57 מ"ר