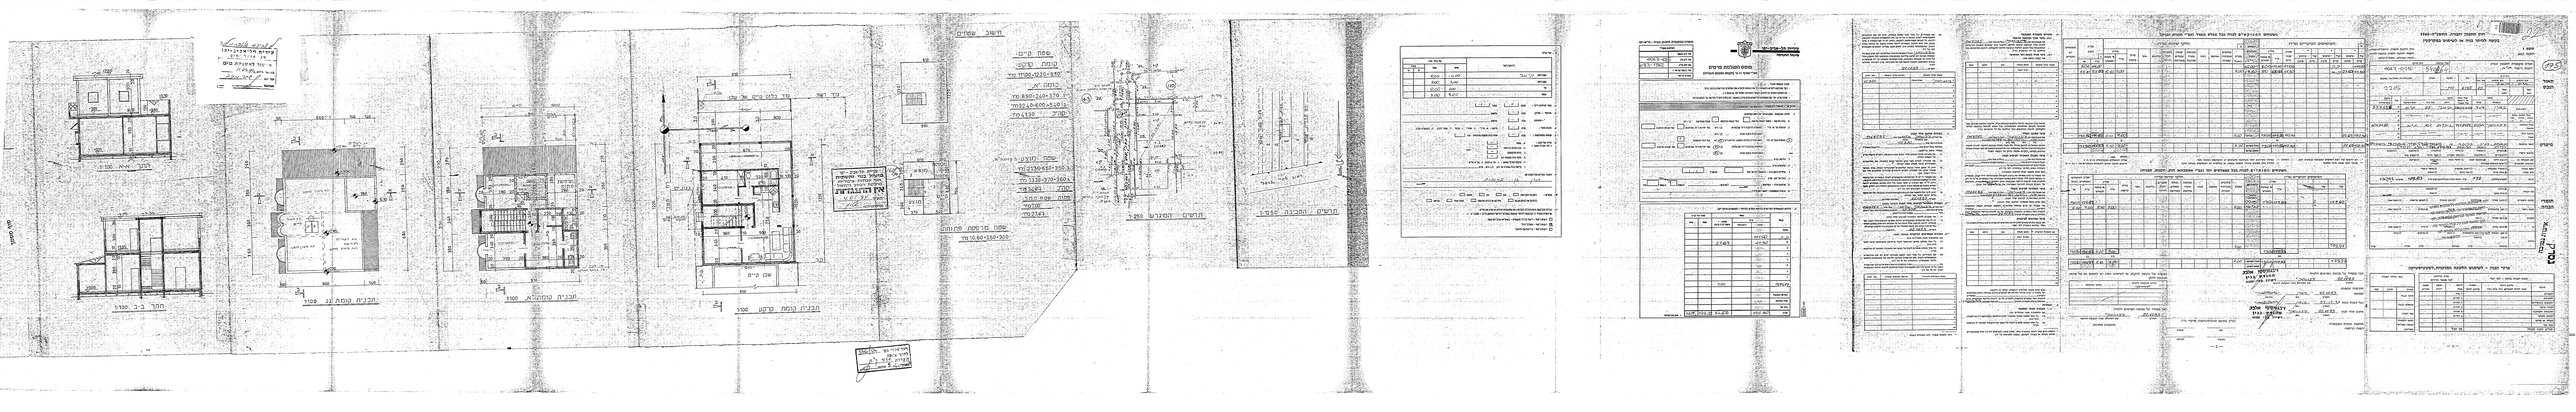

22

012

175

חוק התכנון והבניה, התשכ"ה–1965
בקשה להיתר בניה או לשימוש במקרקעין

חוק התכנון והבניה, התשכ"ה–1965
תקנות התכנון והבניה (בקשה להיתר, תנאיו ואגרות), התש"ל–1970

טופס 1
תקנה 2(א)

ועדה מקומית לתכנון ובניה
רשות רישוי ת"א

מס' תיק: 4047-025
מס' בקשה: 940864

תאור הנכס

התכנית/יות החלה/ות במקום	מגרש	חלקה	גוש	מס' בית	שם הרחוב	שם הישוב
2215		110	6135	25	תשבי	ת"א

	משפחה	פרטי	מס' זהות או רישום של התאגיד	רחוב	מס' בית	ישוב+מיקוד	מס'	טלפון
המבקש	בוין	דוד	58125998	תשבי	25	ת"א	ט.	377196
בעל הזכות בנכס	—"—	—"—	—"—	—"—	—"—	—"—	ט.	
עורך הבקשה הראשי	זיבגורסקי	אלכס	1468785	גורדון	101	ת"א	ט.	6047188
מתכנן שלד הבנין	—"—	—"—	—"—	—"—	—"—	—"—	ט.	

מיפרט

תאור הבקשה: תוספת בניה בקומה א' בשטח 27.67 מ"ר ... הדילה ... בתוספת ... מ"ד (ללא ממ"ד)

שימוש עיקרי: ☒ מגורים ☐ מסחרי ☐ בידור ☐ תעשיה ☐ מלאכה ☐ חקלאי ☐ משרדים ☐ מלונאות ☐ נופש וספורט ☐ בנבי ציבור ☐ שמוש אחר

סוג העבודה או השימוש המבוקש: ☐ בנין חדש ☒ תוספת לבנין ☐ שינוי בבנין ☐ תיקונים ☐ הריסה ☐ שינוי בשימוש ממטרה ... למטרה ...

האם הבניה היא עבור: ☐ משרד ממשלתי ☐ רשות מקומית ☐ מוסד ציבורי ☒ גורם פרטי ☐ בנה ביתך ☐ אחרת

שטח המגרש/חלקה: 138 מ"ר; שטח הבניה הכולל המבוקש: 179.97 מ"ר; % בניה 130.41

חומרי הבניה

סוג הבניה: ☒ רגילה ☐ מתועשת ☐ להרכבה ☐ בית מוכן ☐ אחר

קירות חיצוניים: ☐ בטון מזוין ☒ בלוקים ☐ אבן טבעית ☐ לבנים שרופות ☐ חומר אחר — ידוע לי שהתכנון והפיקוח של התכנית הסניטר...

חומר גימור: ☐ אבן מלאכותית ☒ טיח ☐ חומר אחר — הוראות למתקני תברואה הל"ת 1970 ולפי ...

תקרות: ☒ בטון מזוין ☐ עץ — תקן ישראלי 1205

גג: ☒ בטון מזוין ☐ אסבסט ☐ רעפים ☐ חומר אחר — שהתכנית אינה כוללת צנרת חוץ

גדרות: ☐ אבן טבעית ☐ אבן מלאכותית ☐ בטון ☐ בלוקים ☐ עץ ☐ רשת ☐ ברזל

קיימות ... מ"א; מוצעת ... מ"א; סה"כ ... מ"א

אישור במוכנה

פרטי הבנין – לשימוש הלשכה המרכזית לסטטיסטיקה

יעוד	מספר היחידות (בנין דירות למגורים, בית מלון וכו')	שטח הבנין ברוטו – לפי יעוד	מספר מבנים	מספר קומות	מס' היתר הבניה / תאריך
למגורים					
לאחסנה					
למסחר ולמשרדים					
לבנין ציבור					
לתעשיה ולמלאכה					
למשק חקלאי					
מקלט או מרחב					
מבני עזר					
סך הכל					
סה"כ שטח הבניה					

— 1 —

השטחים המבוקשים לבניה בכל מפלס בנפרד (עפ"י תכנית הבניה)

הקומה והמפלס בבנין	קוד (קיים)	שימוש	סה"כ שטח קיים	מ"ר	% משטח המגרש	מקלט	אחר	סה"כ % משטח המגרש	סה"כ מ"ר	משטחים לא מקורים
±0.00	111.00	ק.ק	111.00	111.00	80.43					
+3.80	41.30 / 27.67	ק. א'	41.30	68.97	50	7.00		5.10	75.97	55.10
סה"כ	152.30 / 27.67		152.30	179.97	130.4	7.00		5.10	186.97	135.50
מעל הקרקע	152.30 / 27.67		152.30	179.97	130.4	7.00		5.10	186.97	135.50

השטחים המותרים לבניה בכל המפלסים יחד (עפ"י אסמכתא: חוק, תקנות, תכנית)

אסמכתא	% משטח המגרש	מ"ר	מקלט	%	מ"ר	סה"כ השטחים המותרים לבניה
תכנית ראשית 2215	130	179.97				
תג"א			7.00	5.10	7.00	
סה"כ	130	179.97	7.00	5.10	7.00	135.50 / 186.97

המקרה של בקשה להקלה או לשימוש חורג יש לחתום גם על פירוט הבקשה להלן:

הנני מצהיר על נכונות הפרטים דלעיל: 22.12.93 — זיבגורסקי — שם וחתימת עורך הבקשה הראשי

חתימות נוספות:

המבקש: בוין — 22.12.93

בעל הזכות בנכס: בוין — 22.12.93

מתכנן שלד הבנין: זיבגורסקי — 22.12.93

זיבגורסקי אלכס
מהנדס בנין
רשיון מס' 15320

חותמת הועדה המקומית / רשות הרישוי

נבדק מטעם הועדה/רשות הרישוי ע"י: שם — תאריך — תפקיד — חתימה

— 2 —

א. מינויים והצהרות המבקש*

1(א). מינוי עורך הבקשה הראשי

אני ממנה בזה את זיבגורסקי בעל/ת מס' זהות 1468785 להיות עורך הבקשה הראשי להיתר, ולייצגני בפני מוסדות התכנון והרשויות המוסמכות בכל הנוגע לטיפול בבקשה להיתר ולקבלתה, לרבות התיקונים בכל שידרשו על ידי הרשויות הנ"ל.

1(ב). מינוי עורכי בקשה (לפי תחומים)

	שמות עורכי הבקשה	תחום פעולה	מען	טלפון	פקס
1.		עורך ראשי			
2.					
3.					
4.					
5.					
6.					
7.					
8.					
9.					
10.					

2. מינוי מתכנן השלד

אני ממנה בזה את זיבגורסקי בעל/ת מס' זהות 1468785 כתובת ת"א גורדון 101 טל' 6047188 להיות אחראי/ת לתכנון השלד של הבנין שעליו מבוקש ההיתר.

3. מינוי הקבלן האחראי לביצוע הבנין

4. מינוי האחראי לביצוע השלד

אני ממנה בזה את זיבגורסקי בעל/ת מס' זהות 1468785 כתובת ת"א גורדון 101 טלפון 6047188 להיות האחראי/ת לביצוע שלד הבנין.

22.12.93 חתימת המבקש

5. מינוי אחראים לביקורת

	שם האחראי לביקורת	תחום פעולה	מען	טלפון	פקס
1.		אחראי ראשי			
2.					
3.					
4.					
5.					

(3) אנו מצהירים, כל אחד לגבי תחום פעולתו, שיש לנו את הכישורים המקצועיים לעורך בקשה זו וכי בדקנו את המסמכים הנוגעים לבקשה, לרבות כל תכנית המתייחסת לבקשה, וידוע לנו כי אם הצהרה זו אינה נכונה, הרי היא תחשב כמסירת ידיעה שהיא כוזבת או מטעה בפרט חשוב, כמשמעותה בסעיף 214 לחוק והננו צפויים לעונשים הקבועים לפי כל דין.

אני זיבגורסקי (עורך הבקשה הראשי) אחראי/ת לכך שהבקשה על נספחיה נערכה לפי מיטב הידיעה המקצועית ובהתאם לכל חיקוק החל על הבנין או העבודה המוצעת.

תאריך: 22.12.93

	שמות עורכי הבקשה	חתימת עורכי הבקשה	מס' רשיון
1.	(עורך ראשי) זיבגורסקי		15320
2.			
3.			
4.			
5.			
6.			
7.			
8.			
9.			
10.			

2. הצהרת מתכנן שלד הבנין

אני החי"מ זיבגורסקי אלכס מס' זהות 1468785, מהנדס רשוי מס' 15320, מצהיר בזאת כדלקמן:

1) אני מסכים להיות מתכנן שלד הבנין נשוא הבקשה, ולקיים פיקוח עליון על הקמת השלד.

תאריך: 22.12.93

3.** הצהרת האחראי לביצוע שלד הבנין (כאשר מונה)

אני החי"מ זיבגורסקי אלכס מס' זהות 1468785, מהנדס רשוי מס' 15320

תאריך: 22.12.93

4.** הצהרת האחראים לביקורת (כאשר מונו)

— 3 —

עיריית תל-אביב-יפו
מינהל התנדסה

הועדה המקומית לתכנון ובניה - ת"א-יפו

לשימוש משרדי	
מס' תיק בקשה	
מס' תיק בנין	4047-025
מס' תיק מידע	מ93-1962
מס' בקשה קודמת *	
מהנדס הרישוי	

טופס השלמת פרטים
עפ"י סעיף 11 ב' (תקנות התכנון והבנייה)

עורך בקשה נכבד
- הנך מתבקש לקרוא בתשומת לב את הטופס ולמלא את הפרטים הנדרשים בכתב ברור.
- את הטופס המלא יש להגיש בצרוף לטופס 1 טופס 1א' או טופס 2 ג.
- טופס מלא יחד עם הנספחים הדרושים ותיק מידע מאושר, הם בסיס להליכי הרישוי עד למתן ההיתר.

חלק א' - תאור הבקשה (לשימוש עורך הבקשה)

1. סיווג הבקשה (סמן בעיגול את הסוג המתאים)

א. בניה חדשה - מספר קומות מלאות ☐ מס' קומות חלקיות ☐ קומה מפולשת כן / לא

ב. תוספת עד 10 מ"ר - במסגרת הרחבת דיור שכונתית כן / לא; מס' יחידות דיור מורחבות ☐ מס' תכנית הרחבה ☐
האם הבניה באגף שלם כן / לא

(ג.) תוספת מעל 10 מ"ר - האם הבניה כוללת הוספת יחידות דיור (כן) לא; מס' יח"ד הנוספות 1
במסגרת הרחבת דיור שכונתית כן (לא); מס' יחידות דיור מורחבות ☐ מס' תכנית הרחבה ☐
האם הבניה באגף שלם כן (לא)

ד. הריסה, פרט ...

ה. שיפוצים, פרט ...

ו. שינוים בזמן בניה - בהמשך להיתר מס' ☐ מתאריך ☐

ז. בניה על הגג, פרט ...

ח. שימוש חורג - משימוש: ... לשימוש: ... בקומה ☐ בשטח ☐ מ"ר

ט. עבודה מצומצמת - תאור העבודה: ...

2. פירוט השטחים הקיימים בהיתר ושלא בהיתר - (שטחים עיקריים)

קומה	קיים בהיתר	קיים ללא היתר	מוצע / * אישור בניה קיימת	הורס לפי תב"ע שטח	הורס לפי תב"ע אחוז
מרתף					
ק.ק	111.00				
א	41.30		27.67		
ב					
ג					
ד					
ה					
ו					
ממ"ד			7.00		
הגביה הקומה					
חדרי מדרגות					
בניני עזר					
סה"כ	152.30		34.67	193.20	140%

* מחק את המיותר

3. קוי בניה

לרחוב/לצד	קוי בניה (מ') מוצע	קוי בניה (מ') מותר	סטיה מ'	סטיה %
שם רחוב תשבי	0.00	0.00		
שם רחוב	3.00	3.00		
צד	0.00	0.00		
אחור	3.00	3.00		

4. מס' יחידות דיור: מוצע 1 מותר 1

5. מרתף - עליון: גבה — שימוש ...
תחתון: גבה — שימוש ...

6. מבנה עזר: גבה — מיקום: א. צדדי ב. אחורי ג. קדמי ד. צמוד לבנין ה. במסגרת הבנין

7. קומה מפולשת: גבה — אחוז בניה בקומה מפולשת (%) ☐

8. בניה על הגג: (לפי תכנית 1680)
א. שטח —
ב. גבה סככה (ברוטו) —
ג. נסיגה מהמעקה —
ד. אחוז בניה משטח הגג —
ה. מיקום קולטי שמש: 1. על גג הבנין 2. על גג עליון
ו. קיימת בניה אחרת על הגג כן / לא, פרט ...

9. תאור הקיים על המגרש: דו־קומתי בן 2 קומות

10. מקרא: ☐ בטון או בטון מזוין ☐ אבן ☐ עץ ☐ איטונג
☐ בלוקים או לבנים סבכות ☐ טיליקט או לבנים ארוזות ☐ חומר אחר ☐ הריסה

11. במידה והבקשה אינה כוללת הקלות ו/או שימושים חורגים נא סמן את הרצ"ם:
אני הח"מ מצהיר כי הבקשה להיתר מוגשת במסלול הרישוי המסומן להלן (100 ב' א'):
☐ רשות רישוי - רישוי בדרך מקוצרת - באחריות עורך הבקשה
☒ רשות רישוי - מסלול רגיל
☐ רשות רישוי - עפ"י מורשה להיתר

חתך א-א 1:100
חתך ב-ב 1:100
תכנית קומת גג 1:100
תכנית קומת א' 1:100
תכנית קומת קרקע 1:100
גדר בלוק קיים של שכן
גדר רשת
שכן קיים
מרפסת פתוחה
ממ"ד
תרשים המגרש 1:250
תרשים הסביבה 1:1250
רחוב לח"י
רח' תשבי

לצרכיה טסיפדה[illegible]
עיריית תל-אביב-יפו
אגף מפעל המים
אישור לאספקת מים
בתנאי מיום 11.04.94
עד יום ... גזבר מפעל
חתימה

עיריית תל-אביב - יפו
מינהל בנוי ותשתית
אגף עבודות ציבוריות
מחלקת הביוב והתעול
אין התנגדות
תאריך 4.05.94
מנהל המחלקה
162/94

רצה אישור מס' 336/94
לתכני אספה
הערות
תאריך 5

חישוב שטחים

שטח קיים:
קומת קרקע:
1. 111.00 = 12.20 × 9.10 מ"ר
קומה "א":
1. 8.90 = 2.40 × 3.70
2. 32.40 = 6.00 × 5.40
סה"כ 41.30 מ"ר

שטח מוצע: בקומה א'
3. 21.35 = 6.40 × 3.50 מ"ר
4. 13.32 = 3.70 × 3.60 מ"ר
סה"כ 34.67 מ"ר
פחות שטח ממ"ד:
7.00 מ"ר
27.67 מ"ר

שטח מרפסת פתוחה:
10.50 = 3.50 × 3.00 מ"ר