575-93 = אד
27.12.93

מפה טופוגרפית
1:250

תל-אביב-יפו
גוש 6135
חלקה 110 (חלק)
שטח לפי נסח 143 מ"ר
שטח מדוד 138 מ"ר
הוכן עבור: מר חוסין
מהות הבקשה - תוספת בניה

עיריית תל-אביב
מינהל ההנדסה
מחלקת המדידות
המפה עברה במחלקות:
☐ דרכים
☑ מים
☑ ביוב
☑ הוחיות צוות
☑ אשפה
☑ חניה
☐ ותיק אירון

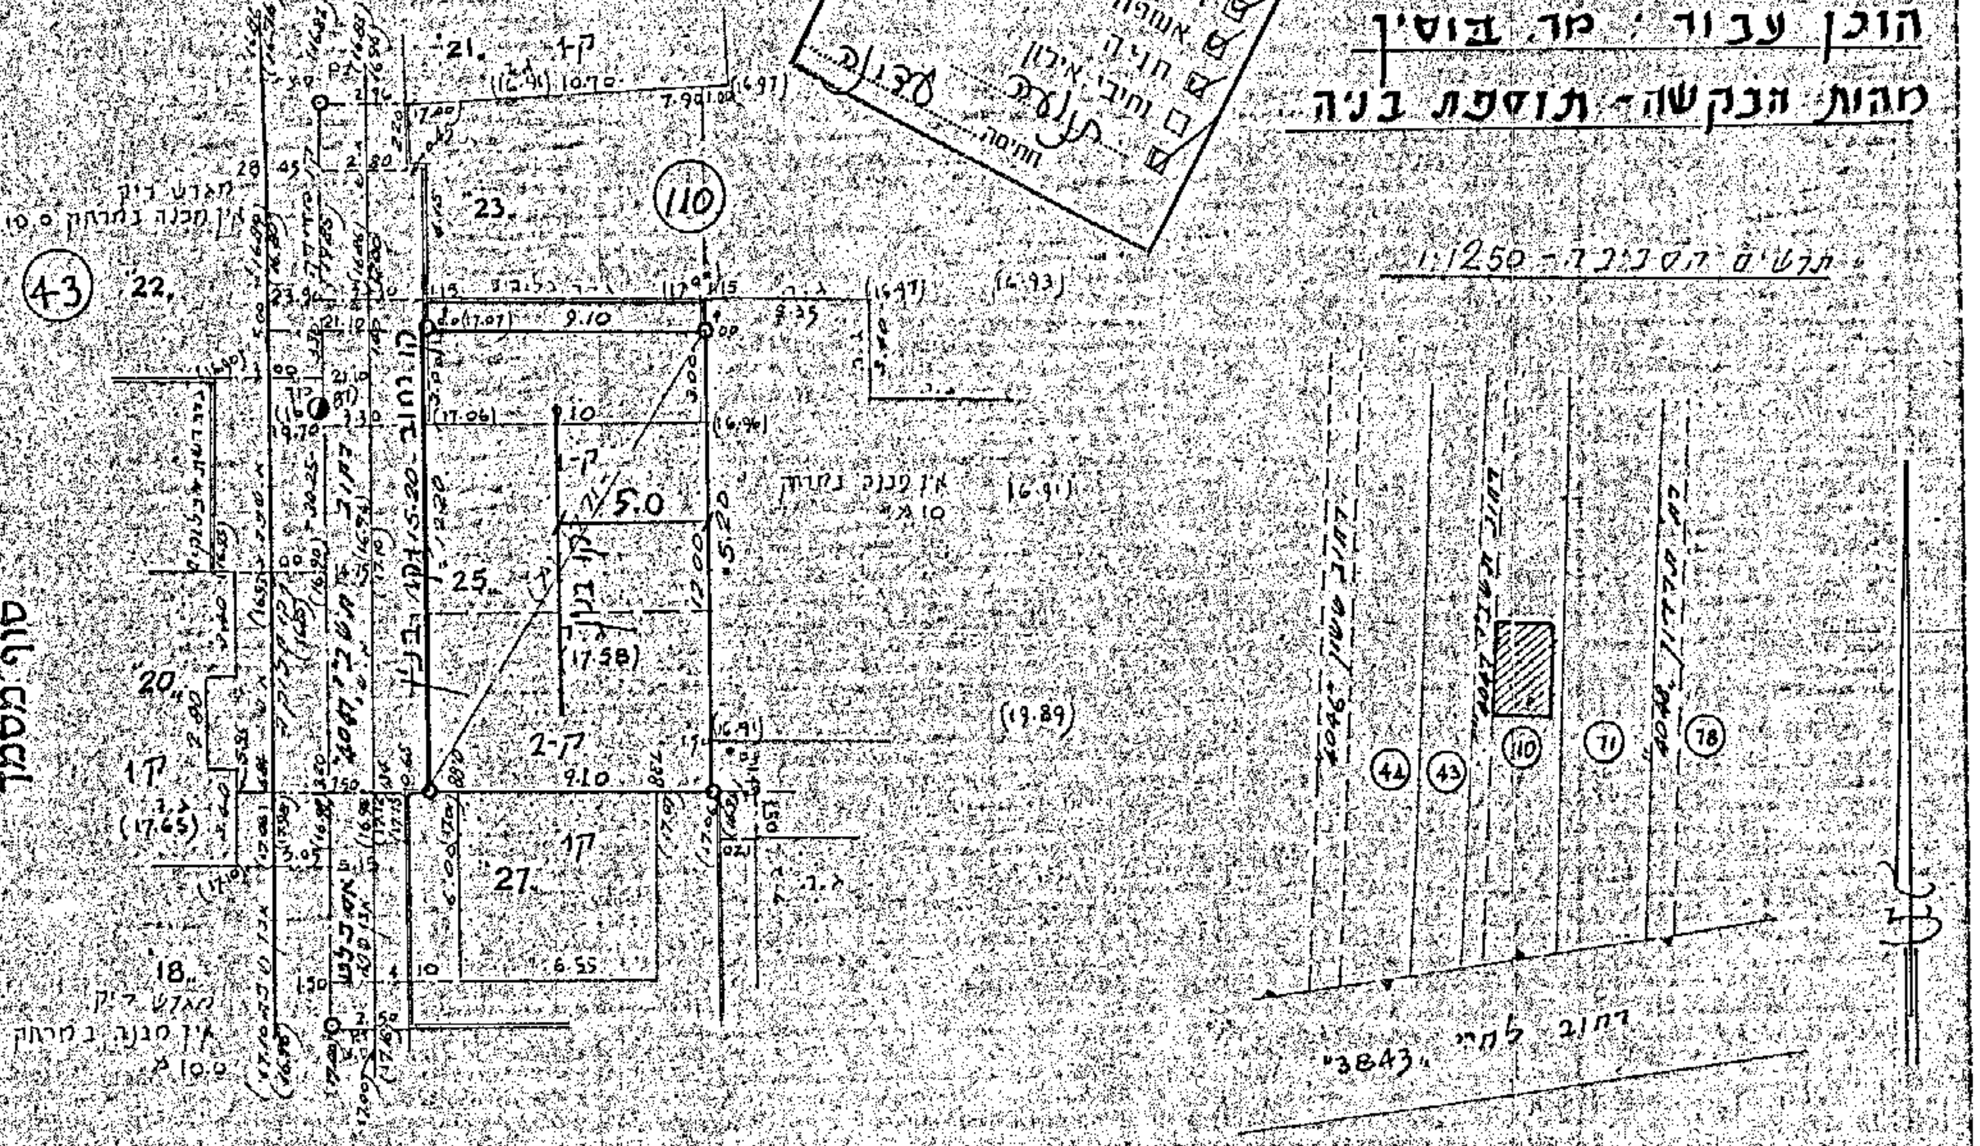

מנהל ההנדסה / אגף תכנון ובנין ערים
מח' שרותי בנין ערים - מדור המידע

הערות למפה טופ' / מצבית

גוש - 6135 חלקה - 110
מס' תיק מידע 1962-92

~~רח' 3671-לוד 37~~
~~רח' 4001-אצ"ל 64~~
~~רח' 4047-תשבי~~ רוחב דרך-8.0

יעוד בתוקף - אזור מגורים ב
תכניות בתוקף - 2215
הערות - לפי תכנית 2215 רחוב 4047-תשבי ברוחב 8-5 מ',
קו בנין 0 מ'. קוי בנין צדדים 3 מ' או 0 מ'
(קירות משותפים) ולאחור 5 מ'..
גובה הבנין 3 קומות ,סה"כ 140 אחוזים.
תכסית קרקע מירבית 60%.
תצפיפות 10 דירות לדונם.
מרתפים לפי תכנית "ע" ויציאות לגג לפי תכנית
1680.אין לגבות היטל השבחה היות והשכונה הוכרזה
כשכונת שקום.המגרש טעון הסדר אשר יעשה במסגרת
הסדר הגוש והשכונה כולה.יש לתאם את התכנון עם
צוות מזרח באגף תב"ע.

נסרק

חתימה 26.12.93
חתימה 26.12
חתימה מנהל מדור המידע

עיריית תל-אביב-יפו
מינהל בינוי ותשתית / אגף עבודות ציבוריות
מחלקת נכסים
חתימה
חתימה
תאריך 27.12.93

הנני מאשר שהתכנית נעשתה לפי חוק תכנון והבניה
הוראות והנחיות עיריית תל-אביב-יפו

לא לצרכי רישום

להבי קוי בנין צדדים
ראה הערות אגף
בנין ערים.

הערות
1. הגבהים מבוססים על גובה ק' 17.549=187
2. המספרים נסוגים מסמנים גובהים

תל-אביב
25.11.1993

מודד מוסמך
רשיון מס' 278

לאון כהנא
משרד טכני למדידות
תכנון ופקות בע"מ
רח' ז'בוטינסקי 152, תל-אביב
טל. 03-6957234

עיריית תל-אביב-יפו / מינהל הנדסה
מחלקת המדידות
אישור כתובת
רחוב תשבי מס' 25 4047
רחוב מס'
רחוב מס'
תאריך 27.12.93 חתימה

שטח הפקעה (לצורך חשוב זכויות בניה)
מאושר (ת.ב.ע) מ"מר (נר)
מוצע (ת.ב.ע) מ"מר (
הערה: שטח הפקעה סופי יקבע במפה לצ"ר