חוק התכנון והבניה, התשכ"ה-1965
תקנות התכנון והבניה (בקשה להיתר, תנאיו ואגרות), התש"ל-1970

הבקשה להיתר - מיועדת להגשה לועדה המקומית לתכנון ובניה של עירית תל-אביב - יפו בלבד

015

הוועדה המקומית לתכנון ולבניה תל-אביב - יפו

טופס 2 (תקנה 2(א))

תיק מס׳: 4047-026

מיפרט 22

70

א. תיאור הבנין

1. המקום	הרחוב	מס׳	גוש	חלקה	תכנית מיתאר מקומית או מפורטת	מגרש
תל - אביב	תשבי	26	6135	43		מגורים

	השם	המען	מס׳ הטלפון
2. המבקש	רוני אהרן קדאל	רח׳ תשבי 26 ת"א	
3. בעל הזכות בנכס	— " —	— " —	
4. עורך הבקשה *	ד"ג גורסקי א	שד׳ נורדאו 88 ת"א	5441488
5. האחראי לביצוע השלד	— " —	— " —	— " —

6. איזור הבניה: ☒ מגורים ☐ מסחר ☐ תעשיה ☐ בנין ציבורי ☐ חקלאי ☐ ....

7. שטח: המגרש/החלקה: 82 מ"ר אחוז הבניה המיתר: ...%

8. מטרת הבנין: ☒ מגורים ☐ הארחה ☐ עסקים ☐ תעשיה ☐ חקלאי ☐ ציבורי ☐ ....

9. מהות הבנין ותכליתו: תוספת לבנין בקומת קרקע.

10. תיאור העבודה המוצעת: ☐ בנין חדש ☒ תוספת לבנין קיים ☐ הריסה ☐ תיקונים ☐ שינוי בבנין ☐ .... ☐ שינוי בשימוש ממטרה .... למטרה ....

11. האם הבניה היא בעד: ☐ משרד ממשלתי ☐ הרשות המקומית ☐ הסוכנות היהודית

ב. היקף הבניה

קומה	קיים: בהיתר	קיים: ללא היתר	מוצע: אישור בניה קיימת	מוצע: בניה חדשה	סך הכל	אחוזי בניה: שטח מחושב באחוזים	אחוזי בניה: %	מגורים בדירות: עד 45 מ"ר	עד 65 מ"ר	עד 90 מ"ר	עד 100 מ"ר	מעל 100 מ"ר	עסק: הארחה וכו׳	ציבורי	שונות	מס׳ חדרים: קיים	מס׳ חדרים: מוצע
1	2	2א	3	3א	4	5	5א	6	7	8	9	10	11	12	13	14	15
מרתף																	
קרקע	48.11			7.10	55.21												
א	27.73				27.73												
ב																	
ג																	
ד																	
ה																	
ו																	
ז																	
הכניסה הקובעת																	
חדרי מדרגות																	
בניני עזר																	
סך הכל	75.84			7.10	82.94												

הגובה המוצע: של הבנין העיקרי .... מ"ס. של בנין עזר .... מ"ס.

ג. השימוש בבנין

1. הבניה המוצעת למגורים

דירות בנות:	שטח כל דירה מ"ר	מספר דירות מכל סוג	כל הדירות	מזה: רצפות חדרי דיור בלבד, ומרפסות מקורות	רצפות חדרי שירות ופרוזדורים בלבד	רצפות של מרפסות בלתי מקורות	מספר החדרים: דיור	מטבחים	אמבטיות	שימוש	אחרים
1			4	5	6	7	8	9	10	11	12
חדר אחד											
2 חדרים											
3 חדרים											
4 חדרים											
5 חדרים											
6 חדרים											
7 חדרים ויותר											
חדרים נוספים לדירות קיימות											
בניני עזר											
סך הכל											

(בכתב יד:) ההיתר לבנית השטח התוספת והשטח המבוקש. הגג יהיה לפי החלטת ועדת הבנין שאושרה. ניתן לשנות את הפתח הקיים לתוספת... מרחב מוגן

(חותמת:) מחלקת פיקוח... תאריך 14.1.98

(חותמת:) גליסינר... מ׳ הנדסה ורישוי...

בסרק

---

2. הבניה הקיימת והמוצעת לתעשיה ולמלאכה

פרטים	קיים: שטח	קיים: גובה	קיים: נפח	קיים: % הבניה	מוצע: שטח	מוצע: גובה	מוצע: נפח	מוצע: % הבניה	סך הכל: שטח	סך הכל: נפח	סך הכל: % הבניה	הערות
1	2	3	4	5	6	7	8	9	10	11	12	13
אולמי מלאכה												
משרדים												
חדרי שירות												
סככות												
בניני עזר												
חדרי מדרגות												
סך הכל												

3. הבניה המוצעת למטרות אחרות (הארחה, עסקים ומשרדים, בניני ציבור, בניני משק חקלאי, מטרות שונות).

השימוש המיועד	סך הכל מ"ר	מזה: חדרים	אולמות	אחסנה	חדרי שירות	מספר חדרים, אולמות וכו׳: חדרים	אולמות	אחסנה	חדרי שירות
1	2	3	4	5	6	7 *	8	9	10
בניני עזר (למעט אלה הנכללים ב-ג(4))									

4. חלקי בנין אחרים - הבניה המוצעת, שטח במ"ר.

חדרי מדרגות	מרפסות שלא נכללו לעיל	מעליות	חדרי הסקה	חדרי כביסה	מקלטים	קיבת שמירה כפולית	מחסנים	מוסכים	בניני עזר נוספים	סך הכל
1	2	3	4	5	6	7	8	9	10	11

ד. חומר הבניה

קירות חיצונים	☐ בטון מזוין	☐ לבני בטון או בלוקים	☐ לבני סיליקט	☐ לבנים שרופות	☐ אבן טבעית	
	☐ אבן מלאכותית	☐ איסבנג	☐ עץ	☐ ברזל		חמרים אחרים
תקרות	☐ בטון מזוין	☐ עץ	☐ חומר אחר			
גג	☐ בטון מזוין	☐ רעפים	☐ אסבסט	☐ פח	☐ חומר אחר	

ה. גדרות

קיימות .... מ"א מוצעות .... מ"א

ו. מקרא

בטון או בטון מזוין — אבן — עץ — איסבנג
בלוקים או לבנים בבטון — סיליקט או לבנים אדומות — חומר אחר — להריסה

הערות: ....

הנני מאשר כי הנתונים הנ"ל נכונים

תאריך 2/1/92 חתימת המבקש .... חתימת עורך הבקשה * ....
התימת האחראי לביצוע השלד .... חתימת בעל הזכות בנכס ....

(חותמות:) א.א. הנדסה מהנדסי בנין

לשימוש הוועדה המקומית בלבד	מס׳ ההיתר	תאריך ההיתר	תאריך התחלת הבניה	תאריך גמר הבניה

אישורים של רשויות חוץ:

חותמת הוועדה המקומית

* היו מספר עורכי בקשה, כאמור בתקנה 2ה׳, יביא במקום כל אלה הראשון שברשימת עורכי הבקשה, כאמור בטופס 1.

עיריית תל אביב - יפו
מינהל ההנדסה

בקשה להיתר בניה

לשימוש משרדי	
מס׳ תיק בקשה	
מס׳ תיק בנין	
מס׳ תיק מידע	
מס׳ בקשה קודמת *	

עורך בקשה נכבד

- הנך מתבקש לקרוא בתשומת לב את הטופס ולמלא את הפרטים הנדרשים בכתב ברור.
- את הטופס המלא יש להגיש בצמוד למפרט (טופס 2).
- טופס מלא, יחד עם תיק צהוב ותיק מידע מאושר, הם בסיס להליכי הרישוי עד למתן ההיתר

חלק א׳ - תאור הבקשה (לשימוש עורך הבקשה)

1. **סיווג הבקשה** (סמן בעיגול את הסוג המתאים)

א. בניה חדשה - מספר קומות מלאות ☐ מס׳ קומות חלקיות ☐ קומה מפולשת כן / לא

ב. תוספת עד 10 מ"ר - במסגרת הרחבת דיור שכונתית כן / לא מס׳ יחידות דיור מורחבות ☐
האם הבניה באגף שלם כן / לא

ג. תוספת מעל 10 מ"ר - במסגרת הרחבת דיור שכונתית כן / לא מס׳ יחידות דיור מורחבות ☐
האם הבניה באגף שלם כן / לא

ד. הריסה, פרט ....

ה. שיפוצים, פרט ....

ו. שינויים בזמן בניה - בהמשך להיתר מס׳ ☐ מתאריך ☐

ז. בניה על הגג, פרט ....

ח. שימוש חורג - משימוש: .... לשימוש: .... בקומה ☐ בשטח ☐ מ"ר

ט. עבודה מצומצמת - תאור העבודה: ....

2. היקף הבניה המוצעת לסמכות זכויות מותרות

קומה	שטח: קיים: בהיתר	קיים: ללא היתר	מוצע: אישור בניה קיימת	מוצע: בניה חדשה	סה"כ	אחוזי בניה ע"פ הבקשה: שטח מחושב **	אחוז	מותר לפי תב"ע: שטח	אחוז	סטיה: שטח	אחוז	סיבת הסטיה/נימוקים
מרתף												
קרקע	48.11			7.10	55.21							
א	27.73				27.73							
ב												
ג												
ד												
ה												
ו												
ז												
הכניסה הקובעת												
חדרי מדרגות												
בניני עזר												
סה"כ	75.84			7.10	82.94							

** באחוזי בניה

* עבור התלמות שפג תוקפן או בקשות להארכת תוקף היתר

---

3. **מהות הבקשה - תאור מילולי** (ראה הנחיות למילוי בטופס מצ"ב)
....

4. **קוי בניה**

לרחוב/לצד	קו בניה (מ׳): מוצע	מותר	סטיה: מ׳	%	רוחב קולונדה (מ׳): מוצע	מותר	סטיה: מ׳	%
שם רחוב								
שם רחוב								
צד								
אחור								

5. **מס׳ יחידות דיור**: מוצע ☐ מותר ☐

6. **מרתף - עליון** גובה ☐ שימוש ....
- תחתון גובה ☐ שימוש ....

7. **מבנה עזר**: גובה ☐ מיקום: א. צדדי ב. אחורי ג. קדמי ד. צמוד לבנין ה. במסגרת הבנין

8. **קומה מפולשת**: גובה ☐ אחוז בניה מקומה מפולשת (%) ☐

9. **בניה על הגג**:
א. שטח ☐
ב. גובה מבנה (ברוטו) ☐
ג. נסיגה מהמעקה ☐
ד. אחוז בניה משטח הגג ☐
ה. מיקום קולטי שמש: 1. על גג הבנין 2. על גג עליון
ו. קיימת בניה אחרת על הגג כן / לא, פרט ....

10. **קיים חדר מדרגות כללי**: כן / לא

11. **נימוקים לבקשה להקלה**
....

12. **תאור הקיים על המגרש**
....

13. אם ניתנה בידך האפשרות לבחור בין מסלול רישוי בדרך מקוצרת ומסלול רישוי בדרך רגילה נא מלא את הד"ם.
אני הח"מ מצהיר כי הבקשה להיתר מוגשת במסלול הרישוי המסומן להלן (סמן ב־"x"):
☐ רשות רישוי - רישוי בדרך מקוצרת - באחריות עורך הבקשה
☐ רשות רישוי - מסלול רגיל

חלק ב׳ - הצהרת עורך הבקשה

אני, הח"מ כלול בפנקס המורשים מצהיר בזאת שהבקשה הוכנה לפי כל דין ותקנה ובהתאם לחוק המידע אשר נמסר לי.
הפרטים, המסמכים, האישורים, ההצהרות וכל הנספחים לבקשה הינם נכונים וחתימתי עליהם יראו אותה כחתימה על הצהרה.

תאריך .... שם עורך הבקשה .... מס׳ רשיון .... חתימה ....

חלק ג׳ (לשימוש משרדי)

1. מועד קבלת בקשה ☐
2. הערות ....

תאריך חתימה .... שם המטפל .... חתימה ....

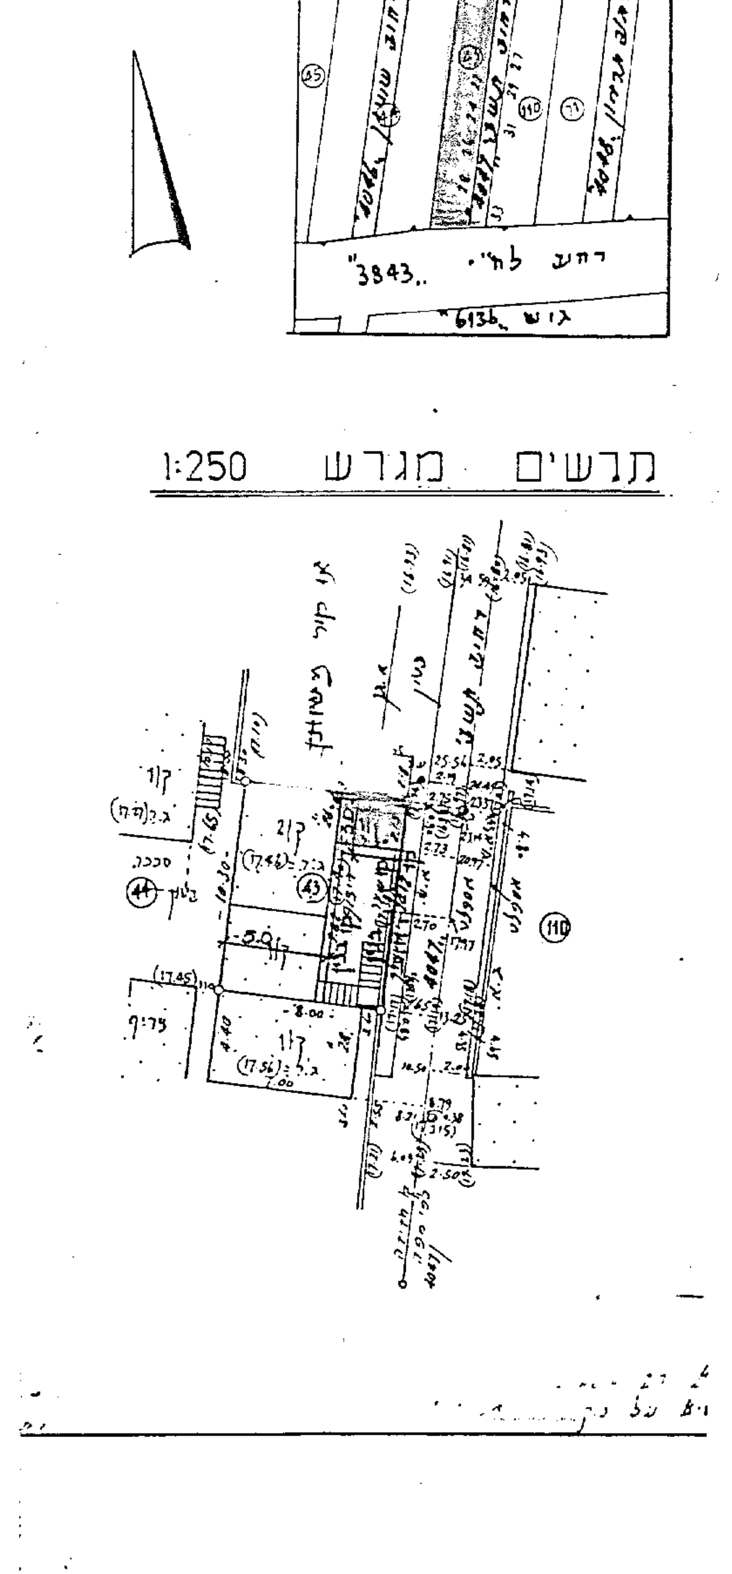

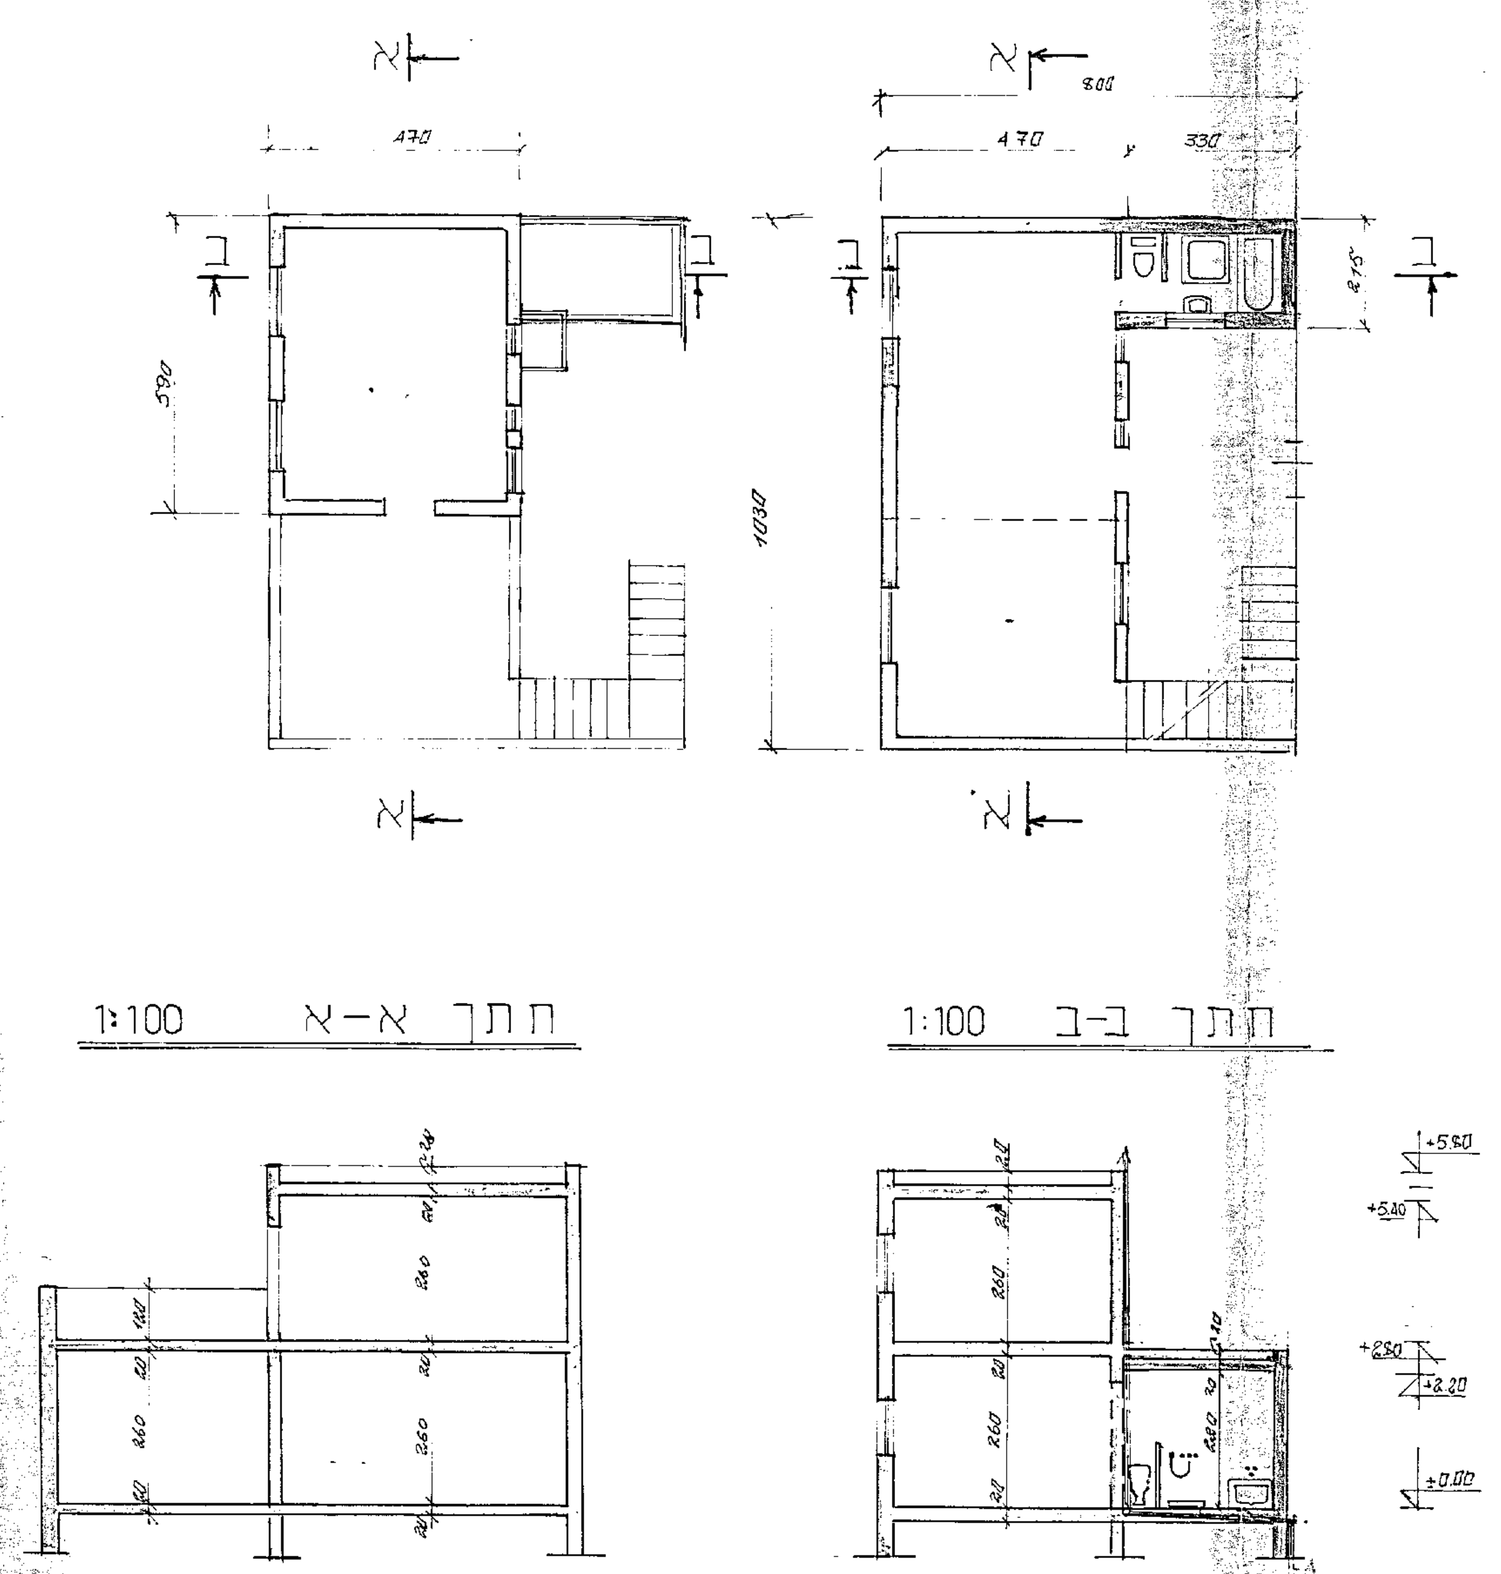

חזית מזרחית 1:100

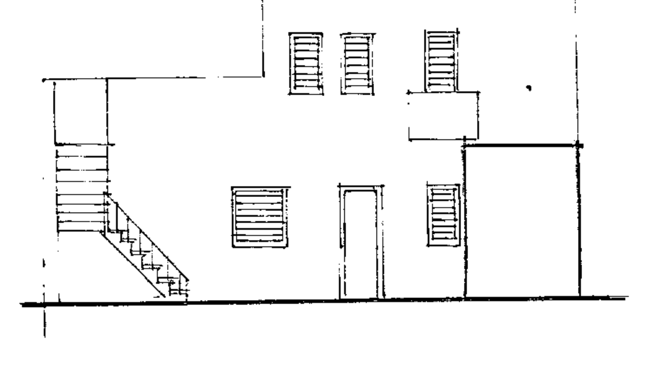

חזית מערבית 1:100

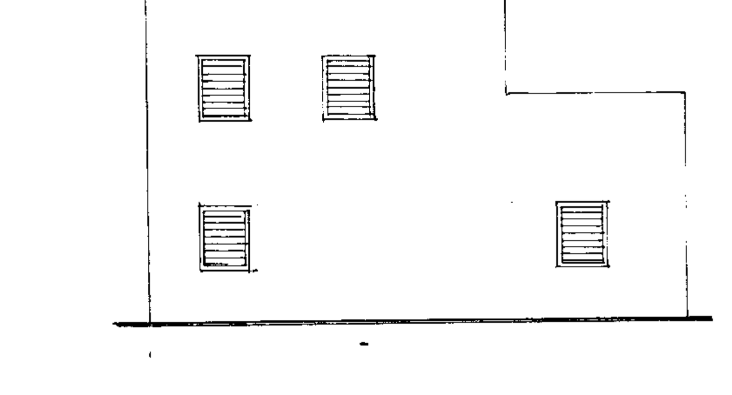

חזית צפונית 1:100

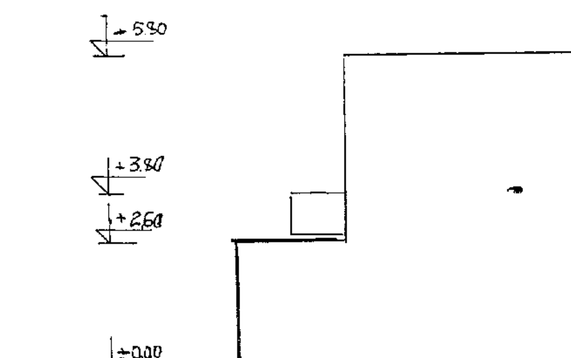

חישוב שטחים

שטח קומת קרקע:
קיים: 10.30×4.70 = 48.11
מוצע: 3.30×2.15 = 7.10
סהכל 55.21

שטח קומה א
קיים 5.90×4.70 = 27.73 מ"ר

שטח מבנה סהכל מ"ר 82.94

סוף מסמך